



VB1

ESC 1:50

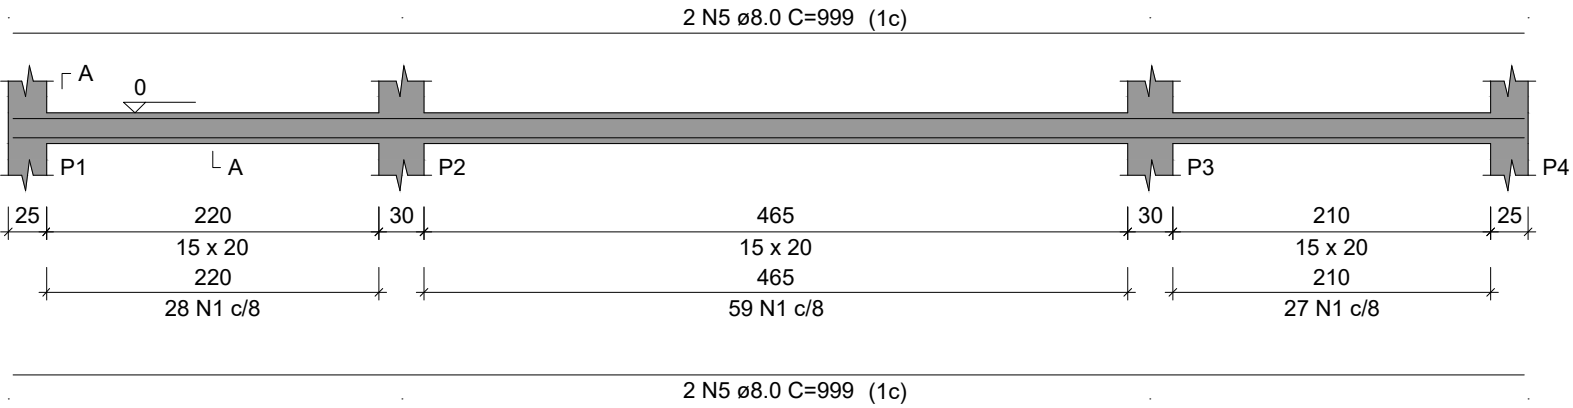


VB2

ESC 1:50

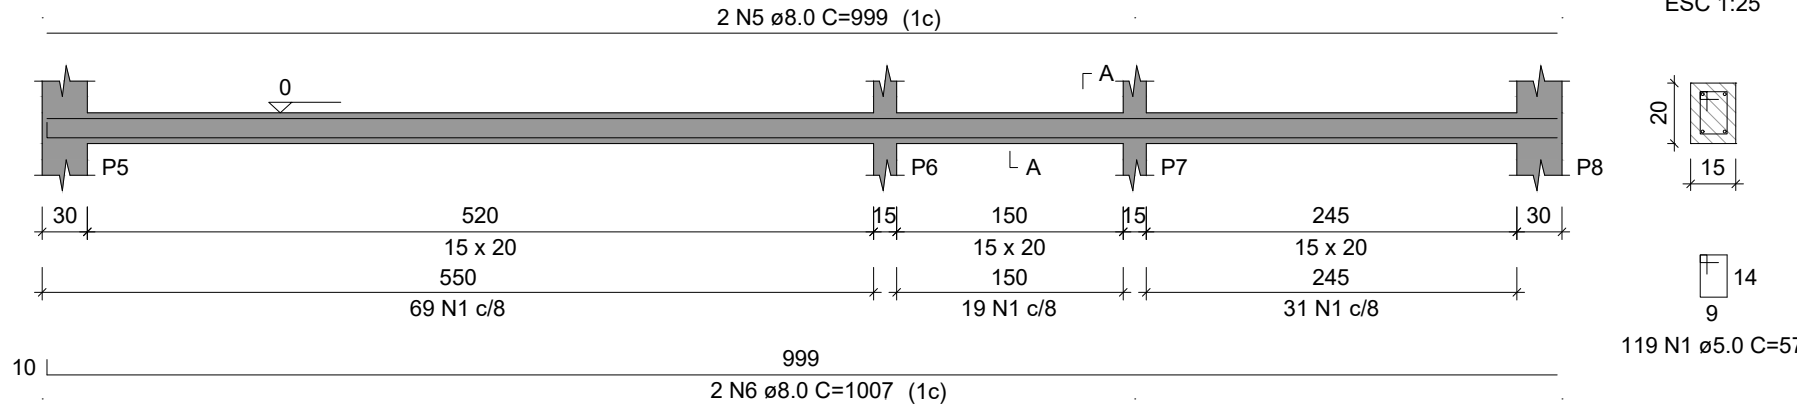


VB3

ESC 1:50

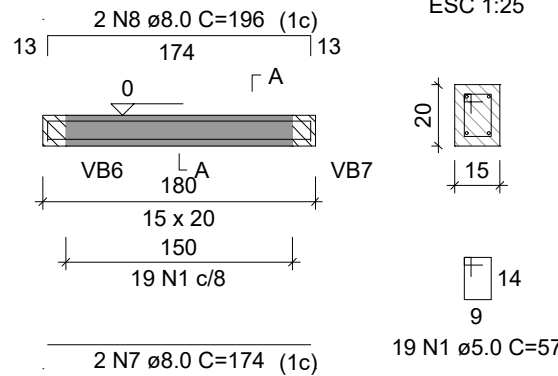


VB4

ESC 1:50

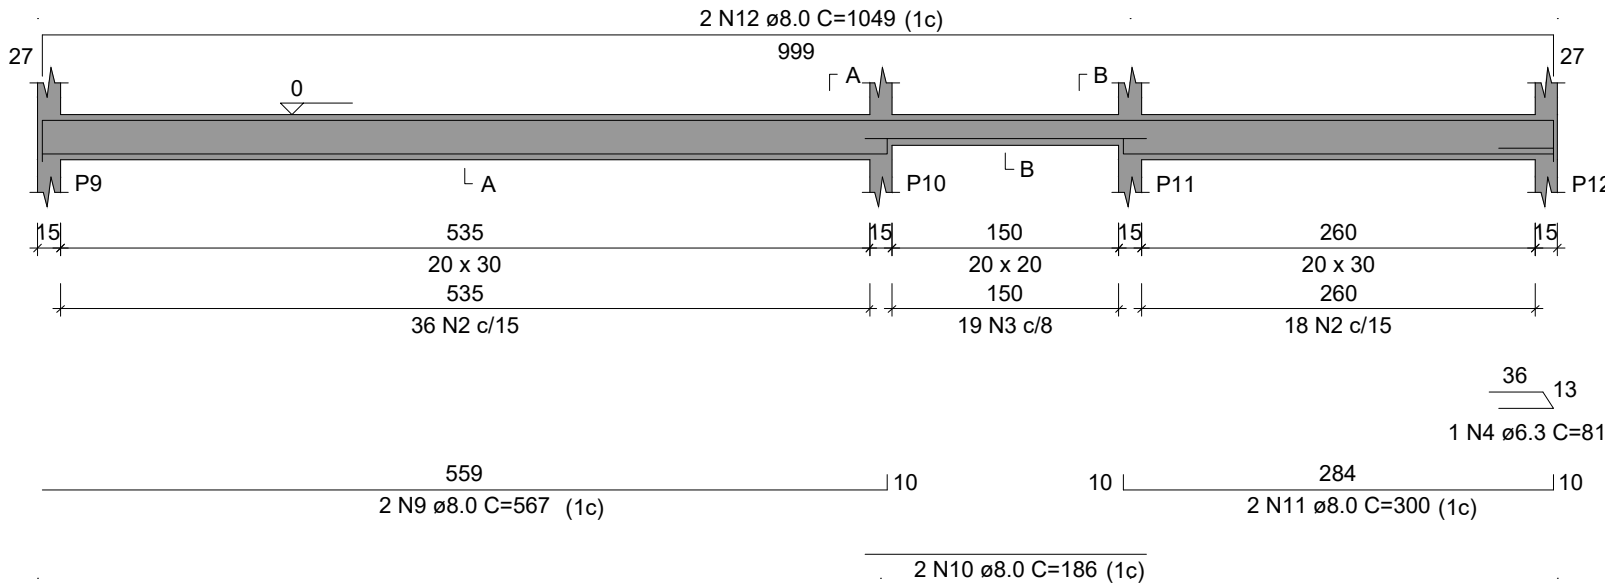


VB5

ESC 1:50

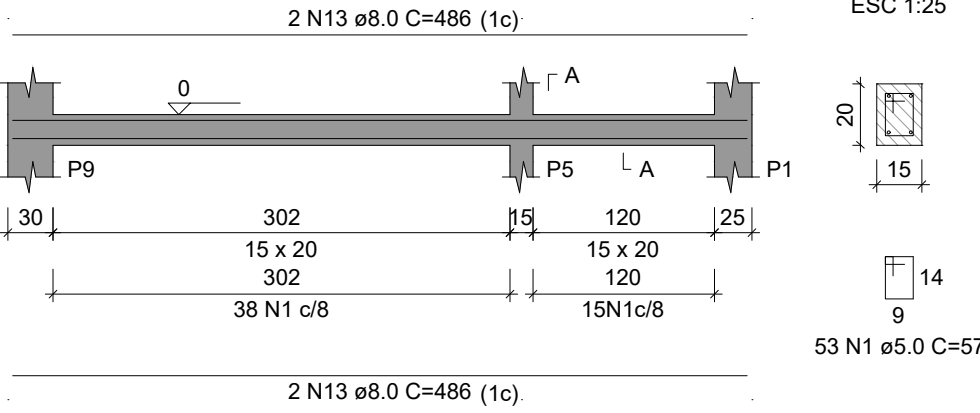


VB6

ESC 1:50

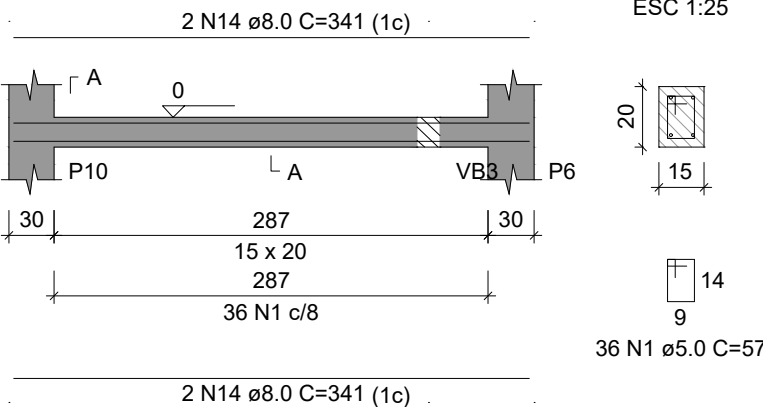


VB7

ESC 1:50

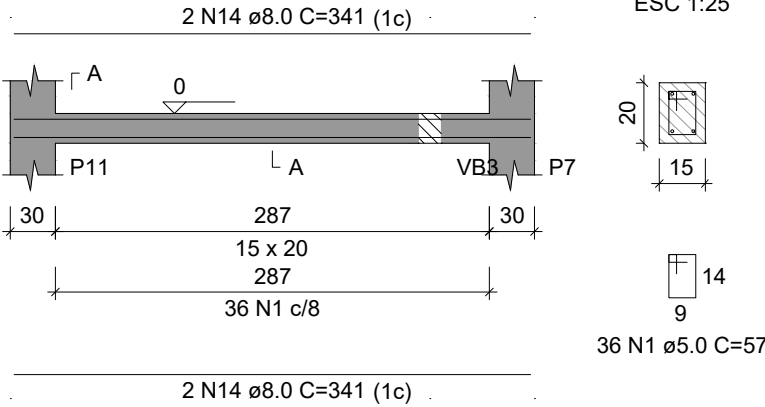

VB8

ESC 1:50

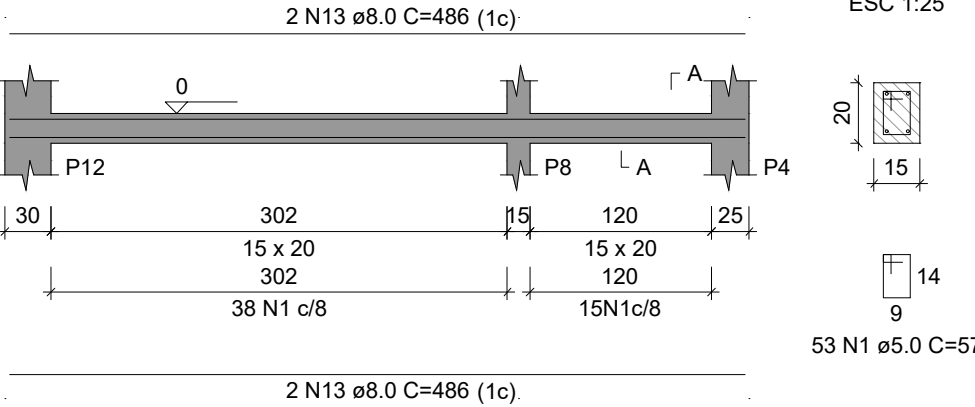

RELAÇÃO DO AÇO

AÇO	N	DIAM (mm)	QUANT	C.UNIT (cm)	C.TOTAL (cm)
CA60	1	5.0	430	57	24510
	2	5.0	54	87	4698
	3	5.0	19	67	1273
	4	6.3	1	81	81
	5	8.0	6	999	5994
	6	8.0	2	1007	2014
	7	8.0	2	174	348
	8	8.0	2	196	392
	9	8.0	2	567	1134
	10	8.0	2	186	372
	11	8.0	2	300	600
	12	8.0	2	1049	2098
	13	8.0	8	486	3888
	14	8.0	8	341	2728

RESUMO DO AÇO

AÇO	DIAM (mm)	C.TOTAL (m)	PESO + 10% (kg)
CA50	6.3	0.8	0.2
	8.0	195.7	84.9
	5.0	304.8	51.7
PESO TOTAL (kg)			
CA50	85.2		
CA60	51.7		

Volume de concreto (C-25) = 1.73 m³

Área de forma = 28.98 m²

PROPRIETÁRIO: PREFEITURA MUNICIPAL DE COREMAS- PB
LINCOLN CARTAXO DE LIRA JUNIOR:06897861405
Assinado de forma digital por LINCOLN CARTAXO DE LIRA JUNIOR:06897861405
Dados: 2025.07.14 11:27:48 -03'00'

PROJETO: LINCOLN CARTAXO DE LIRA JÚNIOR CREA 160.814.689-8

FOLHA	PROJETO: GARAGEM COREMAS (ESTRUTURAL ANEXO I)			
06/09		CONVENIENTE: PREFEITURA MUNICIPAL DE COREMAS-PB CONCENDENTE: PREFEITURA MUNICIPAL DE COREMAS-PB LOCALIDADE: COREMAS- PB		
DESENHO	DATA	RESPONSÁVEL	RUBRICA	DADOS
CÓPIA	JUN/2025	LINCOLN CARTAXO		
VISTO				
ESCALAS	DESENHOS			CONVÊNIO
INDICADO	- VIGAS BALDRAME			ARQUIVO

Aprovações: