




VS200

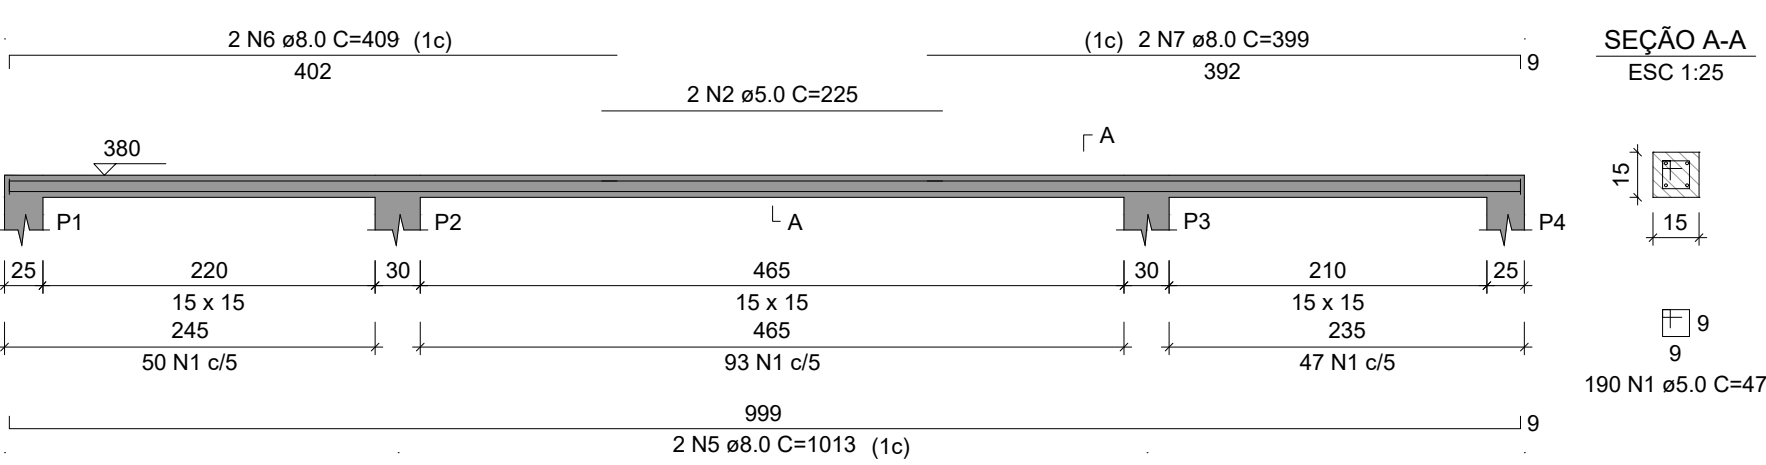


VS201

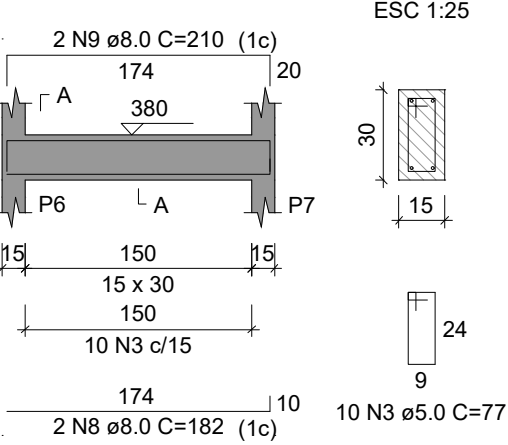


VS202

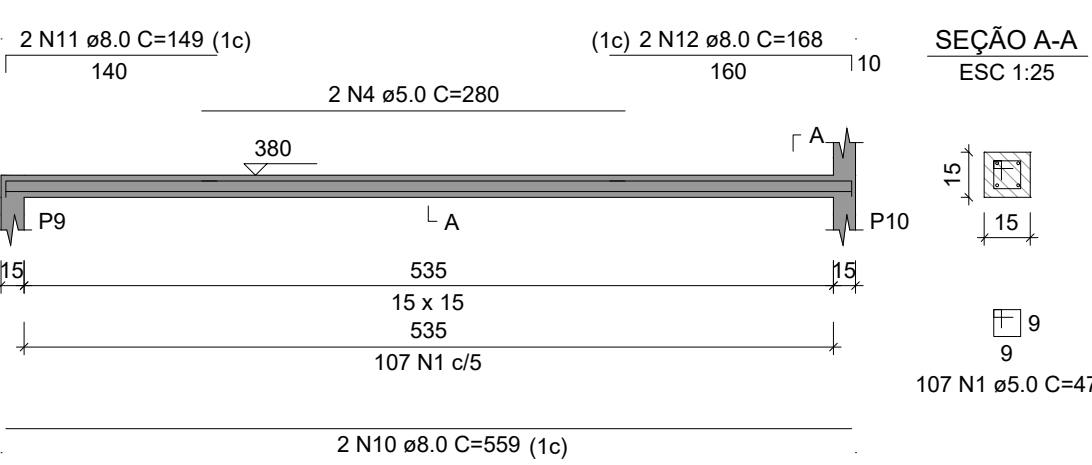


VS203

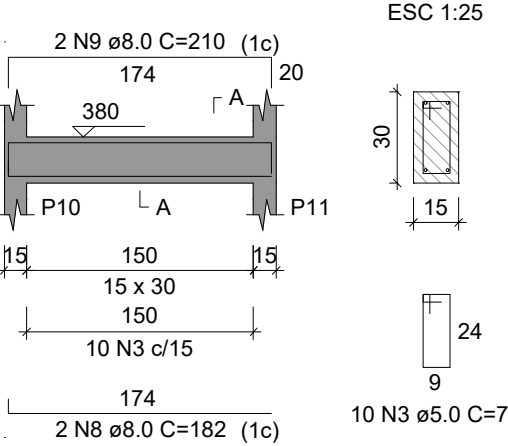


VS204

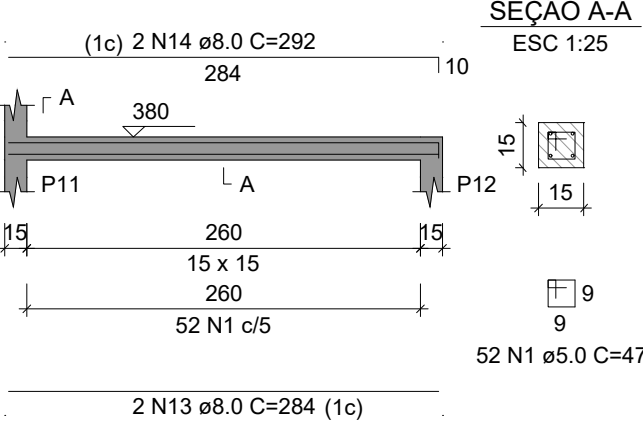


VS205

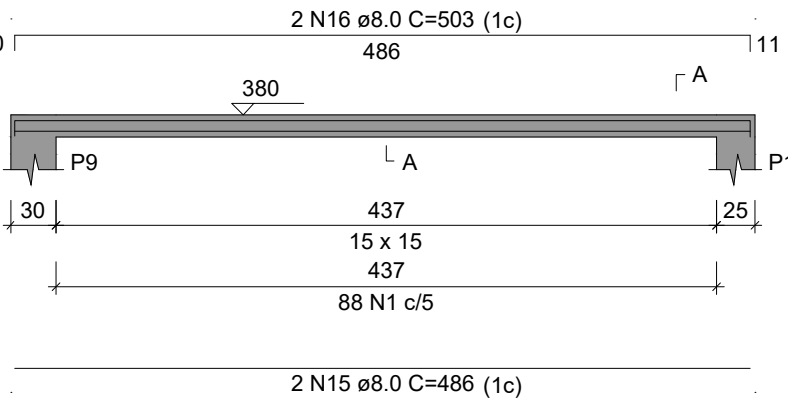


VS206

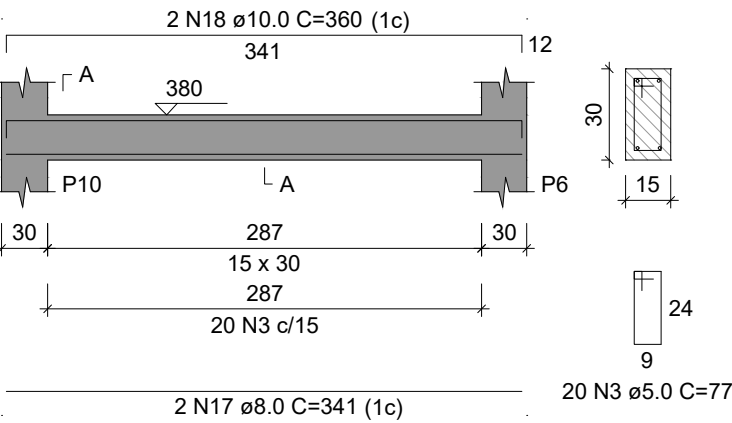

VS207

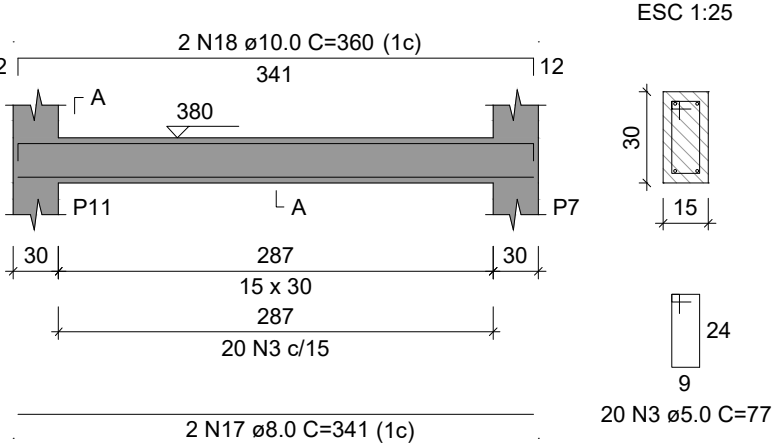

VS208

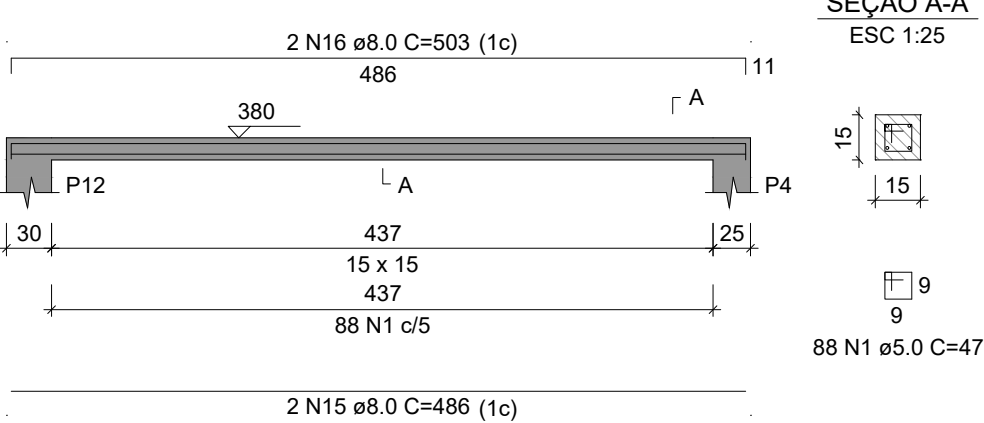

RELAÇÃO DO AÇO

AÇO	N	DIAM (mm)	QUANT	C.UNIT (cm)	C.TOTAL (cm)
CA60	1	5.0	525	47	24675
	2	5.0	2	225	450
	3	5.0	60	77	4620
CA50	4	5.0	2	280	560
	5	8.0	2	1013	2026
	6	8.0	2	409	818
	7	8.0	2	399	798
	8	8.0	4	182	728
	9	8.0	4	210	840
	10	8.0	2	559	1118
	11	8.0	2	149	298
	12	8.0	2	168	336
	13	8.0	2	284	568
	14	8.0	2	292	584
	15	8.0	4	486	1944
	16	8.0	4	503	2012
	17	8.0	4	341	1364
	18	10.0	4	360	1440

RESUMO DO AÇO

AÇO	DIAM (mm)	C.TOTAL (m)	PESO + 10% (kg)
CA50	8.0	134.3	58.3
CA60	10.0	14.4	9.8
CA60	5.0	303.1	51.4
PESO TOTAL (kg)			
CA50	68.1		
CA60	51.4		

Volume de concreto (C-25) = 1.11 m³
Área de forma = 20.70 m²

PROPRIETÁRIO: PREFEITURA MUNICIPAL DE COREMAS- PB
Assinado de forma digital por LINCOLN CARTAXO DE LIRA JUNIOR:06897861405 JUNIOR:06897861405
Dados: 2025.07.14 11:27:22 -03'00'
PROJETO: LINCOLN CARTAXO DE LIRA JÚNIOR CREA 160.814.689-8

FOLHA	PROJETO: GARAGEM COREMAS (ESTRUTURAL ANEXO I)		
	CONVENIENTE: PREFEITURA MUNICIPAL DE COREMAS-PB		
	CONCIDENTE: PREFEITURA MUNICIPAL DE COREMAS-PB		
	LOCALIDADE: COREMAS- PB		
08/09			
DESENHO	DATA	RESPONSÁVEL	RUBRICA
CÓPIA	JUN/2025	LINCOLN CARTAXO	
VISTO			
ESCALAS	DESENHOS		CONVÊNIO
INDICADO	- VIGAS (Nv. +380)		ARQUIVO

Aprovações: