


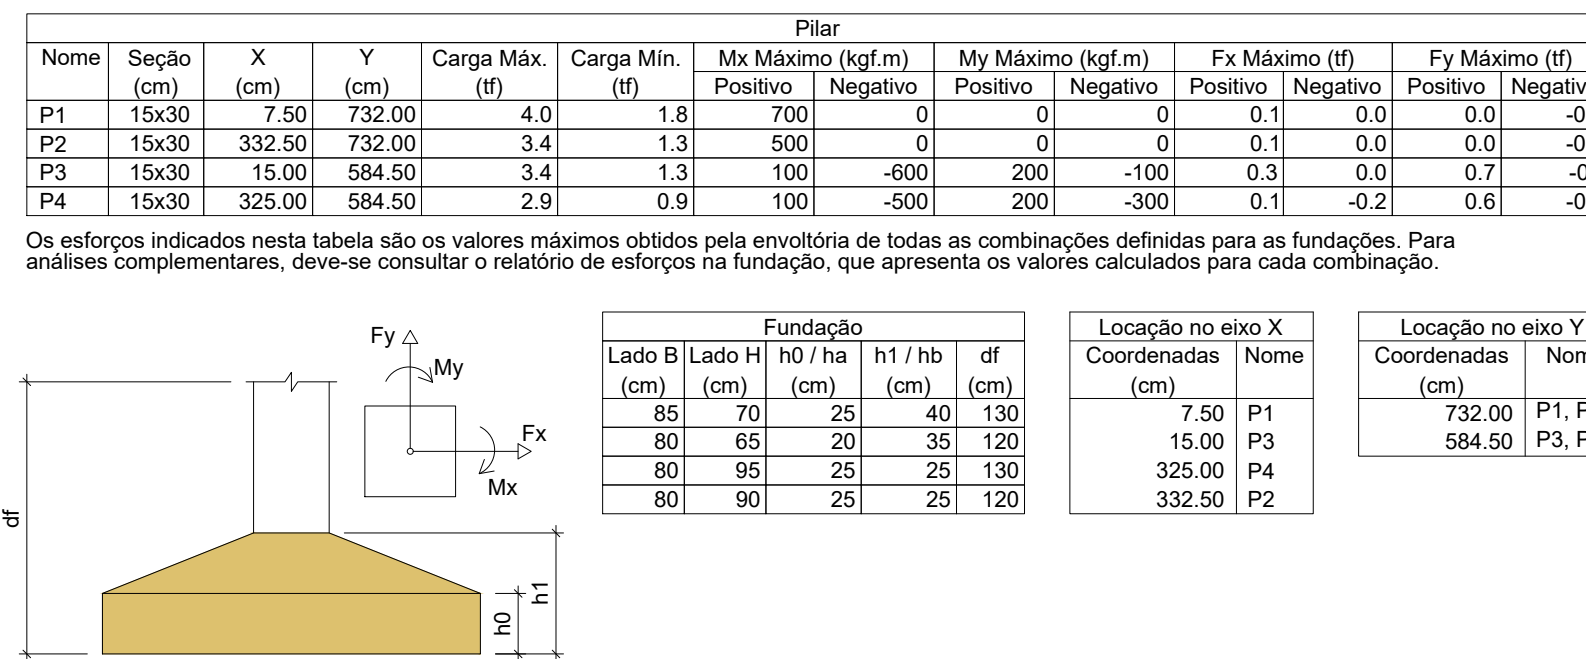

Technical drawing of a rectangular frame structure, showing dimensions and labels for components and sections.

Dimensions:

- Overall width: 340
- Overall height: 325.00
- Inner width: 310
- Inner height: 732.00
- Section A-A height: 147.5
- Section B-B height: 584.50
- Section A-A width: 280
- Section B-B width: 317.5

Labels and Components:

- P1, P2, P3, P4:** Labels for the four corner joints.
- VB1, VB2, VB3, VB4:** Labels for the four vertical beams.
- 15x30:** Label for the corner joints.
- 115x30:** Label for the top horizontal beam.
- 15x30:** Label for the bottom horizontal beam.

Section Lines:

- A-A:** Section line through the top horizontal beam and corner joints.
- B-B:** Section line through the bottom horizontal beam and corner joints.

Technical drawing of a rectangular slab with dimensions and reinforcement details. The overall dimensions are 340 (width) by 170 (height). The slab is reinforced with 15x30 bars. The reinforcement layout includes:

- Top bars: VS1 15x30 (left), VS2 15x30 (right), and VS3 15x30 (bottom).
- Bottom bars: VS4 15x30 (left), VS5 15x30 (right), and VS6 15x30 (top).
- Central circular hole: L1 with diameter $\phi=8$.
- Dimensions: The slab has a central rectangular area of 280x140. The distance from the center to the edges is 30 (left and right) and 15 (top and bottom). The total width is 340 and the total height is 170.
- Reinforcement labels: P1, P2, P3, P4, VS1, VS2, VS3, VS4, VS5, VS6.
- Load: 960 kgf/m².

Lajes					Sobrecarga (kgf/m²)		
Dados					Adicional	Acidental	Localizada
Nome	Tipo	Altura (cm)	Nível (cm)	Peso próprio (kgf/m²)			
L1	Maciça	8	0	380	200	100	50 sim

Área de lajes			
Tipo	Altura (cm)	Bloco de Enchimento	Área (m²)
Maciça	8	-	4.34

Vigas			
Nome	Seção (cm)	Elevação (cm)	Nível (cm)
VS1	15x30	0	38
VS2	15x30	0	38
VS3	15x30	0	38
VS4	15x30	0	38

Pilares			
Nome	Seção (cm)	Elevação (cm)	Nível (cm)
P1	15x30	0	380
P2	15x30	0	380
P3	15x30	0	380
P4	15x30	0	380

Características dos materiais	
fck (kgf/cm²)	Ecs (kgf/cm²)
250	241500

Legenda dos pilares	
	Pilar que morre

Legenda das vigas e paredes	
	Viga