



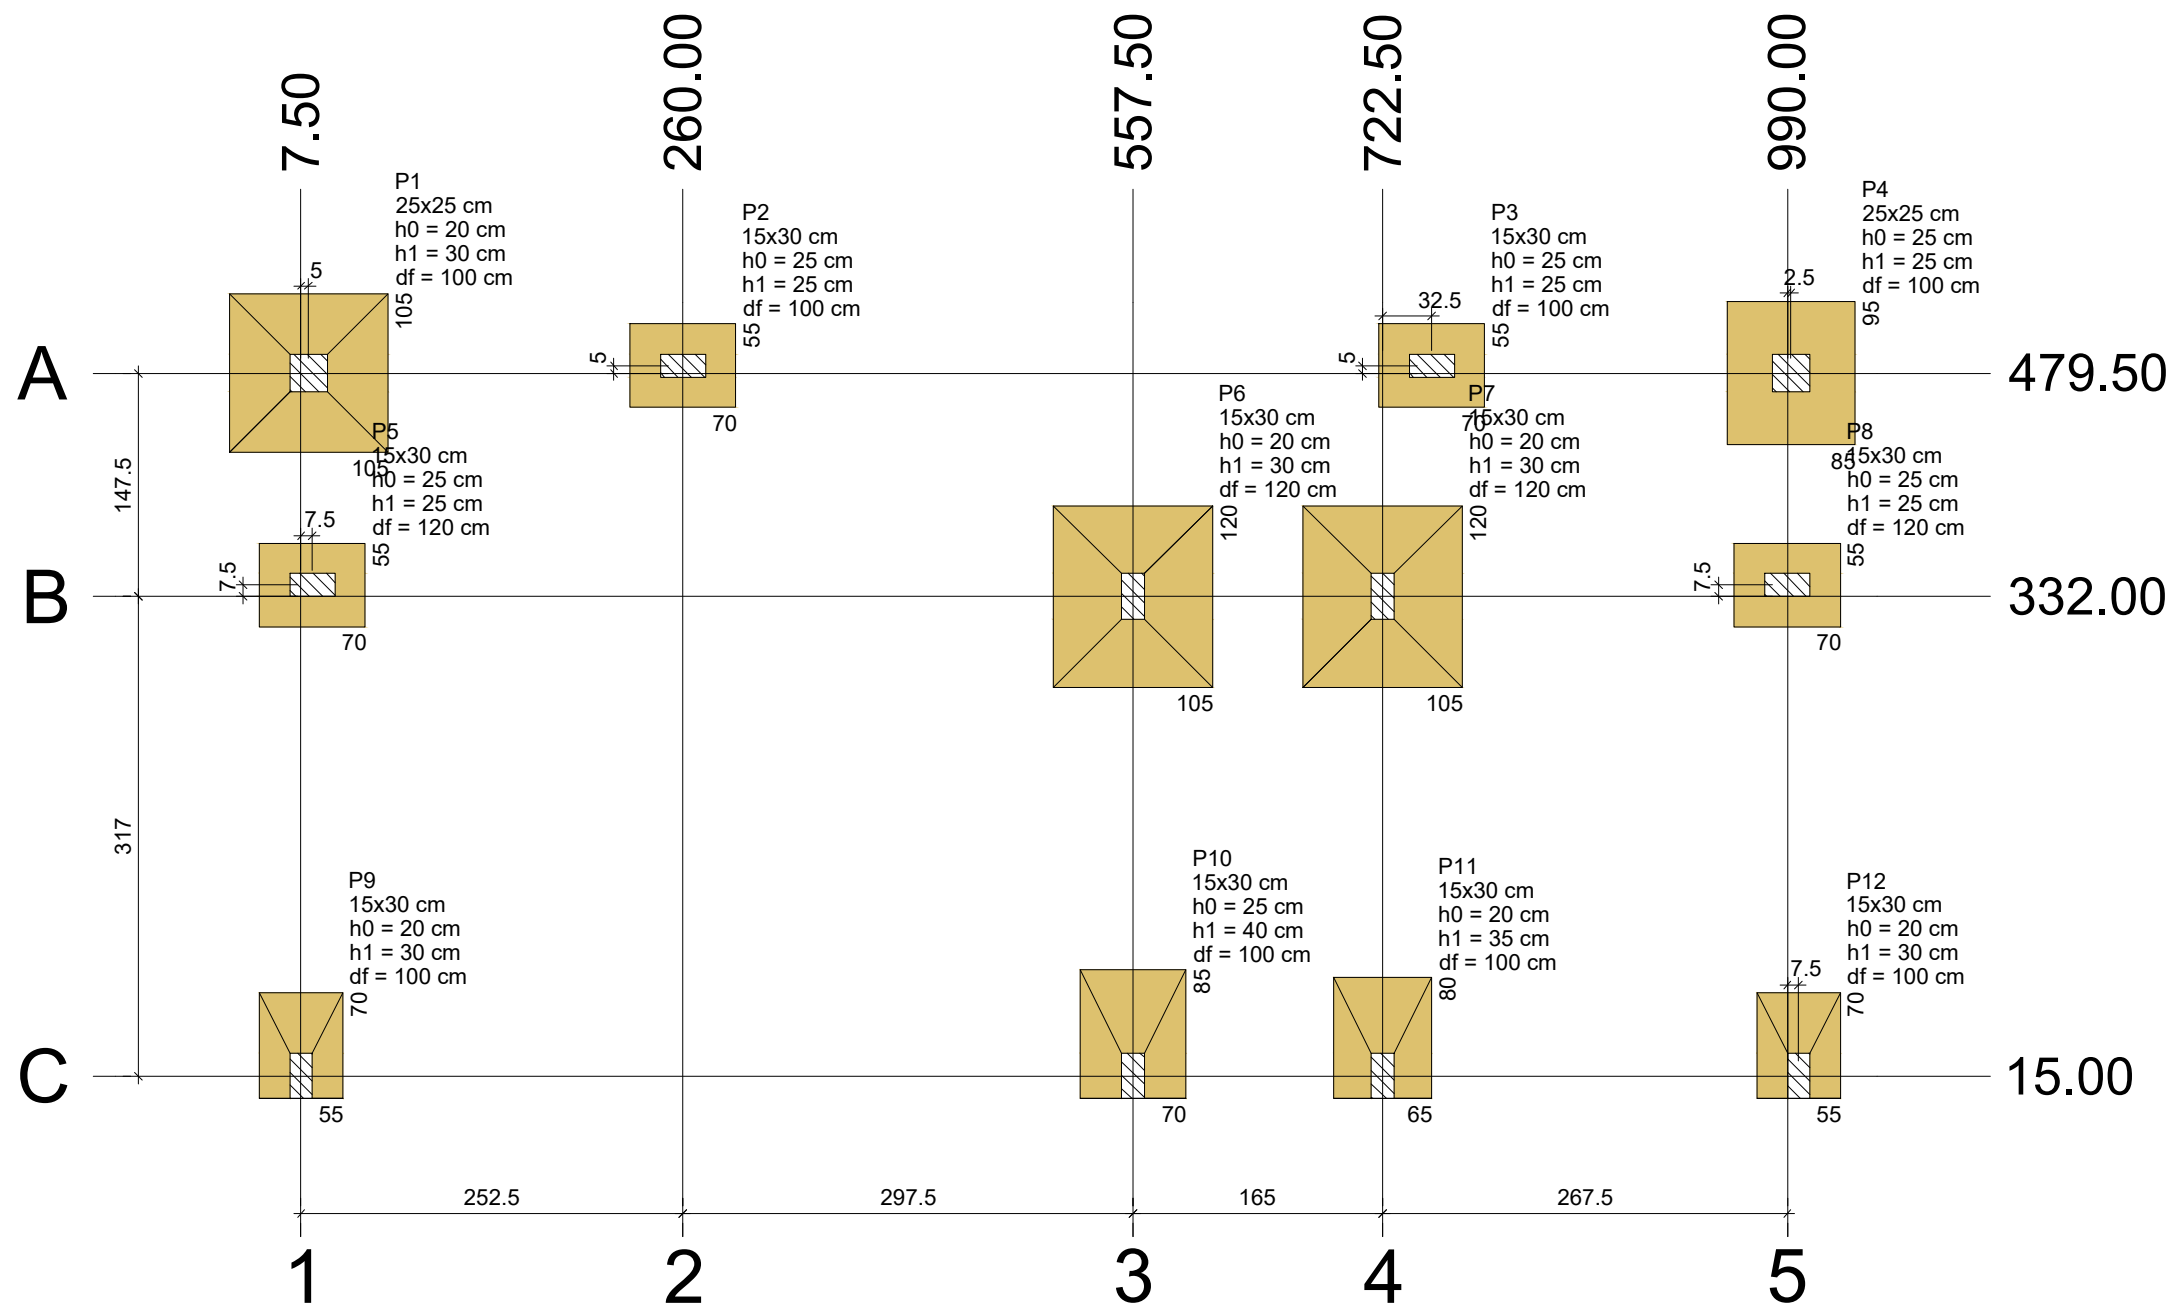

Planta de localização
escala 1:50

Pilar													
Nome	Seção (cm)	X (cm)	Y (cm)	Carga Máx. (tf)	Carga Mín. (tf)	Mx Máximo (kgf.m)		My Máximo (kgf.m)		Fx Máximo (tf)		Fy Máximo (tf)	
						Positivo	Negativo	Positivo	Negativo	Positivo	Negativo	Positivo	Negativo
P1	25x25	12.50	479.50	3.3	1.7	700	-400	100	-200	0.0	-0.3	0.4	-0.5
P2	15x30	260.00	484.50	3.0	2.7	200	-300	300	-200	0.4	0.0	0.1	-0.2
P3	15x30	755.00	484.50	3.0	2.6	200	-300	100	-200	0.0	-0.4	0.1	-0.2
P4	25x25	992.50	479.50	3.3	1.7	600	-700	300	-200	0.3	0.0	0.5	-0.4
P6	15x30	557.50	332.00	4.9	2.9	1300	-300	100	-200	0.0	-0.3	0.0	-1.3
P7	15x30	722.50	332.00	4.5	2.6	1200	-300	200	0	0.2	0.0	0.2	-1.0
P8	15x30	990.00	339.50	2.7	1.4	300	-300	200	-300	0.1	-0.1	0.3	-0.3
P9	15x30	7.50	15.00	2.7	2.3	0	-400	0	0	0.0	-0.1	0.4	0.0
P10	15x30	557.50	15.00	5.6	3.6	0	-1000	0	0	0.2	0.0	1.0	0.0
P11	15x30	722.50	15.00	4.7	2.7	0	-800	0	0	0.1	-0.1	0.8	0.0
P12	15x30	997.50	15.00	2.3	1.8	0	0	0	0	0.1	0.0	0.2	-0.3
P5	15x30	15.00	339.50	2.8	1.6	300	-100	200	-300	0.2	-0.2	0.2	-0.5


Os esforços indicados nesta tabela são os valores máximos obtidos pela envoltória de todas as combinações definidas para as fundações. Para análises complementares, deve-se consultar o relatório de esforços na fundação, que apresenta os valores calculados para cada combinação.

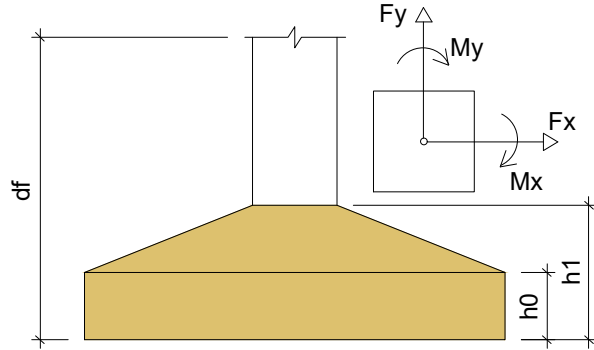

Fundação				
Lado B (cm)	Lado H (cm)	h0 / ha (cm)	h1 / hb (cm)	df (cm)
105	105	20	30	100
55	70	25	25	100
55	70	25	25	100
95	85	25	25	100
105	120	20	30	120
105	120	20	30	120
55	70	25	25	120
70	55	20	30	100
85	70	25	40	100
80	65	20	35	100
70	55	20	30	100
55	70	25	25	120

Locação no eixo X	
Coordenadas (cm)	Nome
7.50	P9
12.50	P1
15.00	P5
260.00	P2
557.50	P6, P10
722.50	P7, P11
755.00	P3
990.00	P8
992.50	P4
997.50	P12

Locação no eixo Y	
Coordenadas (cm)	Nome
484.50	P2, P3
479.50	P1, P4
339.50	P5, P8
332.00	P6, P7
15.00	P9, P10, P11, P12

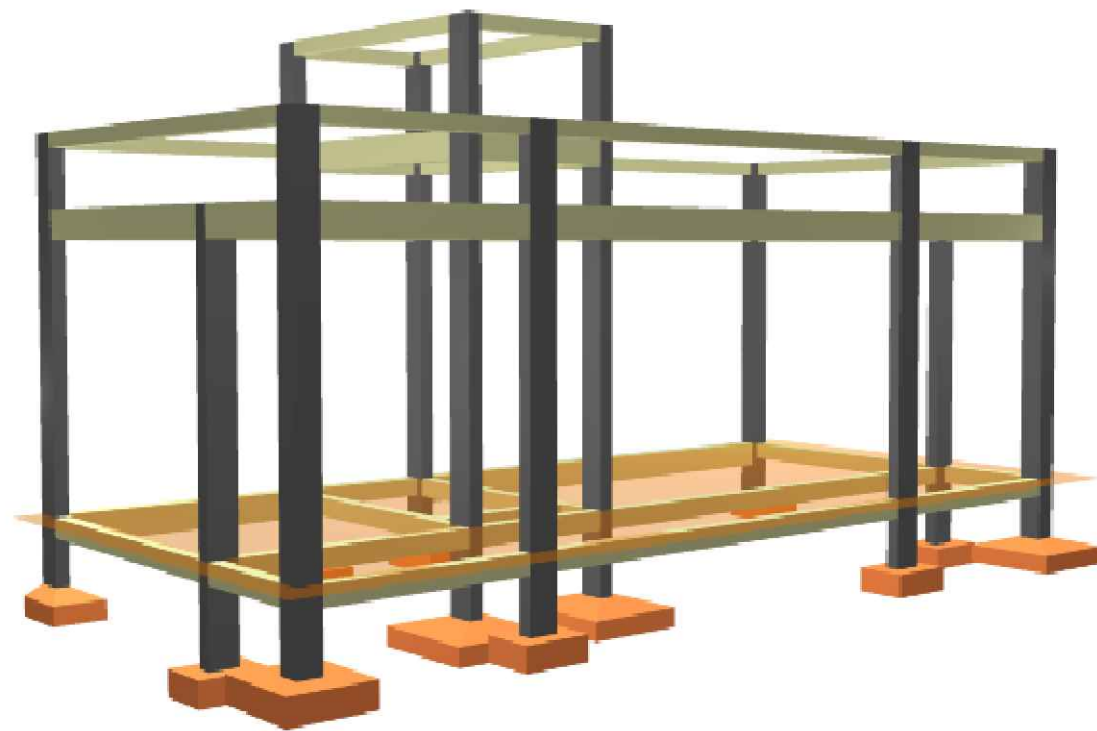


PROPRIETÁRIO: PREFEITURA MUNICIPAL DE COREMAS- PB

LINCOLN CARTAXO DE LIRA JÚNIOR:06897861405
Assinado de forma digital por LINCOLN CARTAXO DE LIRA JÚNIOR:06897861405
Dados: 2025.07.14 11:26:54 -03'00'

PROJETO: LINCOLN CARTAXO DE LIRA JÚNIOR CREA 160.814.689-8

FOLHA	PROJETO: GARAGEM COREMAS (ESTRUTURAL ANEXO I)			
01/09	CONVENIENTE: PREFEITURA MUNICIPAL DE COREMAS-PB CONCIDENTE: PREFEITURA MUNICIPAL DE COREMAS-PB LOCALIDADE: COREMAS- PB			
DESENHO	DATA	RESPONSÁVEL	RUBRICA	DADOS
CÓPIA	JUN/2025	LINCOLN CARTAXO		
VISTO				
ESCALAS	DESENHOS			CONVÊNIO
INDICADO	- PLANTA DE LOCAÇÃO			ARQUIVO

Aprovações:

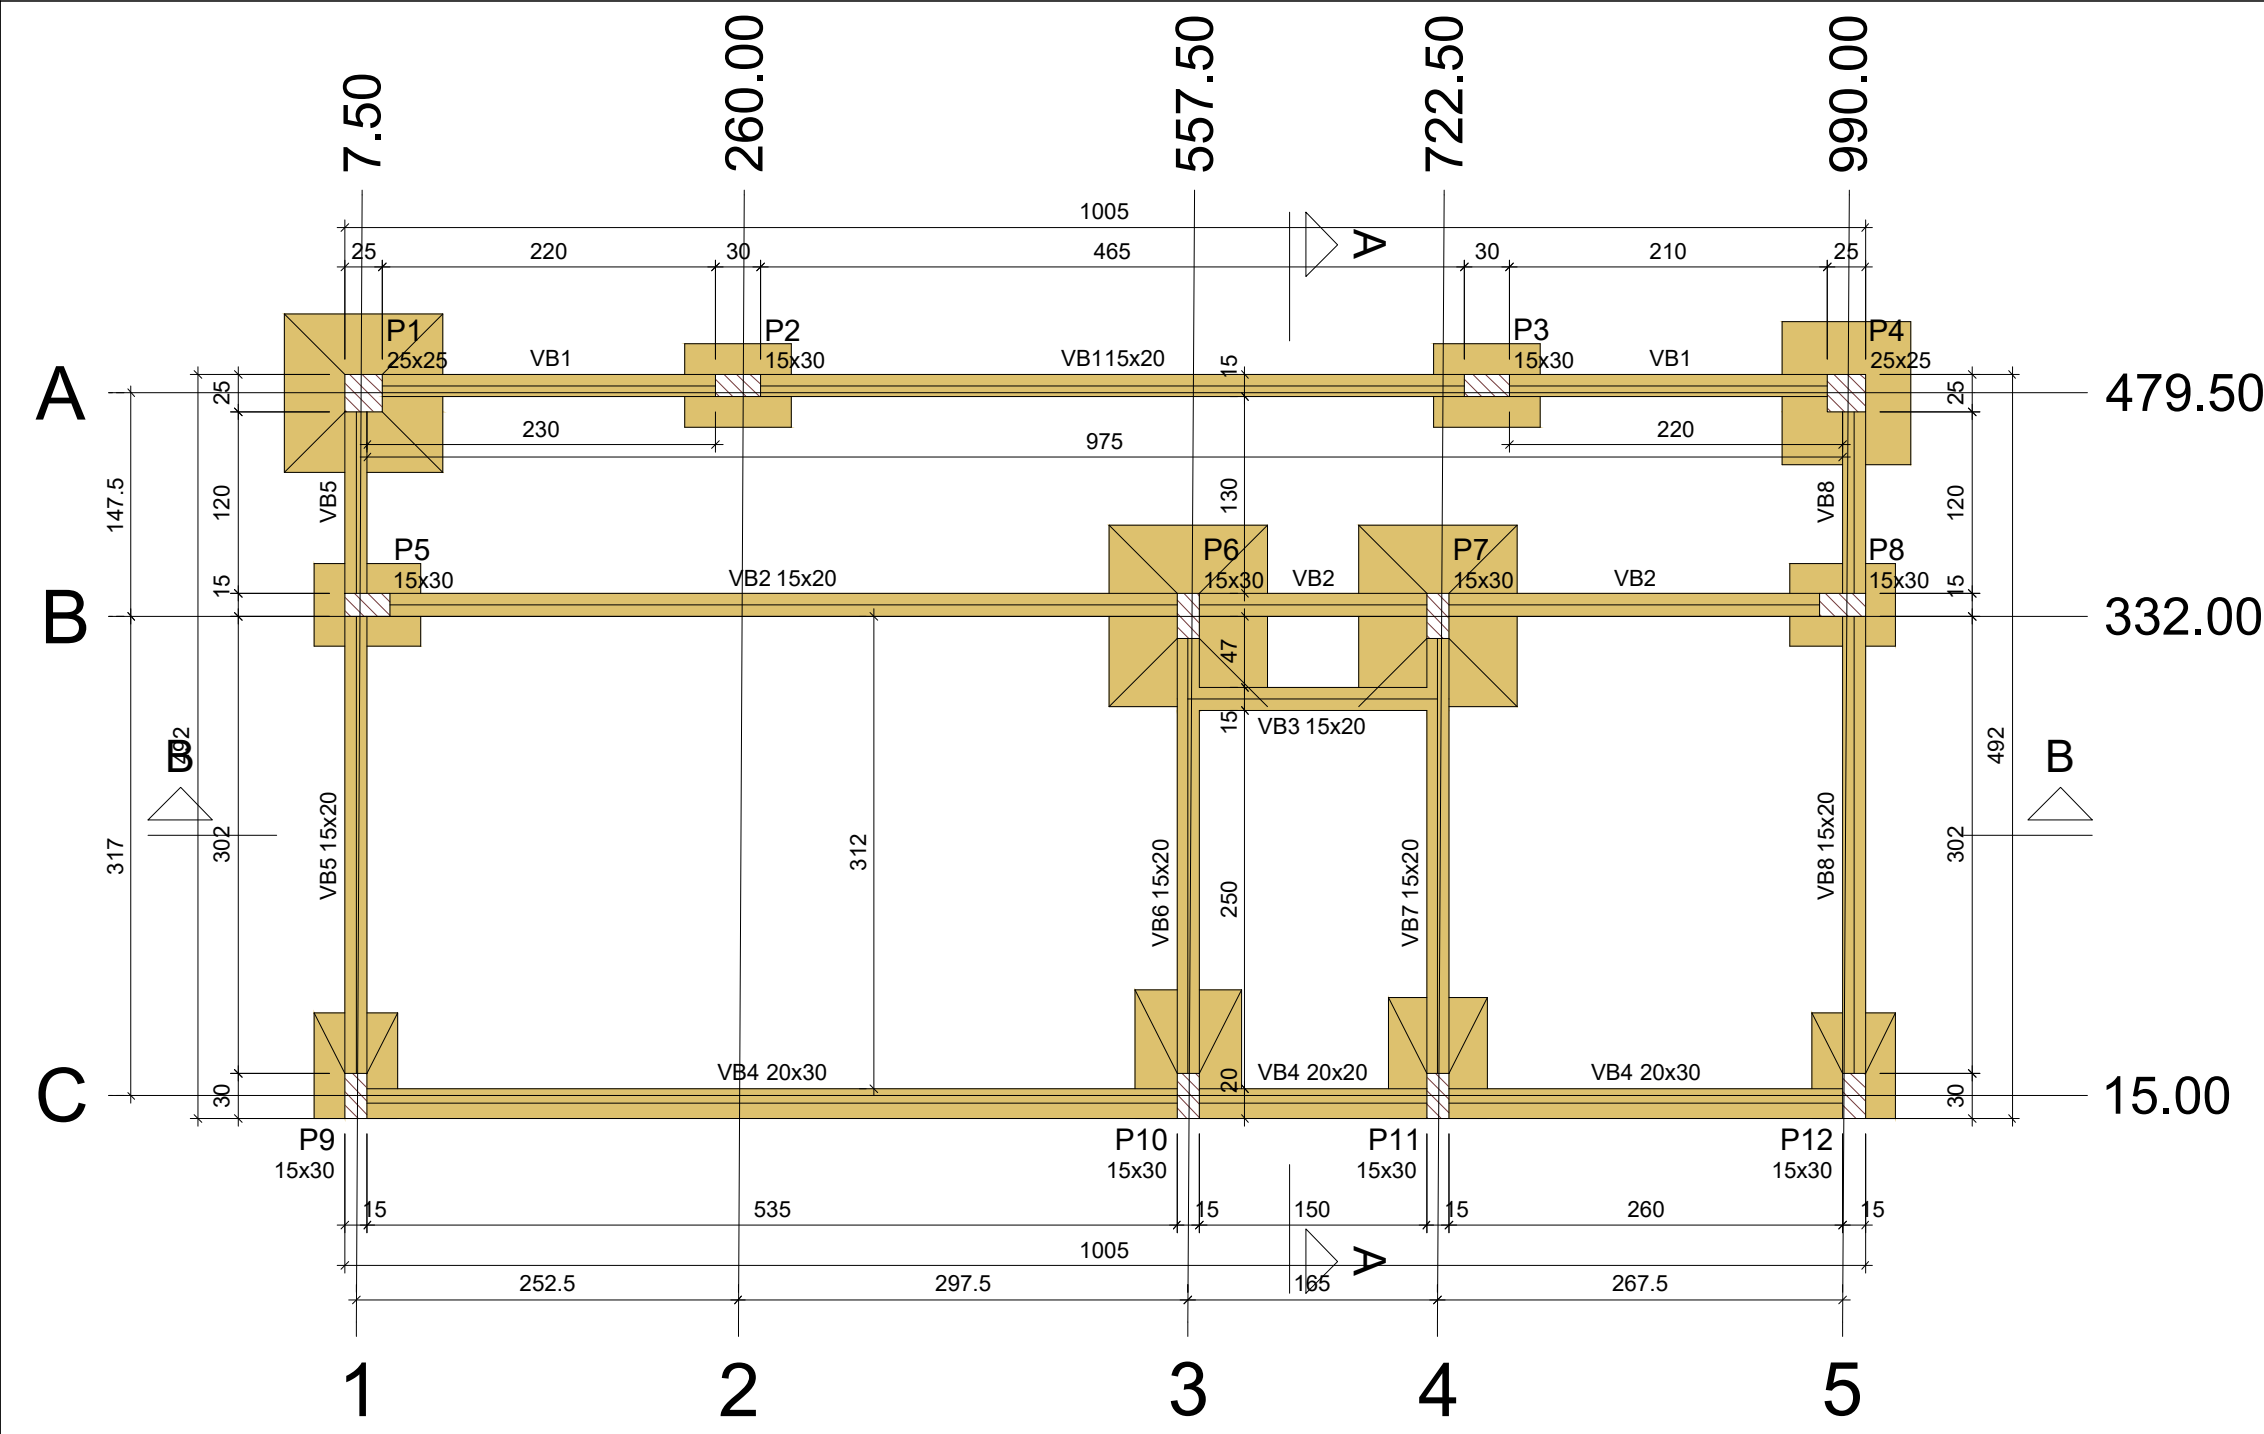

Forma do pavimento +0 (Nível 0)
escala 1:50


Vigas			
Nome	Seção (cm)	Elevação (cm)	Nível (cm)
VB1	15x20	0	0
VB2	15x20	0	0
VB3	15x20	0	0
VB4	20x30	0	0
	20x20	0	0
	20x30	0	0
VB5	15x20	0	0
VB6	15x20	0	0
VB7	15x20	0	0
VB8	15x20	0	0

Características dos materiais	
fck (kgf/cm²)	Ecs (kgf/cm²)
250	241500

Legenda dos pilares	
	Pilar que passa
	Pilar com mudança de seção

Legenda das vigas e paredes	
	Viga

Pilares			
Nome	Seção (cm)	Elevação (cm)	Nível (cm)
P1	25x25	0	0
P2	15x30	0	0
P3	15x30	0	0
P4	25x25	0	0
P6	15x30	0	0
P7	15x30	0	0
P8	15x30	0	0
P9	15x30	0	0
P10	15x30	0	0
P11	15x30	0	0
P12	15x30	0	0
P5	15x30	0	0

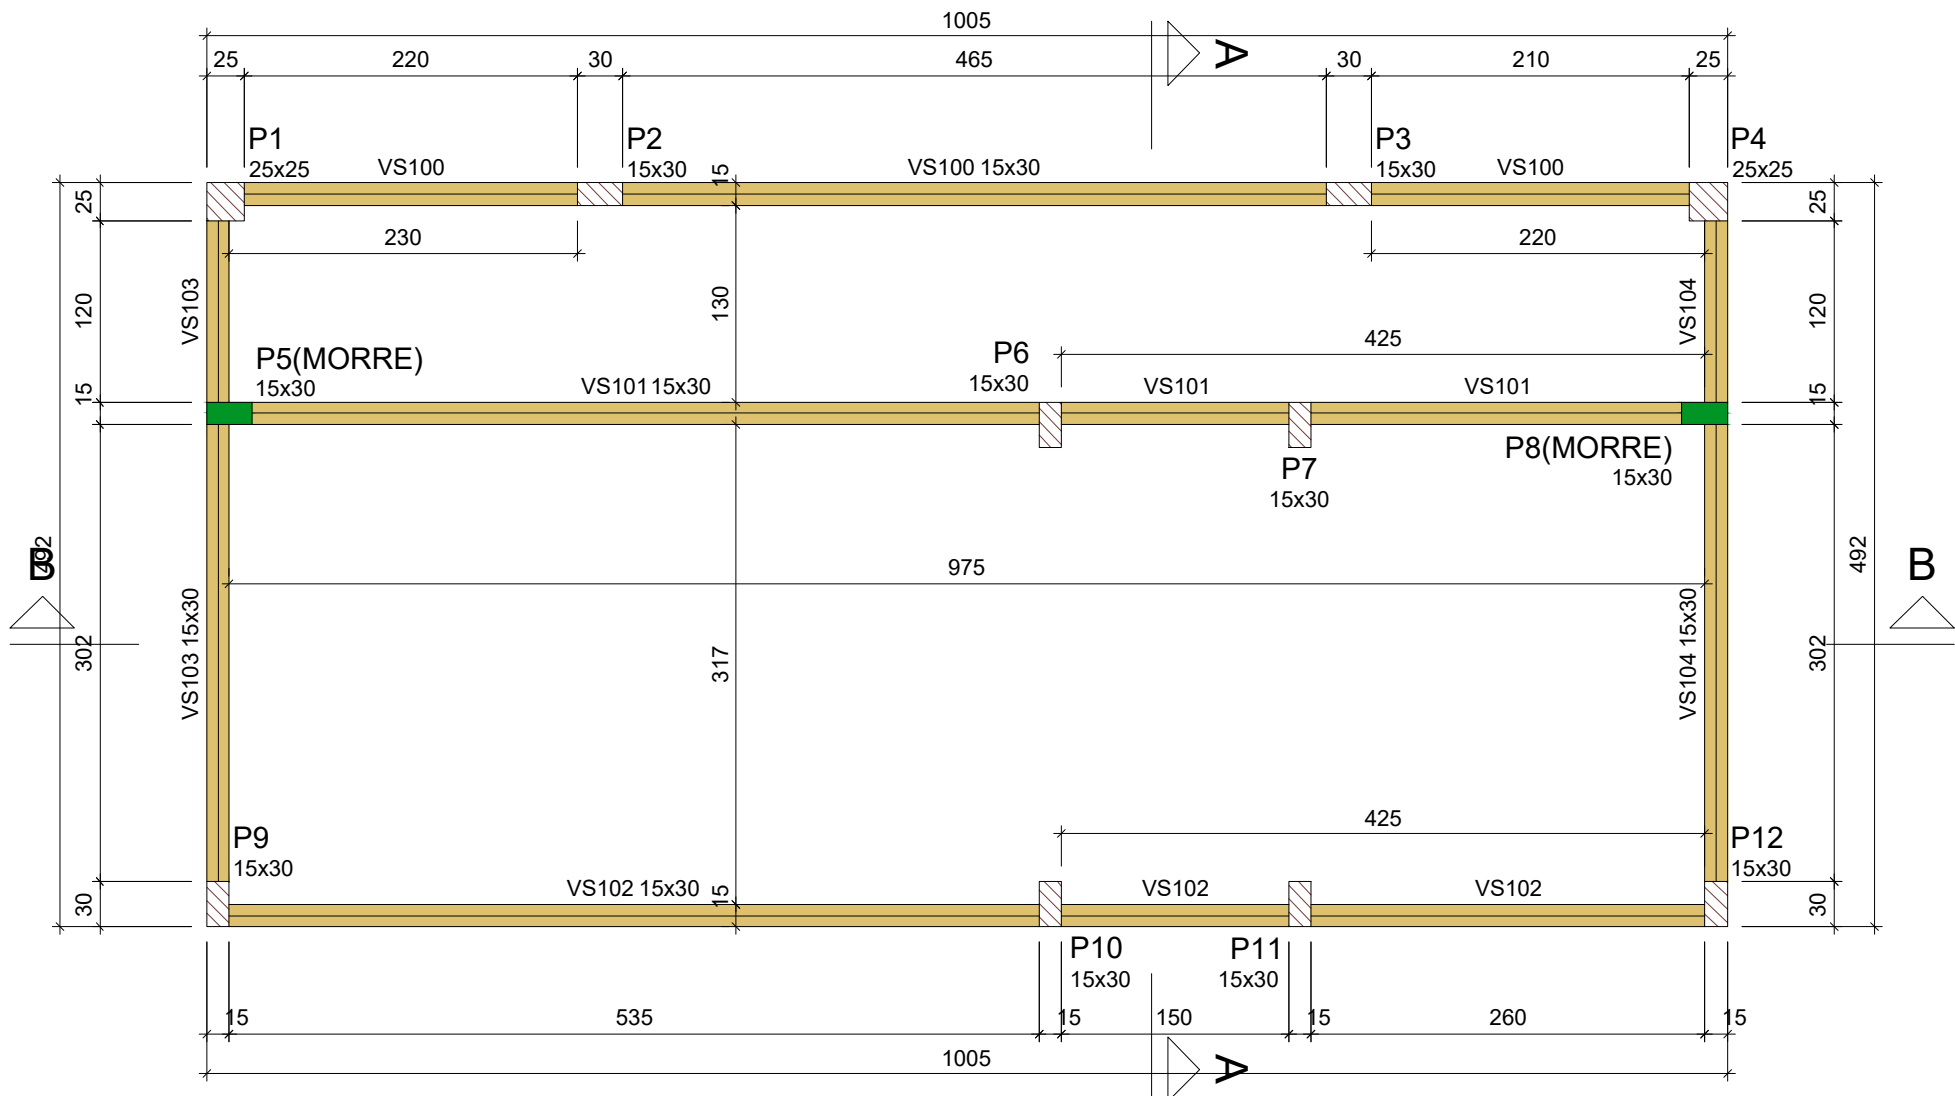

Forma do pavimento +305 (Nível 305)
escala 1:50


Vigas			
Nome	Seção (cm)	Elevação (cm)	Nível (cm)
VS100	15x30	0	305
VS101	15x30	0	305
VS102	15x30	0	305
VS103	15x30	0	305
VS104	15x30	0	305

Características dos materiais	
fck (kgf/cm²)	Ecs (kgf/cm²)
250	241500

Legenda das vigas e paredes	
	Viga

Pilares			
Nome	Seção (cm)	Elevação (cm)	Nível (cm)
P1	25x25	0	305
P2	15x30	0	305
P3	15x30	0	305
P4	25x25	0	305
P6	15x30	0	305
P7	15x30	0	305
P8	15x30	0	305
P9	15x30	0	305
P10	15x30	0	305
P11	15x30	0	305
P12	15x30	0	305
P5	15x30	0	305

Legenda dos pilares	
	Pilar que morre
	Pilar que passa

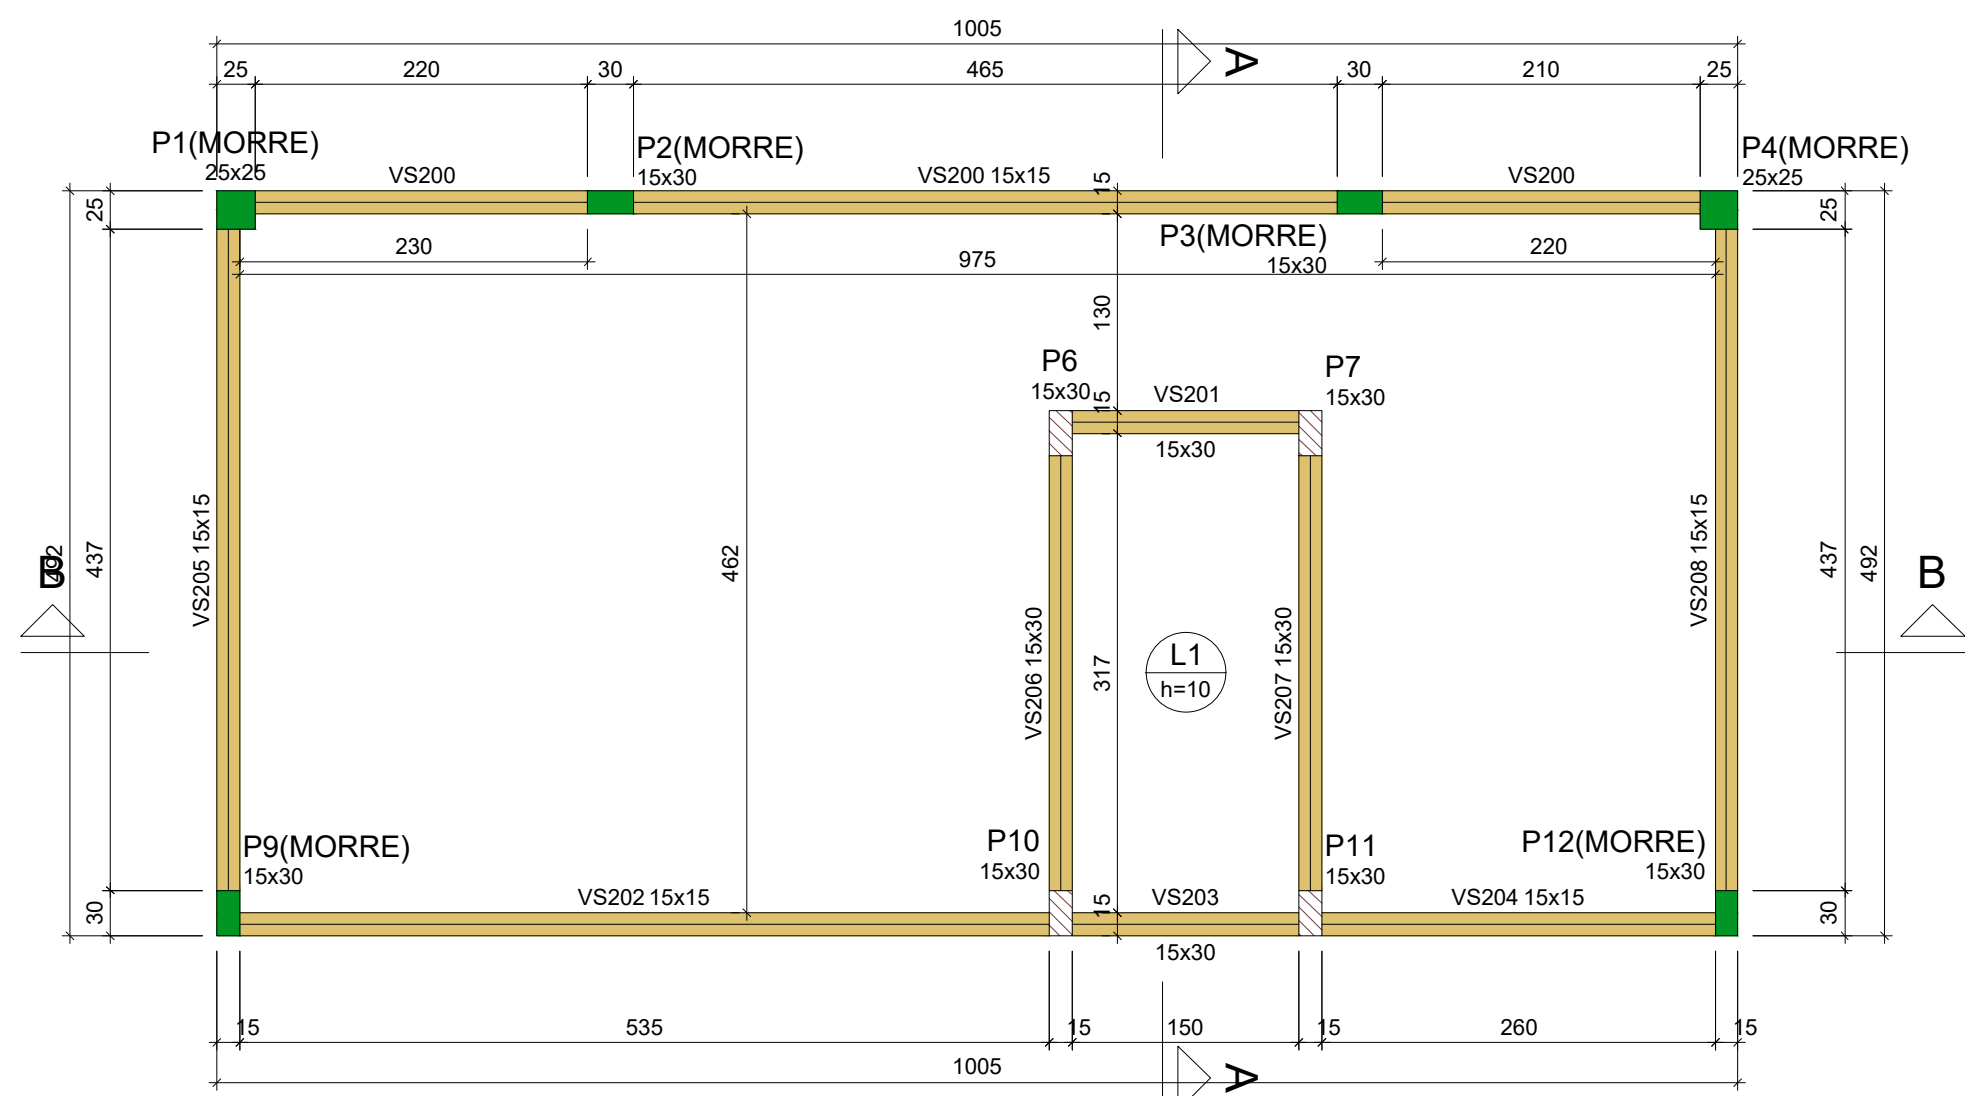

Forma do pavimento +380 (Nível 380)
escala 1:50

Lajes								
Dados					Sobrecarga (kgf/m²)			
Nome	Tipo	Altura (cm)	Elevação (cm)	Nível (cm)	Peso próprio (kgf/m²)	Adicional	Acidental	Água
L1	Maciça	10	0	380	250	100	50	950

Área de lajes			
Tipo	Altura (cm)	Bloco de Enchimento	Área (m²)
Maciça	10	-	4.75

Vigas			
Nome	Seção (cm)	Elevação (cm)	Nível (cm)
VS200	15x15	0	380
VS201	15x30	0	380
VS202	15x15	0	380
VS203	15x30	0	380
VS204	15x15	0	380
VS205	15x15	0	380
VS206	15x30	0	380
VS207	15x30	0	380
VS208	15x15	0	380

Legenda dos pilares	
	Pilar que morre
	Pilar que passa

Legenda das vigas e paredes	
	Viga

Características dos materiais	
fck (kgf/cm²)	Ecs (kgf/cm²)
250	241500


Pilares			
Nome	Seção (cm)	Elevação (cm)	Nível (cm)
P1	25x25	0	380
P2	15x30	0	380
P3	15x30	0	380
P4	25x25	0	380
P6	15x30	0	380
P7	15x30	0	380
P9	15x30	0	380
P10	15x30	0	380
P11	15x30	0	380
P12	15x30	0	380

PROPRIETÁRIO: PREFEITURA MUNICIPAL DE COREMAS- PB	
LINCOLN CARTAXO DE LIRA JUNIOR:06897861405	Assinado de forma digital por LINCOLN CARTAXO DE LIRA JUNIOR:06897861405 Dados: 2025.07.14 11:26:34 -03'00'
PROJETO: LINCOLN CARTAXO DE LIRA JÚNIOR CREA 160.814.689-8	

FOLHA	PROJETO: GARAGEM COREMAS (ESTRUTURAL ANEXO I)
02/09	CONVENIENTE: PREFEITURA MUNICIPAL DE COREMAS-PB
	CONCENDENTE: PREFEITURA MUNICIPAL DE COREMAS-PB
	LOCALIDADE: COREMAS- PB

DESENHO	DATA	RESPONSÁVEL	RUBRICA	DADOS
CÓPIA	JUN/2025	LINCOLN CARTAXO		
VISTO				
ESCALAS	DESENHOS			CONVÊNIO
INDICADO	- PLANTA DE FORMAS -- Pav. +0; -- Pav. +305; -- Pav. +380.			ARQUIVO

Aprovações:

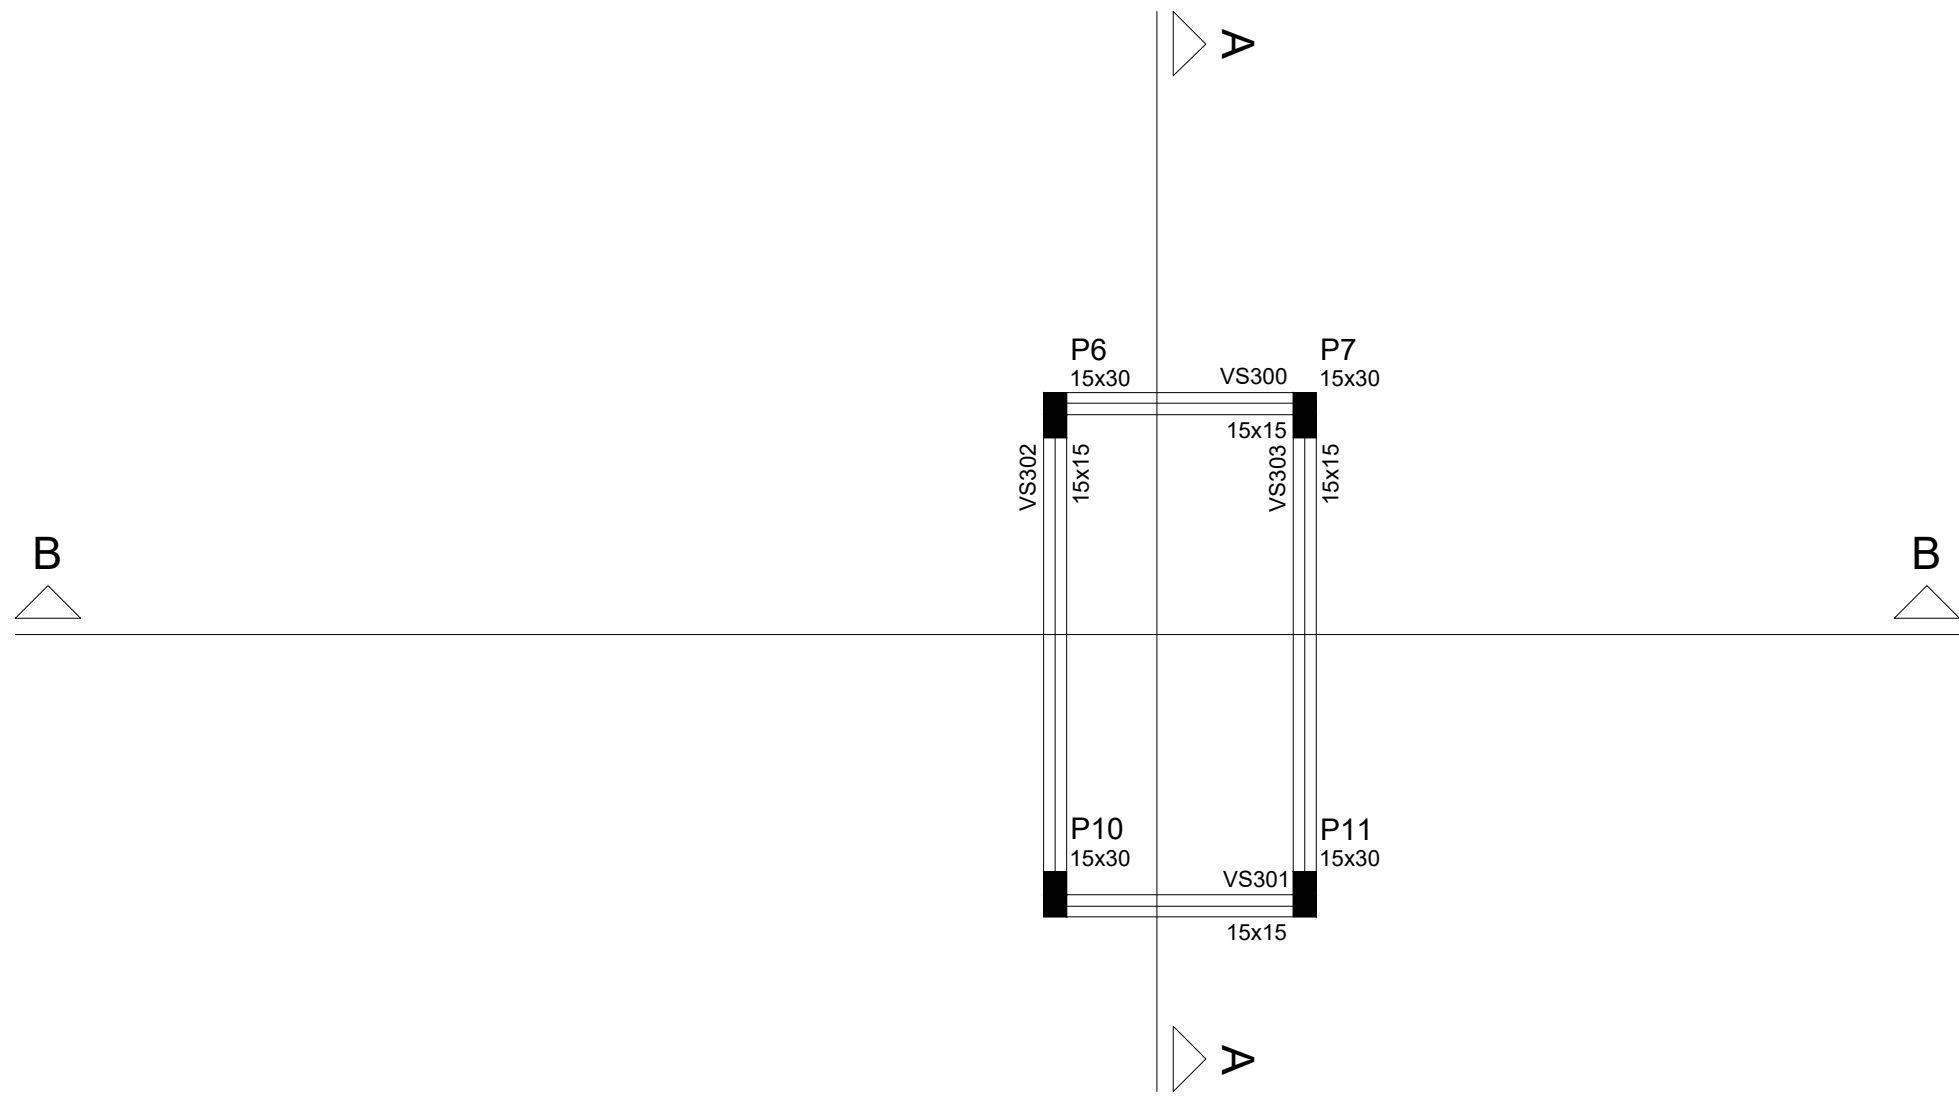


Forma do pavimento +490
escala 1:50

Vigas			
Nome	Seção (cm)	Elevação (cm)	Nível (cm)
VS300	15x15	0	490
VS301	15x15	0	490
VS302	15x15	0	490
VS303	15x15	0	490



Características dos materiais	
fck (kgf/cm²)	Ecs (kgf/cm²)
250	238000

Pilares			
Nome	Seção (cm)	Elevação (cm)	Nível (cm)
P6	15 x 30	0	490
P7	15 x 30	0	490
P10	15 x 30	0	490
P11	15 x 30	0	490


Legenda dos Pilares	
	Pilar que morre
	Pilar que passa
	Pilar que nasce
	Pilar com mudança de seção

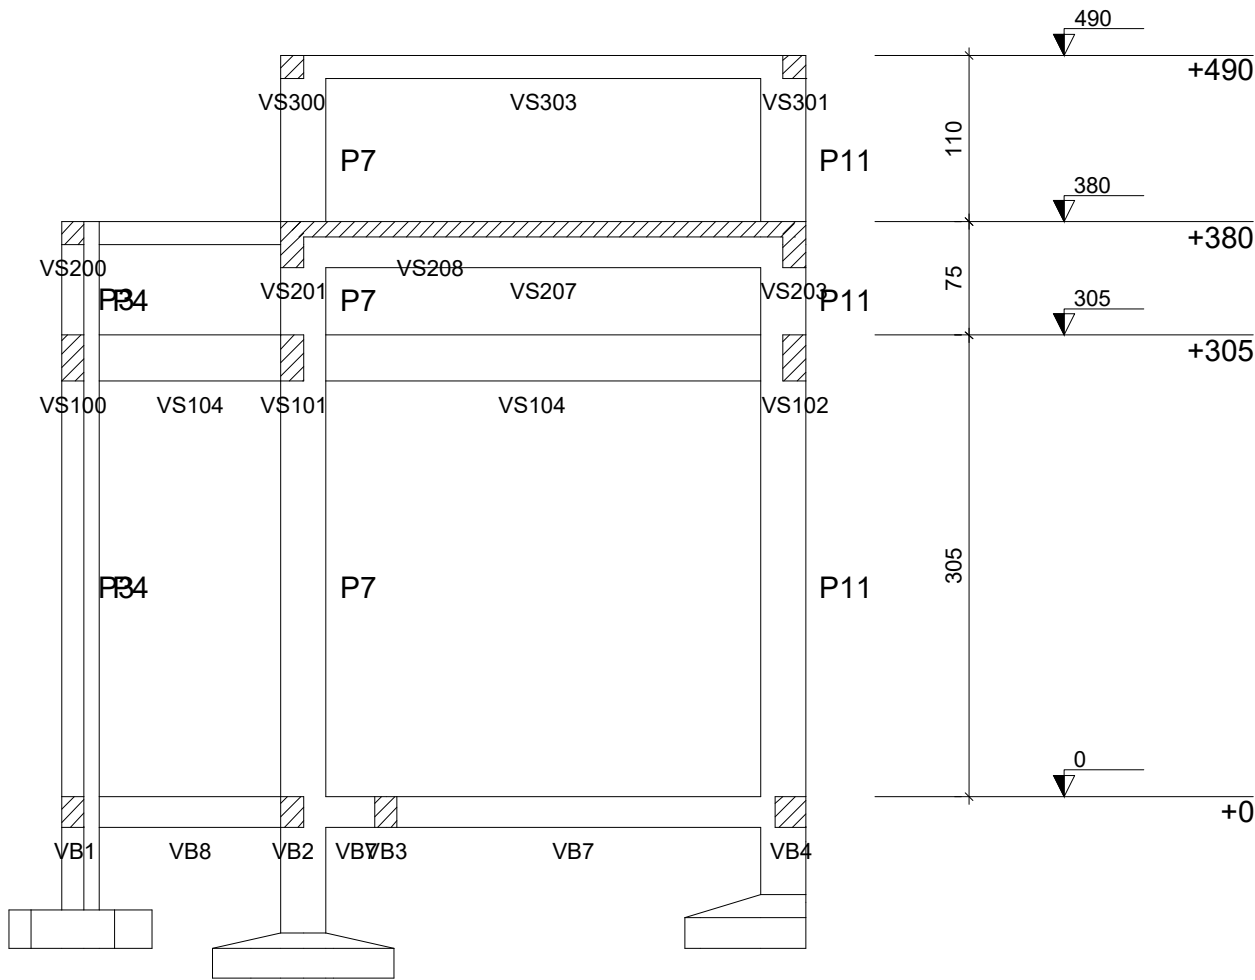

Corte A-A
escala 1:50

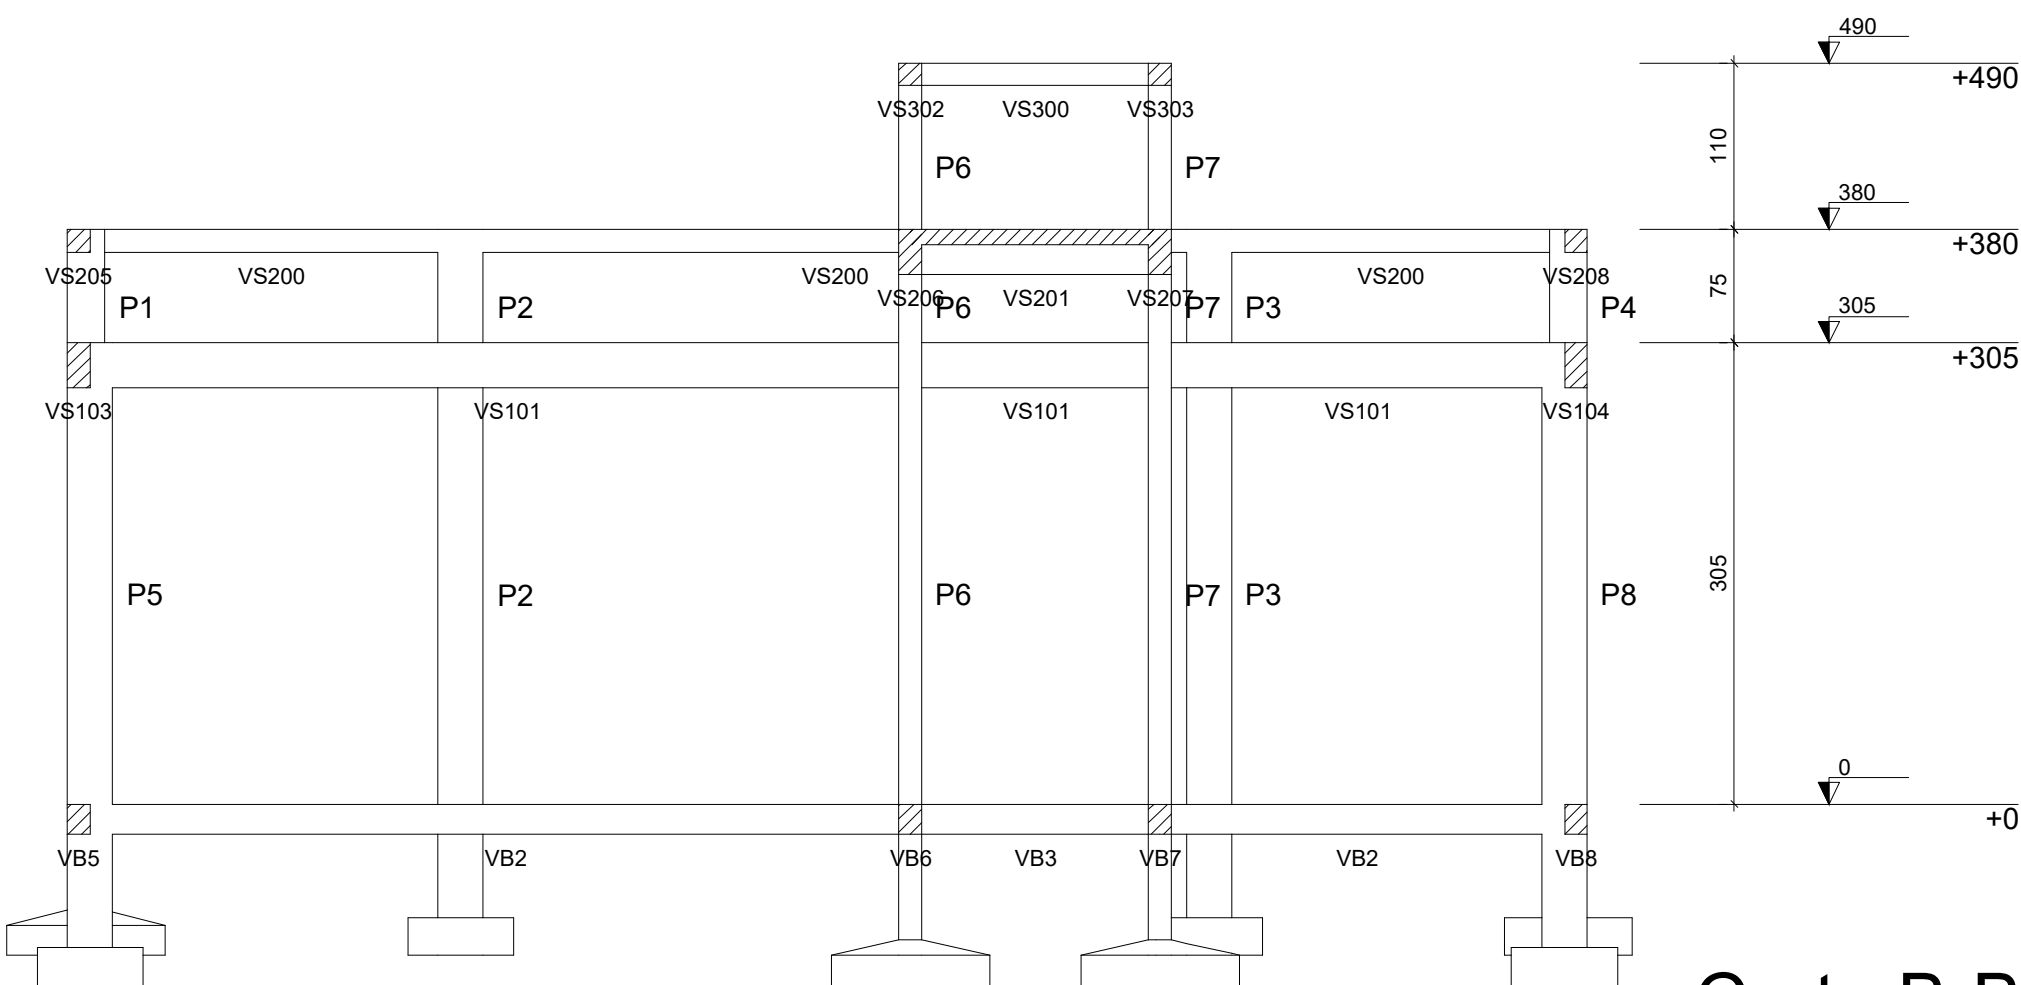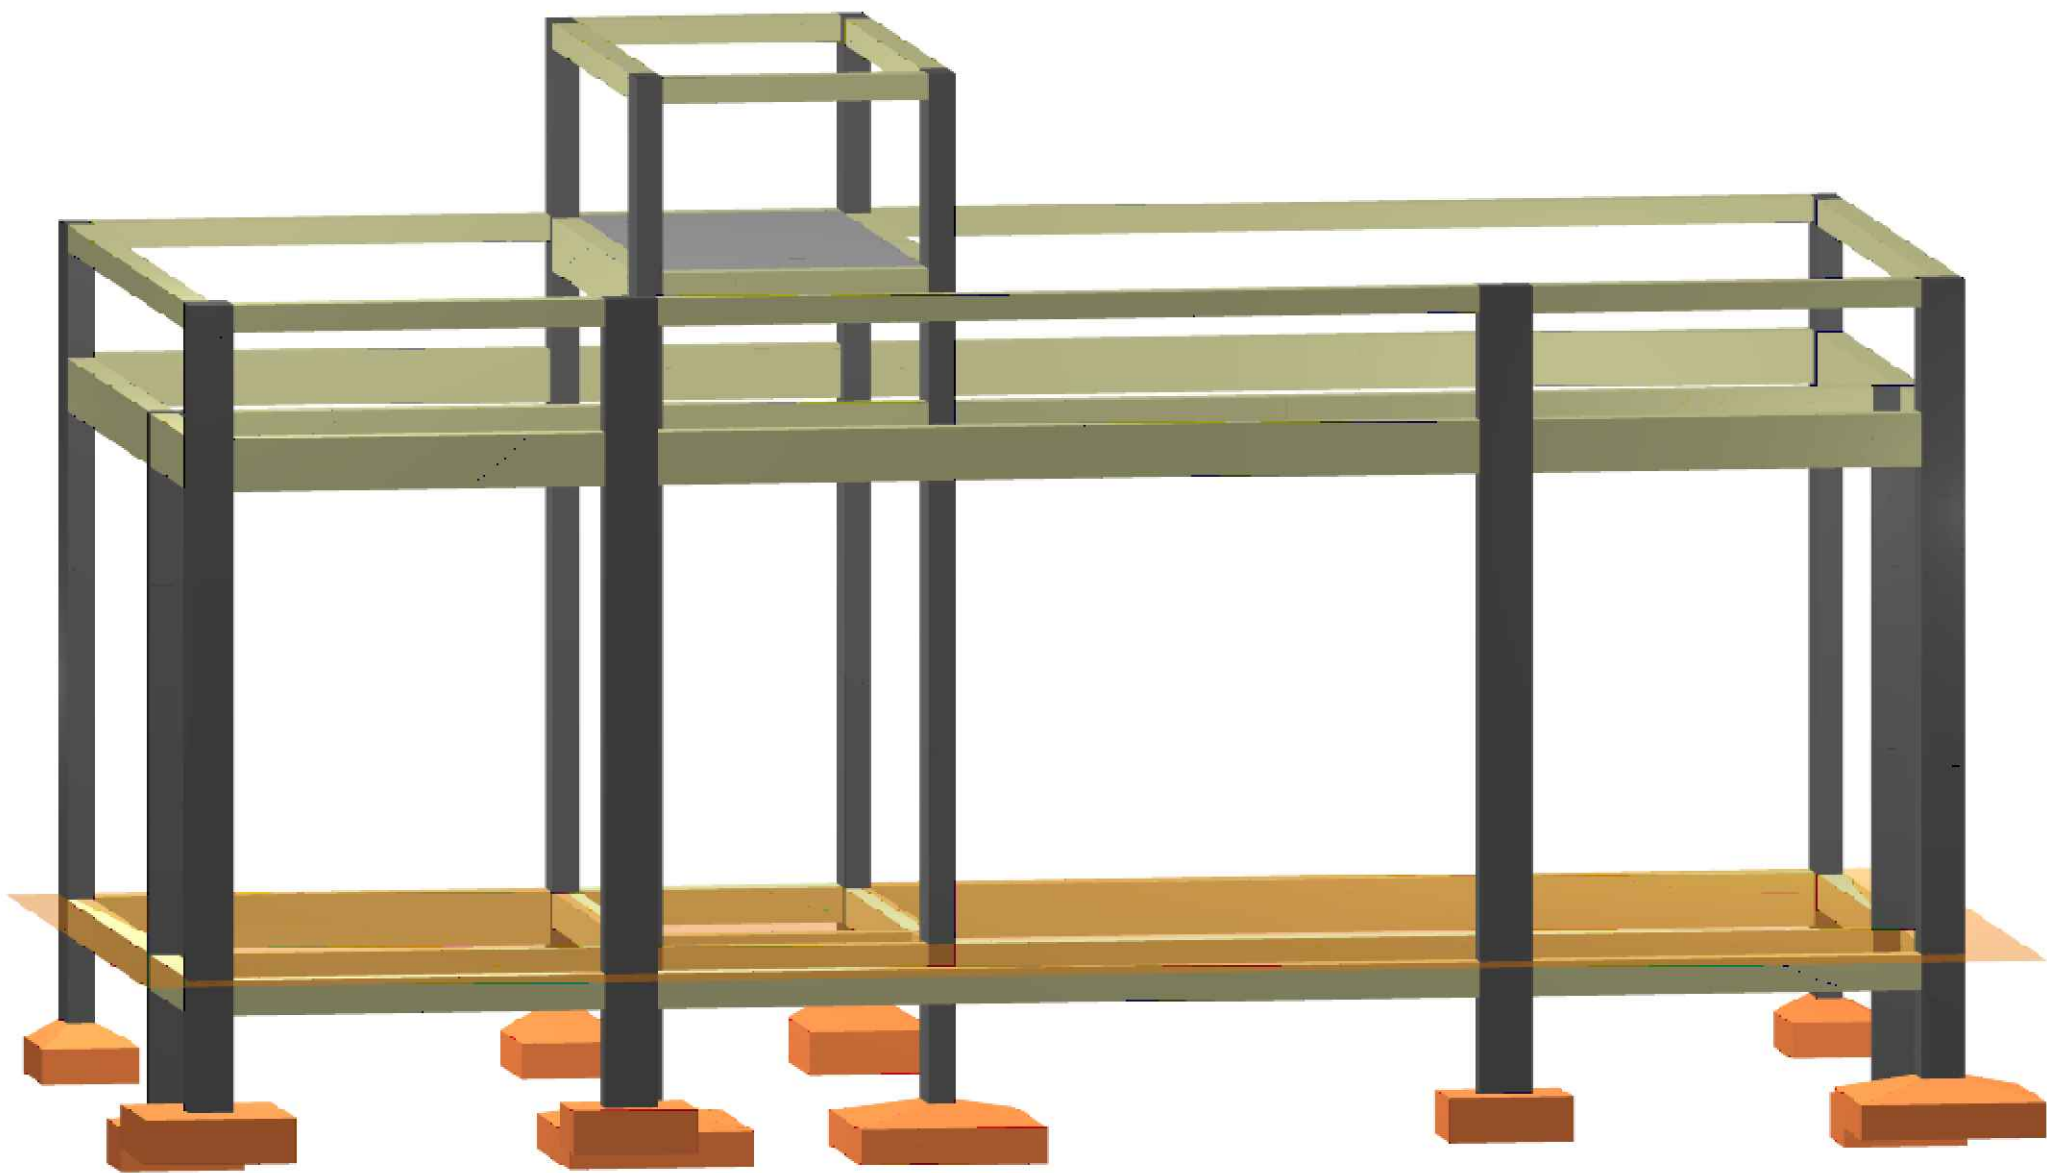

Corte B-B
escala 1:50


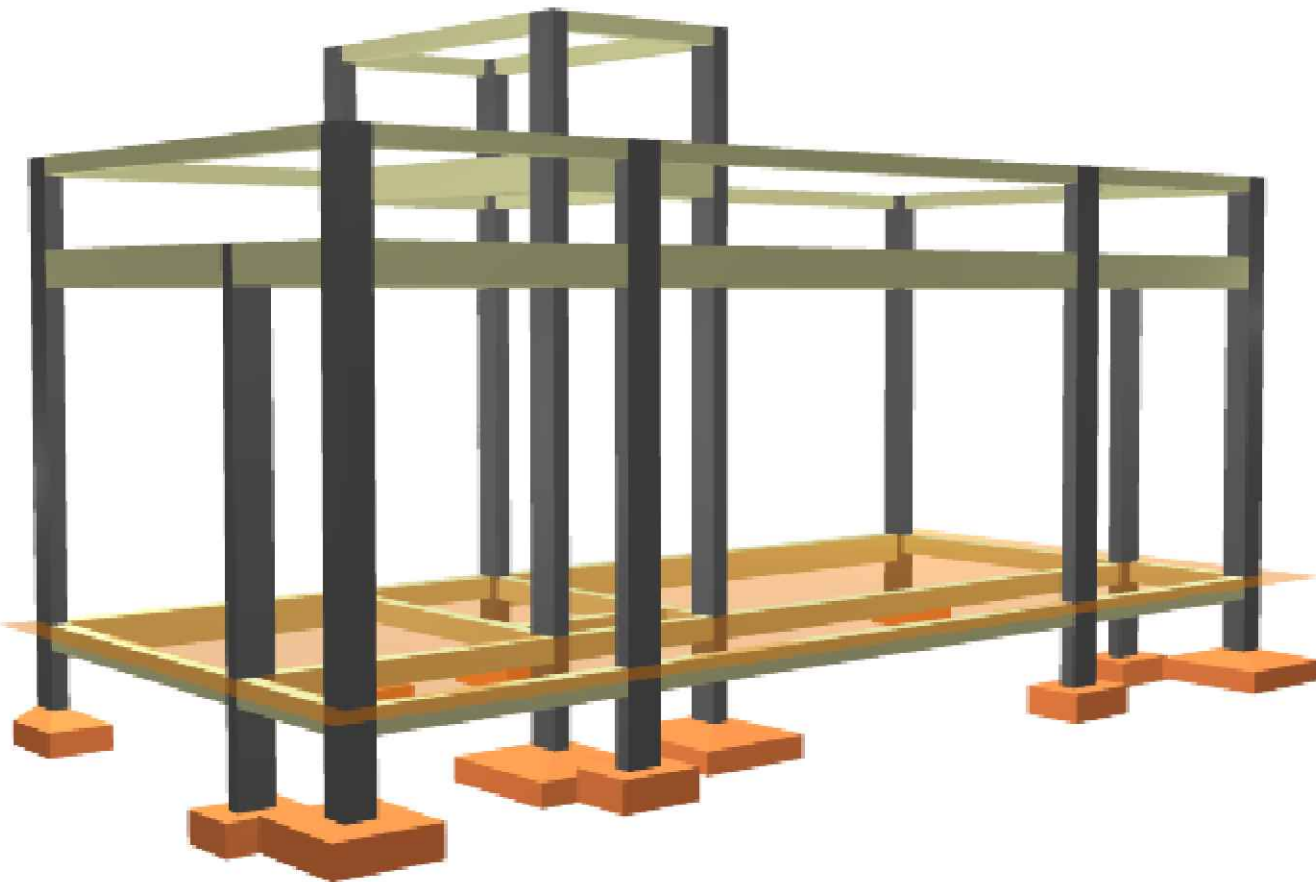


PROPRIETÁRIO: PREFEITURA MUNICIPAL DE COREMAS- PB

LINCOLN CARTAXO DE LIRA JUNIOR:06897861405 Assinado de forma digital por LINCOLN CARTAXO DE LIRA JUNIOR:06897861405
Dados: 2025.07.14 11:27:07 -03'00'

PROJETO: LINCOLN CARTAXO DE LIRA JÚNIOR CREA 160.814.689-8

FOLHA	PROJETO: GARAGEM COREMAS (ESTRUTURAL ANEXO I)		
03/09	CONVENIENTE: PREFEITURA MUNICIPAL DE COREMAS-PB		
	CONCIDENTE: PREFEITURA MUNICIPAL DE COREMAS-PB		
	LOCALIDADE: COREMAS- PB		
DESENHO	DATA	RESPONSÁVEL	RUBRICA
JUN/2025	LINCOLN CARTAXO		
CÓPIA			
VISTO			
ESCALAS	DESENHOS	CONVÊNIO	
INDICADO	- PLANTA DE FORMAS -- Pav. +490. - CORTES -- Corte A-A; -- Corte B-B.	ARQUIVO	

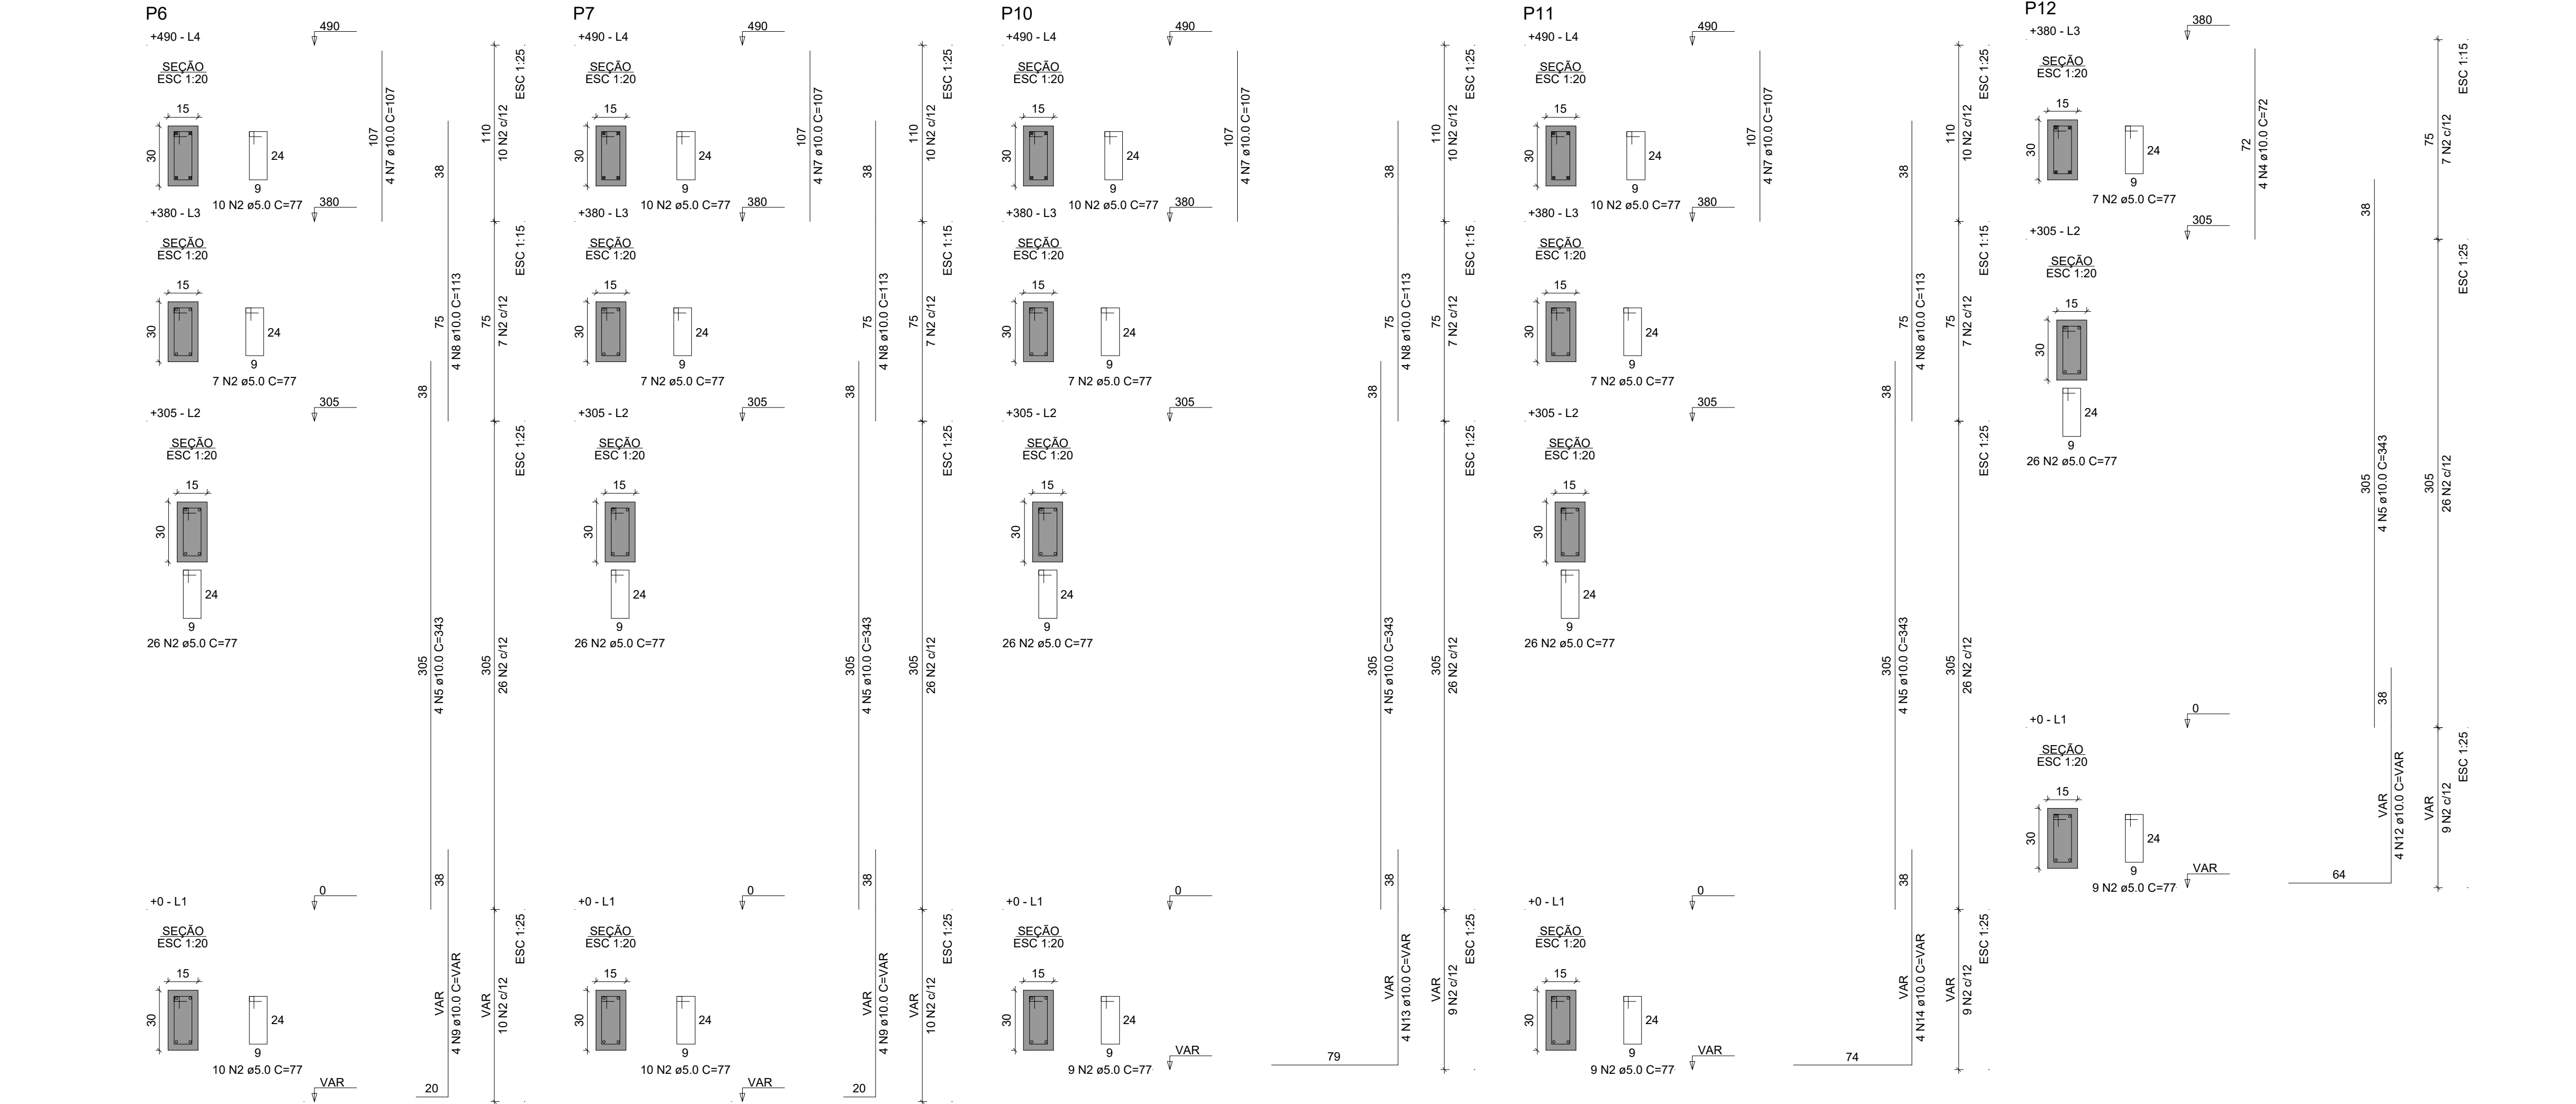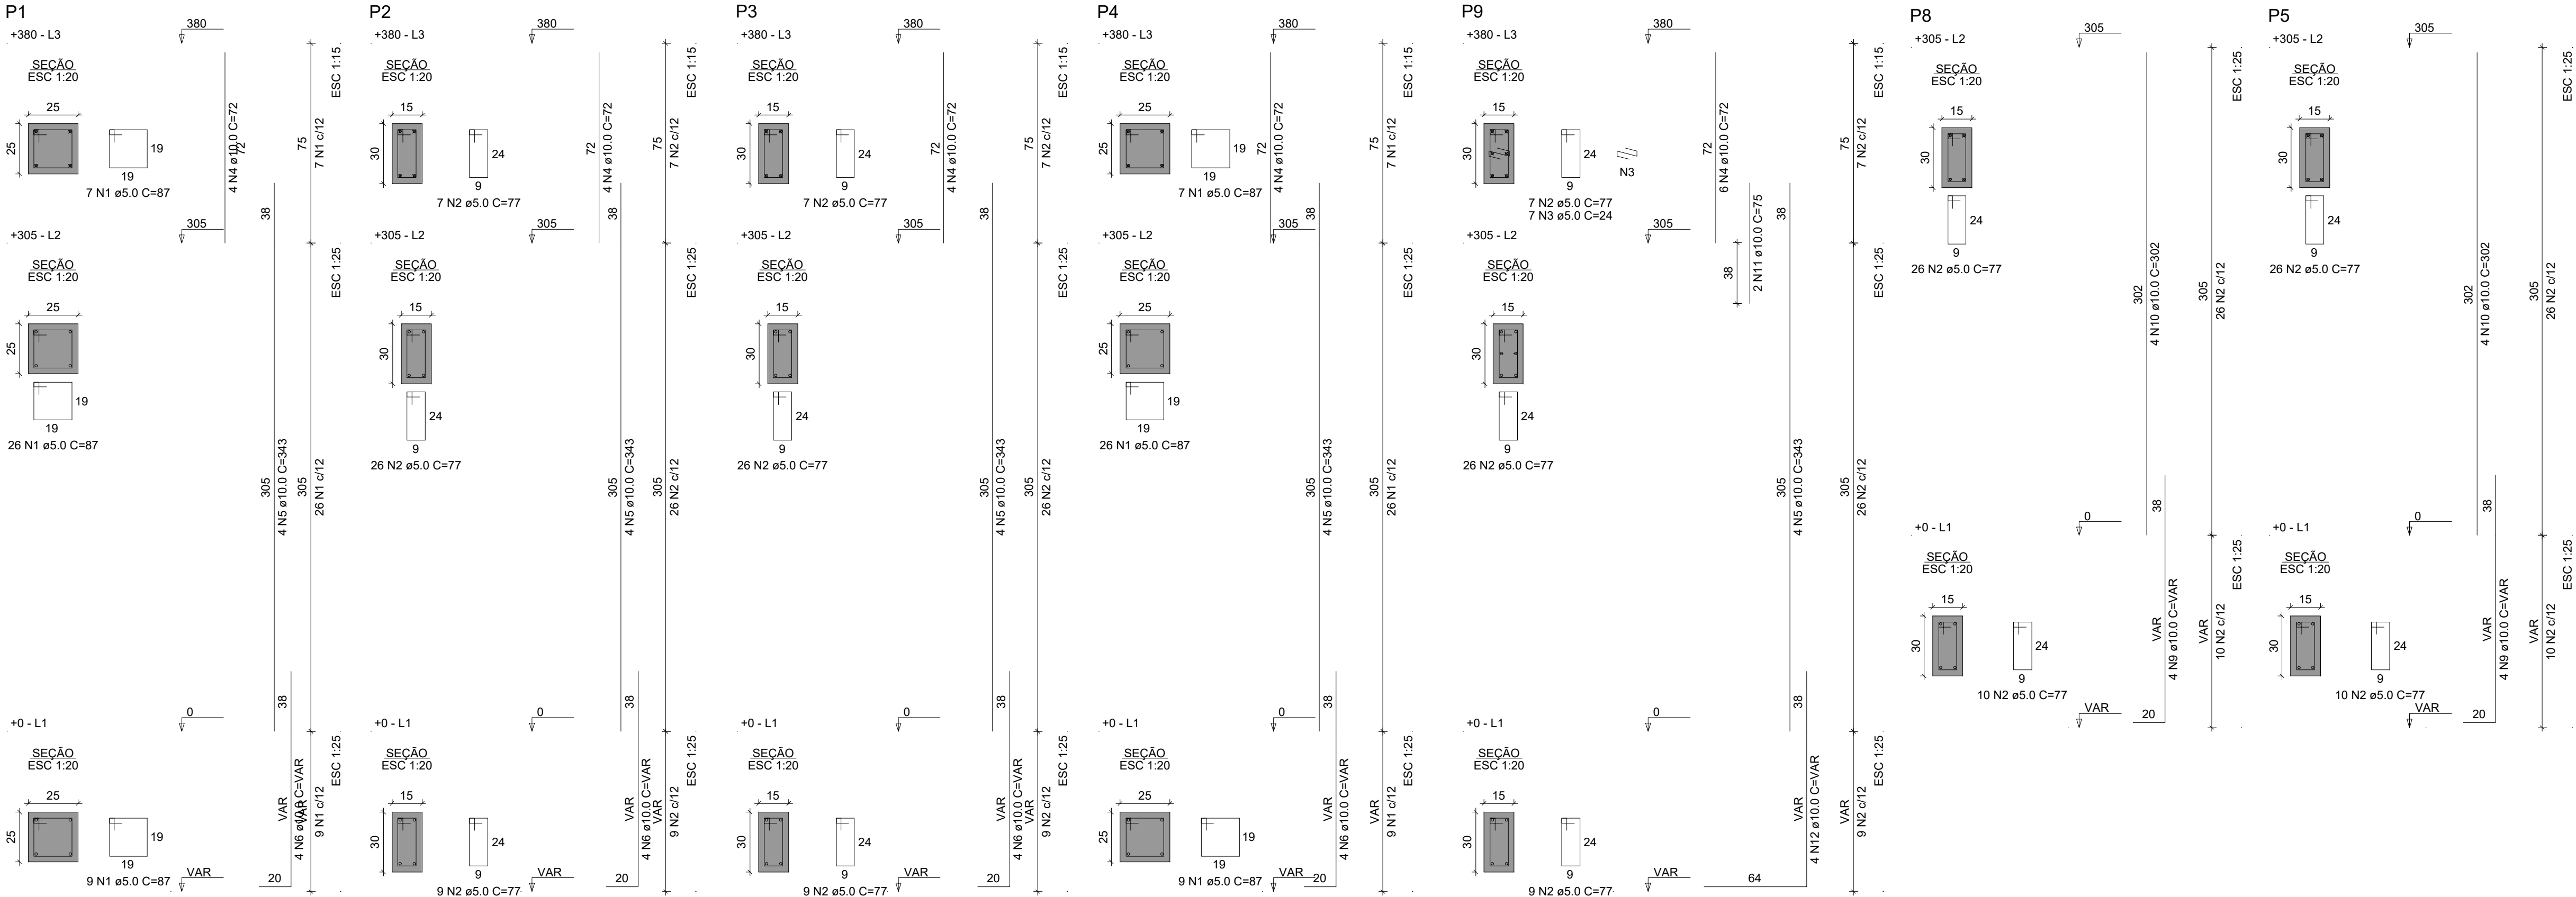

RELAÇÃO DO AÇO

P1-L3	P1-L2	P1-L1
P2-L3	P2-L2	P2-L1
P3-L3	P3-L2	P3-L1
P4-L3	P4-L2	P4-L1
P6-L4	P6-L3	P6-L2
P6-L1	P7-L4	P7-L3
P7-L2	P7-L1	P8-L2
P8-L1	P9-L3	P9-L2
P9-L1	P10-L4	P10-L3
P10-L2	P10-L1	P11-L4
P11-L3	P11-L2	P11-L1
P12-L3	P12-L2	P12-L1
P5-L2	P5-L1	

AÇO	N	DIAM (mm)	QUANT	C.UNIT (cm)	C.TOTAL (cm)
CA60	1	5.0	84	87	7308
	2	5.0	450	77	34650
	3	5.0	7	24	168
	4	10.0	26	72	1872
CA50	5	10.0	40	343	13720
	6	10.0	16	VAR	VAR
	7	10.0	16	107	1712
	8	10.0	16	113	1808
	9	10.0	16	VAR	VAR
	10	10.0	8	302	2416
	11	10.0	2	75	150
	12	10.0	8	VAR	VAR
	13	10.0	4	VAR	VAR
	14	10.0	4	VAR	VAR

RESUMO DO AÇO

AÇO	DIAM (mm)	C.TOTAL (m)	PESO + 10% (kg)
CA50	10.0	301.5	204.4
CA60	5.0	421.3	71.4
PESO TOTAL (kg)			
CA50		204.4	
CA60		71.4	

Volume de concreto (C-25) = 2.93 m³
Área de forma = 56.13 m²

PROPRIETÁRIO: PREFEITURA MUNICIPAL DE COREMAS- PB
LINCOLN CARTAXO DE LIRA JUNIOR:06897861405 Assinado de forma digital por LINCOLN CARTAXO DE LIRA JUNIOR:06897861405
Dados: 2025.07.14 11:28:00 -03'00'

PROJETO: LINCOLN CARTAXO DE LIRA JÚNIOR CREA 160.814.689-8


FOLHA
05/09
PROJETO: GARAGEM COREMAS (ESTRUTURAL ANEXO I)
CONVENIENTE: PREFEITURA MUNICIPAL DE COREMAS-PB
CONCIDENTE: PREFEITURA MUNICIPAL DE COREMAS-PB
LOCALIDADE: COREMAS- PB

DESENHO	DATA	RESPONSÁVEL	RUBRICA	DADOS
COPIA	JUN/2025	LINCOLN CARTAXO		
VISTO				
ESCALAS	DESENHOS	CONVÊNIO		
INDICADO	PILARES	ARQUIVO		

Aprovações:


VB1

ESC 1:50

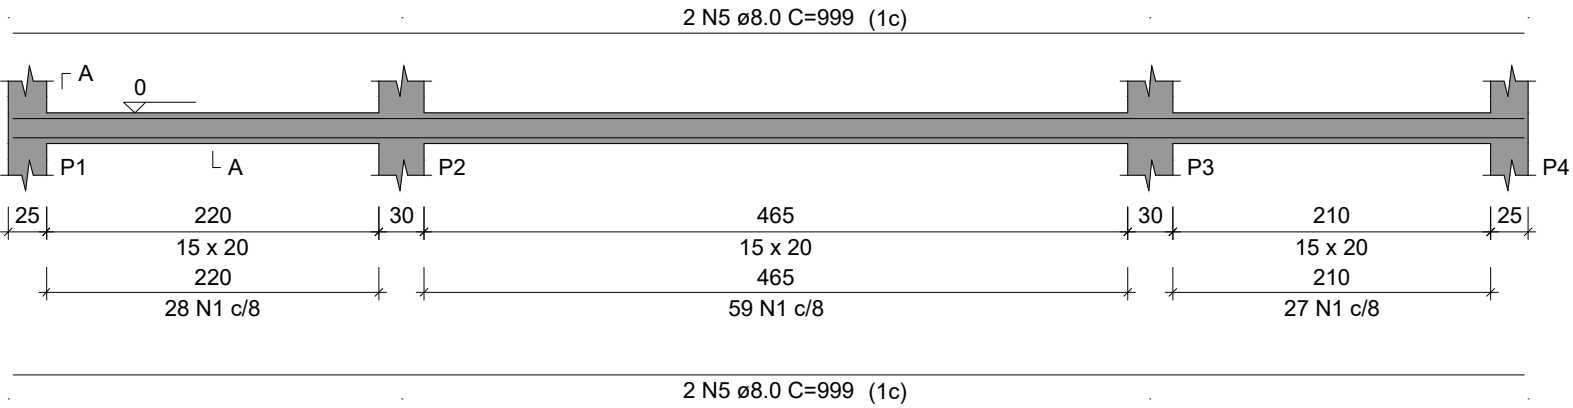


SEÇÃO A-A

ESC 1:25

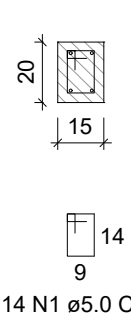


VB2

ESC 1:50

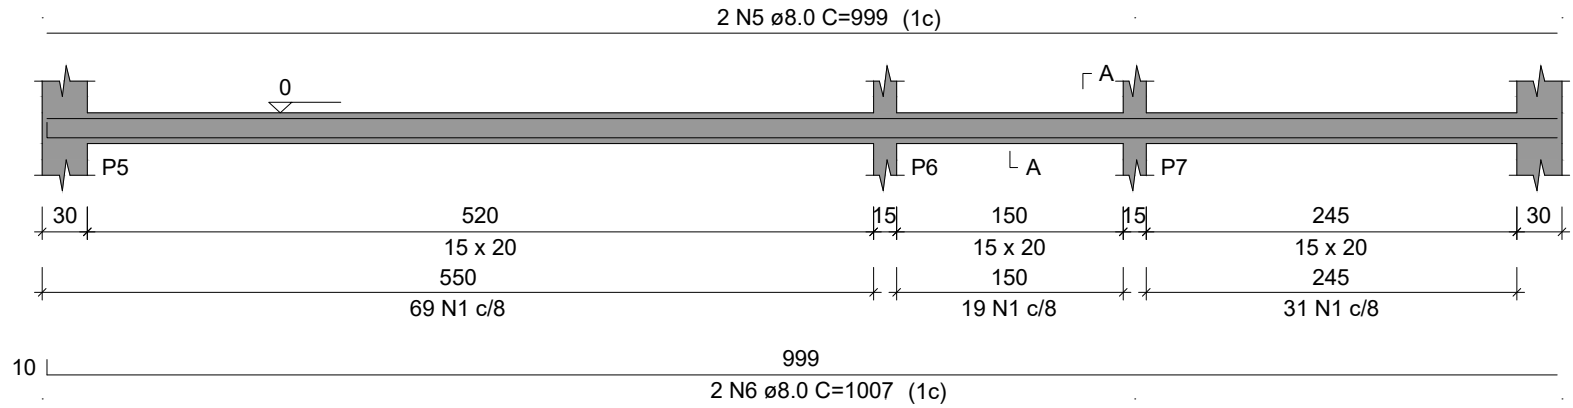


SEÇÃO A-A

ESC 1:25

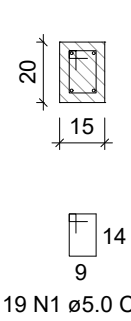


VB3

ESC 1:50

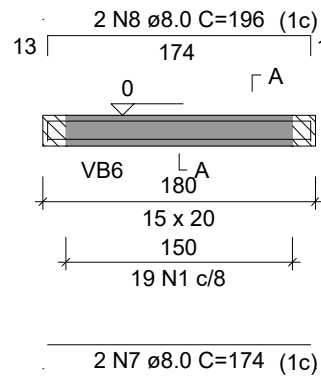


SEÇÃO A-A

ESC 1:25

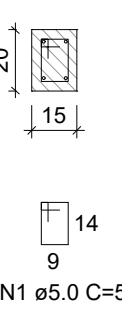


VB4

ESC 1:50

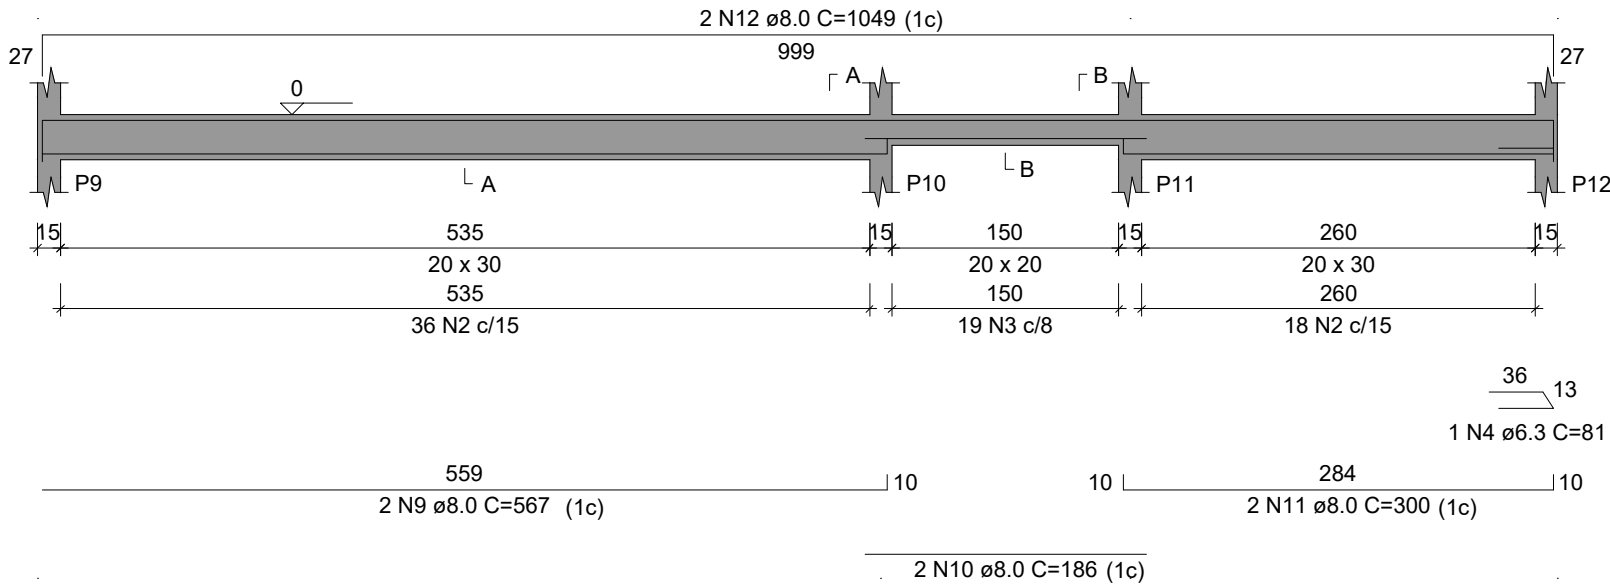


SEÇÃO A-A

ESC 1:25

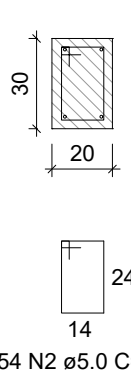


SEÇÃO B-B

ESC 1:25

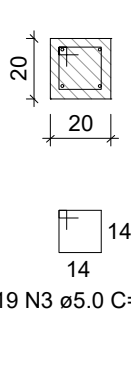


VB5

ESC 1:50

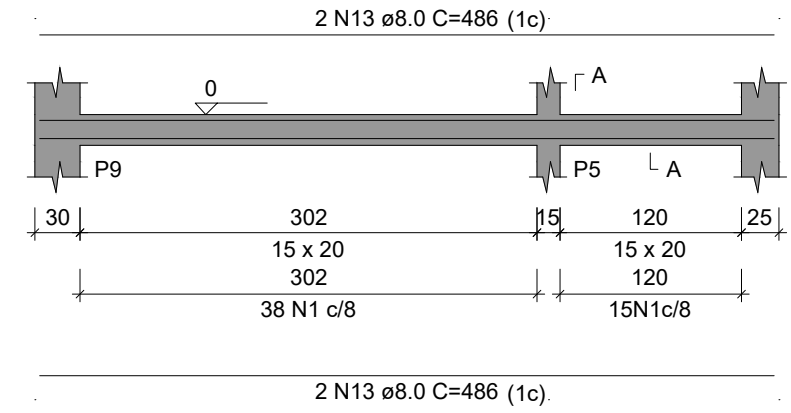


SEÇÃO A-A

ESC 1:25

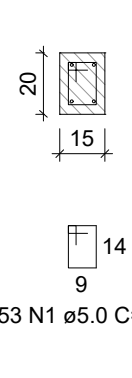


VB6

ESC 1:50

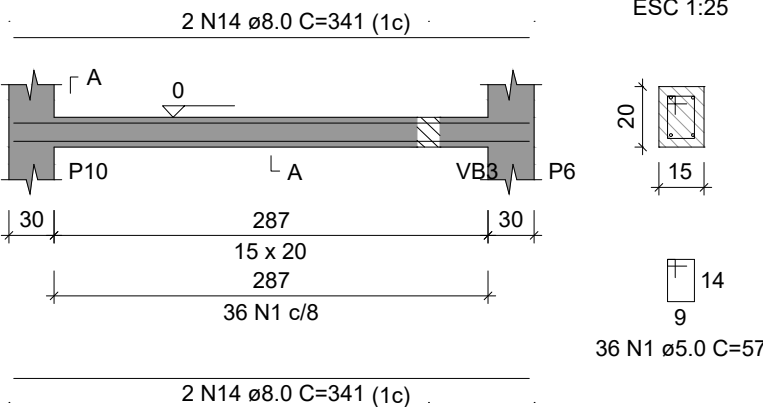


SEÇÃO A-A

ESC 1:25

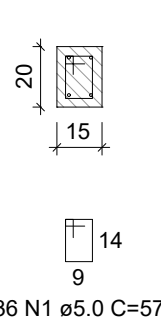


VB7

ESC 1:50

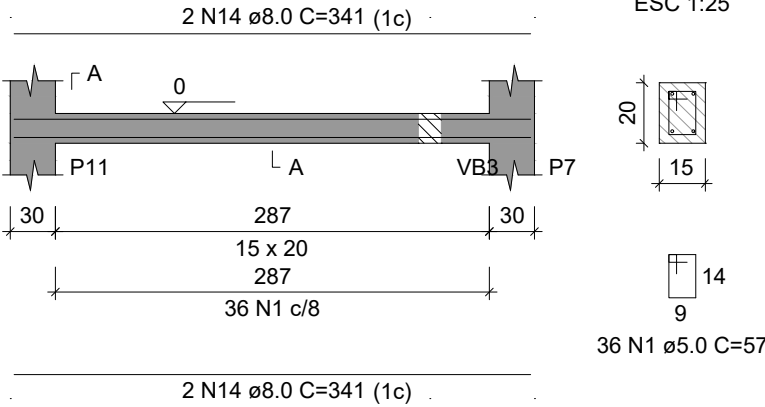


SEÇÃO A-A

ESC 1:25

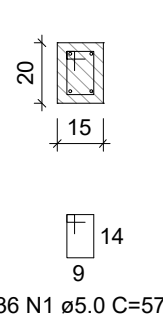


VB8

ESC 1:50

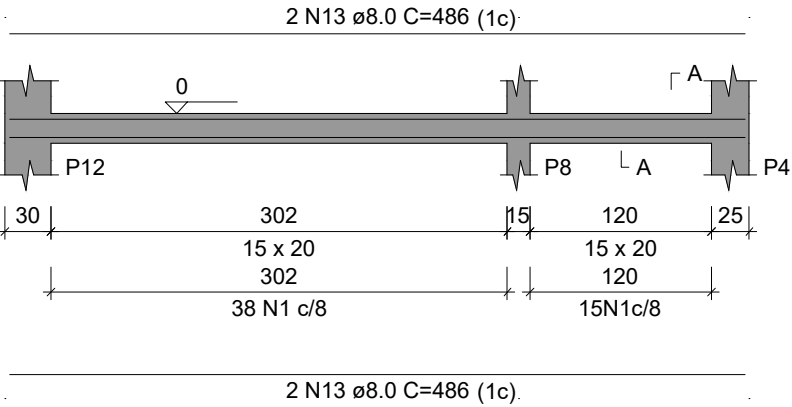

SEÇÃO A-A

ESC 1:25

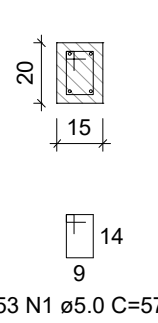

RELAÇÃO DO AÇO

VB1 VB2 VB3
VB4 VB5 VB6
VB7 VB8

RESUMO DO AÇO

AÇO	N	DIAM (mm)	QUANT	C.UNIT (cm)	C.TOTAL (cm)
CA60	1	5.0	430	57	24510
	2	5.0	54	87	4698
	3	5.0	19	67	1273
	4	6.3	1	81	81
	5	8.0	6	999	5994
	6	8.0	2	1007	2014
	7	8.0	2	174	348
	8	8.0	2	196	392
	9	8.0	2	567	1134
	10	8.0	2	186	372
	11	8.0	2	300	600
	12	8.0	2	1049	2098
	13	8.0	8	486	3888
	14	8.0	8	341	2728

AÇO	DIAM (mm)	C.TOTAL (m)	PESO + 10% (kg)
CA50	6.3	0.8	0.2
	8.0	195.7	84.9
	5.0	304.8	51.7
PESO TOTAL (kg)			
CA50	85.2		
CA60	51.7		

Volume de concreto (C-25) = 1.73 m³

Área de forma = 28.98 m²

PROPRIETÁRIO: PREFEITURA MUNICIPAL DE COREMAS- PB
LINCOLN CARTAXO DE LIRA JUNIOR:06897861405
Assinado de forma digital por LINCOLN CARTAXO DE LIRA JUNIOR:06897861405
Dados: 2025.07.14 11:27:48 -03'00'

PROJETO: LINCOLN CARTAXO DE LIRA JÚNIOR CREA 160.814.689-8

FOLHA

06/09

PROJETO: GARAGEM COREMAS (ESTRUTURAL ANEXO I)

CONVENIENTE: PREFEITURA MUNICIPAL DE COREMAS-PB


CONCENDENTE: PREFEITURA MUNICIPAL DE COREMAS-PB

LOCALIDADE: COREMAS- PB

	DATA	RESPONSÁVEL	RUBRICA	DADOS
DESENHO	JUN/2025	LINCOLN CARTAXO		
CÓPIA				
VISTO				
ESCALAS	DESENHOS			CONVÊNIO
INDICADO	- VIGAS BALDRAME			
				ARQUIVO


Aprovações:

VS100
ESC 1:50

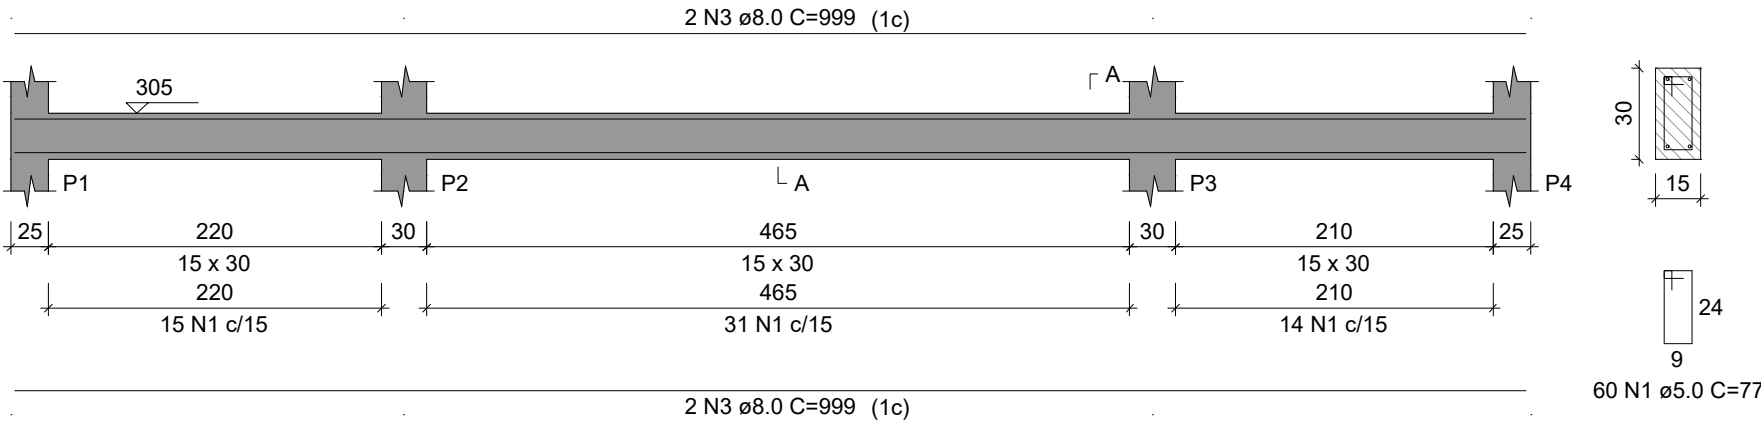


SEÇÃO A-A
ESC 1:25

VS101
ESC 1:50

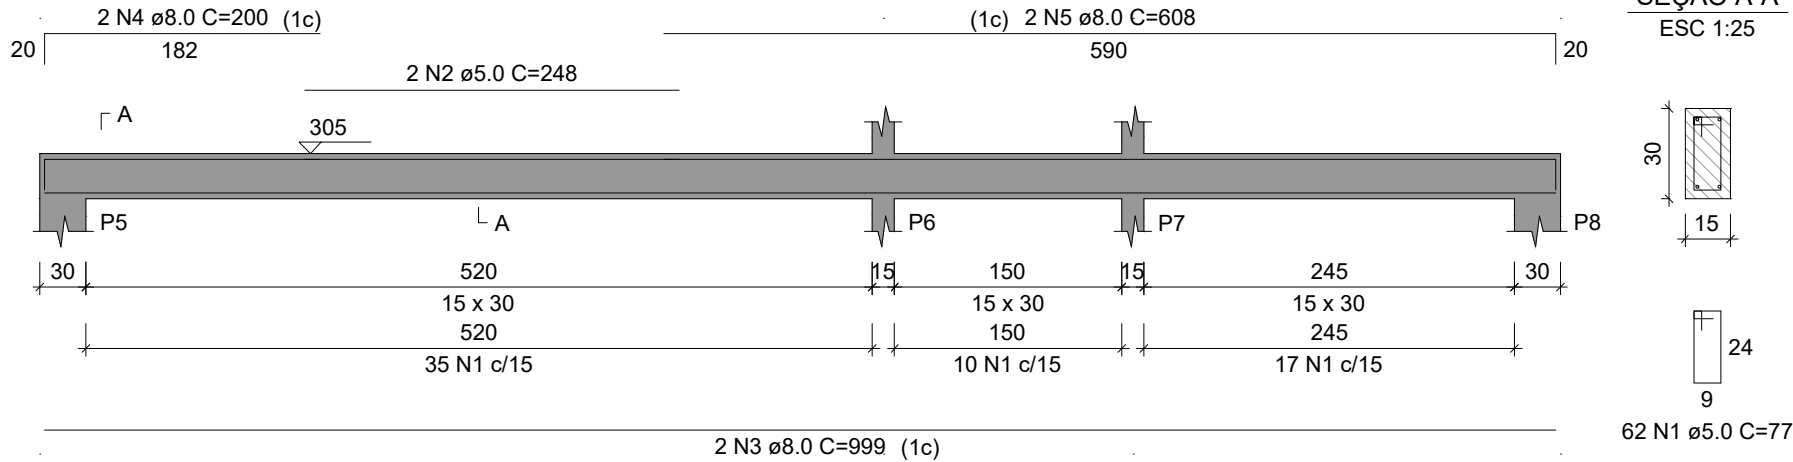


SEÇÃO A-A
ESC 1:25

VS102
ESC 1:50

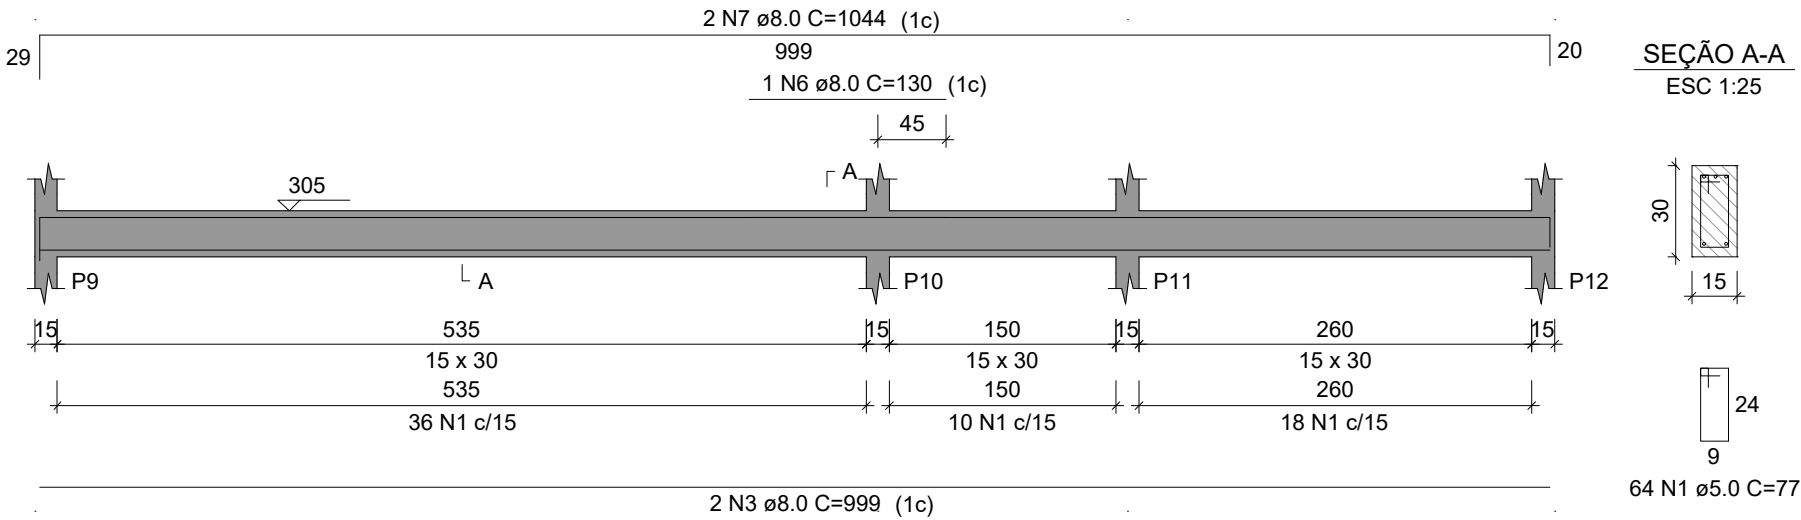


SEÇÃO A-A
ESC 1:25

VS103
ESC 1:50

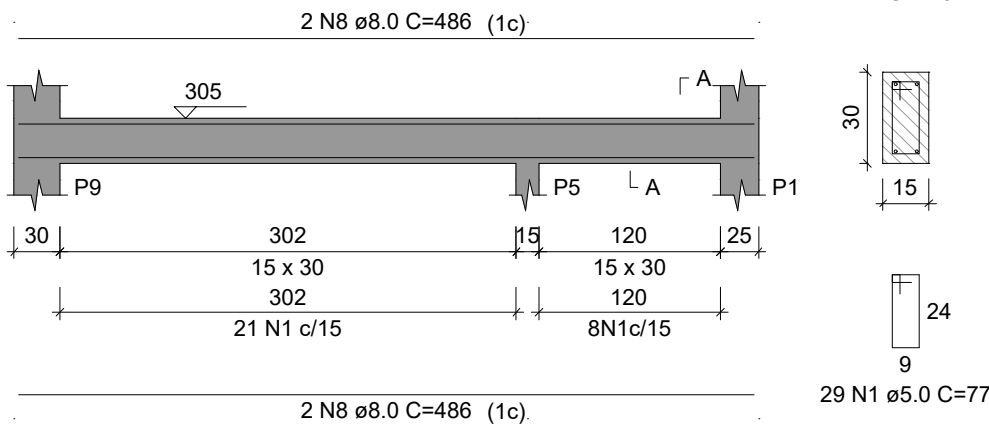

SEÇÃO A-A
ESC 1:25

VS104
ESC 1:50

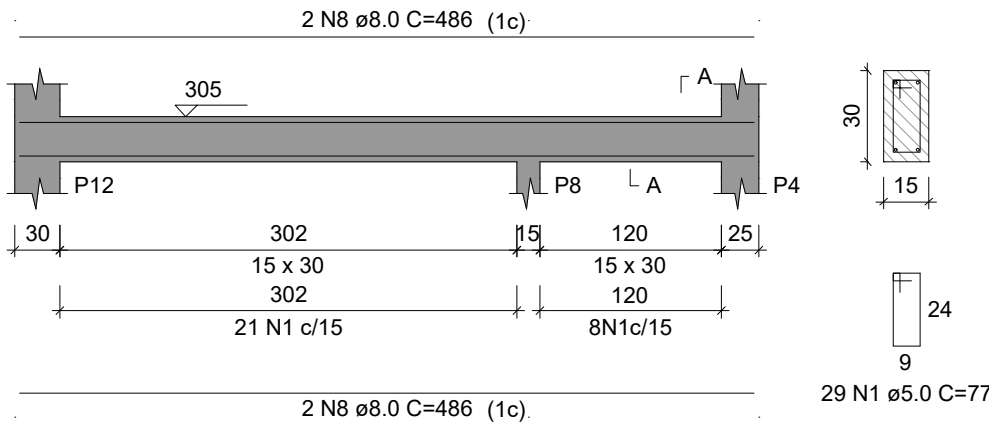

SEÇÃO A-A
ESC 1:25

RELAÇÃO DO AÇO

AÇO	N	DIAM (mm)	QUANT	C.UNIT (cm)	C.TOTAL (cm)
CA60	1	5.0	244	77	18788
	2	5.0	2	248	496
CA50	3	8.0	8	999	7992
	4	8.0	2	200	400
	5	8.0	2	608	1216
	6	8.0	1	130	130
	7	8.0	2	1044	2088
	8	8.0	8	486	3888

RESUMO DO AÇO

AÇO	DIAM (mm)	C.TOTAL (m)	PESO + 10% (kg)
CA50	8.0	157.1	68.2
CA60	5.0	192.8	32.7
PESO TOTAL (kg)			
CA50	68.2		
CA60	32.7		

Volume de concreto (C-25) = 1.80 m³
Área de forma = 29.99 m²

PROPRIETÁRIO: PREFEITURA MUNICIPAL DE COREMAS- PB


LINCOLN CARTAXO DE LIRA JÚNIOR:06897861405
Assinado de forma digital por LINCOLN CARTAXO DE LIRA JÚNIOR:06897861405
Dados: 2025.07.14 11:27:36 -03'00'

PROJETO: LINCOLN CARTAXO DE LIRA JÚNIOR CREA 160.814.689-8


FOLHA	PROJETO: GARAGEM COREMAS (ESTRUTURAL ANEXO I)			
07/09	CONVENENTE: PREFEITURA MUNICIPAL DE COREMAS-PB			
	CONCENDENTE: PREFEITURA MUNICIPAL DE COREMAS-PB			
	LOCALIDADE: COREMAS- PB			
DESENHO	DATA	RESPONSÁVEL	RUBRICA	DADOS
CÓPIA	JUN/2025	LINCOLN CARTAXO		
VISTO				
ESCALAS	DESENHOS			CONVÊNIO
INDICADO	- VIGAS (Nv. +305)			
				ARQUIVO

Aprovações:


VS200

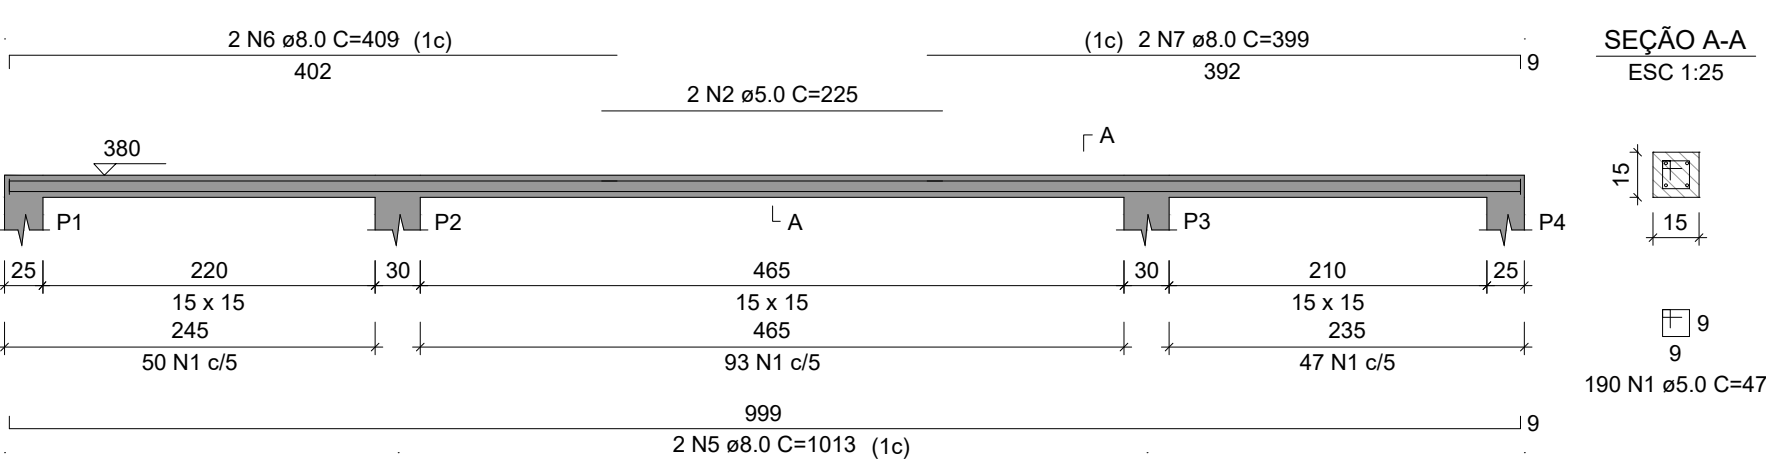


VS201

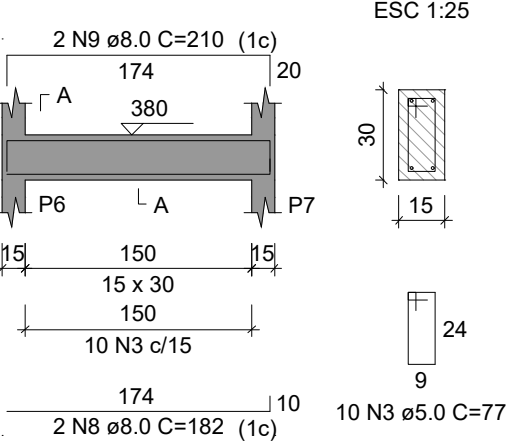


VS202

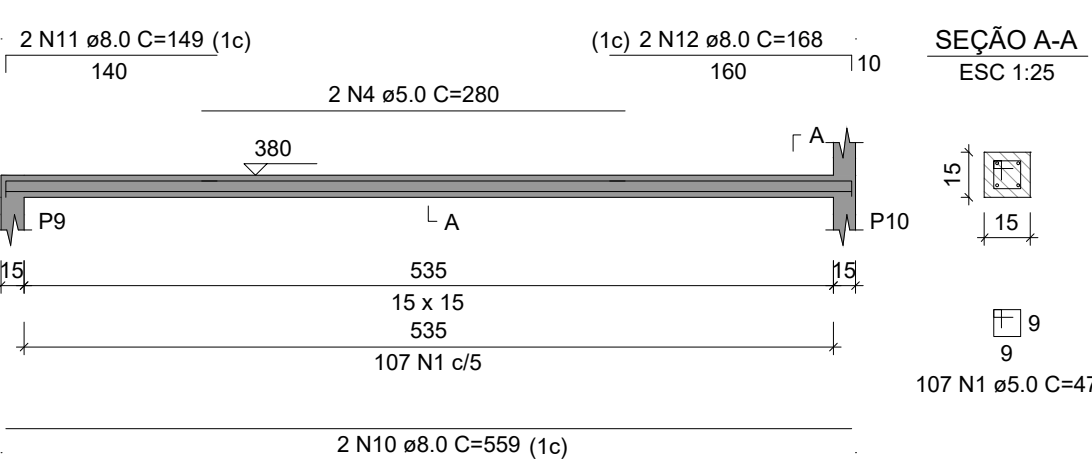


VS203

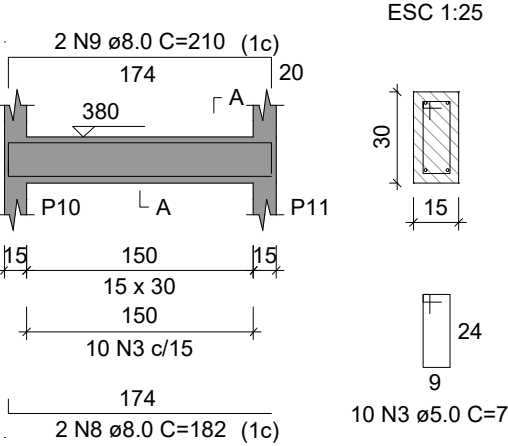


VS204

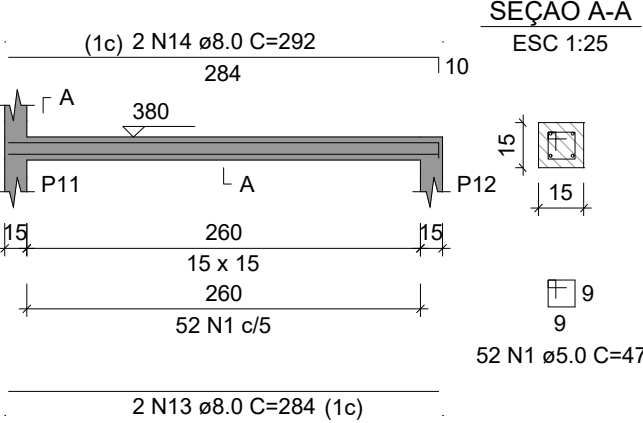


VS205

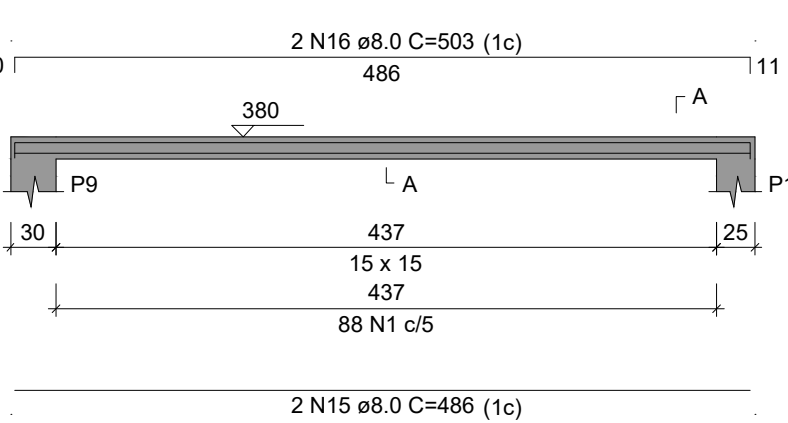


VS206

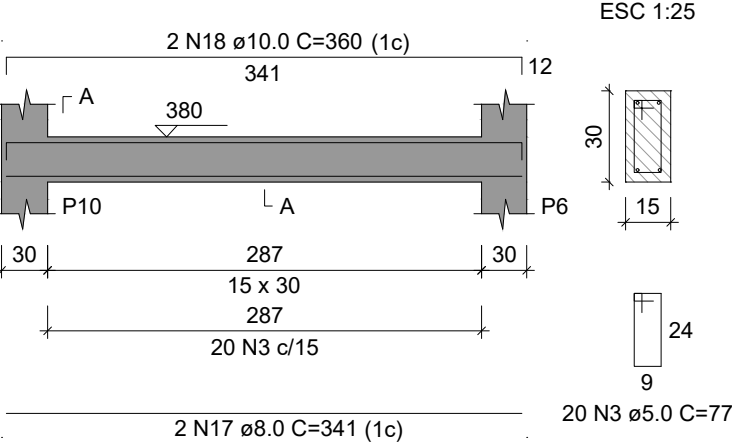

VS207

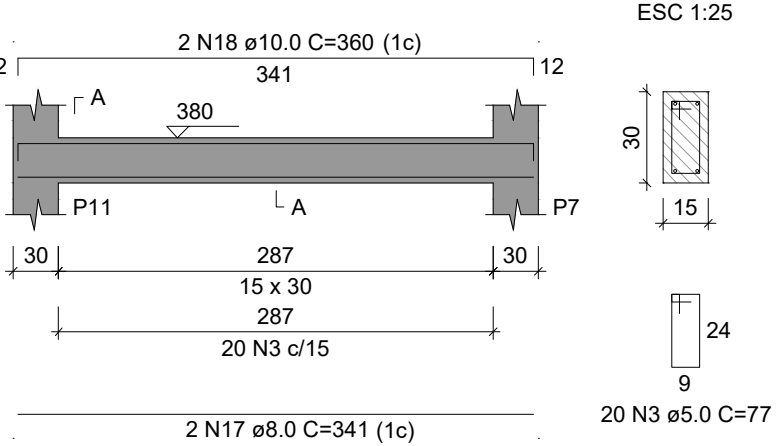

VS208

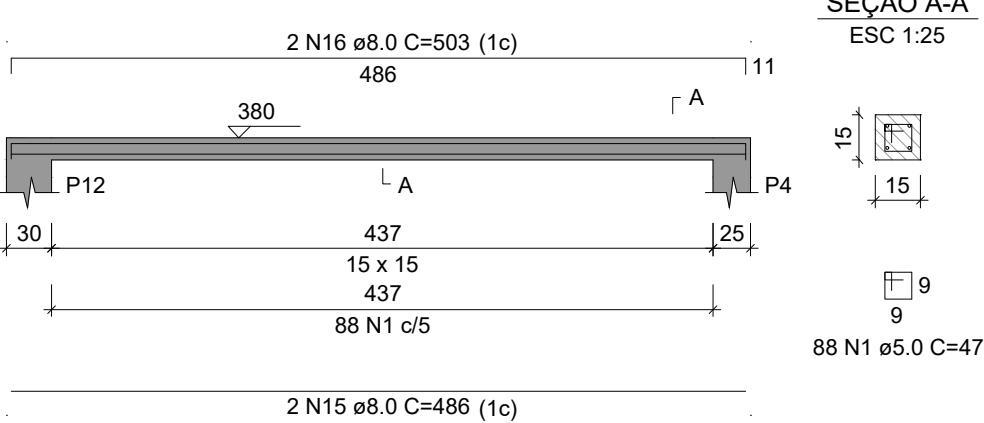

RELAÇÃO DO AÇO

AÇO	N	DIAM (mm)	QUANT	C.UNIT (cm)	C.TOTAL (cm)
CA60	1	5.0	525	47	24675
	2	5.0	2	225	450
	3	5.0	60	77	4620
CA50	4	5.0	2	280	560
	5	8.0	2	1013	2026
	6	8.0	2	409	818
	7	8.0	2	399	798
	8	8.0	4	182	728
	9	8.0	4	210	840
	10	8.0	2	559	1118
	11	8.0	2	149	298
	12	8.0	2	168	336
	13	8.0	2	284	568
	14	8.0	2	292	584
	15	8.0	4	486	1944
	16	8.0	4	503	2012
	17	8.0	4	341	1364
	18	10.0	4	360	1440

RESUMO DO AÇO

AÇO	DIAM (mm)	C.TOTAL (m)	PESO + 10% (kg)
CA50	8.0	134.3	58.3
CA60	10.0	14.4	9.8
CA60	5.0	303.1	51.4
PESO TOTAL (kg)			
CA50	68.1		
CA60	51.4		


Volume de concreto (C-25) = 1.11 m³
Área de forma = 20.70 m²

PROPRIETÁRIO: PREFEITURA MUNICIPAL DE COREMAS- PB
Assinado de forma digital por LINCOLN CARTAXO DE LIRA JUNIOR:06897861405 JUNIOR:06897861405
Dados: 2025.07.14 11:27:22 -03'00'
PROJETO: LINCOLN CARTAXO DE LIRA JÚNIOR CREA 160.814.689-8


FOLHA	PROJETO: GARAGEM COREMAS (ESTRUTURAL ANEXO I)		
	CONVENIENTE: PREFEITURA MUNICIPAL DE COREMAS-PB		
	CONCIDENTE: PREFEITURA MUNICIPAL DE COREMAS-PB		
	LOCALIDADE: COREMAS- PB		
08/09			
DESENHO	DATA	RESPONSÁVEL	RUBRICA
CÓPIA	JUN/2025	LINCOLN CARTAXO	
VISTO			
ESCALAS	DESENHOS		CONVÊNIO
INDICADO	- VIGAS (Nv. +380)		ARQUIVO

Aprovações:


VS300

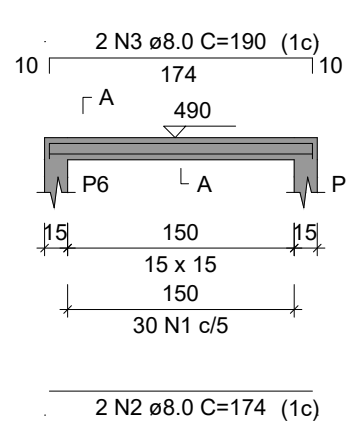


VS301

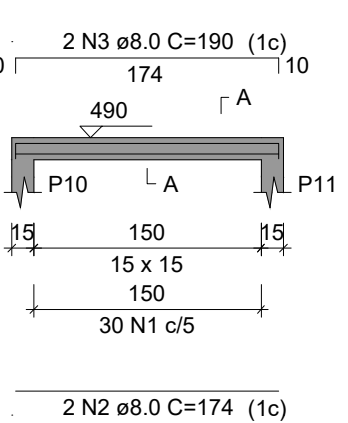

VS302

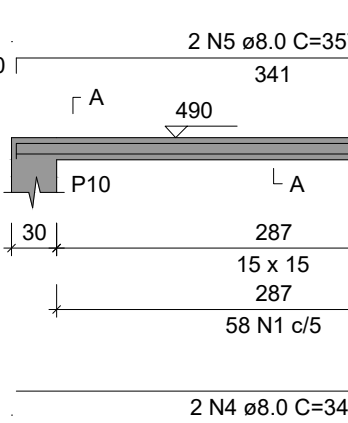

VS303

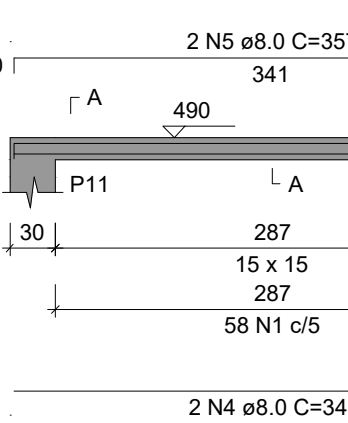

RELAÇÃO DO AÇO

AÇO	N	DIAM (mm)	QUANT	C.UNIT (cm)	C.TOTAL (cm)
CA60	1	5.0	176	47	8272
CA50	2	8.0	4	174	696
	3	8.0	4	190	760
	4	8.0	4	341	1364
	5	8.0	4	357	1428

RESUMO DO AÇO

AÇO	DIAM (mm)	C.TOTAL (m)	PESO + 10% (kg)
CA50	8.0	42.5	18.4
CA60	5.0	82.7	14
PESO TOTAL (kg)			
CA50	18.4		
CA60	14		

Volume de concreto (C-25) = 0.24 m³
Área de forma = 4.74 m²


PROPRIETÁRIO: PREFEITURA MUNICIPAL DE COREMAS- PB

LINCOLN CARTAXO DE LIRA JUNIOR:06897861405
Assinado de forma digital por LINCOLN CARTAXO DE LIRA JUNIOR:06897861405
Dados: 2025.07.14 11:28:26 -03'00'


PROJETO: LINCOLN CARTAXO DE LIRA JÚNIOR CREA 160.814.689-8

FOLHA	PROJETO: GARAGEM COREMAS (ESTRUTURAL ANEXO I)			
09/09	CONVENENTE: PREFEITURA MUNICIPAL DE COREMAS-PB			
	CONCENDENTE: PREFEITURA MUNICIPAL DE COREMAS-PB			
	LOCALIDADE: COREMAS- PB			
	DATA	RESPONSÁVEL	RUBRICA	DADOS
DESENHO	JUN/2025	LINCOLN CARTAXO		
CÓPIA				
VISTO				
ESCALAS	DESENHOS			CONVÊNIO
INDICADO	- VIGAS (Nv. +490) - LAJE (Nv. +380)			ARQUIVO

Aprovações:

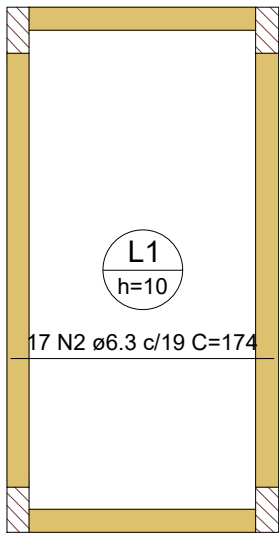

Armação positiva das lajes do pavimento +380 (Eixo X)
escala 1:50

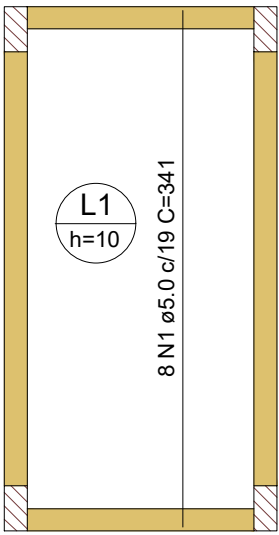

Armação positiva das lajes do pavimento +380 (Eixo Y)
escala 1:50

RELAÇÃO DO AÇO

AÇO	N	DIAM (mm)	QUANT	C.UNIT (cm)	C.TOTAL (cm)
CA60	1	5.0	8	341	2728
CA50	2	6.3	17	174	2958

RESUMO DO AÇO

AÇO	DIAM (mm)	C.TOTAL (m)	PESO + 10% (kg)
CA50	6.3	29.6	8
CA60	5.0	27.3	4.6
PESO TOTAL (kg)			
CA50	8		
CA60	4.6		

Volume de concreto (C-25) = 0.48 m³
Área de forma = 4.80 m²