


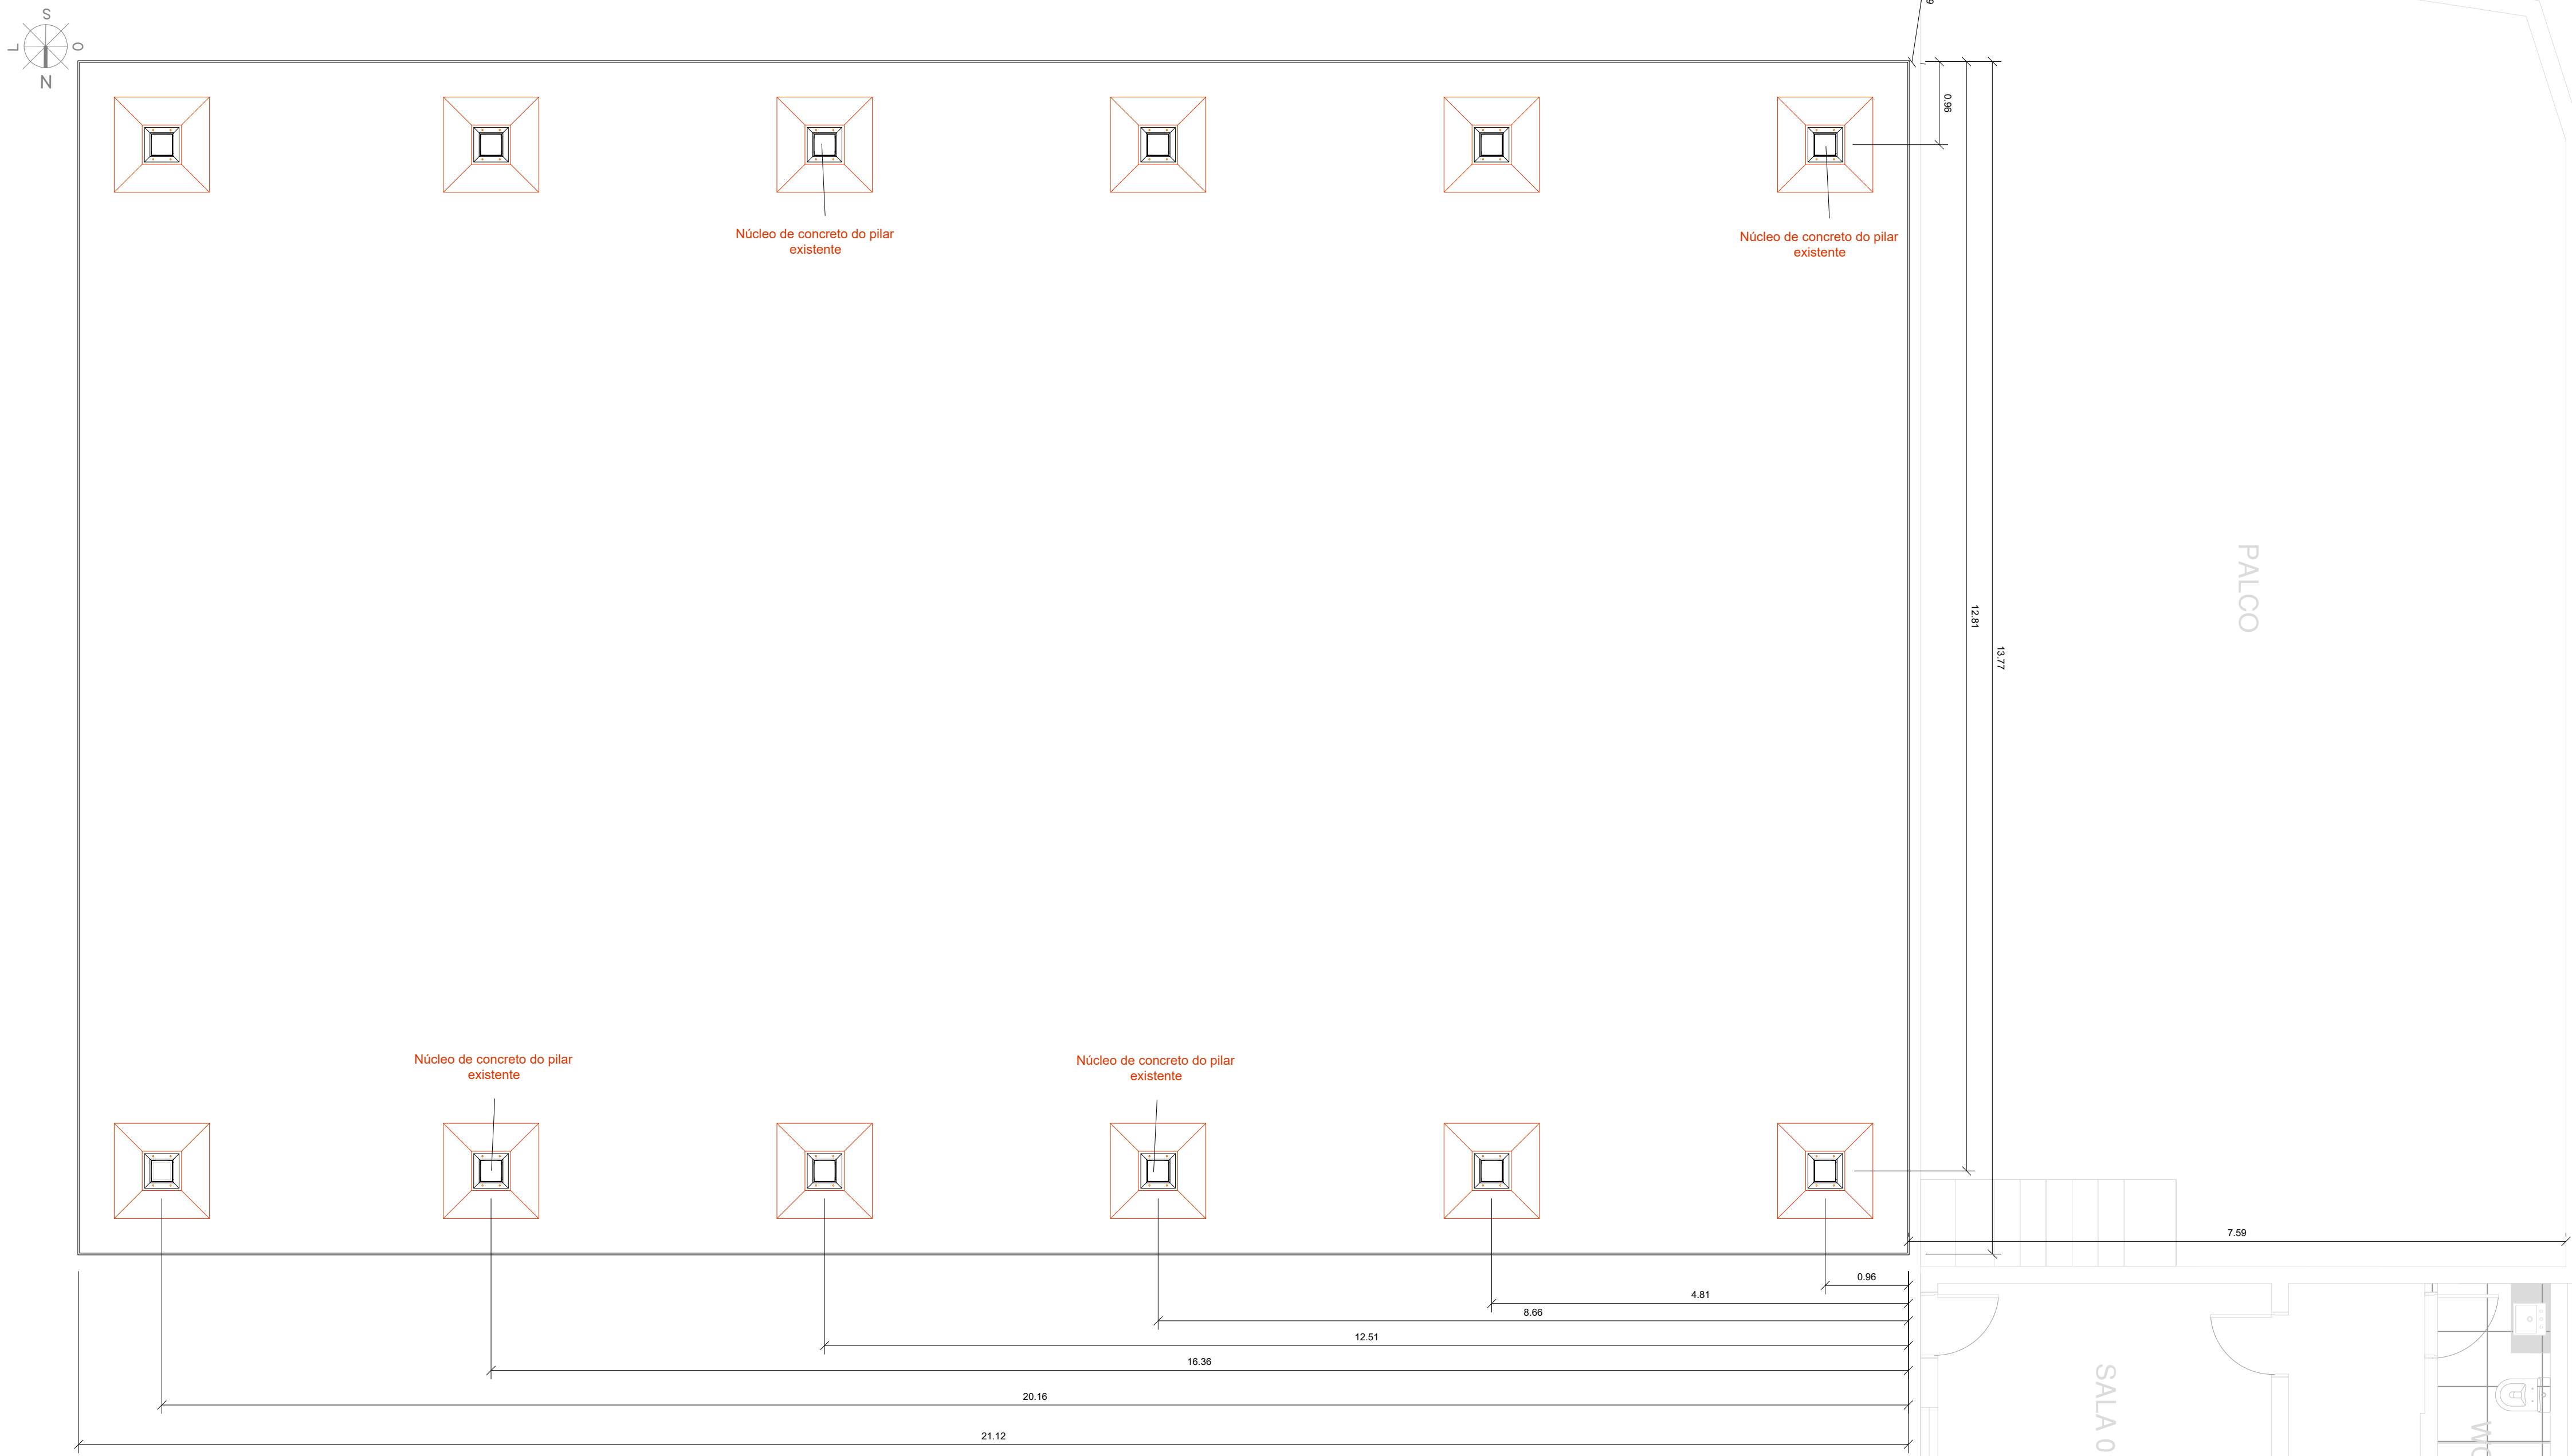

ORIENTAÇÕES PARA PINTURA DE ESTRUTURA METÁLICA (AÇO A36)

As seguintes etapas devem ser rigorosamente seguidas para a pintura dos perfis metálicos, conforme NBR 16204 (Preparação de Superfícies de Aço) e NBR 15962 (Pintura Industrial). O sistema de pintura visa garantir proteção anticorrosiva e durabilidade, adequado ao ambiente de exposição C3 (média corrosividade, conforme NBR 14643).

PREPARAÇÃO DA SUPERFÍCIE

Realizar limpeza inicial para remover óleos, graxas e contaminantes, utilizando desengraxante conforme NBR 16204, método SP 1 (limpeza com solvente).

Executar jateamento abrasivo ao grau Sa 2½ (NBR 16204, equivalente a ISO 8501-1), removendo ferrugem, carepa de laminação e impurezas. Alternativamente, usar lixamento mecânico (escovas de aço ou lixas) até atingir superfície metálica limpa.

Garantir rugosidade de 25 a 50 µm (perfil de ancoragem), conforme NBR 16204, para aderência do revestimento.

Inspeccionar a superfície, garantindo ausência de poeira, umidade ou contaminantes antes da pintura.

APLICAÇÃO DO PRIMER

Aplicar uma camada de primer epóxi com fosfato de zinco, com espessura de filme seco (DFT) de 50 a 75 µm, conforme especificação do fabricante.

Utilizar pistola airless, rolo ou pincel, garantindo aplicação uniforme em todas as faces dos perfis.

Respeitar o tempo de secagem do primer (4 a 24 horas, conforme ficha técnica), verificando condições ambientais (temperatura entre 10°C e 35°C, umidade relativa < 85%, superfície 3°C acima do ponto de orvalho).

APLICAÇÃO DA TINTA EPÓXI

Aplicar duas camadas de tinta epóxi de alta espessura (dois componentes: resina + catalisador), totalizando DFT de 100 a 150 µm, conforme NBR 15962.

Misturar os componentes na proporção INDICADAS pelo fabricante e aplicar com pistola airless, rolo ou pincel, garantindo cobertura homogênea.

Aguardar intervalo de 12 a 24 horas entre camadas, conforme ficha técnica, mantendo condições ambientais adequadas.

ACABAMENTO (OPCIONAL)

Para proteção contra raios UV e maior durabilidade em ambientes externos, aplicar uma camada de poliuretano alifático (DFT de 50 a 75 µm) após cura parcial da epóxi (12 a 24 horas).

Seguir instruções do fabricante para aplicação e cura.

CONDIÇÕES DE APLICAÇÃO

Garantir ventilação adequada durante a aplicação e cura, especialmente em ambientes internos.

Monitorar condições ambientais conforme NBR 15962, evitando pintura em superfícies úmidas ou sob chuva.

Verificar espessura do filme seco (DFT) com medidor apropriado, conforme NBR 10443.

INSPEÇÃO FINAL

Realizar inspeção visual para verificar ausência de falhas (bolhas, crateras ou descascamento).

Confirmar aderência do revestimento, se necessário, por teste conforme NBR 11003 (método de corte em grade).

Garantir cura total do sistema (7 dias, conforme fabricante) antes da exposição a condições severas.

NOTAS:

Consultar fichas técnicas dos produtos para proporções, tempos de cura e espessuras.

Para ambientes de maior corrosividade (C4 ou C5), consultar projetista para adequação do sistema.

Manter registros de aplicação (lotes, condições ambientais, espessuras) para controle de qualidade.


Cargas consideradas em projeto:

- Peso próprio da telha: 4,5 kgf/m²;
- Peso próprio de instalações elétricas e luminárias: 0,21 kgf/m²
- Forro: NÃO INCLUSO

Planta de Localização da Garagem dos carros


ESC 1:50

SAPATAS IDEAIS: ESSE PROJETO ESTRUTURAL FOI CONCEBIDO IDEALIZANDO QUE EXISTEM FUNDAÇÕES PARA OS 12 PILARES QUE SERÃO REFORÇADOS, COM ARMAÇÕES, FCK E DIMENSÕES SEMELHANTES AO MOSTRADO ABAIXO, CASO CONTRÁRIO, FAZ-SE NECESSÁRIO DEMOLIÇÃO E RECONSTRUÇÃO DAS FUNDAÇÕES E DOS PILARES

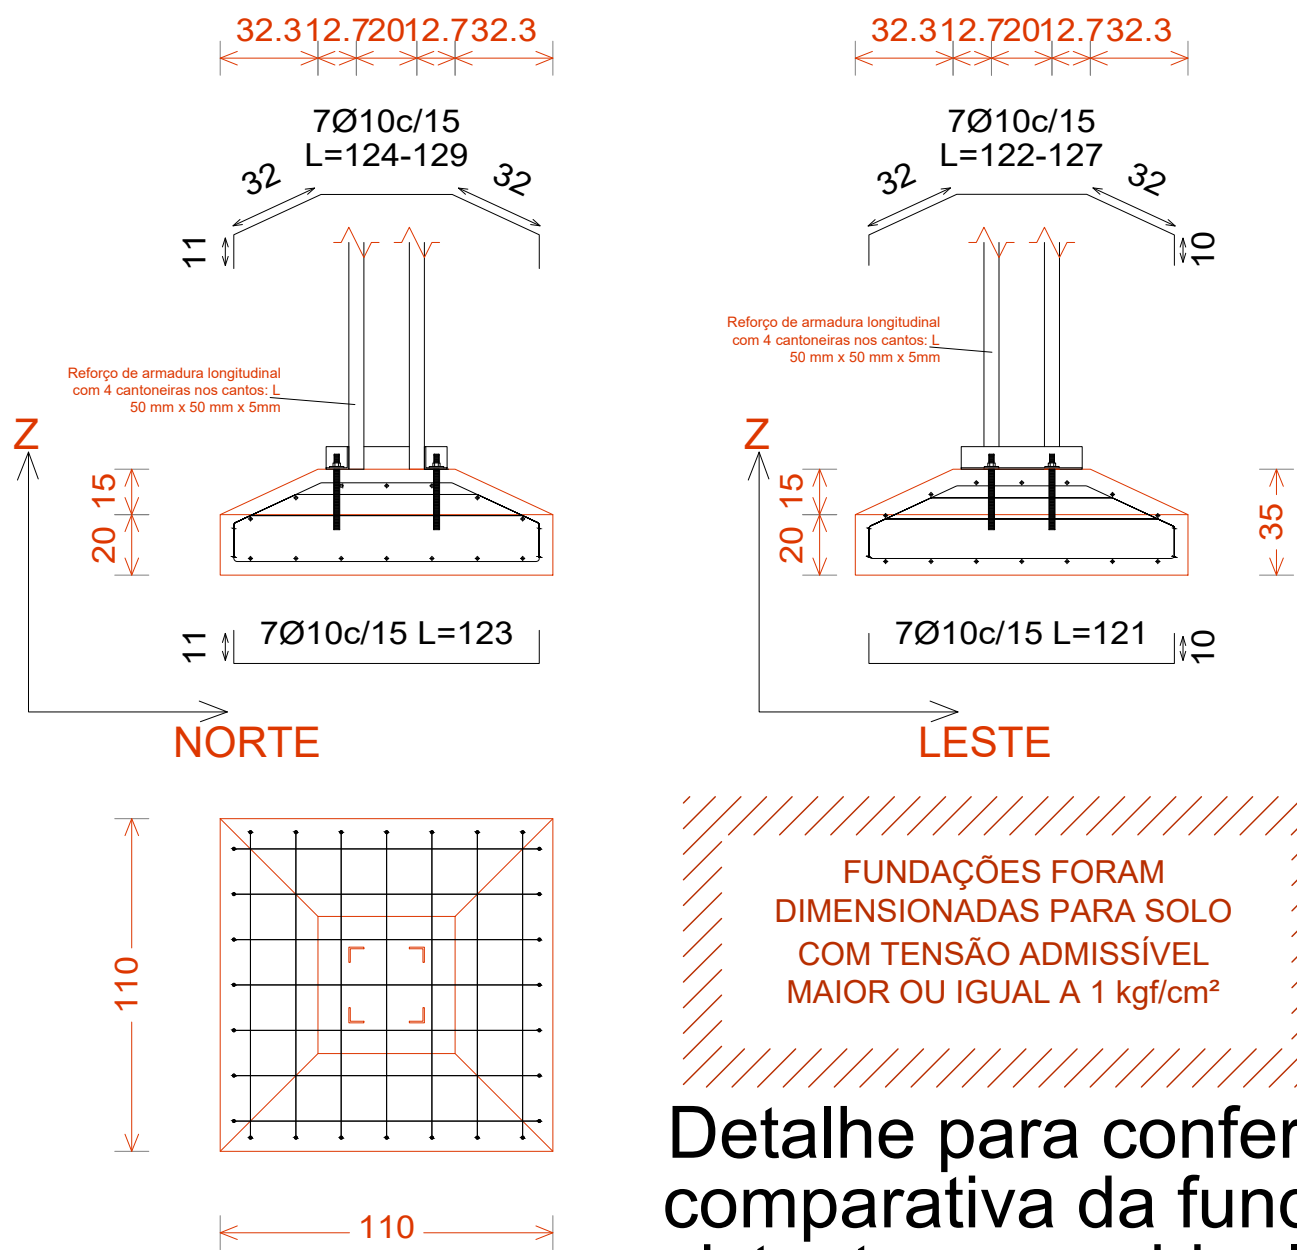


Detalhe para conferência comparativa da fundação existente com a idealizada

ESC 1:25

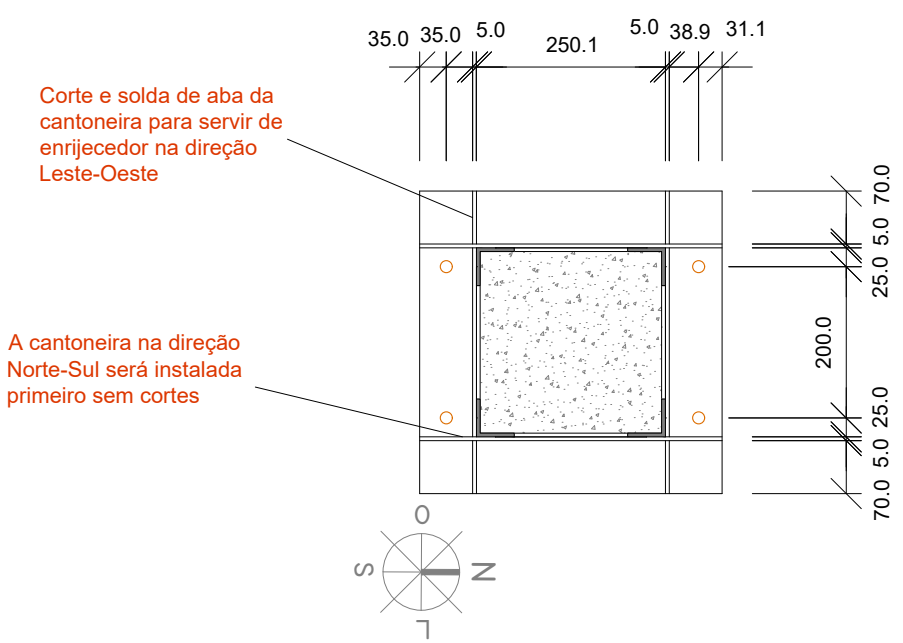


Dimensões de cantoneira de chapa base

ESC 1:10

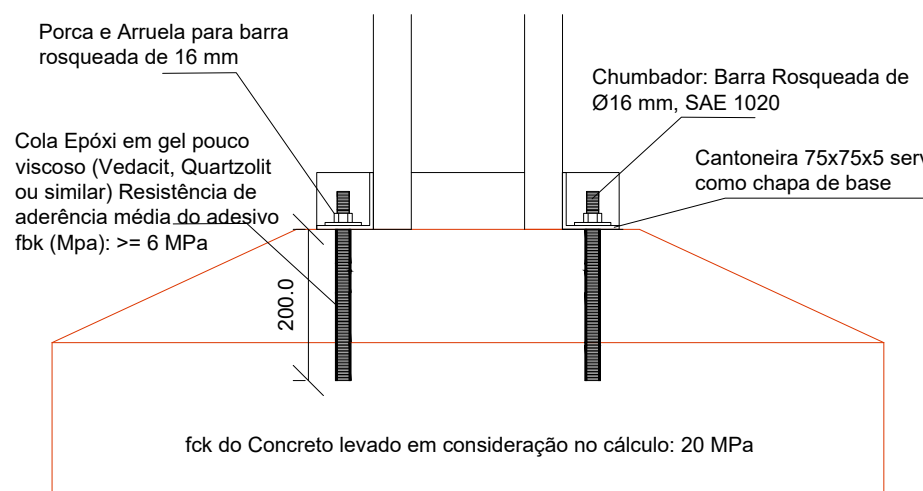

Detalhe do chumbamento


ESC 1:10

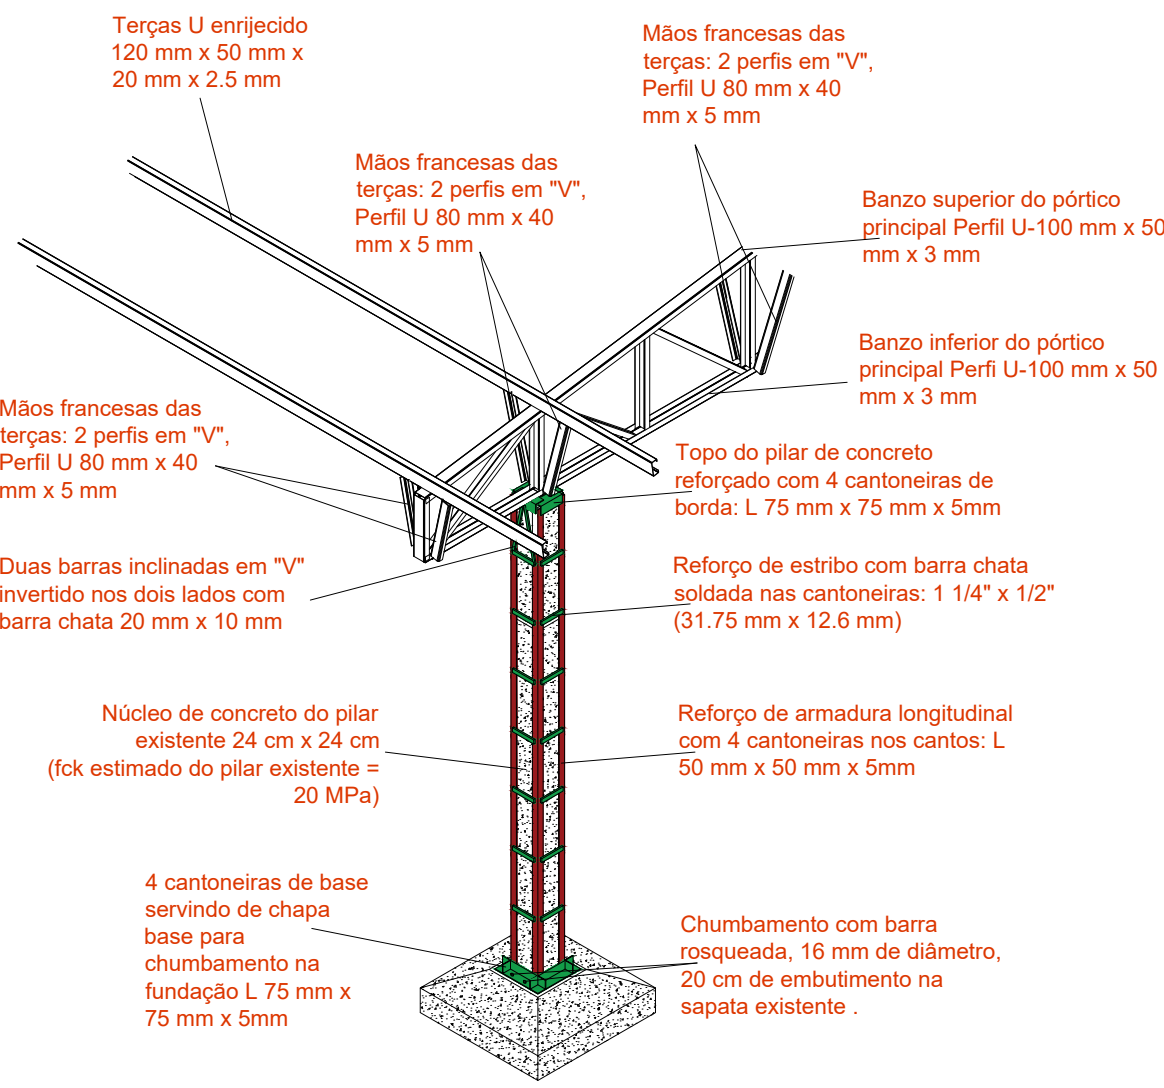

Detalhe Isométrico do Pilar com terças

S/ ESC

GARAGEM DOS CARROS

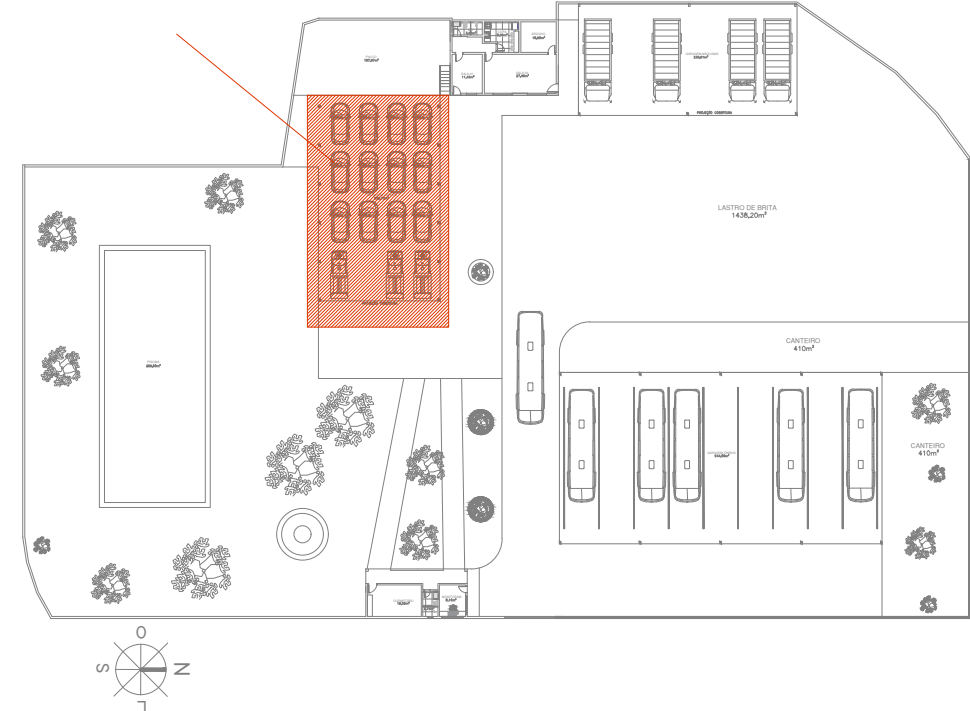

PLANTA DE SITUAÇÃO

ESC 1:750

PROPRIETÁRIO: PREFEITURA MUNICIPAL DE COREMAS - PB			
PROJETO: LINCOLN CARTAXO DE LIRA JÚNIOR CREA 160.814.689-8			
CONSTRUÇÃO: PROJETO DE REFORMA - GARAGEM DE CARROS			
FOLHA	PROJETO: PROJETO DE REFORMA - GARAGEM DE CARROS		
01/03	LOCALIDADE: MUNICÍPIO DE COREMAS - PB		
	DATA	RESPONSÁVEL	RUBRICA
DESENHO	JUN/2023	LINCOLN CARTAXO	
CÓPIA			
VISTO			
ESCALAS	DESENHOS		CONVÊNIO
INDICADAS	• Planta de Locação da Garagem dos carros • Detalhe para conferência comparativa da fundação existente com a idealizada • Detalhe de chapa base e chumbamento • Planta de situação		
			ARQUIVO
Aprovações:			



Av. Monteiro da França, 160, sl. 004A
Maracá, 50130-320 - João Pessoa (PB)
Tel: +55 (81) 99824.4447
e-mail: lclprojetos@hotmail.com