

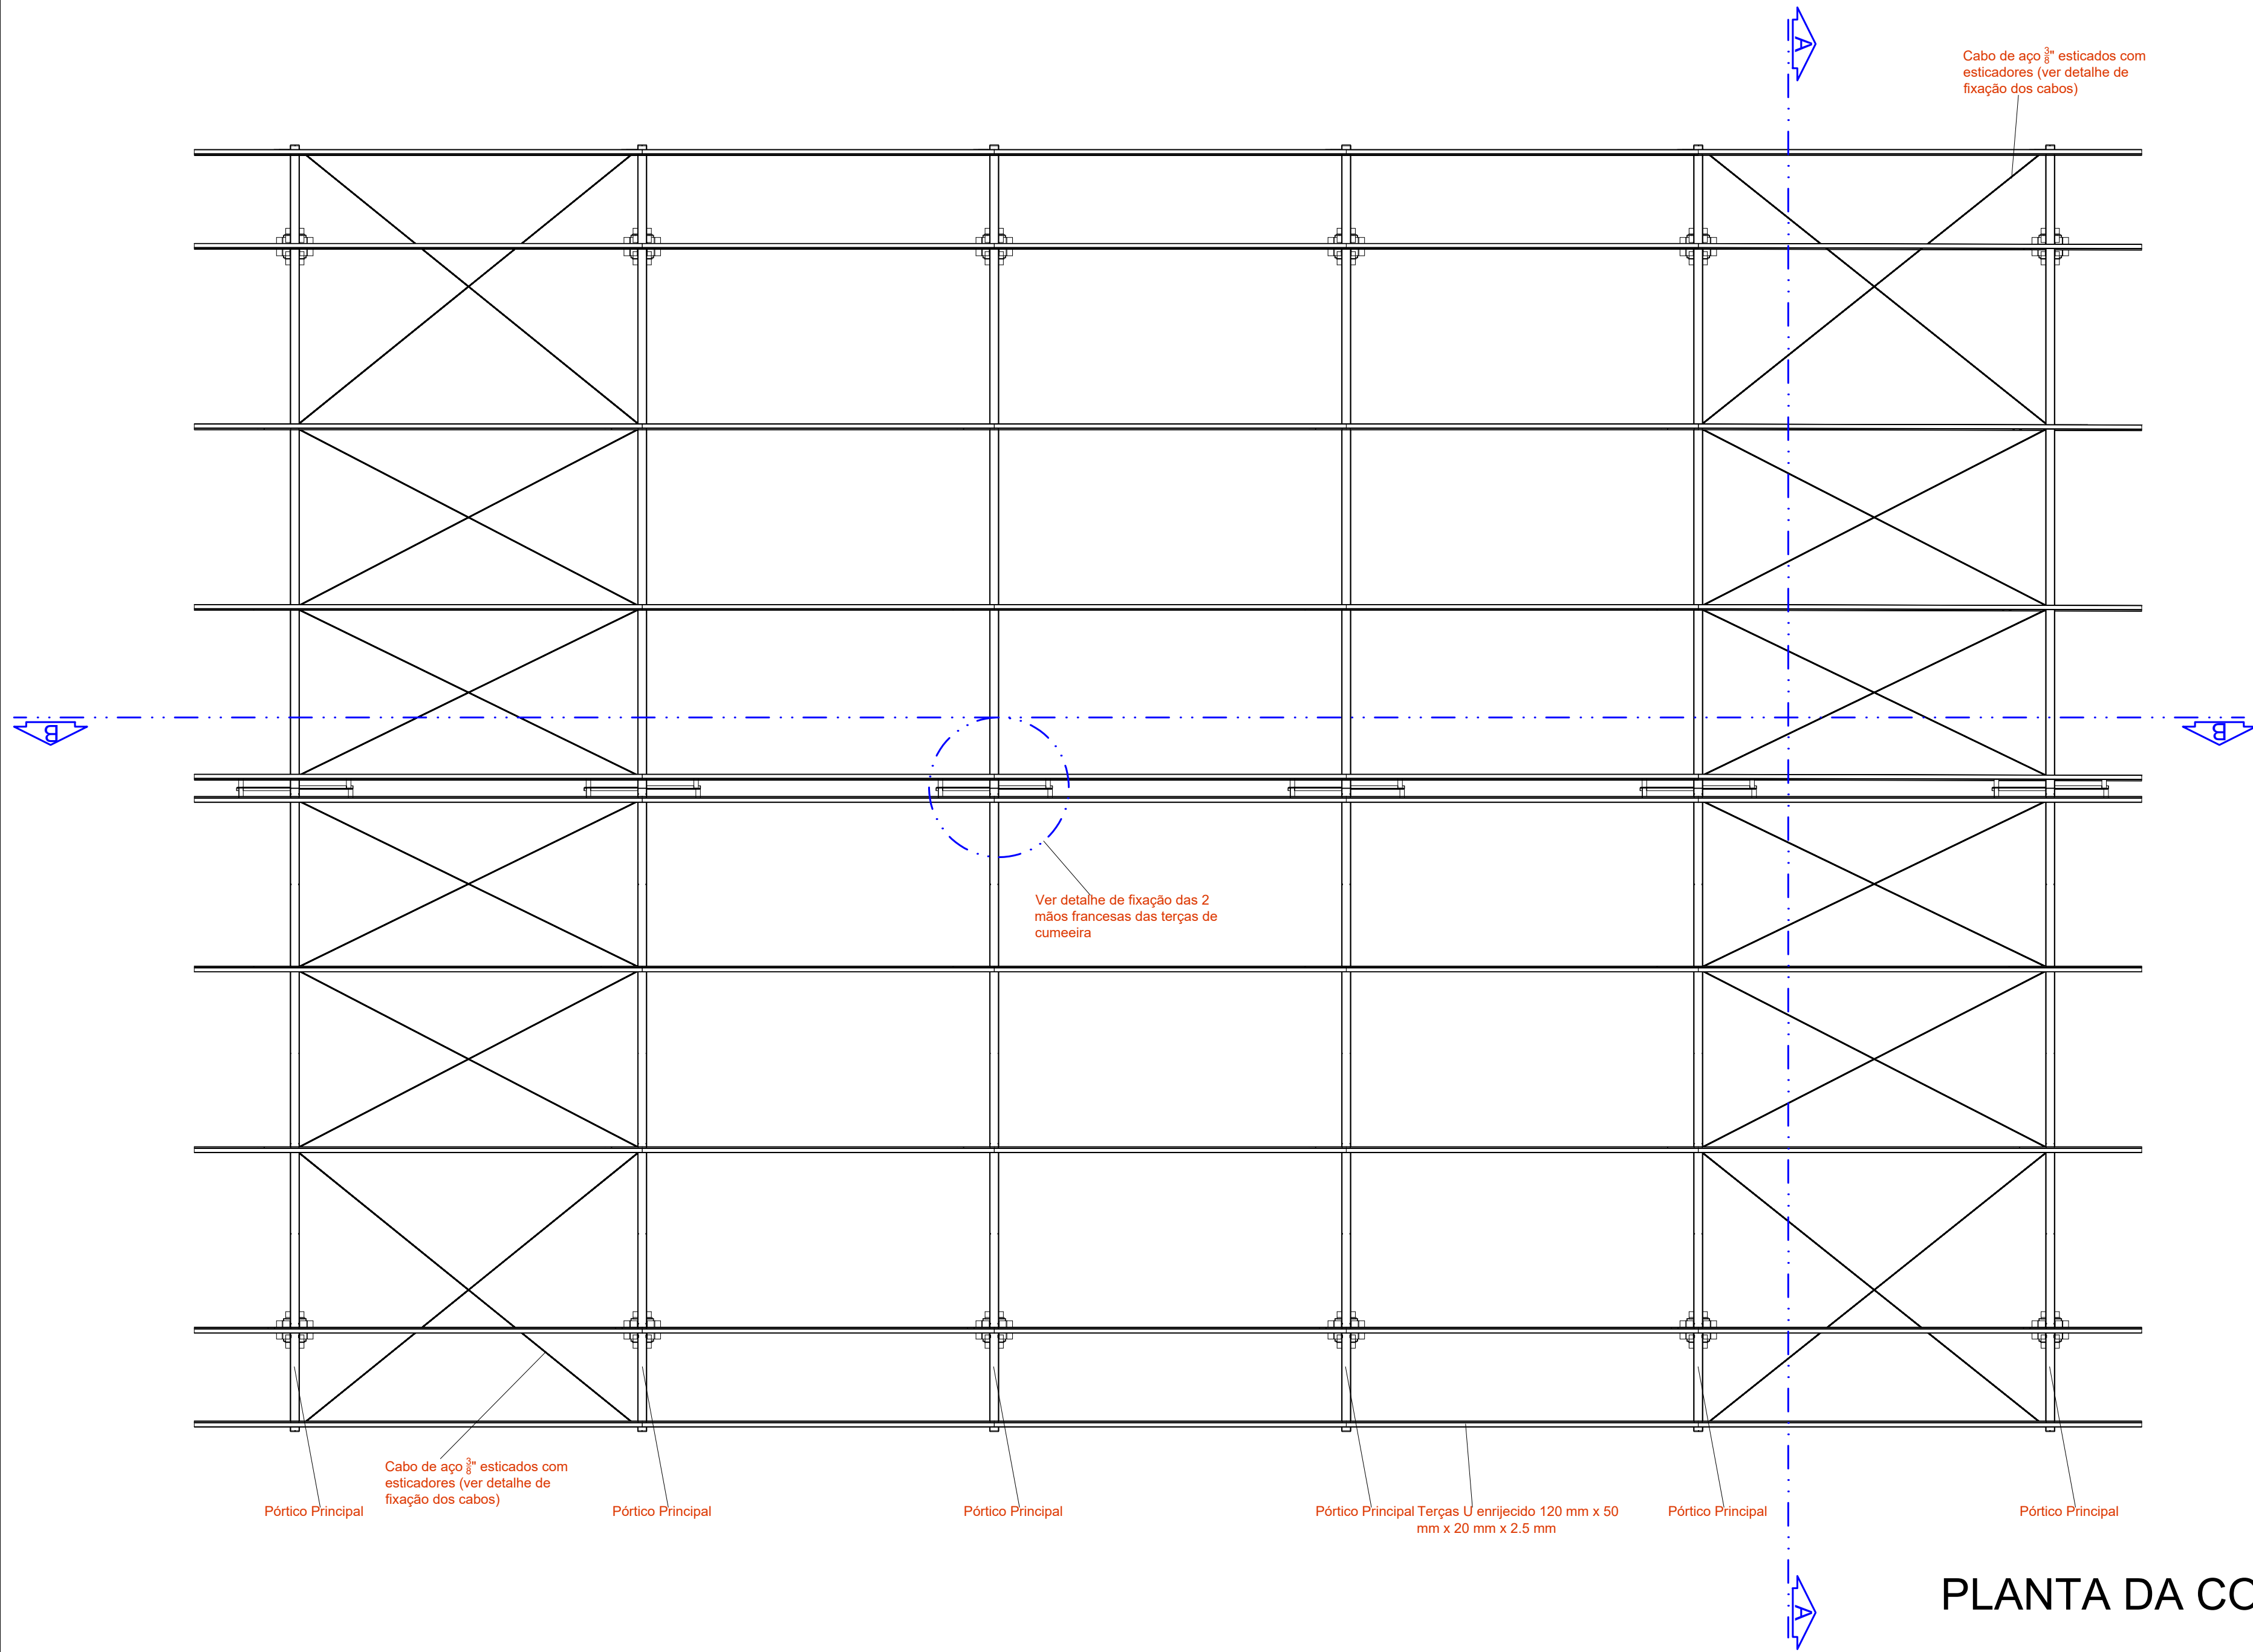
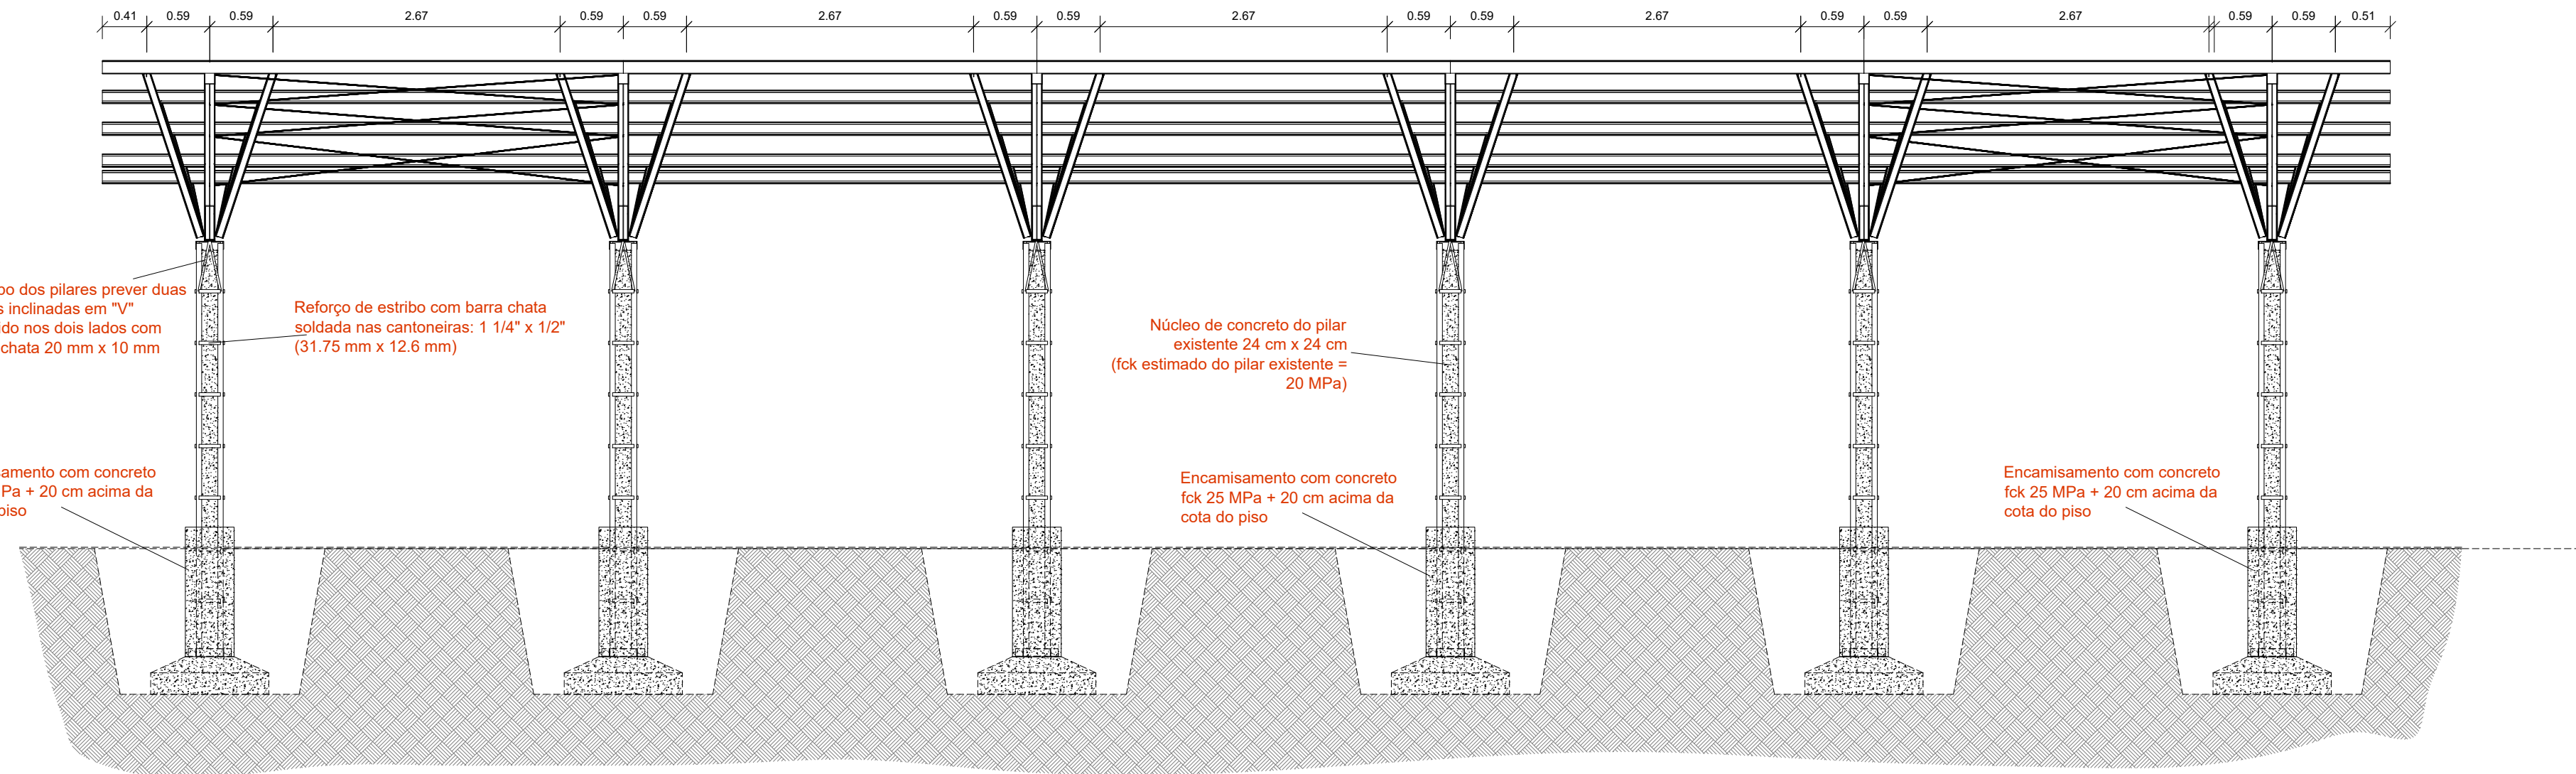


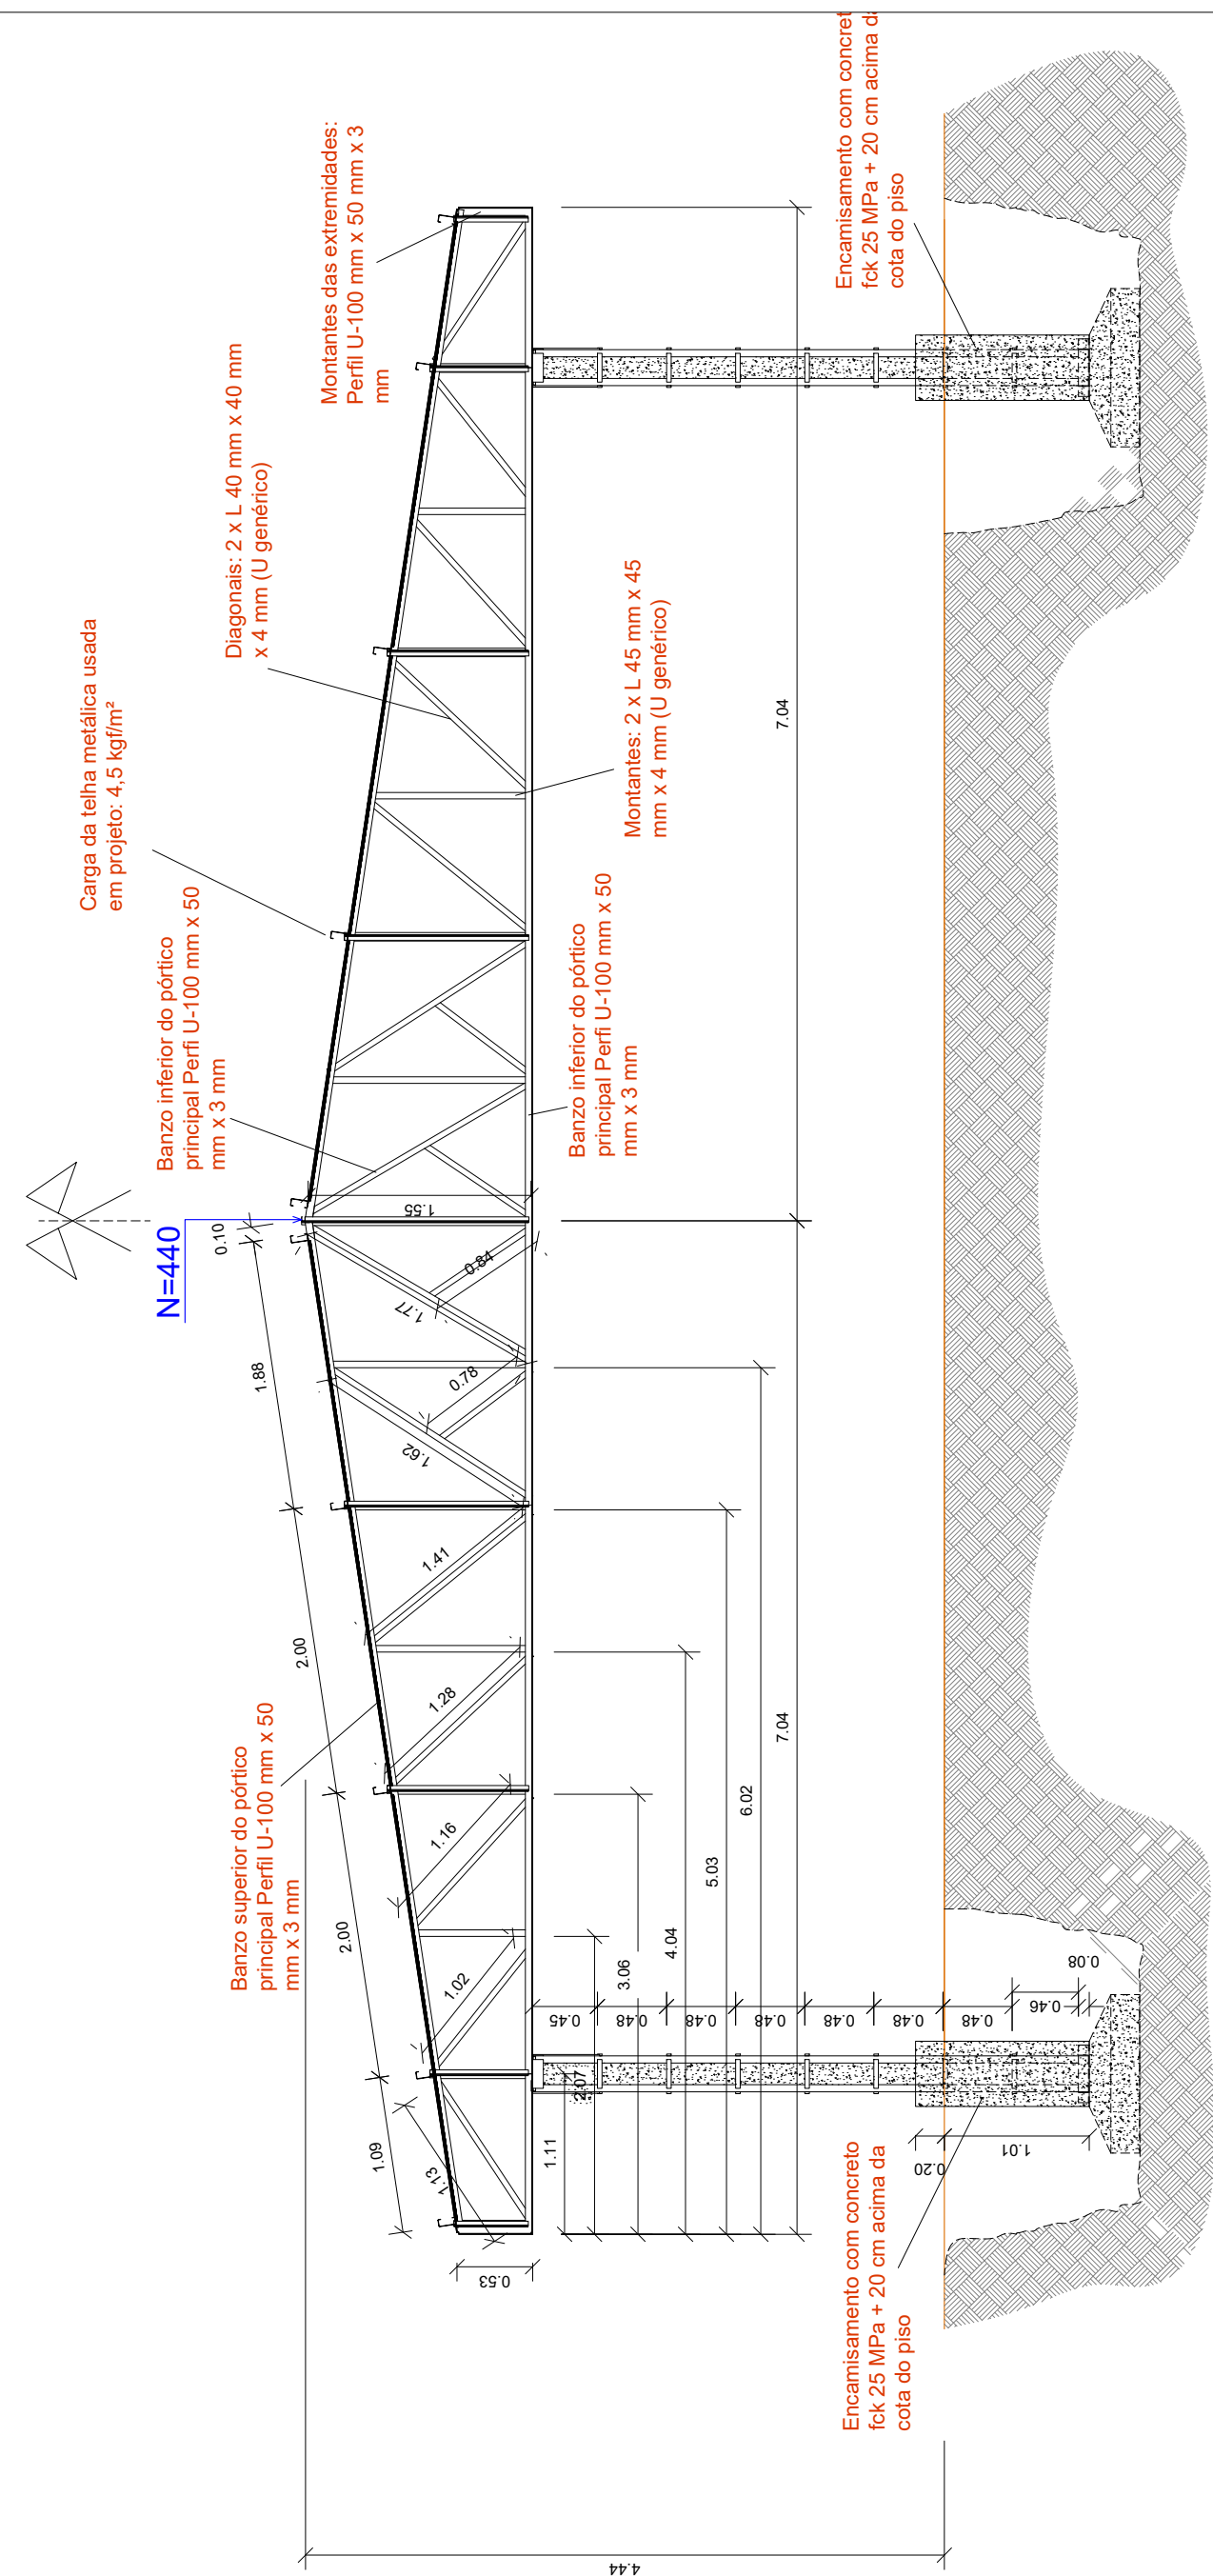

DETALHE DE FIXAÇÃO DOS CABOS

ESC 1:10

Comprimentos mínimos de Filetes de Soldas paralelos ao perfil:			
Peça	Tipo de Solda	Perna (mm)	Comprimento MÍNIMO
Diagonal 2xL em Banzo	Eletrodo E70 18	6 mm	2 x 6 cm (Em cada Cant.)
Montante 2xL em Banzo	Eletrodo E70 18	6 mm	2 x 3 cm (Em cada Cant.)

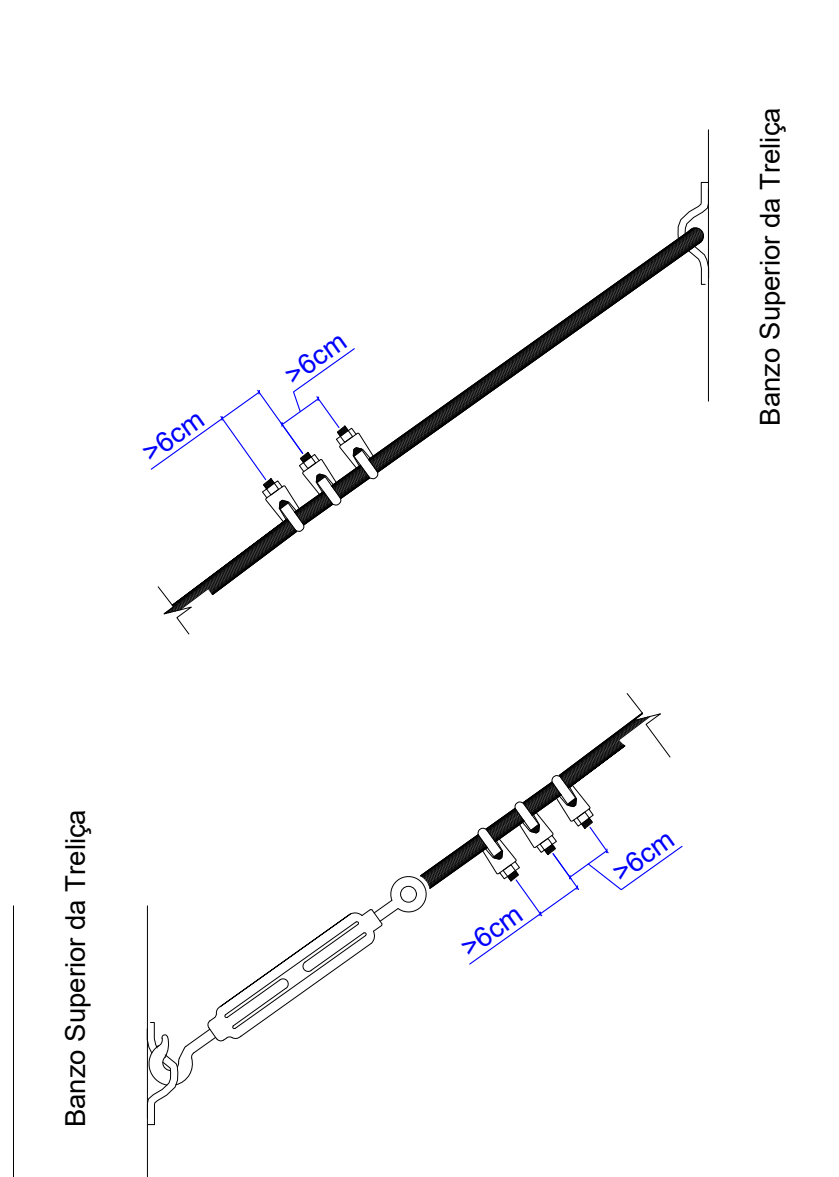

Mãos francesas das terças: 2 perfis em "V", Perfil U 80 mm x 40 mm x 5 mm

Apoio das 2 terças de cumeeira: Cantoneira L 50 mm x 50 mm x 5mm

DETALHE DE FIXAÇÃO DAS 2 MÃOS FRANCESAS DAS TERÇAS DE CUMEEIRA

S/ ESC

PROPRIETÁRIO: PREFEITURA MUNICIPAL DE COREMAS - PB			
LINCOLN CARTAXO DE LIRA JÚNIOR:06897861405		Assinado de forma digital por LINCOLN CARTAXO DE LIRA JÚNIOR:06897861405 Dados: 2025.08.11 13:52:57 -03'00'	
PROJETO: LINCOLN CARTAXO DE LIRA JÚNIOR CREA 160.814.689-B			
CONSTRUÇÃO: PROJETO DE REFORMA - GARAGEM DE CARROS			
FOLHA	PROJETO: PROJETO DE REFORMA - GARAGEM DE CARROS		
02/03	LOCALIDADE: MUNICÍPIO DE COREMAS - PB		
DATA	RESPONSÁVEL	RUBRICA	DADOS
DESIGNO	JUN/2025	LINCOLN CARTAXO	
COPIA			
VIETO			
ESCALAS	DESENHOS	CONVÊNIO	
INDICADAS	• PLANTA DE COBERTA • CORTE AA • CORTE BB • DETALHE DE FIXAÇÃO DAS 2 MÃOS FRANCESAS DAS TERÇAS DE CUMEEIRA	ARQUIVO	
Aprovações:			
LCL PROJETOS			
Av. Monteiro de Franco, 160, II. 030A Maracá, 30030-320 - João Pessoa (PB) Tel: +55 (81) 99694.4447 e-mail: lclprojetos@gmail.com			