


Mãos francesas das terças: 2 perfis em
Perfil U 80 mm x 40 mm x 5 mm (Estão
em todos os apoios TERÇAS - BANZO)

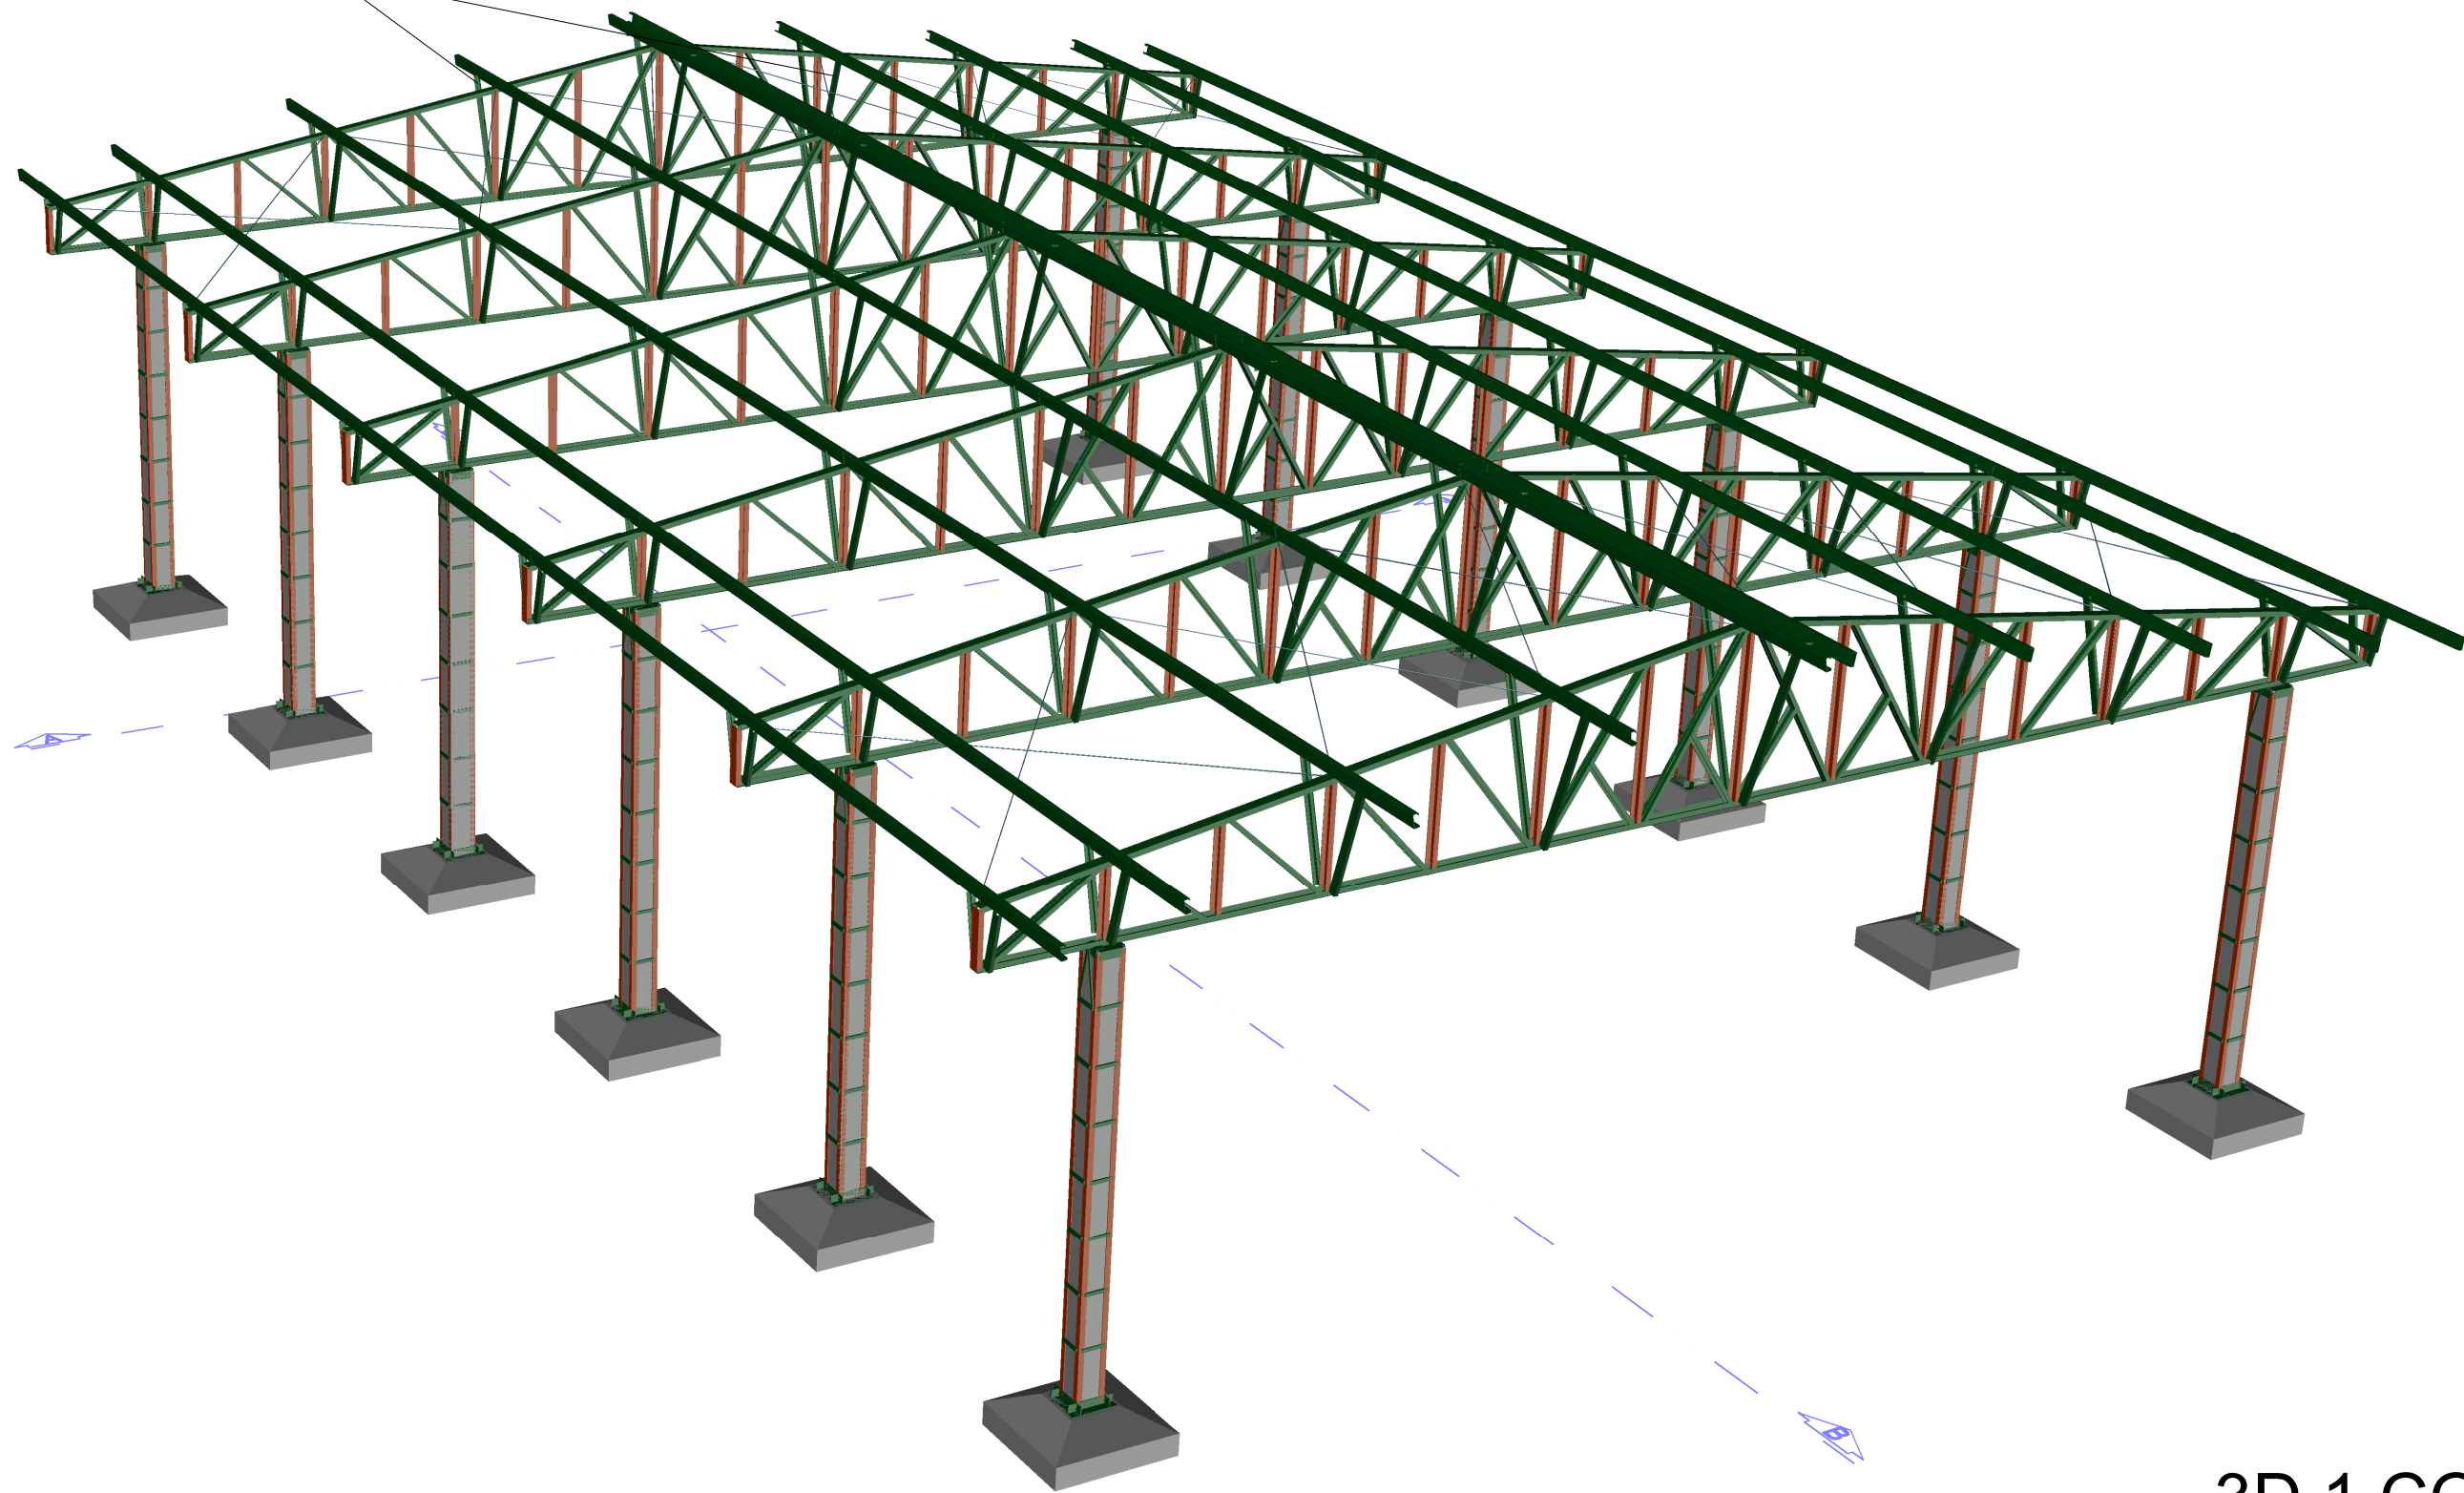


3D 1 COBERTA
ESC 1:50

1.1.1.5.- Tabela resumo

Tabela resumo															
Material		Série	Perfil	Comprimento			Volume			Peso					
Tipo	Designação			Perfil	Série	Material	(m)	Perfil	Série	Material	(m³)	Perfil	Série	Material	(kg)
Aço laminado	A-36 250Mpa	L	L 50 x 50 x 5		186.528		0.090				702.84				
			L 75 x 75 x 5		19.200		0.014				110.63				
			L 45 x 45 x 4, Duplo U união genérica		83.865		0.059				459.52				
			L 40 x 40 x 4, Duplo U união genérica		136.694		0.084				661.00				
			FL 1 1/4" x 1/2" (31.75 mm x 12.6 mm)		67.200	426.287		0.027	0.246		212.71	1933.98			
		Flat bars	FL 20 x 10		23.535			0.005			36.95				
			Cabo de Aço 3/8"		108.042		90.735		0.032		60.43	249.66			
						108.042		625.063		0.008	0.286	60.43	2244.08		
			U	U-100 mm x 50 mm x 3 mm		175.543		0.100			785.66				
				UF-80x5		104.083		0.073			575.10				
Aço dobrado	A-36	C	U enrijecido -120 mm x 50 mm x 20 mm x 2.5 mm		213.000	279.626	0.130	0.173		1017.49	1360.76				
					213.000	492.626	0.130	0.303		1017.49	2378.25				

1.1.1.6.- Quantitativos de superfícies

Perfis de aço: Quantitativos das superfícies a pintar					
Tipo	Série	Perfil	Superfície unitária (m²/m)	Comprimento (m)	Superfície (m²)
Aço laminado	L	L 50 x 50 x 5	0.200	186.528	37.306
		L 75 x 75 x 5	0.300	19.200	5.760
		L 45 x 45 x 4, Duplo U união genérica	0.360	83.865	30.191
		L 40 x 40 x 4, Duplo U união genérica	0.320	136.694	43.742
		FL 1 1/4" x 1/2" (31.75 mm x 12.6 mm)	0.089	67.200	5.974
	FL bars		FL 20 x 10	0.060	23.535
Cabo de Aço		Cabo de Aço 3/8"	0.030	108.042	3.233
				Subtotal	127.618
Aço dobrado	U	U-100 mm x 50 mm x 3 mm	0.386	175.543	67.775
		UF-80x5	0.292	104.083	30.345
	C	U enrijecido - 120 mm x 50 mm x 20 mm x 2.5 mm	0.492	213.000	104.762
				Subtotal	202.881
				Total	330.499

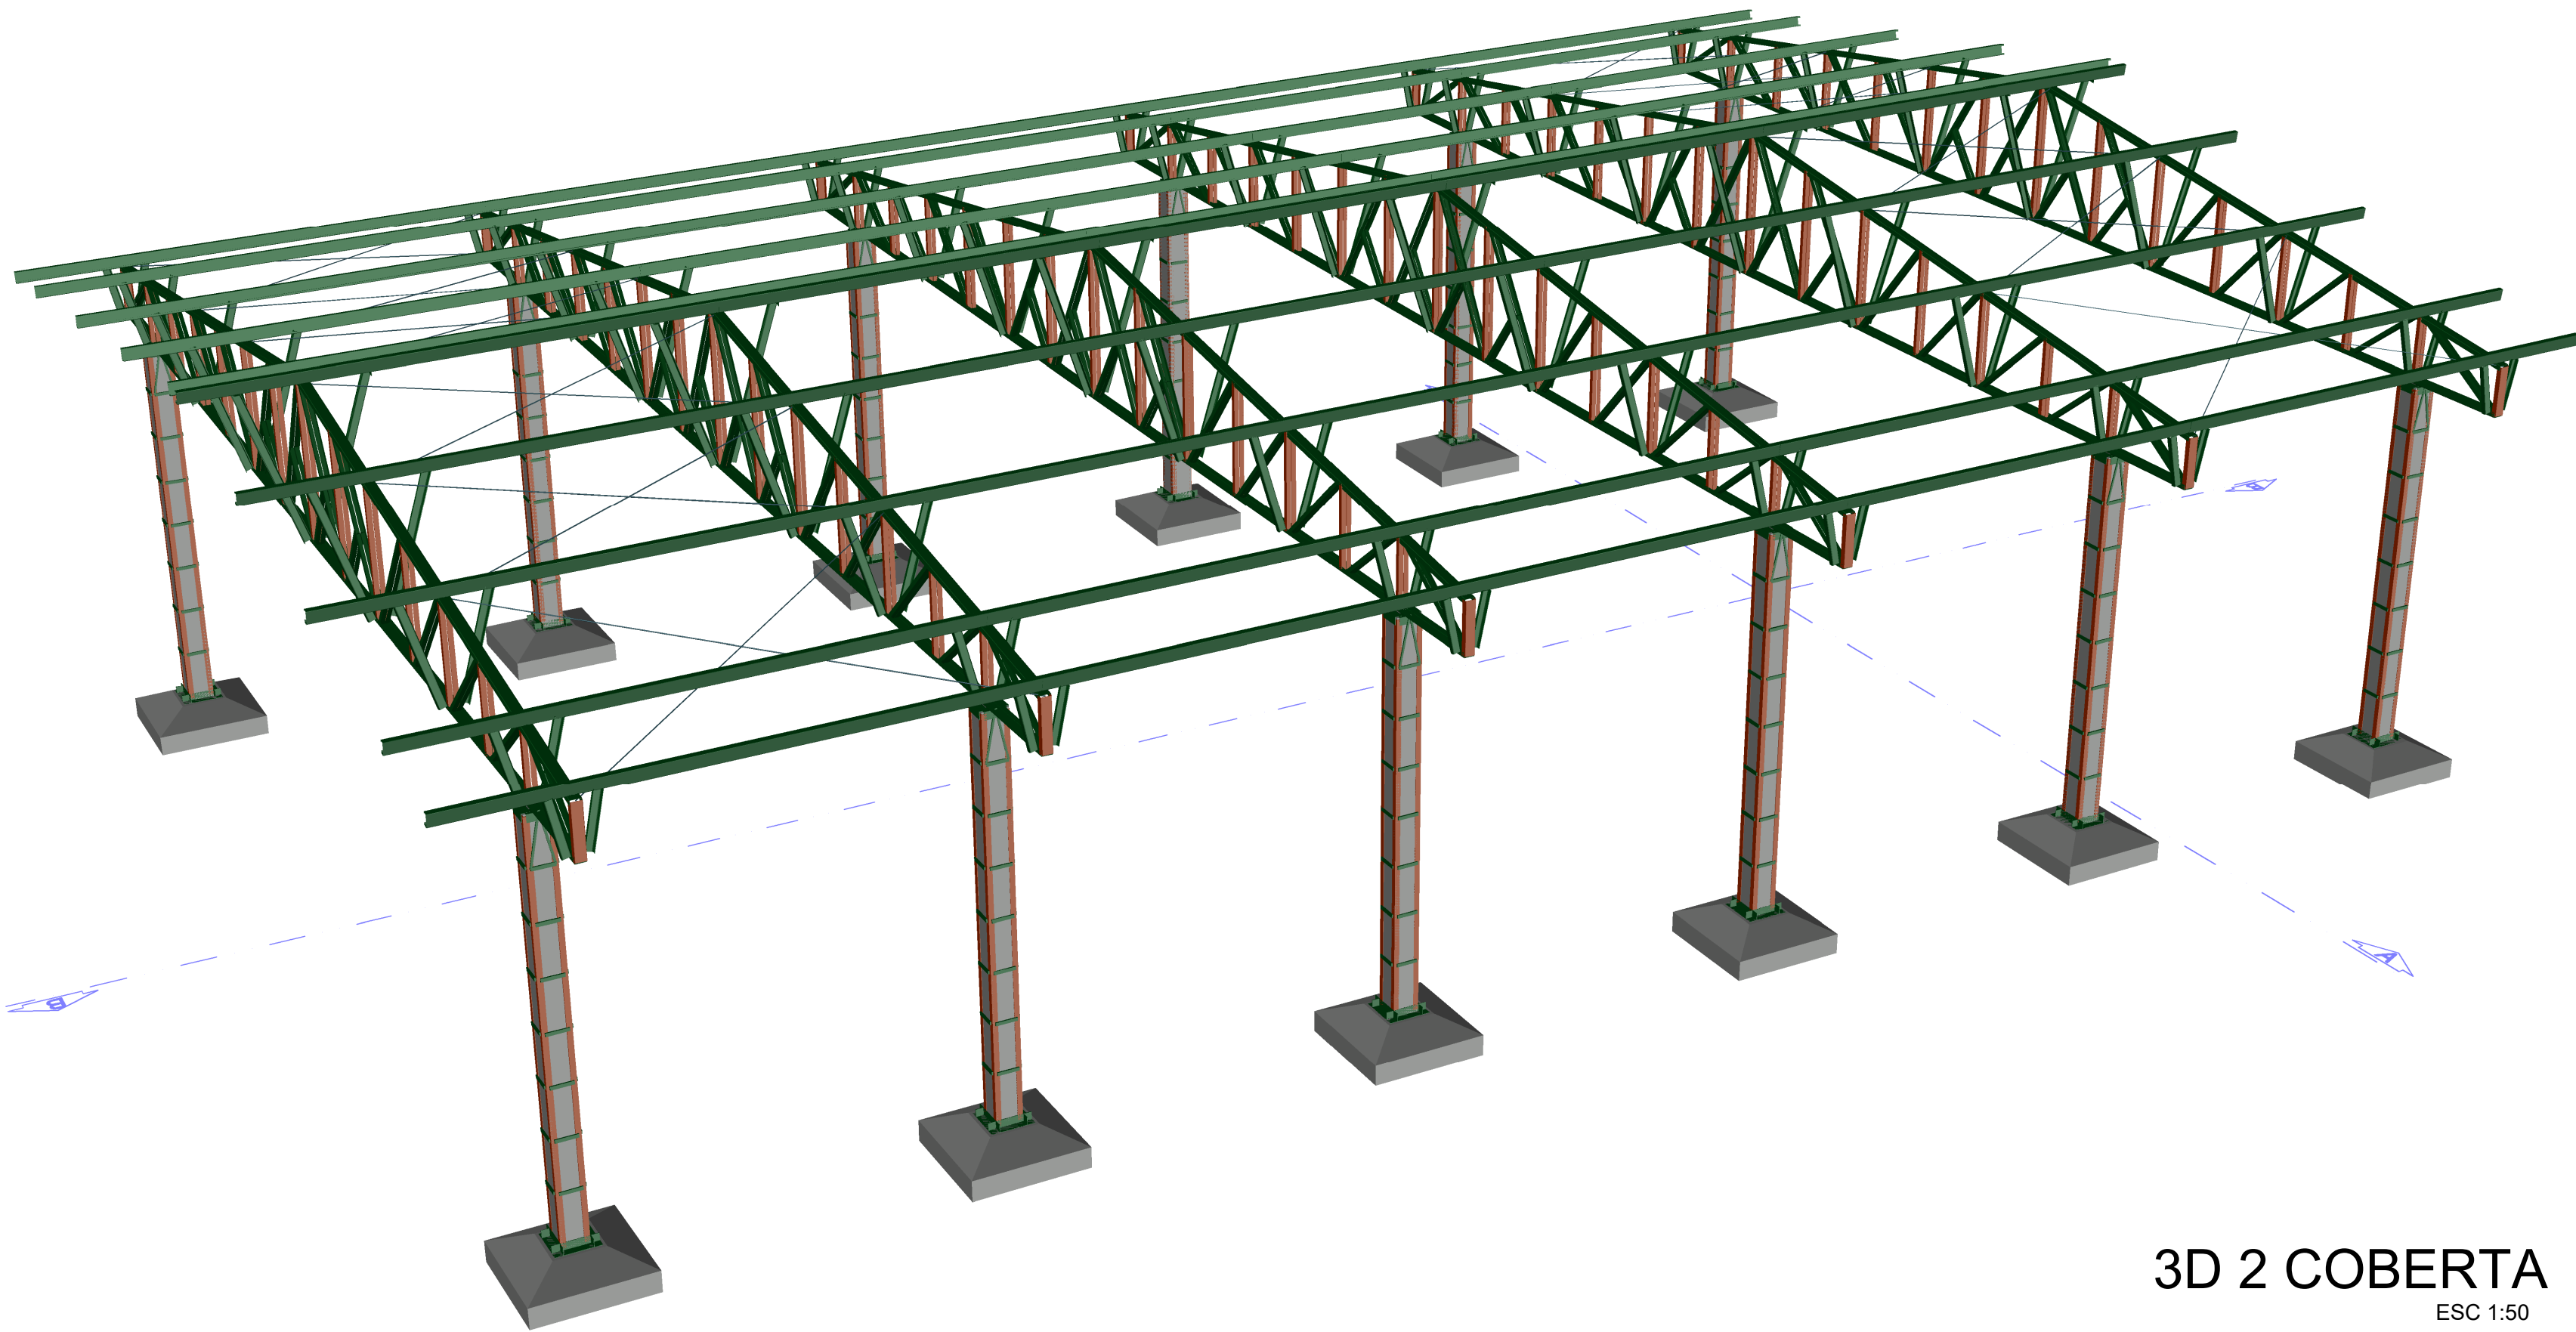

3D 2 COBERTA
ESC 1:50

PROPRIETÁRIO: PREFEITURA MUNICIPAL DE COREMAS - PB
LINCOLN CARTAXO DE LIRA JUNIOR:06897861405
Assinado de forma digital por LINCOLN CARTAXO DE LIRA JUNIOR:06897861405
Dados: 2025.08.11 13:54:09 -03'00'

PROJETO: LINCOLN CARTAXO DE LIRA JÚNIOR CREA 160.814.689-B

CONSTRUÇÃO: PROJETO DE REFORMA - GARAGEM DE CARROS

PROJETO: PROJETO DE REFORMA - GARAGEM DE CARROS

LOCALIDADE: MUNICÍPIO DE COREMAS - PB

DESENHO: JUN 2025 RESPONSÁVEL: LINCOLN CARTAXO RUBRICA: DIADOS

COPIA: VISTO:

ESCALAS: DESENHOS: 3D 1 DA COBERTA 3D 2 DA COBERTA RESUMO DE MATERIAIS CONVÊNIO

INDICADAS: ARQUIVO

Aprovações: