



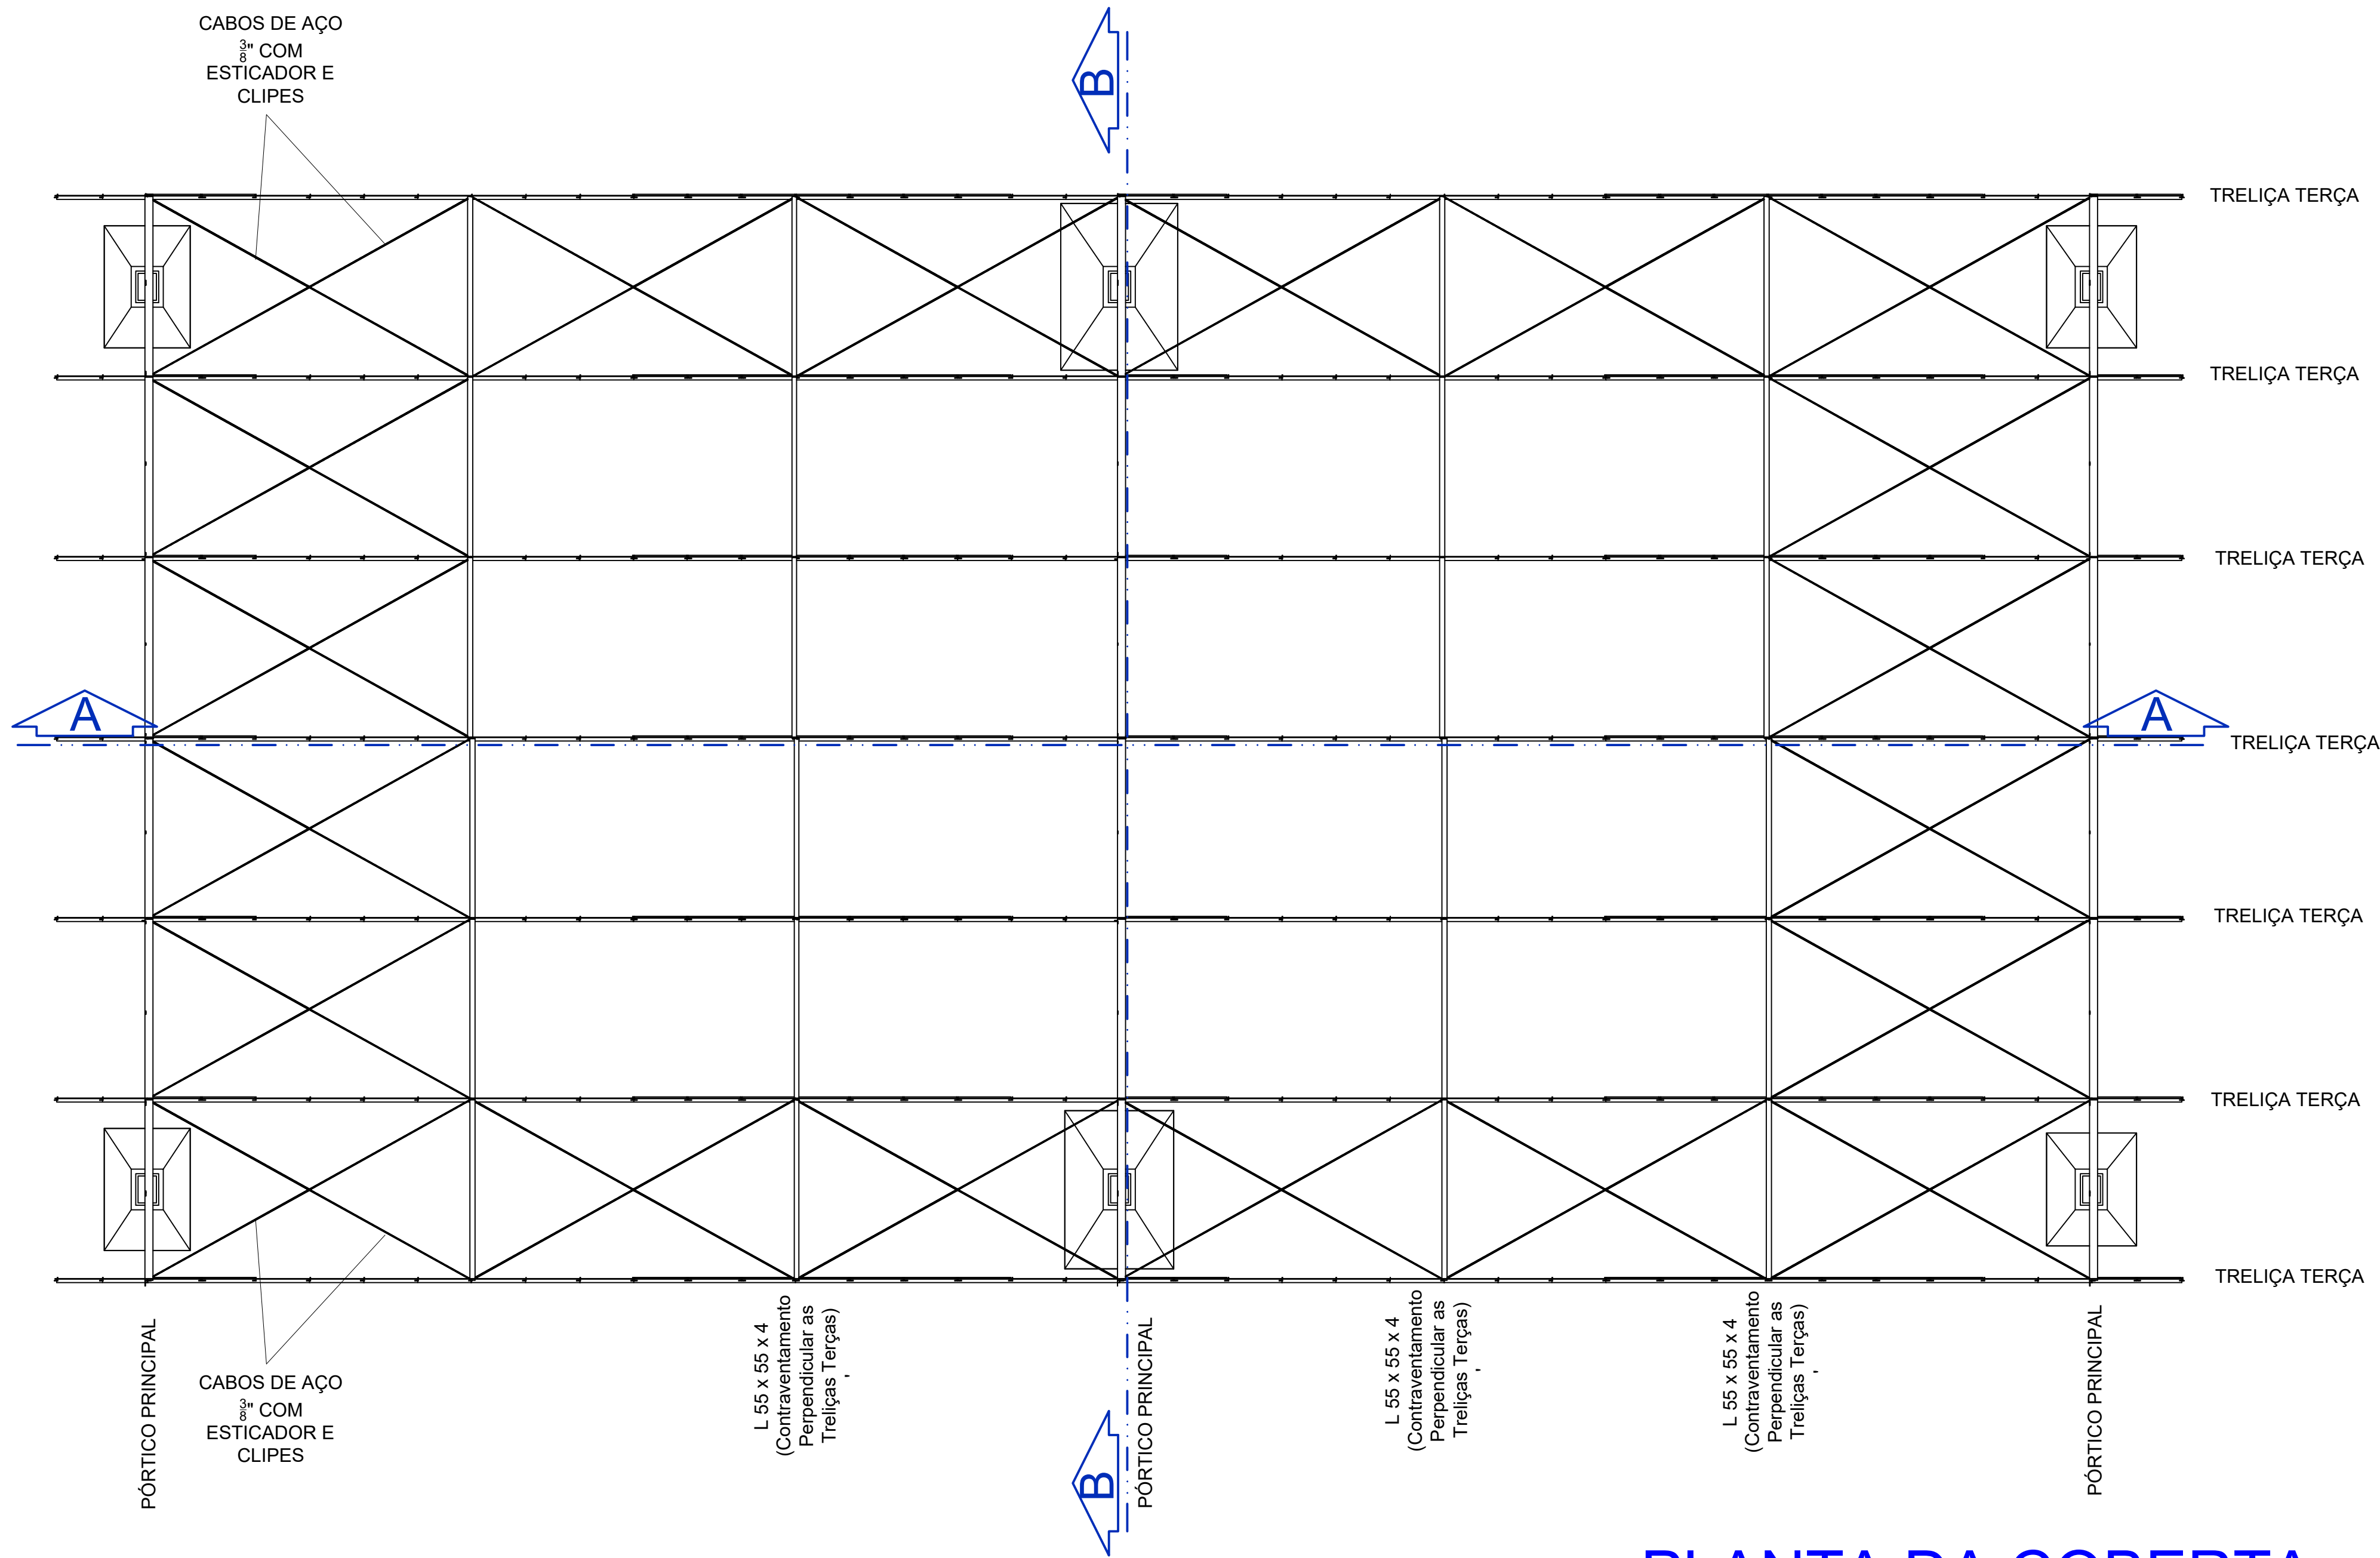

PLANTA DA COBERTA
Escala 1/75

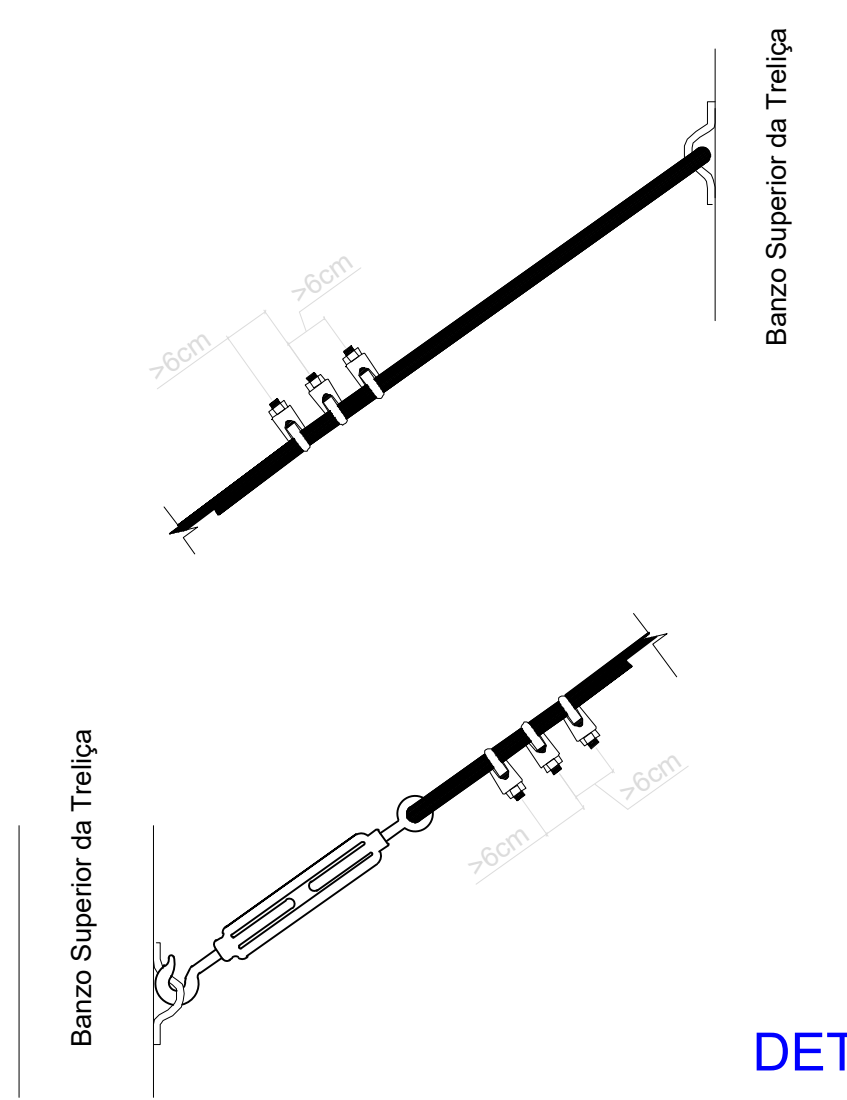

DETALHE DO ESTICADOR
Escala 1/10

ORIENTAÇÕES PARA PINTURA DE ESTRUTURA METÁLICA (AÇO A36)

As seguintes etapas devem ser rigorosamente seguidas para a pintura dos perfis metálicos, conforme NBR 16204 (Preparação de Superfícies de Aço) e NBR 15962 (Pintura Industrial). O sistema de pintura visa garantir proteção anticorrosiva e durabilidade, adequado ao ambiente de exposição C3 (média corrosividade, conforme NBR 14643).

PREPARAÇÃO DA SUPERFÍCIE

Realizar limpeza inicial para remover óleos, graxas e contaminantes, utilizando desengraxante conforme NBR 16204, método SP 1 (limpeza com solvente).

Executar jateamento abrasivo ao grau Sa 2½ (NBR 16204, equivalente a ISO 8501-1), removendo ferrugem, carepa de laminação e impurezas. Alternativamente, usar lixamento mecânico (escovas de aço ou lixas) até atingir superfície metálica limpa.

Garantir rugosidade de 25 a 50 µm (perfil de ancoragem), conforme NBR 16204, para aderência do revestimento.

Inspeccionar a superfície, garantindo ausência de poeira, umidade ou contaminantes antes da pintura.

APLICAÇÃO DO PRIMER

Aplicar uma camada de primer epóxi com fosfato de zinco, com espessura de filme seco (DFT) de 50 a 75 µm, conforme especificação do fabricante.

Utilizar pistola airless, rolo ou pincel, garantindo aplicação uniforme em todas as faces dos perfis.

Respeitar o tempo de secagem do primer (4 a 24 horas, conforme ficha técnica), verificando condições ambientais (temperatura entre 10°C e 35°C, umidade relativa < 85%, superfície 3°C acima do ponto de orvalho).

APLICAÇÃO DA TINTA EPÓXI

Aplicar duas camadas de tinta epóxi de alta espessura (dois componentes: resina + catalisador), totalizando DFT de 100 a 150 µm, conforme NBR 15962.

Misturar os componentes na proporção INDICADAS pelo fabricante e aplicar com pistola airless, rolo ou pincel, garantindo cobertura homogênea.

Aguardar intervalo de 12 a 24 horas entre camadas, conforme ficha técnica, mantendo condições ambientais adequadas.

ACABAMENTO (OPCIONAL)

Para proteção contra raios UV e maior durabilidade em ambientes externos, aplicar uma camada de poliuretano alifático (DFT de 50 a 75 µm) após cura parcial da epóxi (12 a 24 horas).

Seguir instruções do fabricante para aplicação e cura.

CONDIÇÕES DE APLICAÇÃO

Garantir ventilação adequada durante a aplicação e cura, especialmente em ambientes internos.

Monitorar condições ambientais conforme NBR 15962, evitando pintura em superfícies úmidas ou sob chuva.

Verificar espessura do filme seco (DFT) com medidor apropriado, conforme NBR 16204, AÇO 3/8"443.

INSPEÇÃO FINAL

Realizar inspeção visual para verificar ausência de falhas (bolhas, crateras ou descascamento).

Confirmar aderência do revestimento, se necessário, por teste conforme NBR 11003 (método de corte em grade).

Garantir cura total do sistema (7 dias, conforme fabricante) antes da exposição a condições severas.

NOTAS:


Consultar fichas técnicas dos produtos para proporções, tempos de cura e espessuras.

Para ambientes de maior corrosividade (C4 ou C5), consultar projetista para adequação do sistema.


Manter registros de aplicação (lotes, condições ambientais, espessuras) para controle de qualidade.

Cargas consideradas em projeto:

- Peso próprio da telha: 4,5 kg/m² (TP 40 que vence vãos entre terças de 2,40 m);
- Peso próprio de instalações elétricas e luminárias: 0,21 kg/m²
- Fofo: NÃO INCLUSO

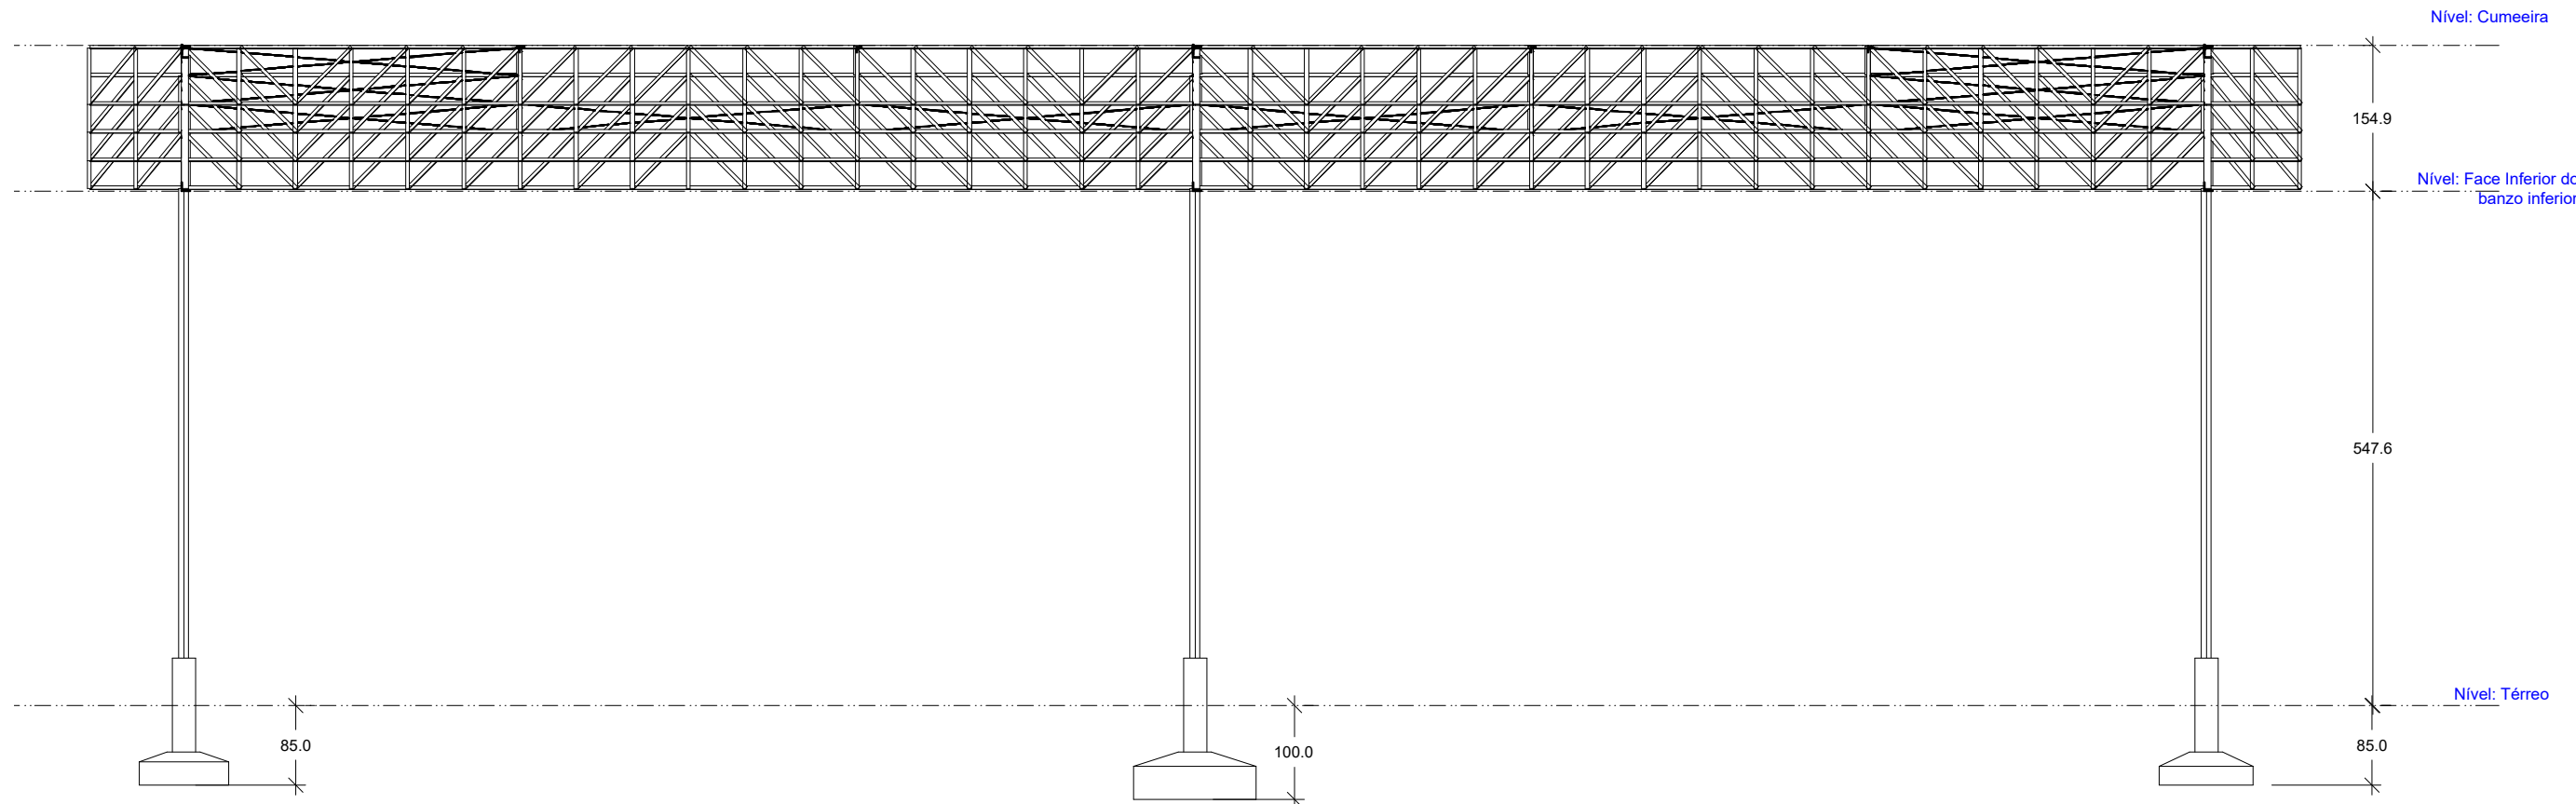

CORTE AA
Escala 1/75

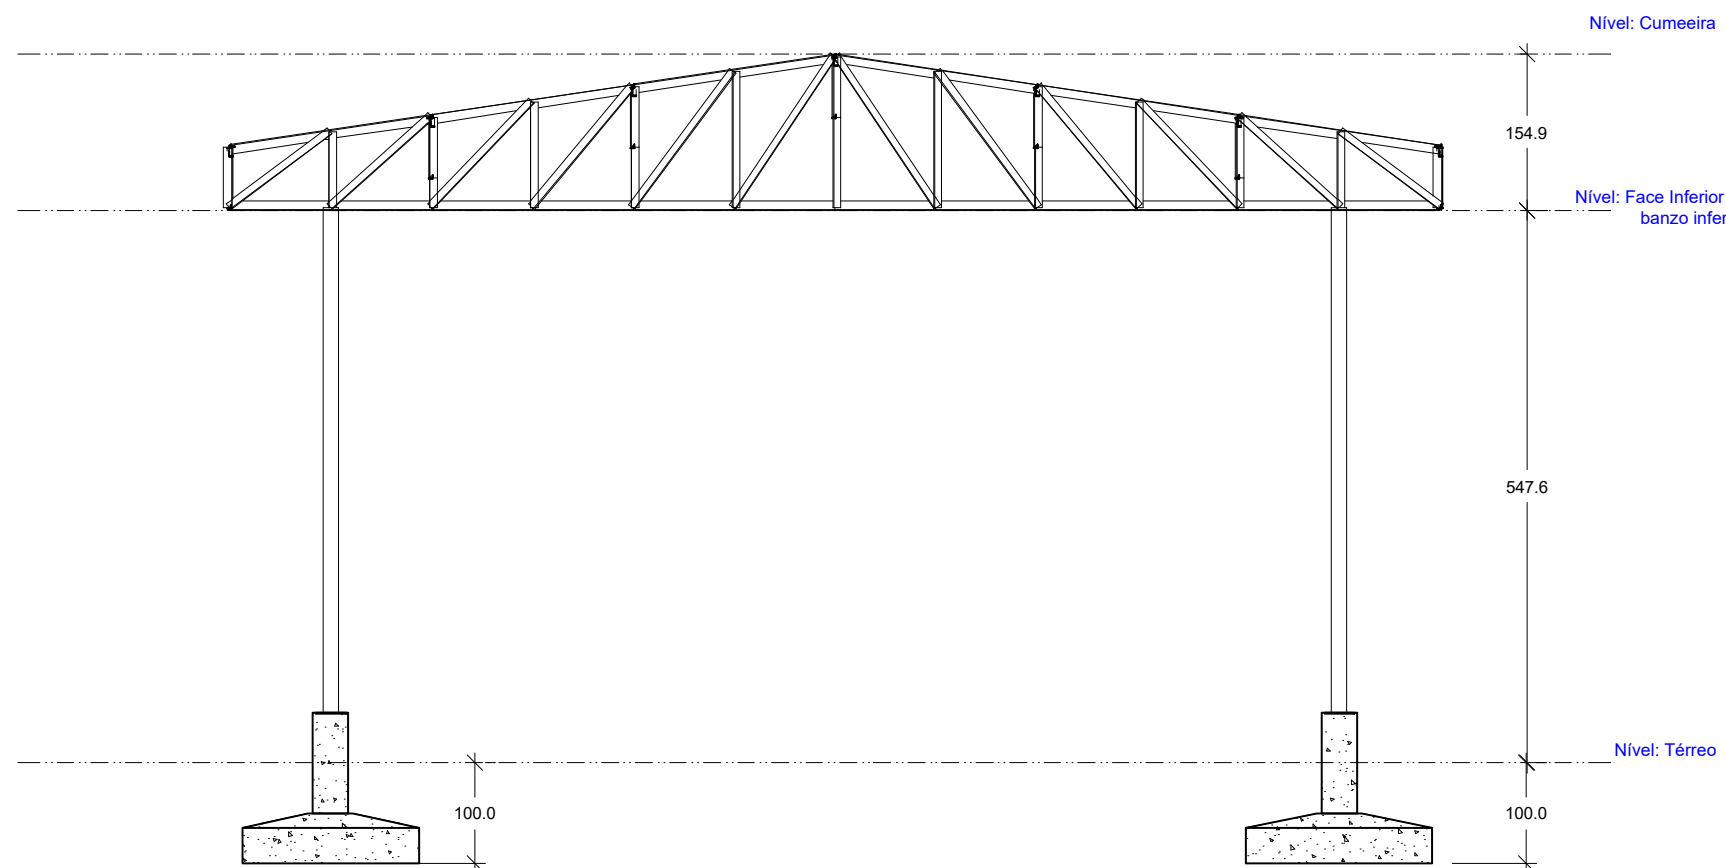

CORTE BB
Escala 1/75

PROPRIETÁRIO: PREFEITURA MUNICIPAL DE COREMAS - PB			
PROJETO: LINCOLN CARTAXO DE LIRA JÚNIOR CREA 160.814.689-8			
CONSTRUÇÃO: PROJETO DE ESTRUTURAL - GARAGEM DAS MÁQUINAS - COREMAS/PB			
FOLHA	PROJETO: PROJETO DE ESTRUTURAL - GARAGEM DAS MÁQUINAS - COREMAS/PB		
(2)/03	LOCALIDADE: MUNICÍPIO DE COREMAS - PB		
DESENHO	DATA	RESPONSÁVEL	RUBRICA
CÓPIA	JUL/2025	LINCOLN CARTAXO	DADOS
VISTO			
ESCALAS	DESENHOS		CONVÊNIO
INDICADAS	• Planta de Coberta		ARQUIVO:
	• Det. Esticador de contraventamento em "X"		
	• Corte AA		
	• Corte BB		
Aprovações:			
LCL PROJETOS			
Av. Monteiro de Franco, 160, sl. 005A Maranhão, 55038-320 - João Pessoa (PB) Tel: +55 (83) 99244.4447 e-mail: lclprojetos@hotmail.com			