




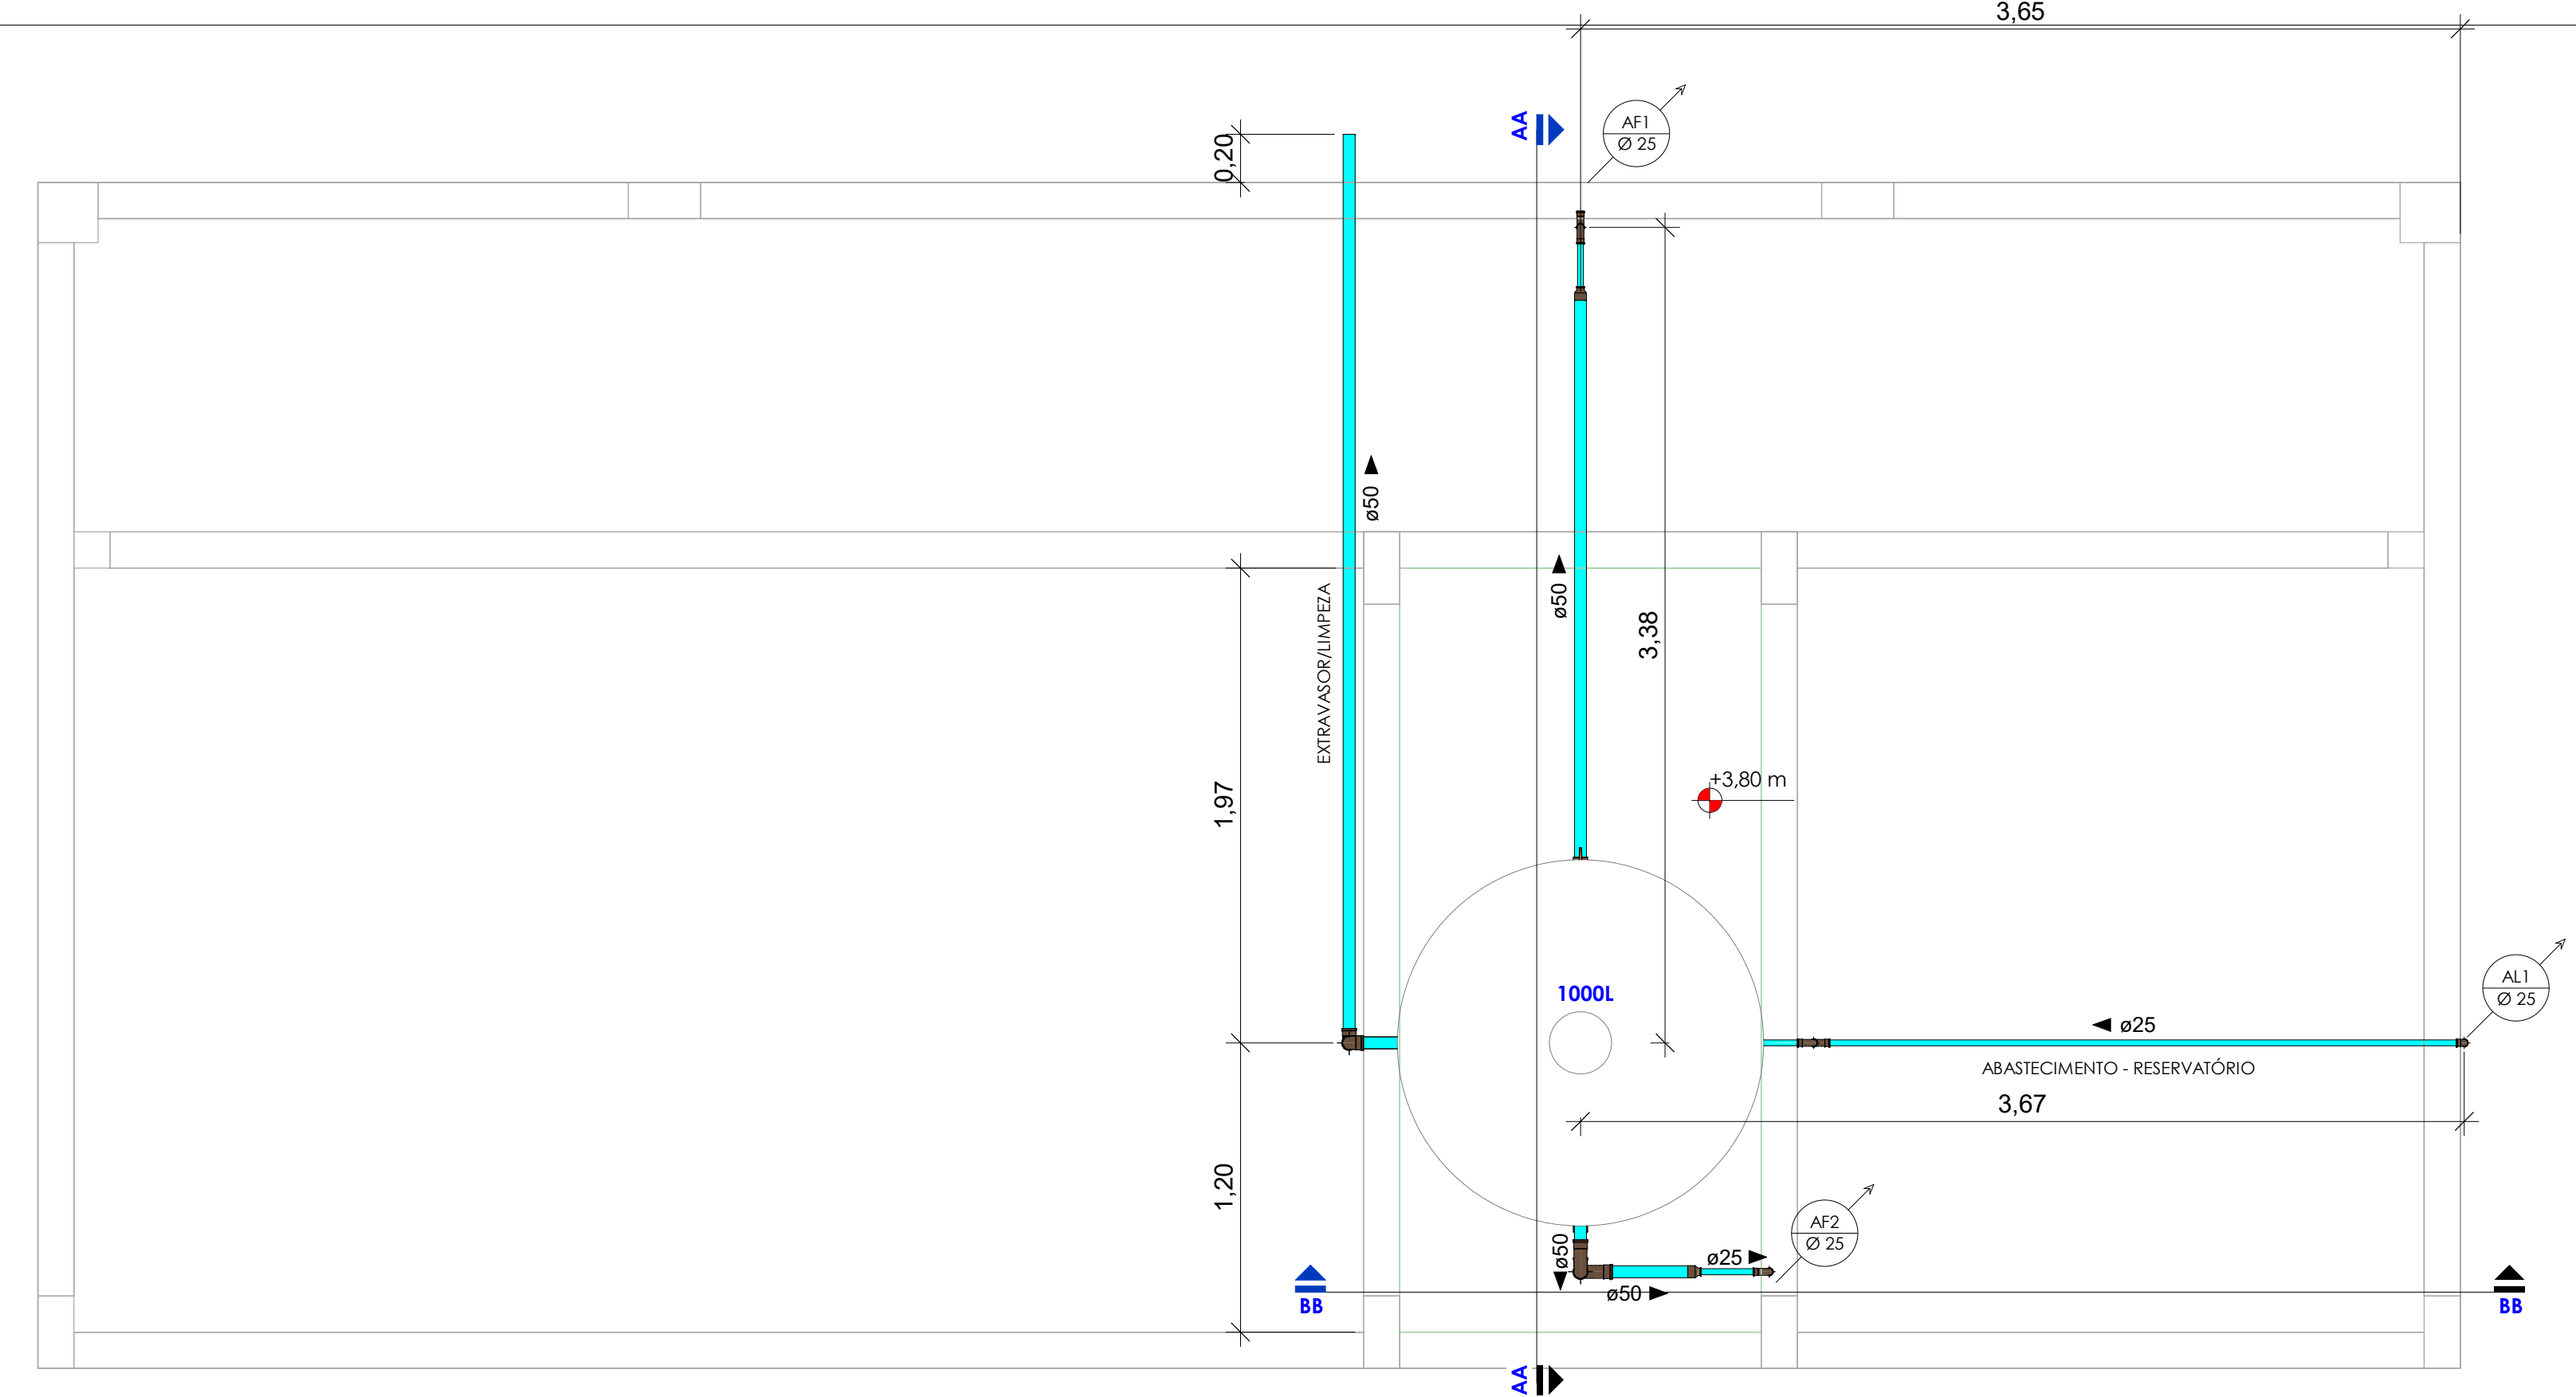


PLANTA BAIXA_ COBERTA - CAIXA_ D'ÁGUA_01 - ESC 1/25

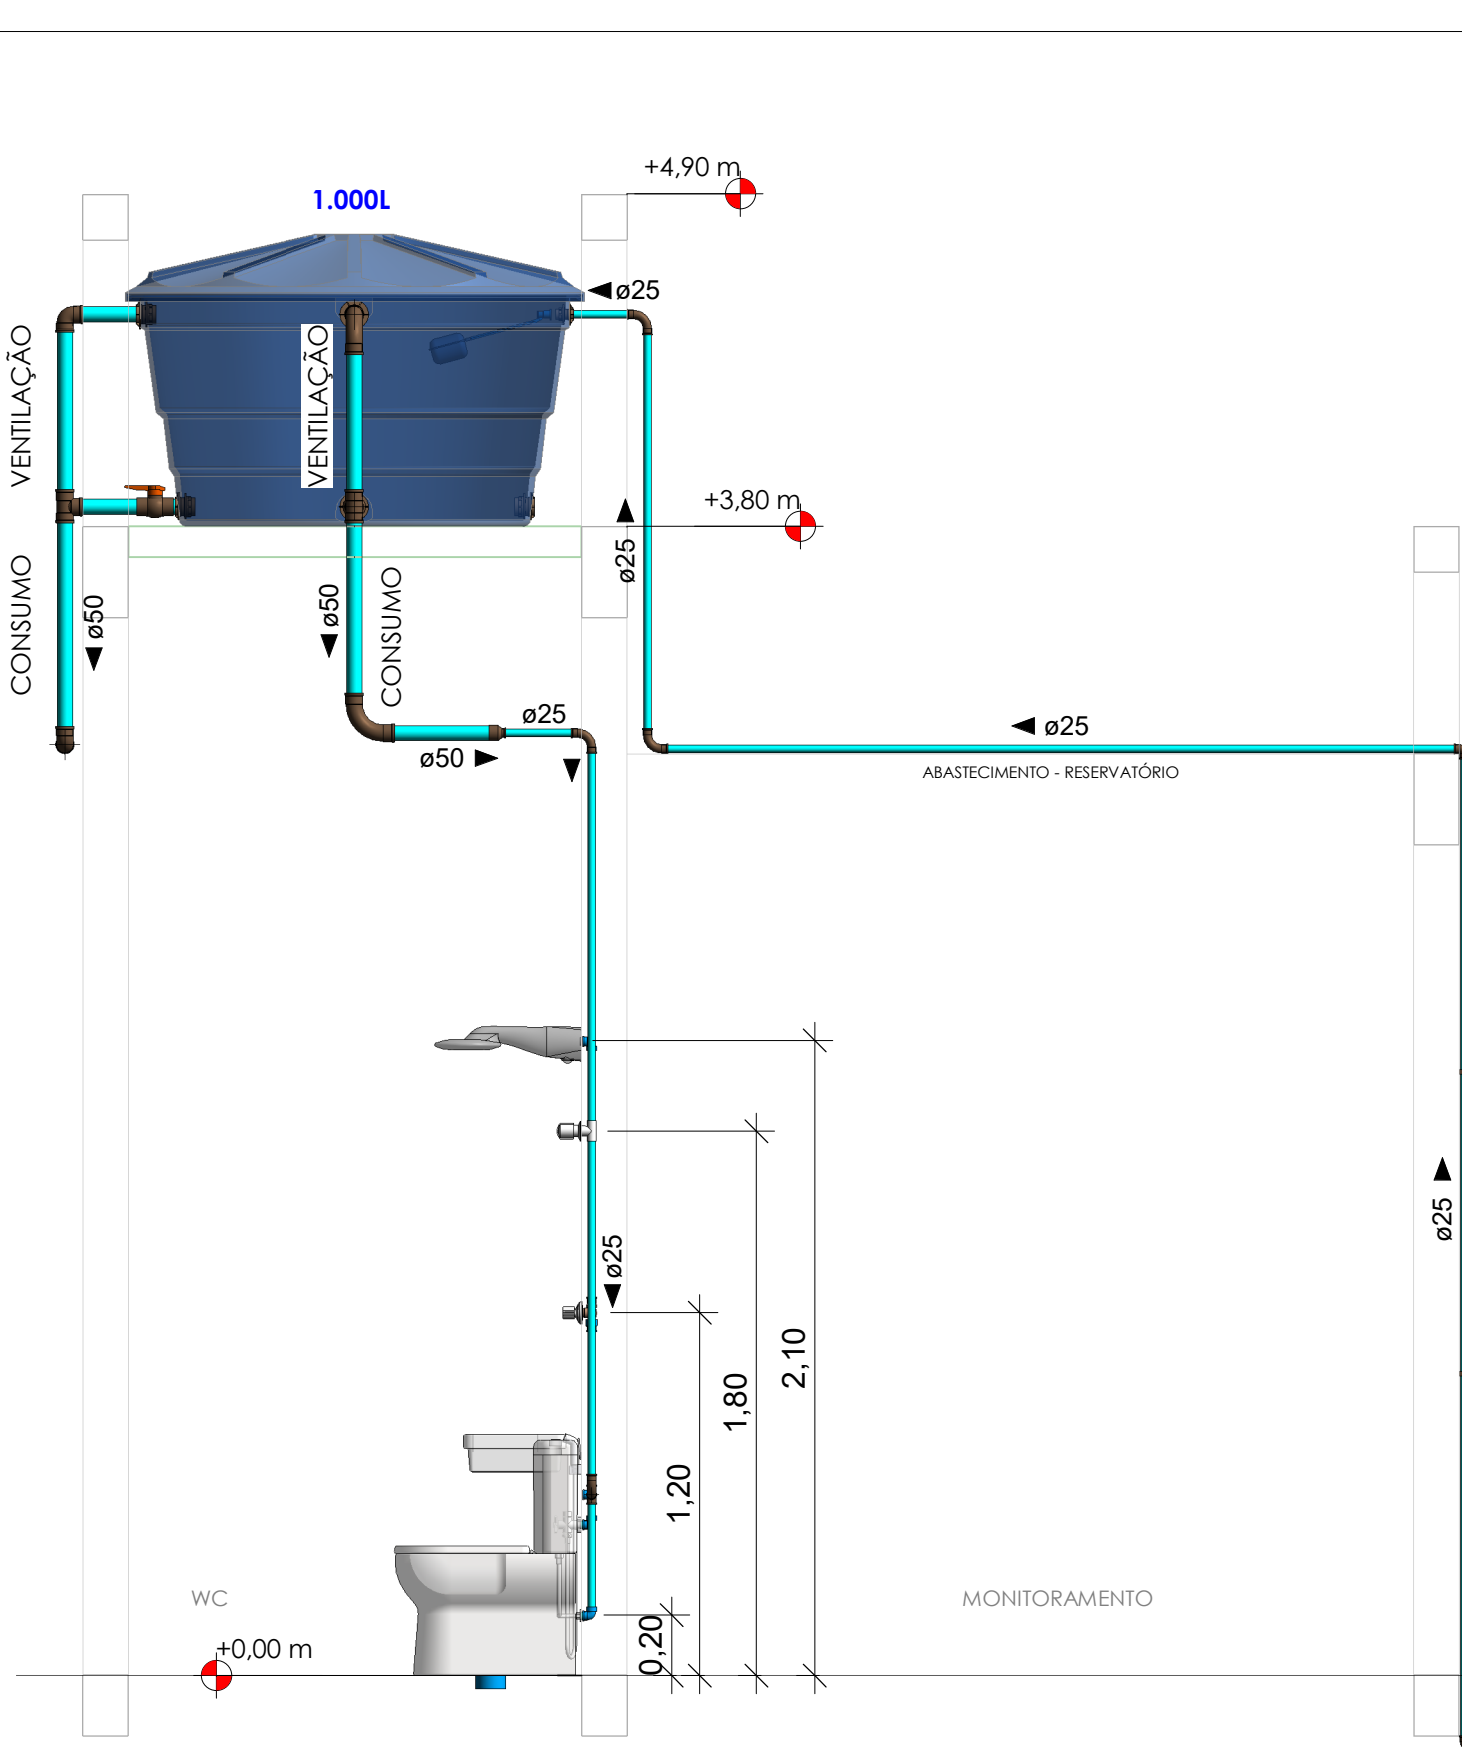


CORTE BB ESC 1/25

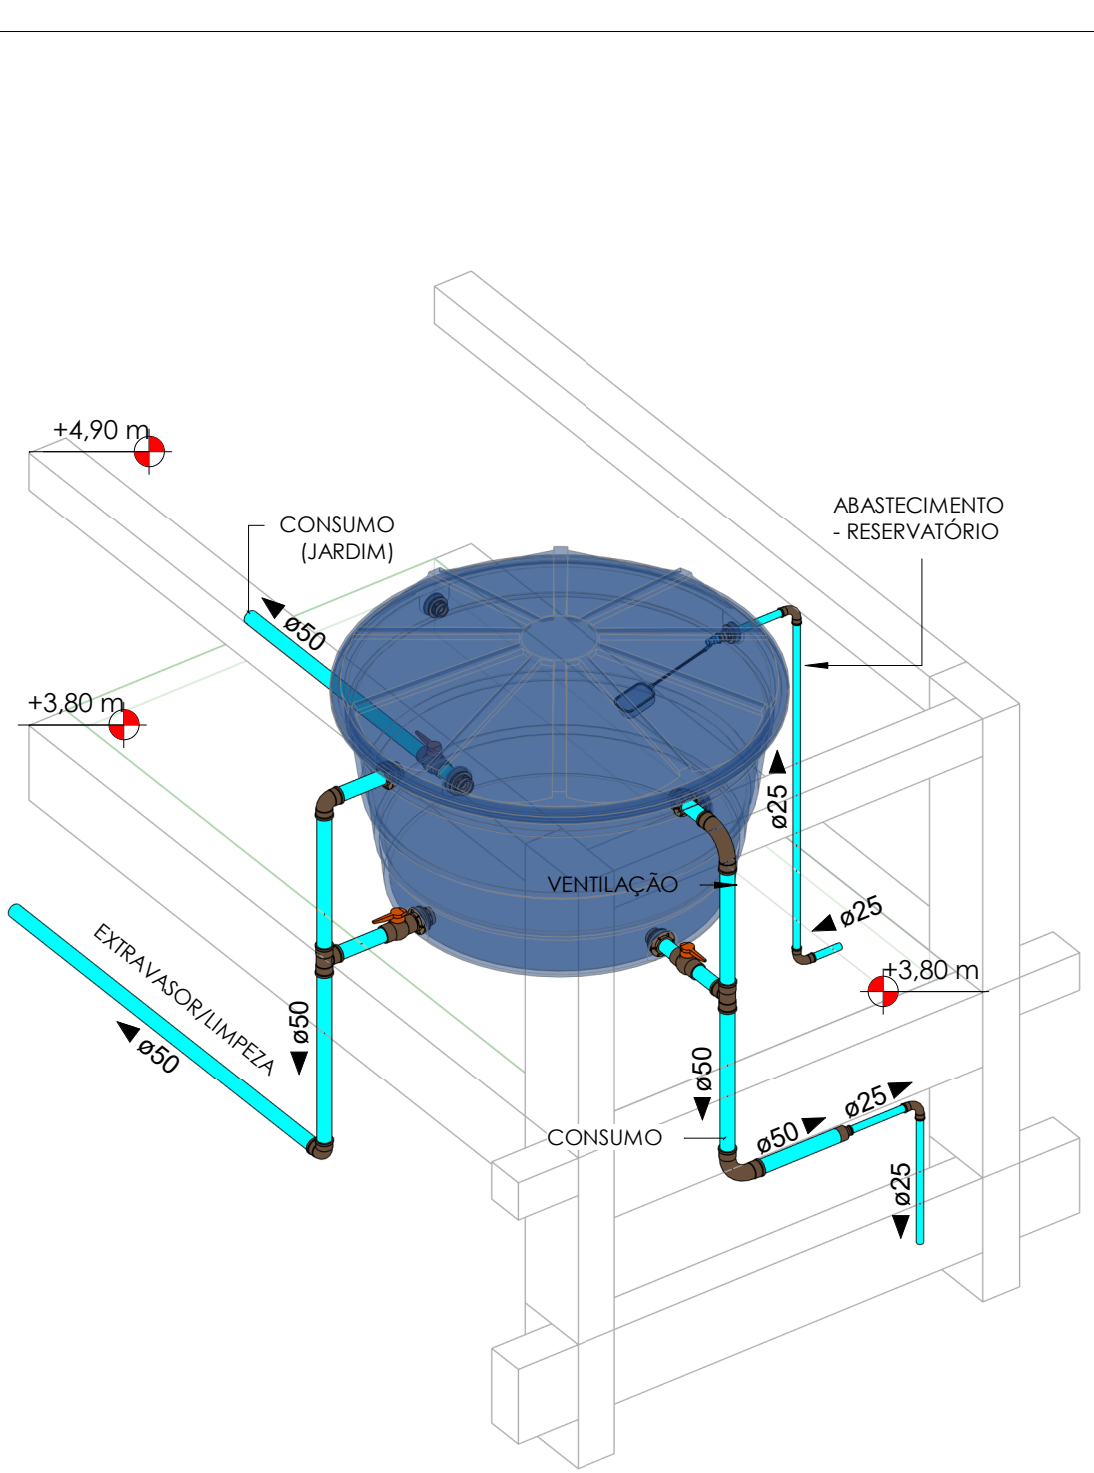


ISOMÉTRICA 02 - WC 2 - ESC 1/25

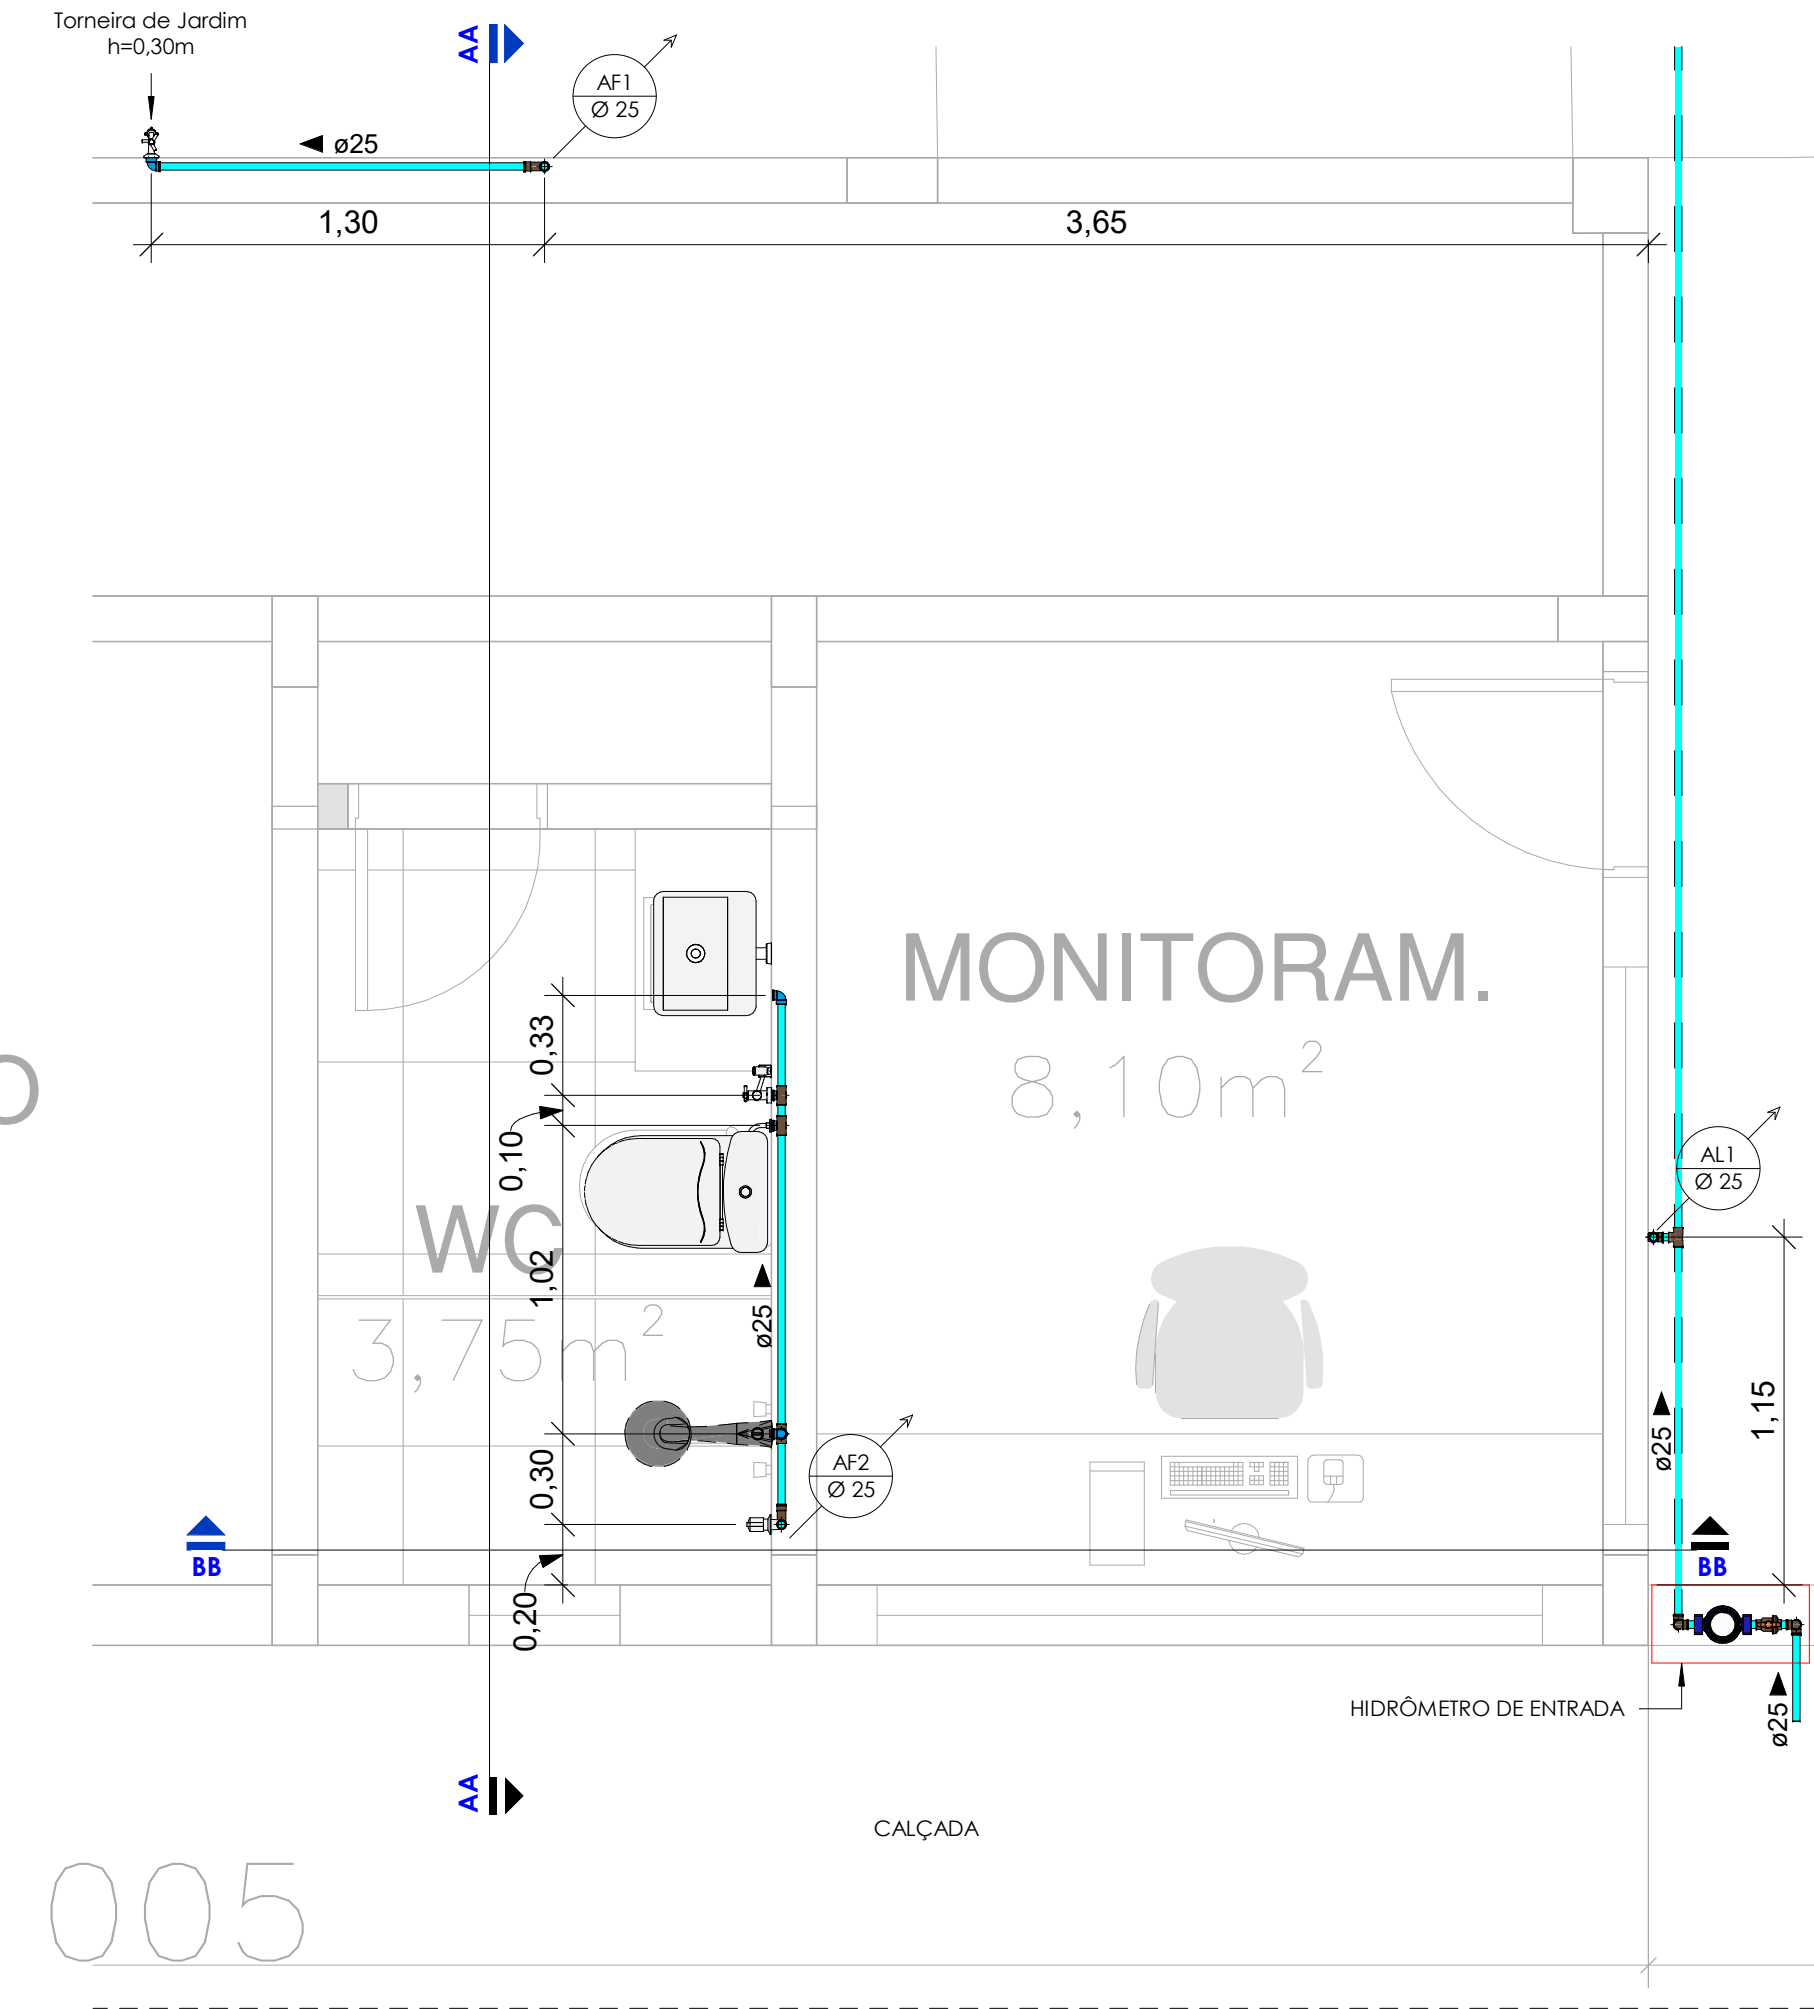

PLANTA BAIXA_ REFORMA_GARAGEM_TÉRREO_DORMITÓRIO_WC_MONITORAMENTO - ESC 1/25

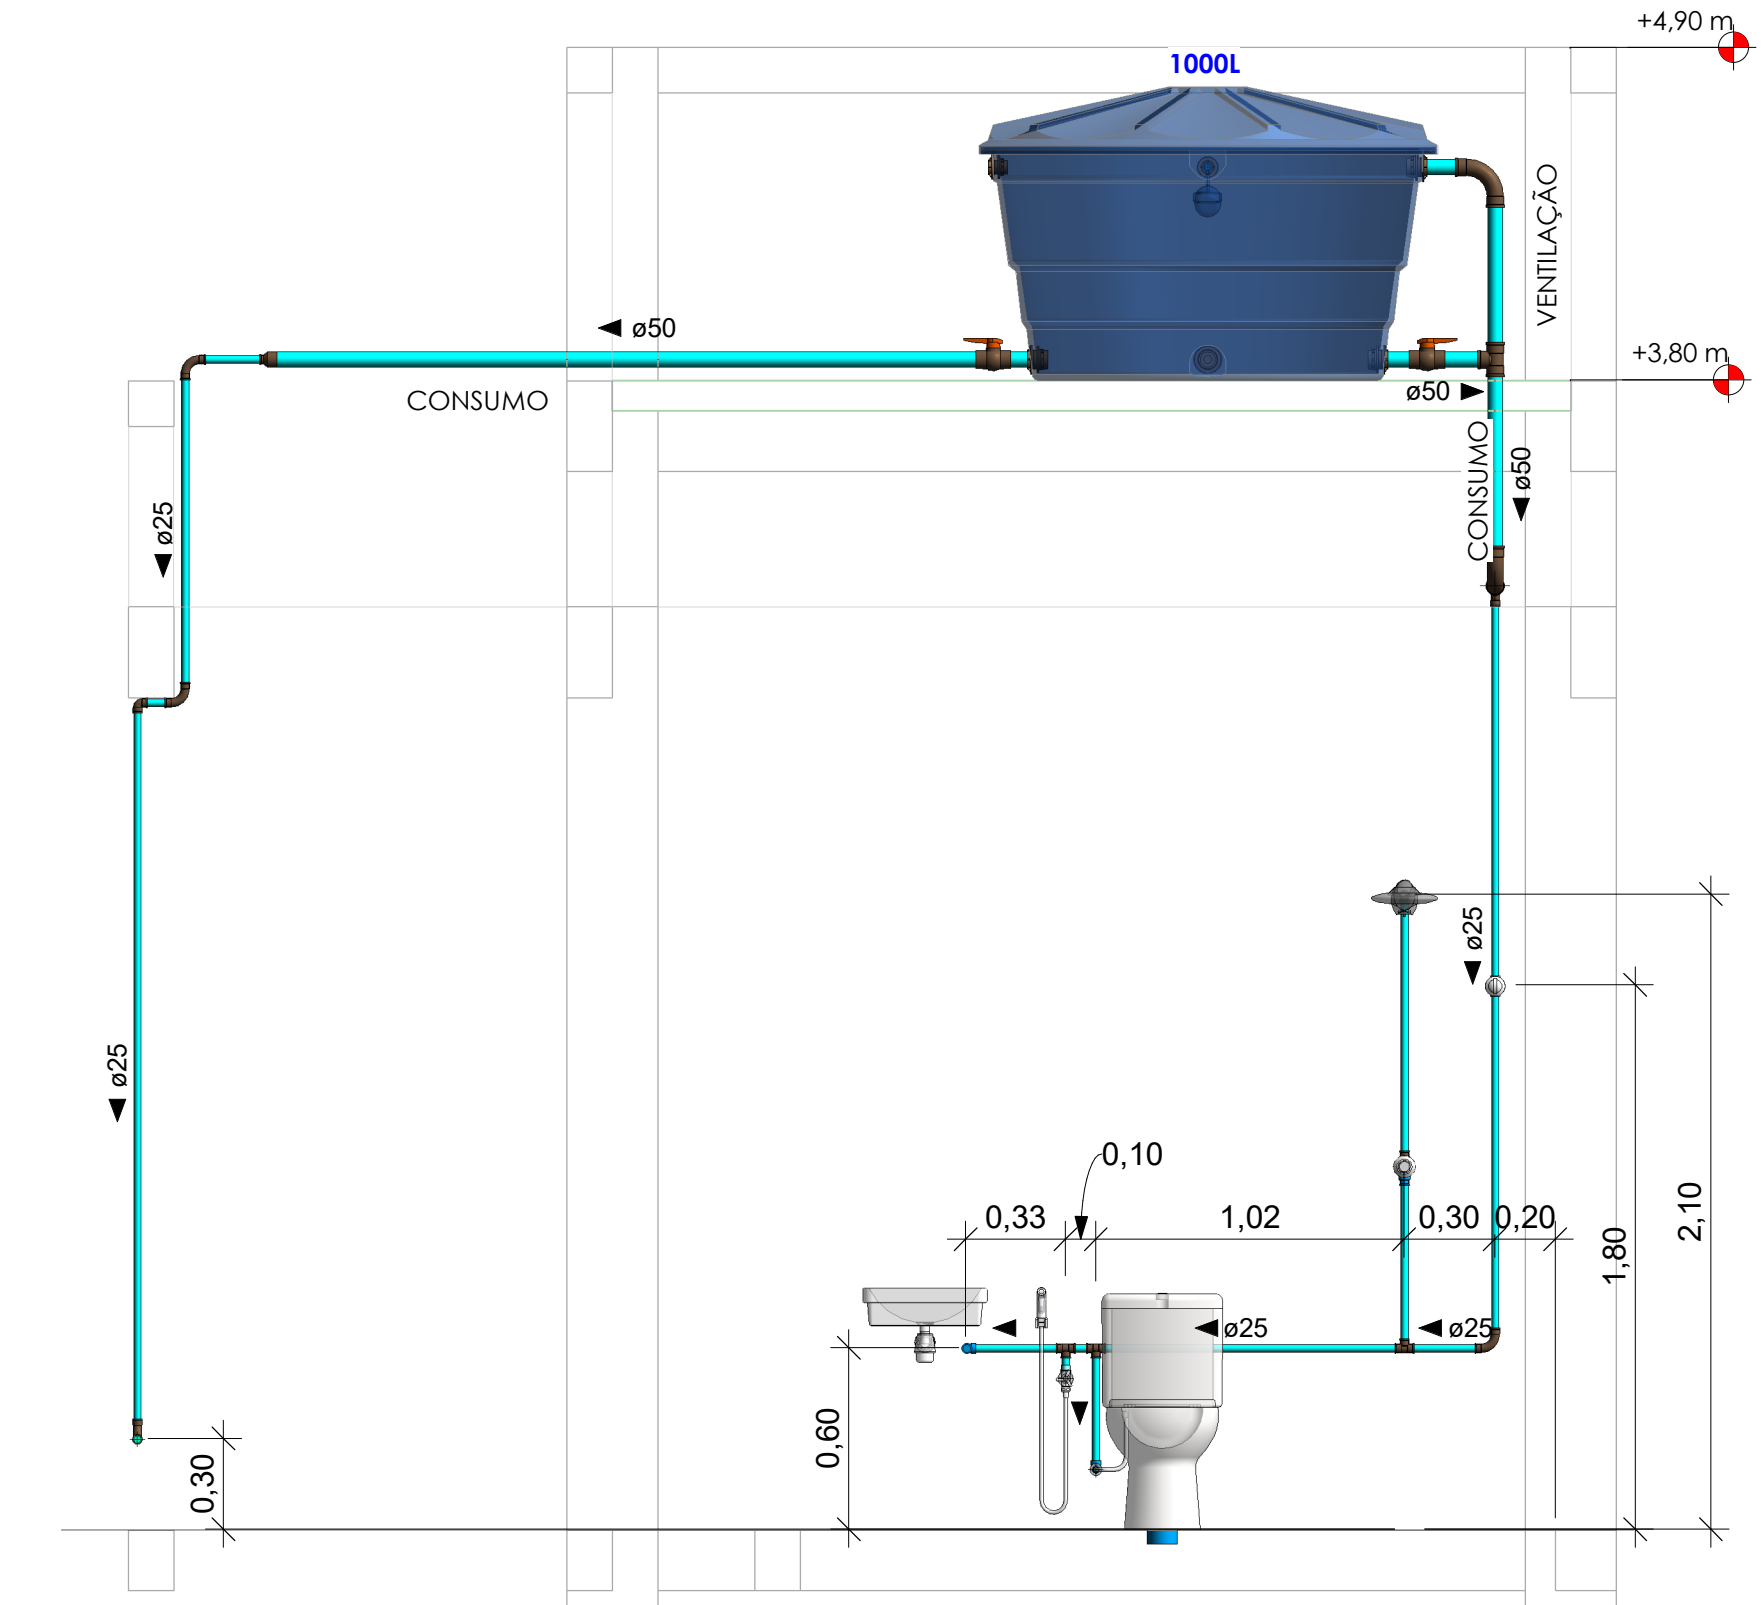

CORTE AA ESC 1/25

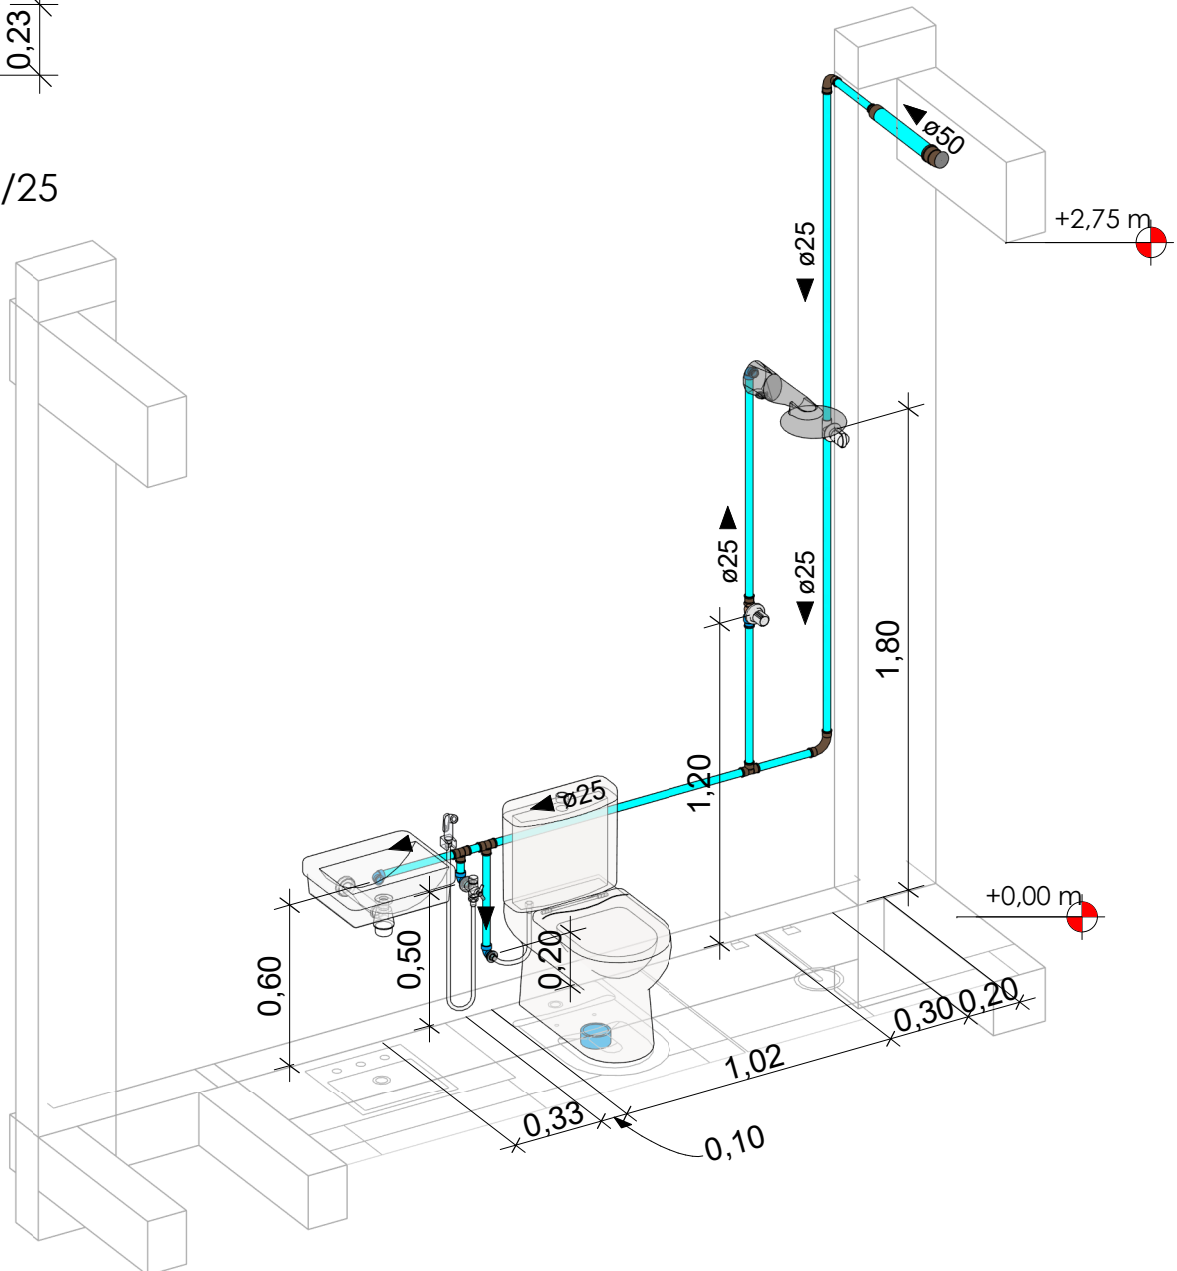

ISOMÉTRICA 01 - WC 1 - ESC 1/25

LEGENDA:

- TUBULAÇÃO PVC BRANCO - ESGOTO
- TUBULAÇÃO PVC BRANCO SN - VENTILAÇÃO ESGOTO
- TUBULAÇÃO PVC MARROM - ÁGUA FRIA
- AL-*nn* -ALIMENTAÇÃO DO RESERV. SUPERIOR
nn: número da coluna
xx: diâmetro nominal da coluna
- CV-*nn* -COLUNA DE VENTILAÇÃO
nn: número da coluna
xx: diâmetro nominal da coluna
- AF-*nn* -COLUNA DE ÁGUA FRIA (BARRILETE)
nn: número da coluna
xx: diâmetro nominal da coluna

TABELA DE ALTURAS		
SIGLA	PONTO	ALTURA
CH	CHUVEIRO	2,10 m
LV	LAVATÓRIO	0,95 m
VS	VASO SANITÁRIO	0,20 m
RG	REGISTRO DE GAVETA	1,80 m
RP	REGISTRO DE PRESSÃO	1,20 m
PIA	PIA DE COZINHA	0,90 m
TQ	TANQUE	1,10 m

PROPRIETÁRIO: PREFEITURA MUNICIPAL DE COREMAS - PB
LINCOLN CARTAXO DE LIRA JÚNIOR:06897861405

Assinado de forma digital por LINCOLN CARTAXO DE LIRA JÚNIOR:06897861405
Dados: 2025.08.11 14:39:31 -03'00'

PROJETO: LINCOLN CARTAXO DE LIRA JÚNIOR CREA 160.814.689-8

PROJETO: INSTALAÇÕES HIDRÁULICAS DA REFORMA DA GARAGEM DE COREMAS

CONCEDENTE: PREFEITURA MUNICIPAL DE COREMAS - PB
CONVENIENTE: MUNICÍPIO DE COREMAS - PB
LOCAL: COREMAS - PB

RESPONSÁVEL TÉCNICO	RUBRICA	DADOS
DATA: 17/06/2025	LINCOLN CARTAXO	CREA 160.814.689-8
CÓPIA		
VISTO		

PRANCHA: 02 / 03

DESCRIÇÃO: PLANTA BAIXA - CAIXA D'ÁGUA, TÉRREO CORTES E ISOMÉTRICAS

ESCALA: INDICADA

Av. Gov. Flavio R. Coutinho, 500, sl. 601
Jd. Oceania, 58037-005 - João Pessoa (PB)
Tel +55 99924.4447
e-mail: contato@lclprojetos.com