


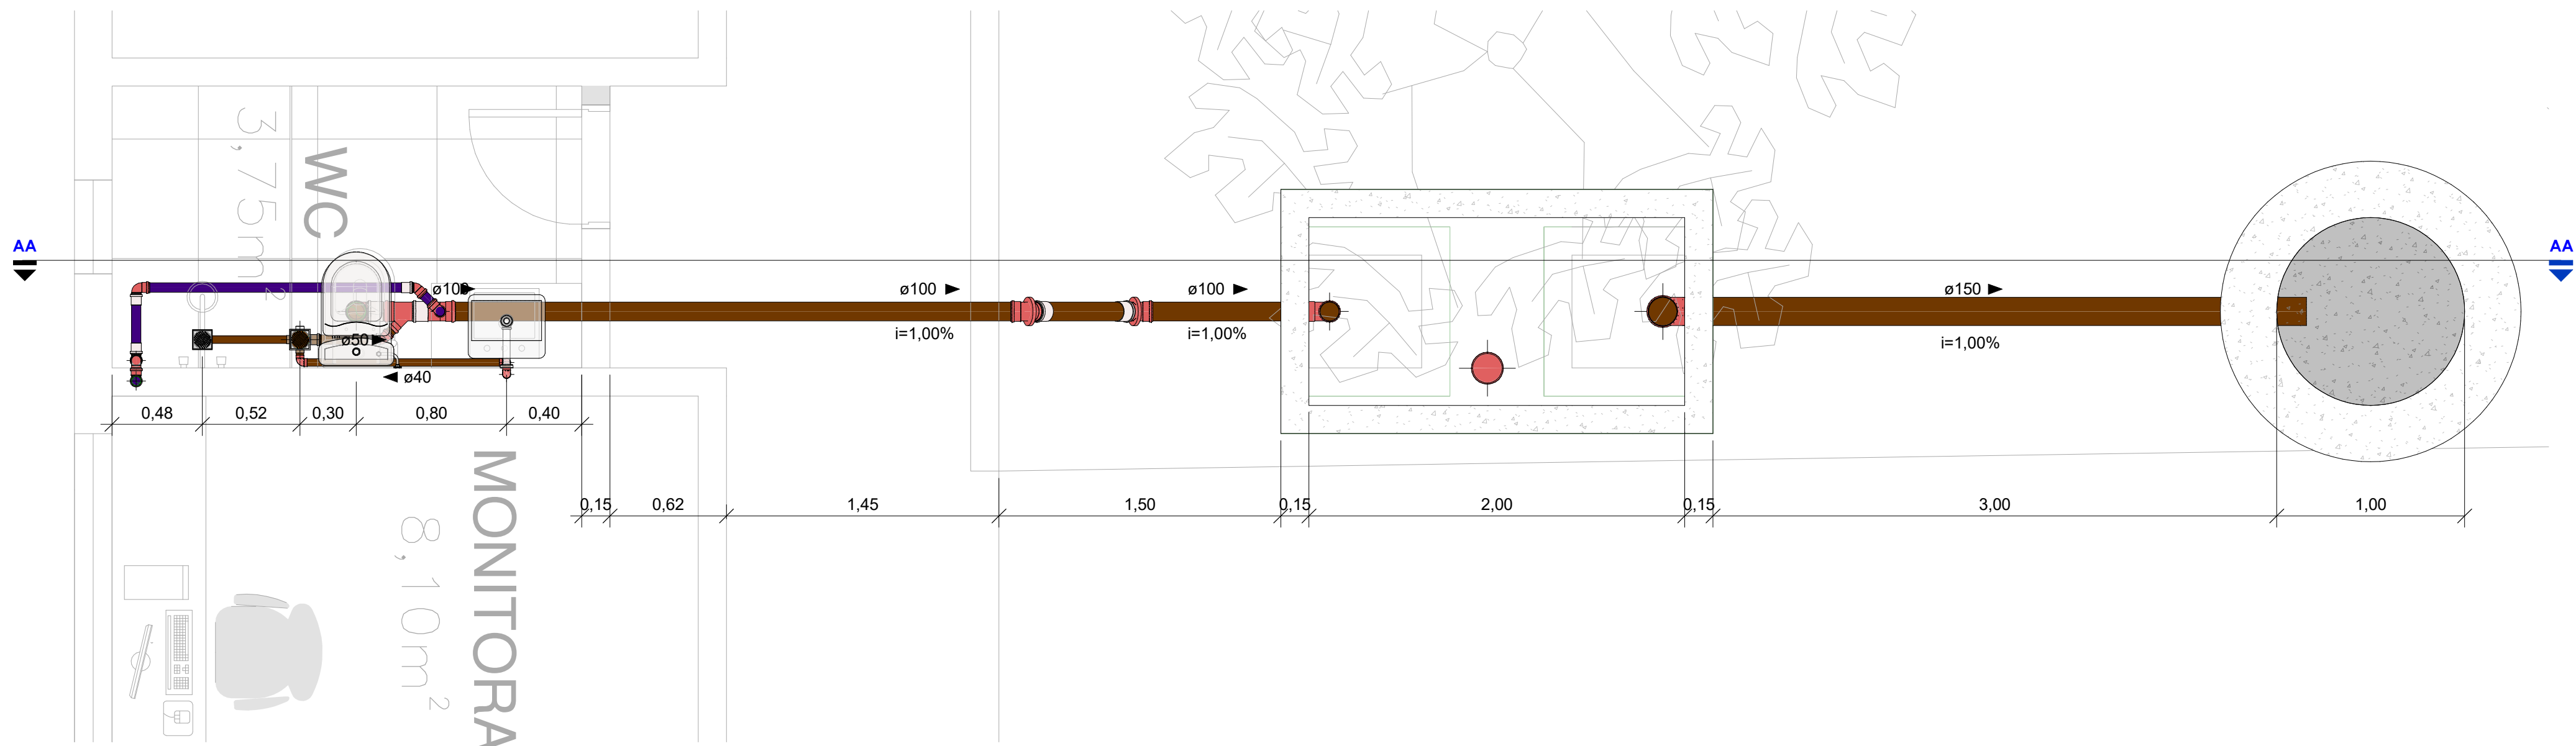

PLANTA BAIXA _DORMITÓRIO_WC_MONITORAMENTO_ - ESC

1/25

MEMORIAL TÉCNICO F.S 01

NORMAS SEGUIDAS

NBR: 13969 - Unidades de Tratamento Complementar e Disposição Final dos Efluentes Líquidos - Projeto, Construção e Operação;

NBR 17076 - Projeto de sistema de tratamento de esgoto de menor porte. Requisitos;

NBR: 7229 - Projeto, Construção e Operação de Sistemas de Tanques Sépticos

DADOS PARA ELABORAÇÃO

Número de Contribuintes (N): 5 Pessoas
Contribuição de Despejos (a): 80
Período de Detenção (T): 1,00
Intervalo de Limpeza (Anos): 1 anos
Temperatura Ambiente > 20 °C
Taxa de Acumulação de Lodo Fresco (LF): 97
Volume Mínimo (L): 1.449 L ou 1,449 m³

DIMENSÕES TANQUE SÉPTICO


B (Base): 1,00 m
L (Largura): 2,00 m
H (Altura): 1,00 m
Volume Real (L): 2.000 L ou 2,0 m³

ÁREA DE INFILTRAÇÃO SUMIDOURO

Volume de Contribuição (V): 400 L/pessoa.dia
Coeficiente de Infiltração (C1): 105,00 (Área bem selecionada e limpa, variando a areia grossa com cascalho).
Área de Infiltração Mínima (m²): 3,81 m²


DIMENSÕES SUMIDOURO

Diâmetro (m): 1,00 m
Profundidade Útil (m): 2,00 m
Dimensões: Informadas em Planta Baixa
Área de Infiltração Lateral (m²): 6,30 m²
Área de Infiltração Fundo (m²): 0,80 m²
Área de Infiltração Total (m²): 7,1 m²

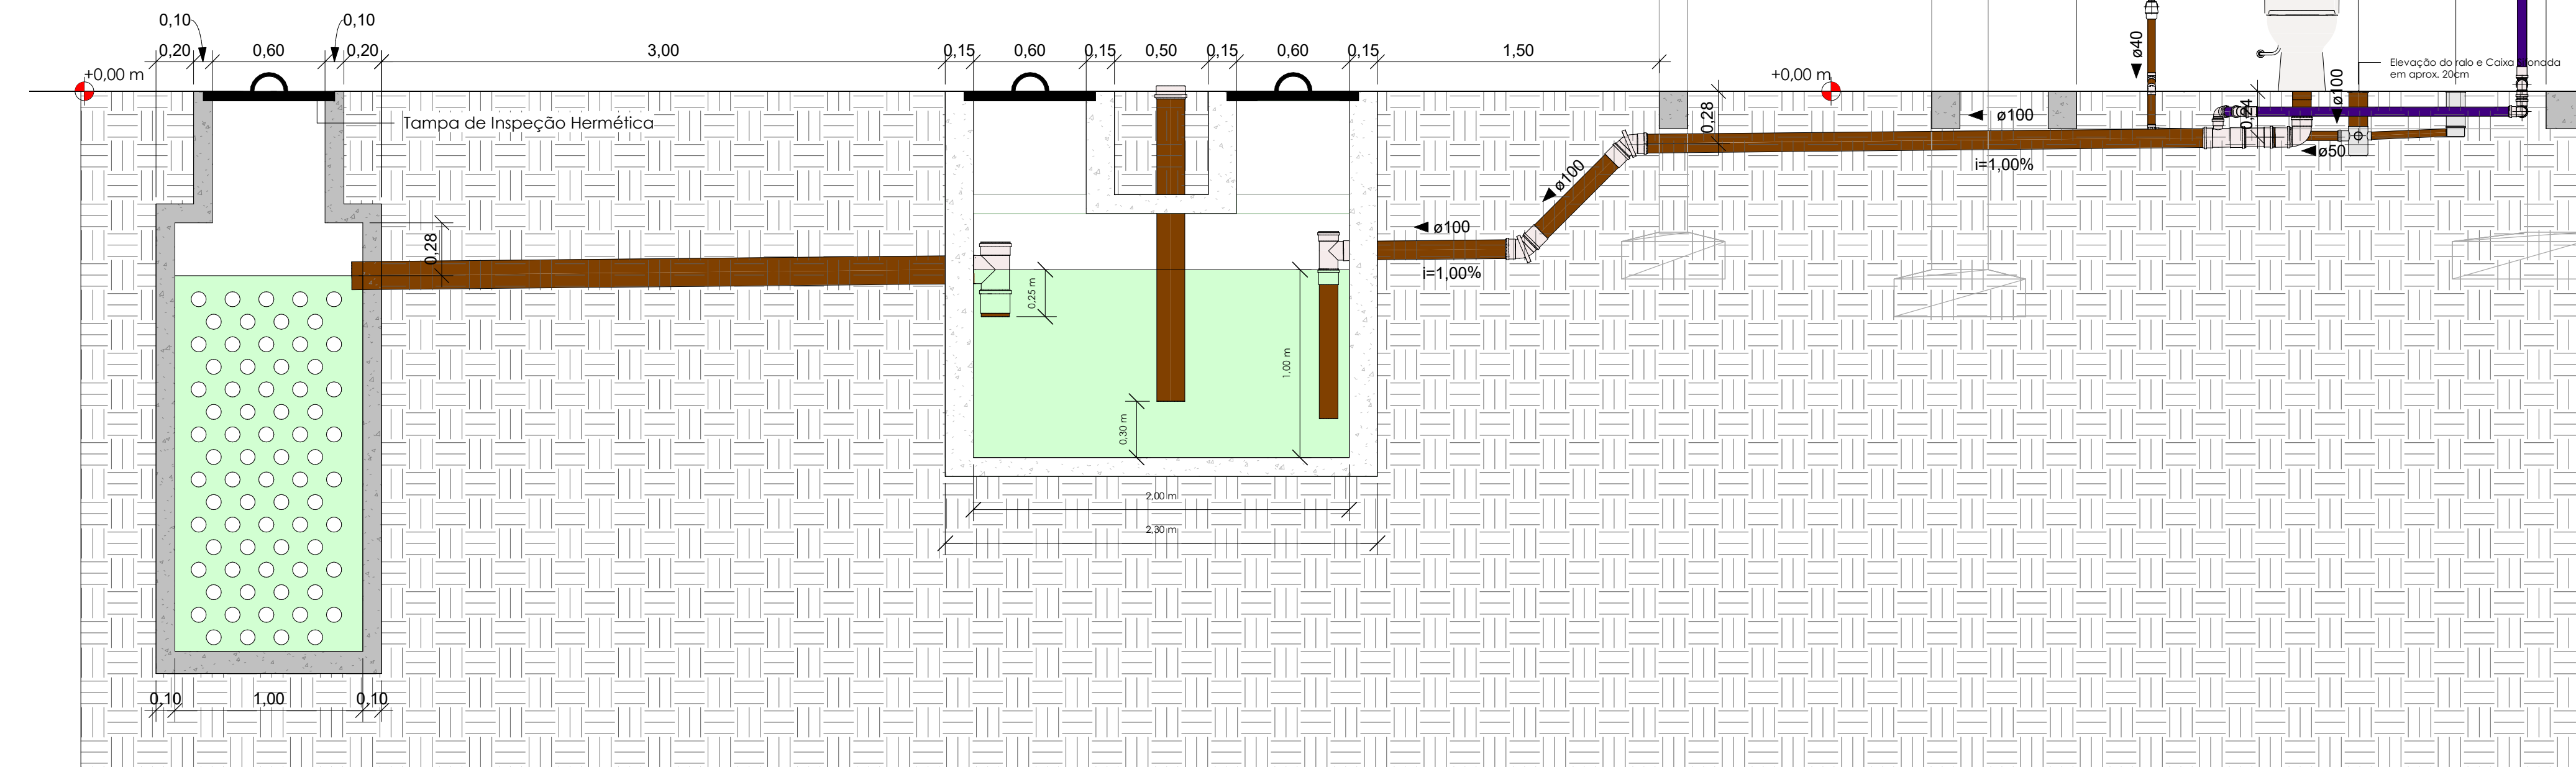

CORTE AA

ESC 1/25

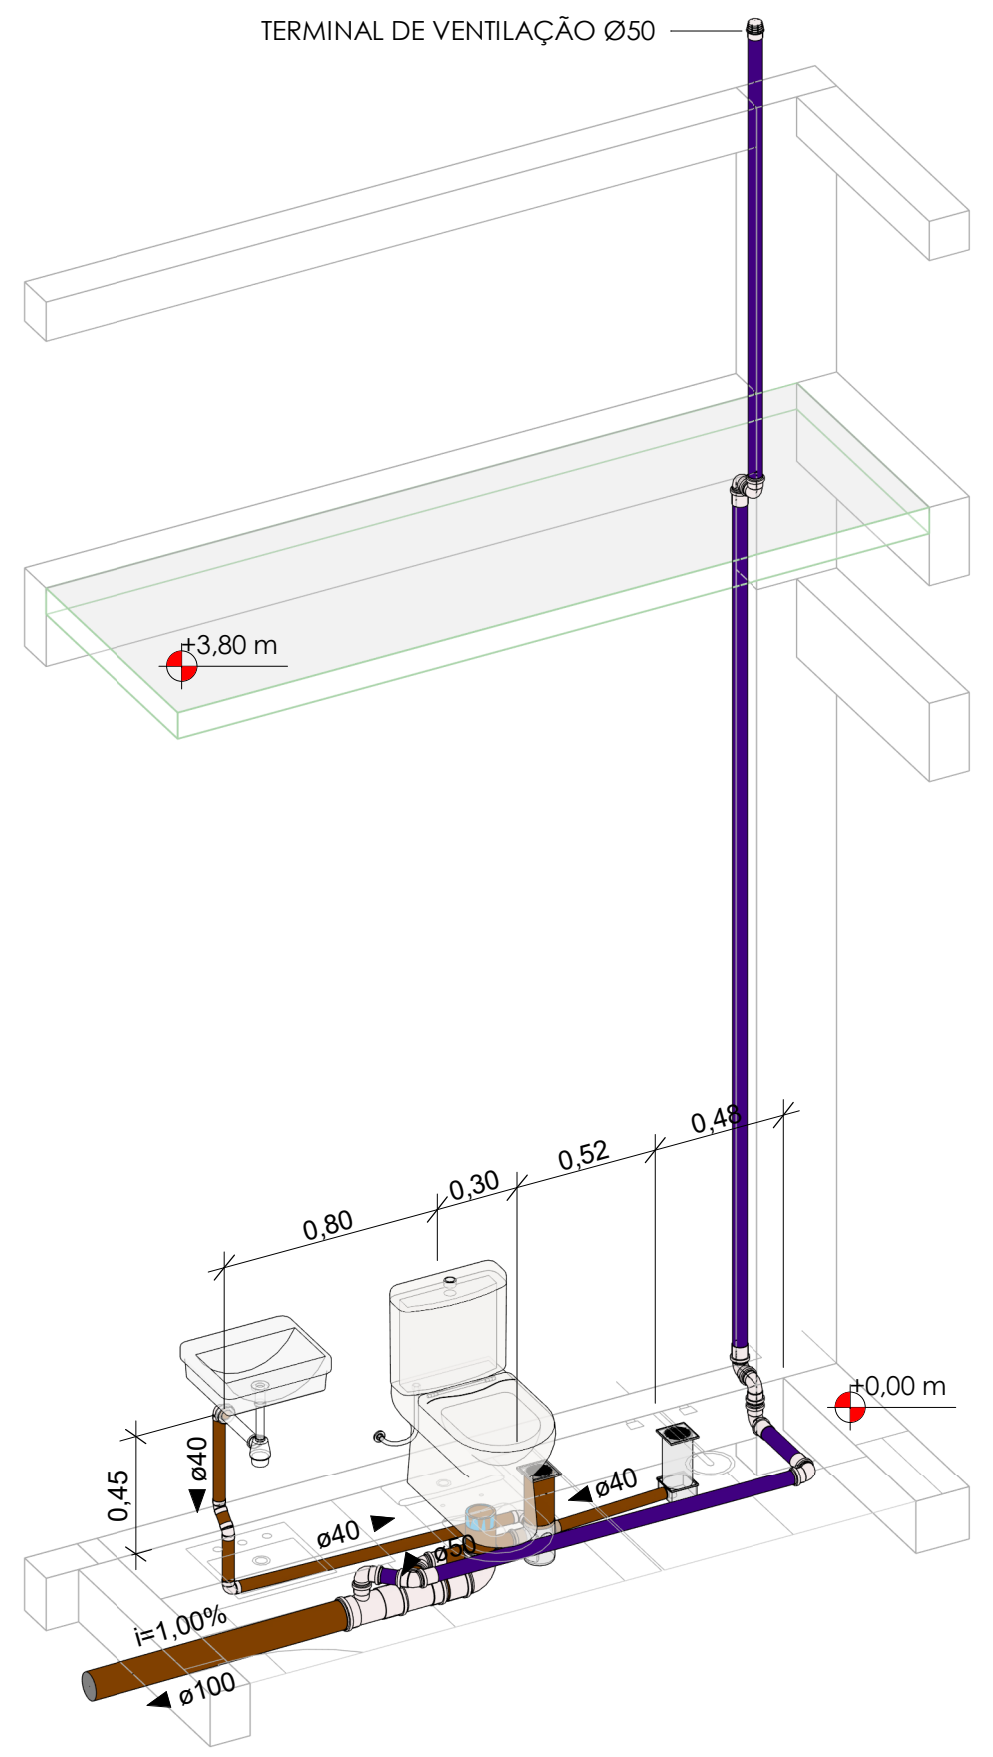

ISOMÉTRICA 02 - WC_MONITORAMENTO - ESC

1/25

LEGENDA:

- TUBULAÇÃO PVC BRANCO - ESGOTO
- TUBULAÇÃO PVC BRANCO SN - VENTILAÇÃO ESGOTO
- TUBULAÇÃO PVC MARROM - ÁGUA FRIA
- TUBO DE QUEDA DE ESGOTO
nn: número da coluna
xx: diâmetro nominal da coluna
- COLUNA DE VENTILAÇÃO
nn: número da coluna
xx: diâmetro nominal da coluna
- COLUNA DE ÁGUA FRIA (BARRILETE)
nn: número da coluna
xx: diâmetro nominal da coluna

CONFORME SUGERIDO PELA ABNT NBR 17076, É NECESSÁRIO UM ESTUDO TÉCNICO DO SOLO PARA VERIFICAÇÃO DA ABSORÇÃO DO SOLO EXISTENTE. O PRESENTE PROJETO NÃO CONTEMPLA OS DADOS DO SOLO LOCAL DESTE EMPREENDIMENTO. VISTO QUE NÃO FOI ENCAMINHADO PELA PREFEITURA, TAIS CÁLCULOS AQUI DESCRITOS SÃO INTERPRETADOS COMO MODELO PADRÃO E QUE NÃO CARACTERIZAM A SITUAÇÃO REAL.

PROPRIETÁRIO: PREFEITURA MUNICIPAL DE COREMAS - PB
LINCOLN CARTAXO DE LIRA JÚNIOR
06897861405
Dados: 2025.06.19 17:30:04 -03'00'

PROJETO: LINCOLN CARTAXO DE LIRA JÚNIOR CREA 160.814.689-8

PROJETO: INSTALAÇÕES SANITÁRIAS DA REFORMA DA GARAGEM DE COREMAS
CONCEDENTE: PREFEITURA MUNICIPAL DE COREMAS - PB
CONVENIENTE: MUNICÍPIO DE COREMAS - PB
LOCAL: COREMAS - PB

DATA	19/06/2025	LINCOLN CARTAXO	RUBRICA	DADOS
CÓPIA				CREA 160.814.689-8
VISTO				

PRANCHA: 01 / 03
DESCRIÇÃO: PLANTA BAIXA - DORMITÓRIO, WC, MONITOR. FOSSA E SUMIDOURO, CORTE, MEMORIAL TÉCNICO E ISOMÉTRICA
ESCALA: INDICADA



Av. Gov. Flavio R. Coutinho, 500, sl. 601
Jd. Oceania, 58037-005 - João Pessoa (PB)
Tel +55 99924.4447
e-mail: contato@lclprojetos.com