




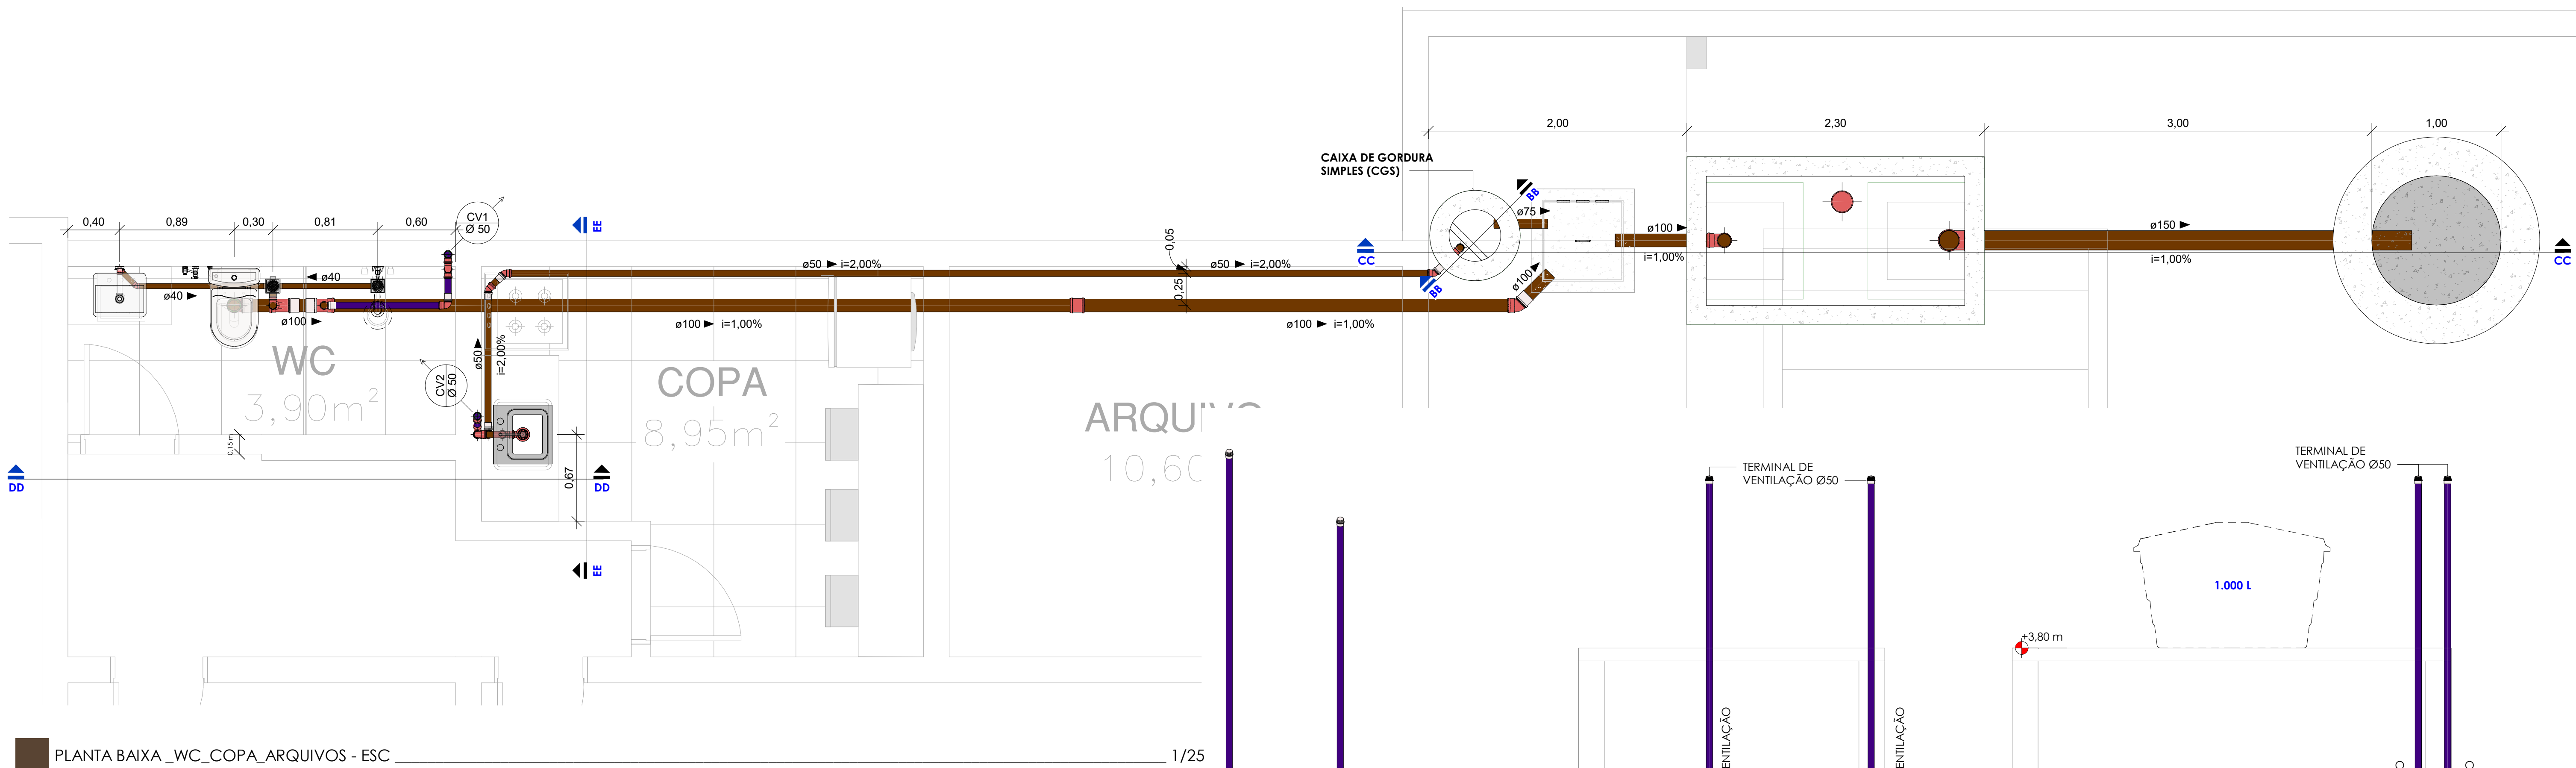


PLANTA BAIXA_WC_COPA_ARQUIVOS - ESC. 1/25

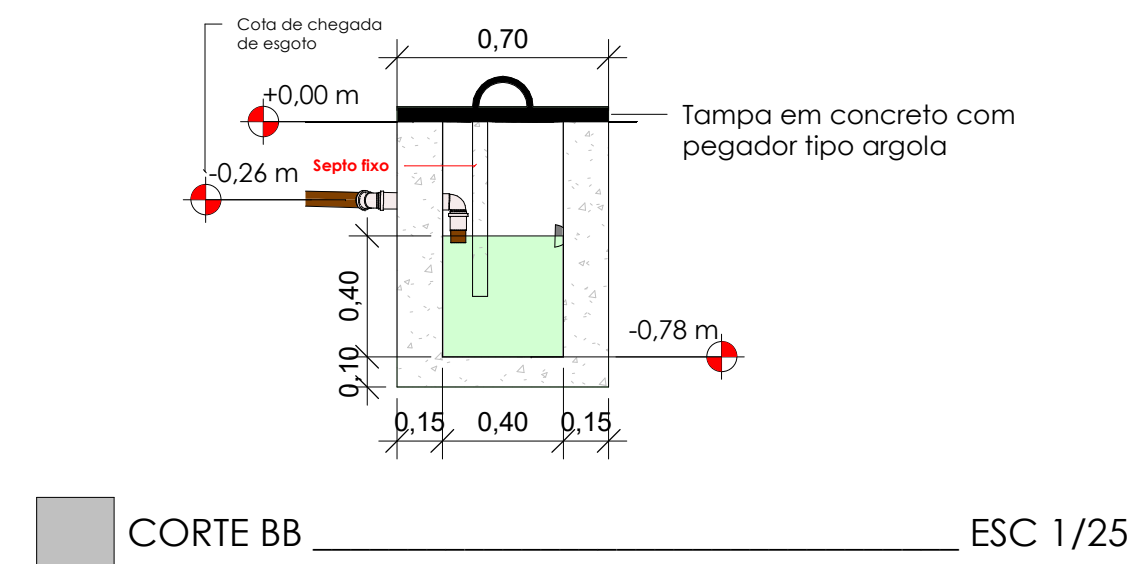


CORTE BB ESC 1/25

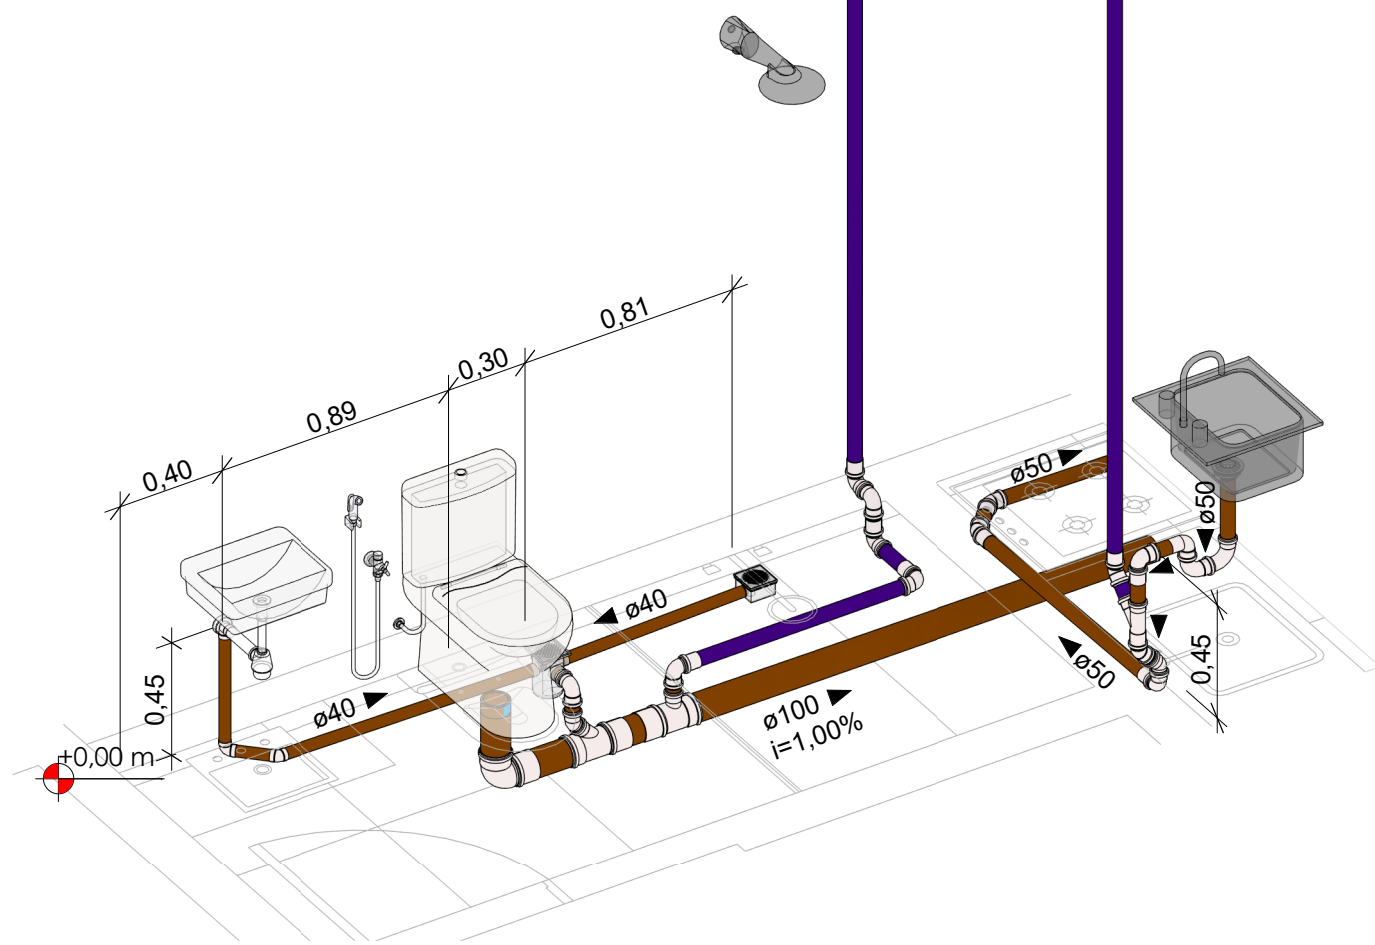

ISOMÉTRICAS 01 - WC_COPA - ESC 1/25

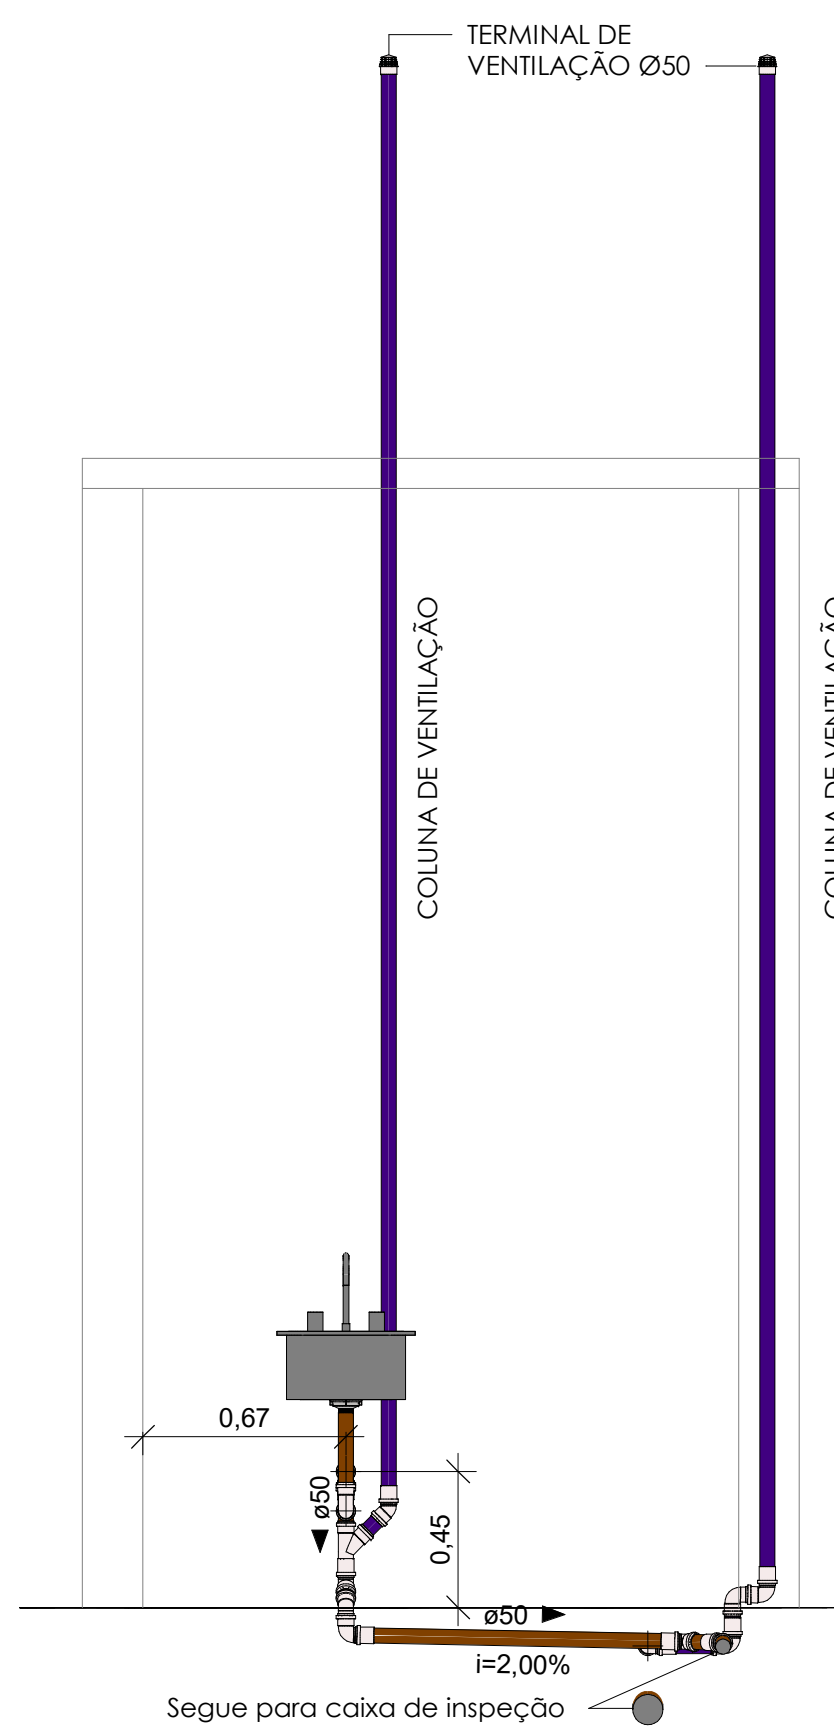

CORTE EE ESC 1/25

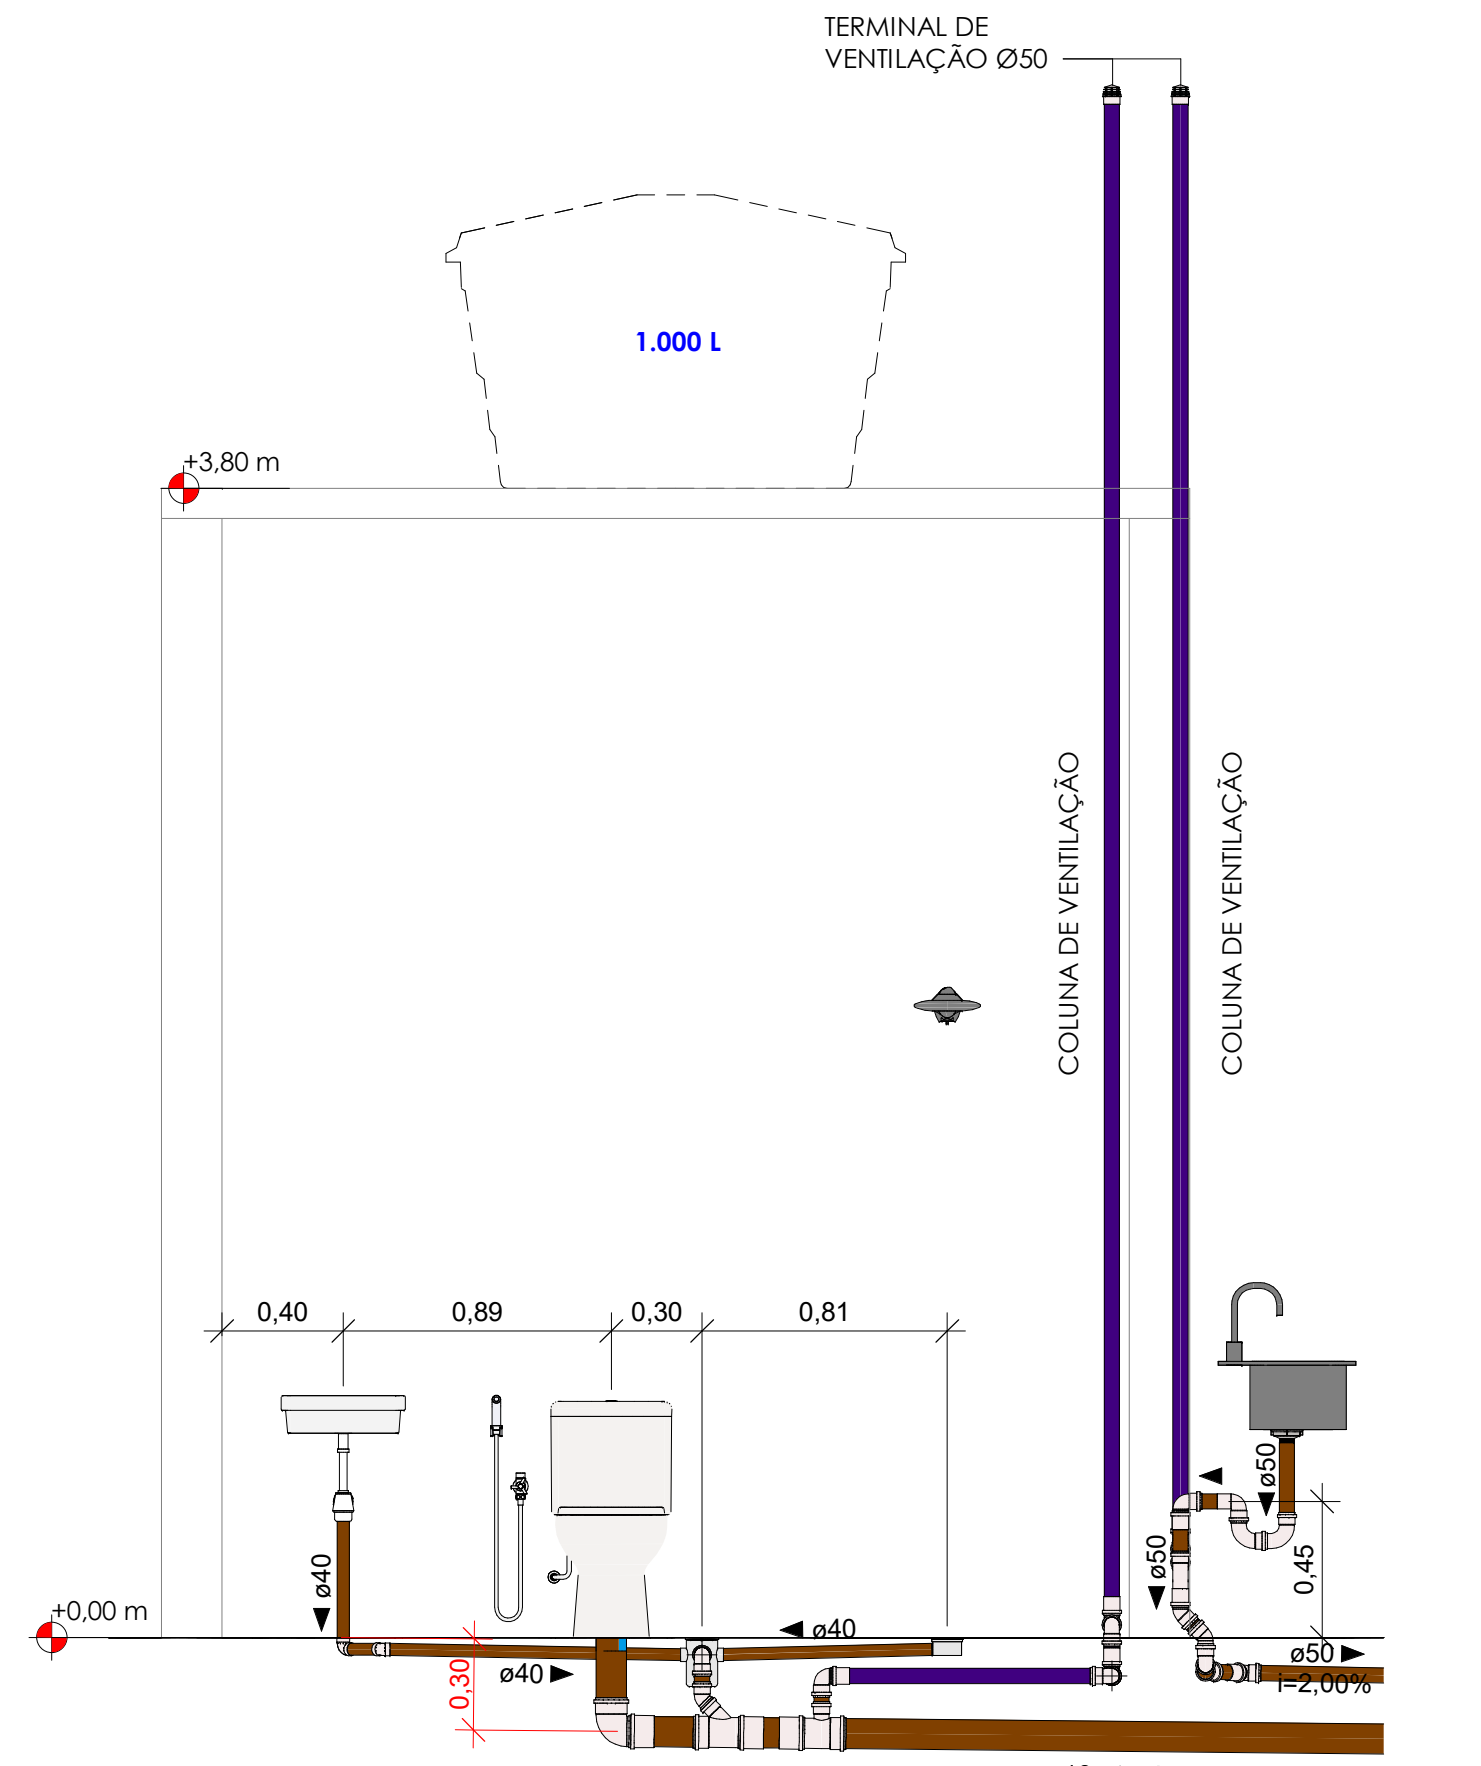

CORTE DD ESC 1/25

MEMORIAL TÉCNICO F.S 02

NORMAS SEGUIDAS

NBR: 13969 - Unidades de Tratamento Complementar e Disposição Final dos Efluentes Líquidos - Projeto, Construção e Operação;

NBR 17076 - Projeto de sistema de tratamento de esgoto de menor porte. Requisitos;

NBR: 7229 - Projeto, Construção e Operação de Sistemas de Tanques Sépticos

DADOS PARA ELABORAÇÃO

Número de Contribuintes (N): 5 Pessoas
Contribuição de Despejos (q): 80
Período de Detenção (T): 1,00
Intervalo de Limpeza (Anos): 1 anos
Temperatura Ambiente > 20 °C
Taxa de Acumulação de Lodo Fresco (Lf): 97
Volume Mínimo (L): 1.449 L ou 1,449 m³

DIMENSÕES TANQUE SÉPTICO


B (Base): 1,00 m
L (Largura): 2,00 m
H (Altura): 1,00 m
Volume Real (L): 2.000 L ou 2,0 m³

ÁREA DE INFILTRAÇÃO SUMIDOURO

Volume de Contribuição (V): 400 L/pessoa.dia
Coeficiente de Infiltração (C1): 105,00 (Areia bem selecionada e limpa, variando a areia grossa com cascalho).
Área de Infiltração Mínima (m²): 3,81 m²

DIMENSÕES SUMIDOURO

Diâmetro (m): 1,00 m
Profundidade Útil (m): 2,00 m
Dimensões: Informadas em Planta Baixa
Área de Infiltração Lateral (m²): 6,30 m²
Área de Infiltração Fundo (m²): 0,80 m²
Área de Infiltração Total (m²): 7,1 m²

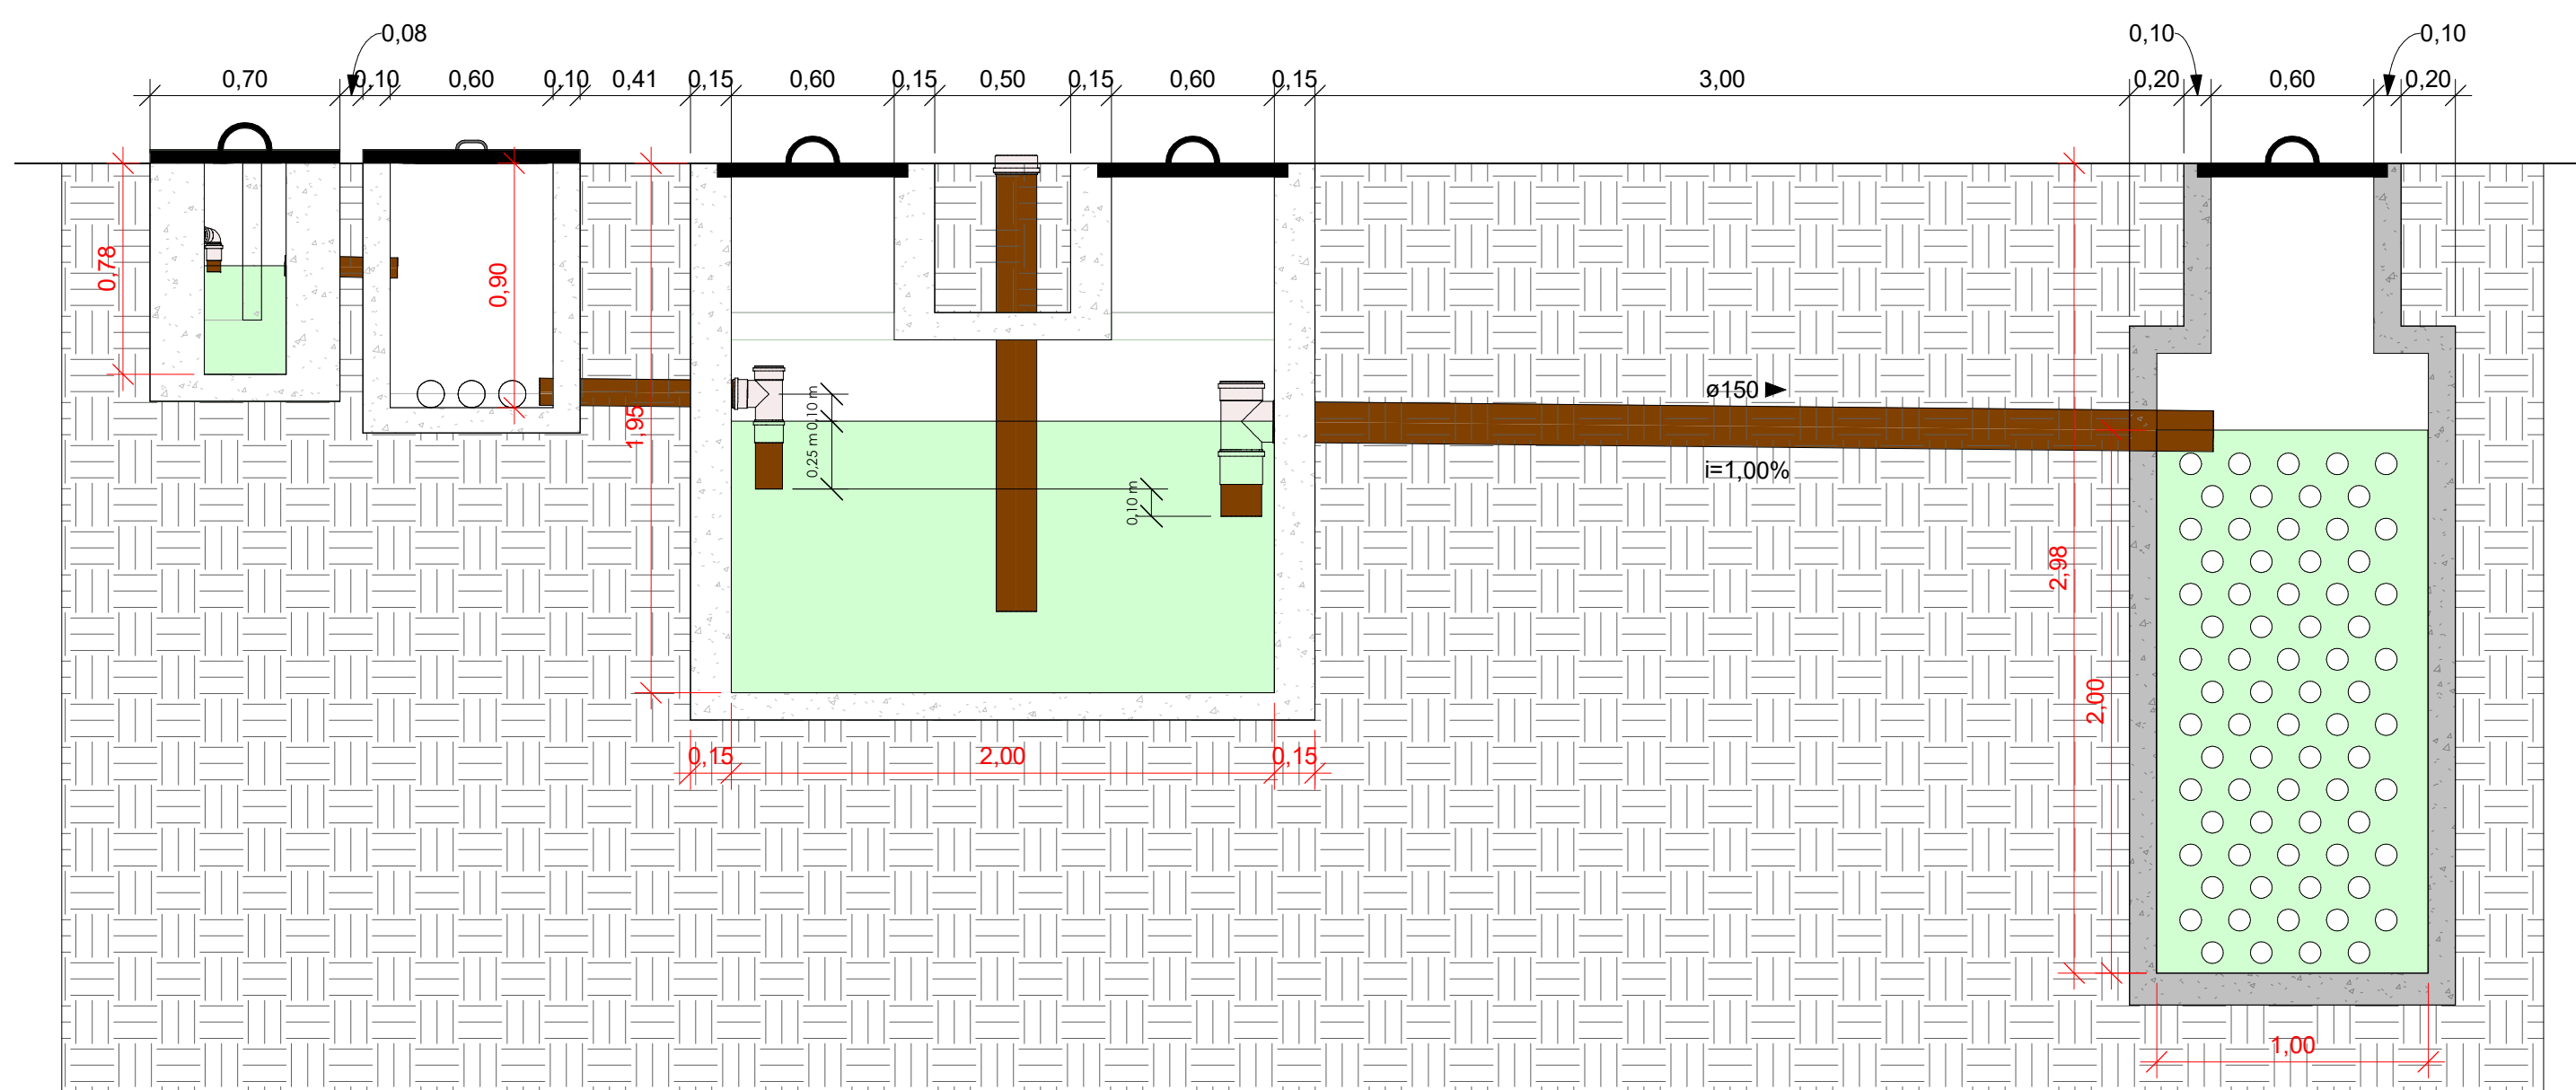

CORTE CC ESC 1/25

CONFORME SUGERIDO PELA ABNT NBR 17076, É NECESSÁRIO UM ESTUDO TÉCNICO DO SOLO PARA VERIFICAÇÃO DA ABSORÇÃO DO SOLO EXISTENTE. O PRESENTE PROJETO NÃO CONTEMPLA OS DADOS DO SOLO LOCAL DESTA EMPREENDIMENTO. VISTO QUE NÃO FOI ENCAMINHADO PELA PREFEITURA, TALS CÁLCULOS AQUI DESCRITOS SÃO INTERPRETADOS COMO MODELO PADRÃO E QUE NÃO CARACTERIZAM A SITUAÇÃO REAL.

PROPRIETÁRIO:	PREFEITURA MUNICIPAL DE COREMAS - PB		
PROJETO:	LINCOLN CARTAXO DE LIRA JÚNIOR CREA 160.814.689-8		
PROJETO:	INSTALAÇÕES SANITÁRIAS DA REFORMA DA GARAGEM DE COREMAS		
CONCEDENTE:	PREFEITURA MUNICIPAL DE COREMAS - PB		
CONVENIENTE:	MUNICÍPIO DE COREMAS - PB		
LOCAL:	COREMAS - PB		
PRANCHA:	02 / 03	DESCRIÇÃO:	ESCALA:
		PLANTA BAIXA - WC, COPA E ARQUIVO FOSSA E SUMIDOURO, CORTES, MEMORIAL TÉCNICO E ISOMÉTRICA	INDICADA



Av. Gov. Flavio R. Coutinho, 500, sl. 601
Jd. Oceania, 58037-005 - João Pessoa (PB)
Tel +55 99924.4447
e-mail: contato@lclprojetos.com