

Peças hidráulicas e sanitárias	
Quantidade	Descrição
1	
2	Antiespuma 100 mm, Esgoto - TIGRE
2	Caixa Sifonada Montada com Grelha e Porta Grelha Quadrados Brancos 100 x 150 x 50mm, Esgoto - TIGRE
2	Porta Grelha Quadrado p/ Grelha Quadrada Branca 100mm, Esgoto - TIGRE
2	Prolongamento p/ Caixa Sifonada 100 x 100mm, Esgoto - TIGRE
2	Ralo Quadrado Montado - Branco c/ grelha branca 100x53x40mm, Esgoto - TIGRE
1	Caixa de Inspeção de Alvenaria - Dimensões internas de 60x60cm
2	Bacia Sanitária com Caixa Acoplada
1	Chuveiro
1	Ducha higiênica
2	Cuba de sobrepor
2	Sifão para lavatório 1"x1.1/2" com tubo de 300 mm
2	Flexível 300mm aço inox

Tabela de conexão de tubo GUARITA					
Contagem	Tigre: Descrição	Tigre: Fabricante	Tigre: Linha	Tigre: Produto	Tigre: Sistema

2					
2	Cap 150mm, Esgoto Série Normal - TIGRE	© Tigre S/A	Série Normal	Cap	Esgoto
2	Curva 90° Curta 50mm, Esgoto Série Normal - TIGRE	© Tigre S/A	Série Normal	Curva 90°	Esgoto
2	Curvar 45° 100mm, Esgoto Série Normal - TIGRE	© Tigre S/A	Série Normal	Curvar	Esgoto
3	Joelho 45° 40mm, Esgoto Série Normal - TIGRE	© Tigre S/A	Série Normal	Joelho	Esgoto
9	Joelho 45° 50mm, Esgoto Série Normal - TIGRE	© Tigre S/A	Série Normal	Joelho	Esgoto
1	Joelho 45° 100mm, Esgoto Série Normal - TIGRE	© Tigre S/A	Série Normal	Joelho	Esgoto
5	Joelho 90° 40mm, Esgoto Série Normal - TIGRE	© Tigre S/A	Série Normal	Joelho	Esgoto
17	Joelho 90° 50mm, Esgoto Série Normal - TIGRE	© Tigre S/A	Série Normal	Joelho	Esgoto
2	Joelho 90° 100mm, Esgoto Série Normal - TIGRE	© Tigre S/A	Série Normal	Joelho	Esgoto
1	Junção Simples 50 x 50mm, Esgoto Série Normal - TIGRE	© Tigre S/A	Série Normal	Tê/Junção	Esgoto
2	Junção Simples 100 x 50mm, Esgoto Série Normal - TIGRE	© Tigre S/A	Série Normal	<varia>	Esgoto
1	Luva de Correr 100mm, Esgoto Série Normal - TIGRE	© Tigre S/A	Série Normal	Luva	Esgoto
18	Luva Simples 50mm, Esgoto Série Normal - TIGRE	© Tigre S/A	Série Normal	Luva	Esgoto
10	Luva Simples 100mm, Esgoto Série Normal - TIGRE	© Tigre S/A	Série Normal	Luva	Esgoto
2	Luva Simples 150mm, Esgoto Série Normal - TIGRE	© Tigre S/A	Série Normal	Luva	Esgoto
3	Terminal de Ventilação 50mm, Esgoto Série Normal - TIGRE	© Tigre S/A	Série Normal	Terminal	Esgoto
2	Tê 100 x 50mm, Esgoto Série Normal - TIGRE	© Tigre S/A	Série Normal	Tê/Junção	Esgoto
2	Tê 100 x 100mm, Esgoto Série Normal - TIGRE	© Tigre S/A	Série Normal	Tê/Junção	Esgoto
2	Tê 150 x 150mm, Esgoto Série Normal - TIGRE	© Tigre S/A	Série Normal	Tê/Junção	Esgoto

Caixas - Ralos - Complementos			
Quantidade	Descrição	Tipo de sistema	Fabricante
1	Caixa de Inspeção de Alvenaria - Dimensões internas de 60x60cm	Inspeção/ Esgoto	Moldada In Loco


Tubos de PVC Rígidos para Esgoto - Guarita	
Diâmetro	Comprimento (m)

40 mm	4,36
50 mm	28,17
75 mm	0,42
100 mm	17,08
150 mm	10,39


Conexões - Esgoto	
Quantidade	Descrição
2	Anel de vedação para Vaso Sanitário

LEGENDA:


- TUBULAÇÃO PVC BRANCO - ESGOTO
- TUBULAÇÃO PVC BRANCO SN - VENTILAÇÃO ESGOTO
- TUBULAÇÃO PVC MARROM - ÁGUA FRIA
- TQ-nn
Øxx -TUBO DE QUEDA DE ESGOTO
nn: número da coluna
xx: diâmetro nominal da coluna
- CV-nn
Øxx -COLUNA DE VENTILAÇÃO
nn: número da coluna
xx: diâmetro nominal da coluna
- AF-nn
Øxx -COLUNA DE ÁGUA FRIA (BARRILETE)
nn: número da coluna
xx: diâmetro nominal da coluna

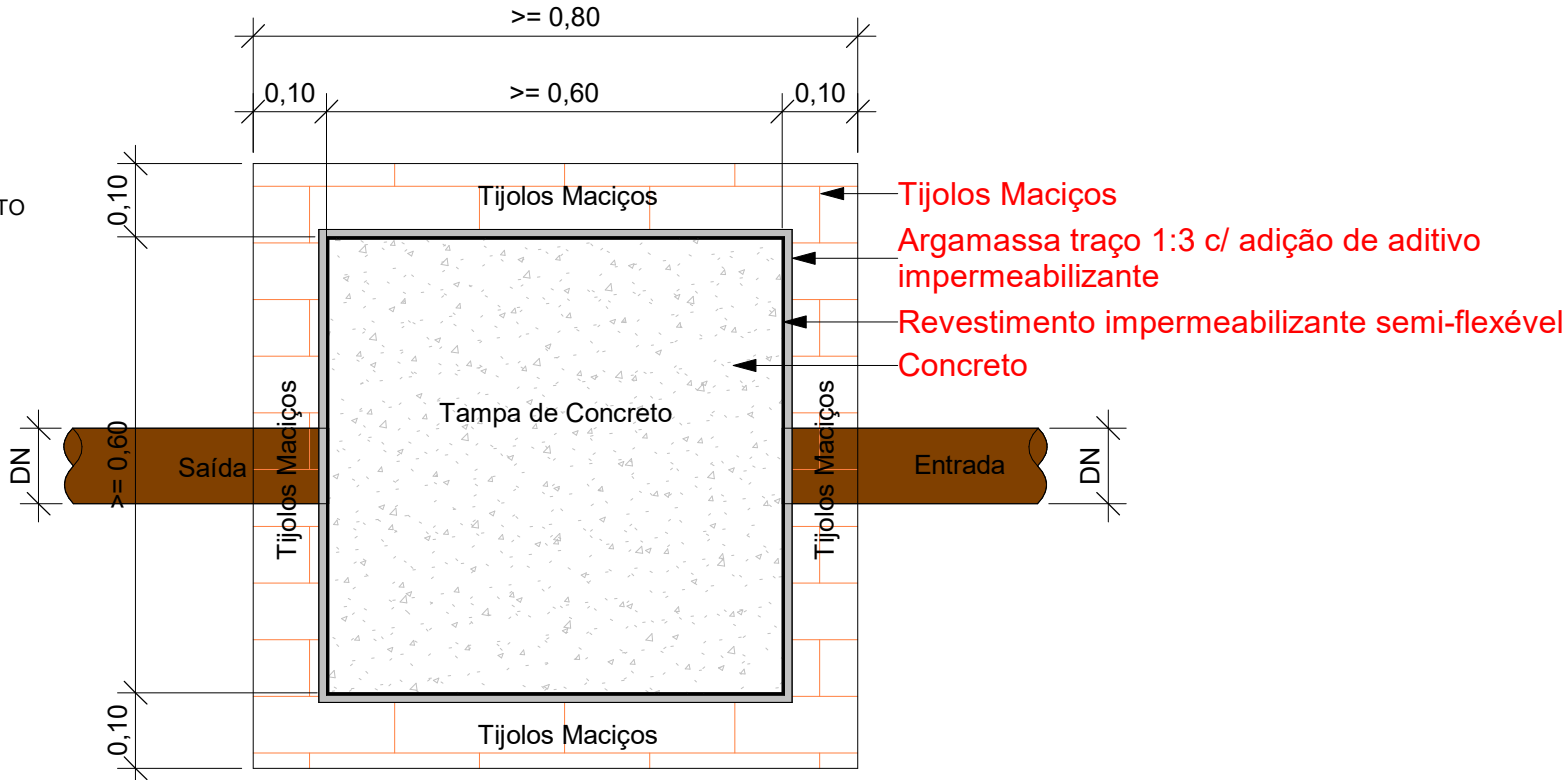

Planta Baixa - Caixa de inspeção
1 : 10

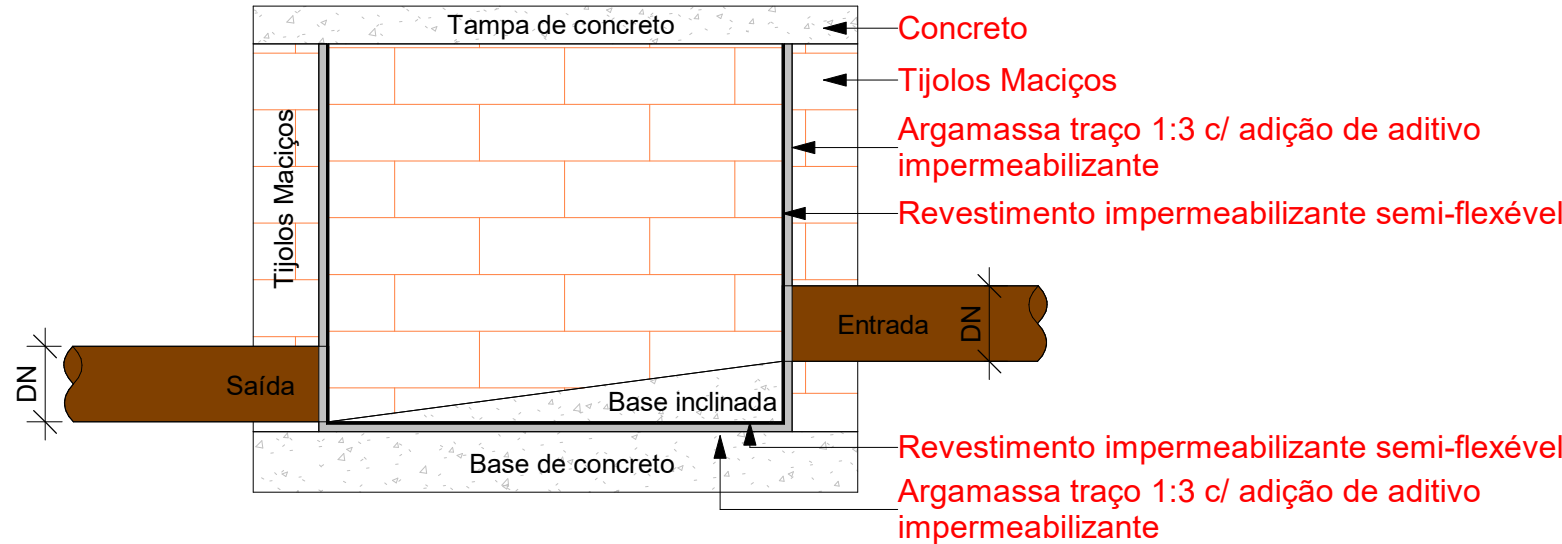

Corte lateral - Caixa de inspeção
1 : 10

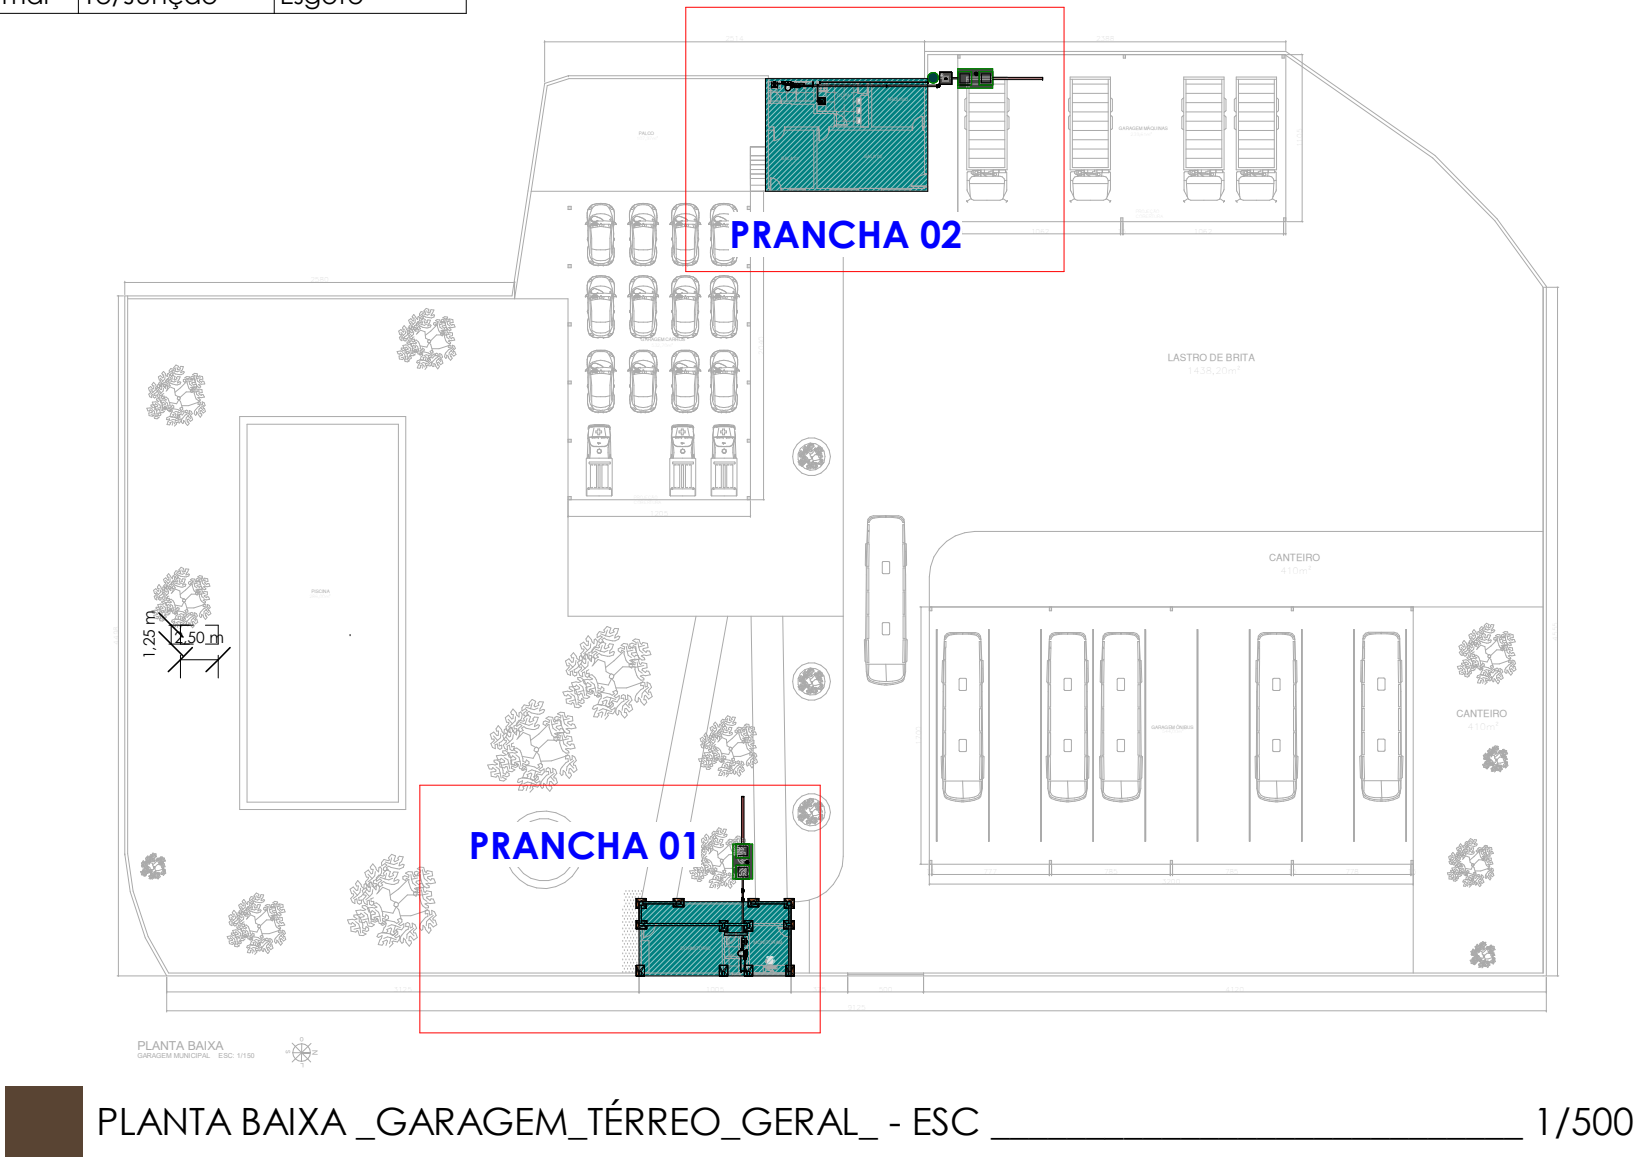

PROPRIETÁRIO: PREFEITURA MUNICIPAL DE COREMAS - PB

PROJETO: LINCOLN CARTAXO DE LIRA JÚNIOR CREA 160.814.689-8

PROJETO: INSTALAÇÕES SANITÁRIAS DA REFORMA DA GARAGEM DE COREMAS
CONCEDENTE: PREFEITURA MUNICIPAL DE COREMAS - PB
CONVENIENTE: MUNICÍPIO DE COREMAS - PB
LOCAL: COREMAS - PB

		RESPONSÁVEL TÉCNICO	RUBRICA	DADOS
DATA	19/06/2025	LINCOLN CARTAXO		CREA 160.814.689-8
CÓPIA				
VISTO				

PRANCHA: 03 / 03
DESCRIÇÃO: PLANTA BAIXA - GERAL TÉRREO
MAPEAMENTO DAS PRANCHAS
QUANTITATIVOS E CORTE
ESCALA: INDICADA



Av. Gov. Flavio R. Coutinho, 500, sl. 601
Jd. Oceania, 58037-005 - João Pessoa (PB)
Tel +55 99924.4447
e-mail: contato@lclprojetos.com