




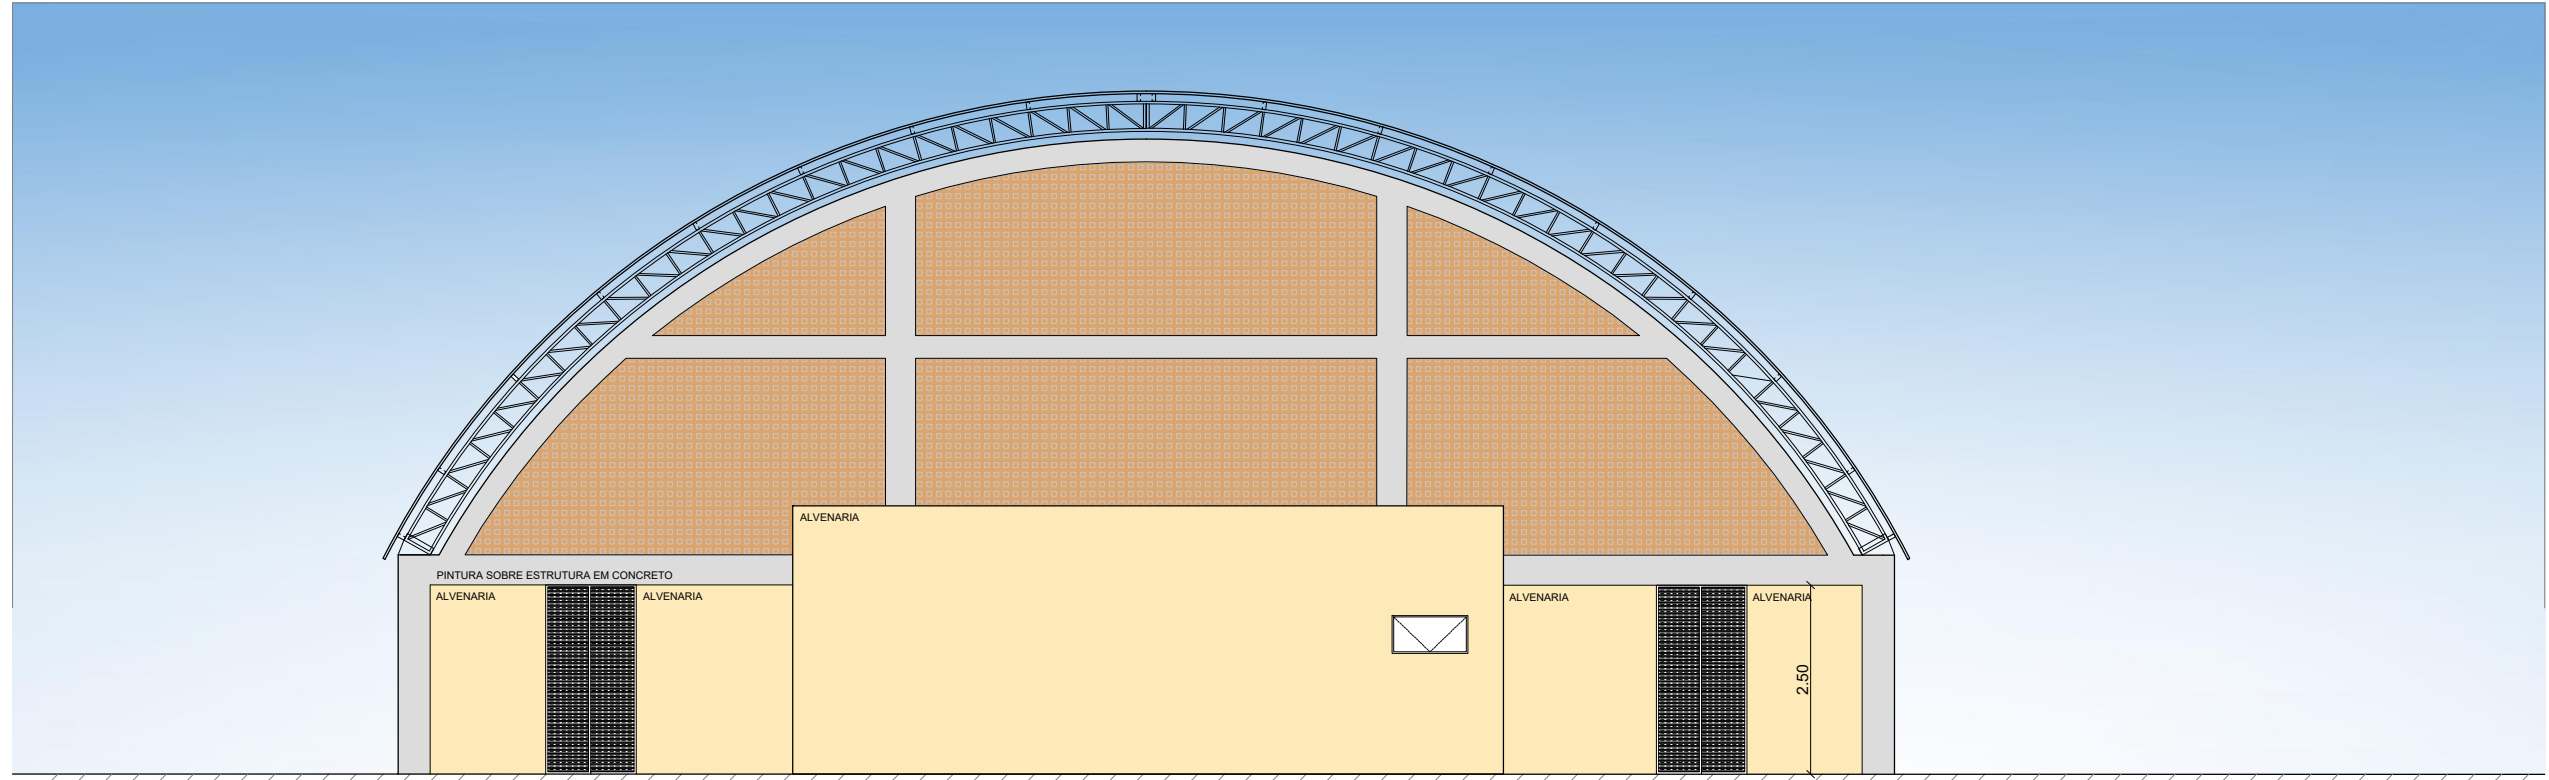


FACHADA 01
Escala 1:100

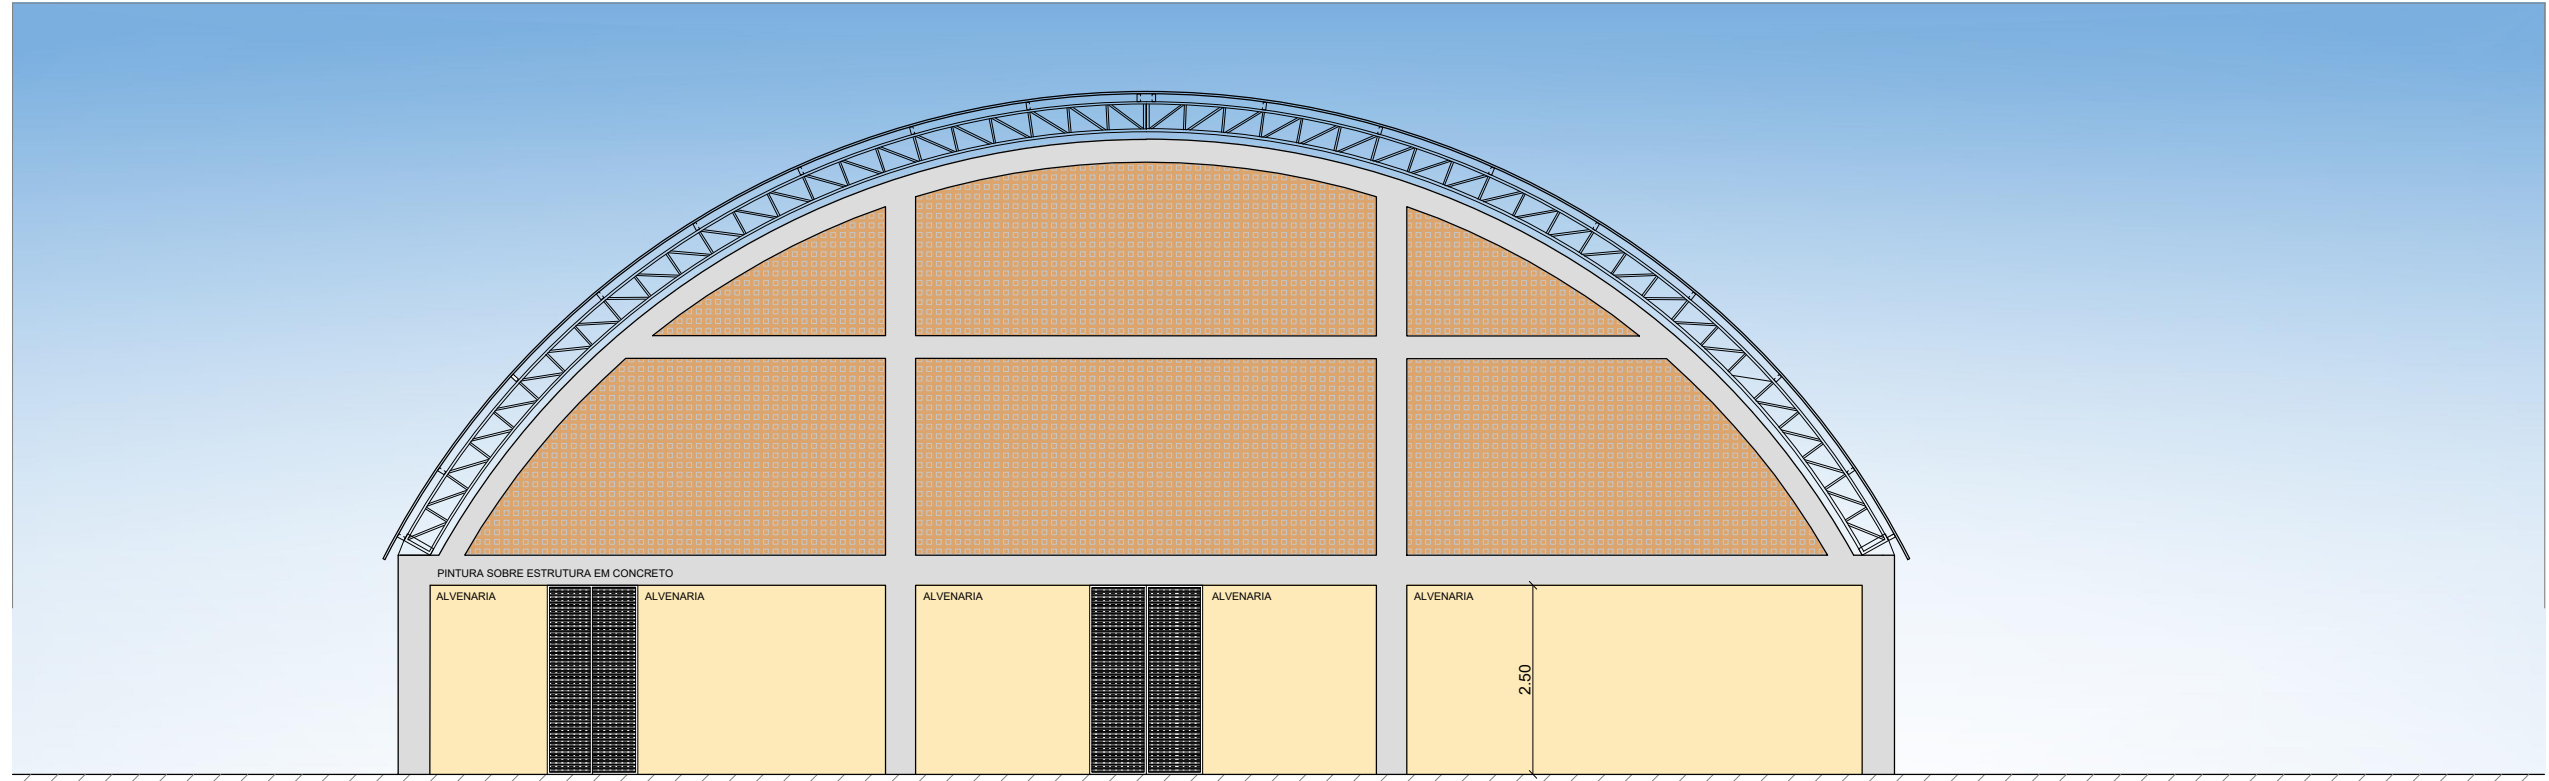

FACHADA 03
Escala 1:100

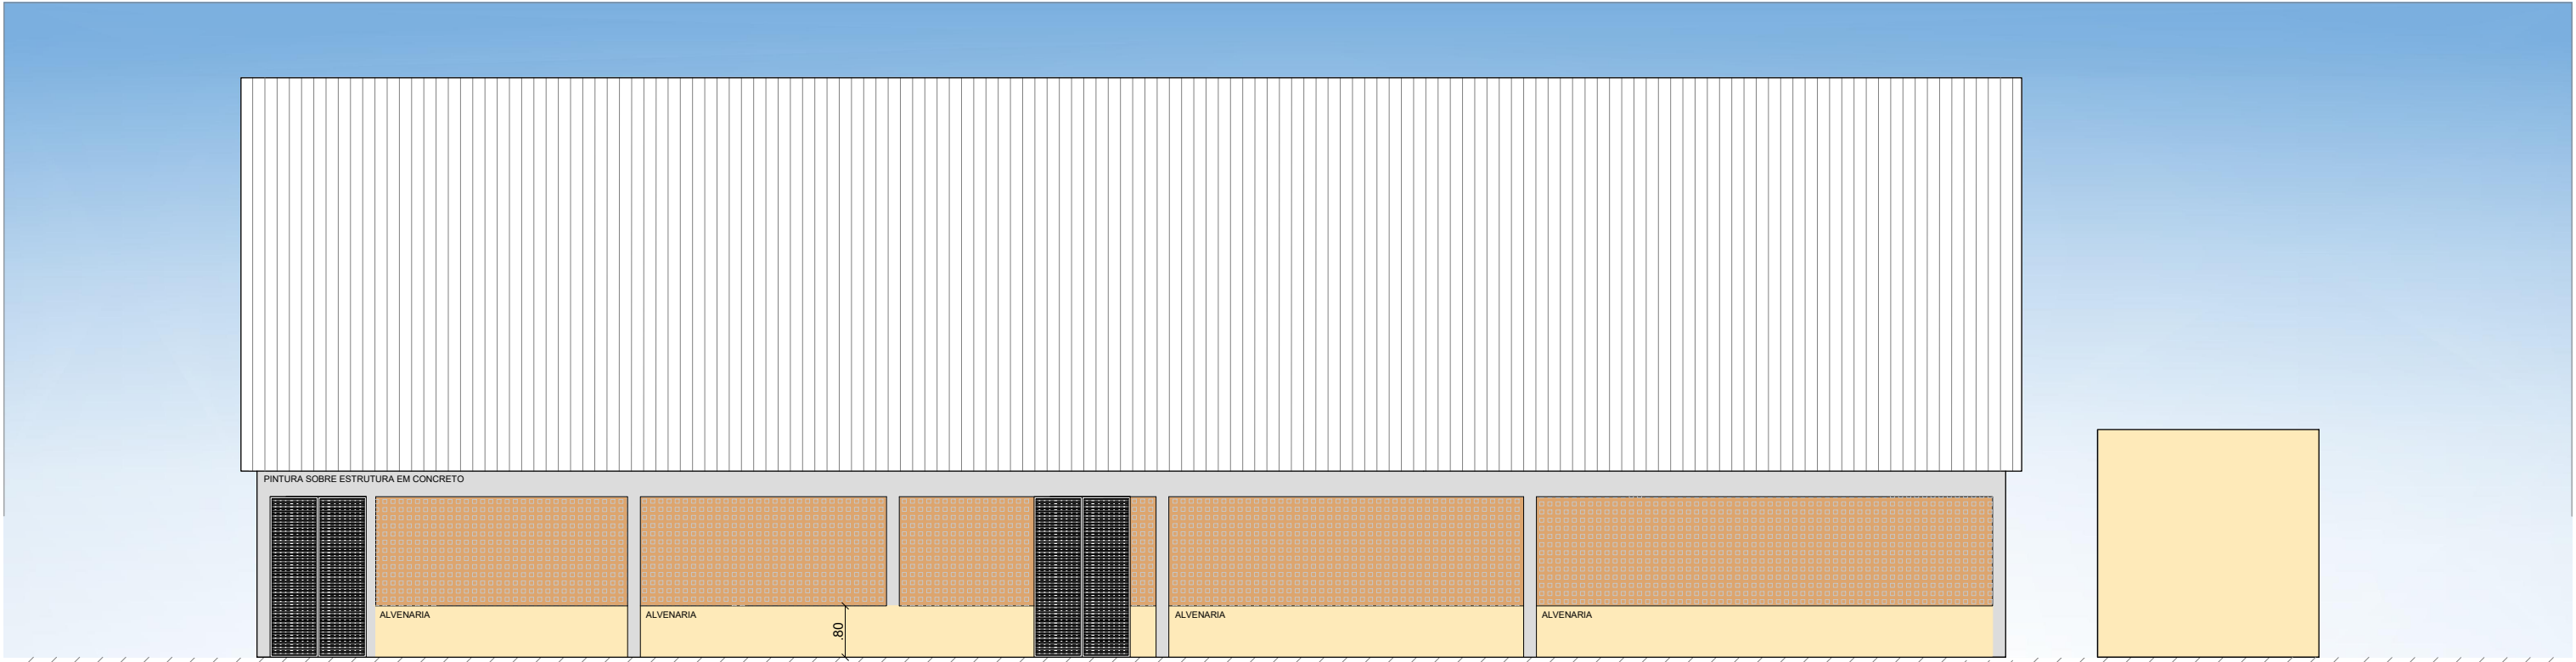

FACHADA 02
Escala 1:100

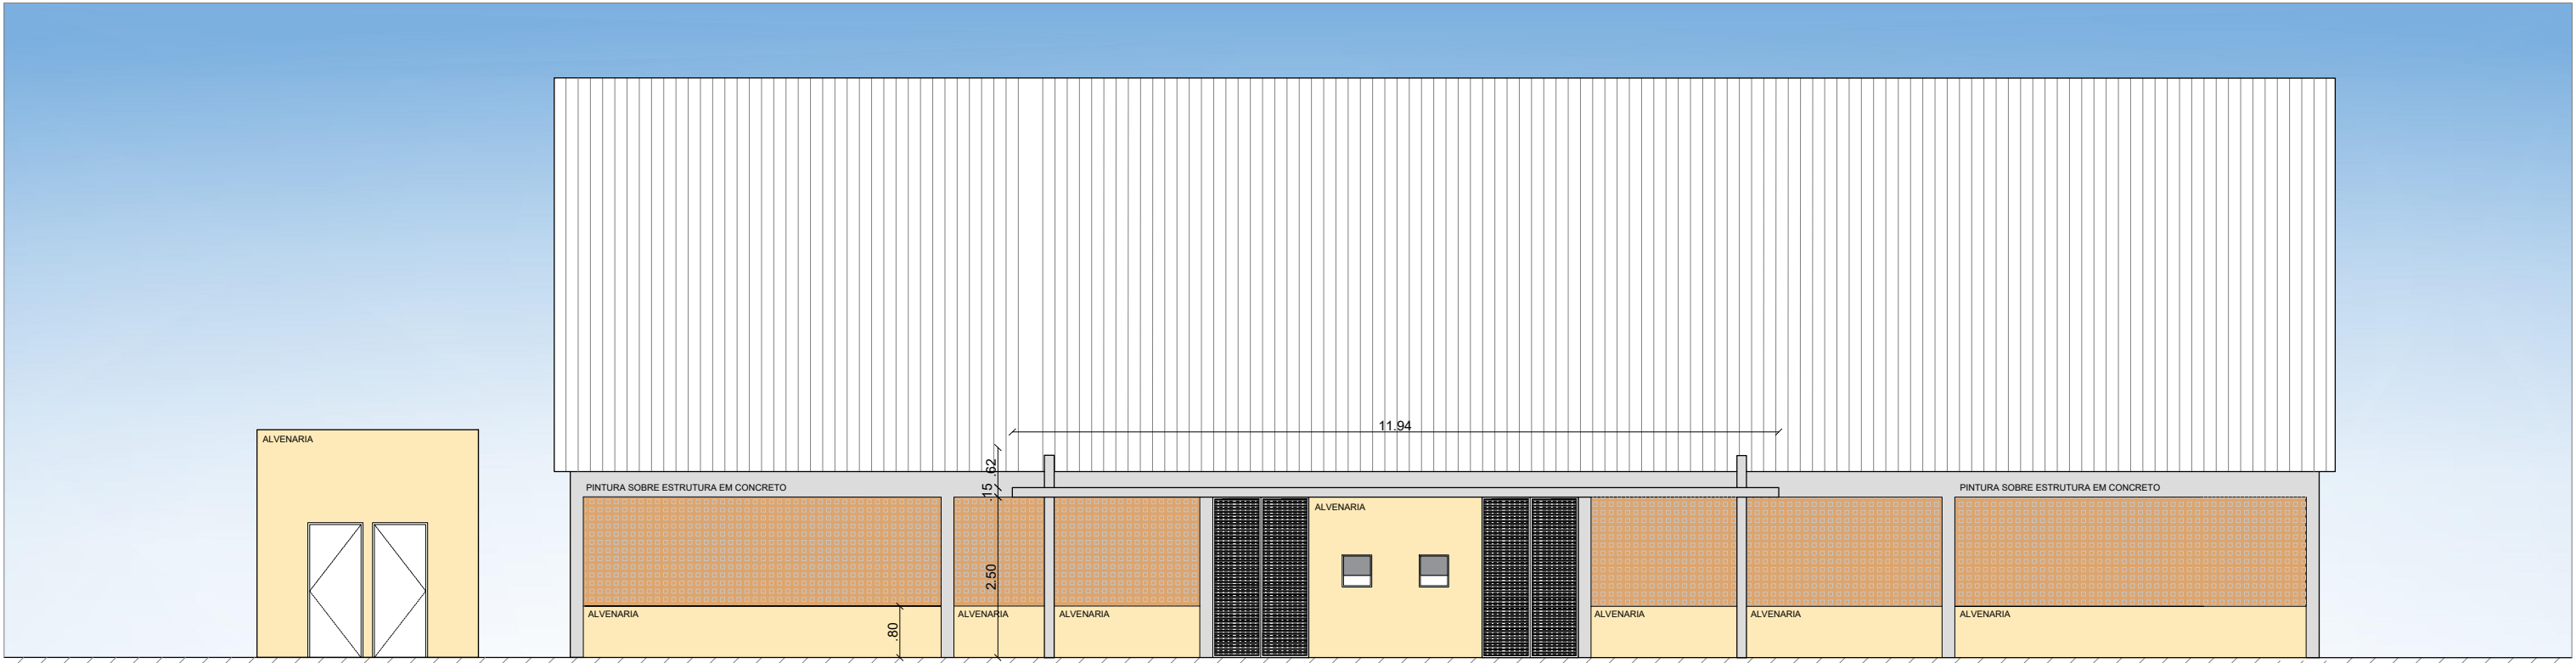

FACHADA 04
Escala 1:100

QUADRO DE REVESTIMENTO - FACHADAS	
CONVENÇÃO	DESCRIÇÃO
	PAREDES EM ALVENARIA PINTADAS COM TINTA LÁTEX ACRÍLICA PARA ÁREAS EXTERNAS
	ESTRUTURA EM CONCRETO ARMADO REVESTIDA COM PINTURA LÁTEX ACRÍLICA PARA ÁREAS EXTERNAS
	COBOGÔ CERÂMICO

PROPRIETÁRIO: PREFEITURA MUNICIPAL DE COREMAS - PB

LINCOLN CARTAXO DE LIRA JÚNIOR:06897861405 Assinado de forma digital por LINCOLN CARTAXO DE LIRA JÚNIOR:06897861405
Dados: 2026.08.07 15:09:35 -03'00'

PROJETO: LINCOLN CARTAXO DE LIRA JÚNIOR CREA 160.814.689-8

CONSTRUÇÃO:

FOLHA 01/01

PROJETO: CONSTRUÇÃO DE GINÁSIO POLIESPORTIVO

CONVENENTE: PREFEITURA MUNICIPAL DE COREMAS - PB

CONVENIADO: MUNICÍPIO DE COREMAS - PB

LOCALIDADE: MUNICÍPIO DE COREMAS - PB

	DATA	RESPONSÁVEL	RUBRICA	DADOS
DESENHO	AGO/2025	LINCOLN CARTAXO		
CÓPIA				
VISTO				
ESCALAS	DESENHOS			CONVÊNIO
INDICADAS	FACHADAS DETALHAMENTO DE PÓRTICO QUADRO DE REVESTIMENTOS: FACHADAS			ARQUIVO

Aprovações: