



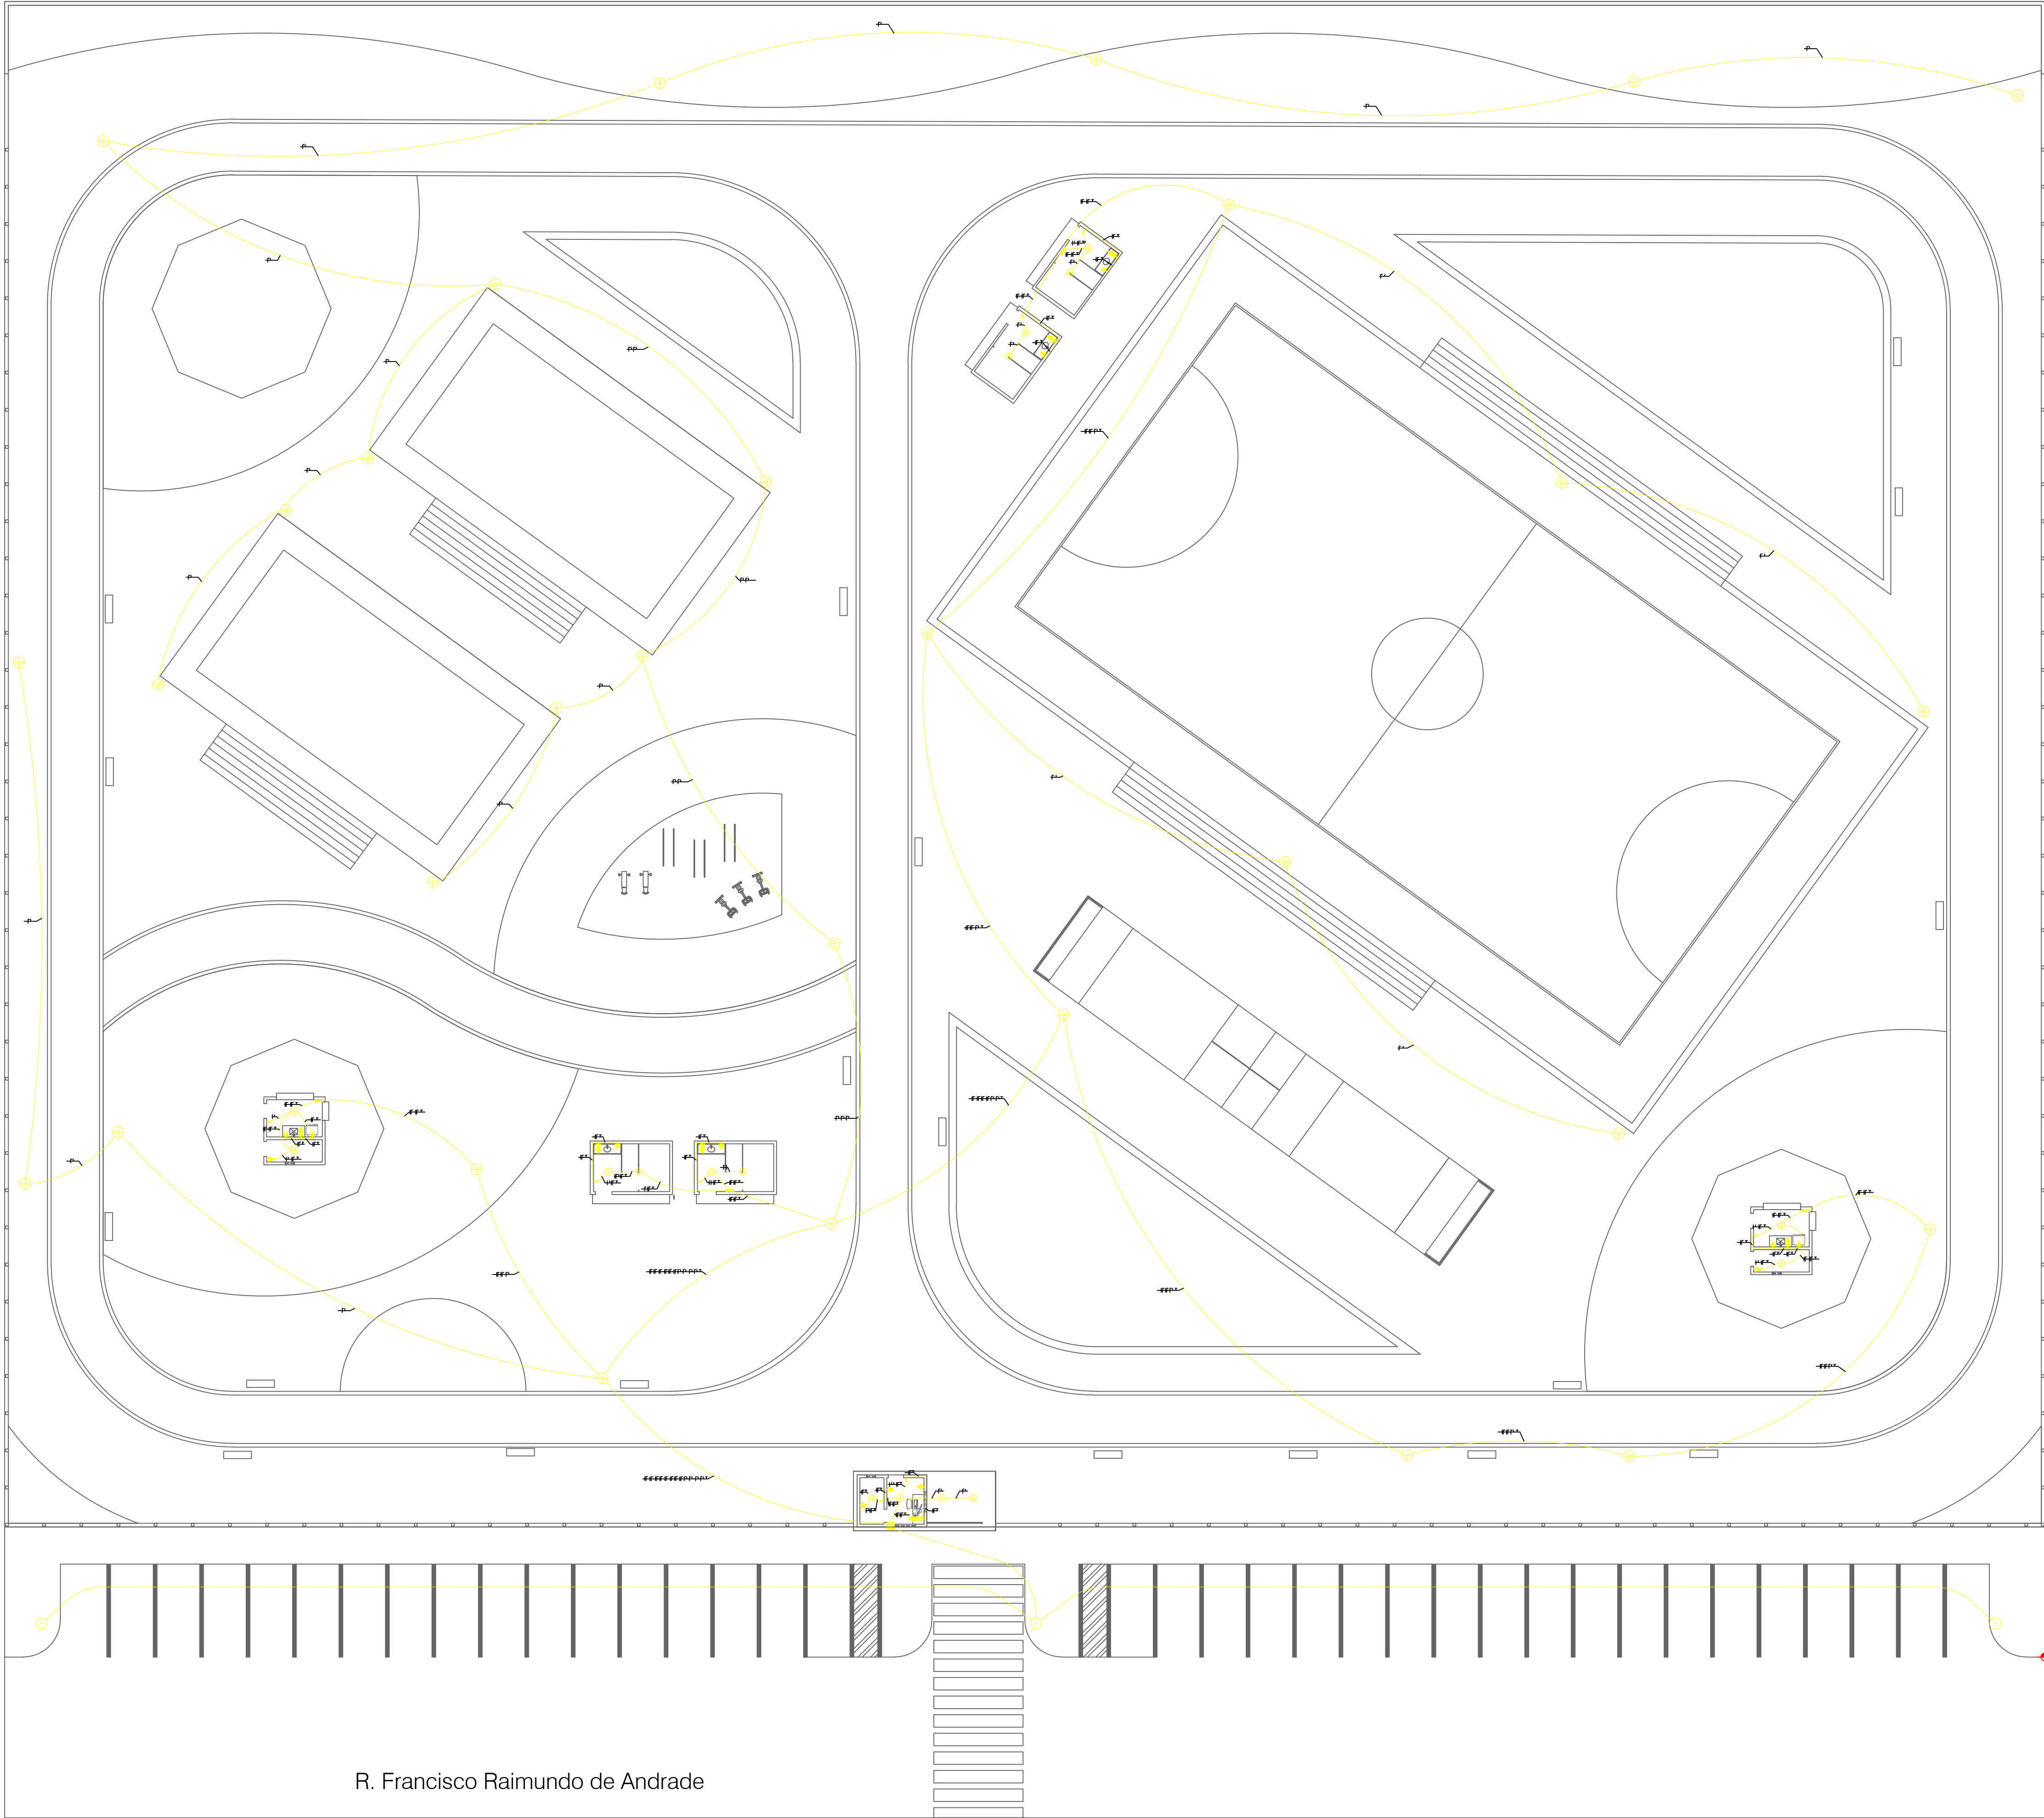

R. Francisco Raimundo de Andrade

PLANTA GERAL - COBERTA
COMPLEXO ESPORTIVO

ESC: 1/200

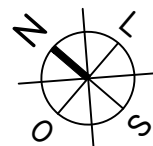


Projeto:

Projeto de Urbanismo Vila Olimpica

Desenhos:

PLANTA BAIXA COM DETALHAMENTO DOS PONTOS ELÉTRICOS

		QUADRO DE CARGAS - GERAL														
		Tensões (V)								Pot (W)						
Grupo	Descrição	10	20	100	200	300	600	1000	1800	For (VA)	Pot (VA)	IP	Tensão (V)	Corrente (A)	Cond. (mm²)	Restrição (A)
1	Iluminação Exterior		2			5				20	20	1	220	0,04	1,5	10
2	Tomadas Gerais		2			5				1000	1000	1	220	0,02	2,5	10
3	Iluminação Interiores 1		4			5		1		20	20	1	220	0,48	1,5	10
4	Tomadas Interiores 1		4			5				600	600	1	220	0,75	2,5	10
5	Iluminação Interiores 2		4			5				20	20	1	220	0,48	1,5	10
6	Tomadas Interiores 2		4			5				600	600	1	220	0,75	2,5	10
7	Iluminação Garagem 1		2			5				40	40	1	220	0,22	1,5	10
8	Tomadas Garagem 1		2			5				100	100	1	220	0,27	2,5	10
9	Iluminação Garagem 2		2			5				40	40	1	220	0,22	1,5	10
10	Tomadas Garagem 2		2			5				100	100	1	220	0,27	2,5	10
11	Tomadas Garagem 3			11		5				1100	1100	1	220	1,01	2,5	10
12	Iluminação Portas - Frente				11	5				1100	1100	1	220	1,45	2,5	10
13	Iluminação Portas - Quadra 1 Local				8					800	800	1	220	0,44	2,5	10
14	Iluminação Portas - Quadra 2 Local				2	1				800	800	1	220	0,44	2,5	10
15	Iluminação Portas - Quadra 3 Local				2	1				800	800	1	220	0,44	2,5	10
TOTAL		60	21	9	27			1		7980	7980	1	220	58,29	5,0	10

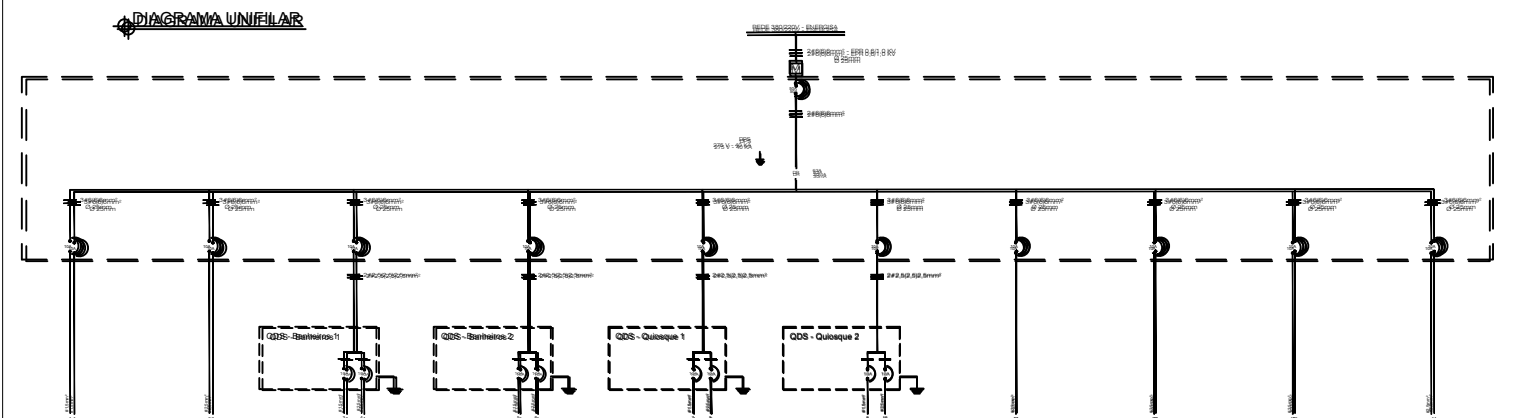

Observações:

- Conferir todas as medidas em obra antes da execução dos serviços.
- Não executar alterações sem autorização prévia do responsável técnico.
- Qualquer divergência entre projeto e condições de campo deverá ser comunicada ao responsável técnico para análise e aprovação.
- Todas as instalações deverão ser executadas por mão de obra qualificada, seguindo as normas técnicas vigentes e as recomendações dos fabricantes dos materiais empregados.
- O dimensionamento e posicionamentos indicados em projeto prevalecem sobre quaisquer informações complementares aqui descritas.

Esta prancha apresenta os detalhamentos das instalações elétricas devendo sua execução seguir rigorosamente as dimensões, níveis, materiais e especificações indicados em projeto.

- A alimentação da edificação será realizada através do quadro geral de distribuição (QDG), conforme indicado em projeto.
- Todos os circuitos deverão ser identificados e distribuídos conforme o diagrama unifilar e o quadro de cargas apresentados em projeto.
- As emendas de condutores somente poderão ser executadas no interior de caixas de passagem, caixas de derivação ou quadros elétricos.
- Todos os condutores deverão possuir isolamento adequado à tensão de operação e serem instalados sem danos mecânicos.
- Os condutores deverão possuir seção nominal conforme especificado em projeto.
- Os circuitos de iluminação, tomadas de uso geral (TUG), tomadas de uso específico (TUE) e equipamentos deverão respeitar as bitolas indicadas no quadro de cargas.
- Os eletrodutos deverão possuir diâmetros compatíveis com a quantidade e seção dos condutores instalados.
- Não será permitida a ocupação excessiva dos eletrodutos, devendo ser respeitadas as taxas máximas de ocupação previstas em norma.
- O quadro de distribuição deverá possuir barramentos independentes para neutro e aterramento.
- Todos os dispositivos de proteção deverão ser instalados conforme especificado em projeto.
- Os circuitos deverão ser protegidos por disjuntores termomagnéticos compatíveis com suas respectivas cargas.
- Quando especificado em projeto, deverão ser instalados dispositivos DR e DPS.
- Os quadros de distribuição deverão ser instalados nos locais indicados em projeto, garantindo fácil acesso para operação e manutenção.
- Não executar alterações sem autorização prévia do responsável técnico.
- Qualquer divergência entre projeto e condições de campo deverá ser comunicada ao responsável técnico para análise e aprovação.

Projetista:

Fernando Matias Mamede

RESPONSÁVEL TÉCNICO
Fernando Matias Mamede
Engenheiro Civil
Crea: 162056275-8

Proprietário:

Prefeitura Municipal de Coremas

PROPRIETÁRIO(A)

Endereço/Obra: Rua Francisco Raimundo de Andrade, DNOCS, Coremas - PB, 58770-000

ÁREAS	m²
Área do Terreno	10.733,41
Estacionamento	519,11
Calçada	249,64
Área verde	4.281,11

Prancha:

08/14