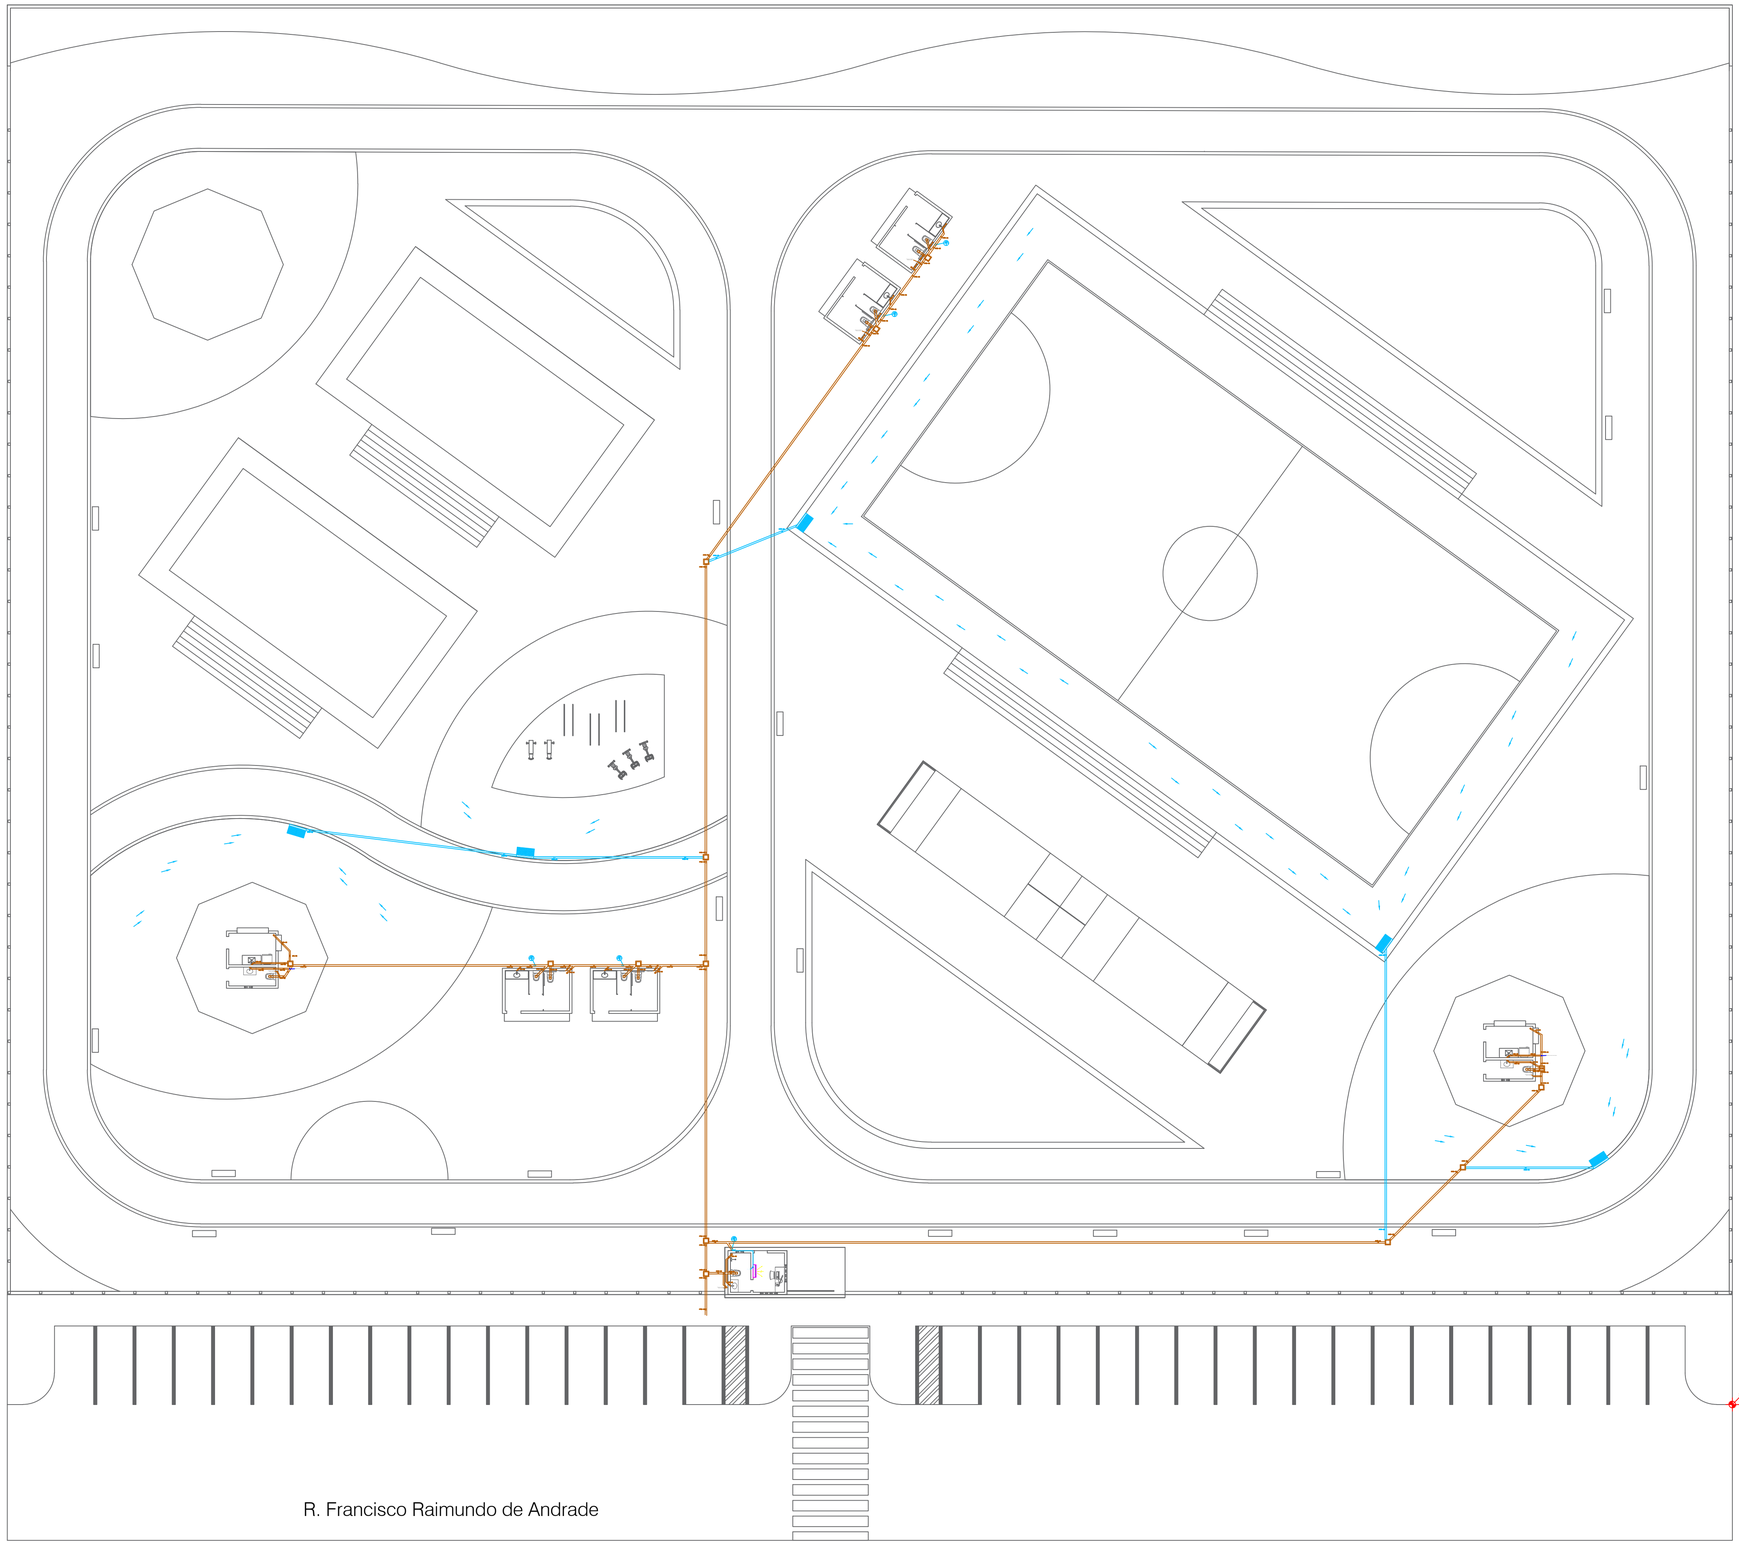


PLANTA GERAL - COBERTA
COMPLEXO ESPORTIVO ESC: 1/200

Projeto:

Projeto de Urbanismo Vila Olimpica

Desenhos:

PLANTA BAIXA COM DETALHAMENTO DOS PONTOS DE ESGOTO SANITÁRIO

- Conferir todas as medidas em obra antes da execução dos serviços.
- Não executar alterações sem autorização prévia do responsável técnico.
- Qualquer divergência entre projeto e condições de campo deverá ser comunicada ao responsável técnico para análise e aprovação.
- Todas as instalações deverão ser executadas por mão de obra qualificada, seguindo as normas técnicas vigentes e as recomendações dos fabricantes dos materiais empregados.
- Os diâmetros, declividades, cotas e posicionamentos indicados em projeto prevalecem sobre quaisquer informações complementares aqui descritas.

Esta prancha apresenta os detalhamentos das instalações de esgoto sanitário devendo sua execução seguir rigorosamente as dimensões, níveis, materiais e especificações indicados em projeto.

- Ramais de esgoto sanitário: DN 75 mm com declividade mínima de 1%.
- Ramais de bacias sanitárias: DN 100 mm com declividade mínima de 1%.
- Coletor principal de esgoto: DN 100 mm com declividade mínima de 1%.
- O sistema contará com caixas de inspeção nos locais indicados em projeto.
- O sistema será provido de ventilação sanitária através de tubulações de ventilação dimensionadas e posicionadas conforme projeto.
- Todas as conexões deverão ser executadas no sentido do fluxo, respeitando os diâmetros, declividades e cotas indicados em projeto.
- Antes da entrada em operação, deverá ser realizado teste de estanqueidade em toda a rede.

Projetista:
Fernando Matias Mamede

RESPONSÁVEL TÉCNICO
Fernando Matias Mamede
Engenheiro Civil
Crea: 162056275-8

Proprietário:
Prefeitura Municipal de Coremas

PROPIETÁRIO(A)

Endereço/Obra: Rua Francisco Raimundo de Andrade, DNOCS, Coremas - PB, 58770-000

ÁREAS	m²
Área do Terreno	10.733,41
Estacionamento	519,11
Calçada	249,64
Área verde	4.281,11

Prancha:
13/14