




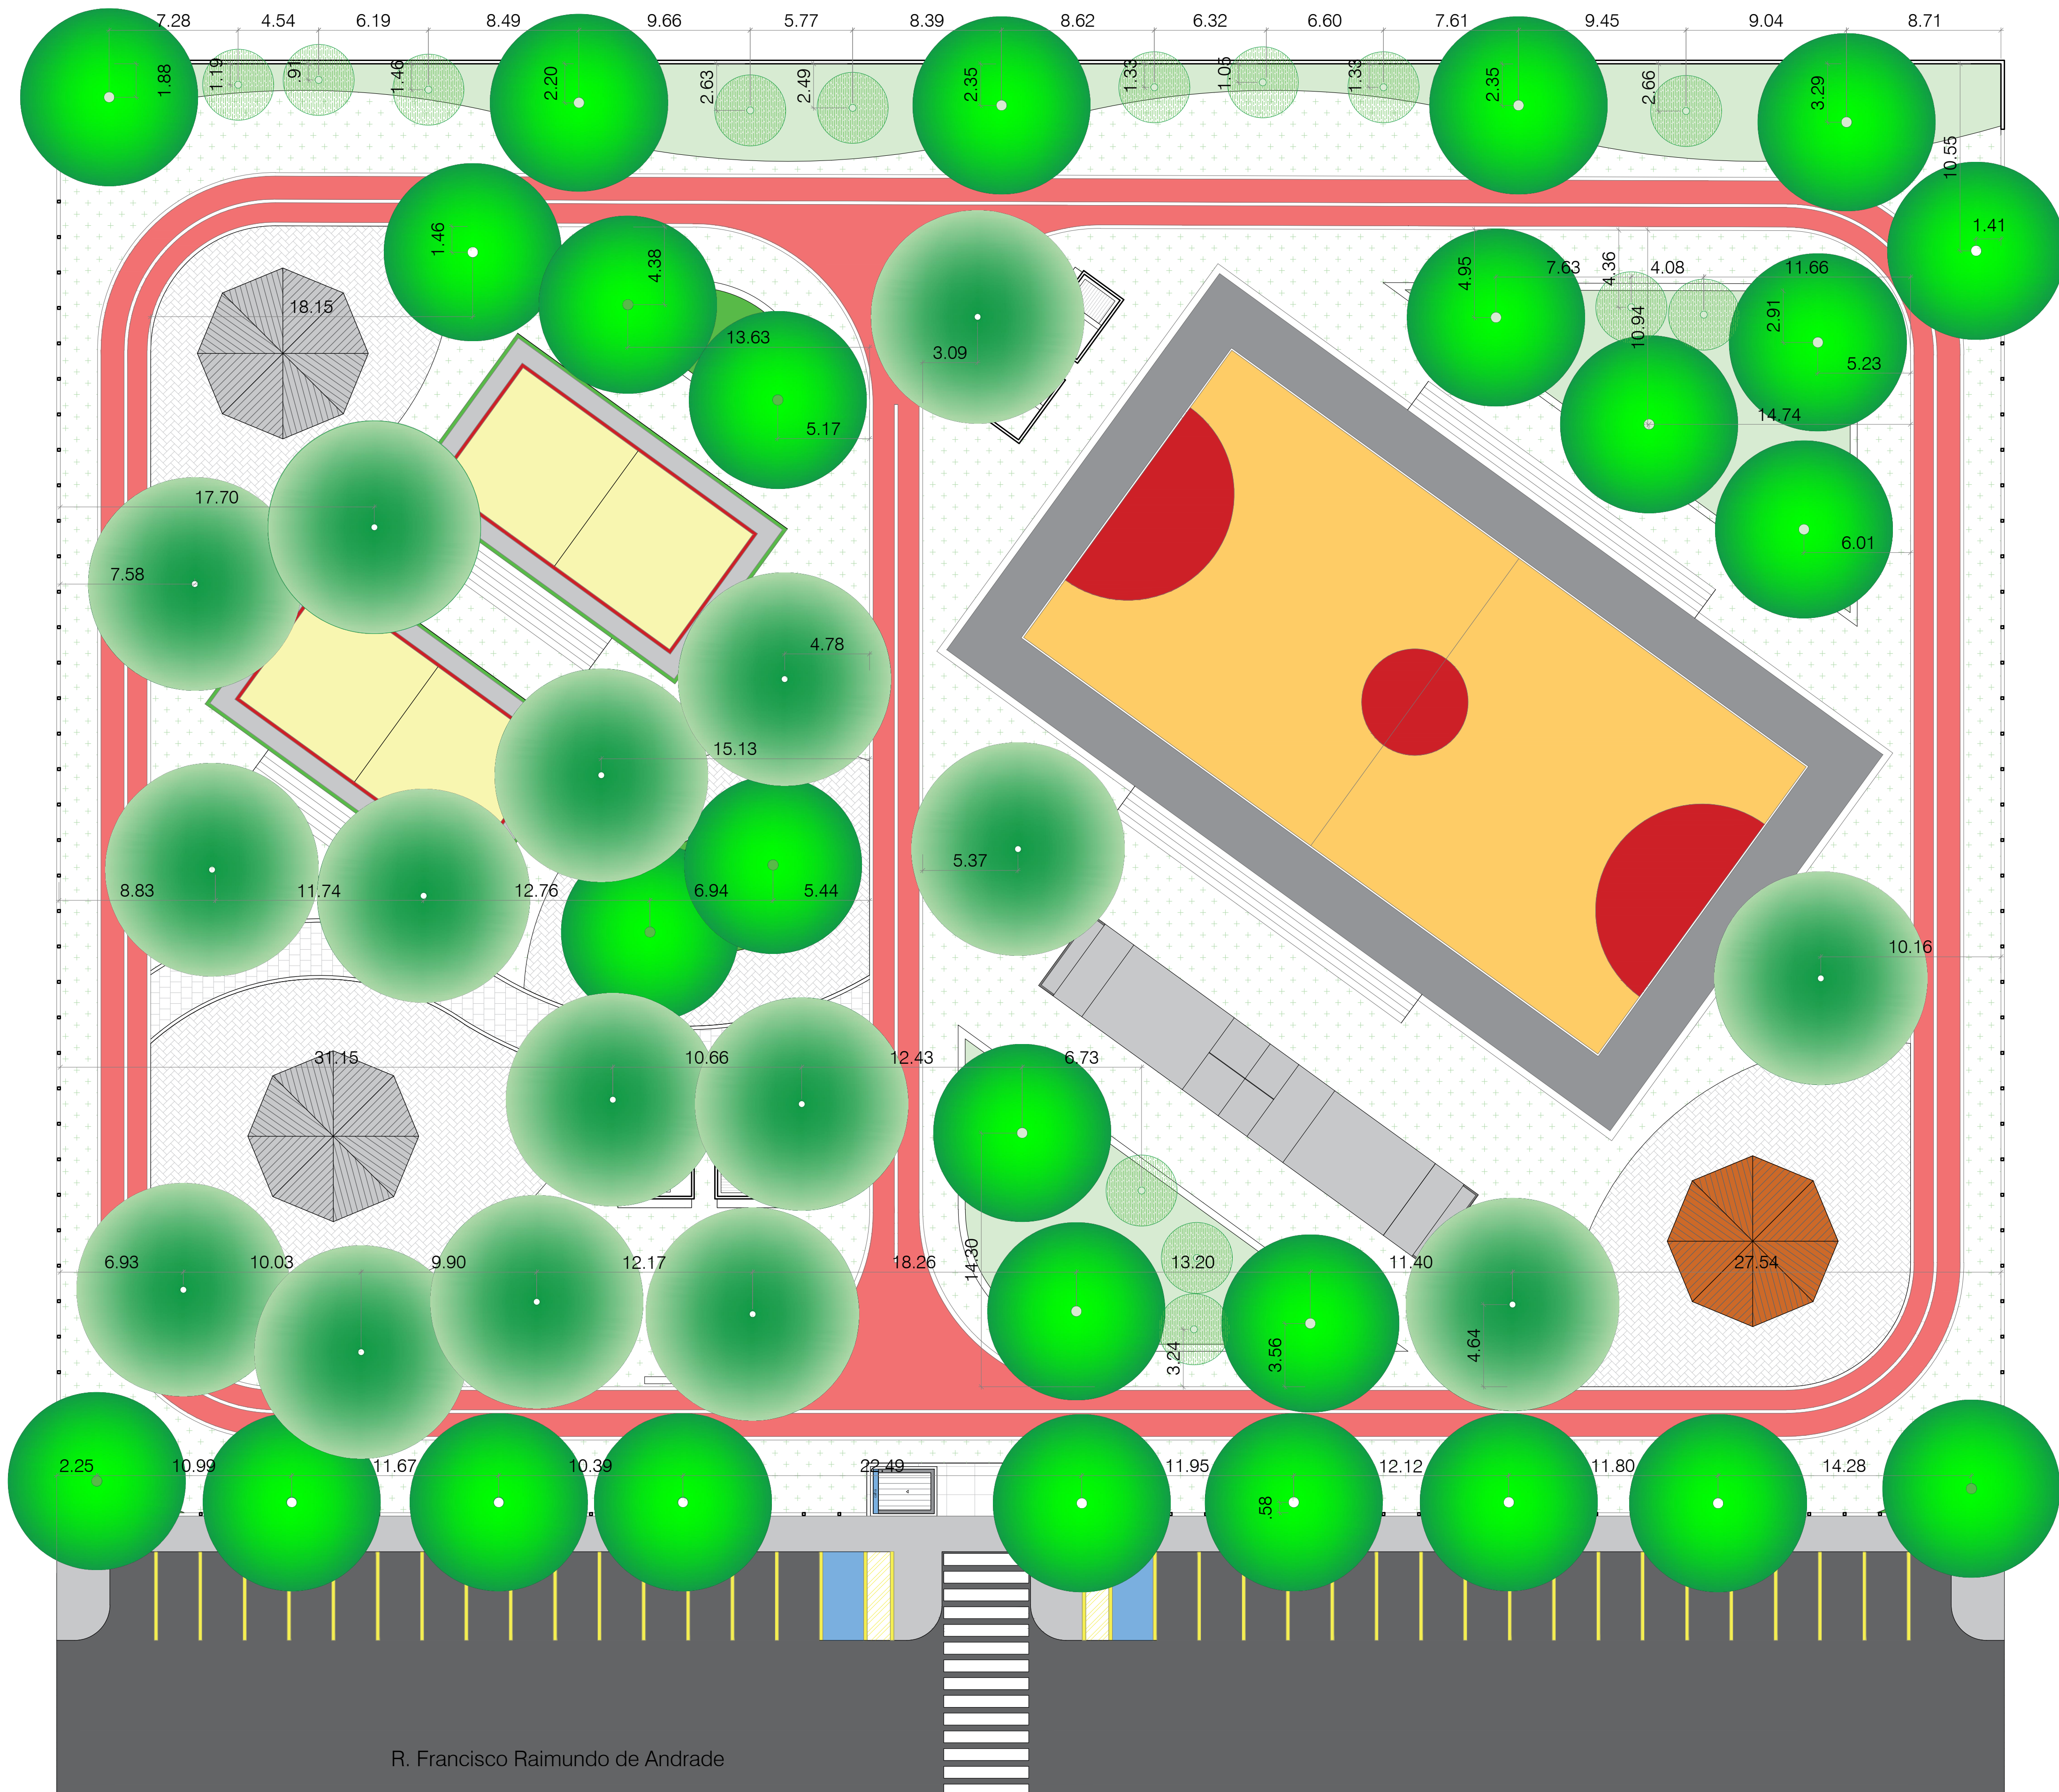

PLANTA GERAL - COBERTA
COMPLEXO ESPORTIVO
ESC: 1/200

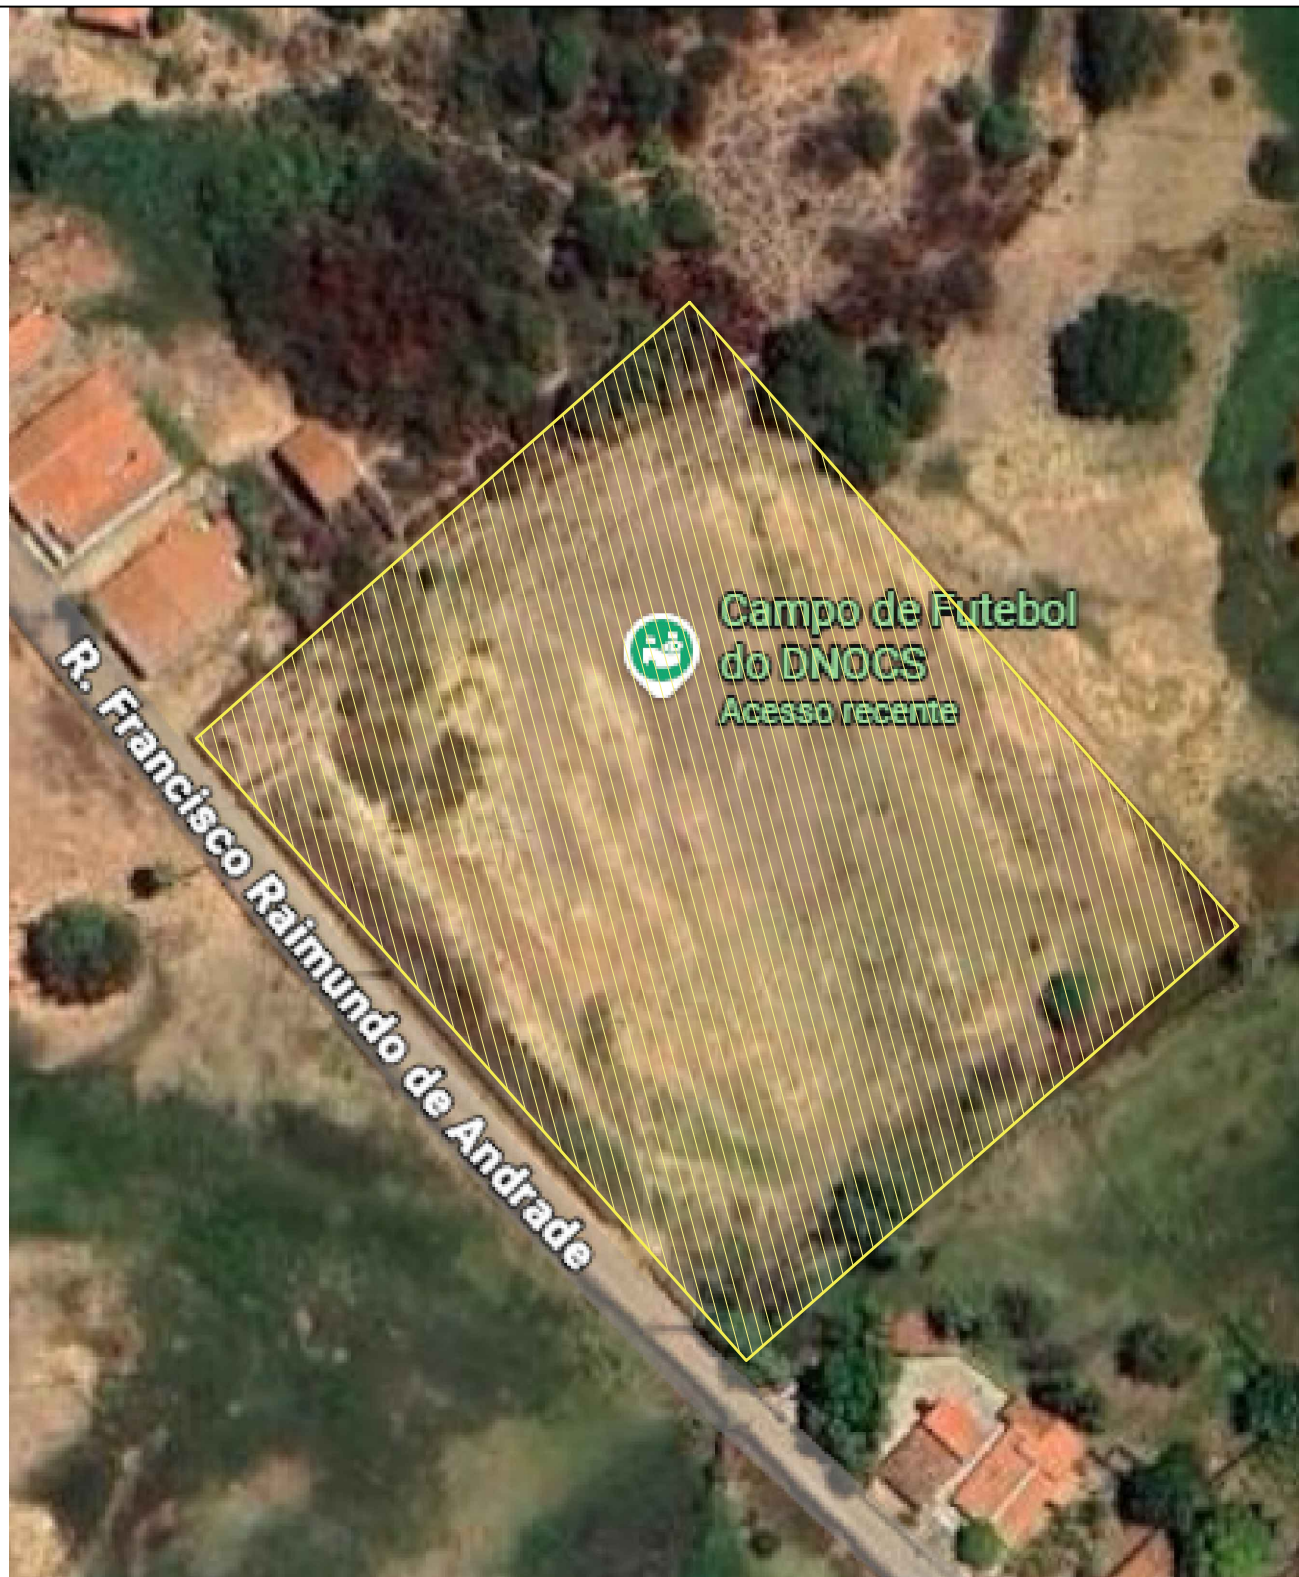

PLANTA DE LOCALIZAÇÃO
COMPLEXO ESPORTIVO
ESC: 1/1000

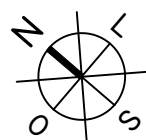


QUADRO DE ÁREAS:

- Banheiros: 68,12m²
- Pracinhas (piso de intertravado): 1.252,49m²
- Pista de corrida: 1.261,55m²
- Calçada: 249,64m²
- Pista de skate: 135,00m²
- Quadra de futsal (total): 1.269,00m²
- Quadra de areia 01: 203,40m²
- Quadra de areia 02: 203,40m²
- Guarita: 24,48m²
- Estacionamento: 519,11m²

Documento assinado digitalmente
gov.br
KIRYA CRISTINE BATISTA JUSTINO
Data: 10/09/2024 09:15:46-0300
Verifique em <https://validar.br.gov.br>

Projeto: Projeto de Urbanismo Vila Olímpica		Prancha nº: 01/05		
Desenhos: PLANTA GERAL COBERTA (COPA VEGETAÇÃO) PLANTA DE LOCALIZAÇÃO QUADRO DE ÁREAS				
Proprietário: PREFEITURA MUNICIPAL DE COREMAS				
Endereço/Obra: R. Francisco Raimundo de Andrade, bairro DNOCS, Coremas				
ÁREAS	m²	Data: MAIO/2026		
Área do Terreno	10.733,41	Área Total Construída	4.821,36m²	Desenhista: KIRYA CRISTINNE
Estacionamento	519,11	T. Ocupação	25,33%	
Calçada	249,64	I. Aproveitamento	0,44	
Área verde	4.281,11	T. Permeabilidade do Solo	39,88%	
Técnicos Responsáveis				
PROPRIETÁRIO (A): _____ RESPONSÁVEL TÉCNICO: _____				
ARQUITETURA E URBANISMO C.A. ALVES & P. (011) 9835.0759 (WH)				

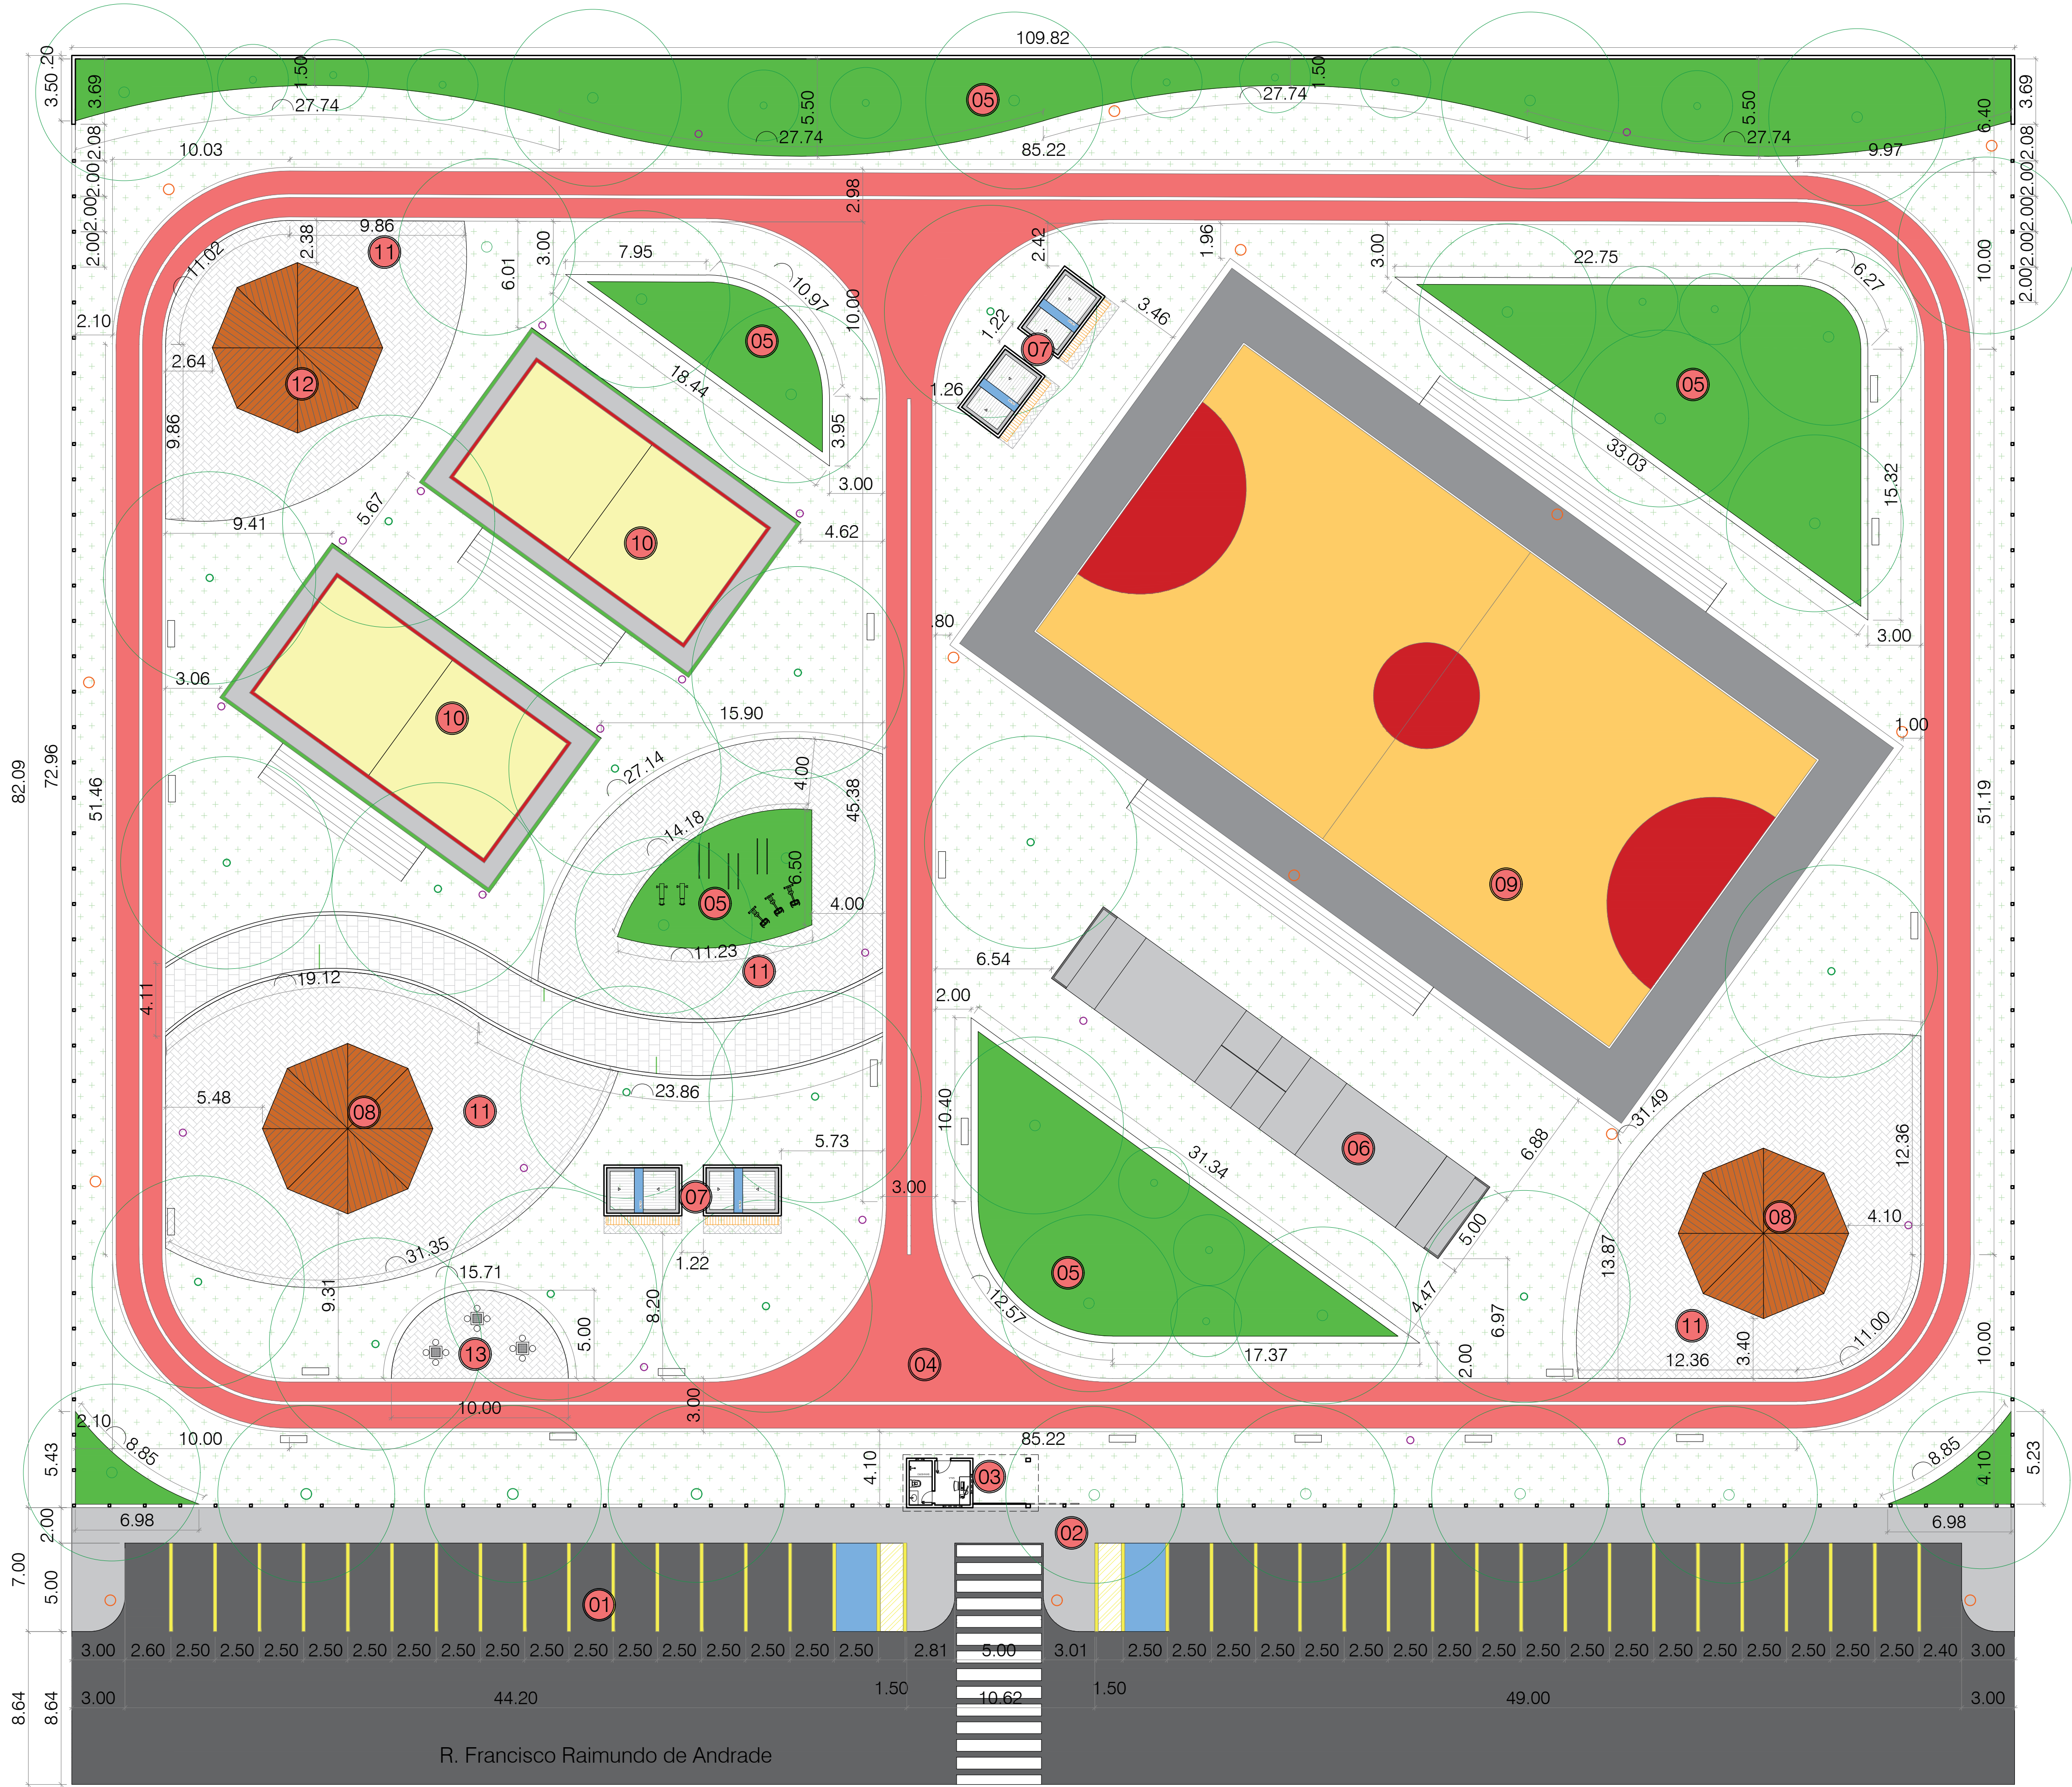

Quadro de especificações:

- Planta Sibipiruna
- Planta Palmeira Areca
- Planta Oiti
- Piso do terreno natural
- Gramma esmeralda
- Pista feita de concreto e pintura
- Piso intertravado
- Rua asfaltada
- Pintura de piso para vaga de deficiente
- Pintura de piso para estacionamento
- Poste de concreto (5m)
- Poste de concreto (10m)

- 01 Estacionamento
- 02 Calçada
- 03 Guarita
- 04 Pista de corrida
- 05 Canteiro com grama
- 06 Pista de skate
- 07 Banheiros
- 08 Quiosque
- 09 Quadra futsal
- 10 Quadra de areia
- 11 Praça com intertravado
- 12 Pergolado
- 13 Praça para jogos

Projeto:
**Projeto de Urbanismo
Vila Olímpica**

Prancha n°:
02/05

Desenhos:
**PLANTA BAIXA
LEGENDA**

ESCALAS INDICADAS

Proprietário:
PREFEITURA MUNICIPAL DE COREMAS

Endereço/Obra: **R. Francisco Raimundo de Andrade, bairro DNOCS, Coremas**

ÁREAS	m²	Área Total Construída	4.821,36m²	Data:	MAIO/2026
Área do Terreno	10.733,41	T. Ocupação	25,33%	Desenhista:	KIRYA CRISTINNE
Estacionamento	519,11	L. Aproveitamento	0,44		
Calçada	249,64	T. Permeabilidade do Solo	39,88%		
Área verde	4.261,11				

Técnicos Responsáveis


PROPRIETÁRIO (A):


RESPONSÁVEL TÉCNICO

ARQUITETURA E URBANISMO
CAU 0105963-3
(11) 99830-0759 (11h)


PLANTA BAIXA
COMPLEXO ESPORTIVO

ESC: 1/500

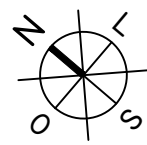


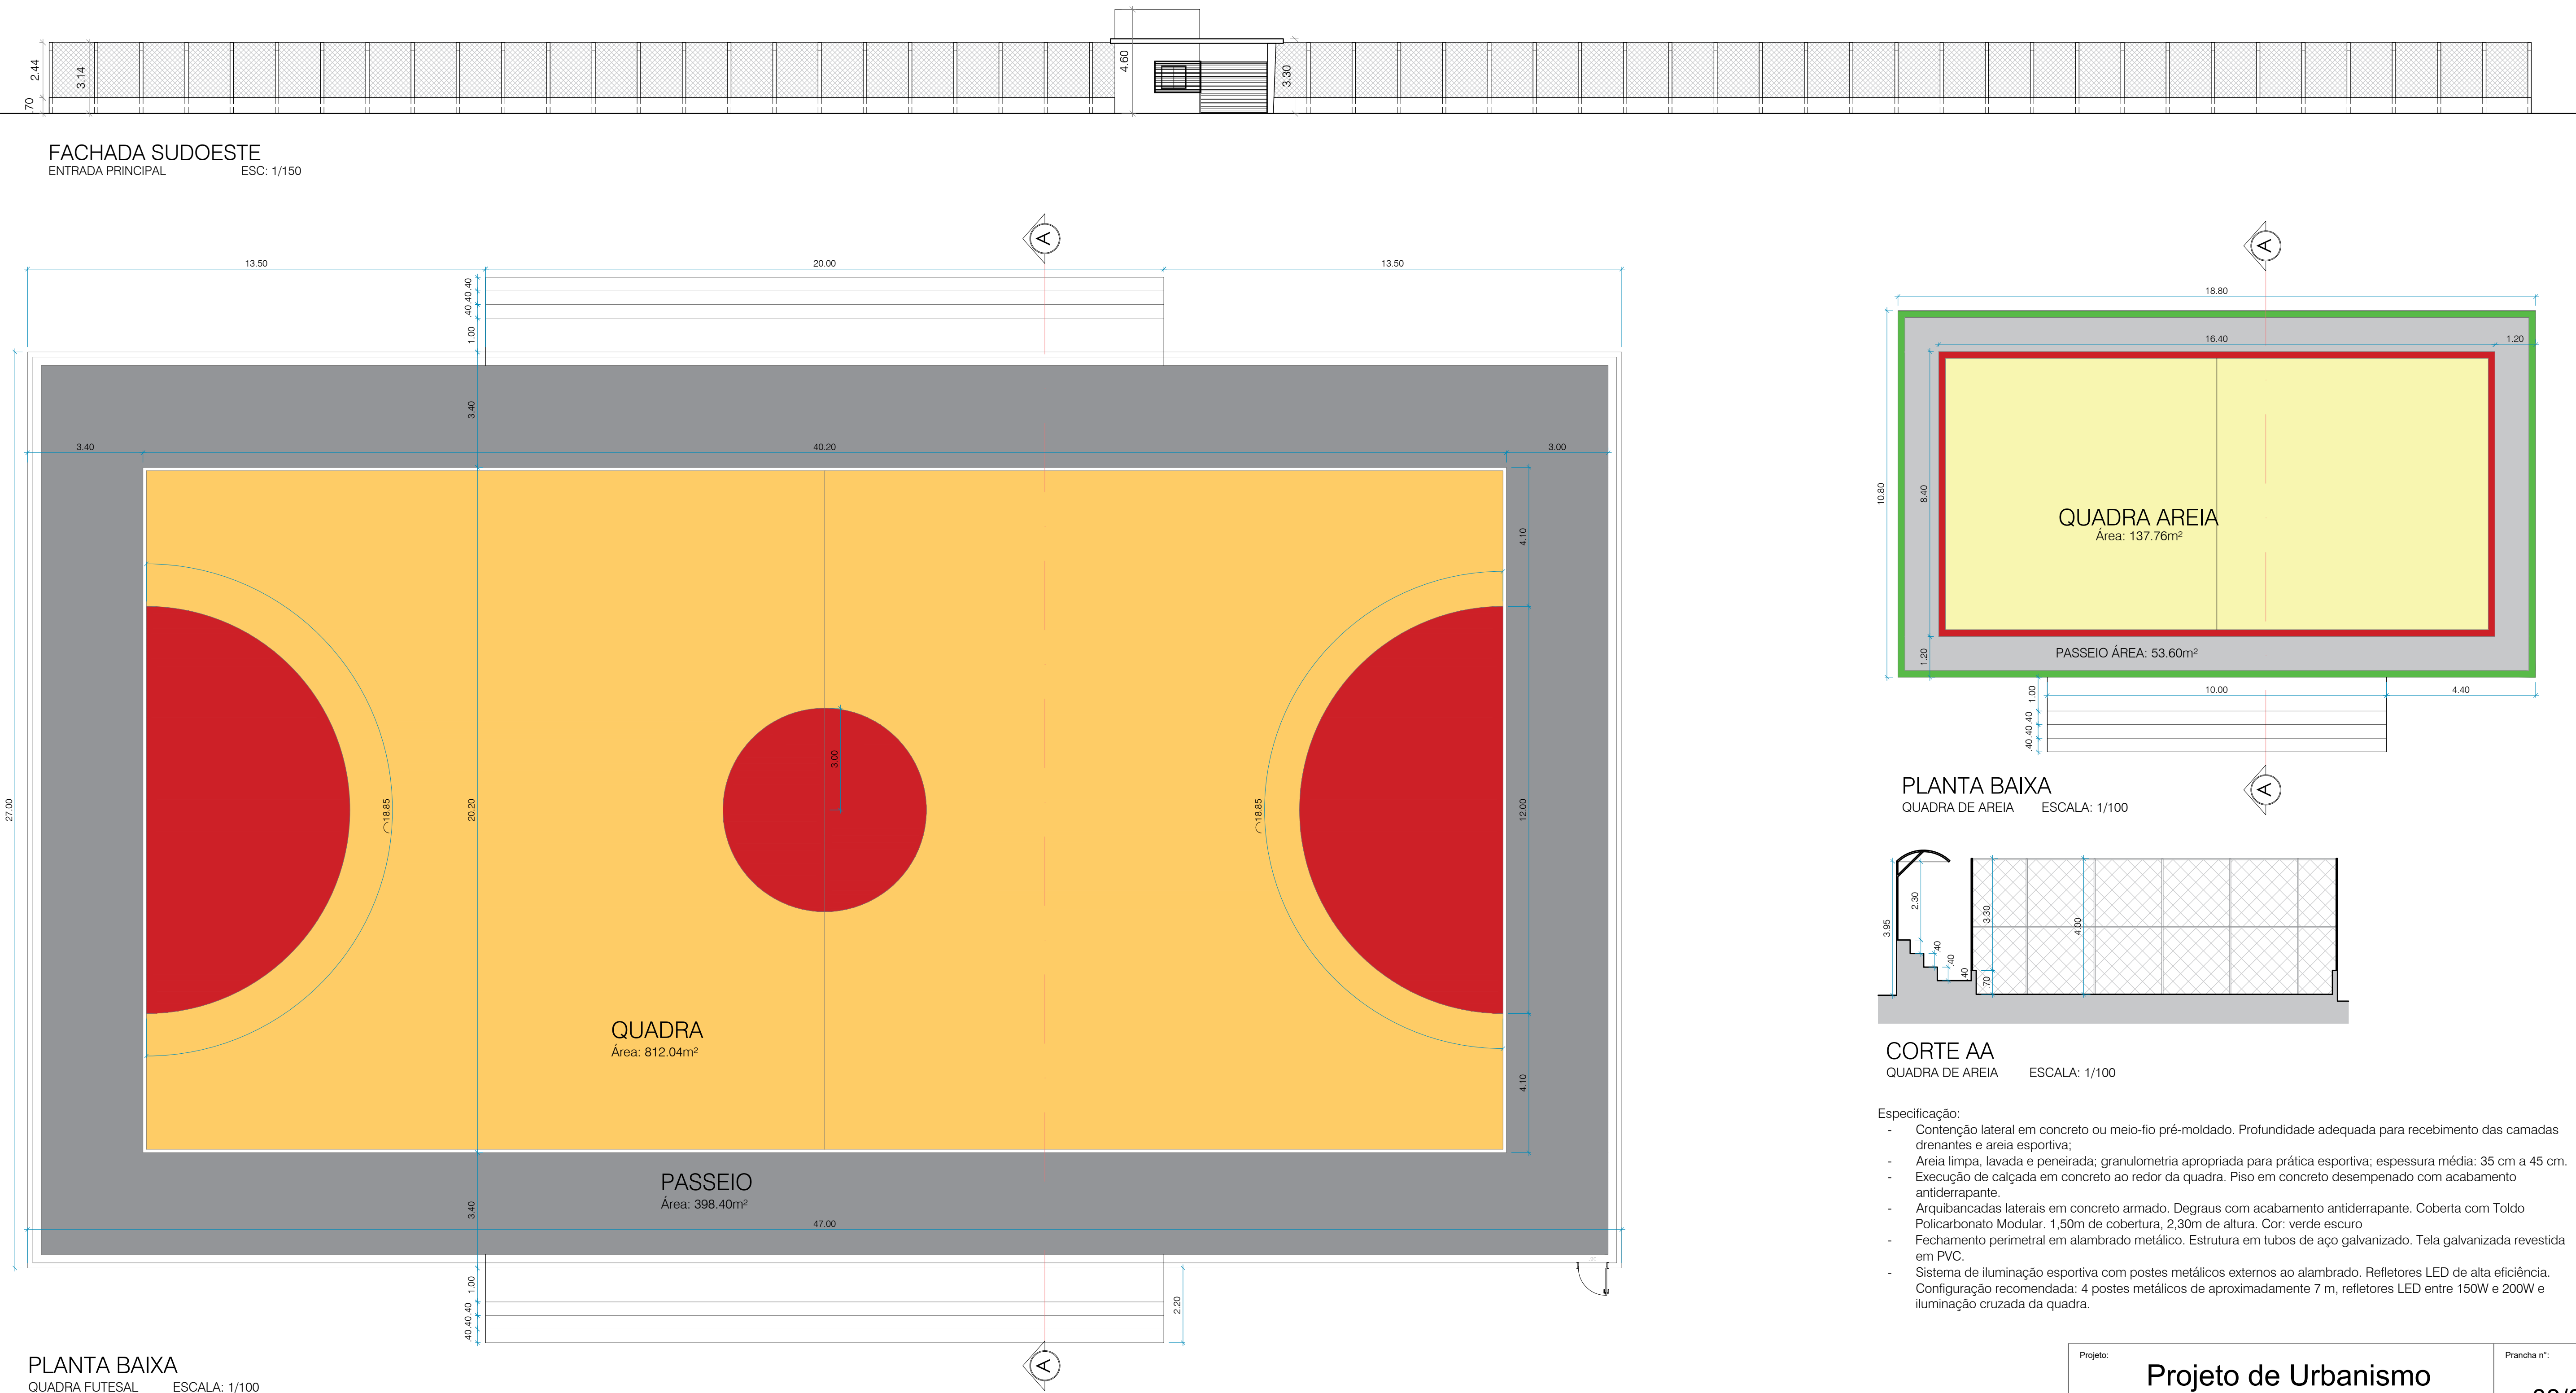


PLANTA BAIXA
QUADRA FUTESAL
ESCALA: 1/100

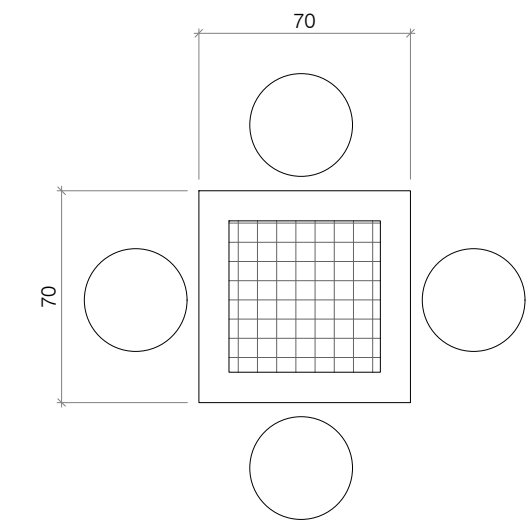

DETALHE
MESA DE JOGOS
ESC: 1/25

MESA DE JOGOS DE CONCRETO
COM 04 BANCOS DE CONCRETO
E DESENHO XADREZ NO TAMPO DA MESA


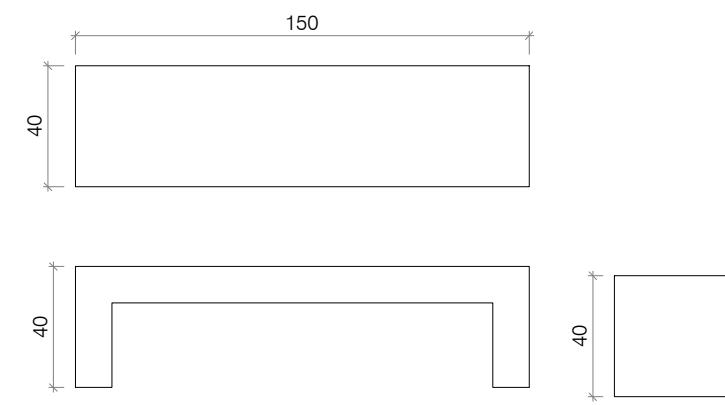
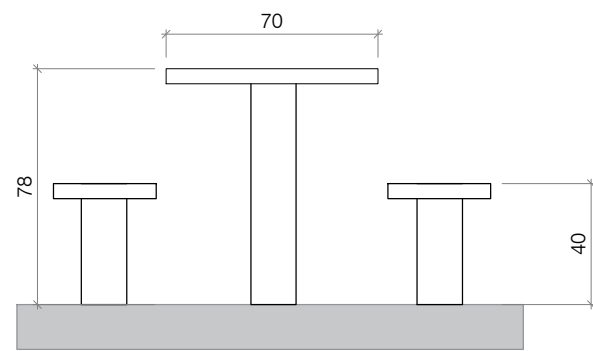


DETALHE BANCO
BANCO DE CONCRETO
ESC: 1/25






- Especificação:
- Contenção lateral em concreto ou meio-fio pré-moldado. Profundidade adequada para recebimento das camadas drenantes e areia esportiva;
 - Areia limpa, lavada e peneirada; granulometria apropriada para prática esportiva; espessura média: 35 cm a 45 cm.
 - Execução de calçada em concreto ao redor da quadra. Piso em concreto desempenado com acabamento antiderrapante.
 - Arquibancadas laterais em concreto armado. Degraus com acabamento antiderrapante. Coberta com Toldo Policarbonato Modular. 1,50m de cobertura, 2,30m de altura. Cor: verde escuro
 - Fechamento perimetral em alambrado metálico. Estrutura em tubos de aço galvanizado. Tela galvanizada revestida em PVC.
 - Sistema de iluminação esportiva com postes metálicos externos ao alambrado. Refletores LED de alta eficiência. Configuração recomendada: 4 postes metálicos de aproximadamente 7 m, refletores LED entre 150W e 200W e iluminação cruzada da quadra.


Projeto:		Prancha nº:	
Projeto de Urbanismo Vila Olímpica		03/05	
Desenhos:			
FACHADA QUADRA FUTSAL QUADRAS DE AREIA		BANCOS DE CONCRETO MESA DE JOGOS IMAGEM	
		ESCALAS INDICADAS	
Proprietário:			
PREFEITURA MUNICIPAL DE COREMAS			
Endereço/Obra: R. Francisco Raimundo de Andrade, bairro DNOCS, Coremas			
ÁREAS		Data:	
Área do Terreno	m²	Área Total Construída	m²
Estacionamento	519,11	T. Ocupação	25,33%
Calçada	249,64	I. Aproveitamento	0,44
Área verde	4.261,11	T. Permeabilidade do Solo	39,88%
Desenhista:		KIRYA CRISTINNE	
Técnicos Responsáveis			
PROPRIETÁRIO (A):		RESPONSÁVEL TÉCNICO	
 ARQUITETURA E URBANISMO CAYO ALVES LIMA ☎ (11) 9635.0755 (WH)			

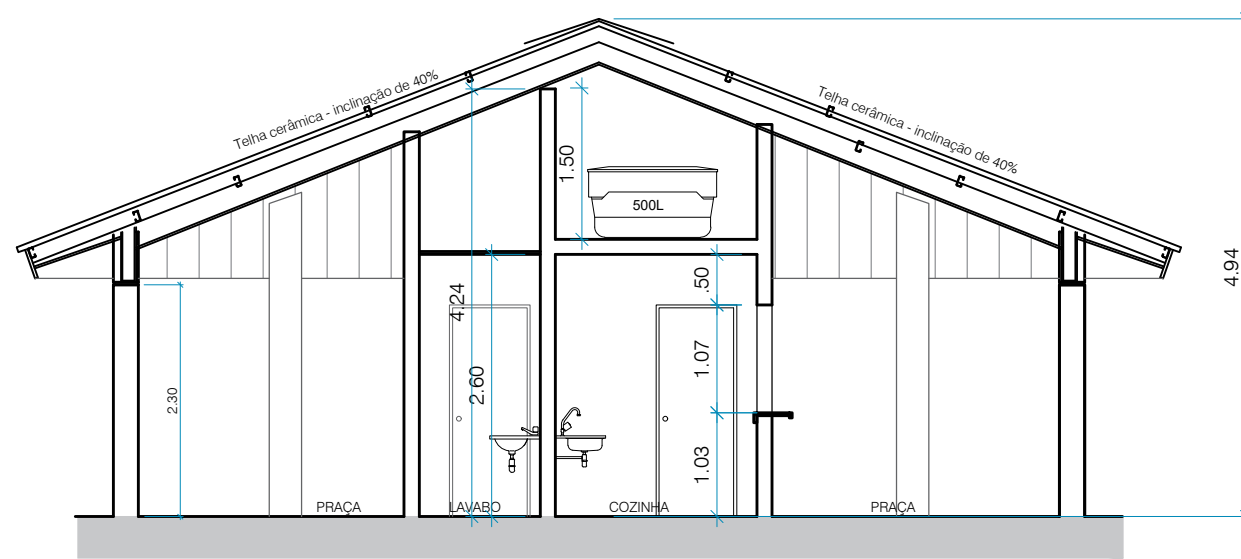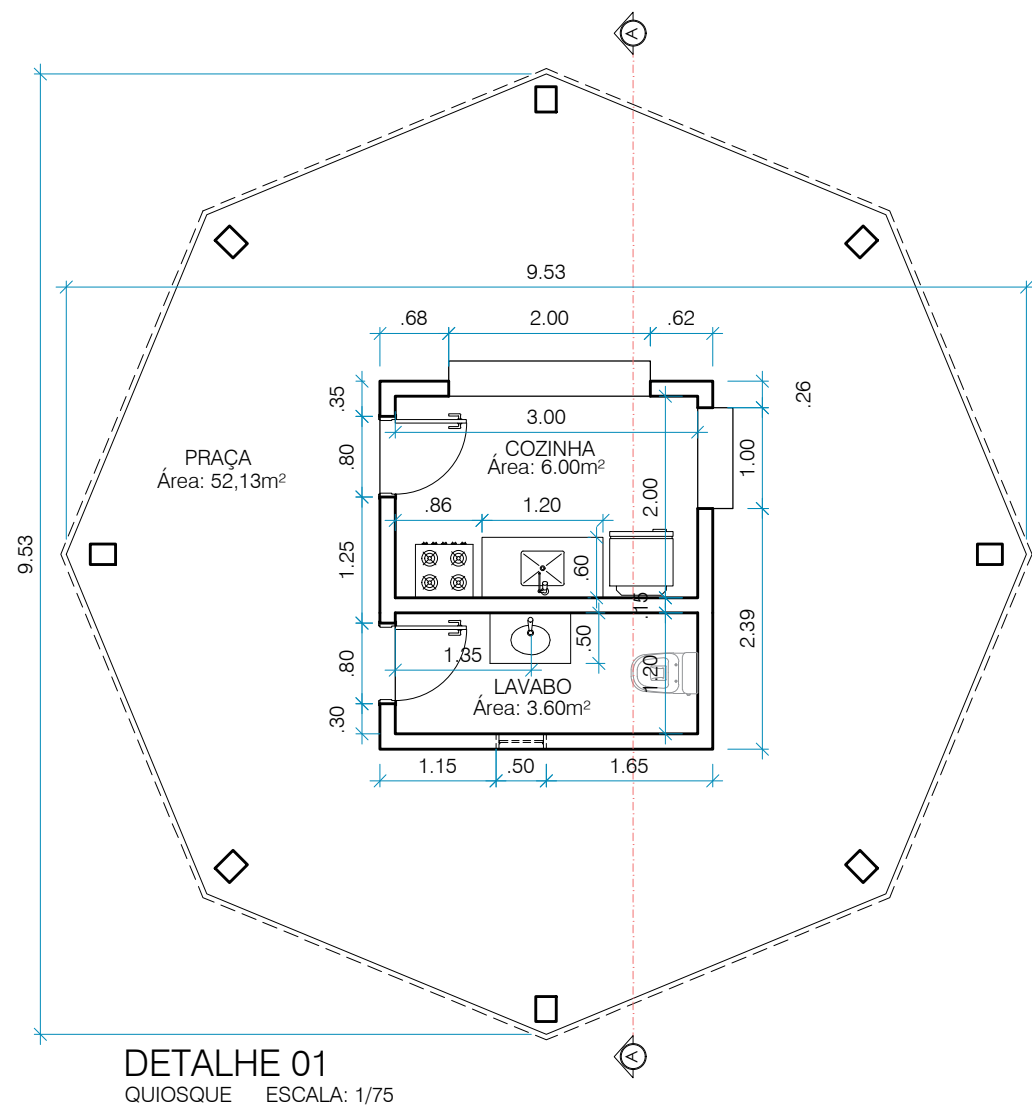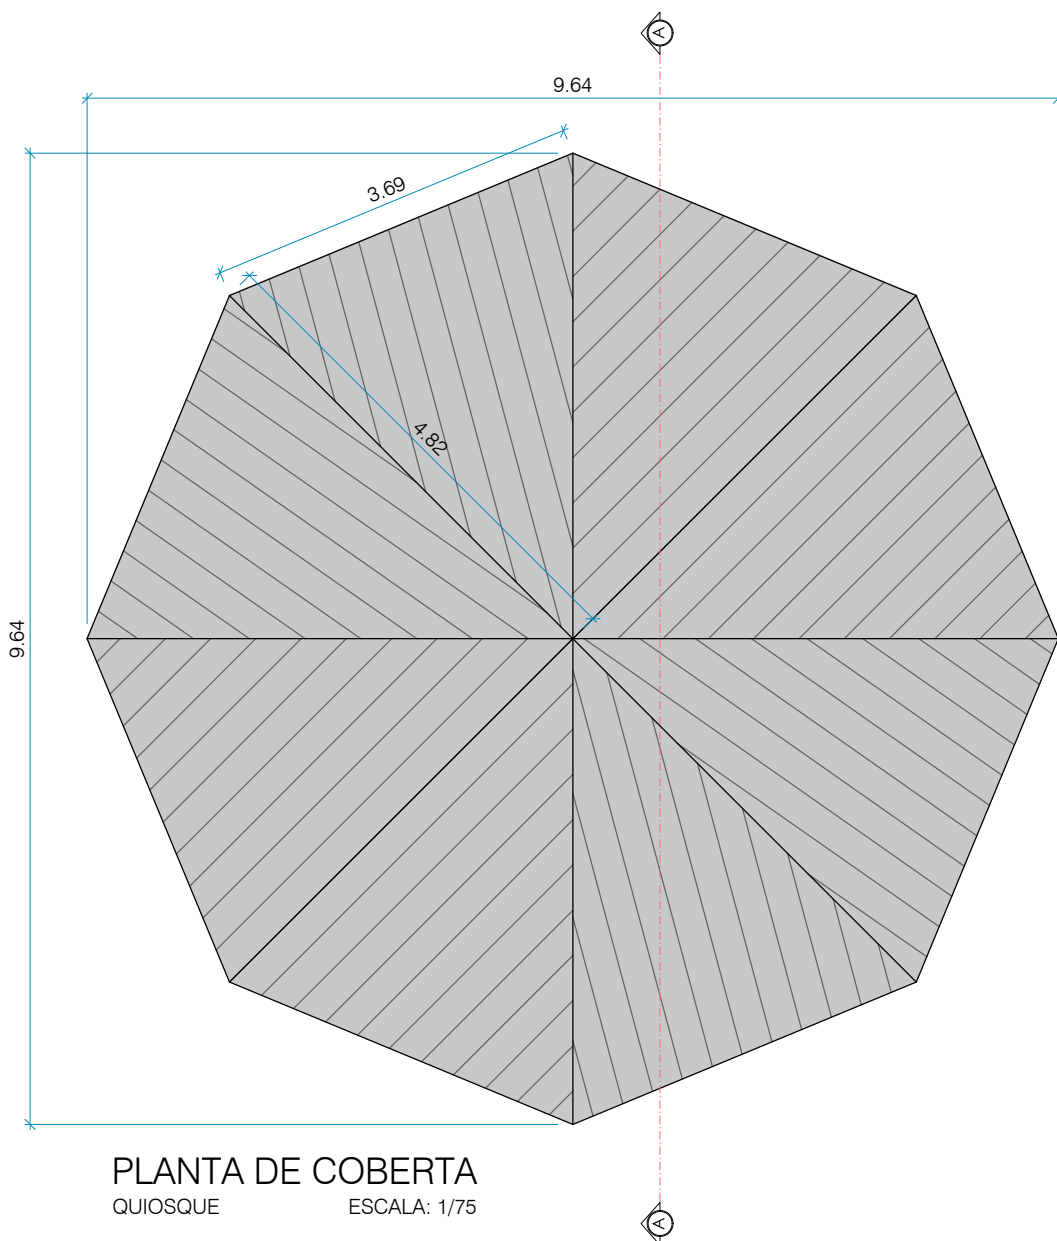


- Especificação:
- Quiosque de alvenaria, emassado e pintado com cor branca. Piso e parede internos revestidos com revestimento cerâmico e rejuntados. Banheiro e cozinha com bancadas de granito preto.
 - Teto fechado com material de pvc na cor branca com estrutura necessária para tal aplicação. Iluminado com luminárias de teto plafon 30x30cm.
 - Estrutura necessária para sustentação de caixa de água de 500l.
 - Balcão de atendimento com pedra de mármore cor preta.
 - Cobertura externa e geral feita com estrutura de madeira e telhas de cerâmica e pilares de cimento.
 - Piso externo de intertravado cinza, seguindo a praça ao redor do quiosque. Detalhe: piso elevado 4cm do piso da praça externa.

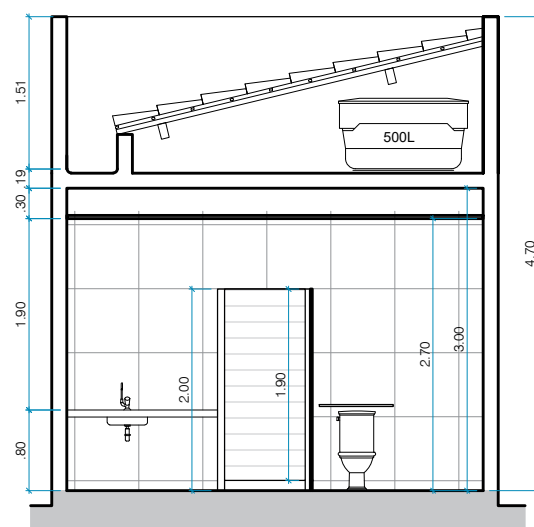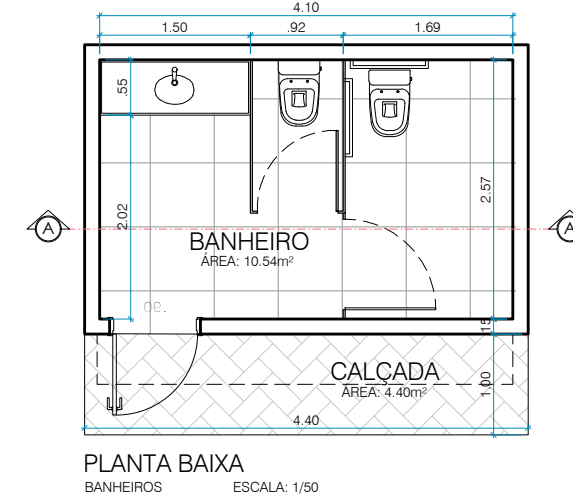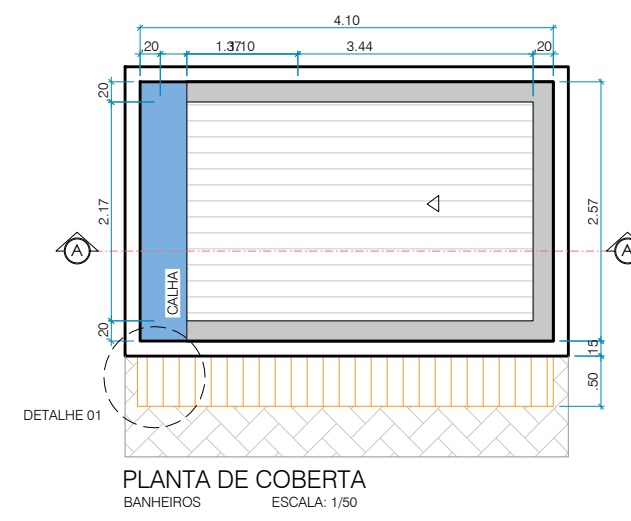

- Especificação:
- Banheiro de alvenaria, com piso e parede internos revestidos com revestimento cerâmico e rejuntados.
 - Bancadas e divisórias de granito preto. Porcelâneas brancas e cubas de flocamento de embúfir.
 - Porta, para as cabines, de alumínio;
 - Teto fechado com material de pvc na cor branca com estrutura necessária para tal aplicação. Espaço iluminado com luminárias de teto plafon 30x30cm.
 - Estrutura necessária para sustentação de caixa de água de 500l e fechado com telha de flocamento.
 - Piso externo de intertravado cinza.
 - Parede externa rebocada, emassada e pintada de branco. Com uma parede aderida com indicação criativa de banheiro.
 - Marquise feita de telha metálica pintada de amarelo apoiada por mdo francesa feita de ferro pintado de amarelo.



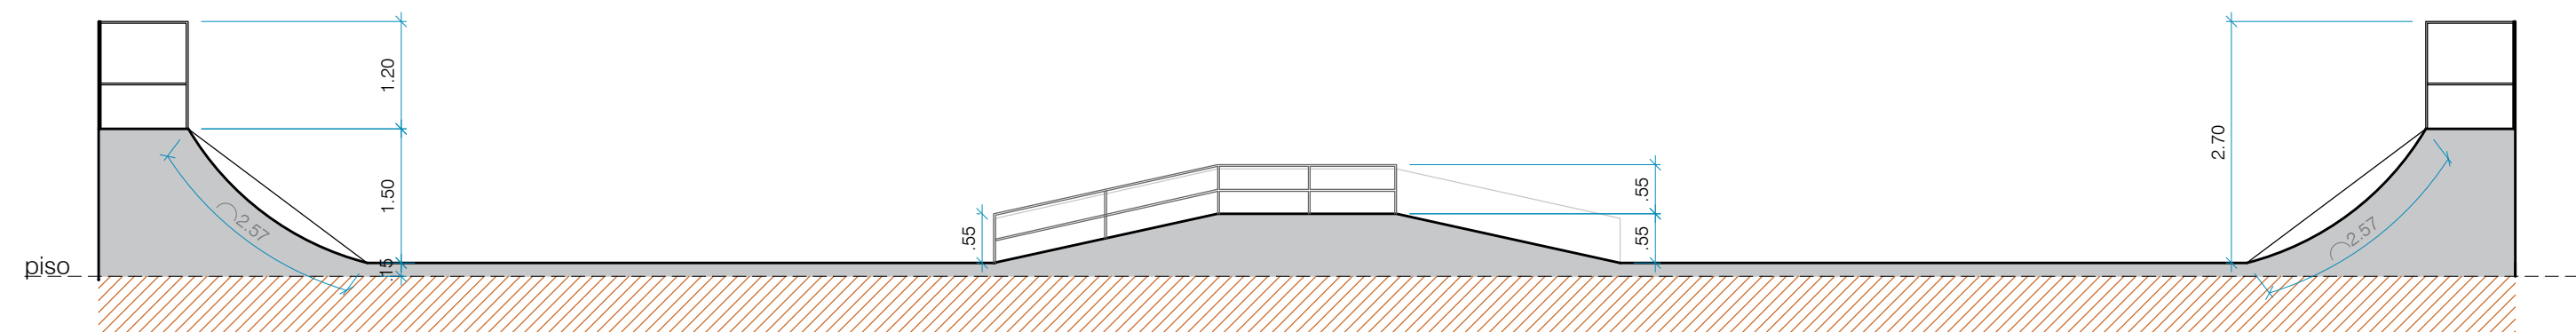


CORTE AA
PISTA DE SKATE ESCALA: 1/100

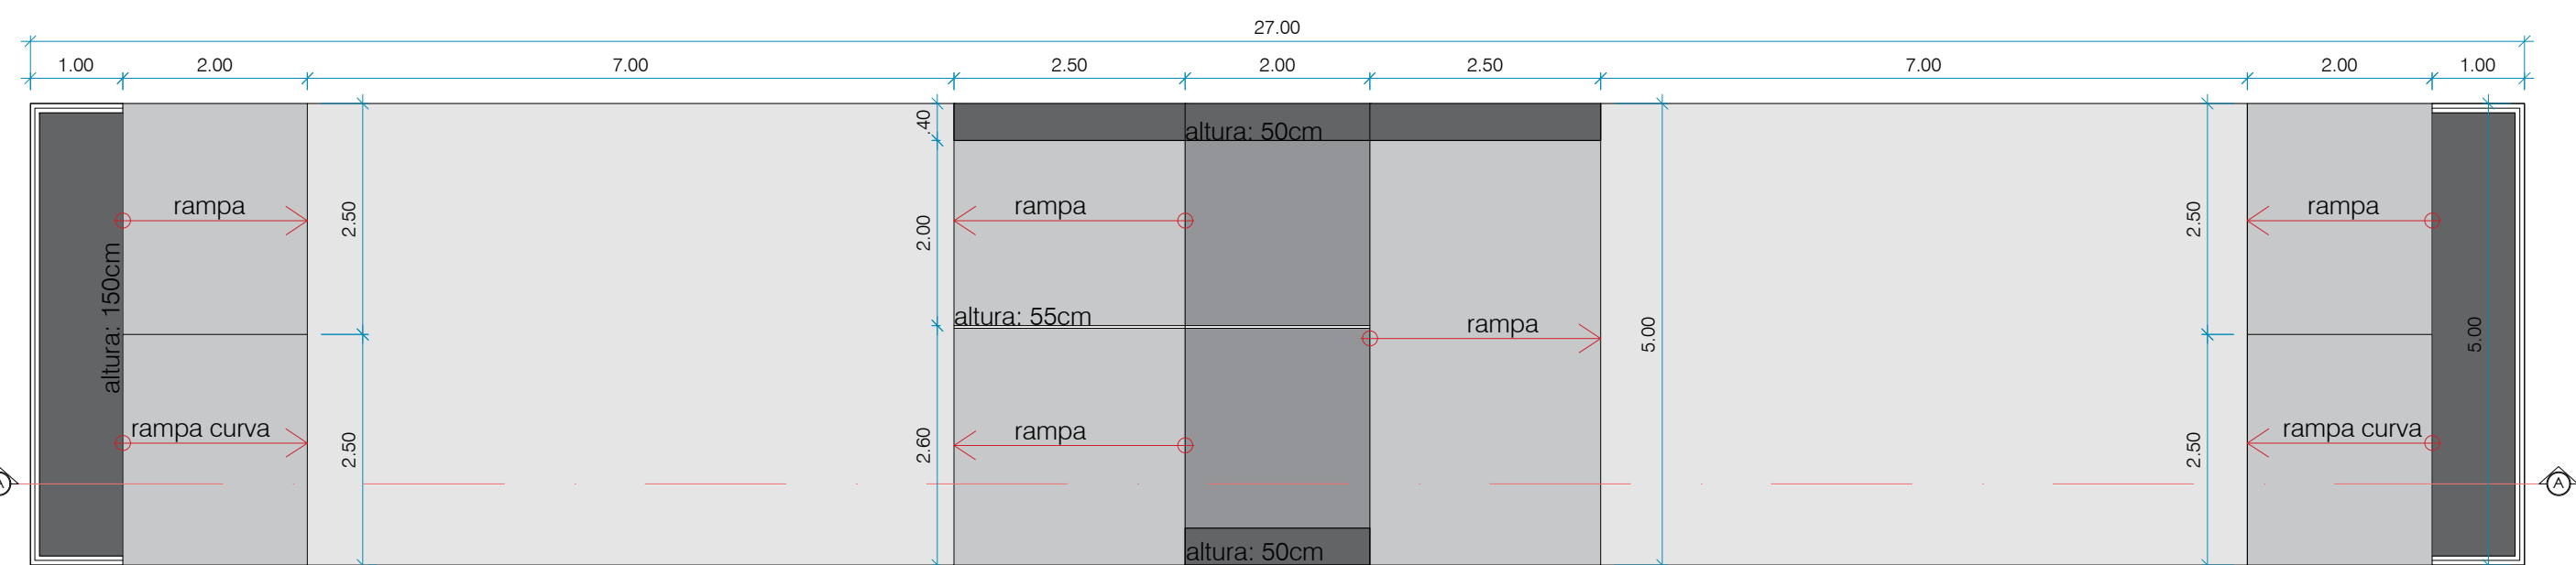


PLANTA BAIXA
PISTA DE SKATE ESCALA: 1/100


- Especificação:
- Acabamento em concreto liso polido.
 - Corrimãos (handrails): Tubo de aço galvanizado ou inox e fixação chumbada no concreto;
 - Guarda corpo de Aço galvanizado ou inox, sendo tubos metálicos com: Montantes verticais a cada 1,20 m e travessas horizontais.

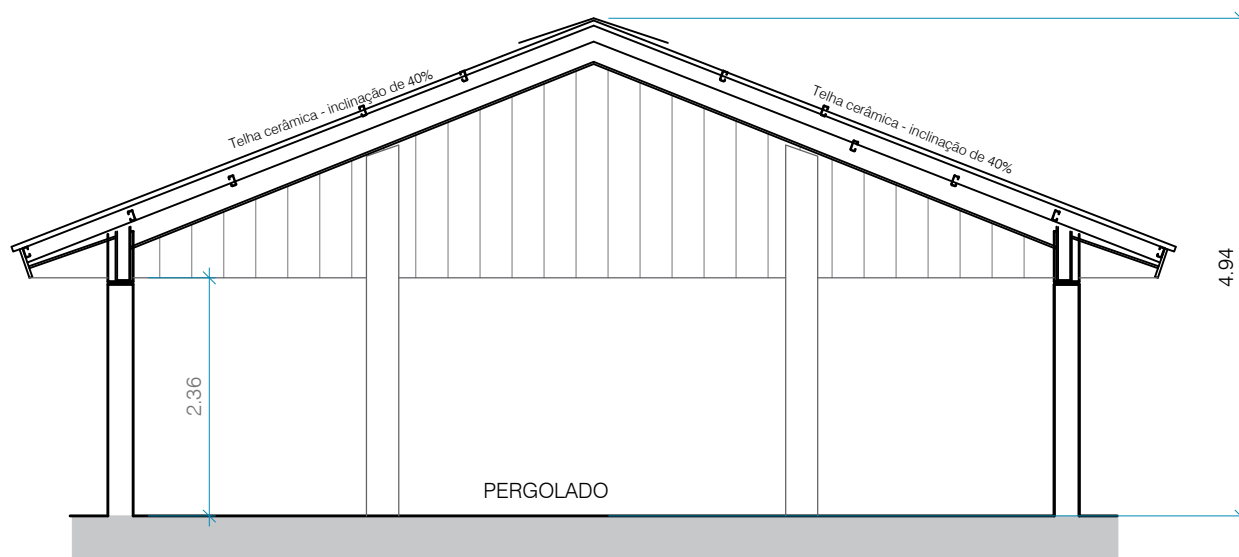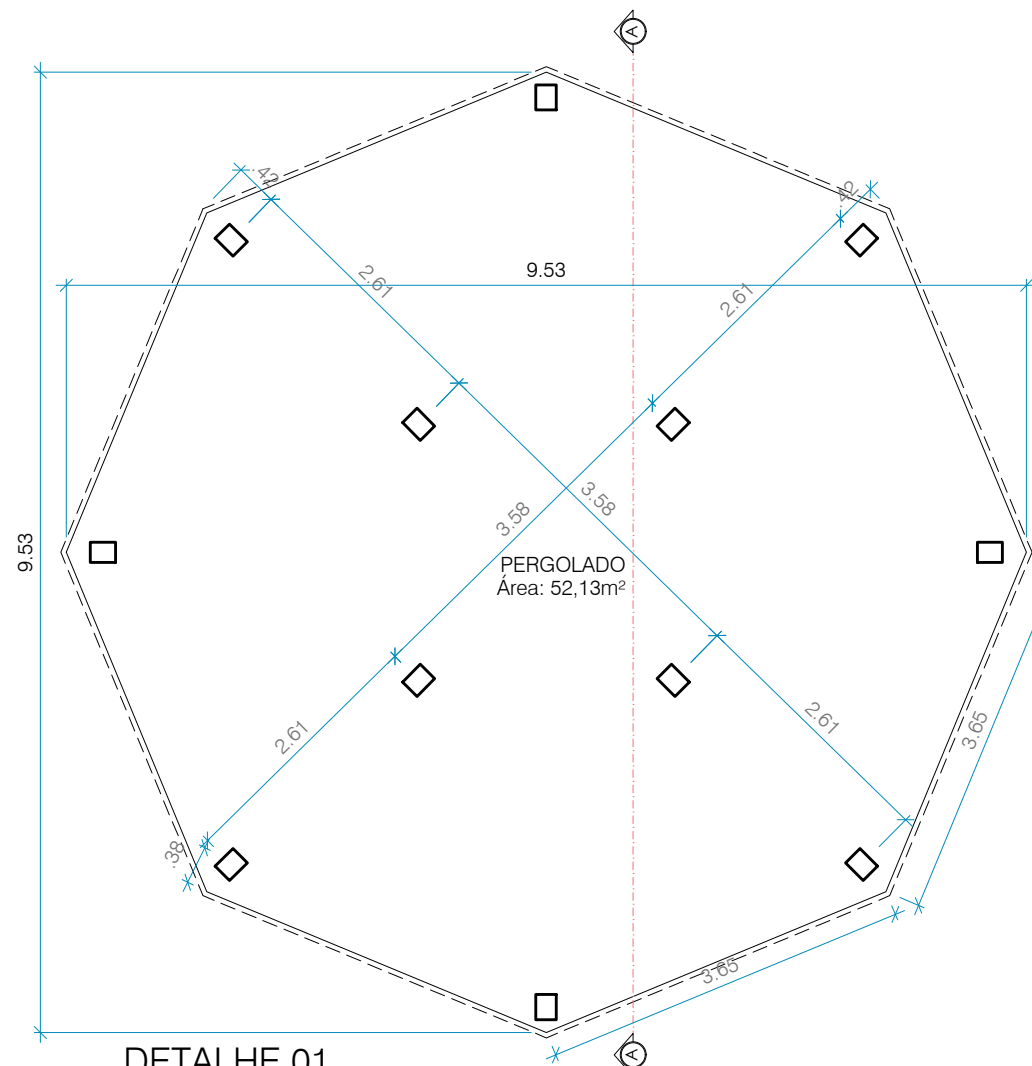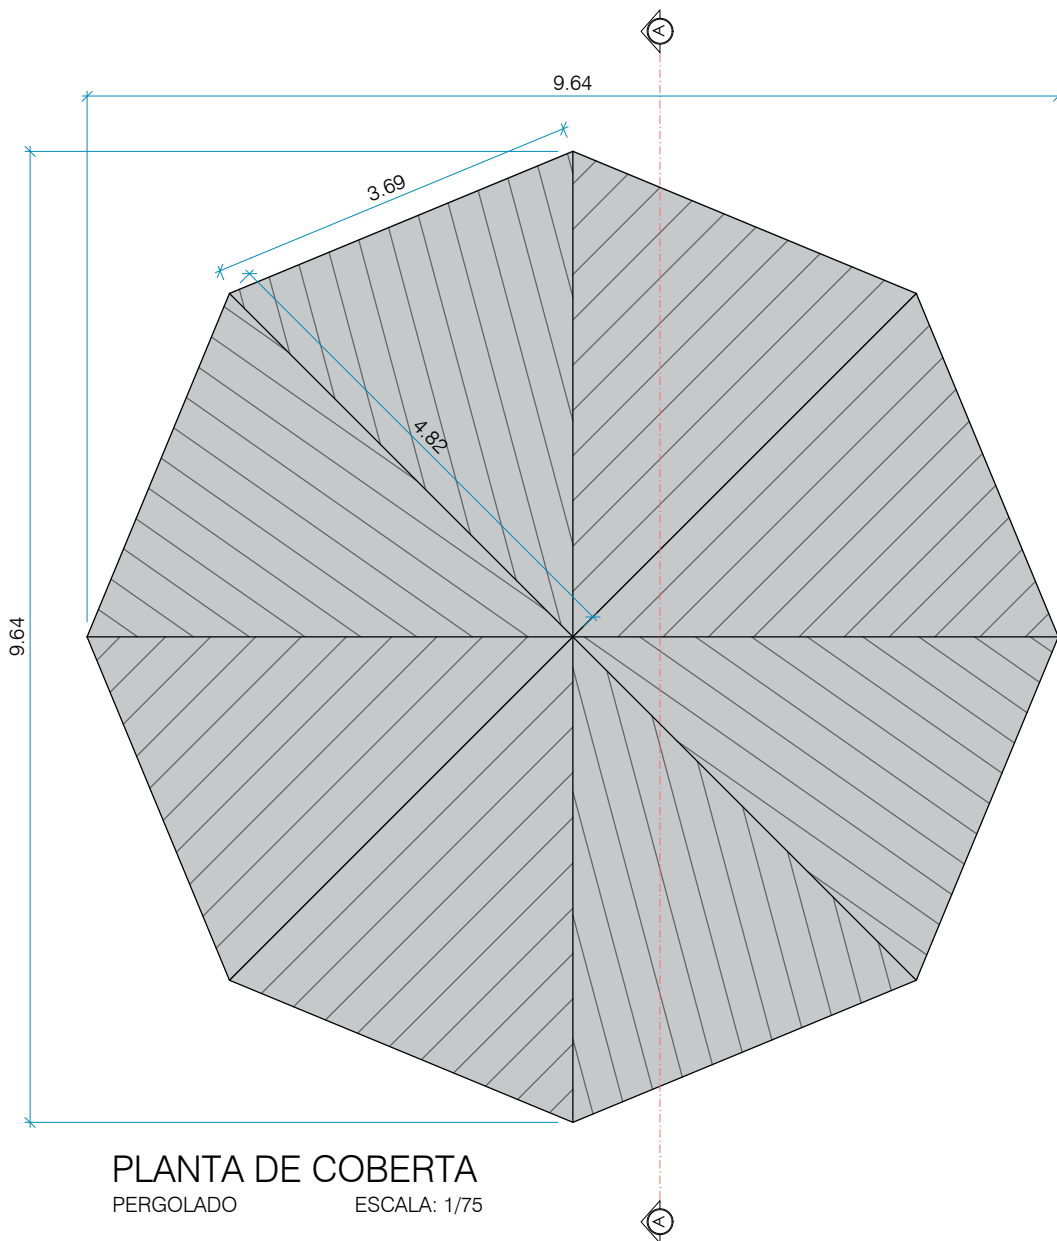


- Especificação:
- Pergolado com pilares de alvenaria, revestidos com revestimento cerâmico e rejuntados.
 - Coberta feita de estrutura de madeira e telha ceramica; iluminado com luminárias de teto tubular.
 - Piso com pedra intertravado cinza, seguindo a praça ao redor do pergolado.

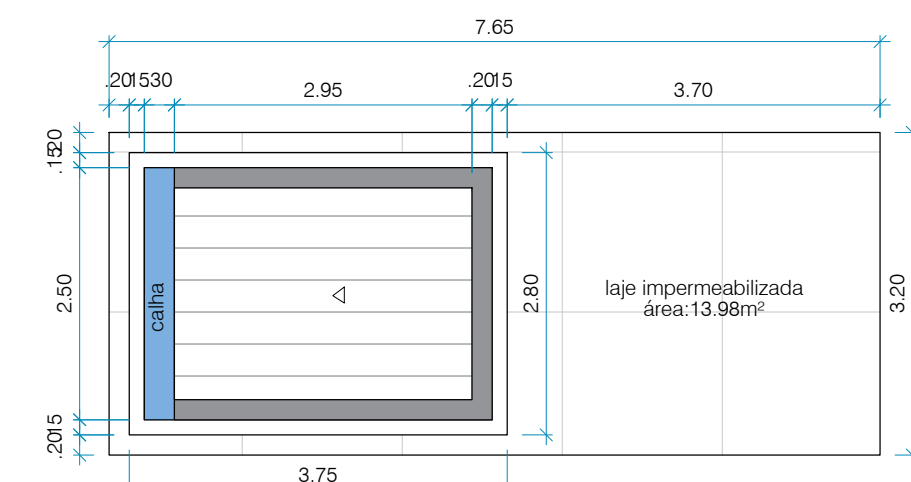


PLANTA DE COBERTA
GUARITA ESCALA: 1/75

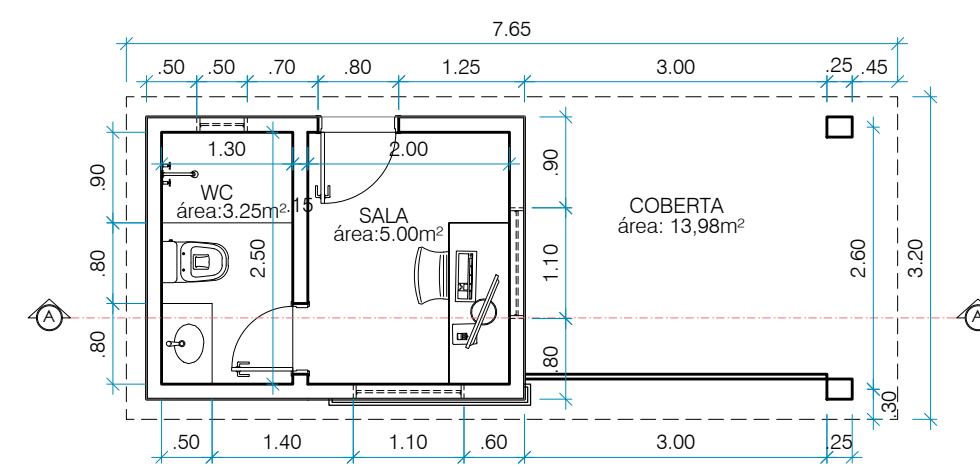

PLANTA BAIXA
GUARITA ESCALA: 1/75

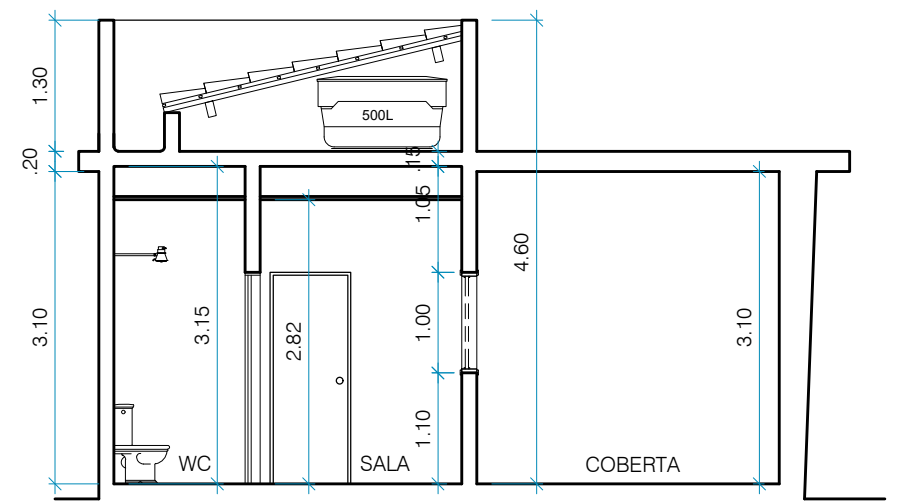

CORTE AA
GUARITA ESCALA: 1/75

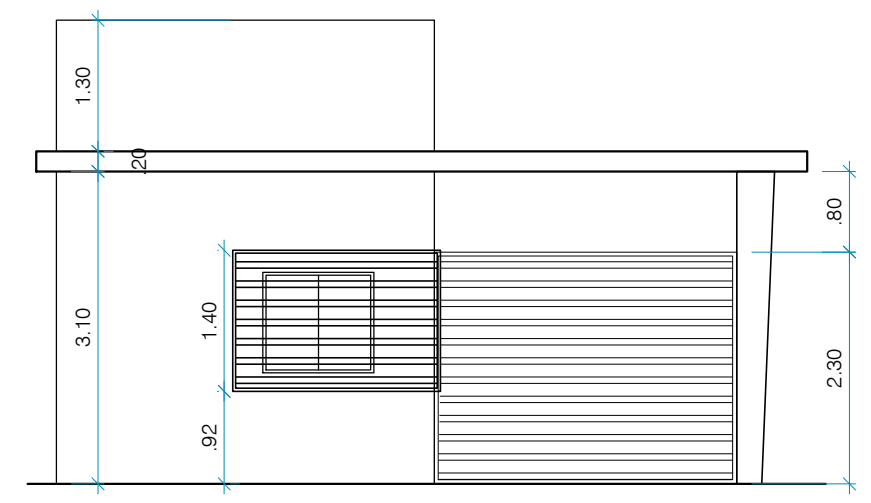

FACHADA SUDOESTE
GUARITA ESCALA: 1/75

Projeto: Projeto de Urbanismo Vila Olímpica		Prancha nº: 04/05
Desenhos: QUIOSQUE PERGOLADO BANHEIRO		PISTA DE SKATE GUARITA ESCALAS INDICADAS
Proprietário: PREFEITURA MUNICIPAL DE COREMAS		
Endereço/Obra: R. Francisco Raimundo de Andrade, bairro DNOCS, Coremas		
ÁREAS	m²	Data:
Área do Terreno	10.733,41	MAIO/2026
Estacionamento	519,11	Desenhista:
Calçada	249,64	KIRYA CRISTINNE
Área verde	4.281,11	
Área Total Construída	4.821,36m²	
T. Ocupação	25,33%	
I. Aproveitamento	0,44	
T. Permeabilidade do Solo	39,88%	
Técnicos Responsáveis		
PROPRIETÁRIO (A):		RESPONSÁVEL TÉCNICO
ARQUITETURA E URBANISMO CAVALHEIRO & ASSOCIADOS © (R) 19835.0759 (R)11		



VISTA DA ENTRADA DA VILA, CONSEGUIMOS VER A FAIXA DE PEDRESTE, GUARITA E CALÇADA.



VISTA DA PISTA DE CORRIDA, CONSEGUIMOS VER TAMBÉM OS BANHEIROS E CANTEIROS



VISTA DO CANTEIRO QUE IRÁ RECEBER OS EQUIPAMENTOS PARA CALISTENIA



VISTA DA PISTA DE CORRIDA COM ACESSO A QUADRA, ARQUIBANCADAS E CANTEIRO




VISTA DA QUADRA DE FUTSAL, AO LADO TEMOS OS BANHEIROS E CANTEIROS PARA ARVORES



VISTA DA PISTA DE SKATE



DETALHE DE COMO PODE SER A PLANTAÇÃO DAS ARVORES PROXIMAS AO MURO DE ENTRADA

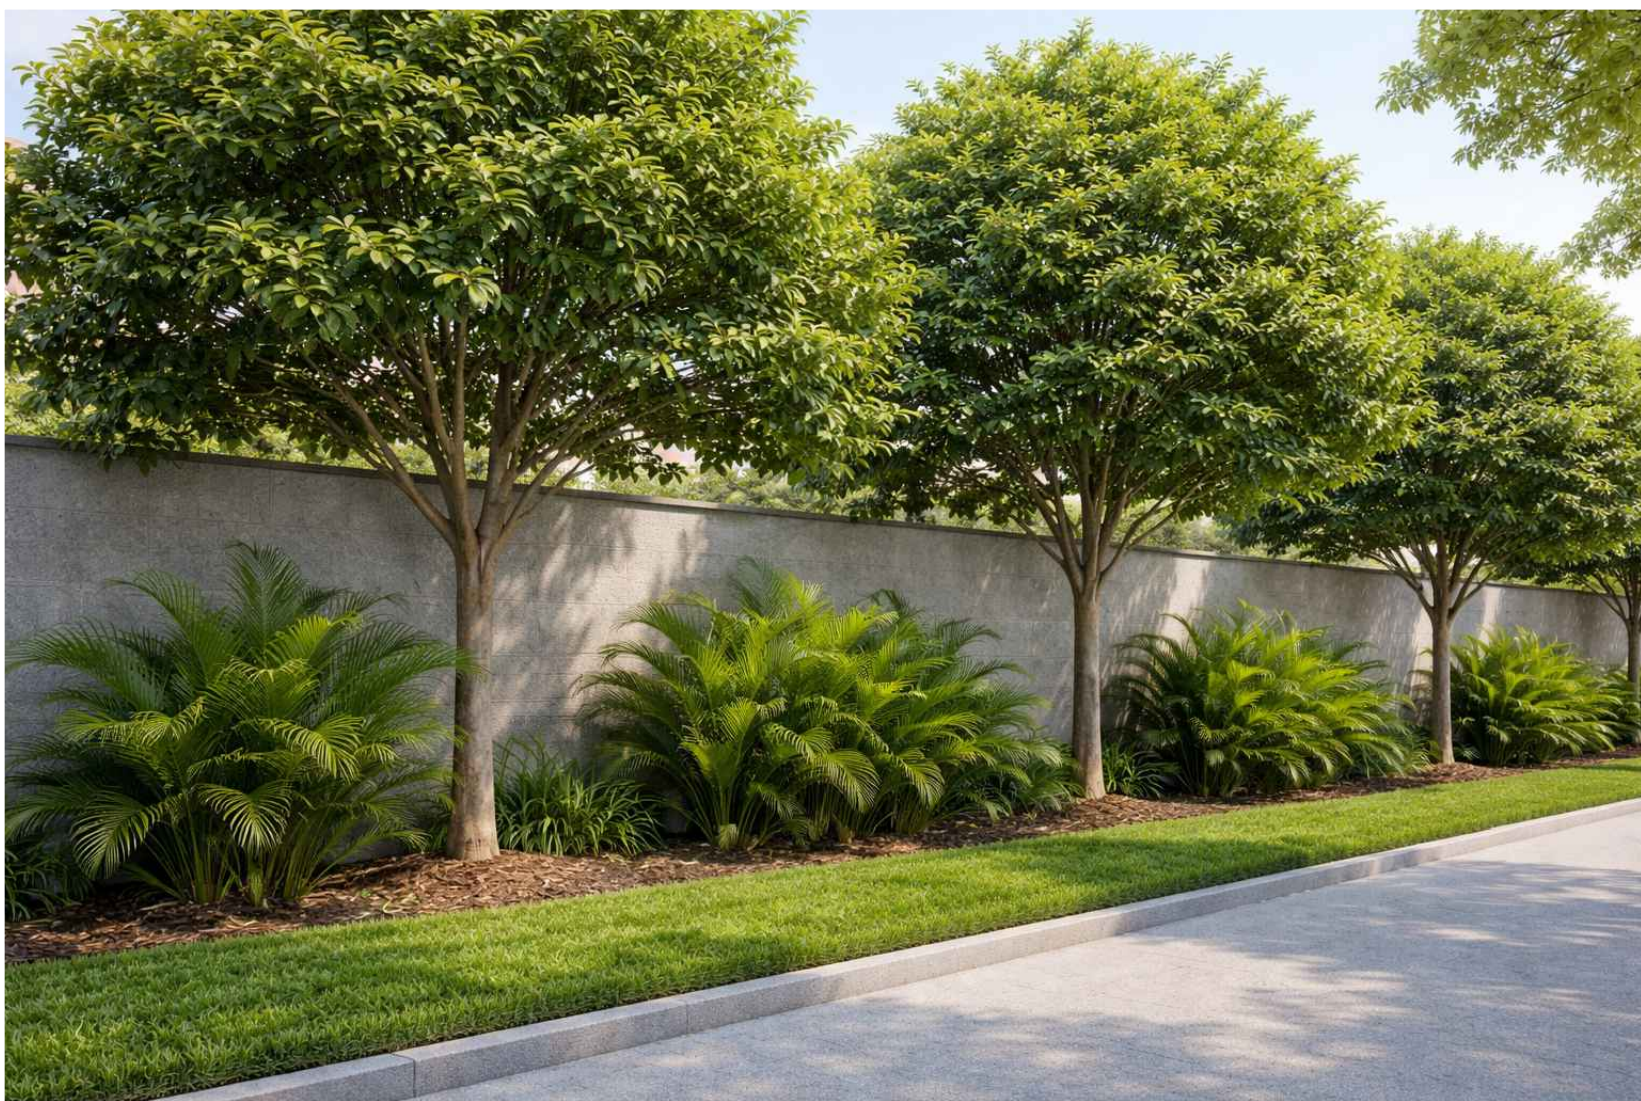

DETALHE DE COMO PODE SER APLICADA A VEGETAÇÃO DO CANTEIRO A NORDESTE DO PROJETO, MURO FINAL




VISTA DO QUIOSQUE.

Projeto: Projeto de Urbanismo Vila Olímpica		Prancha n°: 05/05
Desenhos: IMAGENS		ESCALAS INDICADAS
Proprietário: PREFEITURA MUNICIPAL DE COREMAS		
Endereço/Obra: R. Francisco Raimundo de Andrade, bairro DNOCS, Coremas		
ÁREAS	m²	Área Total Construída
Área do Terreno	10.733,41	4.821,36m²
Estacionamento	519,11	T. Ocupação
Calçada	249,64	25,33%
Área verde	4.281,11	I. Aproveitamento
		0,44
		T. Permeabilidade do Solo
		39,88%
Técnicos Responsáveis		Data: MAIO/2026
_____ PROPRIETÁRIO (A)		Desenhista: KIRYA CRISTINNE
_____ RESPONSÁVEL TÉCNICO		
		

Projeto: **Projeto de Urbanismo Vila Olimpica**

Desenhos: **PLANTA BAIXA DE LOCAÇÃO DOS ELEMENTOS ESTRUTURAIS**

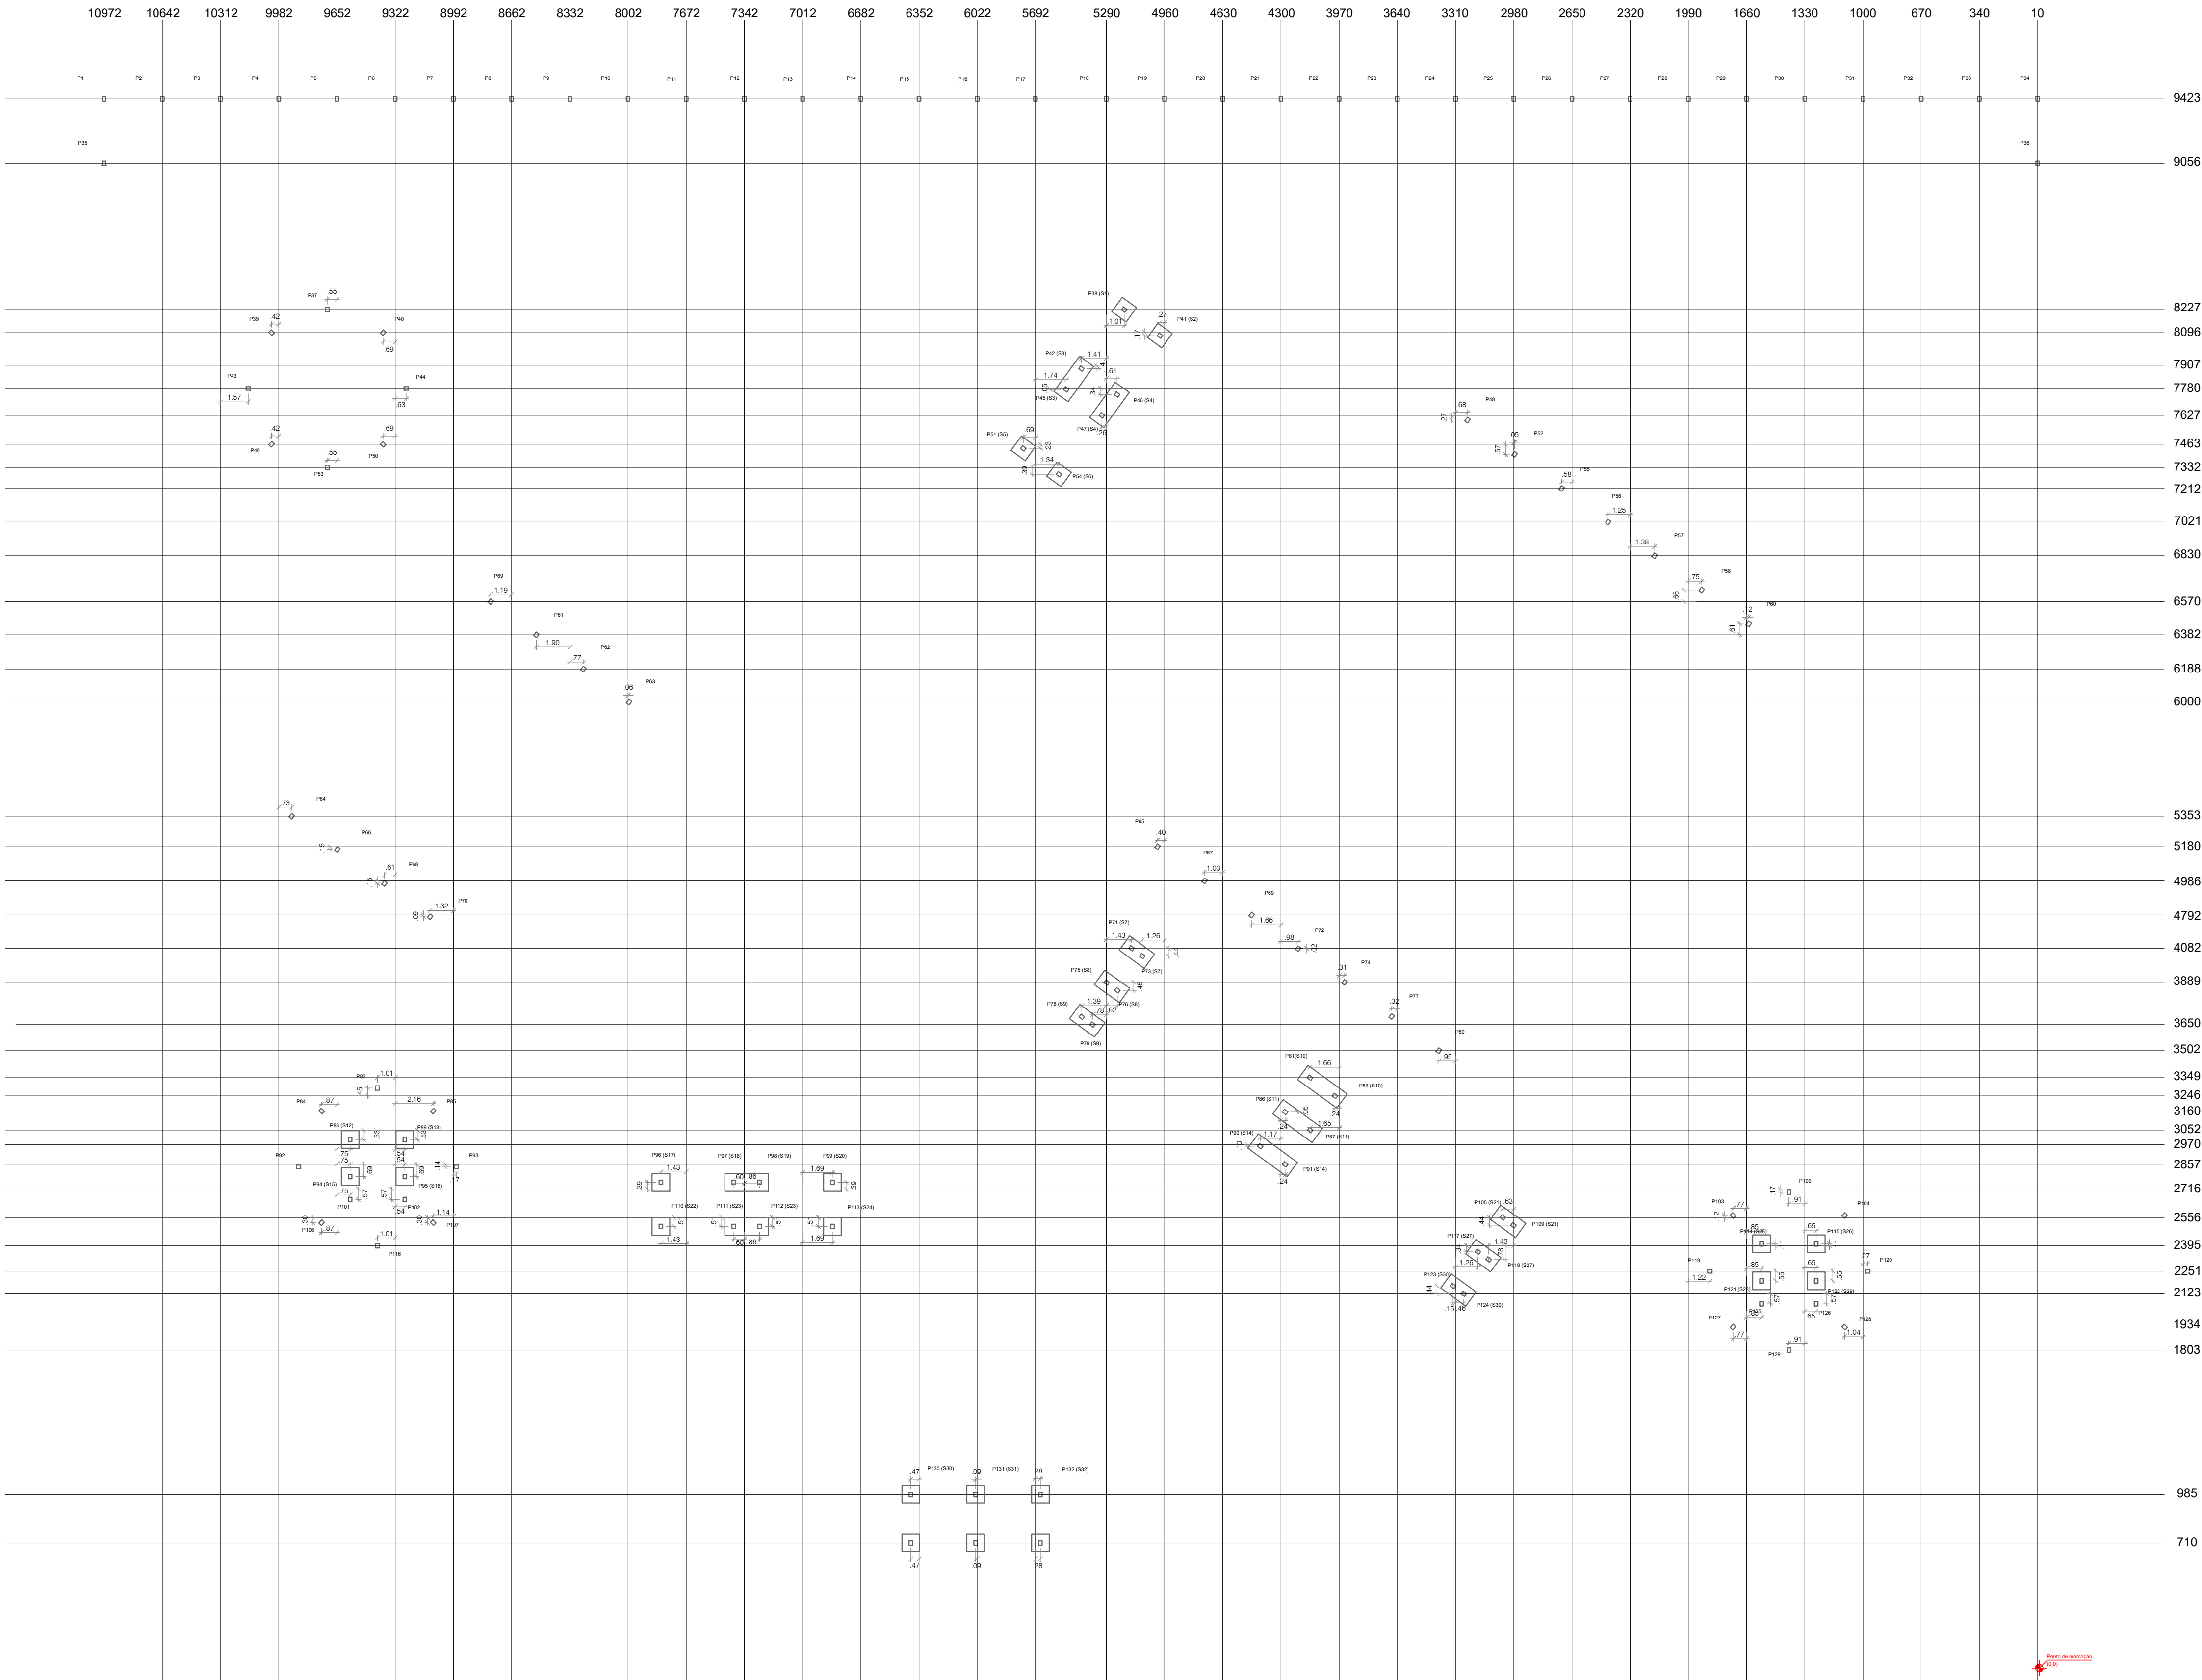

- Observações:
- Conferir todas as medidas em obra antes da execução dos serviços.
 - Não executar alterações sem autorização prévia do responsável técnico.
 - Qualquer divergência entre projeto e condições de campo deverá ser comunicada ao responsável técnico para análise e aprovação.
 - Todas as instalações deverão ser executadas por mão de obra qualificada, seguindo as normas técnicas vigentes e as recomendações dos fabricantes dos materiais empregados.
 - O dimensionamento e posicionamentos indicados em projeto prevalecem sobre quaisquer informações complementares aqui descritas.

A locação foi dimensionadas e deverá ser executadas conforme projeto.

- Os eixos de locação foram definidos a partir dos centros dos pilares, constituindo as referências principais para implantação da estrutura.
- Todas as cotas apresentadas referem-se às distâncias entre eixos centrais dos pilares, salvo indicação em contrário.
- Antes do início da execução, deverão ser conferidas em campo todas as medidas, níveis e alinhamentos.
- Qualquer divergência entre o projeto e as condições encontradas no local deverá ser comunicada ao responsável técnico para análise e aprovação.
- A locação da obra deverá ser realizada por profissional habilitado, utilizando equipamentos adequados para garantir a precisão dos alinhamentos e dimensões projetadas.
- Nenhum elemento estrutural deverá ser executado sem prévia conferência dos eixos de locação e respectivos níveis.

Projetista: **Fernando Matias Mamede**

RESPONSÁVEL TÉCNICO
Fernando Matias Mamede
Engenheiro Civil
Crea: 162056275-8



Proprietário: **Prefeitura Municipal de Coremas**

PROPRIETÁRIO(A)




Endereço/Obra: **Rua Francisco Raimundo de Andrade, DNOCS, Coremas - PB, 58770-000**

ÁREAS	m²
Área do Terreno	10.733,41
Estacionamento	519,11
Calçada	249,64
Área verde	4.281,11

Prancha:

01/14

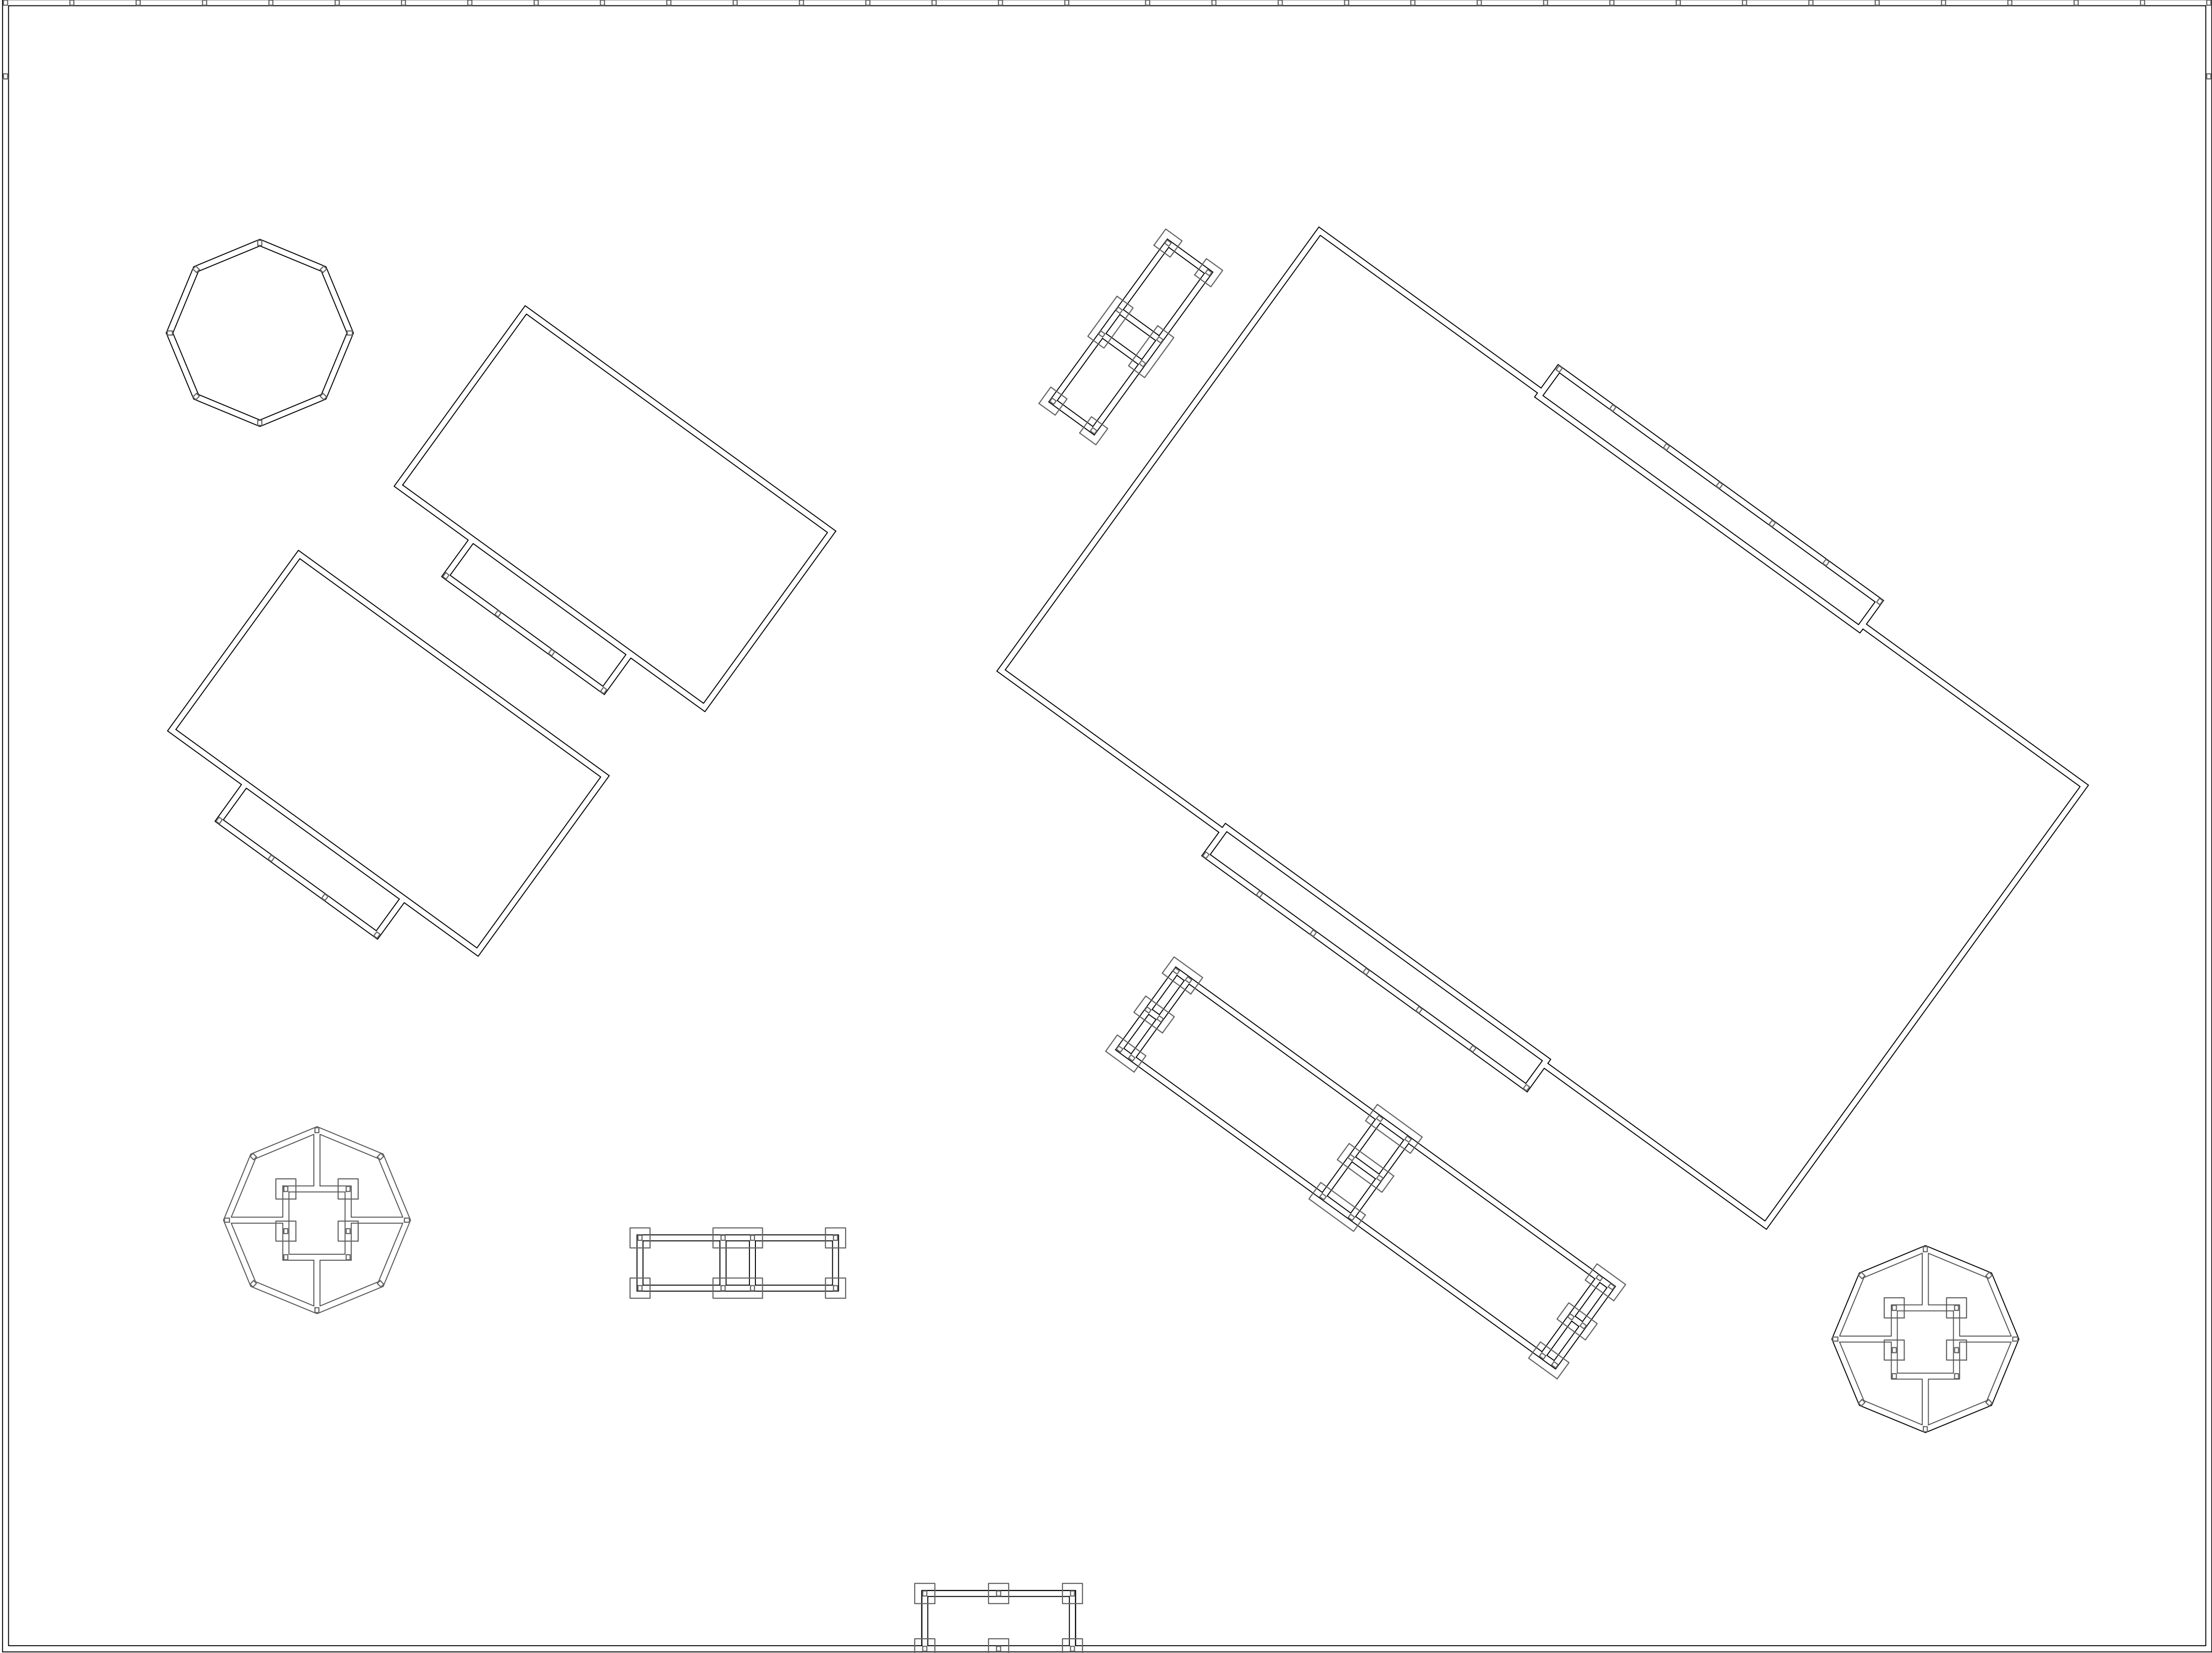

Projeto:

Projeto de Urbanismo Vila Olimpica

Desenhos:

PLANTA BAIXA DE LOCAÇÃO DOS ELEMENTOS ESTRUTURAIS

Observações:

- Conferir todas as medidas em obra antes da execução dos serviços.
- Não executar alterações sem autorização prévia do responsável técnico.
- Qualquer divergência entre projeto e condições de campo deverá ser comunicada ao responsável técnico para análise e aprovação.
- Todas as instalações deverão ser executadas por mão de obra qualificada, seguindo as normas técnicas vigentes e as recomendações dos fabricantes dos materiais empregados.
- O dimensionamento e posicionamentos indicados em projeto prevalecem sobre quaisquer informações complementares aqui descritas.

A locação foi dimensionadas e deverá ser executadas conforme projeto.

Esta prancha apresenta a disposição das sapatas, vigas baldrame e pilares da edificação.

- As vigas baldrame deverão ser executadas conforme dimensões de 0,30m x 0,30m, indicados em projeto estrutural.
- As sapatas deverão ser executadas nas dimensões especificadas, respeitando os níveis de assentamento definidos em projeto.
- Os pilares deverão ser posicionados conforme indicado nesta prancha e detalhados nos respectivos desenhos estruturais.
- Antes da concretagem, deverão ser conferidos alinhamentos, níveis, dimensões, armaduras e cobrimentos.
- O fundo das escavações deverá estar limpo, regularizado e livre de materiais inadequados à fundação.
- Qualquer divergência entre as condições encontradas em campo e as previstas em projeto deverá ser comunicada ao responsável técnico para análise e aprovação.
- Todos os serviços deverão atender às especificações do projeto estrutural e às normas técnicas vigentes.

Projeta:

Fernando Matias Mamede

RESPONSÁVEL TÉCNICO
Fernando Matias Mamede
Engenheiro Civil
Crea: 162056275-8

Proprietário:

Prefeitura Municipal de Coremas

PROPRIETÁRIO(A)

Endereço/Obra:

Rua Francisco Raimundo de Andrade, DNOCS, Coremas - PB, 58770-000

ÁREAS

m²

Área do Terreno10.733,41

Estacionamento519,11

Calçada249,64

Área verde4.281,11

Prancha:


02/14

Ponto de mercado

(0,00)

S1=S2=S5=S6=S12=S13=S15=S16=S17=S19=S21=S23=S24=S25=S27=S28=S30=S31=S32=S33=S34=S35
100 x 100 cm


S3=S4=S18=S22
100 x 247 cm

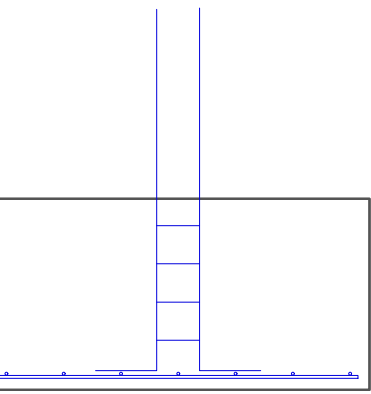

4 N2 - Ø10.0 C= 110




4 N3 - Ø5.0 C= 66

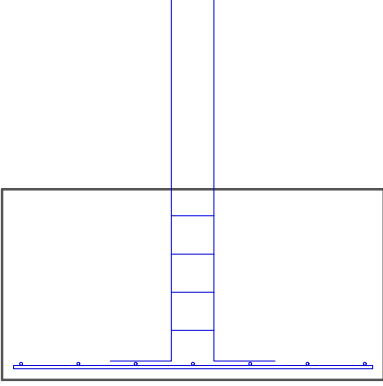


8 N2 - Ø10.0 C= 110



4 N3 - Ø5.0 C= 66

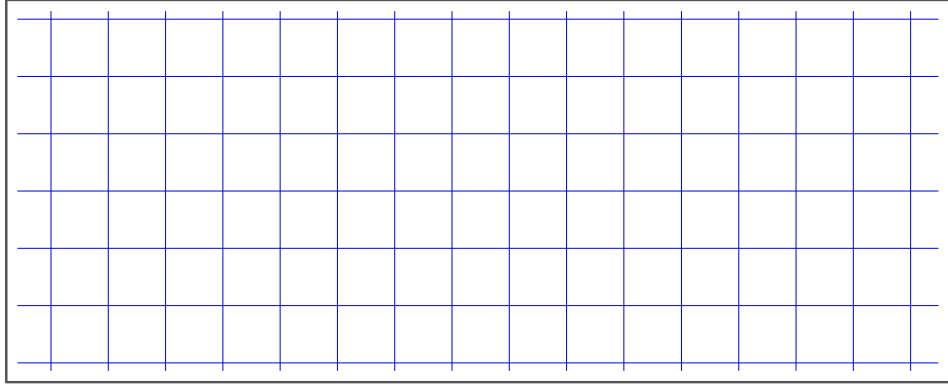


16 N1 - Ø8.0 C= 94

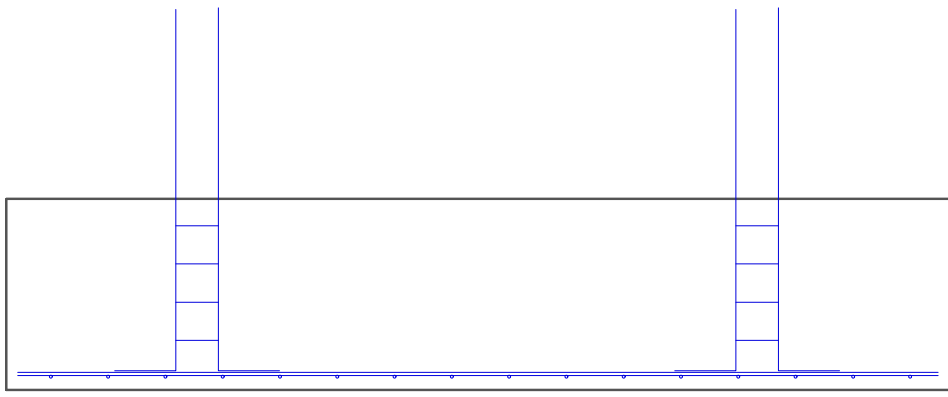

7 N4 - Ø8.0 C= 241


S7=S8=S9=S20=S26=S29
100 x 175 cm

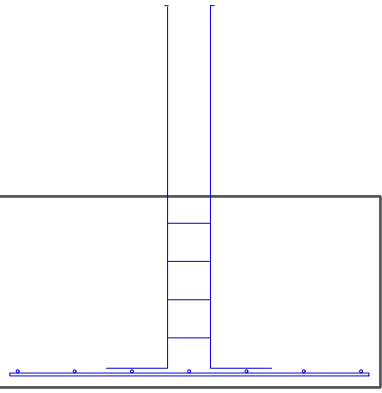


8 N2 - Ø10.0 C= 110



4 N3 - Ø5.0 C= 66

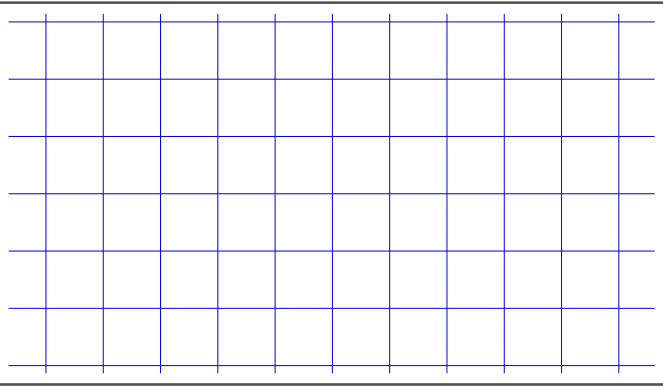


11 N1 - Ø8.0 C= 94

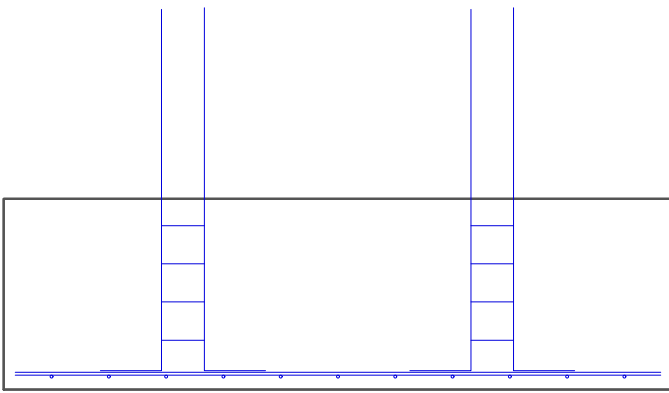

7 N5 - Ø8.0 C= 169


S10=S11=S14
100 x 275 cm

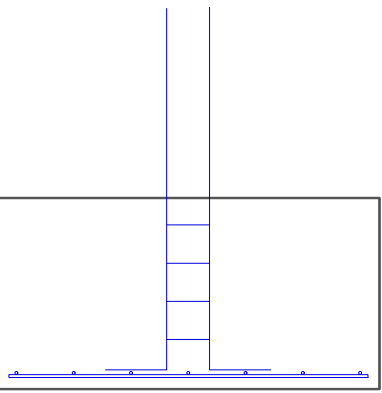


8 N2 - Ø10.0 C= 110



4 N3 - Ø5.0 C= 66

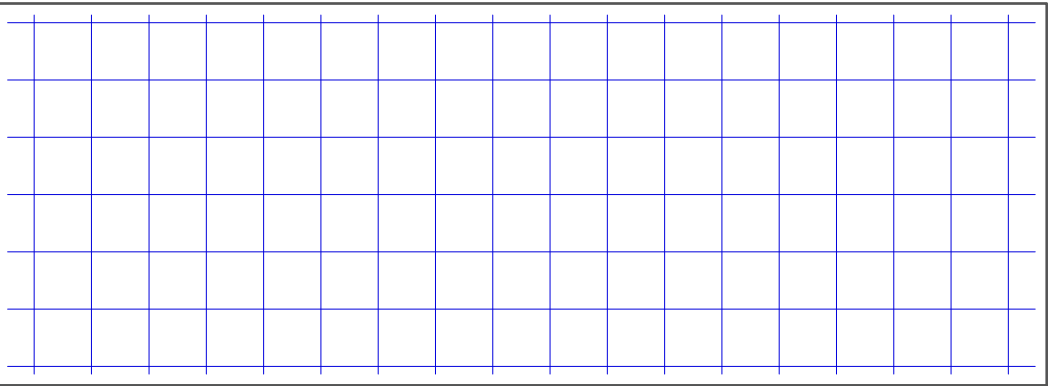

18 N1 - Ø8.0 C= 94

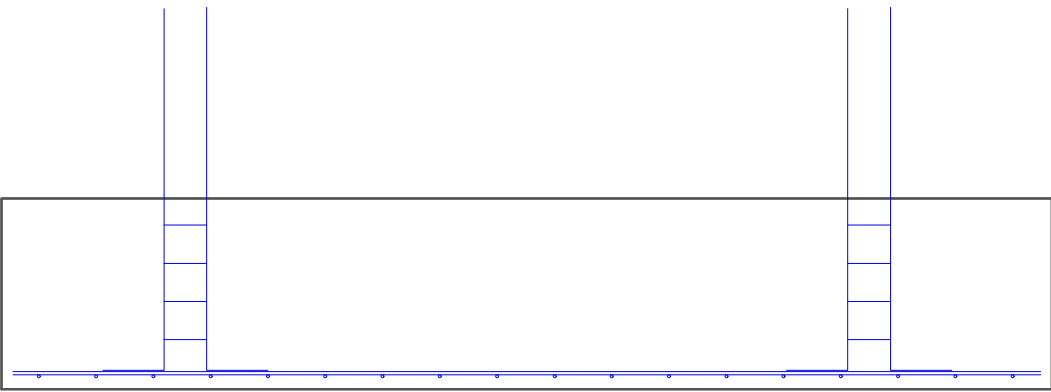

7 N6 - Ø8.0 C= 269

Projeto:

Projeto de Urbanismo Vila Olimpica

Desenhos:

PLANTA BAIXA DE LOCAÇÃO DOS ELEMENTOS ESTRUTURAIS

Observações:

- Conferir todas as medidas em obra antes da execução dos serviços.
- Não executar alterações sem autorização prévia do responsável técnico.
- Qualquer divergência entre projeto e condições de campo deverá ser comunicada ao responsável técnico para análise e aprovação.
- Todas as instalações deverão ser executadas por mão de obra qualificada, seguindo as normas técnicas vigentes e as recomendações dos fabricantes dos materiais empregados.
- O dimensionamento e posicionamentos indicados em projeto prevalecem sobre quaisquer informações complementares aqui descritas.

Esta prancha apresenta os detalhamentos das sapatas da edificação, contendo dimensões, níveis, armaduras e demais informações necessárias para sua execução.

- Todas as sapatas deverão ser executadas rigorosamente conforme as dimensões indicadas nos detalhamentos.
- As armaduras deverão ser montadas conforme bitolas, quantidades, espaçamentos, comprimentos de ancoragem e dobramentos especificados em projeto.
- Deverão ser respeitados os cobrimentos mínimos das armaduras conforme especificado no projeto estrutural e nas normas técnicas vigentes.
- Os arranques dos pilares deverão ser posicionados e fixados conforme os detalhamentos apresentados.
- Antes da concretagem, deverão ser conferidas as dimensões das formas, posicionamento das armaduras, cobrimentos, arranques e níveis de assentamento.
- O fundo das escavações deverá estar limpo, regularizado e livre de materiais orgânicos ou inadequados.
- Não será permitida a concretagem sem a prévia conferência das armaduras e das dimensões indicadas em projeto.
- Qualquer divergência identificada em campo deverá ser comunicada ao responsável técnico para análise e aprovação.
- Todos os serviços deverão atender às especificações do projeto estrutural e às normas técnicas vigentes.

Projetista:

Fernando Matias Mamede

RESPONSÁVEL TÉCNICO
Fernando Matias Mamede
Engenheiro Civil
Crea: 162056275-6

Proprietário:

Prefeitura Municipal de Coremas

PROPRIETÁRIO(A)


Endereço/Obra: Rua Francisco Raimundo de Andrade, DNOCS, Coremas - PB, 58770-000

ÁREAS	m²
Área do Terreno	10.733,41
Estacionamento	519,11
Calçada	249,64
Área verde	4.281,11


Prancha:

03/14


P1 = P2 = P3 = P4 = P5 = P6 = P7 = P8 = P9 = P10 = P11 = P12 = P13 = P14 = P15 = P16 = P17 = P18 = P19 = P20 = P21 = P22 = P23 = P24 = P25 = P26 = P27 = P28 = P29 = P30 = P31 = P32 = P33 = P34 = P35 = P36
20 x 20 cm

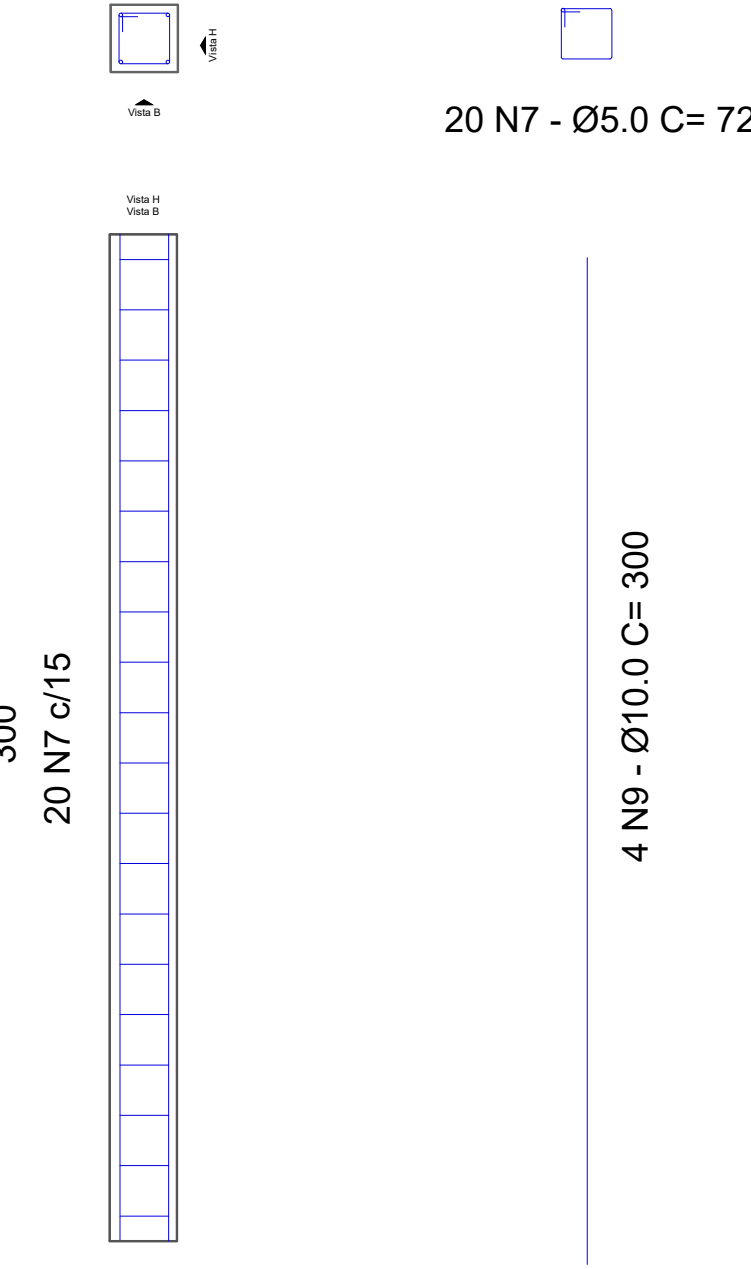


P37 = P39 = P40 = P43 = P44 = P49 = P50 = P53 = P82 = P84 = P85 = P92 = P93 = P100 = P103 = P104 = P106 = P107 = P116 = P119 = P120 = P127 = P128 = P129
20 x 25 cm

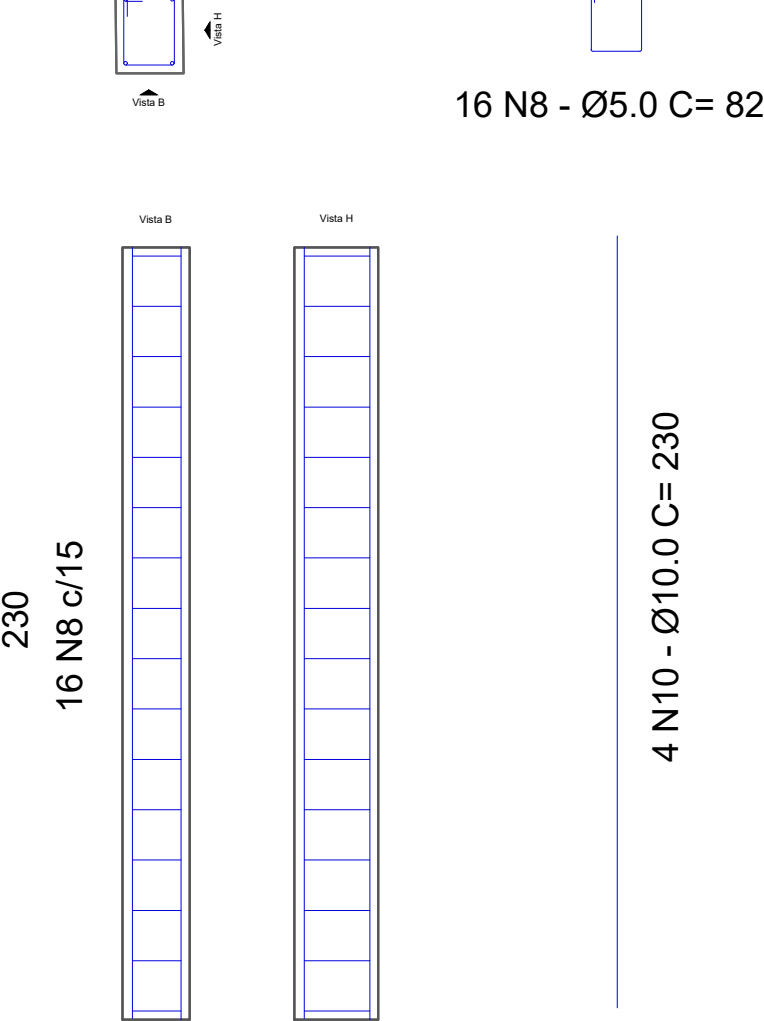


P88 = P89 = P101 = P102 = P114 = P115 = P125 = P126
20 x 25 cm

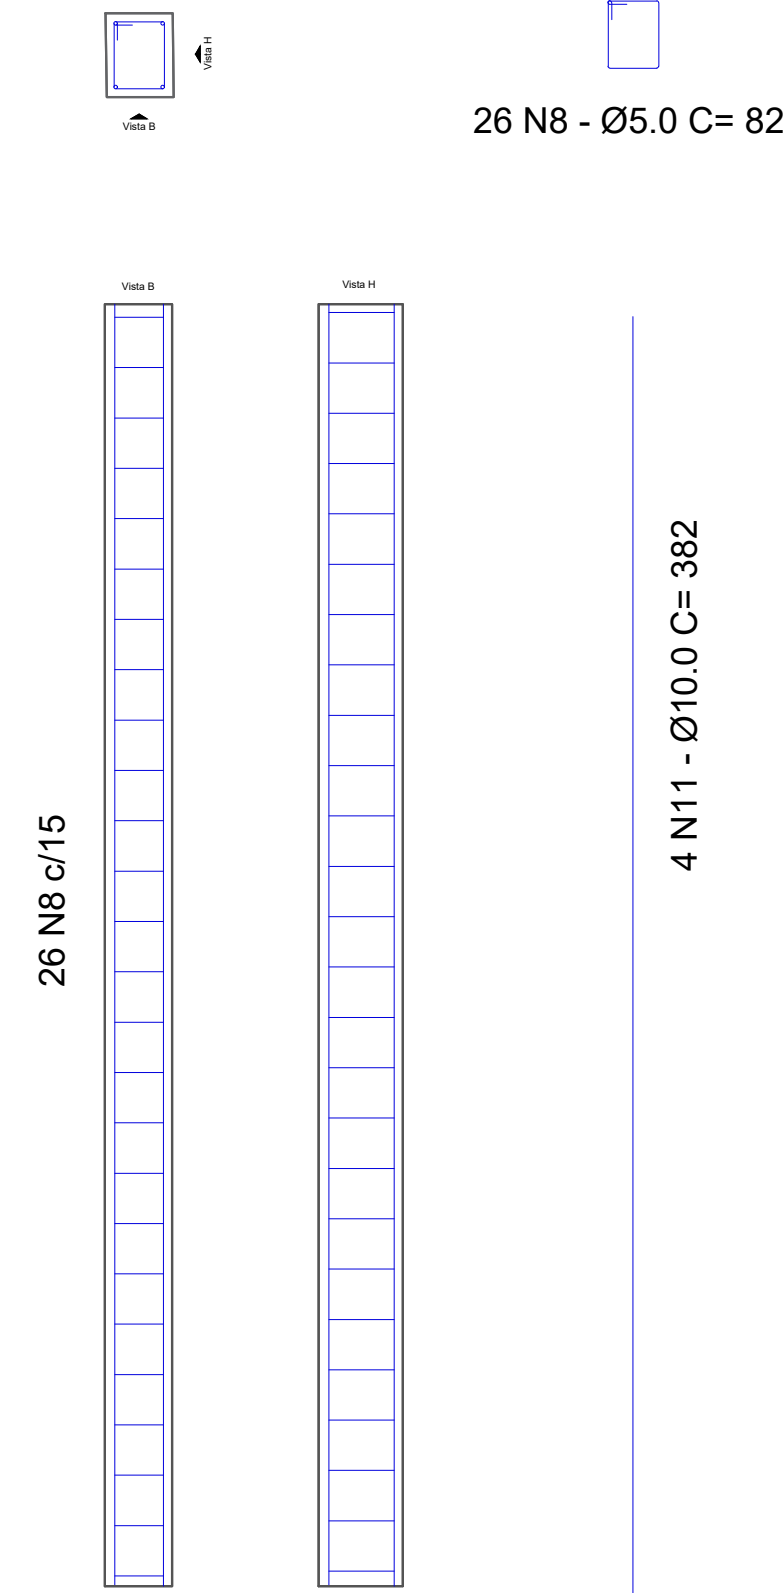


P94 = P95 = P121 = P122
20 x 25 cm

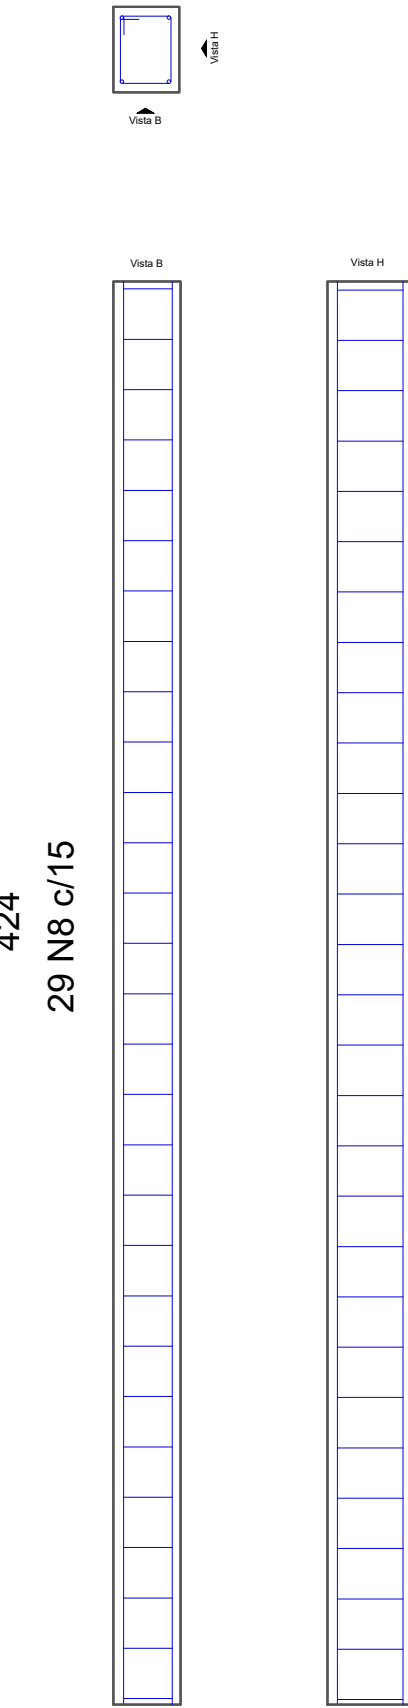


P38 = P41 = P42 = P45 = P46 = P47 = P51 = P54 = P96 = P97 = P98 = P99 = P110 = P111 = P112 = P113
20 x 25 cm

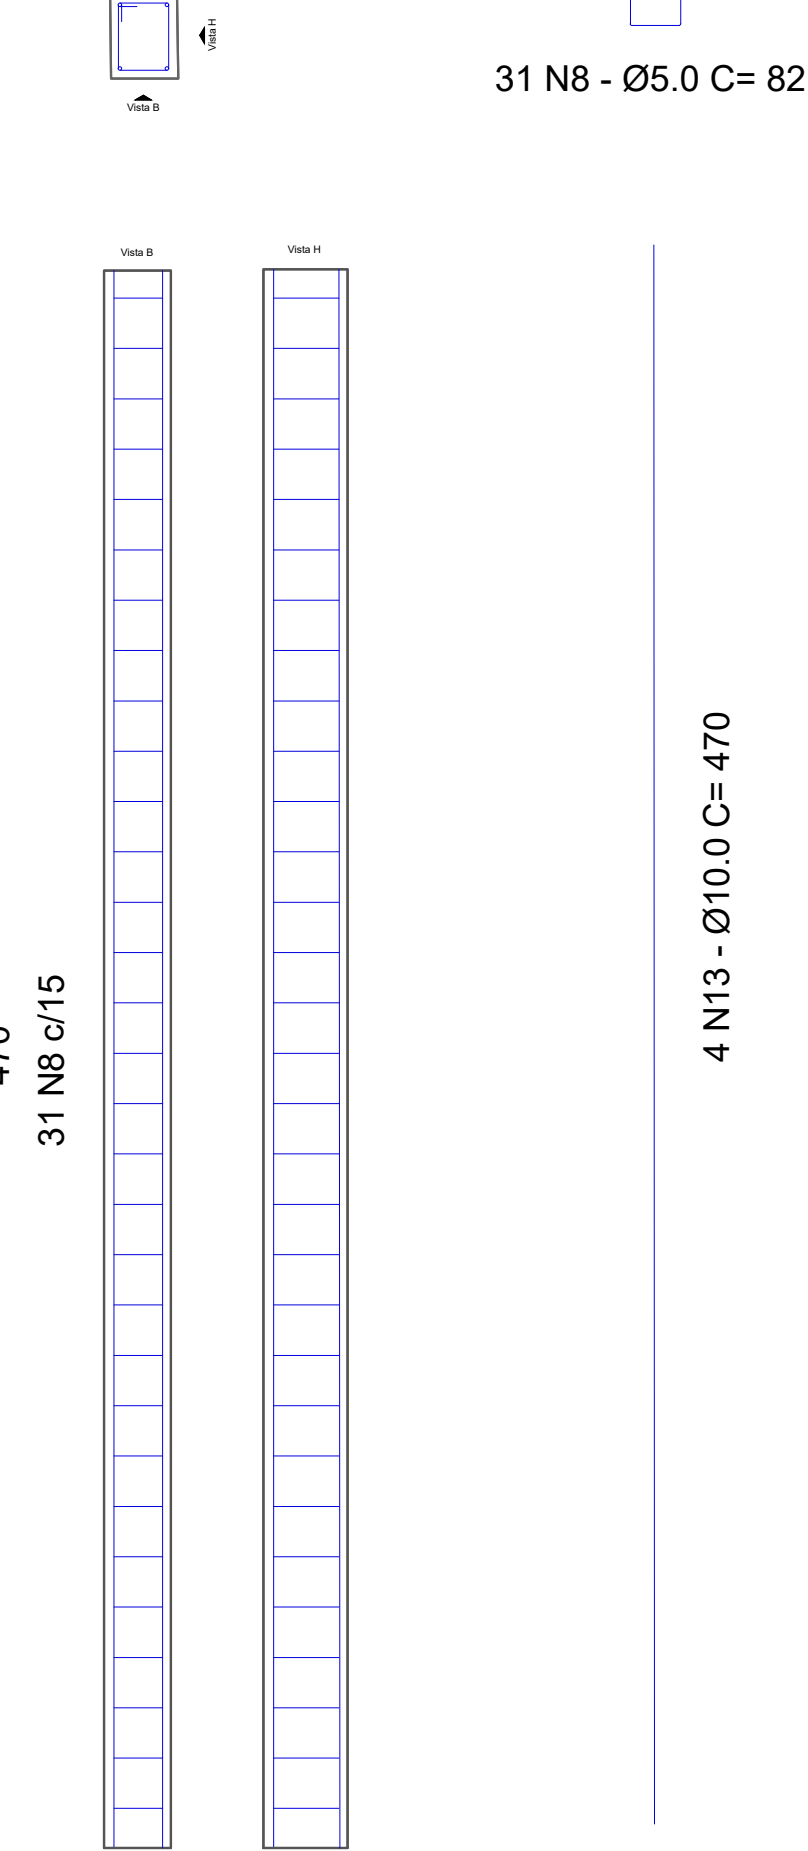


P48 = P52 = P55 = P56 = P57 = P58 = P59 = P60 = P61 = P62 = P63 = P64 = P65 = P66 = P67 = P68 = P69 = P70 = P72 = P74 = P77 = P80
20 x 25 cm

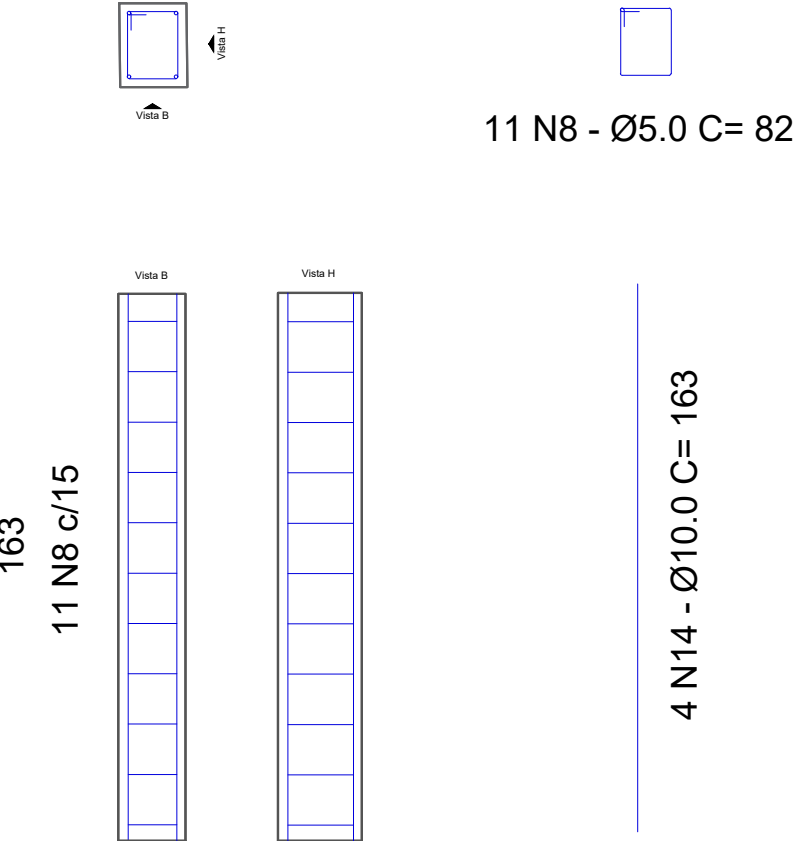


P71 = P773 = P75 = P76 = P78 = P79 = P105 = P109 = P117 = P118 = P123 = P124
20 x 25 cm

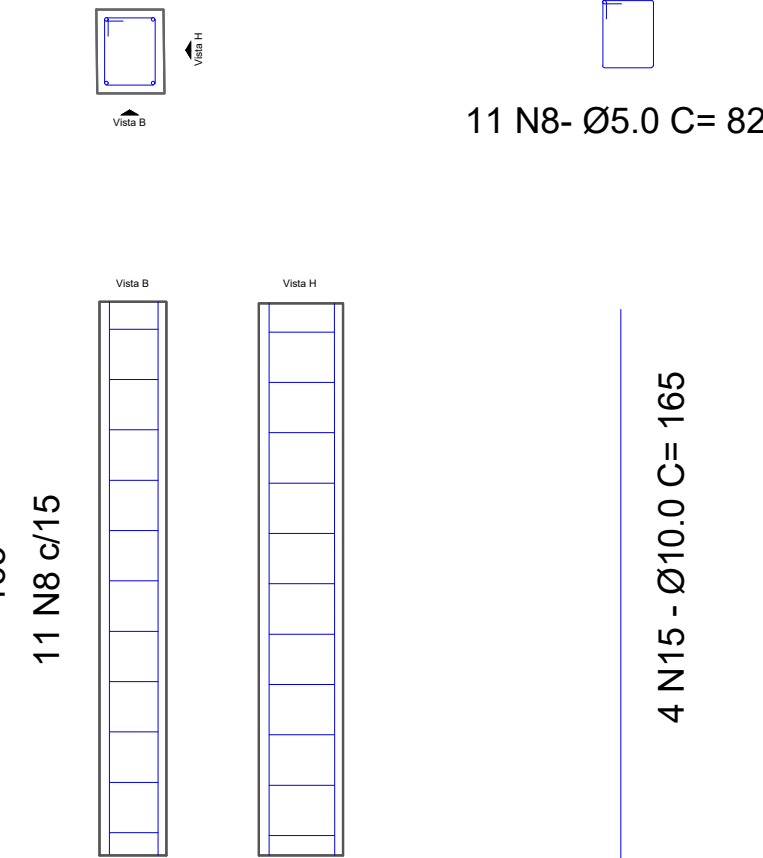


P81 = P83 = P86 = P87 = P90 = P91
20 x 25 cm

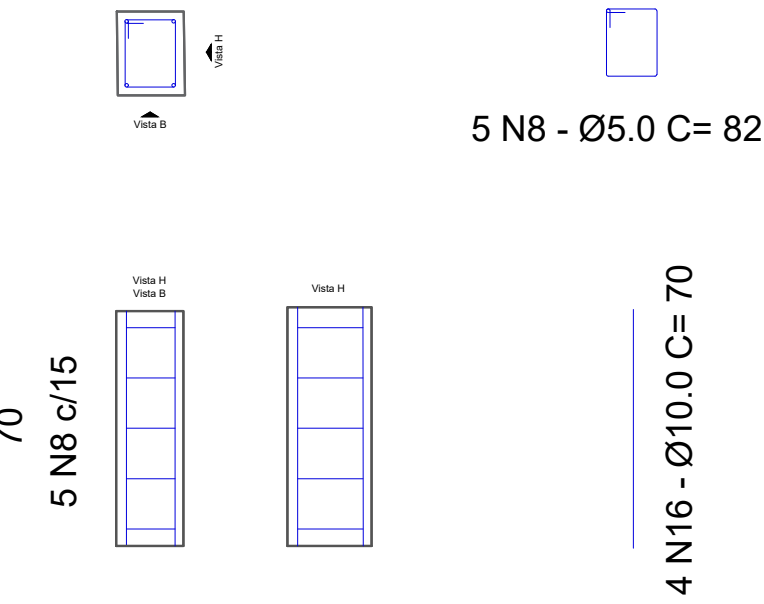

P130 = P131 = P133 = P134
20 x 25 cm

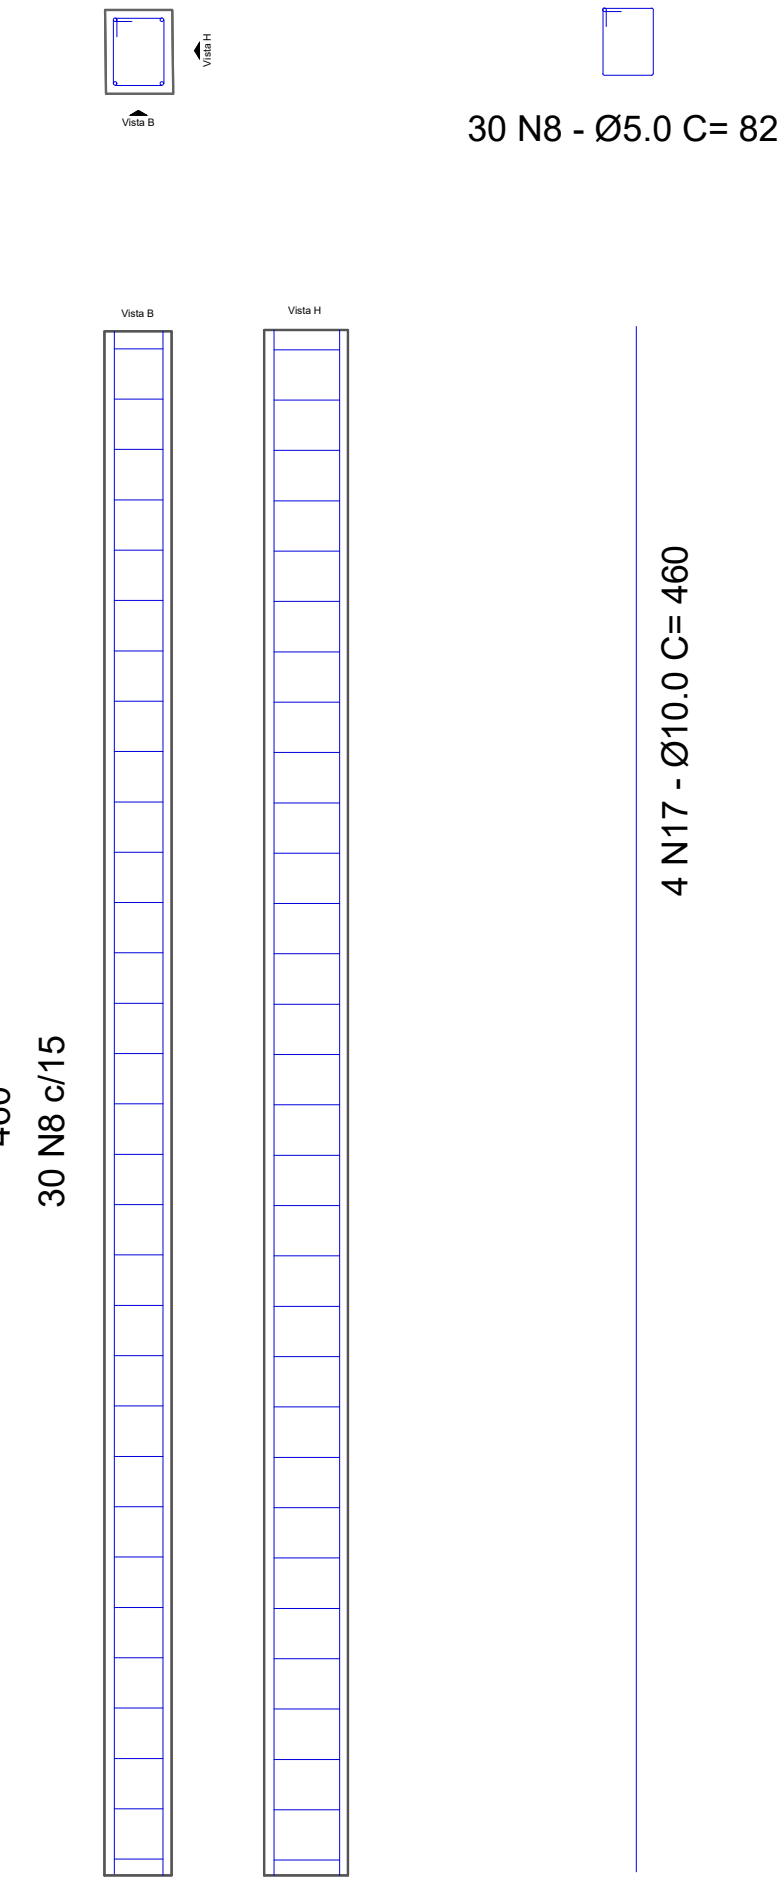

P132 = P135
20 x 25 cm

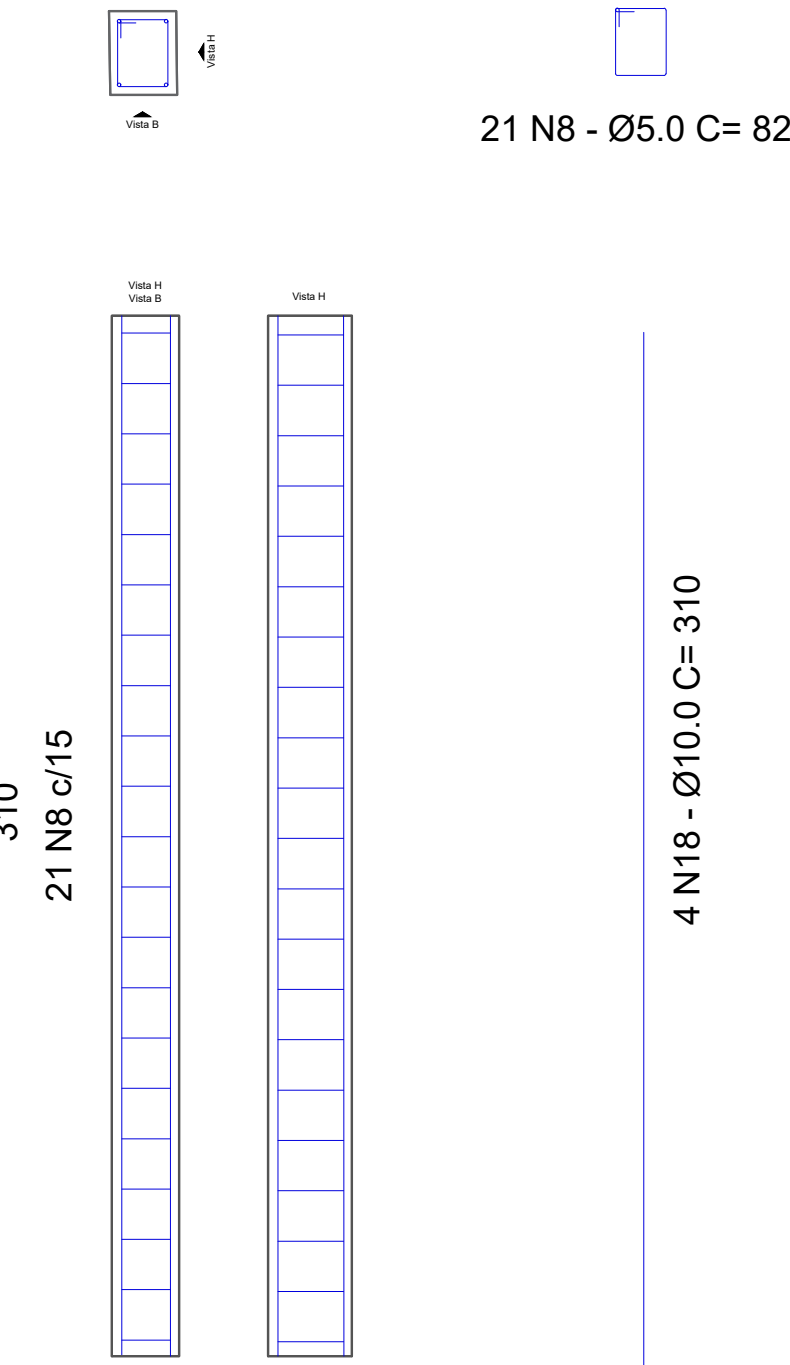

Projeto:

Projeto de Urbanismo Vila Olimpica

Desenhos:

PLANTA BAIXA DE LOCAÇÃO DOS ELEMENTOS ESTRUTURAIS

Observações:

- Conferir todas as medidas em obra antes da execução dos serviços.
- Não executar alterações sem autorização prévia do responsável técnico.
- Qualquer divergência entre projeto e condições de campo deverá ser comunicada ao responsável técnico para análise e aprovação.
- Todas as instalações deverão ser executadas por mão de obra qualificada, seguindo as normas técnicas vigentes e as recomendações dos fabricantes dos materiais empregados.
- O dimensionamento e posicionamentos indicados em projeto prevalecem sobre quaisquer informações complementares aqui descritas.

Esta prancha apresenta os detalhamentos dos pilares da edificação, contendo dimensões, armaduras longitudinais, armaduras transversais (estribos), emendas e demais informações necessárias para sua execução.

- Todos os pilares deverão ser executados rigorosamente conforme as dimensões indicadas nos detalhamentos estruturais.
- As armaduras longitudinais deverão ser montadas conforme as bitolas, quantidades, comprimentos de ancoragem e posicionamentos especificados em projeto.
- Os estribos deverão ser executados conforme diâmetros, espaçamentos, dimensões e dobramentos indicados nos detalhamentos.
- Deverão ser respeitados os cobrimentos mínimos das armaduras conforme especificado em projeto e nas normas técnicas vigentes.
- As emendas, transpasse das barras e ancoragens deverão seguir rigorosamente as especificações apresentadas nos detalhamentos estruturais.
- Os pilares deverão ser posicionados conforme os eixos estruturais definidos em projeto.
- Antes da concretagem, deverão ser conferidos alinhamento, prumo, dimensões das formas, posicionamento das armaduras, espaçamento dos estribos, cobrimentos e locação dos arranques.
- Não será permitida a alteração das armaduras, dimensões ou posicionamento dos pilares sem autorização do responsável técnico.
- Qualquer divergência identificada em campo deverá ser comunicada ao responsável técnico para análise e aprovação.
- Todos os serviços deverão atender às especificações do projeto estrutural e às normas técnicas vigentes.

Projetista:

Fernando Matias Mamede

RESPONSÁVEL TÉCNICO
Fernando Matias Mamede
Engenheiro Civil
Crea: 162056275-6

Proprietário:

Prefeitura Municipal de Coremas

PROPRIETÁRIO(A)

Endereço/Obra:

Rua Francisco Raimundo de Andrade, DNOCS, Coremas - PB, 58770-000

ÁREAS

m²

Área do Terreno

10.733,41

Estacionamento

519,11

Calçada

249,64



Área verde

4.281,11

Prancha:


04/14

V1=V2=V3
15 x 25 cm

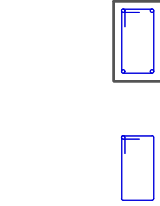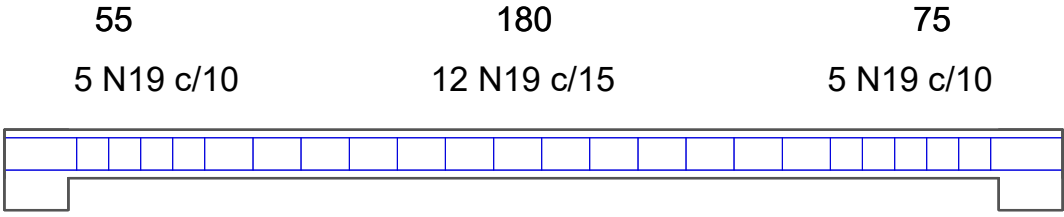


22 N19 - Ø5.0 C= 72

V4=V5
15 x 25 cm

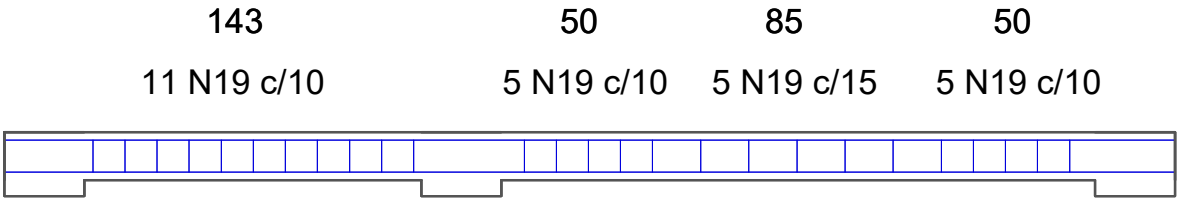



26 N19 - Ø5.0 C= 72

V6=V10
15 x 25 cm

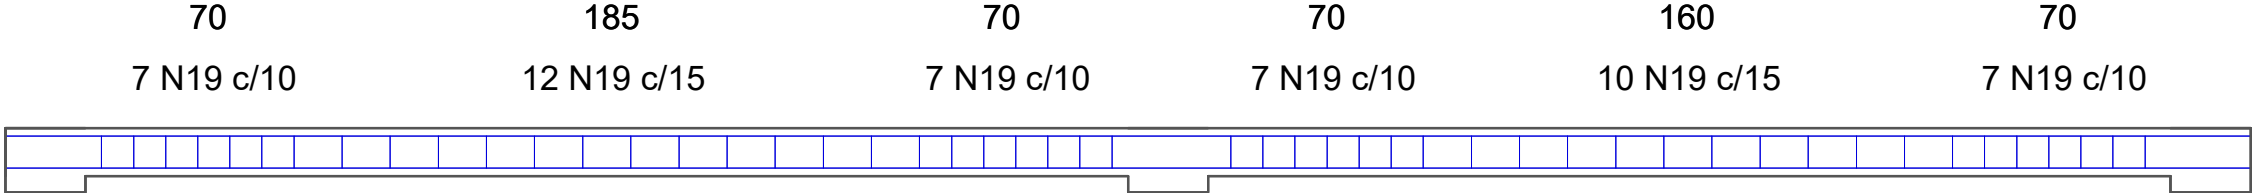


50 N19 - Ø5.0 C= 72

V7=V8=V9
15 x 25 cm

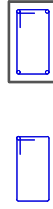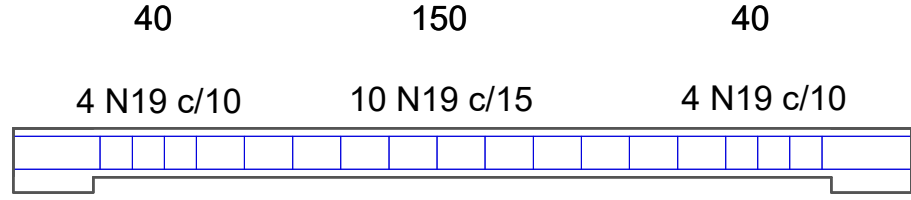



18 N19 - Ø5.0 C= 72

V12=V13
15 x 25 cm

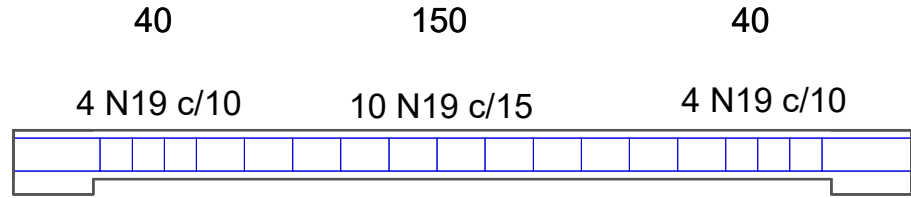

18 N19 - Ø5.0 C= 72


V11=V14
15 x 30 cm

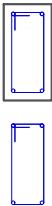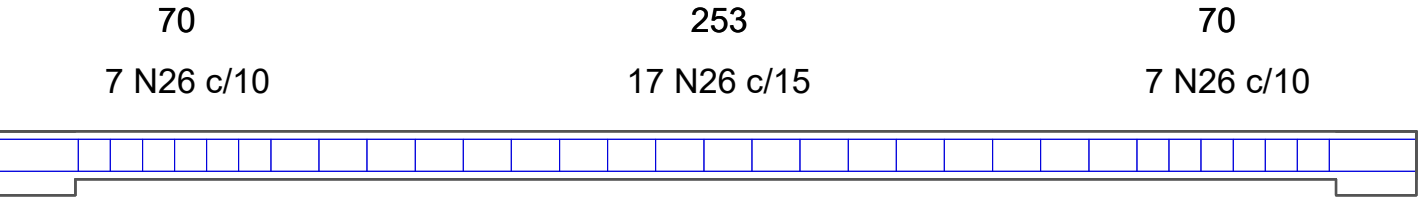


4 N25 - Ø10.0 C= 438

31 N26 - Ø5.0 C= 82


QUIOSQUE

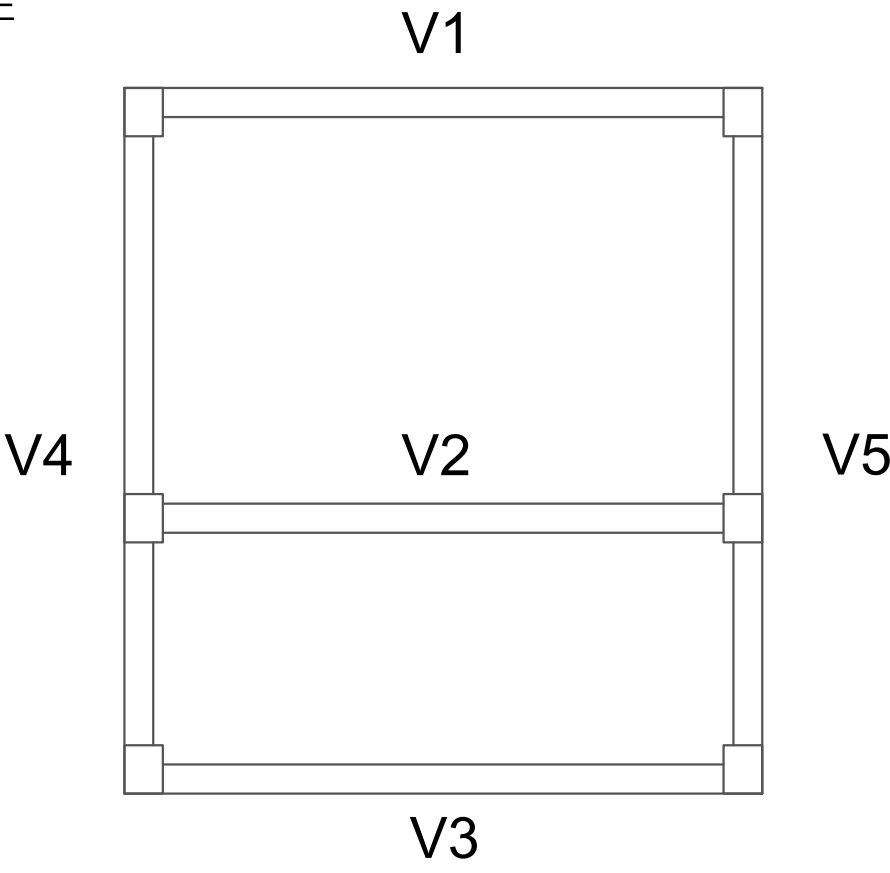

GUARITA

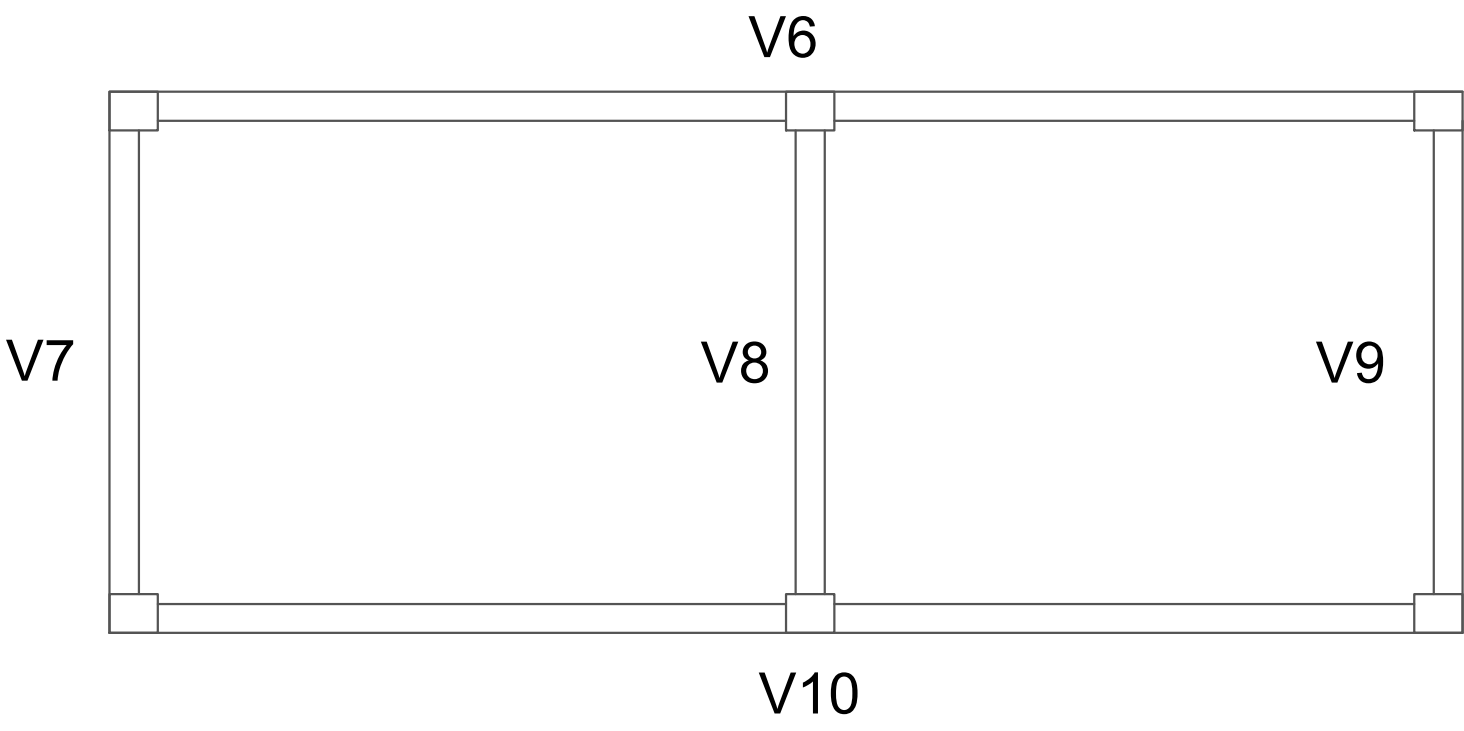

BANHEIROS

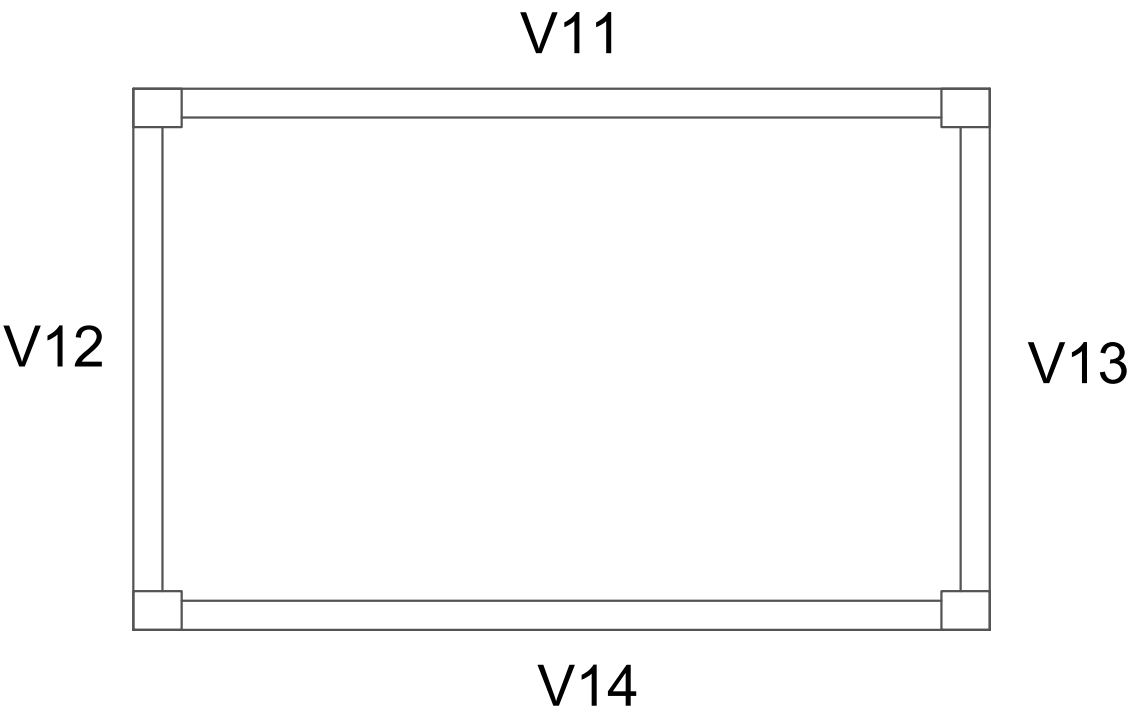

Projeto:

Projeto de Urbanismo Vila Olimpica

Desenhos:

PLANTA BAIXA DE LOCAÇÃO DOS ELEMENTOS ESTRUTURAIS

Observações:

- Conferir todas as medidas em obra antes da execução dos serviços.
- Não executar alterações sem autorização prévia do responsável técnico.
- Qualquer divergência entre projeto e condições de campo deverá ser comunicada ao responsável técnico para análise e aprovação.
- Todas as instalações deverão ser executadas por mão de obra qualificada, seguindo as normas técnicas vigentes e as recomendações dos fabricantes dos materiais empregados.
- O dimensionamento e posicionamentos indicados em projeto prevalecem sobre quaisquer informações complementares aqui descritas.

Esta prancha apresenta os detalhamentos das vigas da edificação, contendo dimensões, armaduras longitudinais, armaduras transversais (estribos), ancoragens, emendas e demais informações necessárias para sua execução.

- Todas as vigas deverão ser executadas rigorosamente conforme as dimensões indicadas nos detalhamentos estruturais.
- As armaduras longitudinais superiores e inferiores deverão ser montadas conforme as bitolas, quantidades, comprimentos, ancoragens e posicionamentos especificados em projeto.
- Os estribos deverão ser executados conforme diâmetros, espaçamentos, dimensões e dobramentos indicados nos detalhamentos.
- Deverão ser respeitados os cobrimentos mínimos das armaduras conforme especificado em projeto e nas normas técnicas vigentes.
- As emendas, transpasse das barras e ancoragens deverão seguir rigorosamente as especificações apresentadas nos detalhamentos estruturais.
- As passagens de tubulações, eletrodutos ou quaisquer outros elementos através das vigas somente poderão ser executadas quando previstas em projeto ou autorizadas pelo responsável técnico.
- Antes da concretagem, deverão ser conferidos alinhamento, nivelamento, dimensões das formas, posicionamento das armaduras, espaçamento dos estribos, cobrimentos e demais elementos previstos em projeto.
- Não será permitida a alteração das armaduras, dimensões ou posicionamento das vigas sem autorização do responsável técnico.
- Qualquer divergência identificada em campo deverá ser comunicada ao responsável técnico para análise e aprovação.
- Todos os serviços deverão atender às especificações do projeto estrutural e às normas técnicas vigentes.

Projetista:

Fernando Matias Mamede

RESPONSÁVEL TÉCNICO
Fernando Matias Mamede
Engenheiro Civil
Crea: 162056275-6



Proprietário:

Prefeitura Municipal de Coremas



PROPRIETÁRIO(A)


Endereço/Obra: Rua Francisco Raimundo de Andrade, DNOCS, Coremas - PB, 58770-000

ÁREAS	m²
Área do Terreno	10.733,41
Estacionamento	519,11
Calçada	249,64
Área verde	4.281,11


Prancha:

05/14



QUIOSQUE

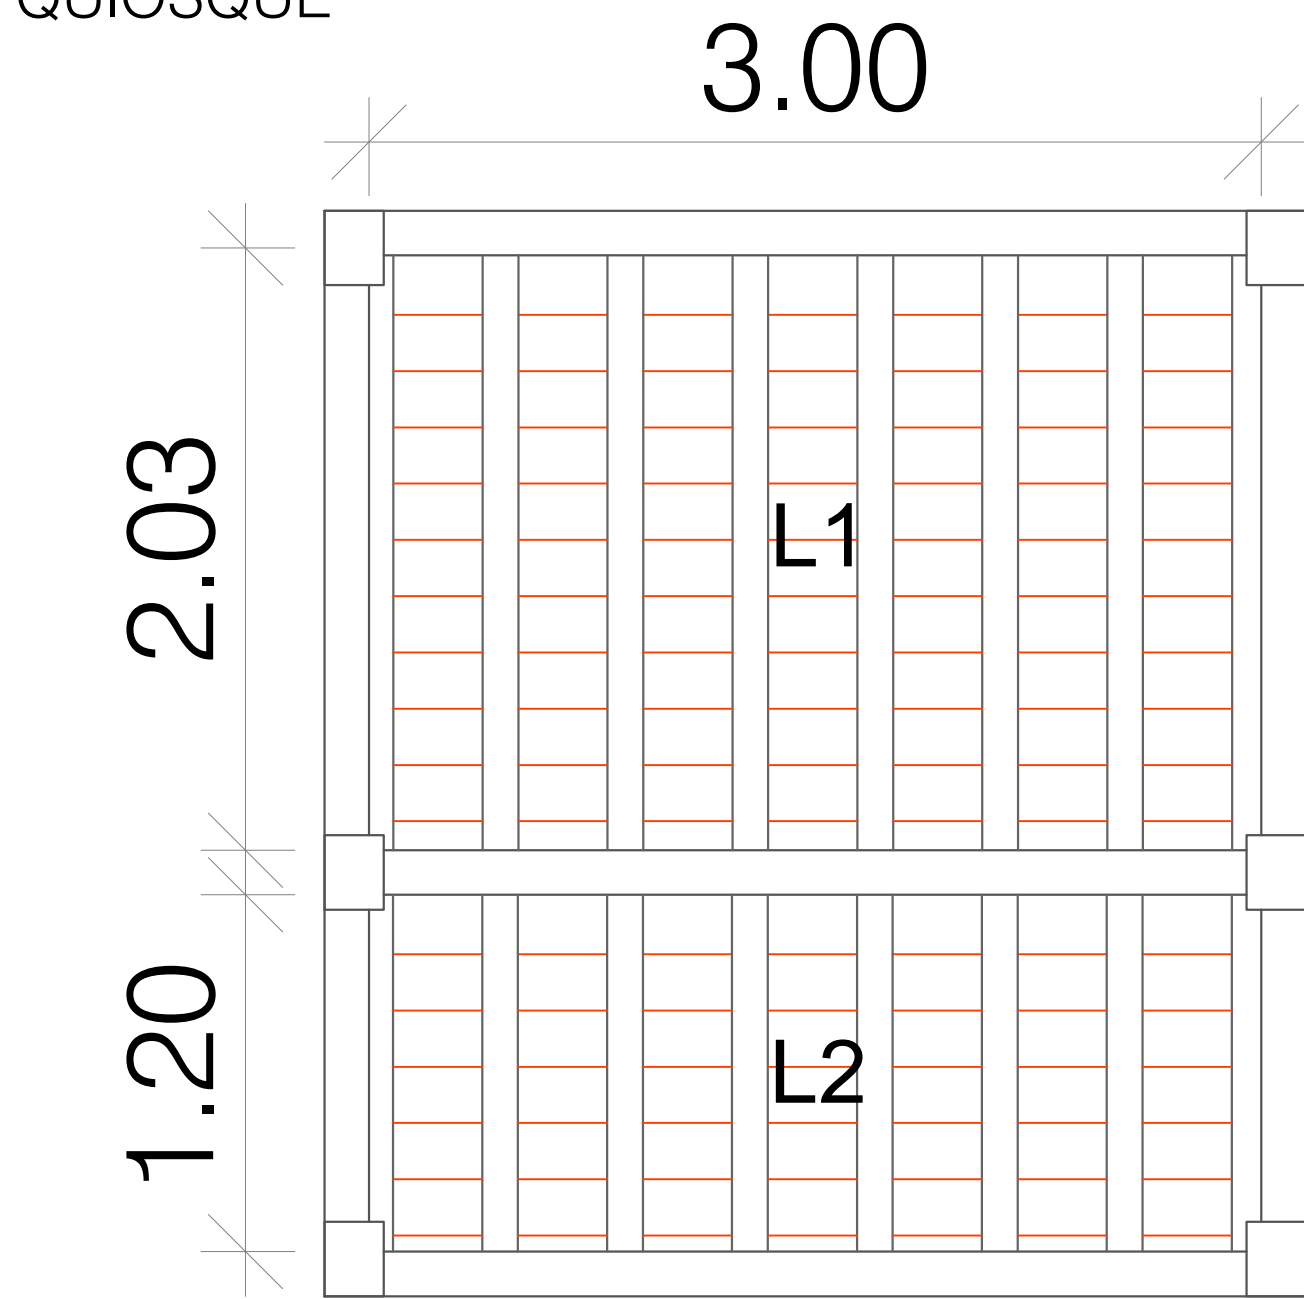

GUARITA

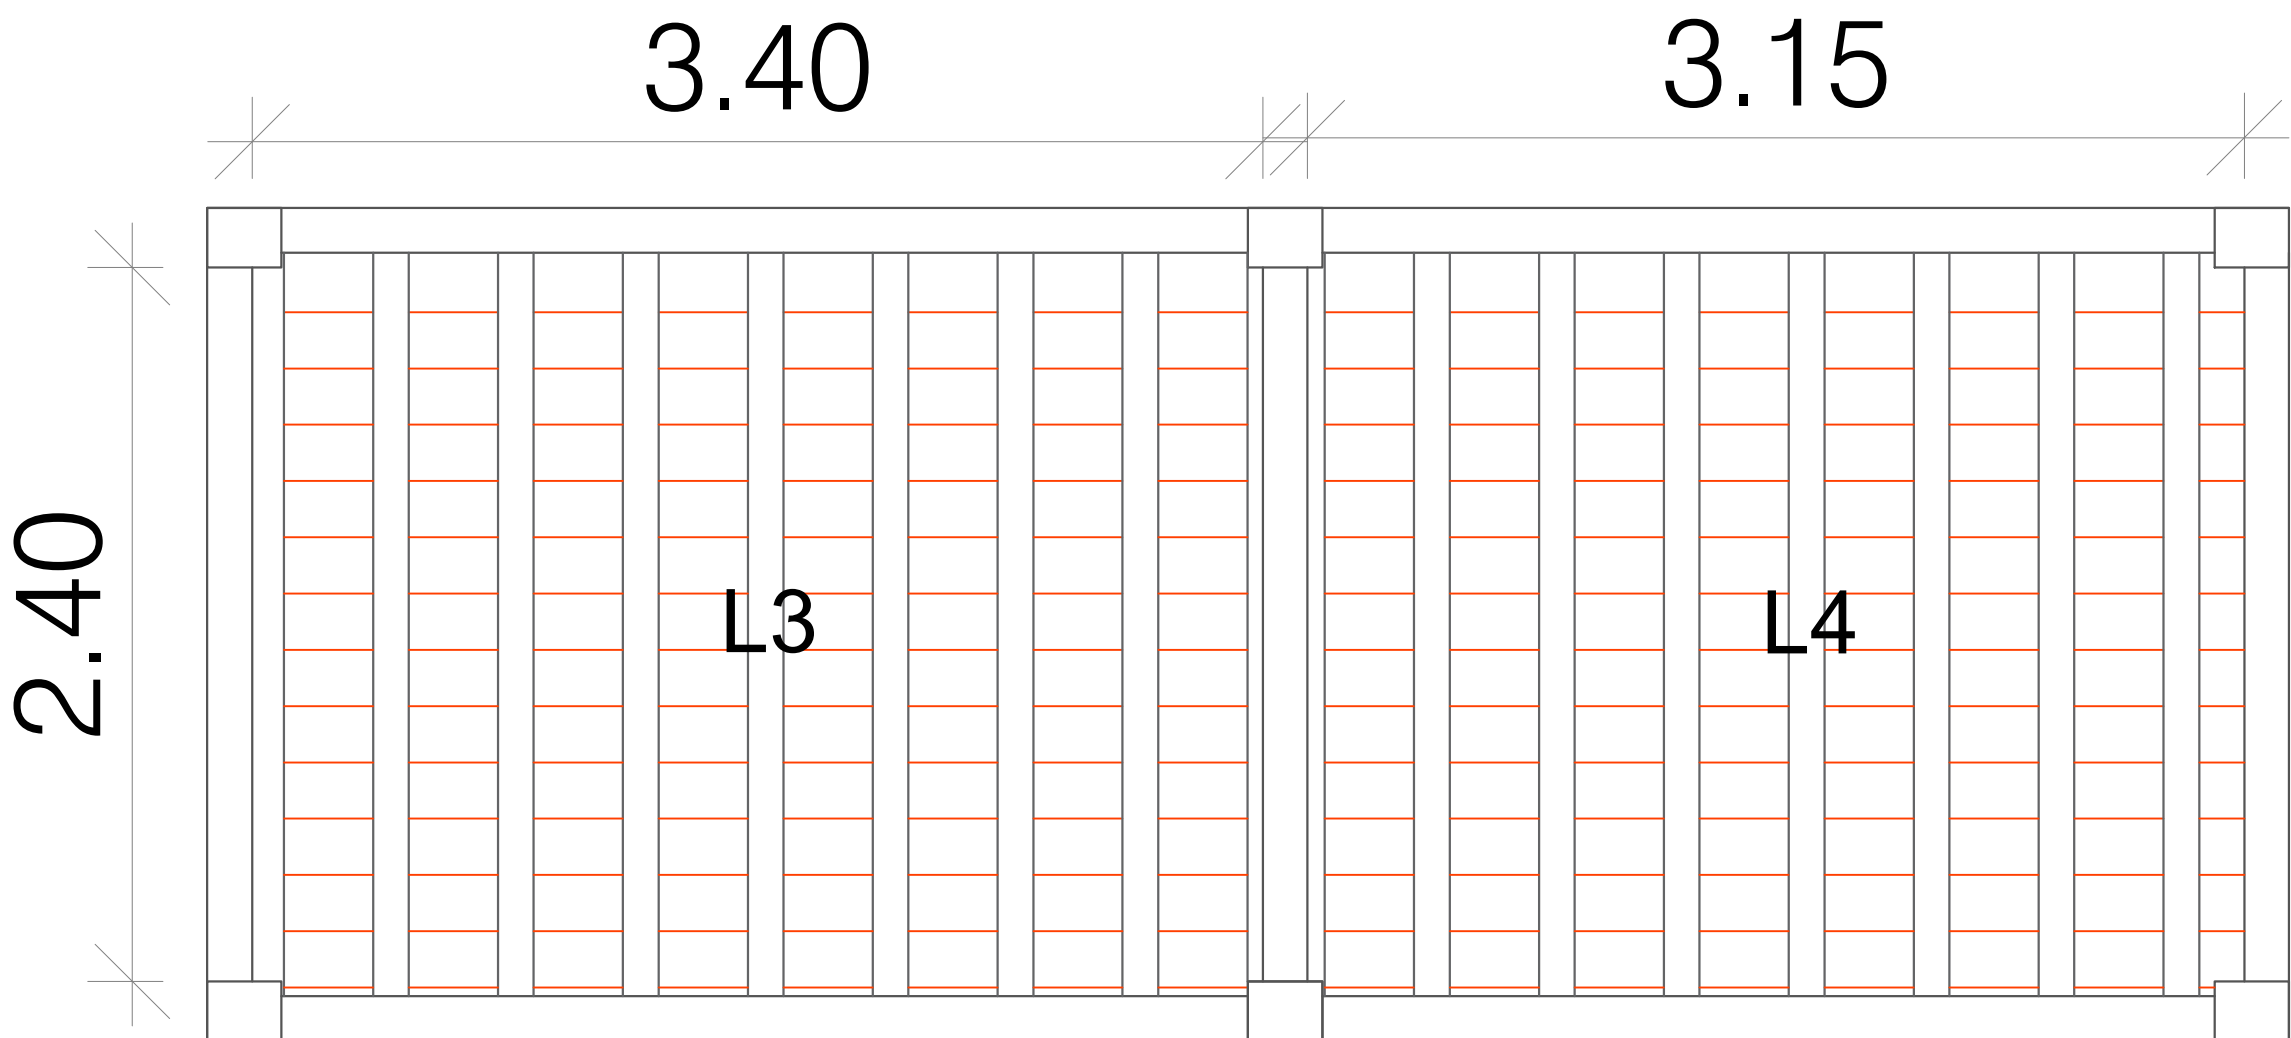

BANHEIROS

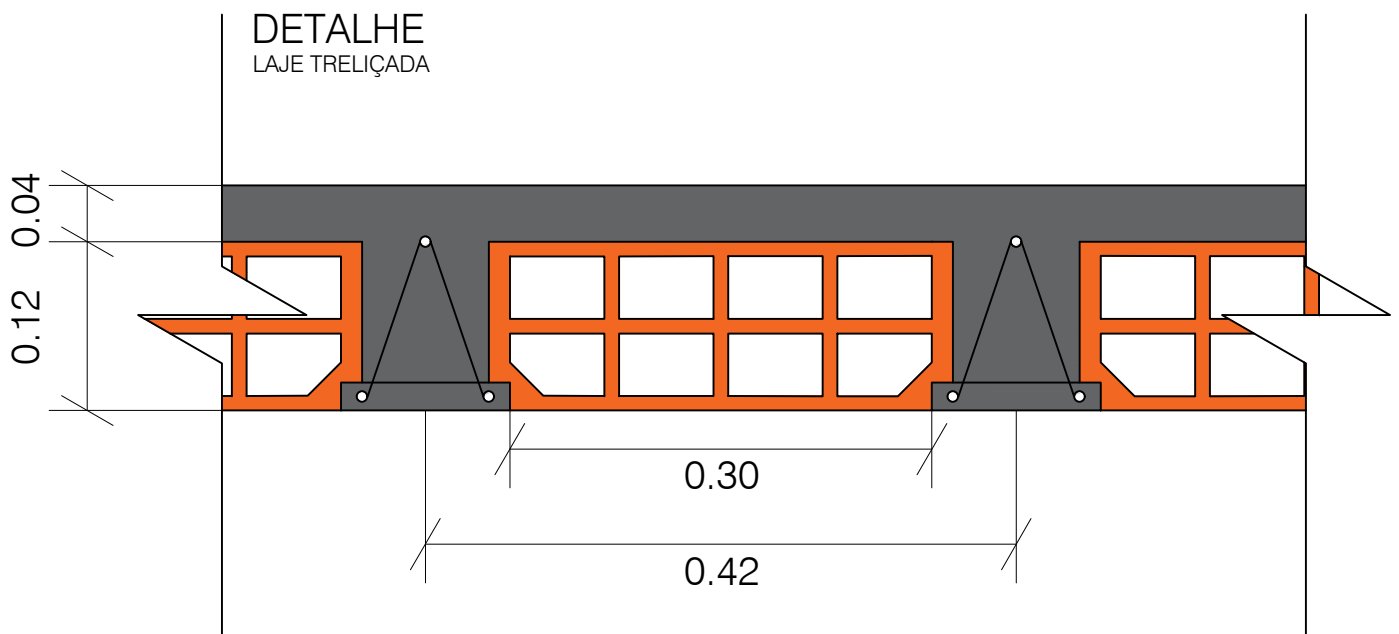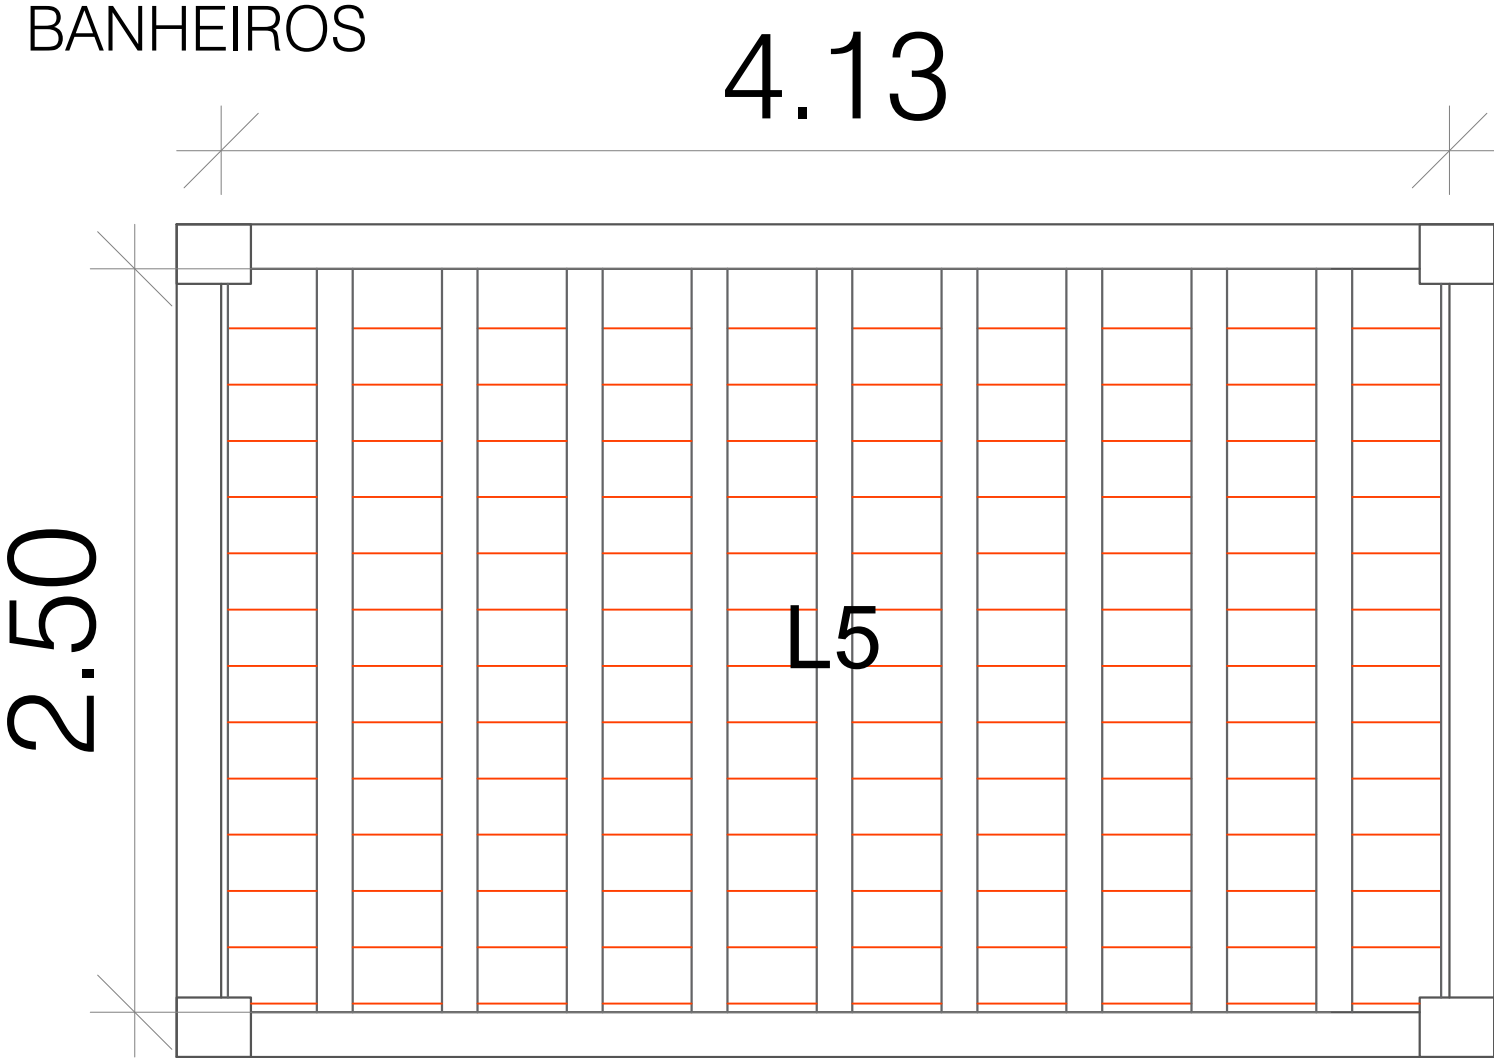

Projeto:

Projeto de Urbanismo Vila Olimpica

Desenhos:

PLANTA BAIXA DE LOCAÇÃO DOS ELEMENTOS ESTRUTURAIS

Observações:

- Conferir todas as medidas em obra antes da execução dos serviços.
- Não executar alterações sem autorização prévia do responsável técnico.
- Qualquer divergência entre projeto e condições de campo deverá ser comunicada ao responsável técnico para análise e aprovação.
- Todas as instalações deverão ser executadas por mão de obra qualificada, seguindo as normas técnicas vigentes e as recomendações dos fabricantes dos materiais empregados.
- O dimensionamento e posicionamentos indicados em projeto prevalecem sobre quaisquer informações complementares aqui descritas.

Esta prancha apresenta os detalhamentos das lajes da edificação, contendo informações de espessura, altura total, altura da capa de concreto, armaduras complementares, reforços e demais elementos necessários para sua execução.

- As lajes serão executadas em sistema treliçado com elementos de enchimento em bloco cerâmico, conforme especificado em projeto.
- A altura das vigotas treliçadas, a espessura da capa de concreto, a altura total da laje e os elementos de enchimento deverão seguir rigorosamente as especificações indicadas nos detalhamentos estruturais.
- As armaduras complementares, armaduras negativas, armaduras de distribuição, reforços localizados e demais elementos estruturais deverão ser executados conforme bitolas, quantidades, comprimentos e posicionamentos definidos em projeto.
- Os escoramentos deverão permanecer instalados durante o período mínimo necessário para garantir a adequada resistência do concreto, conforme orientação técnica e cronograma de execução.
- Antes da concretagem, deverão ser conferidos o posicionamento das vigotas, alinhamento, nivelamento, escoramento, armaduras complementares, instalações embutidas e demais elementos previstos em projeto.
- Não será permitida a abertura de furos, rasgos ou remoção de elementos estruturais sem autorização do responsável técnico.
- As passagens de instalações elétricas, hidráulicas e sanitárias deverão respeitar as posições previstas em projeto.
- Qualquer divergência identificada em campo deverá ser comunicada ao responsável técnico para análise e aprovação.
- Todos os serviços deverão atender às especificações do projeto estrutural e às normas técnicas vigentes.

Projetista:

Fernando Matias Mamede

RESPONSÁVEL TÉCNICO
Fernando Matias Mamede
Engenheiro Civil
Crea: 162056275-6

Proprietário:

Prefeitura Municipal de Coremas

PROPRIETÁRIO(A)

Endereço/Obra:

Rua Francisco Raimundo de Andrade, DNOCS, Coremas - PB, 58770-000

ÁREAS

m²

Área do Terreno

10.733,41

Estacionamento

519,11

Calçada

249,64

Área verde

4.281,11

Prancha:


06/14

MAMEDE

PROJ. CIVIL

PREFEITURA MUNICIPAL DE COREMAS

1 DE ABRIL DE 2014

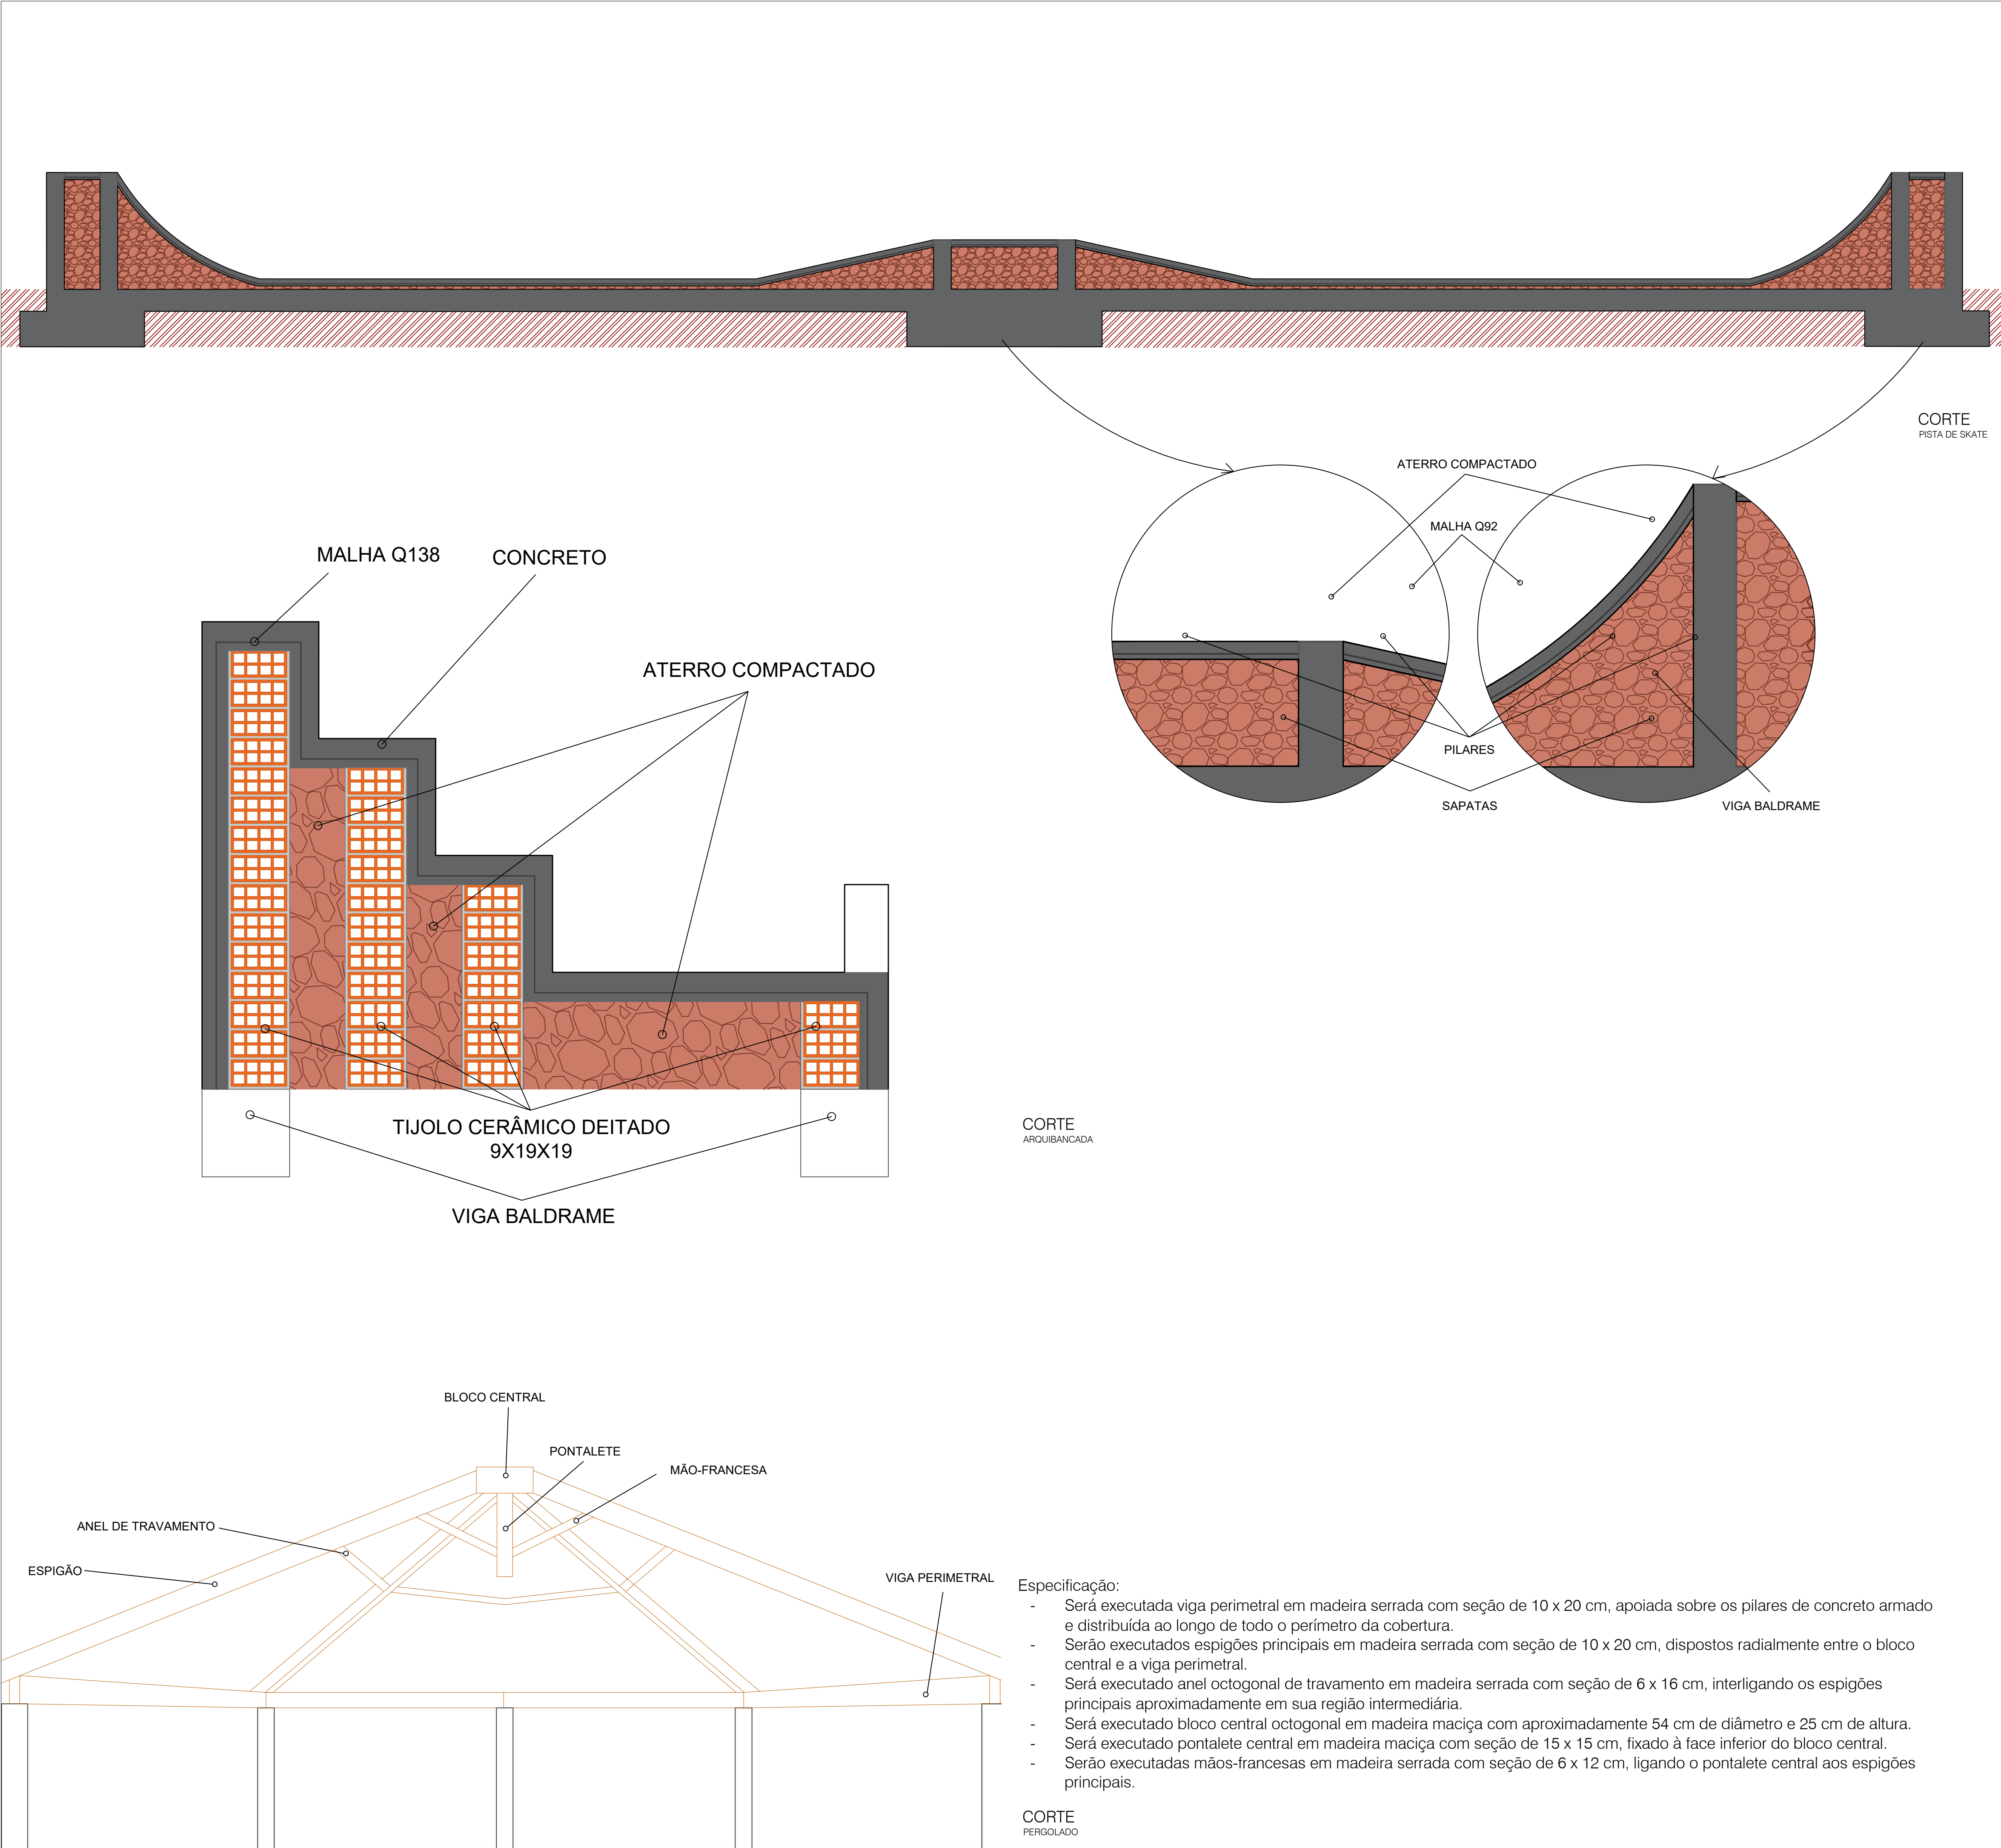

Projeto:

Projeto de Urbanismo Vila Olimpica

Desenhos:

PLANTA BAIXA DE LOCAÇÃO DOS ELEMENTOS ESTRUTURAIS

Observações:

- Conferir todas as medidas em obra antes da execução dos serviços.
- Não executar alterações sem autorização prévia do responsável técnico.
- Qualquer divergência entre projeto e condições de campo deverá ser comunicada ao responsável técnico para análise e aprovação.
- Todas as instalações deverão ser executadas por mão de obra qualificada, seguindo as normas técnicas vigentes e as recomendações dos fabricantes dos materiais empregados.
- O dimensionamento e posicionamentos indicados em projeto prevalecem sobre quaisquer informações complementares aqui descritas.

Esta prancha apresenta os detalhamentos construtivos da pista de skate e das arquibancadas, devendo sua execução seguir rigorosamente as dimensões, níveis, materiais e especificações indicados em projeto.

- A pista de skate deverá ser executada sobre aterro devidamente compactado.
- O aterro deverá ser realizado em camadas sucessivas de, no máximo, 20 cm de espessura, com compactação adequada de cada camada, até atingir os níveis definidos em projeto.
- Sobre o aterro compactado deverá ser executada uma capa de concreto com espessura de 10 cm.
- A capa de concreto deverá ser armada com tela soldada tipo Q92, posicionada conforme detalhamento apresentado em projeto.
- As superfícies deverão apresentar acabamento uniforme, respeitando os níveis, inclinações e geometrias indicadas nos detalhamentos.
- Os pilares de sustentação deverão ser executados conforme os detalhamentos específicos constantes na prancha de pilares.

- As arquibancadas deverão ser executadas conforme as dimensões e níveis indicados em projeto.
- Cada degrau será formado por alvenaria de vedação executada com tijolos cerâmicos assentados horizontalmente, conforme detalhamento apresentado.
- Os espaços internos entre os elementos de contenção deverão ser preenchidos com aterro compactado.
- O aterro deverá ser executado em camadas sucessivas de, no máximo, 20 cm de espessura, com compactação adequada de cada camada.
- Sobre o aterro compactado deverá ser executada uma capa de concreto com espessura de 10 cm.
- A capa de concreto das arquibancadas deverá ser armada com tela soldada tipo Q138, posicionada conforme detalhamento estrutural.

Projetista:

Fernando Matias Mamede

RESPONSÁVEL TÉCNICO
Fernando Matias Mamede
Engenheiro Civil
Crea: 162056275-6

Proprietário:

Prefeitura Municipal de Coremas

PROPRIETÁRIO(A)

Endereço/Obra:

Rua Francisco Raimundo de Andrade, DNOCS, Coremas - PB, 58770-000

ÁREAS

m²

Área do Terreno

10.733,41

Estacionamento

519,11

Calçada


249,64

Área verde


4.281,11

Prancha:


07/14

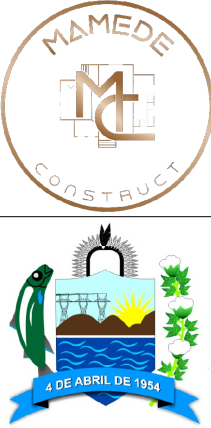


Detalhamento Eletrico - Banheiros 1

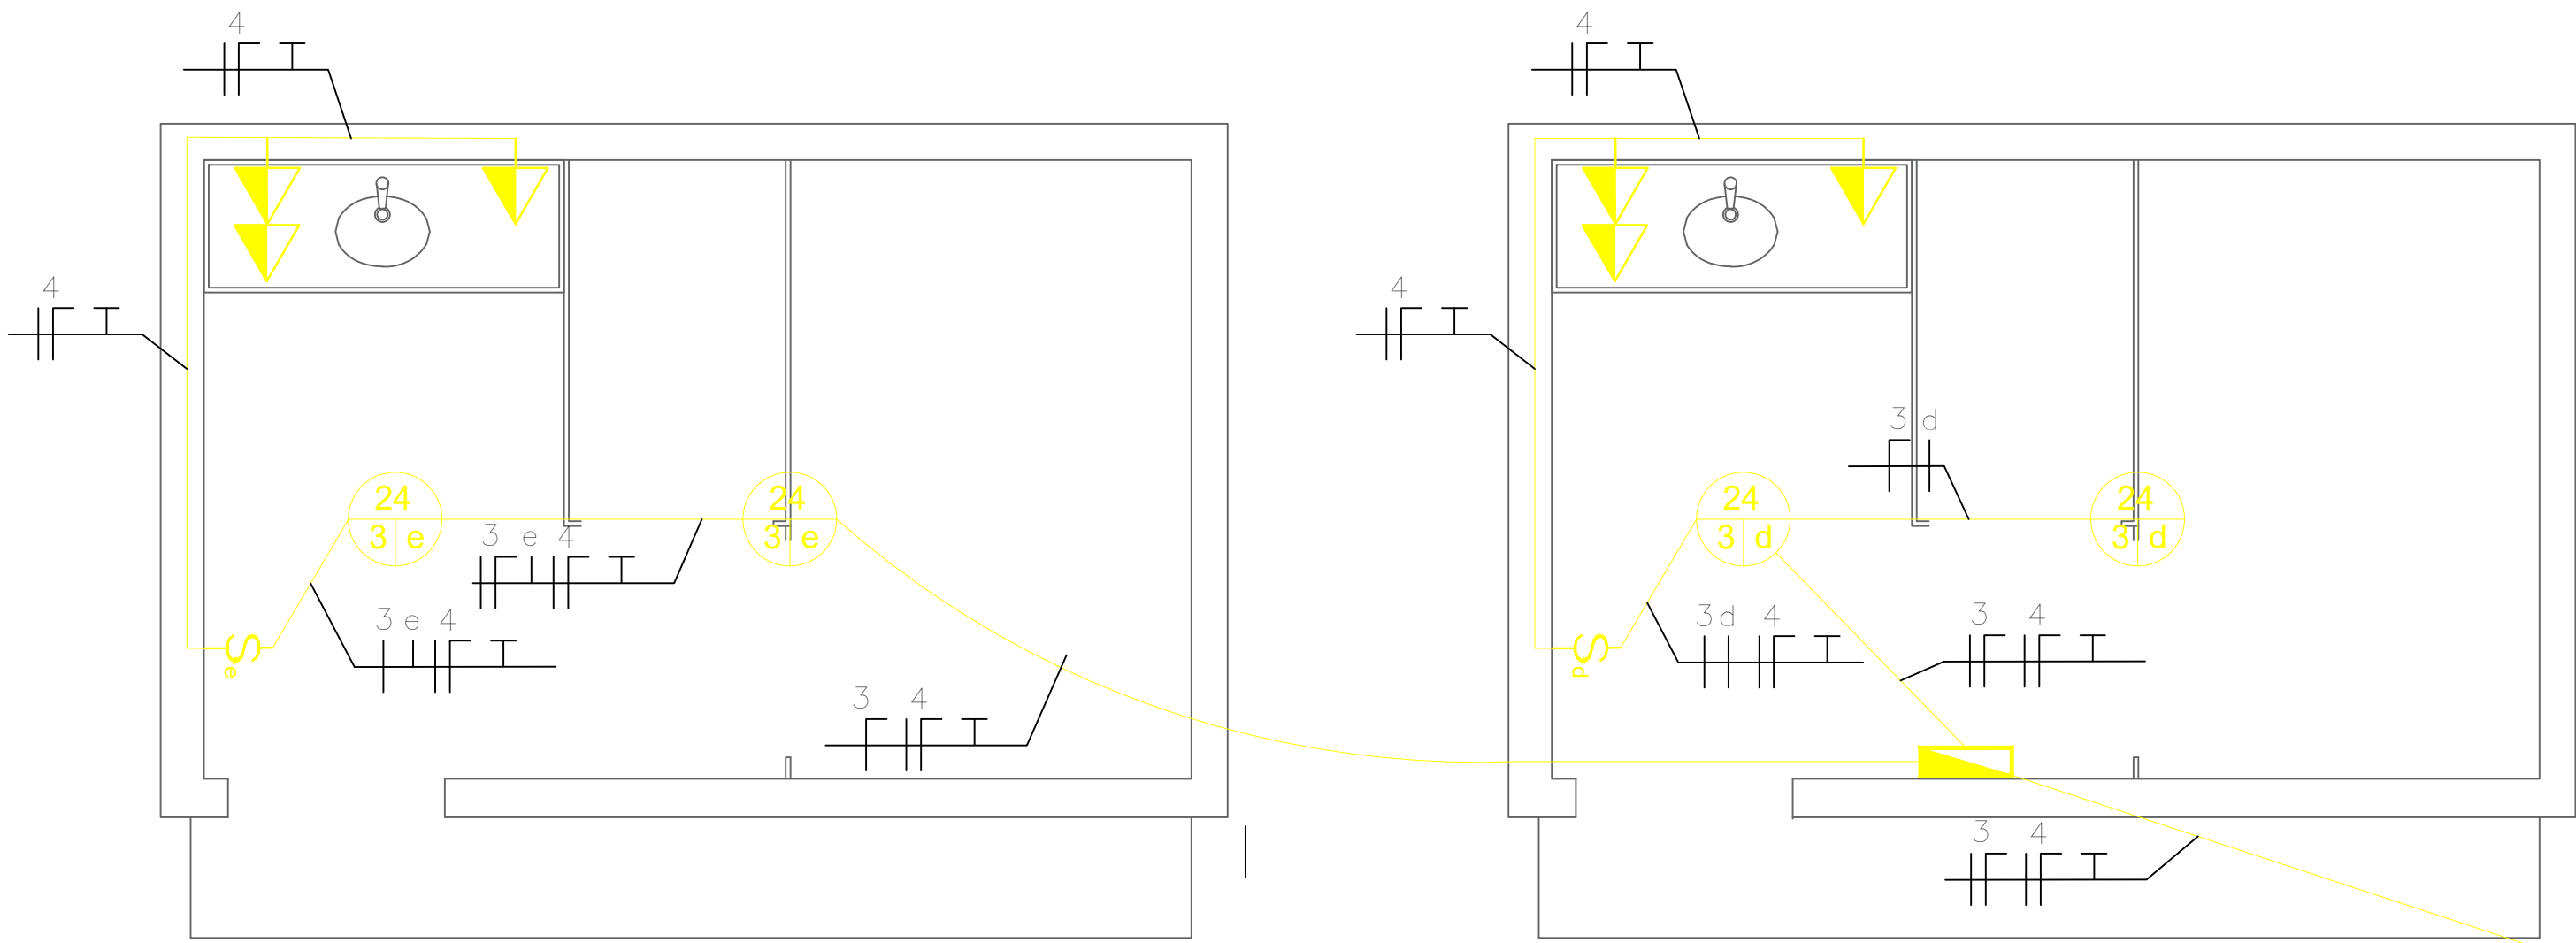


Detalhamento Eletrico - Quiosque 1

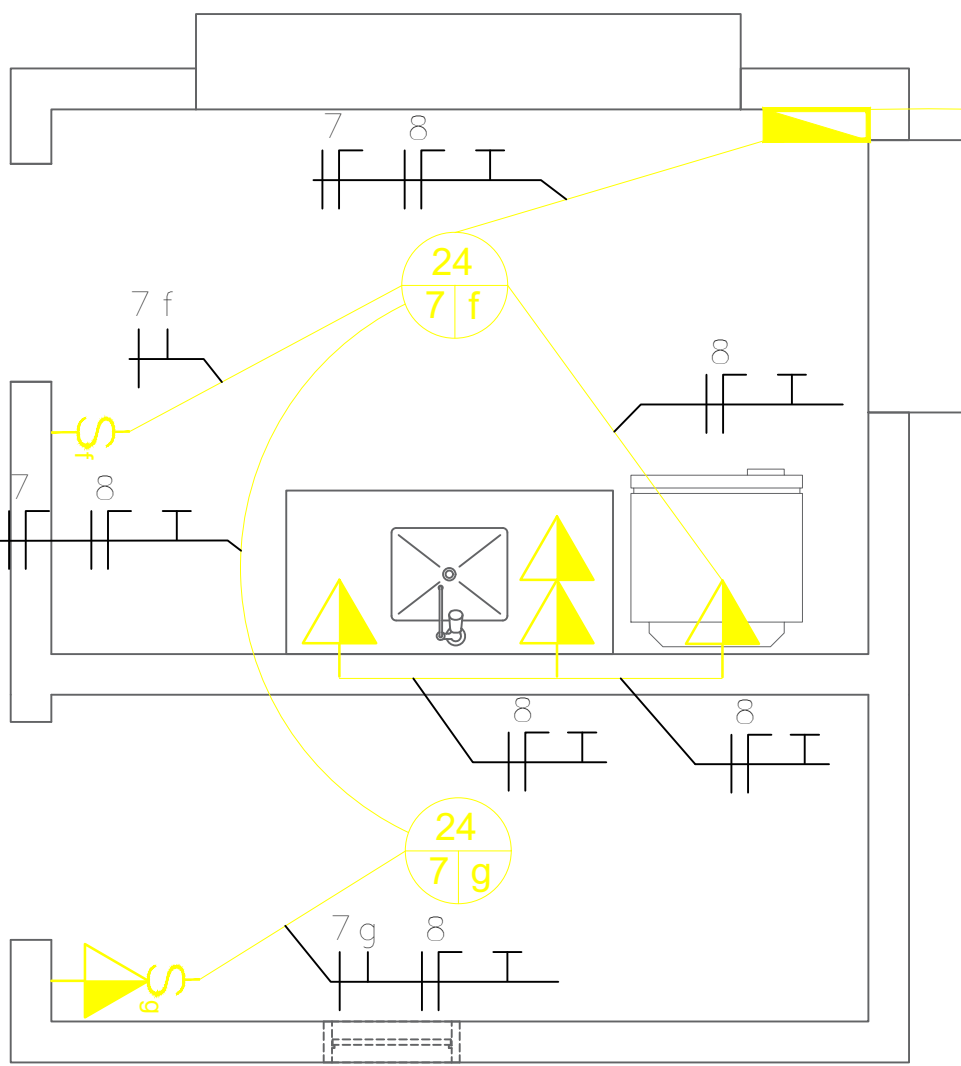


Detalhamento Eletrico - Banheiros 2

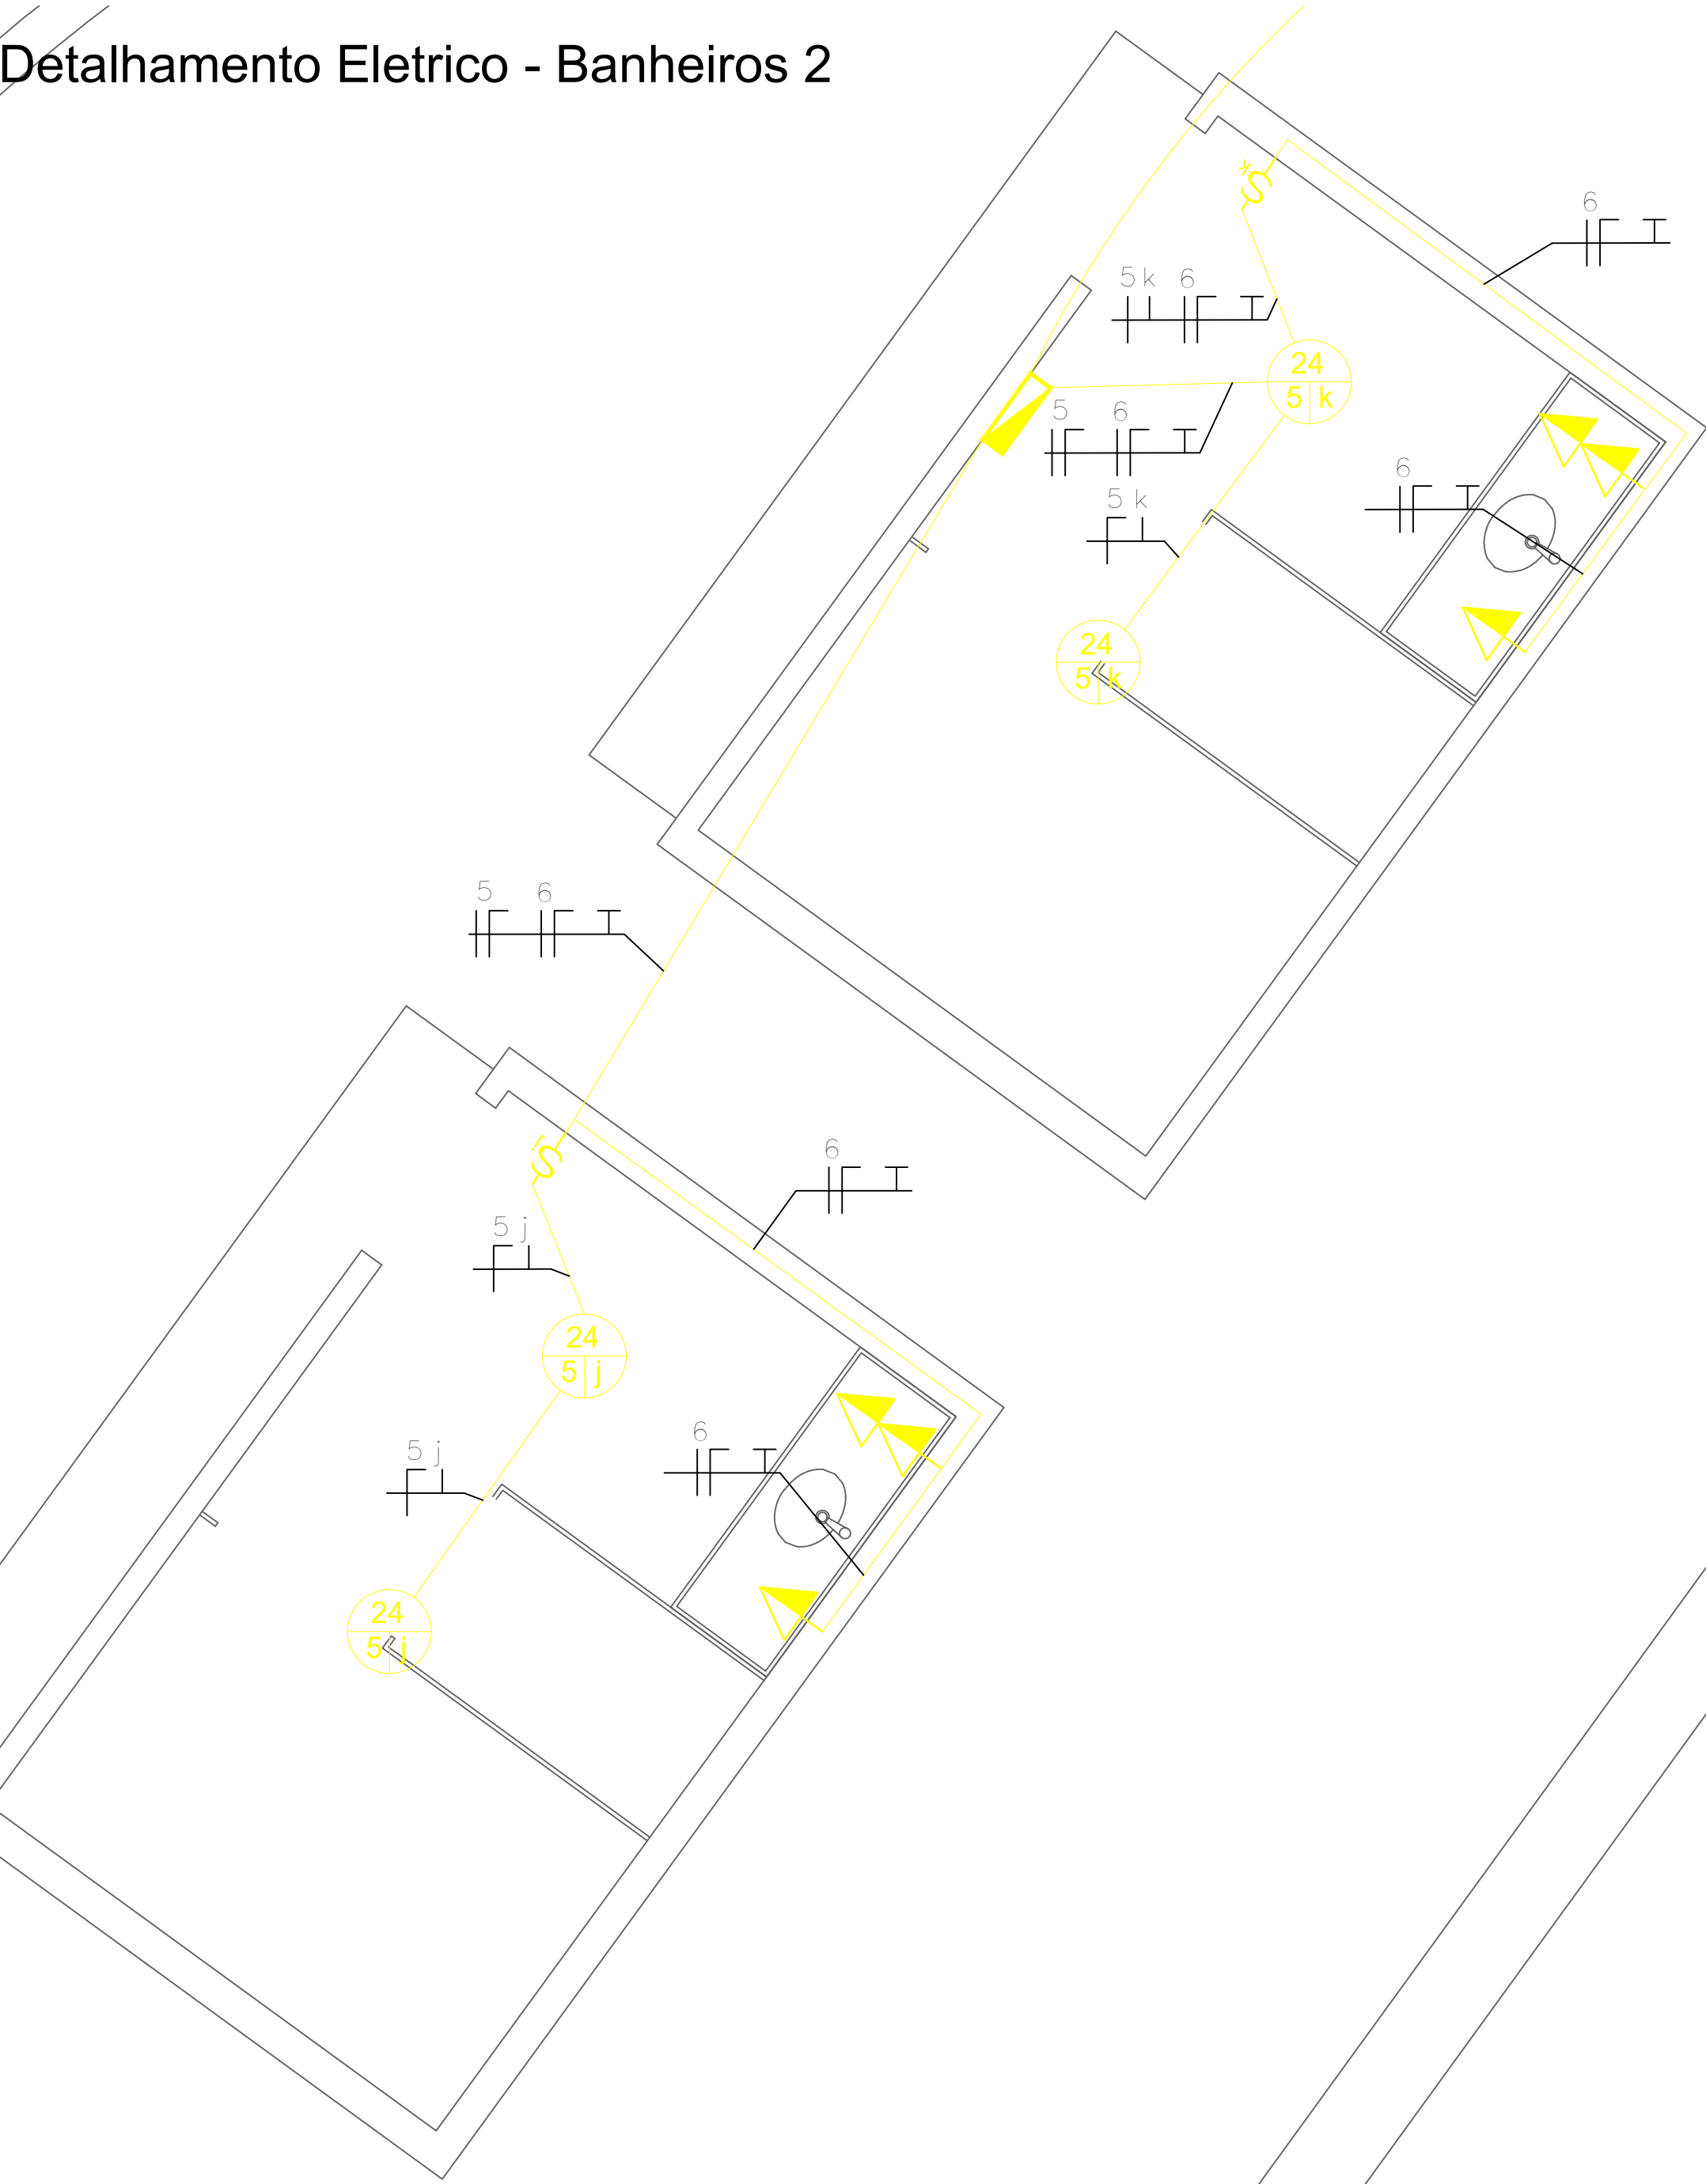

Detalhamento Eletrico - Quiosque 2

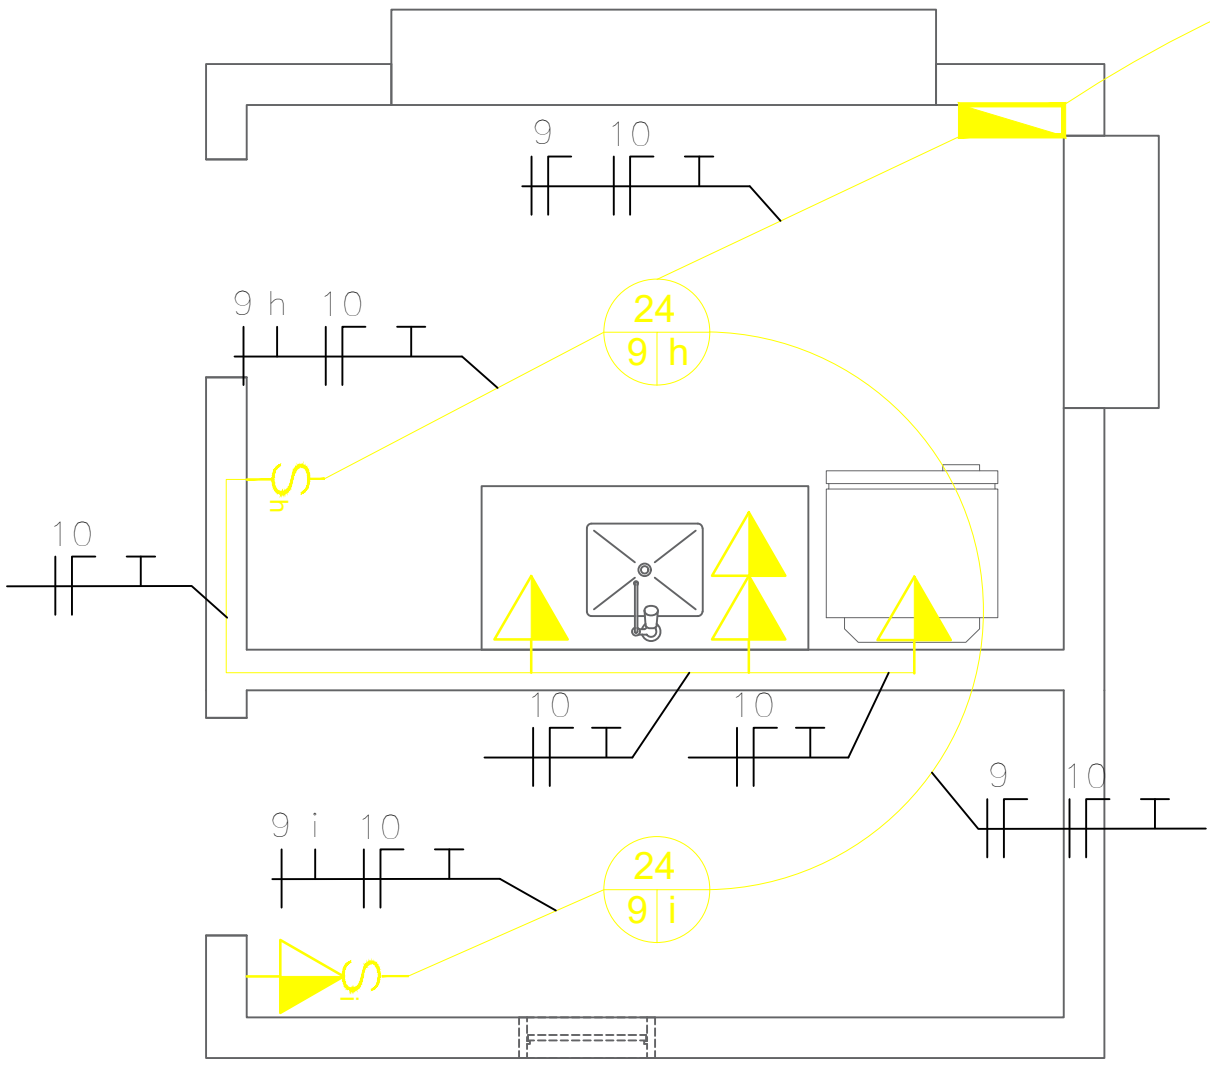

Detalhamento Eletrico - Guarita

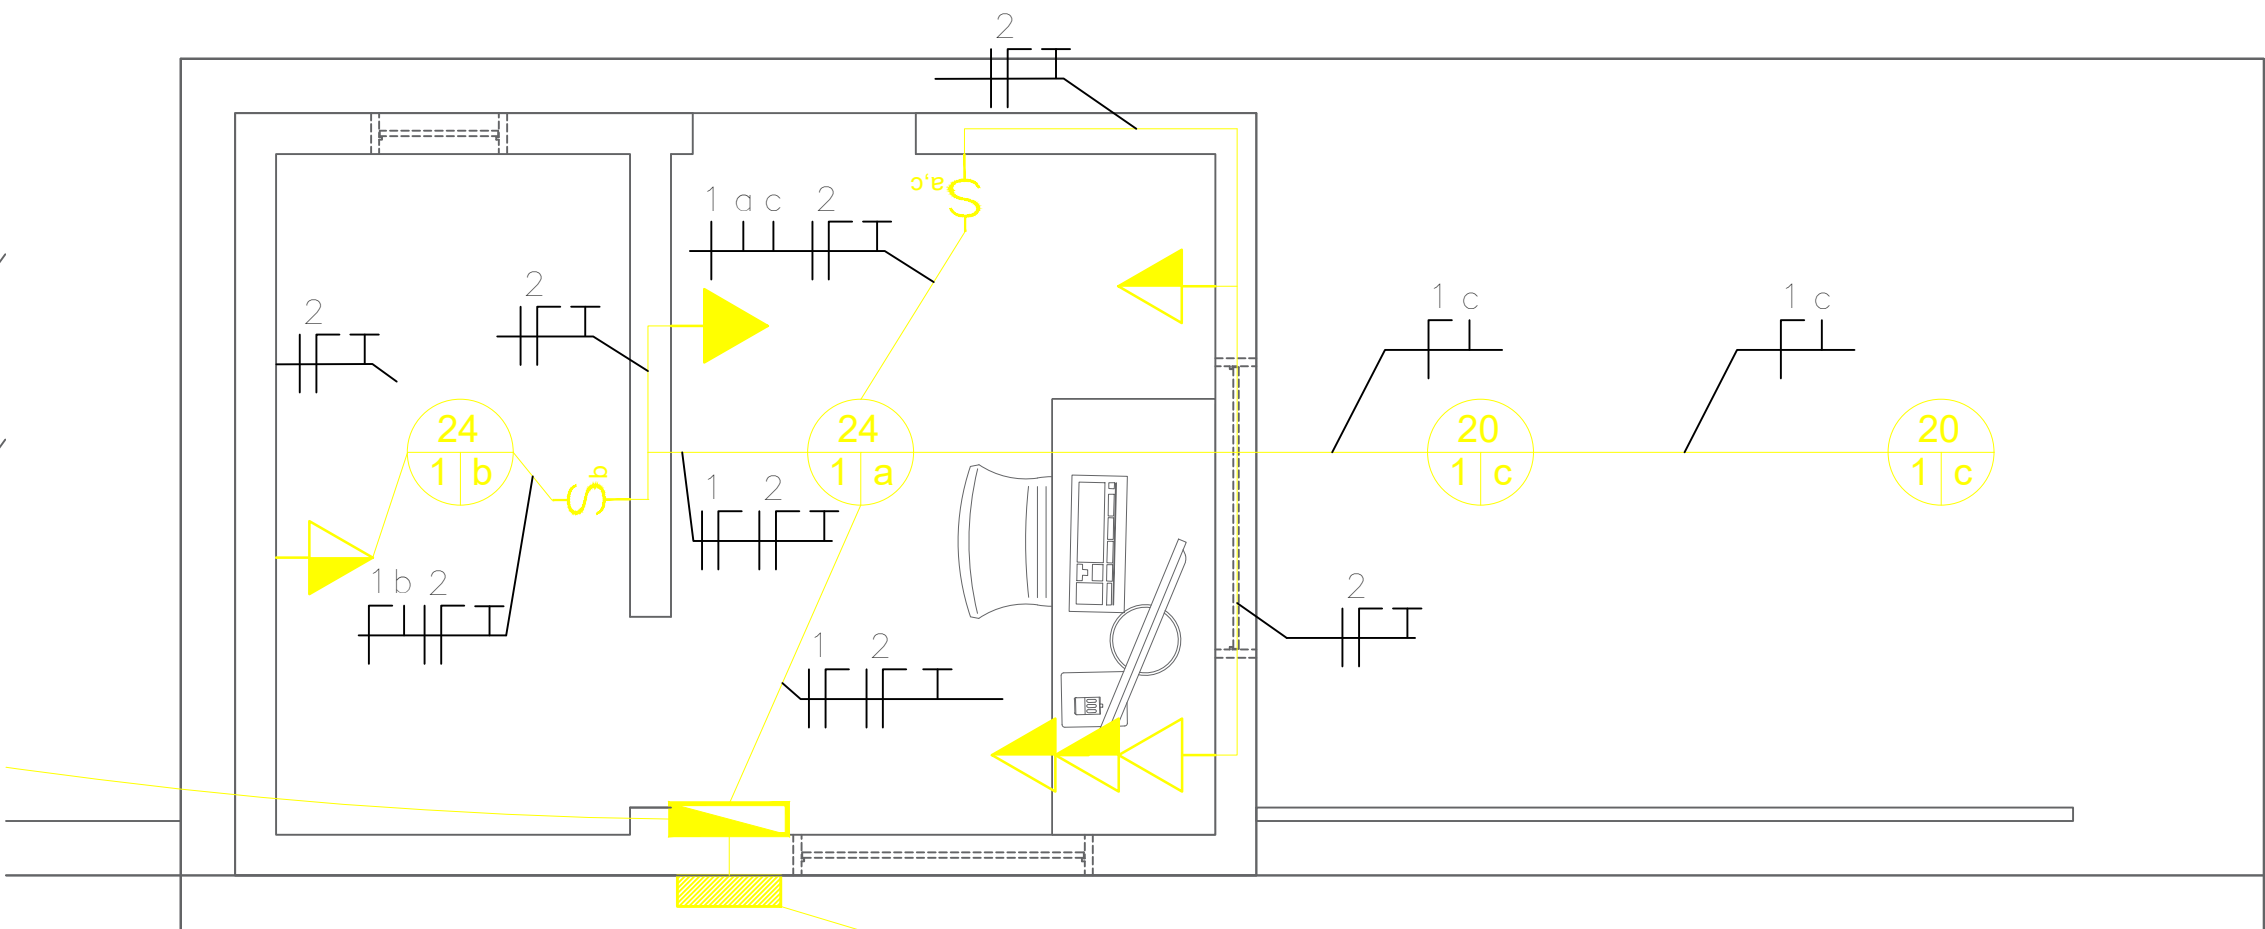

Projeto:

Projeto de Urbanismo Vila Olimpica

Desenhos:

PLANTA BAIXA COM DETALHAMENTO DOS PONTOS ELÉTRICOS

Ordem	Descrição	QUADRO DE CARGAS - GERAL										Pot (VA)	Pot (VA)	IP	Tensão (V)	Corrente (A)	Qual. (mm²)	Proteção (A)
		10	20	30	40	50	60	70	80	90	100							
1	Iluminação Geral	10	20	30	40	50	60	70	80	90	100	100	100	1	220	0,45	1,5	10
2	Tomadas Gerais	10	20	30	40	50	60	70	80	90	100	100	100	1	220	0,45	1,5	10
3	Iluminação Banheiro 1	10	20	30	40	50	60	70	80	90	100	100	100	1	220	0,45	1,5	10
4	Tomadas Banheiro 1	10	20	30	40	50	60	70	80	90	100	100	100	1	220	0,45	1,5	10
5	Iluminação Banheiro 2	10	20	30	40	50	60	70	80	90	100	100	100	1	220	0,45	1,5	10
6	Tomadas Banheiro 2	10	20	30	40	50	60	70	80	90	100	100	100	1	220	0,45	1,5	10
7	Iluminação Quiosque 1	10	20	30	40	50	60	70	80	90	100	100	100	1	220	0,45	1,5	10
8	Tomadas Quiosque 1	10	20	30	40	50	60	70	80	90	100	100	100	1	220	0,45	1,5	10
9	Iluminação Quiosque 2	10	20	30	40	50	60	70	80	90	100	100	100	1	220	0,45	1,5	10
10	Tomadas Quiosque 2	10	20	30	40	50	60	70	80	90	100	100	100	1	220	0,45	1,5	10
11	Iluminação Pontos - Torres	10	20	30	40	50	60	70	80	90	100	100	100	1	220	0,45	1,5	10
12	Iluminação Pontos - Quadra 1 Local	10	20	30	40	50	60	70	80	90	100	100	100	1	220	0,45	1,5	10
13	Iluminação Pontos - Quadra 2 Local	10	20	30	40	50	60	70	80	90	100	100	100	1	220	0,45	1,5	10
14	Iluminação Pontos - Quadra 3 Local	10	20	30	40	50	60	70	80	90	100	100	100	1	220	0,45	1,5	10
TOTAL		10	20	30	40	50	60	70	80	90	100	100	100	1	220	0,45	1,5	10

DIAGRAMA UNIFILAR

Observações:

- Conferir todas as medidas em obra antes da execução dos serviços.
- Não executar alterações sem autorização prévia do responsável técnico.
- Qualquer divergência entre projeto e condições de campo deverá ser comunicada ao responsável técnico para análise e aprovação.
- Todas as instalações deverão ser executadas por mão de obra qualificada, seguindo as normas técnicas vigentes e as recomendações dos fabricantes dos materiais empregados.
- O dimensionamento e posicionamentos indicados em projeto prevalecem sobre quaisquer informações complementares aqui descritas.

Esta prancha apresenta os detalhes das instalações elétricas devendo sua execução seguir rigorosamente as dimensões, níveis, materiais e especificações indicados em projeto.

- A alimentação da edificação será realizada através do quadro geral de distribuição (QDG), conforme indicado em projeto.
- Todos os circuitos deverão ser identificados e distribuídos conforme o diagrama unifilar e o quadro de cargas apresentados em projeto.
- As emendas de condutores somente poderão ser executadas no interior de caixas de passagem, caixas de derivação ou quadros elétricos.
- Todos os condutores deverão possuir isolamento adequado à tensão de operação e serem instalados sem danos mecânicos.
- Os condutores deverão possuir seção nominal conforme especificado em projeto.
- Os circuitos de iluminação, tomadas de uso geral (TUG), tomadas de uso específico (TUE) e equipamentos deverão respeitar as bitolas indicadas no quadro de cargas.
- Os eletrodutos deverão possuir diâmetros compatíveis com a quantidade e seção dos condutores instalados.
- Não será permitida a ocupação excessiva dos eletrodutos, devendo ser respeitadas as taxas máximas de ocupação previstas em norma.
- O quadro de distribuição deverá possuir barramentos independentes para neutro e aterramento.
- Todos os dispositivos de proteção deverão ser instalados conforme especificado em projeto.
- Os circuitos deverão ser protegidos por disjuntores termomagnéticos compatíveis com suas respectivas cargas.
- Quando especificado em projeto, deverão ser instalados dispositivos DR e DPS.
- Os quadros de distribuição deverão ser instalados nos locais indicados em projeto, garantindo fácil acesso para operação e manutenção.
- Não executar alterações sem autorização prévia do responsável técnico.
- Qualquer divergência entre projeto e condições de campo deverá ser comunicada ao responsável técnico para análise e aprovação.

Projetista:

Fernando Matias Mamede

RESPONSÁVEL TÉCNICO

Fernando Matias Mamede

Engenheiro Civil

Crea: 162056275-8

Proprietário:

Prefeitura Municipal de Coremas

PROPRIETÁRIO(A)

Endereço/Obra:

Rua Francisco Raimundo de Andrade, DNOCS, Coremas - PB, 58770-000

ÁREAS

m²

Área do Terreno

10.733,41

Estacionamento

519,11

Calçada


249,64

Área verde

4.281,11

Prancha:


09/14

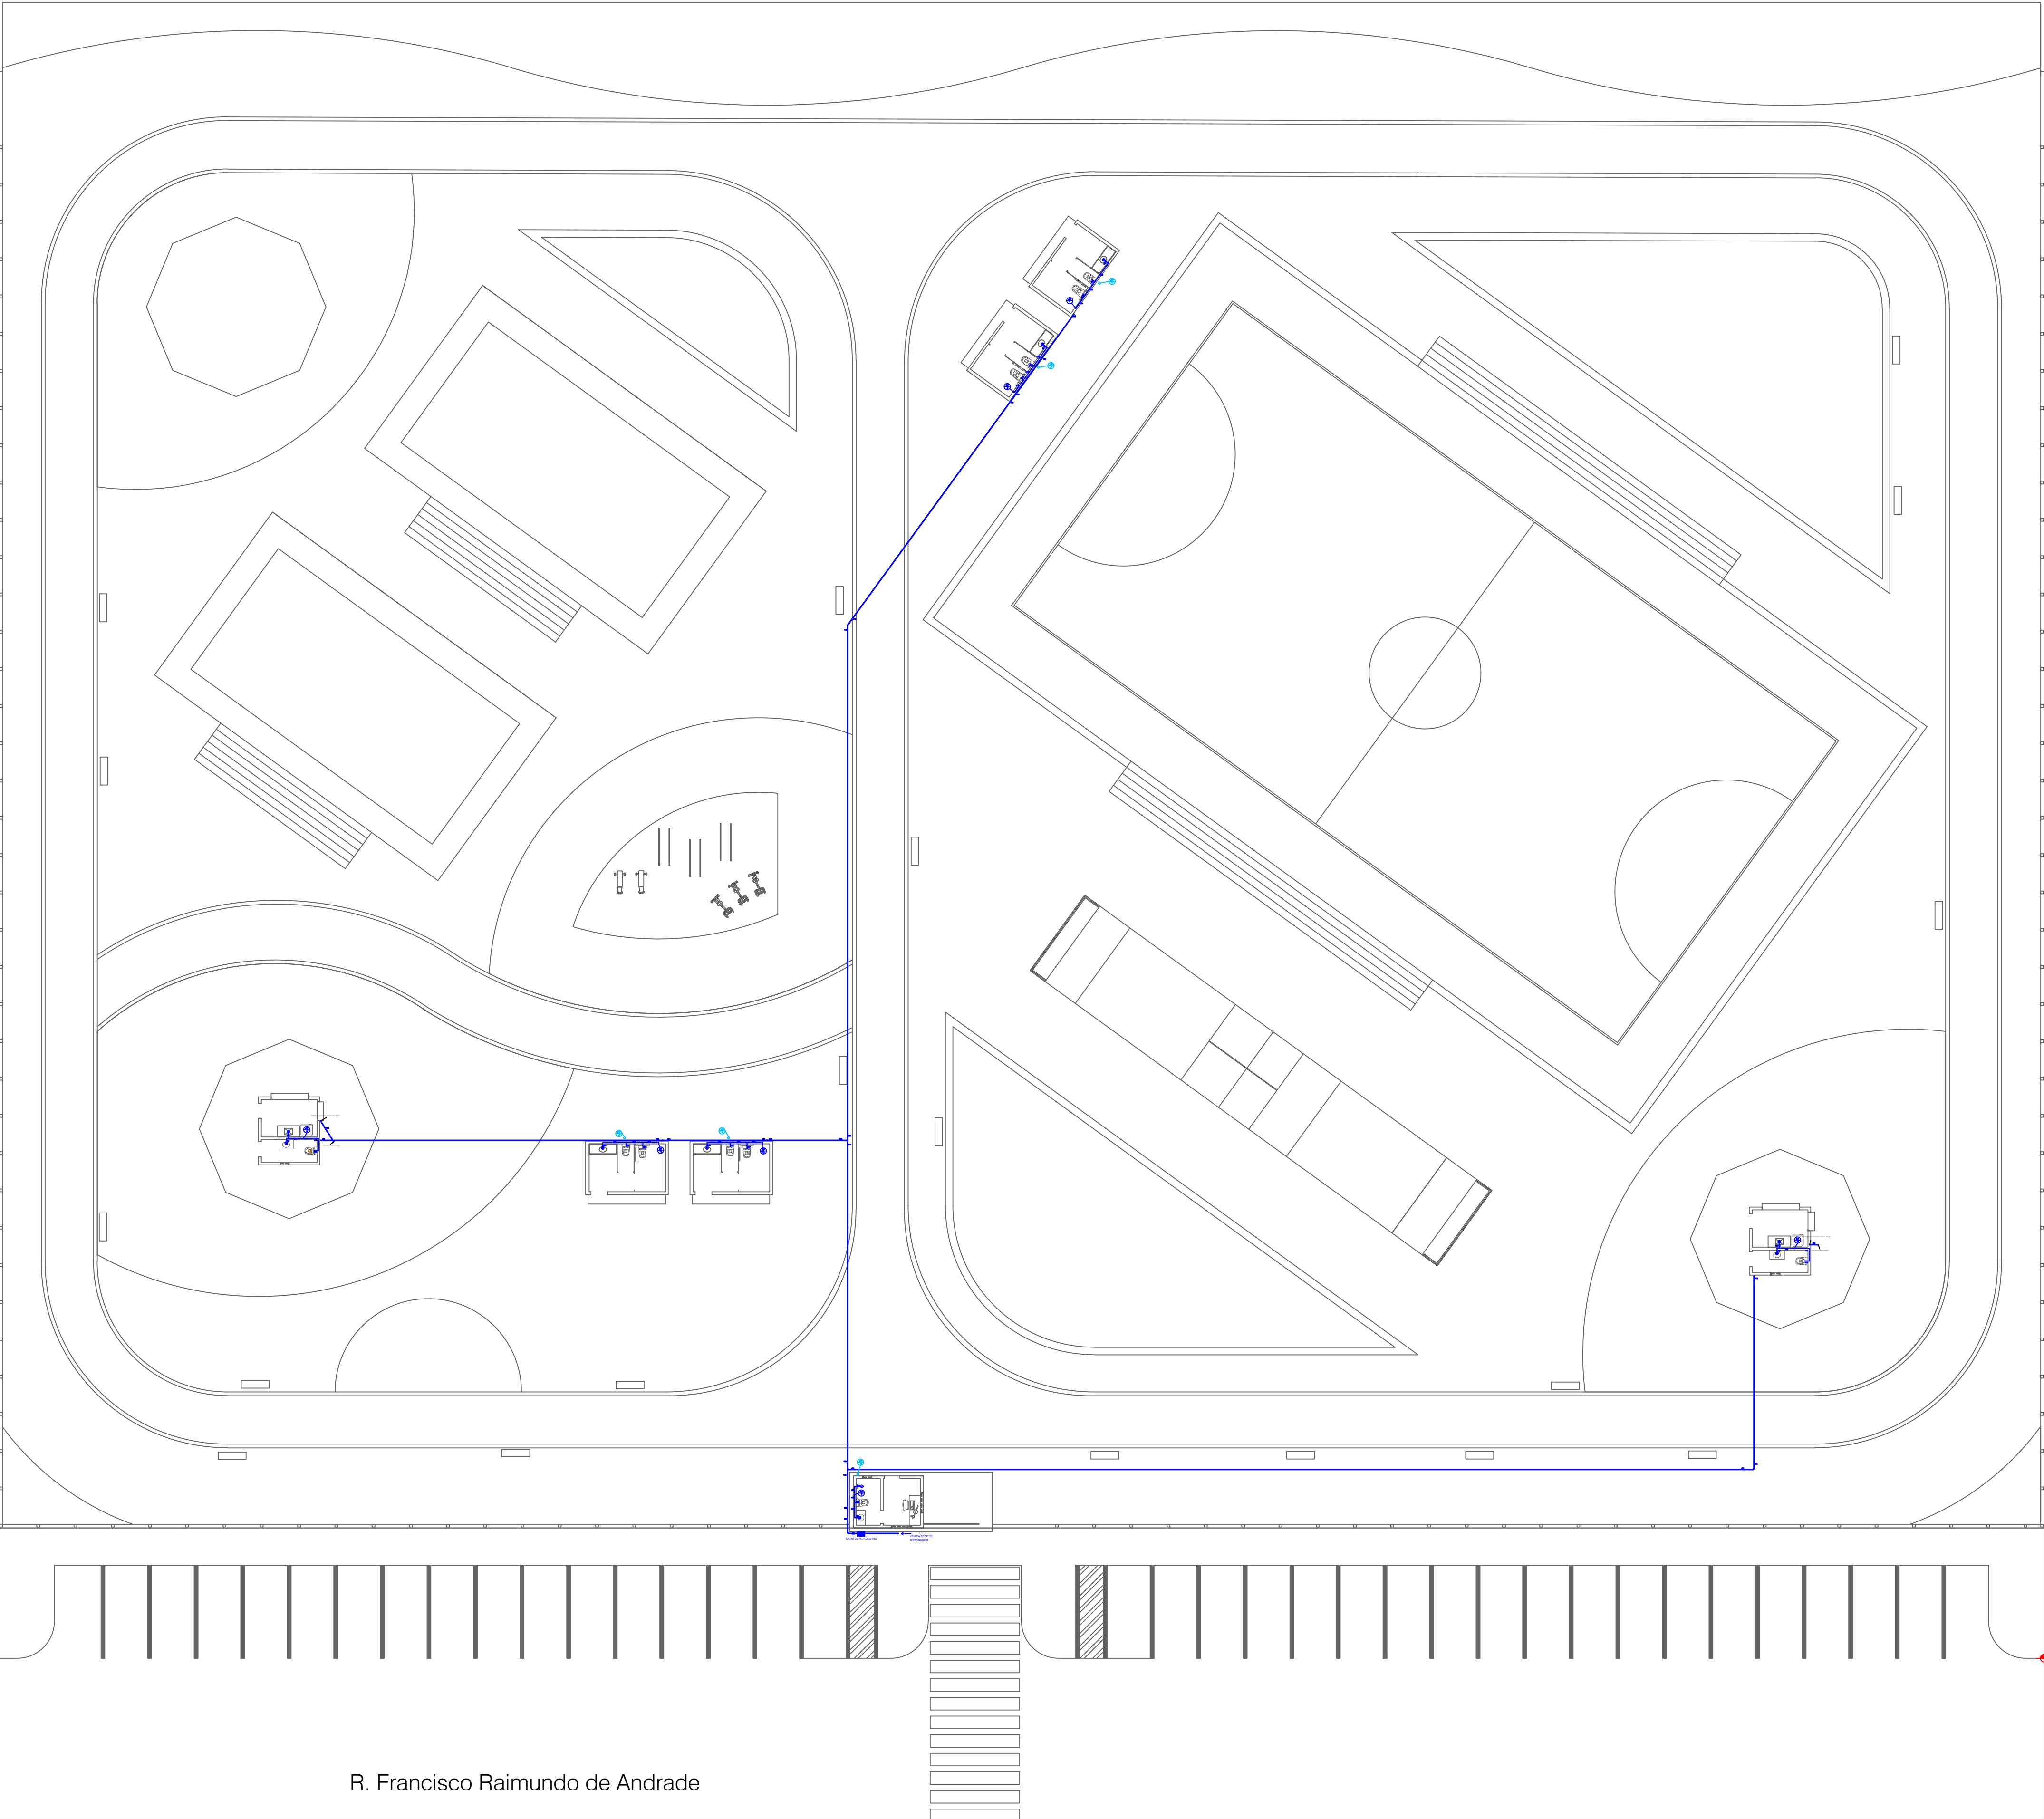

R. Francisco Raimundo de Andrade

PLANTA GERAL - COBERTA
COMPLEXO ESPORTIVO

ESC: 1/200

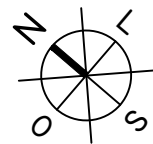

Projeto:

Projeto de Urbanismo Vila Olimpica

Desenhos:

PLANTA BAIXA COM DETALHAMENTO DOS PONTOS DE ÁGUAS FRIAS E PLUVIAIS

Observações:

- Conferir todas as medidas em obra antes da execução dos serviços.
- Não executar alterações sem autorização prévia do responsável técnico.
- Qualquer divergência entre projeto e condições de campo deverá ser comunicada ao responsável técnico para análise e aprovação.
- Todas as instalações deverão ser executadas por mão de obra qualificada, seguindo as normas técnicas vigentes e as recomendações dos fabricantes dos materiais empregados.
- O dimensionamento e posicionamentos indicados em projeto prevalecem sobre quaisquer informações complementares aqui descritas.

Esta prancha apresenta os detalhes das instalações de águas frias devendo sua execução seguir rigorosamente as dimensões, níveis, materiais e especificações indicados em projeto.

- Tubulação de abastecimento e distribuição principal: DN 32 mm.
- Tubulações de alimentação dos pontos de consumo: DN 25 mm.
- O reservatório superior será composto por:

Tubulação de alimentação controlada por torneira de boia;

Tubulação de abastecimento da rede de distribuição;

Tubulação de ventilação prolongada acima do nível máximo de água do reservatório;

Tubulação de limpeza (dreno) para esgotamento total do reservatório;

Extravasor (ladrão) interligado ao dreno, destinado à descarga do excedente de água em caso de falha do sistema de controle de nível.

• Todas as tubulações deverão ser executadas conforme os diâmetros, cotas e posicionamentos indicados em projeto.

• Deverão ser realizados testes de estanqueidade antes do fechamento de paredes, pisos e forros.

As instalações de águas pluviais foram dimensionadas e deverão ser executadas conforme as prescrições da ABNT NBR 10844.

- As águas provenientes da cobertura serão captadas por calhas e conduzidas através de condutores verticais e horizontais até o ponto de lançamento previsto em projeto.
- O extravasor do reservatório superior será direcionado para a rede de drenagem pluvial.
- As tubulações deverão obedecer aos diâmetros e declividades especificados em projeto.
- Deverá ser garantido o livre escoamento das águas pluviais, evitando acúmulo ou retorno de fluxo.
- As calhas, condutores e dispositivos de captação deverão permanecer livres de obstruções.

Projetista:

Fernando Matias Mamede

RESPONSÁVEL TÉCNICO

Fernando Matias Mamede

Engenheiro Civil

Crea: 162056275-8

Proprietário:

Prefeitura Municipal de Coremas

PROPRIETÁRIO(A)

Endereço/Obra:


Rua Francisco Raimundo de Andrade, DNOCS, Coremas - PB, 58770-000

ÁREAS	m²
Área do Terreno	10.733,41
Estacionamento	519,11
Calçada	249,64
Área verde	4.281,11

Prancha:

10/14


Detalhamento Hidráulico - Banheiros 1

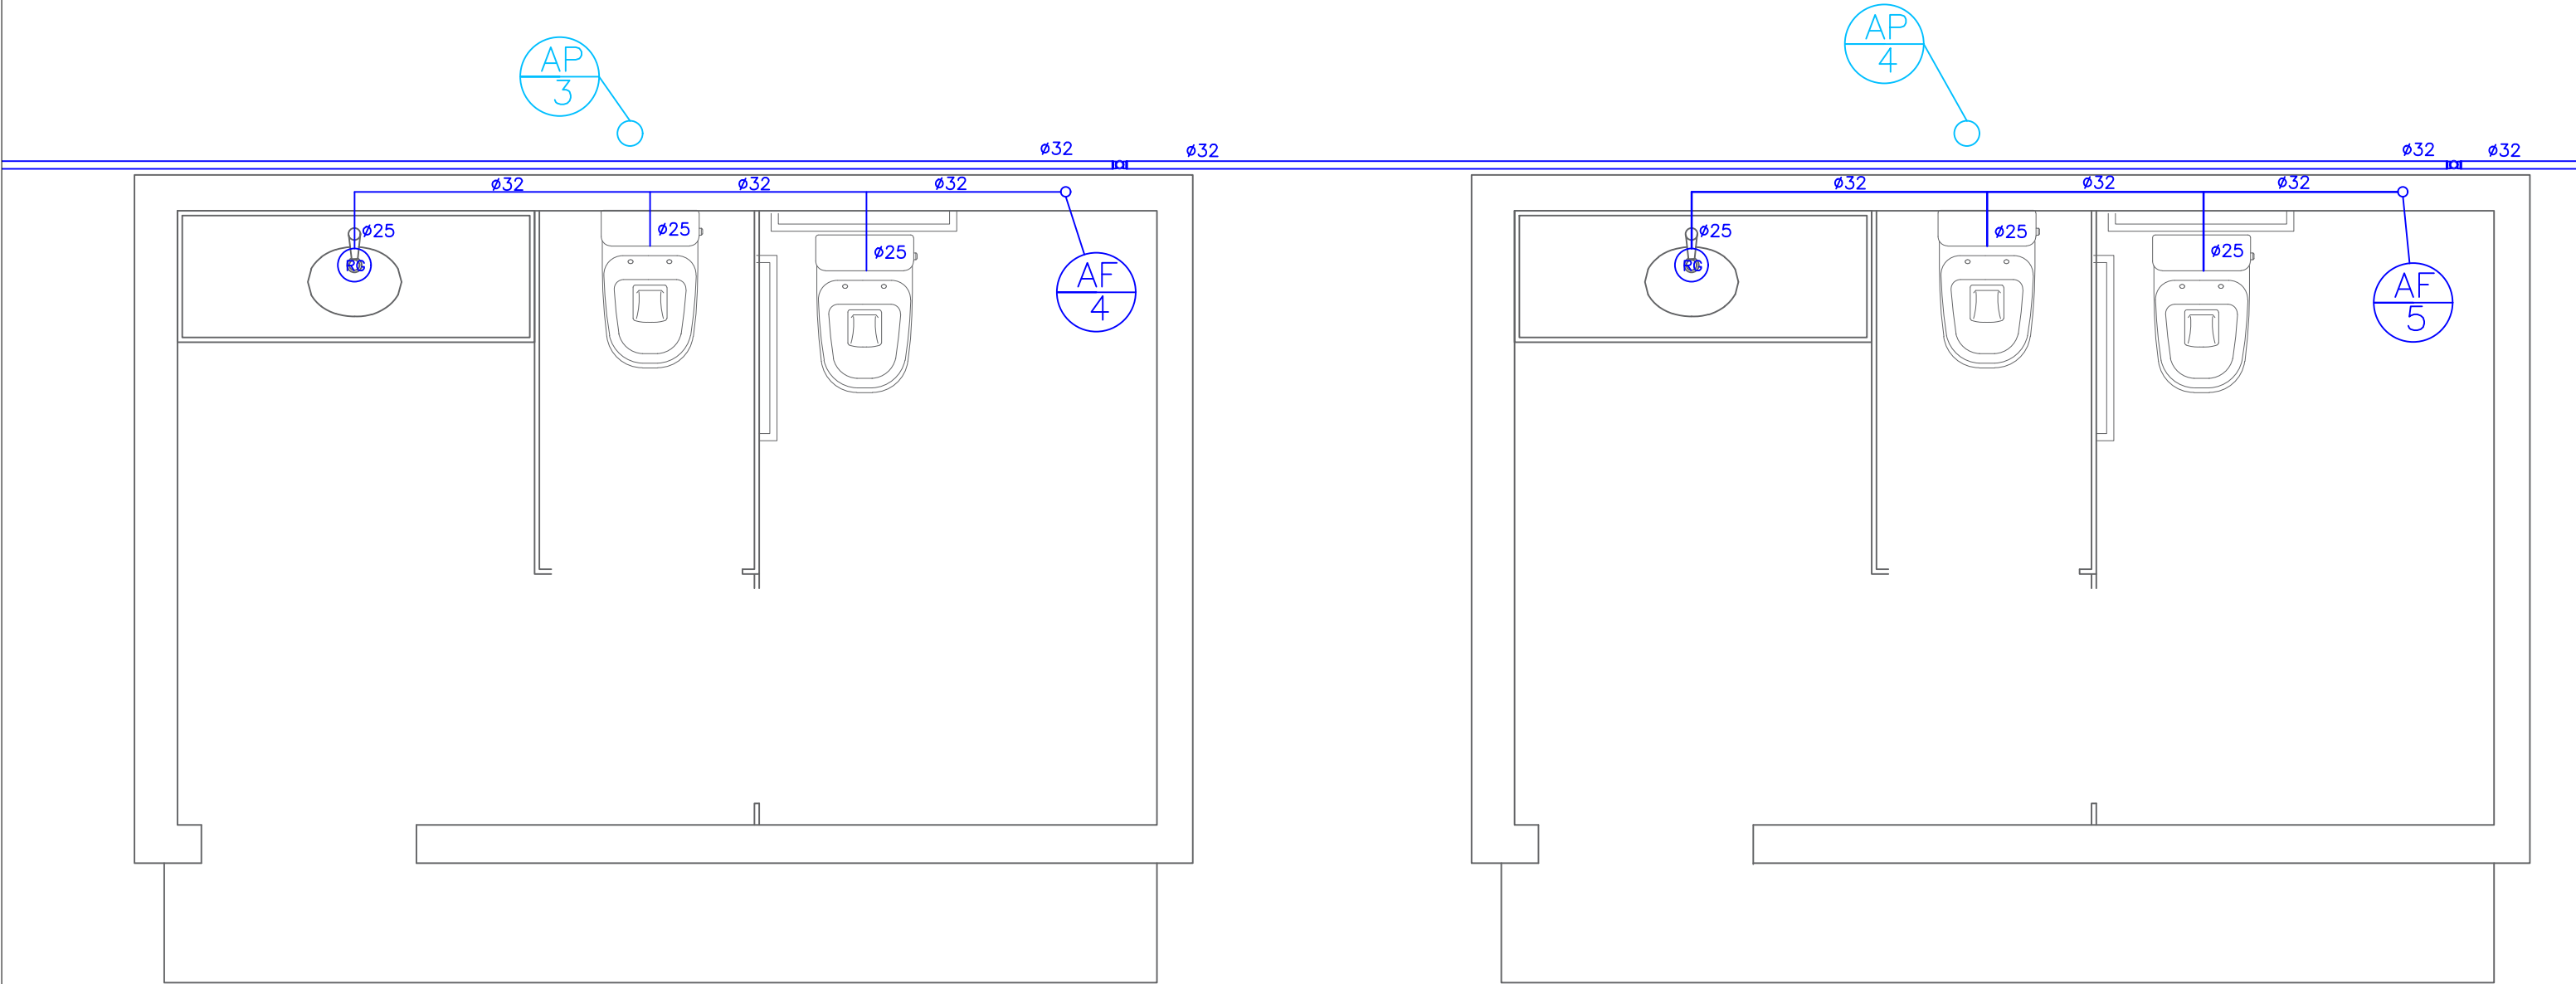


Detalhamento Hidráulico - Banheiros 2




Detalhamento Hidráulico - Quiosque 1

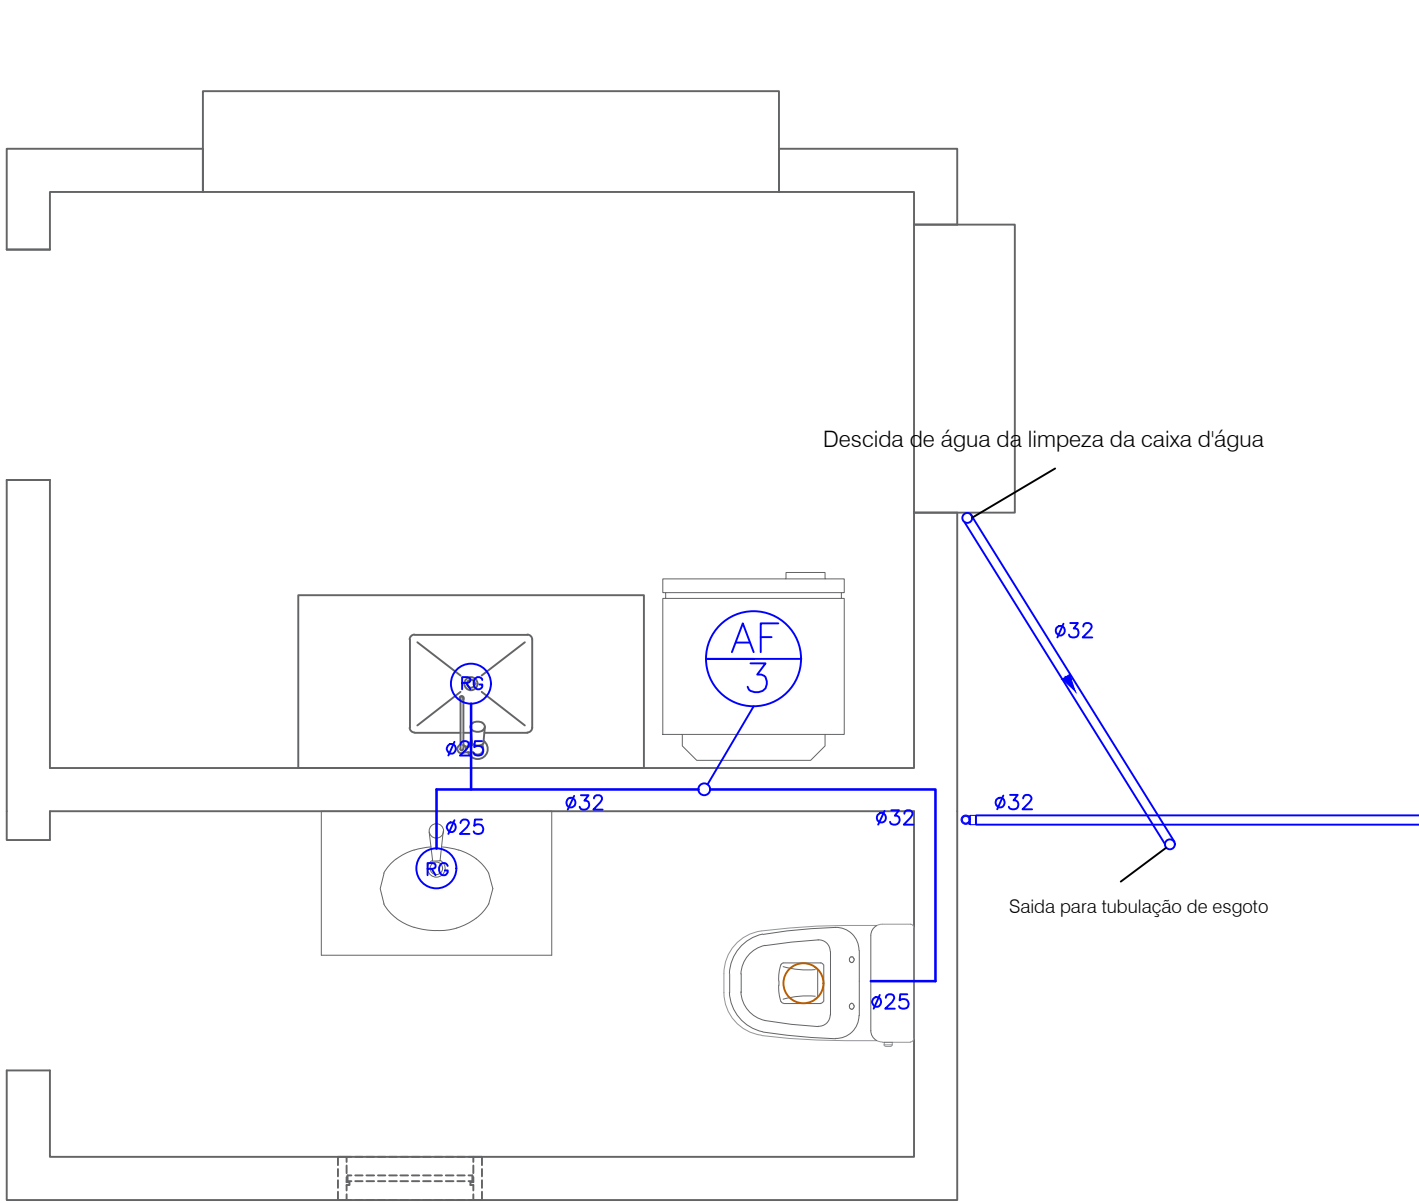

Detalhamento Hidráulico - Quiosque 2

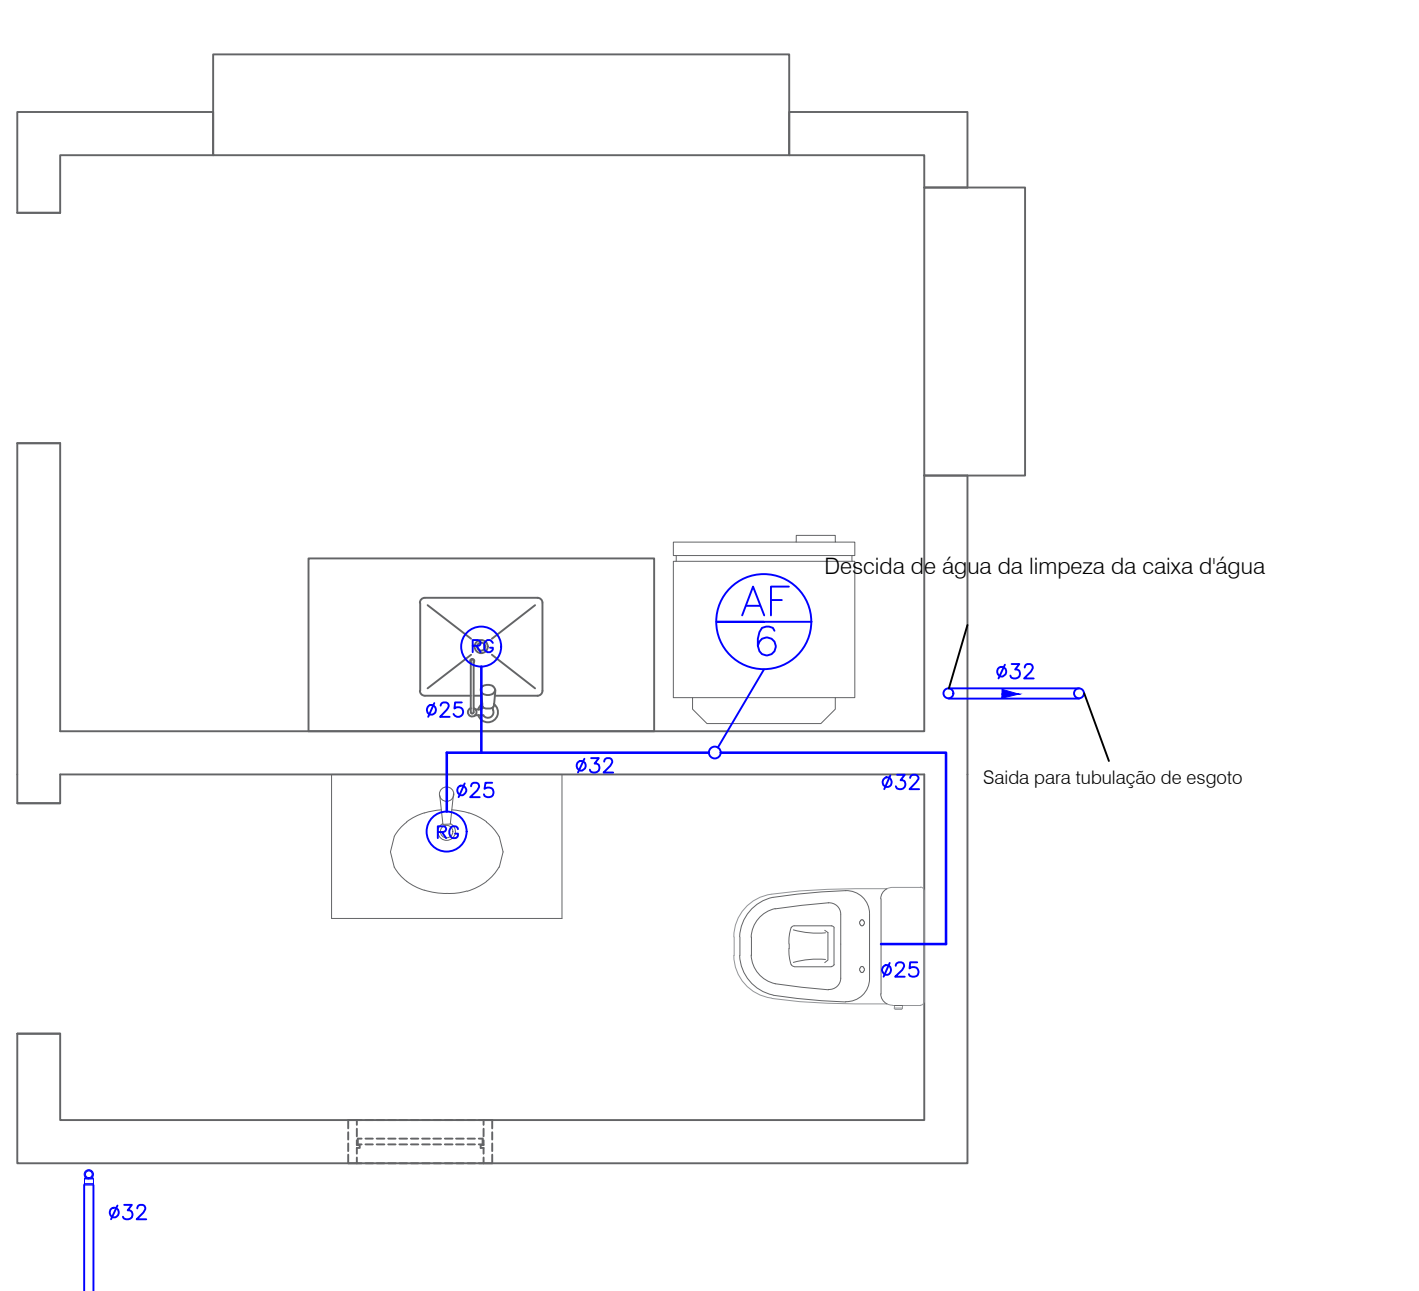

Detalhamento Hidráulico - Guarita

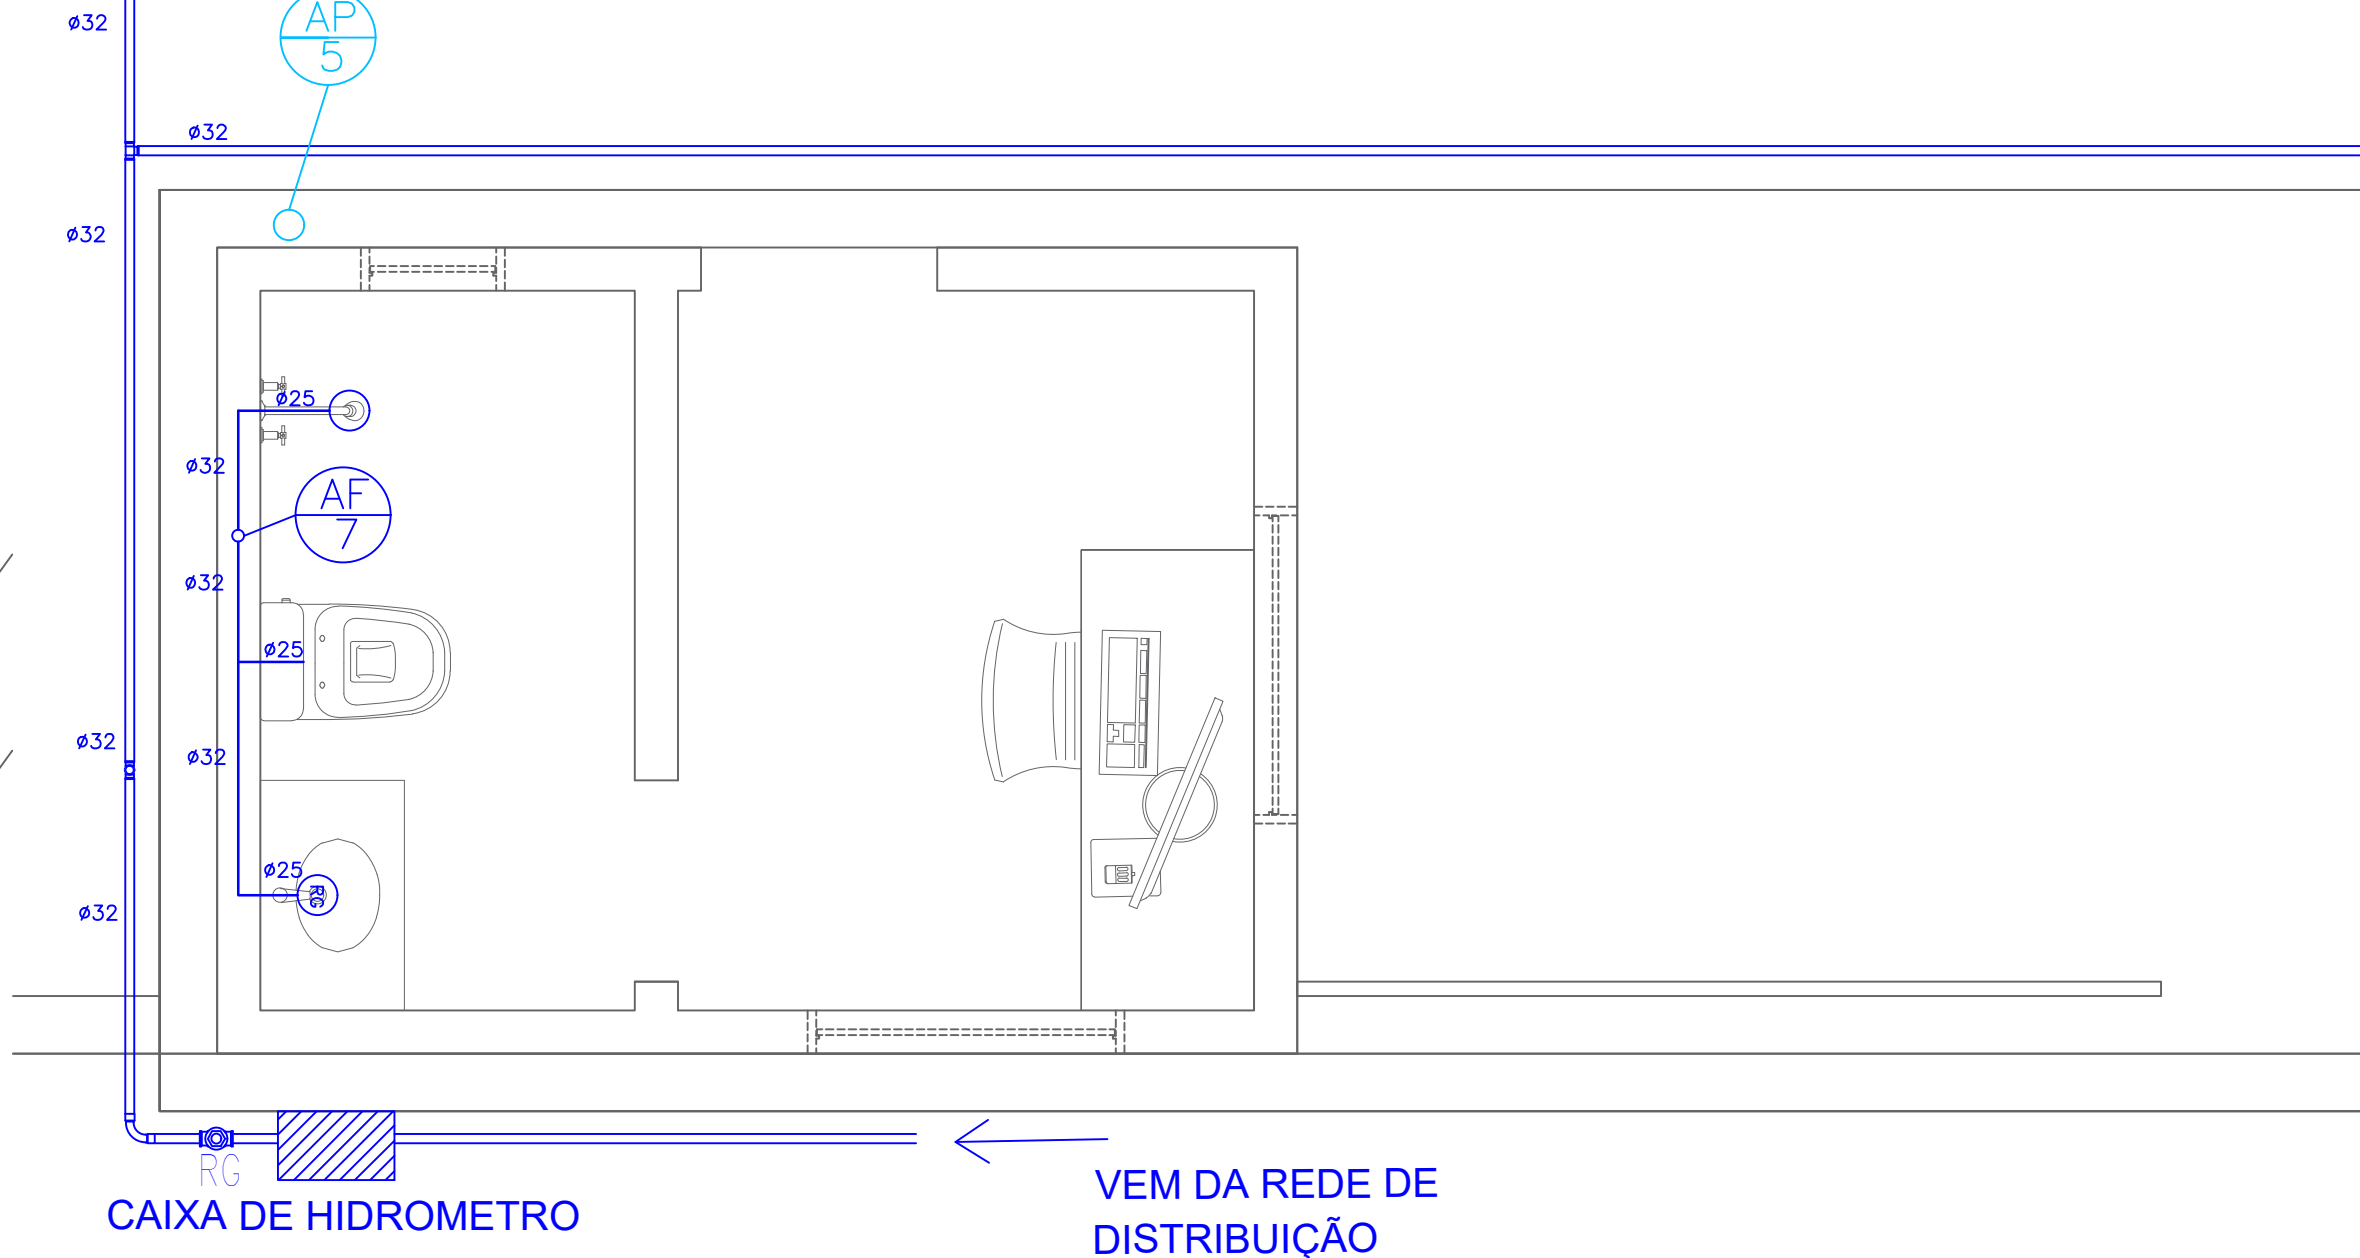

Projeto:

Projeto de Urbanismo Vila Olimpica

Desenhos:

PLANTA BAIXA COM DETALHAMENTO DOS PONTOS DE ÁGUAS FRIAS E PLUVIAIS

Observações:

- Conferir todas as medidas em obra antes da execução dos serviços.
- Não executar alterações sem autorização prévia do responsável técnico.
- Qualquer divergência entre projeto e condições de campo deverá ser comunicada ao responsável técnico para análise e aprovação.
- Todas as instalações deverão ser executadas por mão de obra qualificada, seguindo as normas técnicas vigentes e as recomendações dos fabricantes dos materiais empregados.
- O dimensionamento e posicionamentos indicados em projeto prevalecem sobre quaisquer informações complementares aqui descritas.

Esta prancha apresenta os detalhes das instalações de águas frias devendo sua execução seguir rigorosamente as dimensões, níveis, materiais e especificações indicados em projeto.

- Tubulação de abastecimento e distribuição principal: DN 32 mm.
- Tubulações de alimentação dos pontos de consumo: DN 25 mm.
- O reservatório superior será composto por:

Tubulação de alimentação controlada por torneira de boia;

Tubulação de abastecimento da rede de distribuição;

Tubulação de ventilação prolongada acima do nível máximo de água do reservatório;

Tubulação de limpeza (dreno) para esgotamento total do reservatório;

Extravasor (ladrão) interligado ao dreno, destinado à descarga do excedente de água em caso de falha do sistema de controle de nível.

- Todas as tubulações deverão ser executadas conforme os diâmetros, cotas e posicionamentos indicados em projeto.
- Deverão ser realizados testes de estanqueidade antes do fechamento de paredes, pisos e forros.

As instalações de águas pluviais foram dimensionadas e deverão ser executadas conforme as prescrições da ABNT NBR 10844.

- As águas provenientes da cobertura serão captadas por calhas e conduzidas através de condutores verticais e horizontais até o ponto de lançamento previsto em projeto.
- O extravasor do reservatório superior será direcionado para a rede de drenagem pluvial.
- As tubulações deverão obedecer aos diâmetros e declividades especificados em projeto.
- Deverá ser garantido o livre escoamento das águas pluviais, evitando acúmulo ou retorno de fluxo.
- As calhas, condutores e dispositivos de captação deverão permanecer livres de obstruções.

Projeta:

Fernando Matias Mamede

RESPONSÁVEL TÉCNICO

Fernando Matias Mamede

Engenheiro Civil

Crea: 162056275-8

Proprietário:

Prefeitura Municipal de Coremas

PROPRIETÁRIO(A)

Endereço/Obra:

Rua Francisco Raimundo de Andrade, DNOCS, Coremas - PB, 58770-000

ÁREAS

m²

Área do Terreno

10.733,41

Estacionamento

519,11

Calçada

249,64


Área verde

4.281,11


Prancha:

11/14


Detalhamento Hidráulico - Banheiros 1

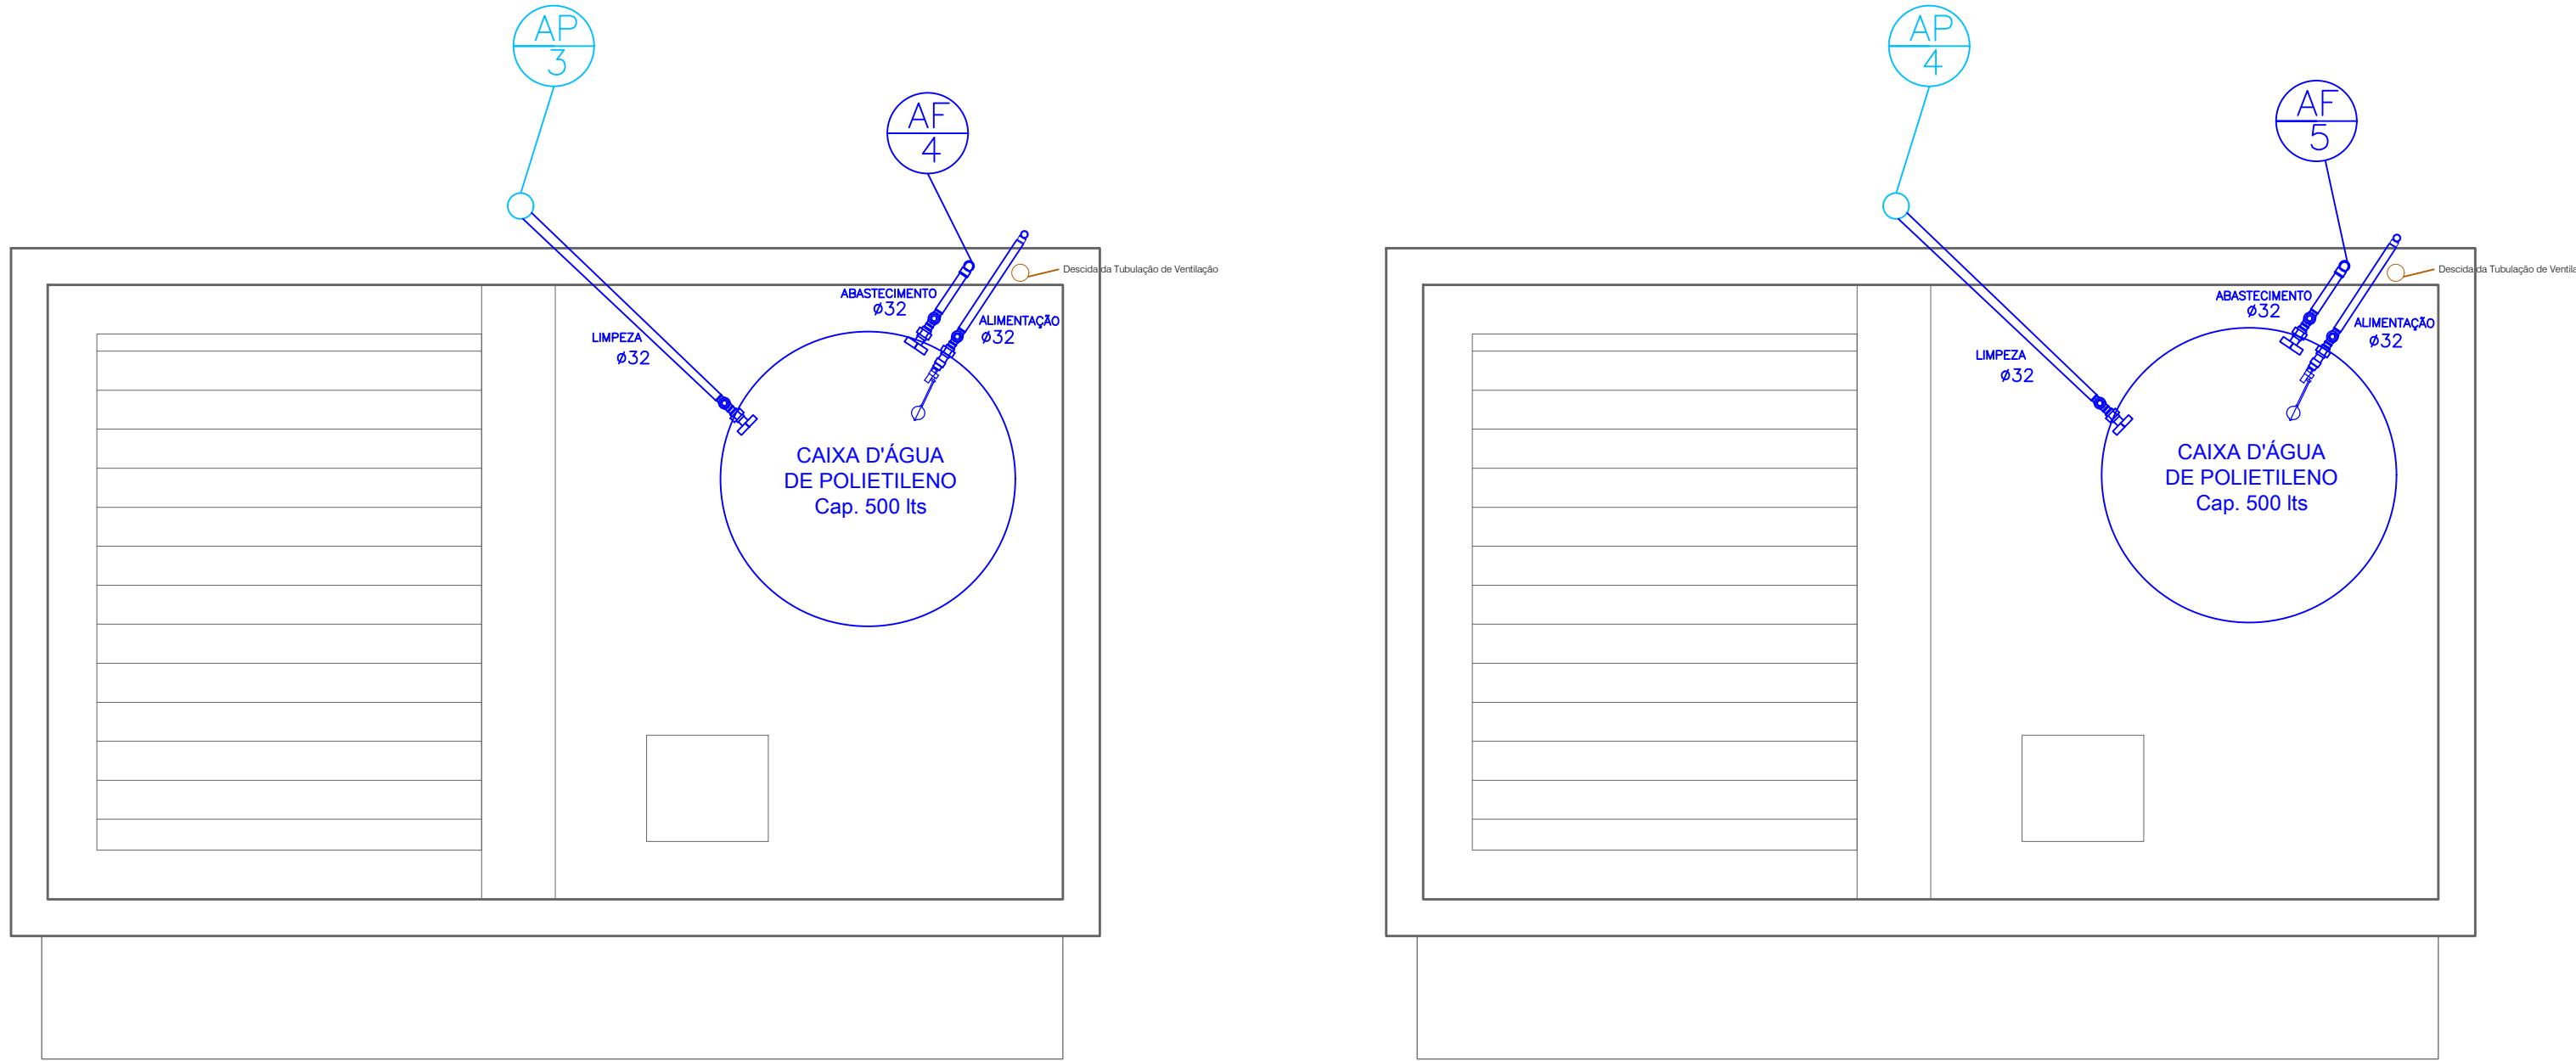


Detalhamento Hidráulico - Banheiros 2

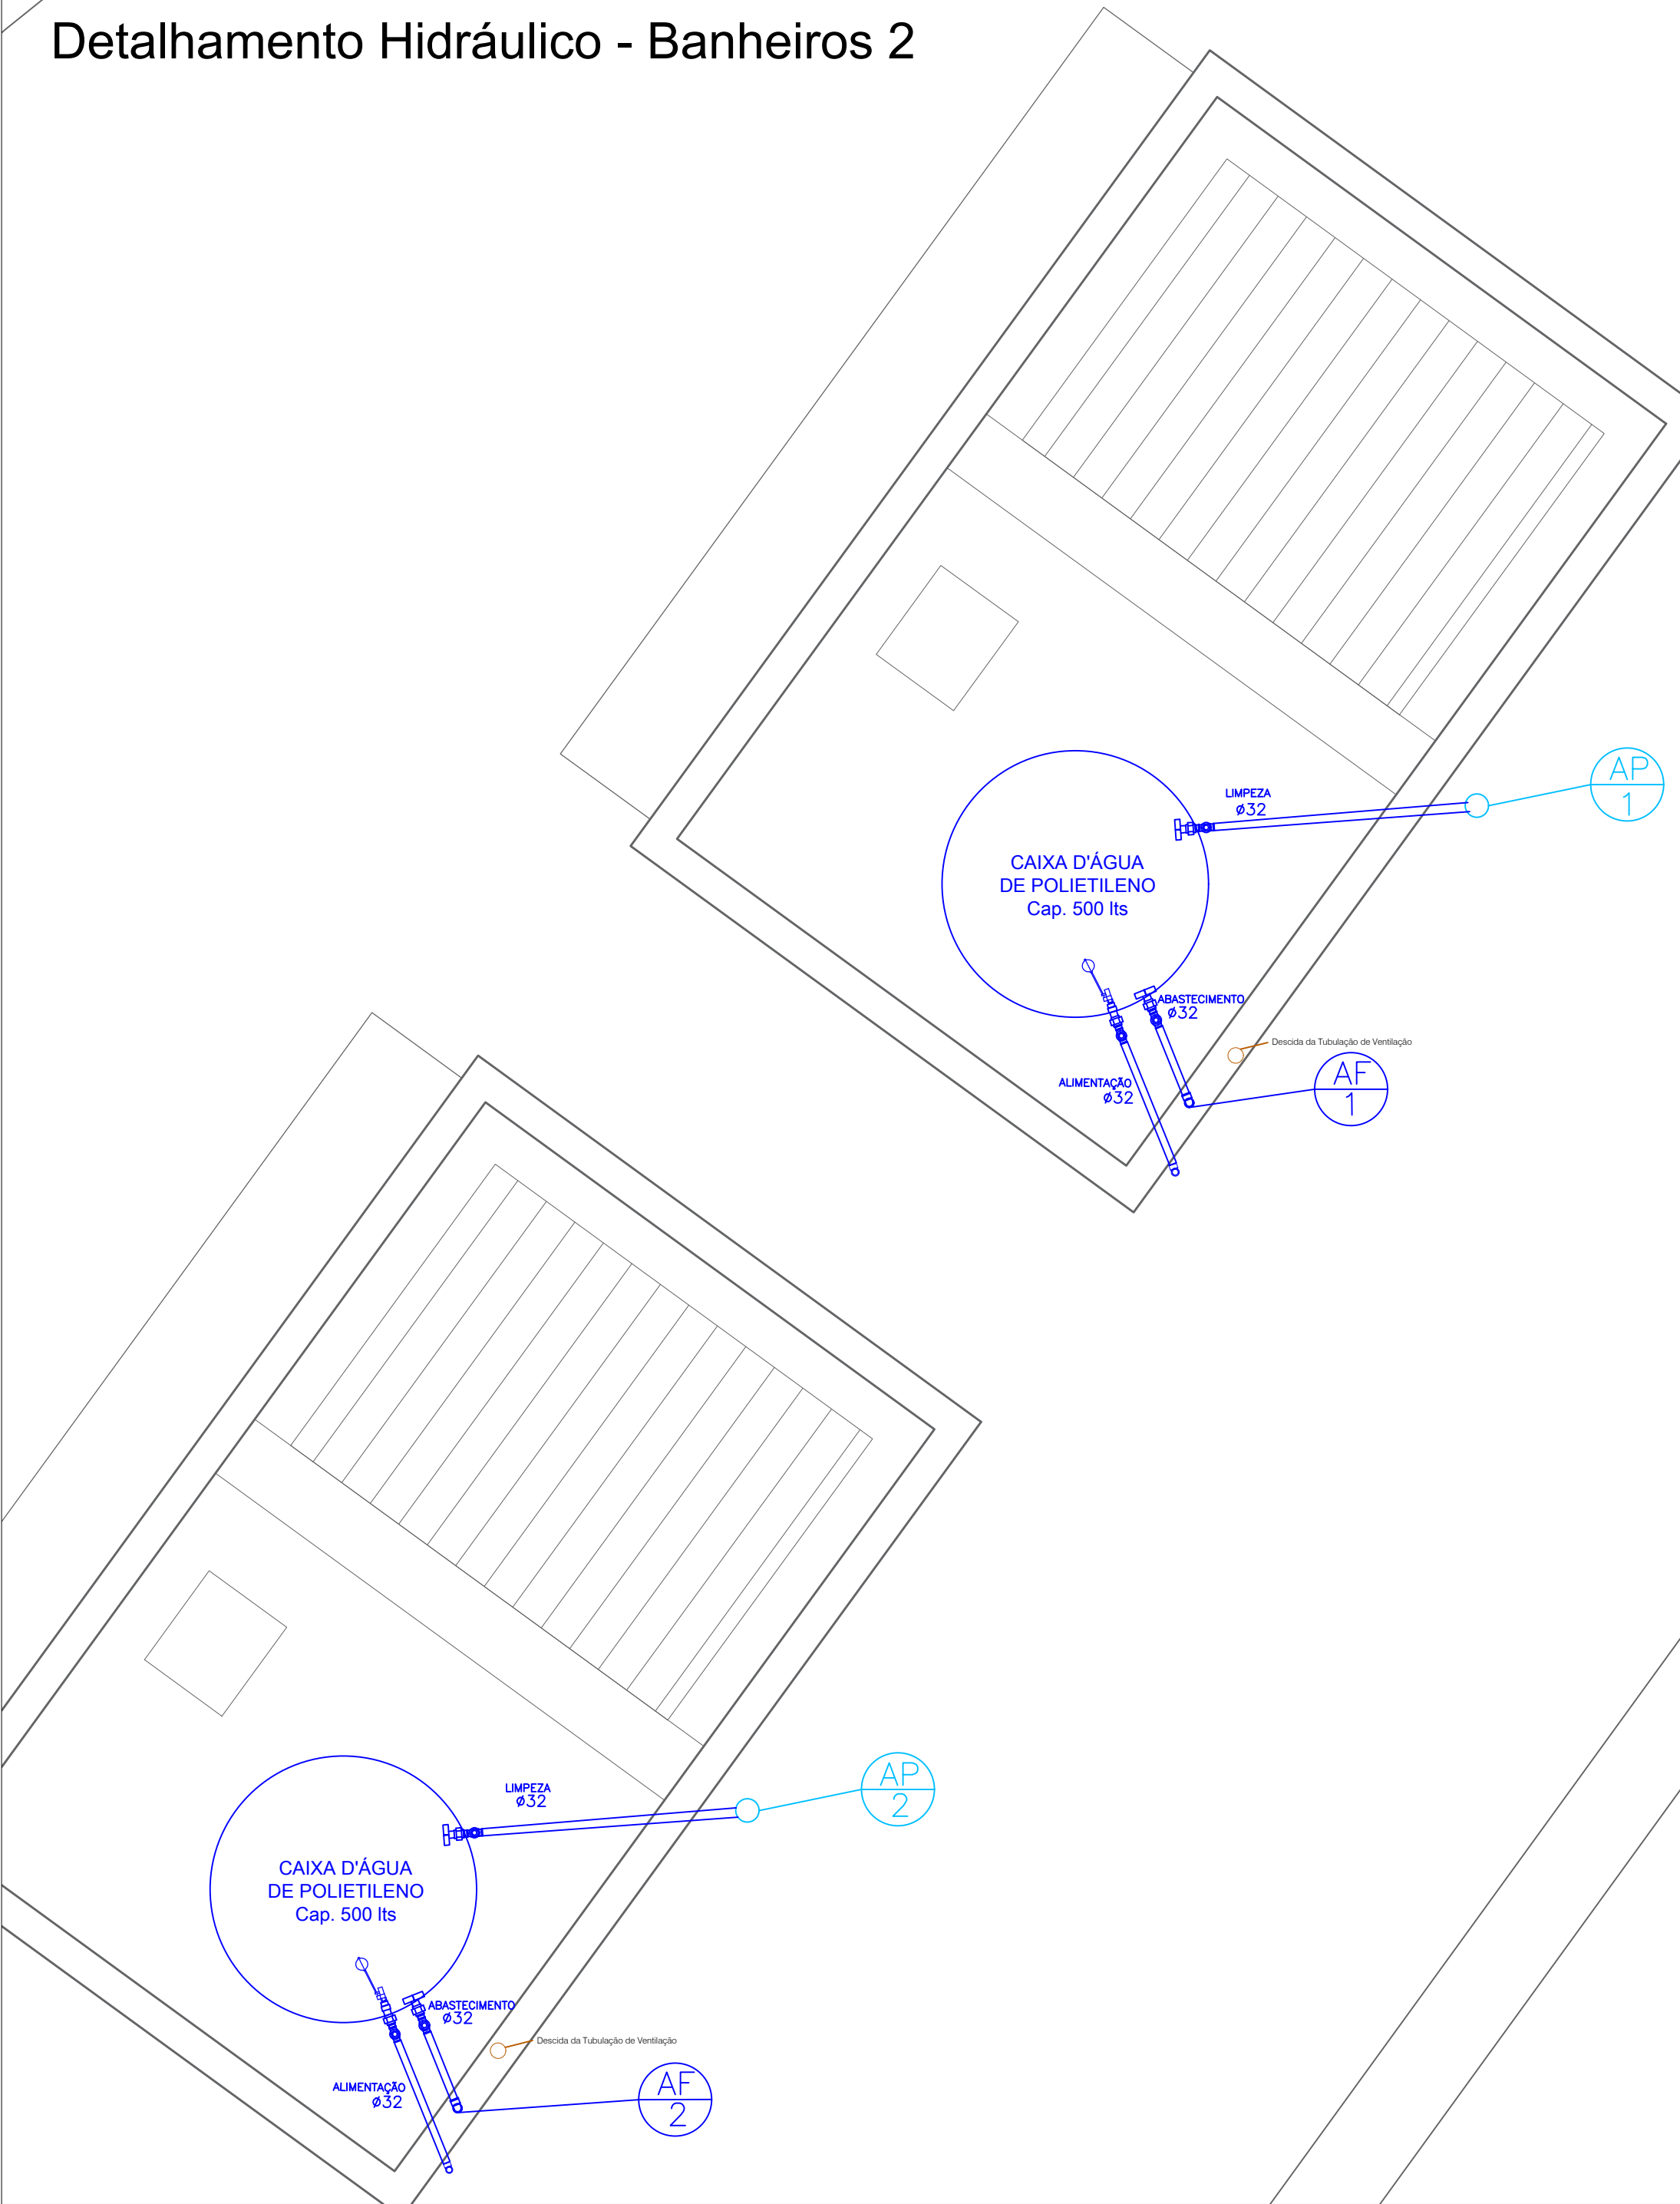


Detalhamento Hidráulico - Guarita

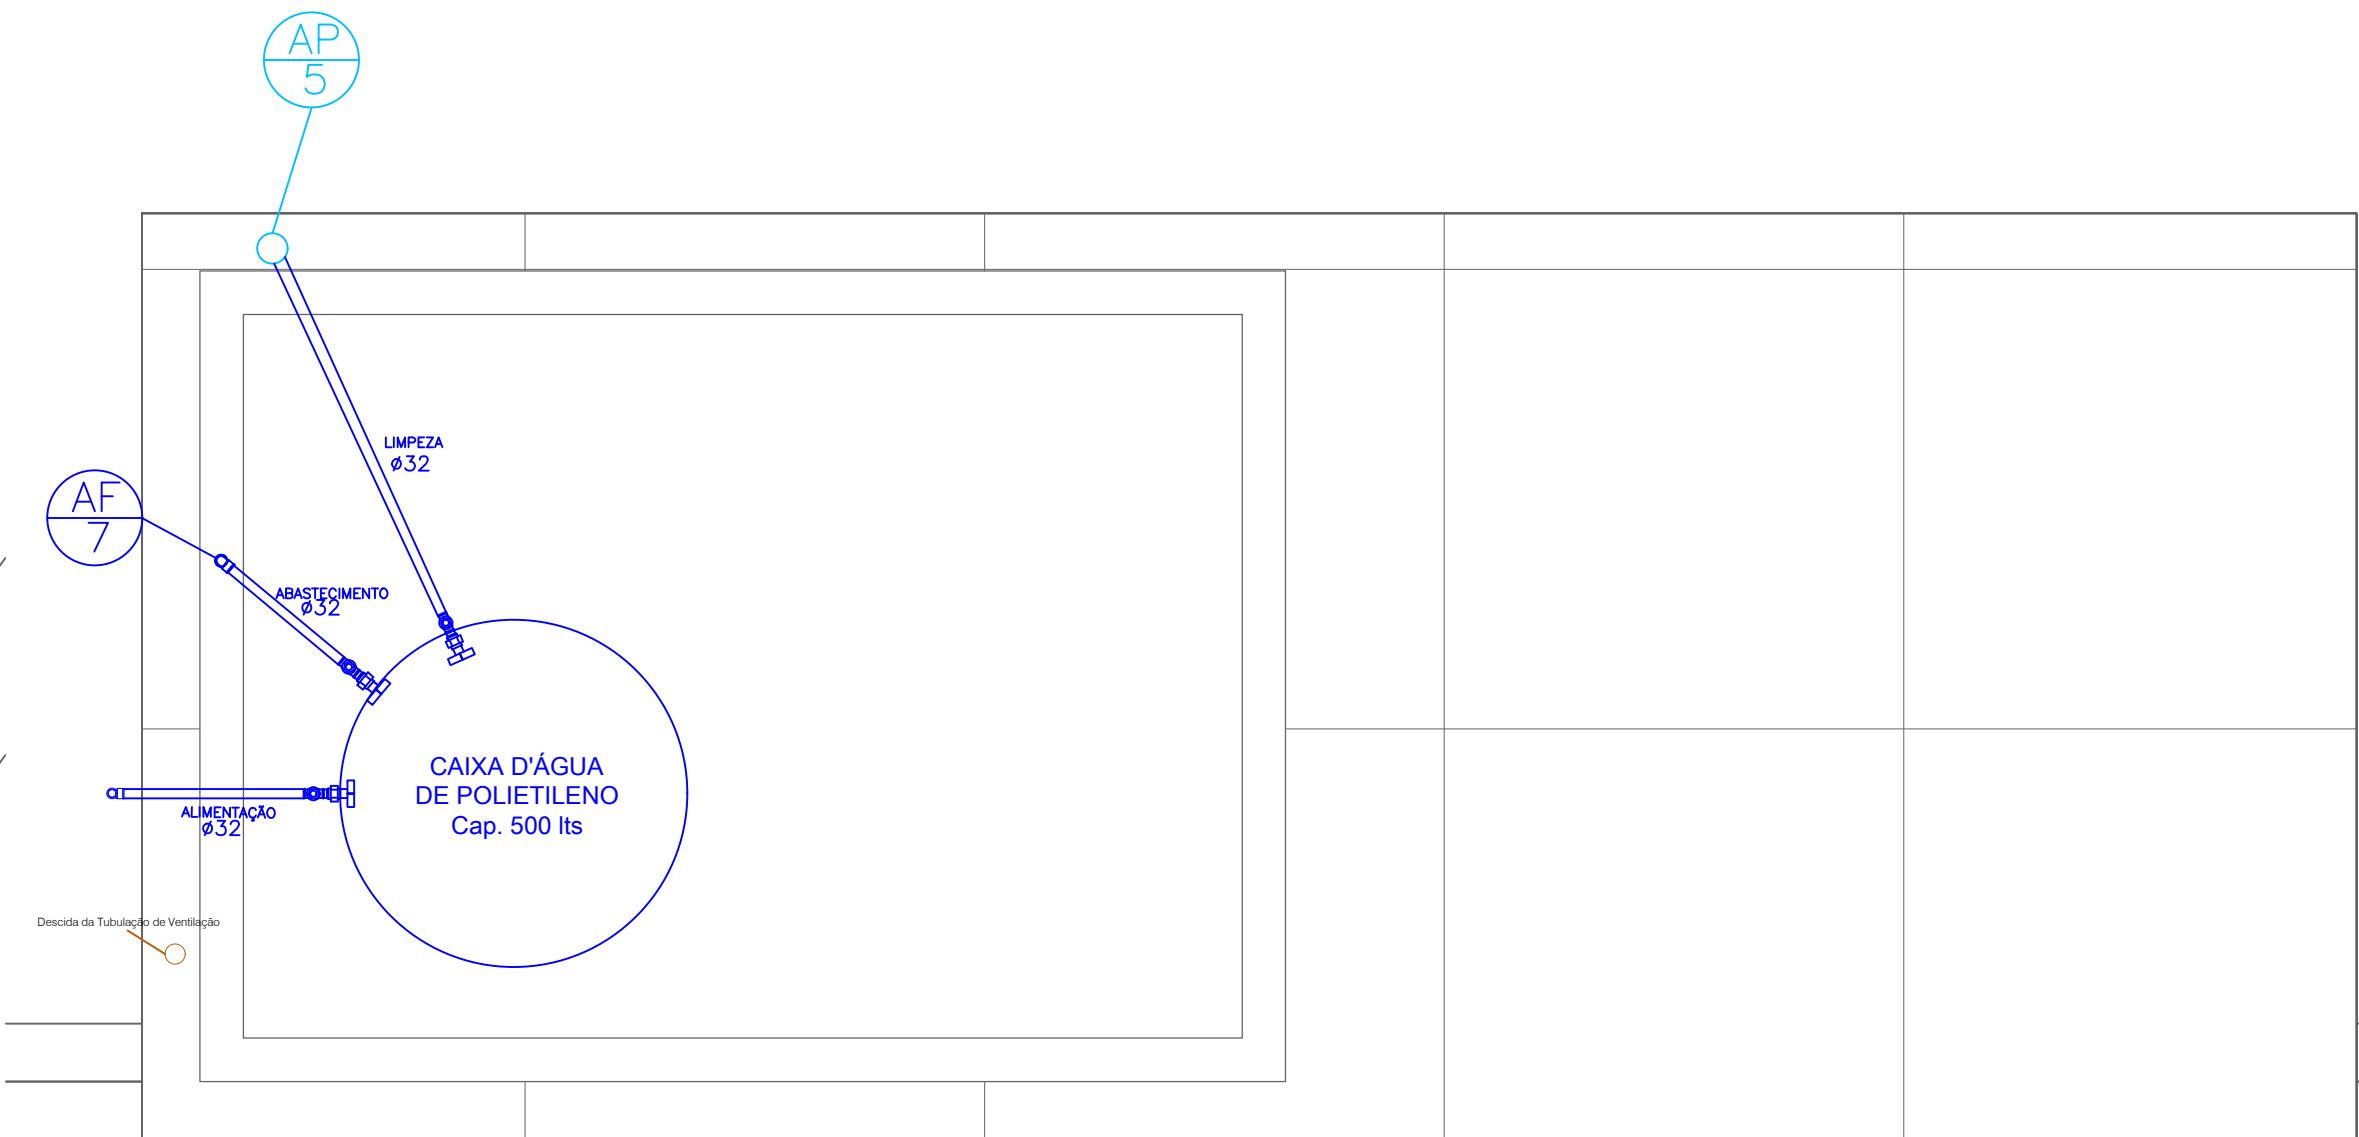

Detalhamento Hidráulico - Quiosque 1

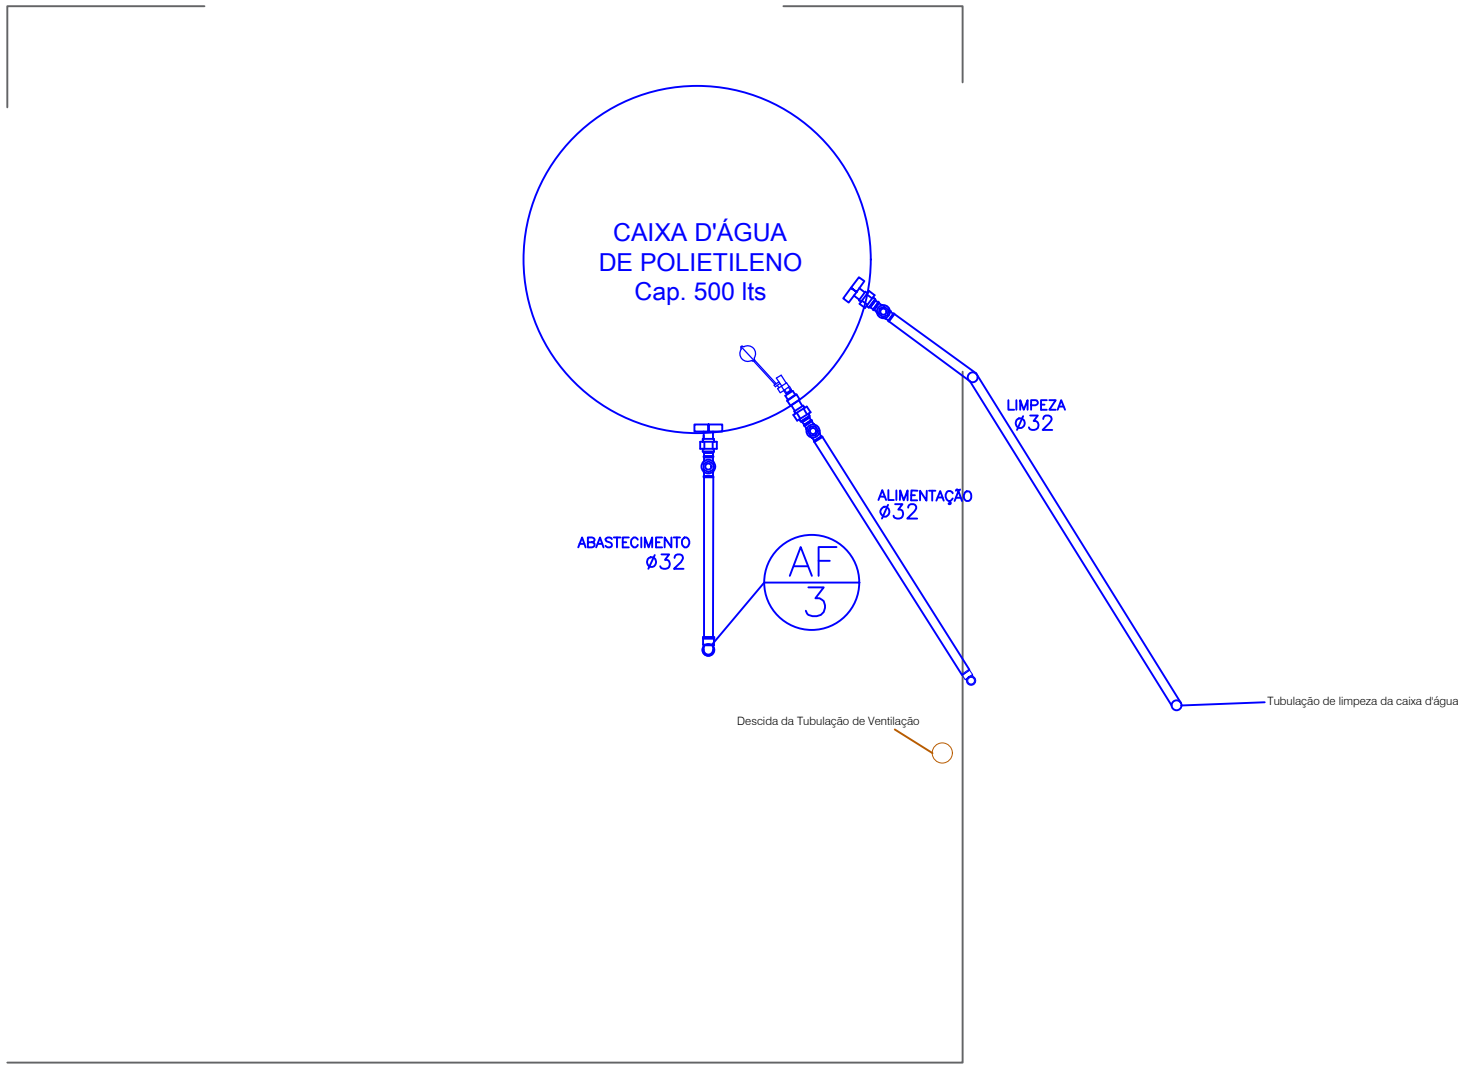

Detalhamento Hidráulico - Quiosque 2

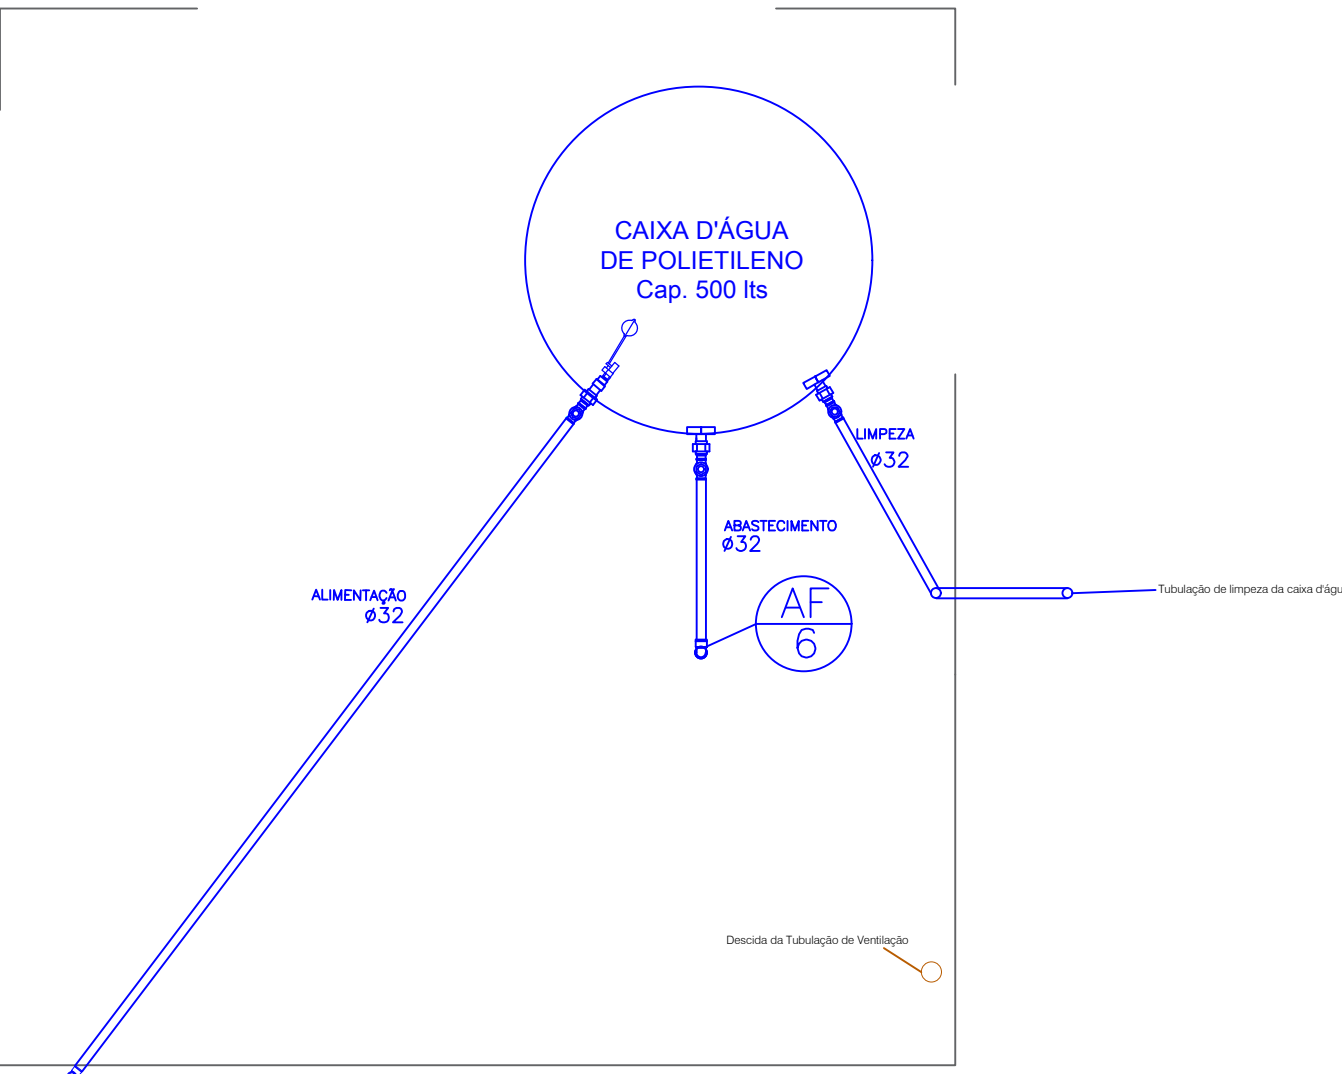

Projeto:Projeto de Urbanismo Vila Olimpica

Desenhos:PLANTA BAIXA COM DETALHAMENTO DOS PONTOS DE ÁGUAS FRIAS E PLUVIAIS

Observações:

- Conferir todas as medidas em obra antes da execução dos serviços.
- Não executar alterações sem autorização prévia do responsável técnico.
- Qualquer divergência entre projeto e condições de campo deverá ser comunicada ao responsável técnico para análise e aprovação.
- Todas as instalações deverão ser executadas por mão de obra qualificada, seguindo as normas técnicas vigentes e as recomendações dos fabricantes dos materiais empregados.
- O dimensionamento e posicionamentos indicados em projeto prevalecem sobre quaisquer informações complementares aqui descritas.

Esta prancha apresenta os detalhes das instalações de águas frias devendo sua execução seguir rigorosamente as dimensões, níveis, materiais e especificações indicados em projeto.

- Tubulação de abastecimento e distribuição principal: DN 32 mm.
- Tubulações de alimentação dos pontos de consumo: DN 25 mm.
- O reservatório superior será composto por:

Tubulação de alimentação controlada por torneira de boia;
Tubulação de abastecimento da rede de distribuição;
Tubulação de ventilação prolongada acima do nível máximo de água do reservatório;
Tubulação de limpeza (dreno) para esgotamento total do reservatório;
Extravasor (ladrão) interligado ao dreno, destinado à descarga do excedente de água em caso de falha do sistema de controle de nível.
• Todas as tubulações deverão ser executadas conforme os diâmetros, cotas e posicionamentos indicados em projeto.
• Deverão ser realizados testes de estanqueidade antes do fechamento de paredes, pisos e forros.

As instalações de águas pluviais foram dimensionadas e deverão ser executadas conforme as prescrições da ABNT NBR 10844.

- As águas provenientes da cobertura serão captadas por calhas e conduzidas através de condutores verticais e horizontais até o ponto de lançamento previsto em projeto.
- O extravasor do reservatório superior será direcionado para a rede de drenagem pluvial.
- As tubulações deverão obedecer aos diâmetros e declividades especificados em projeto.
- Deverá ser garantido o livre escoamento das águas pluviais, evitando acúmulo ou retorno de fluxo.
- As calhas, condutores e dispositivos de captação deverão permanecer livres de obstruções.

Projeta: Fernando Matias Mamede

RESPONSÁVEL TÉCNICO

Fernando Matias Mamede

Engenheiro Civil

Crea: 162056275-8

PROPRIETÁRIO(A)


Prefeitura Municipal de Coremas

Endereço/Obra: Rua Francisco Raimundo de Andrade, DNOCS, Coremas - PB, 58770-000


ÁREAS	m²
Área do Terreno	10.733,41
Estacionamento	519,11
Calçada	249,64
Área verde	4.281,11

Prancha:12/14


Detalhamento Hidráulico - Banheiros 1

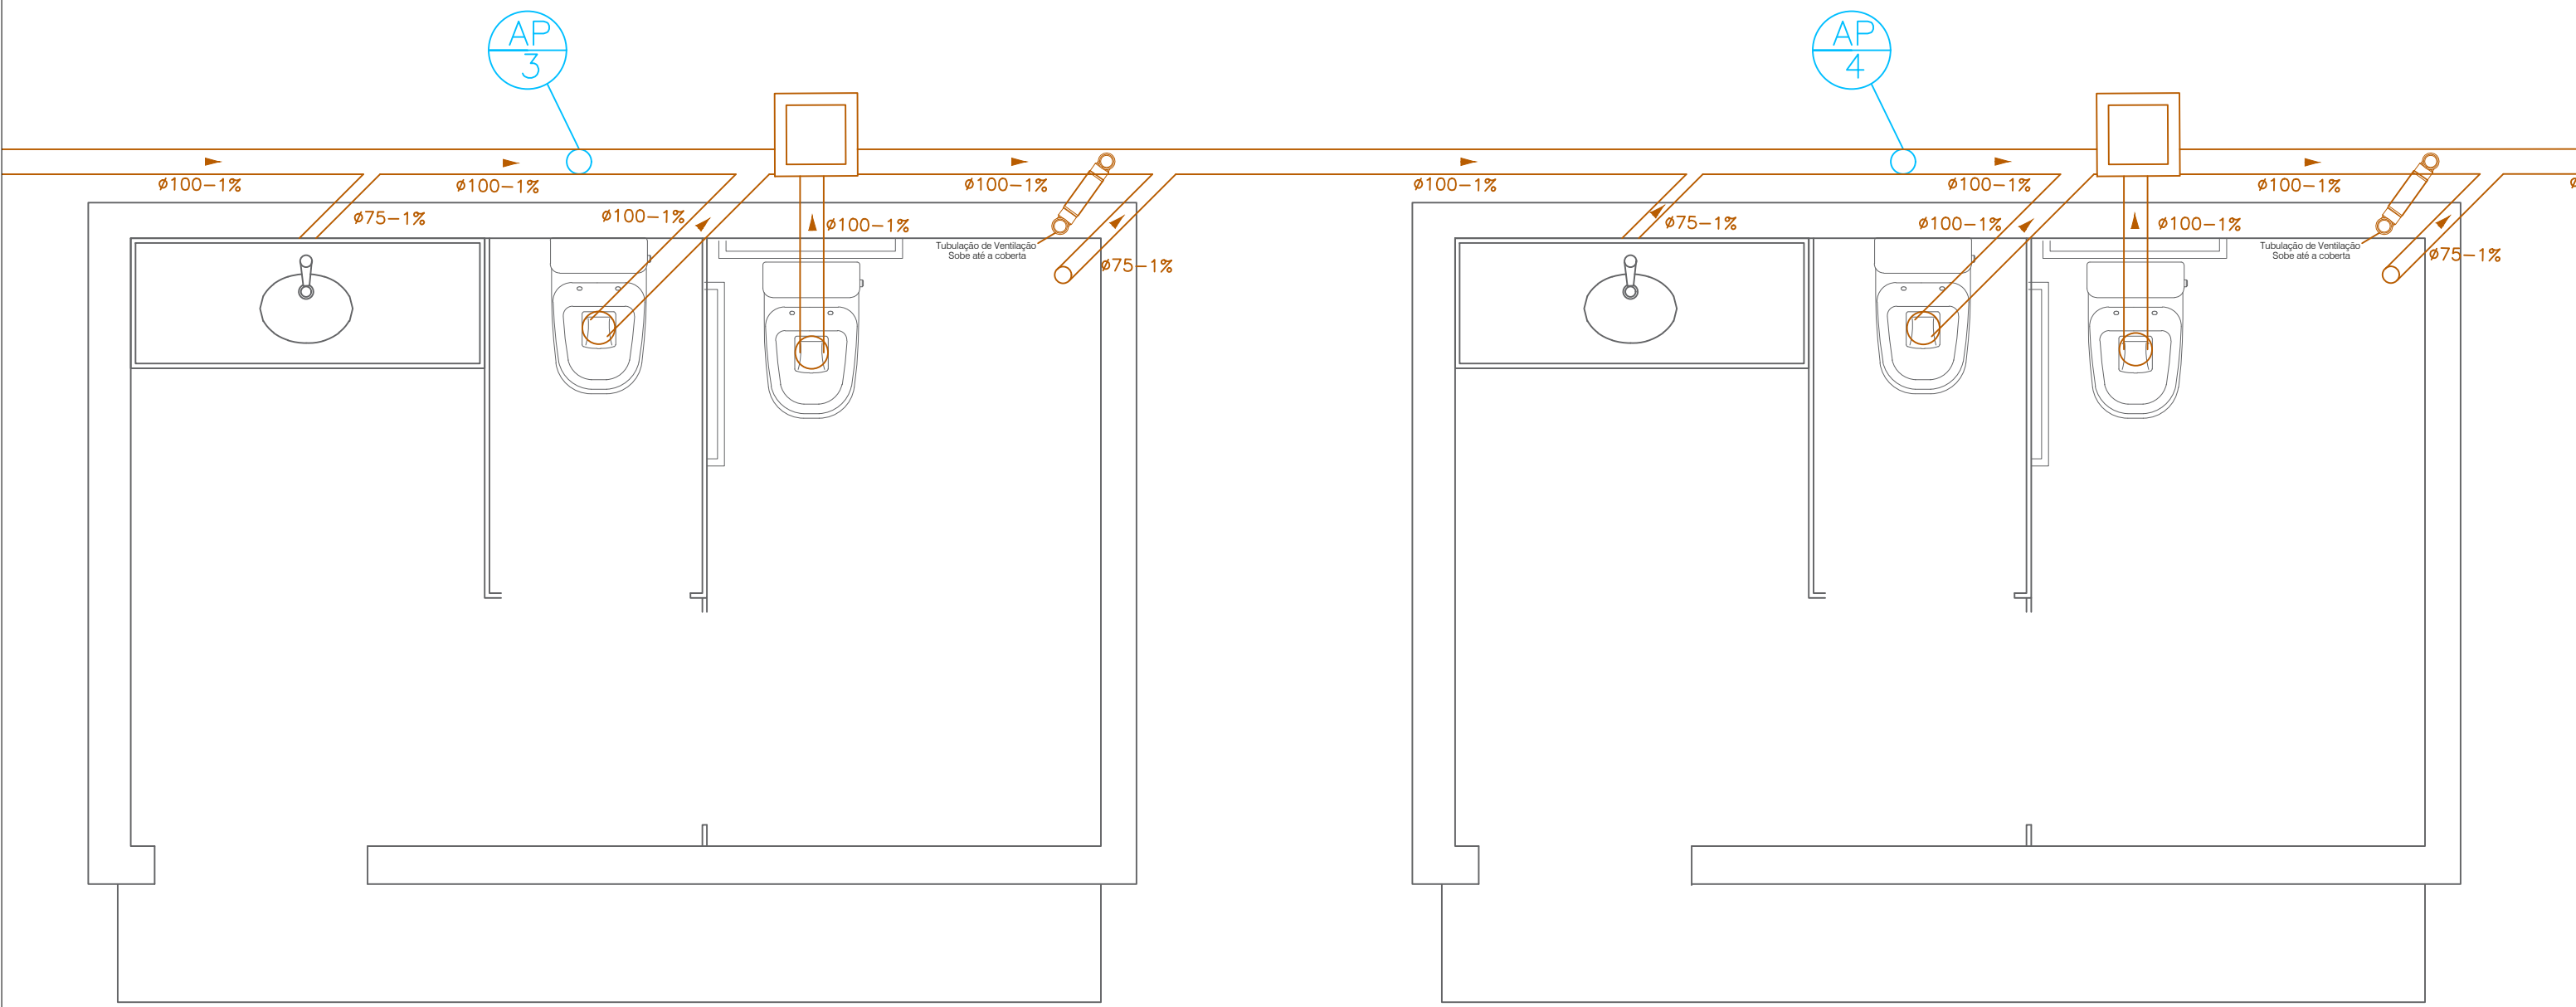


Detalhamento Hidráulico - Banheiros 2

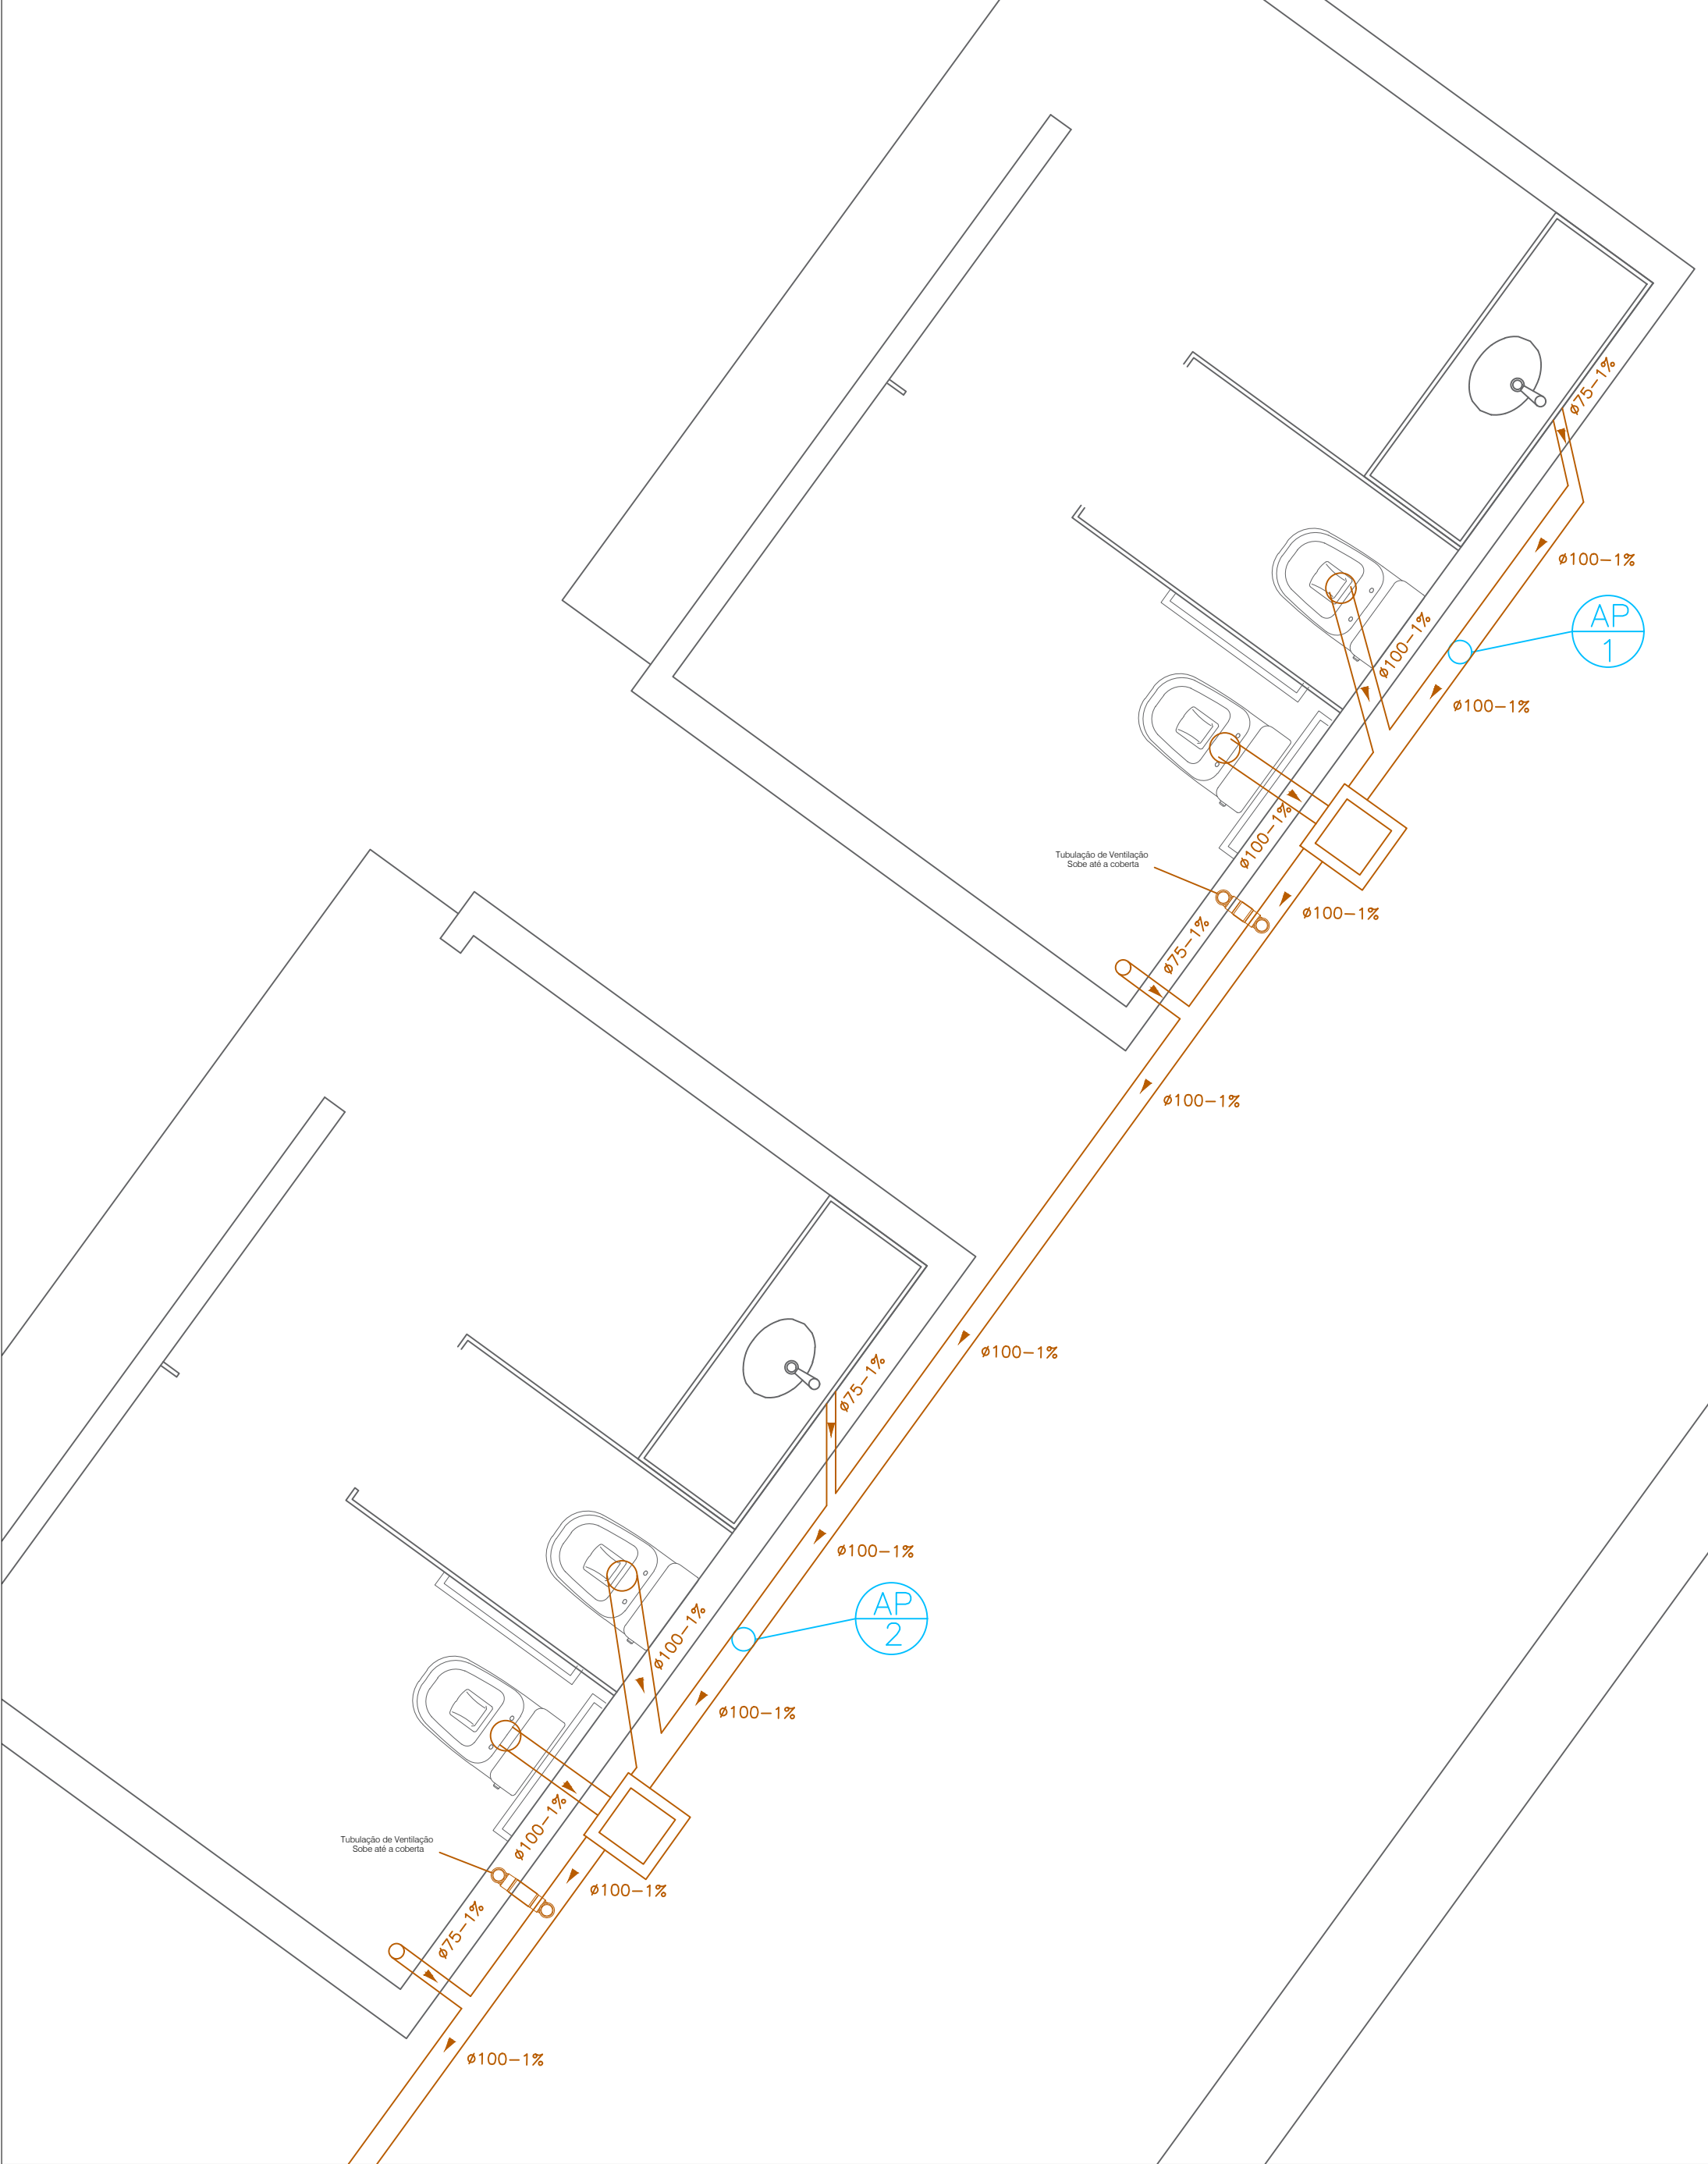


Detalhamento Hidráulico - Guarita

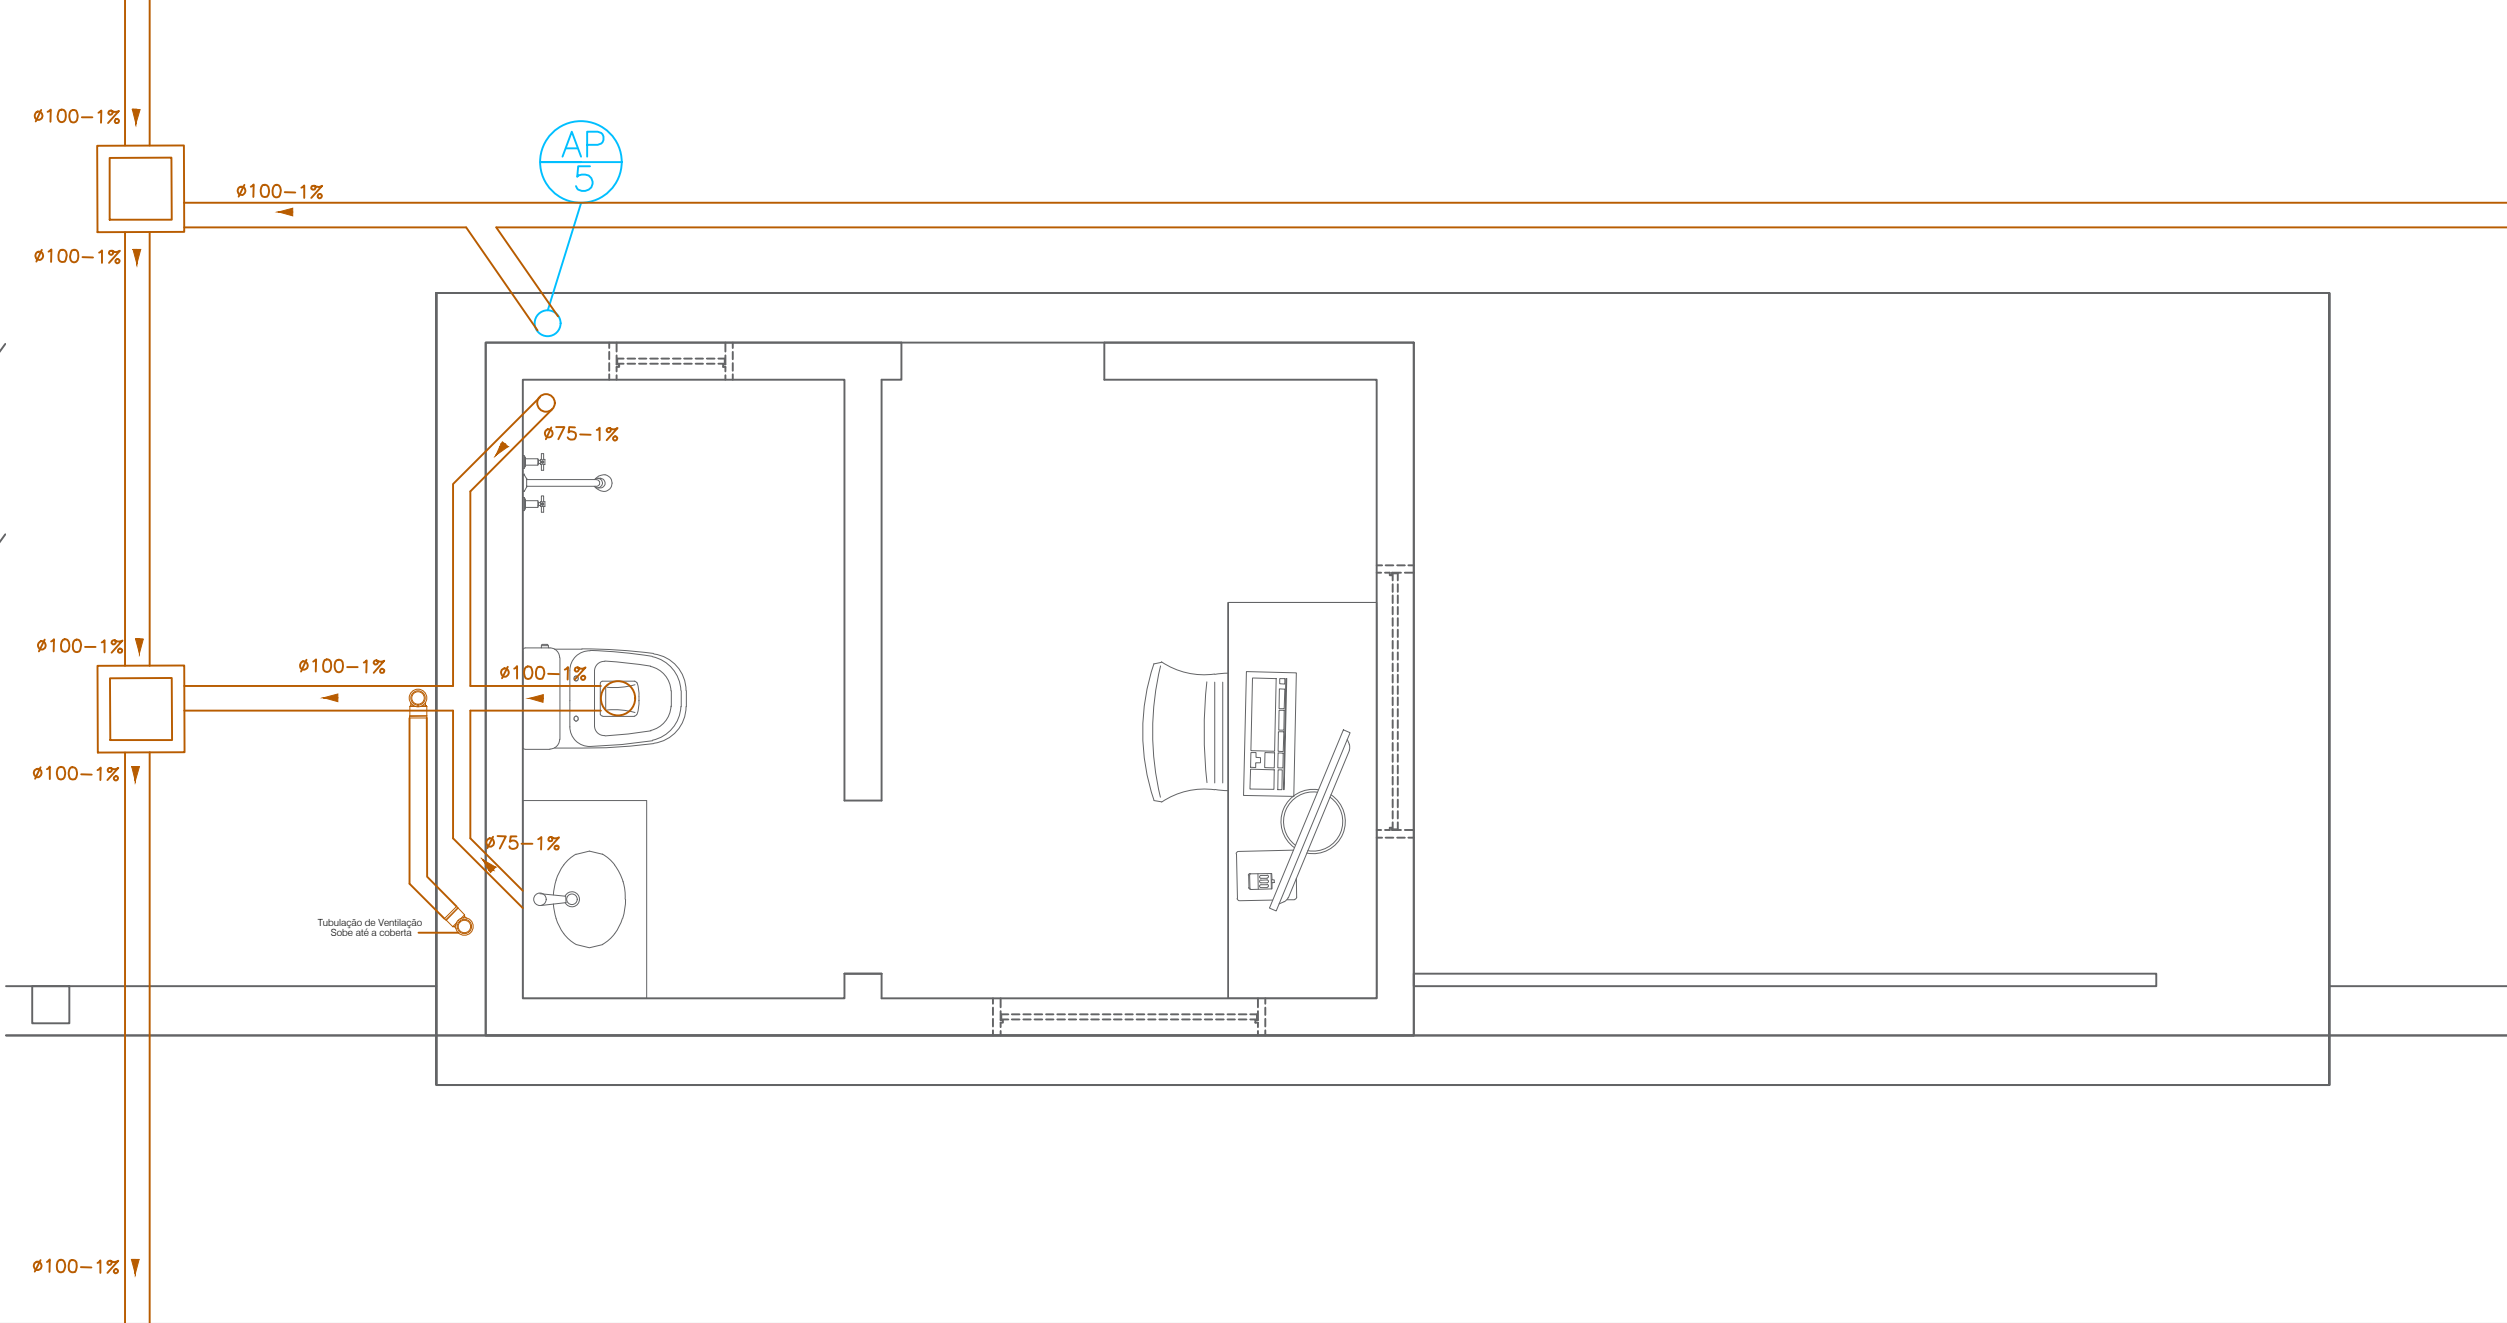

Detalhamento Hidráulico - Quiosque 1

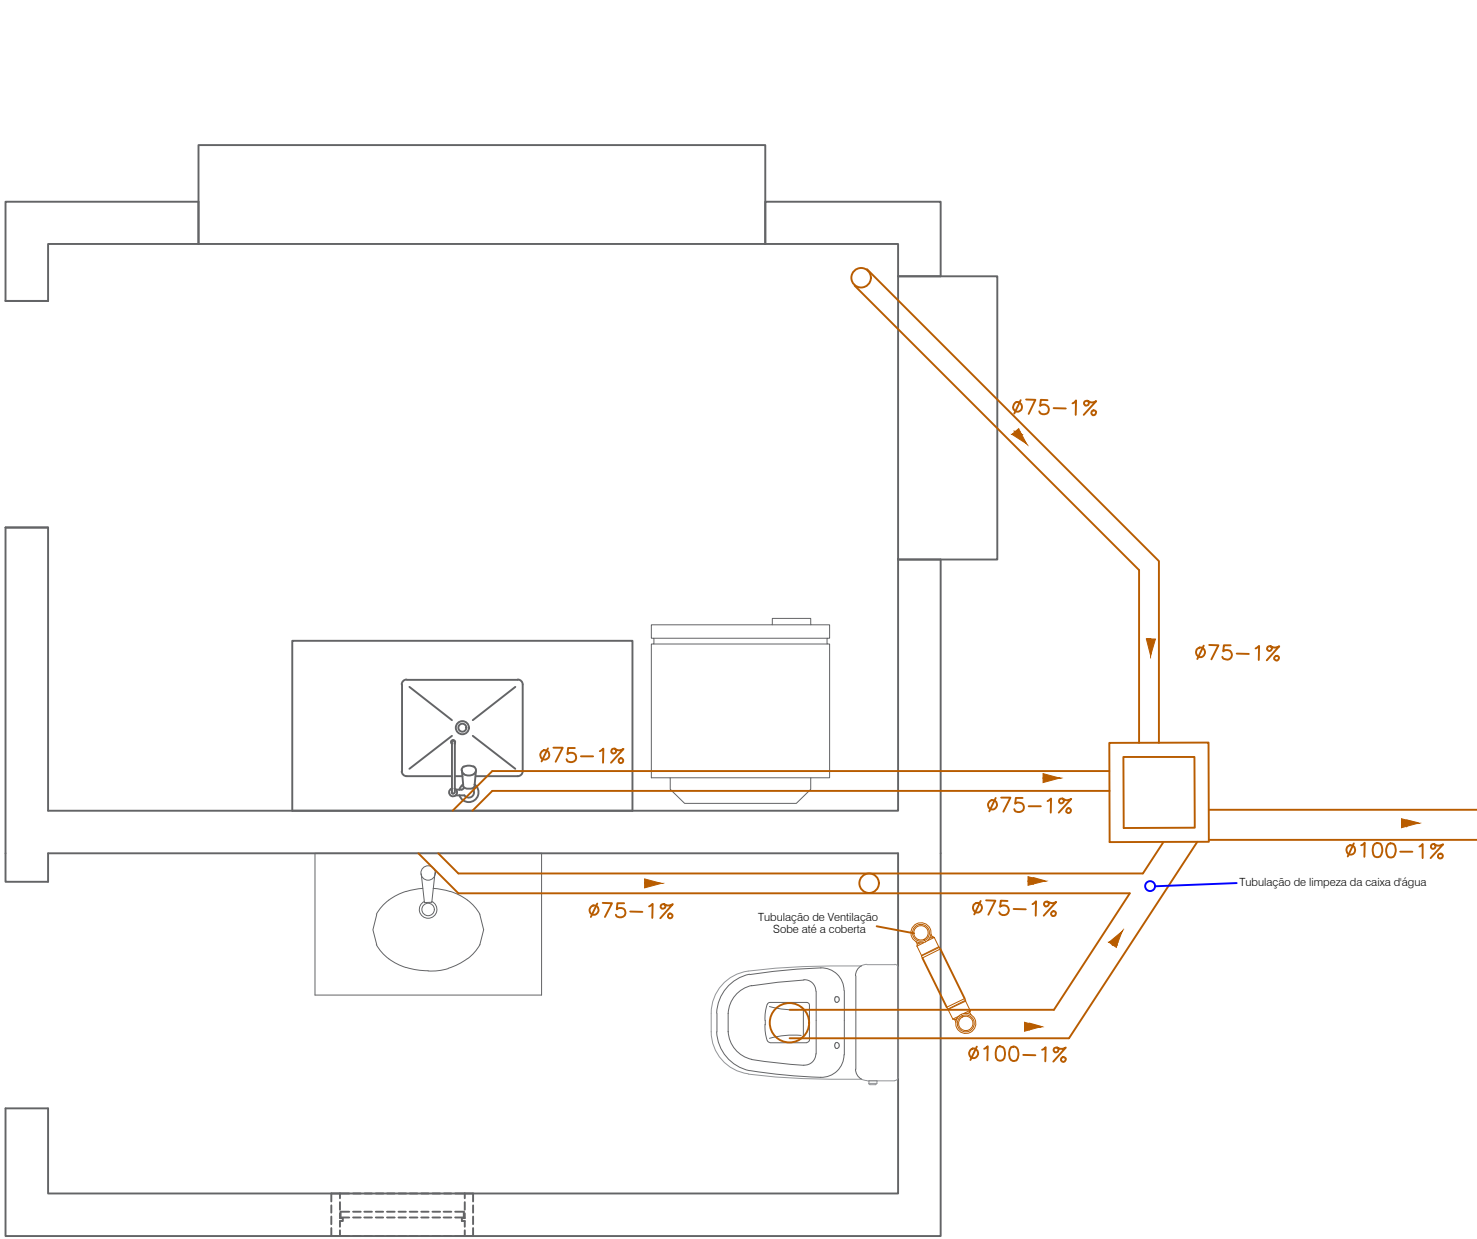

Detalhamento Hidráulico - Quiosque 2

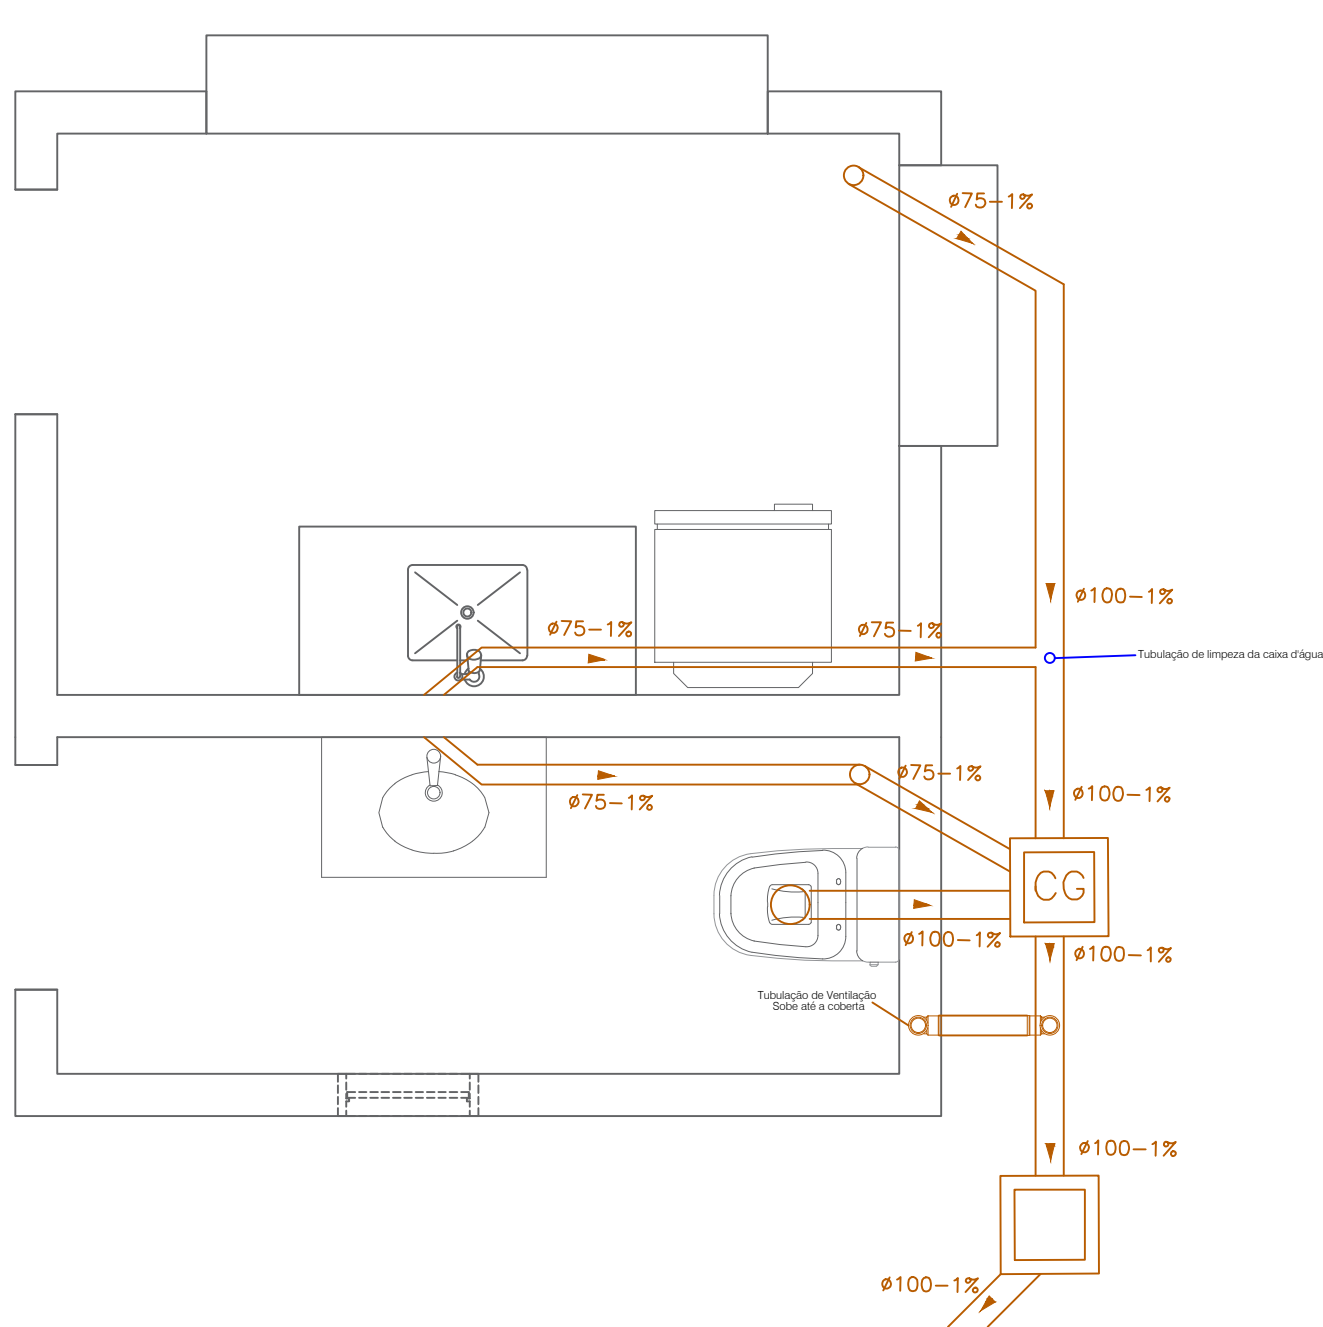

Projeto:

Projeto de Urbanismo Vila Olimpica

Desenhos:

PLANTA BAIXA COM DETALHAMENTO DOS PONTOS DE ESGOTO SANITÁRIO

Conferir todas as medidas em obra antes da execução dos serviços.

Não executar alterações sem autorização prévia do responsável técnico.

Qualquer divergência entre projeto e condições de campo deverá ser comunicada ao responsável técnico para análise e aprovação.

Todas as instalações deverão ser executadas por mão de obra qualificada, seguindo as normas técnicas vigentes e as recomendações dos fabricantes dos materiais empregados.

O dimensionamento e posicionamentos indicados em projeto prevalecem sobre quaisquer informações complementares aqui descritas.

Esta prancha apresenta os detalhamentos das instalações de esgoto sanitário devendo sua execução seguir rigorosamente as dimensões, níveis, materiais e especificações indicados em projeto.

Ramais de esgoto sanitário: DN 75 mm com declividade mínima de 1%.

Ramais de bacias sanitárias: DN 100 mm com declividade mínima de 1%.

Coletor principal de esgoto: DN 100 mm com declividade mínima de 1%.

O sistema contará com caixas de inspeção nos locais indicados em projeto.

O sistema será provido de ventilação sanitária através de tubulações de ventilação dimensionadas e posicionadas conforme projeto.

Todas as conexões deverão ser executadas no sentido do fluxo, respeitando os diâmetros, declividades e cotas indicados em projeto.

Antes da entrada em operação, deverá ser realizado teste de estanqueidade em toda a rede.

Projetista:

Fernando Matias Mamede

RESPONSÁVEL TÉCNICO

Fernando Matias Mamede

Engenheiro Civil

Crea: 162056275-8

Proprietário:

Prefeitura Municipal de Coremas

PROPRIETÁRIO(A)

Endereço/Obra:

Rua Francisco Raimundo de Andrade, DNOCS, Coremas - PB, 58770-000

ÁREAS

Área do Terreno

Estacionamento

Calçada

Área verde

m²

10.733,41

519,11

249,64

4.281,11

Prancha:

14/14

MAMEDE

ENGENHEIRO

1975


1975

1975

1975

Projeto: **Projeto de Urbanismo Vila Olimpica**

Desenhos: **PLANTA BAIXA DE LOCAÇÃO DOS ELEMENTOS ESTRUTURAIS**

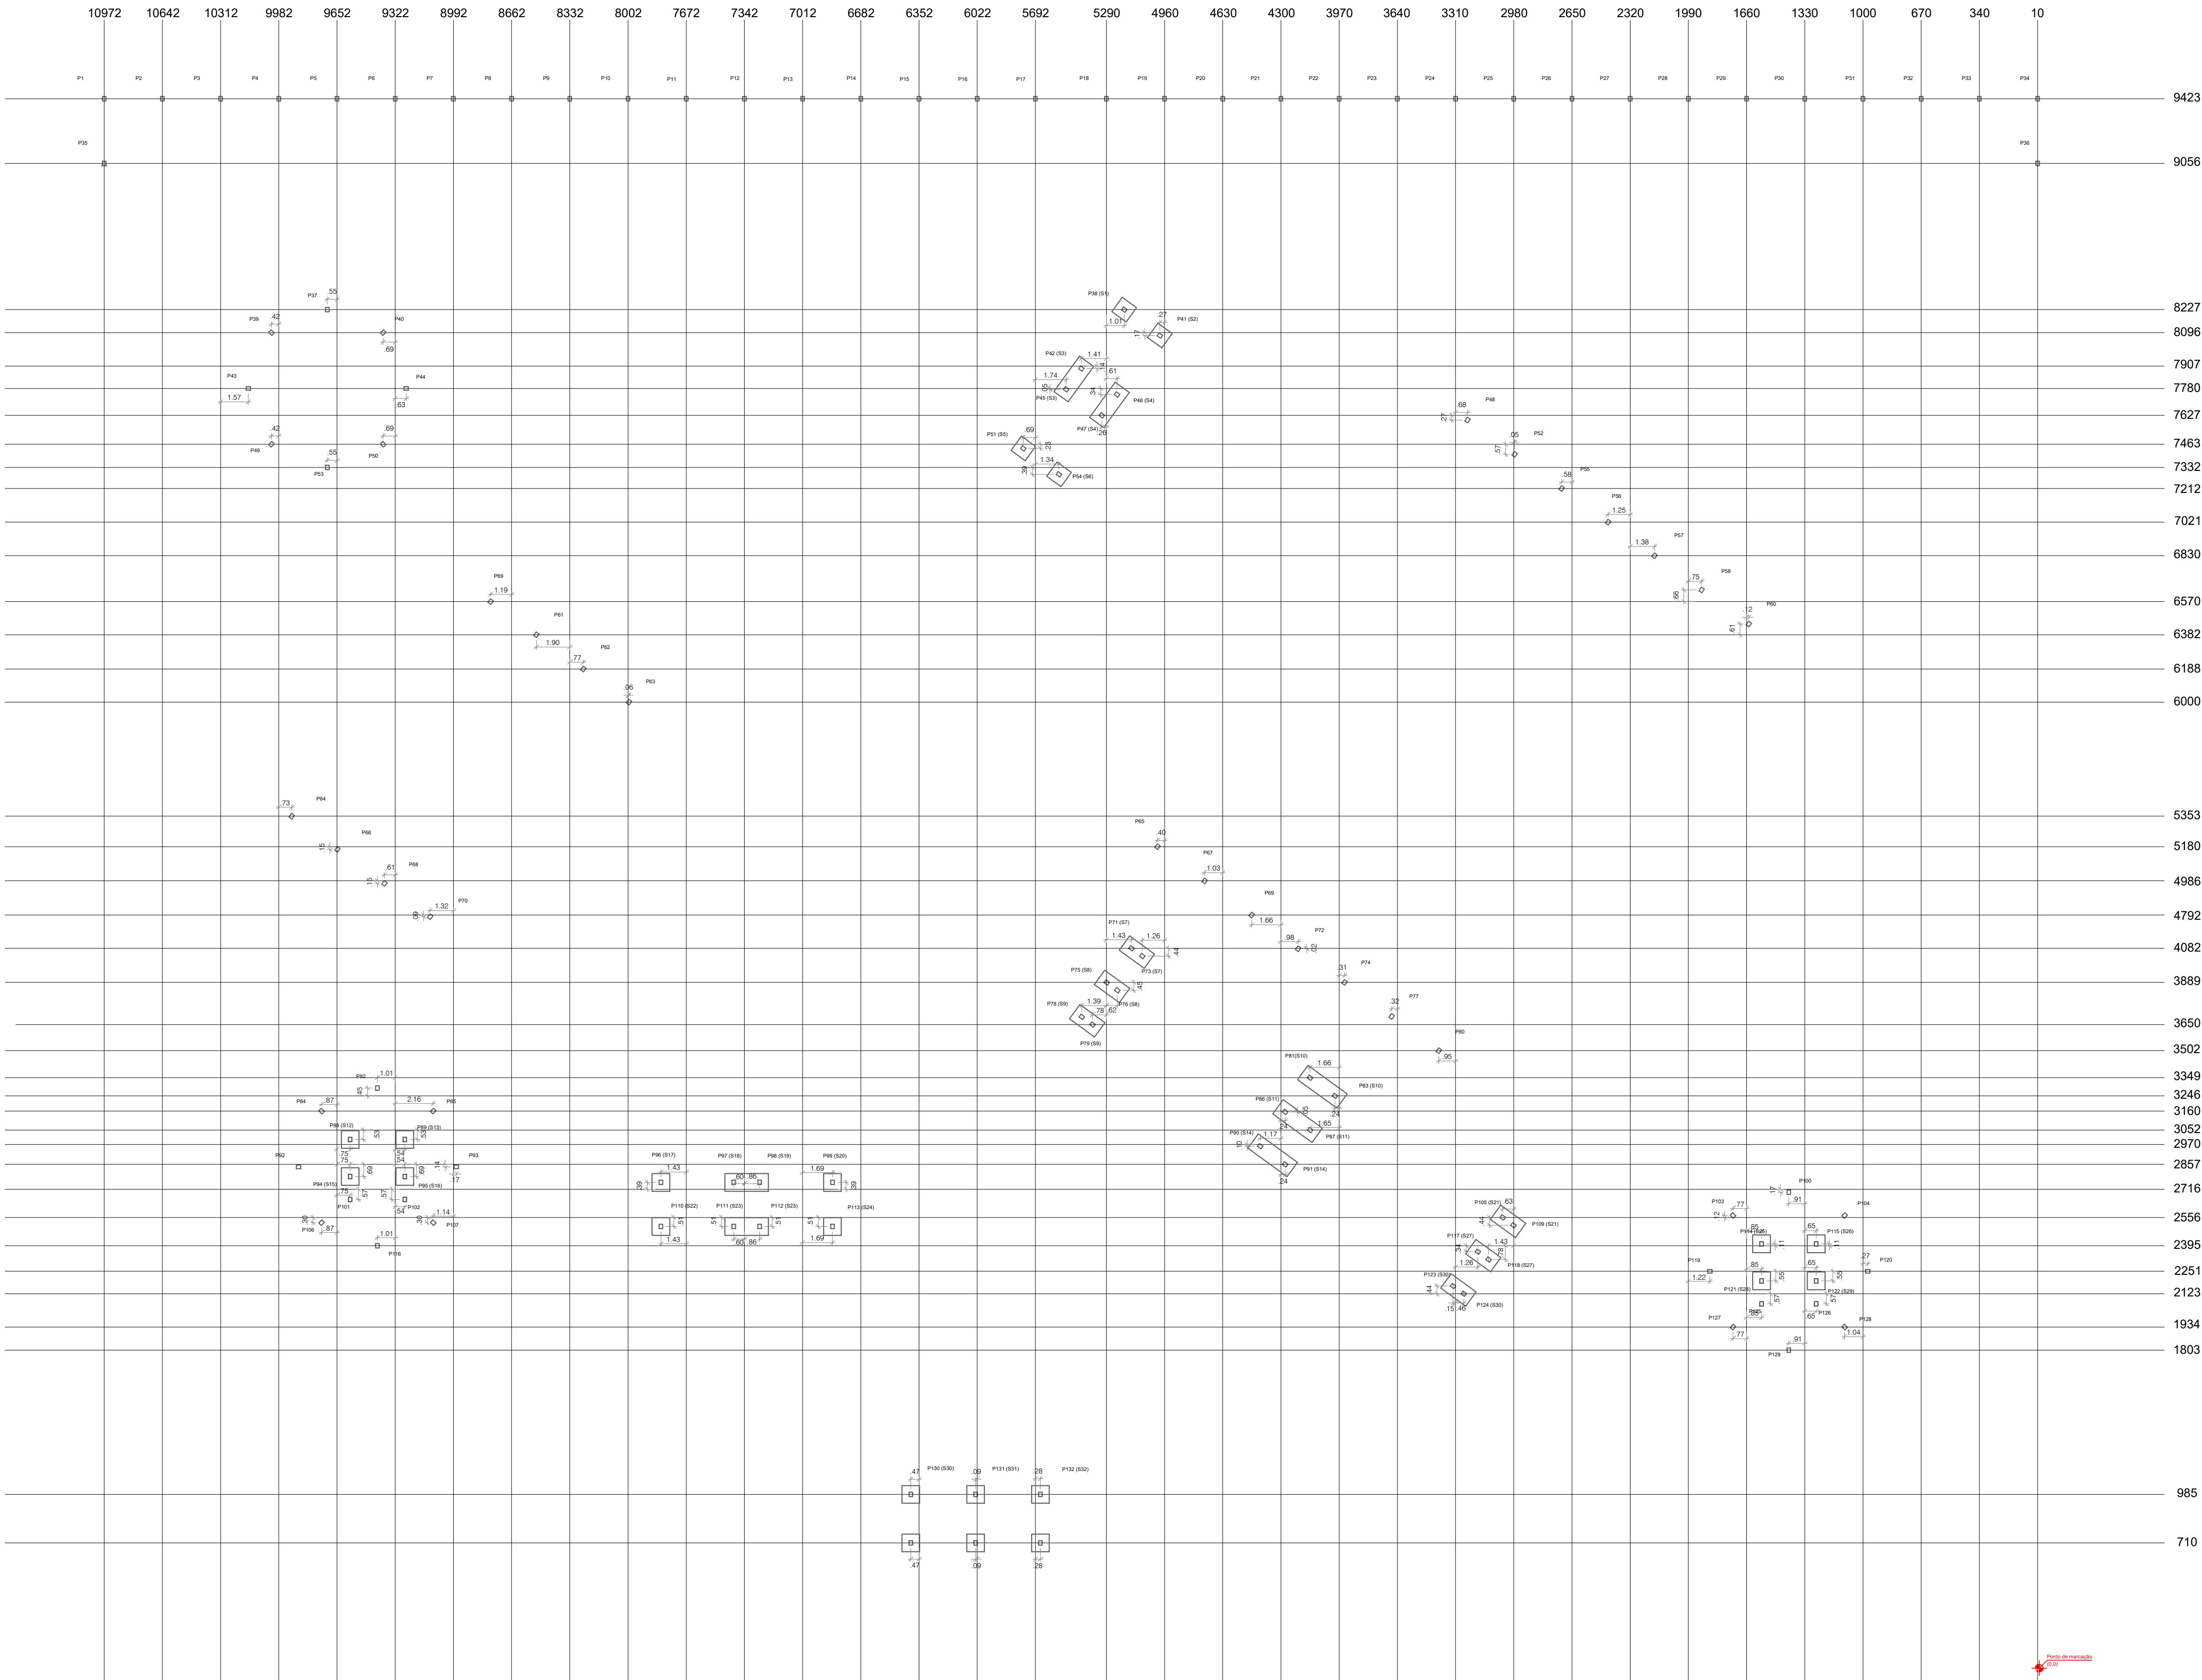

- Observações:
- Conferir todas as medidas em obra antes da execução dos serviços.
 - Não executar alterações sem autorização prévia do responsável técnico.
 - Qualquer divergência entre projeto e condições de campo deverá ser comunicada ao responsável técnico para análise e aprovação.
 - Todas as instalações deverão ser executadas por mão de obra qualificada, seguindo as normas técnicas vigentes e as recomendações dos fabricantes dos materiais empregados.
 - O dimensionamento e posicionamentos indicados em projeto prevalecem sobre quaisquer informações complementares aqui descritas.

A locação foi dimensionadas e deverá ser executadas conforme projeto.

- Os eixos de locação foram definidos a partir dos centros dos pilares, constituindo as referências principais para implantação da estrutura.
- Todas as cotas apresentadas referem-se às distâncias entre eixos centrais dos pilares, salvo indicação em contrário.
- Antes do início da execução, deverão ser conferidas em campo todas as medidas, níveis e alinhamentos.
- Qualquer divergência entre o projeto e as condições encontradas no local deverá ser comunicada ao responsável técnico para análise e aprovação.
- A locação da obra deverá ser realizada por profissional habilitado, utilizando equipamentos adequados para garantir a precisão dos alinhamentos e dimensões projetadas.
- Nenhum elemento estrutural deverá ser executado sem prévia conferência dos eixos de locação e respectivos níveis.

Projetista: **Fernando Matias Mamede**

RESPONSÁVEL TÉCNICO
Fernando Matias Mamede
Engenheiro Civil
Crea: 162056275-8



Proprietário: **Prefeitura Municipal de Coremas**

PROPRIETÁRIO(A)




Endereço/Obra: **Rua Francisco Raimundo de Andrade, DNOCS, Coremas - PB, 58770-000**

ÁREAS	m²
Área do Terreno	10.733,41
Estacionamento	519,11
Calçada	249,64
Área verde	4.281,11

Prancha:

01/14

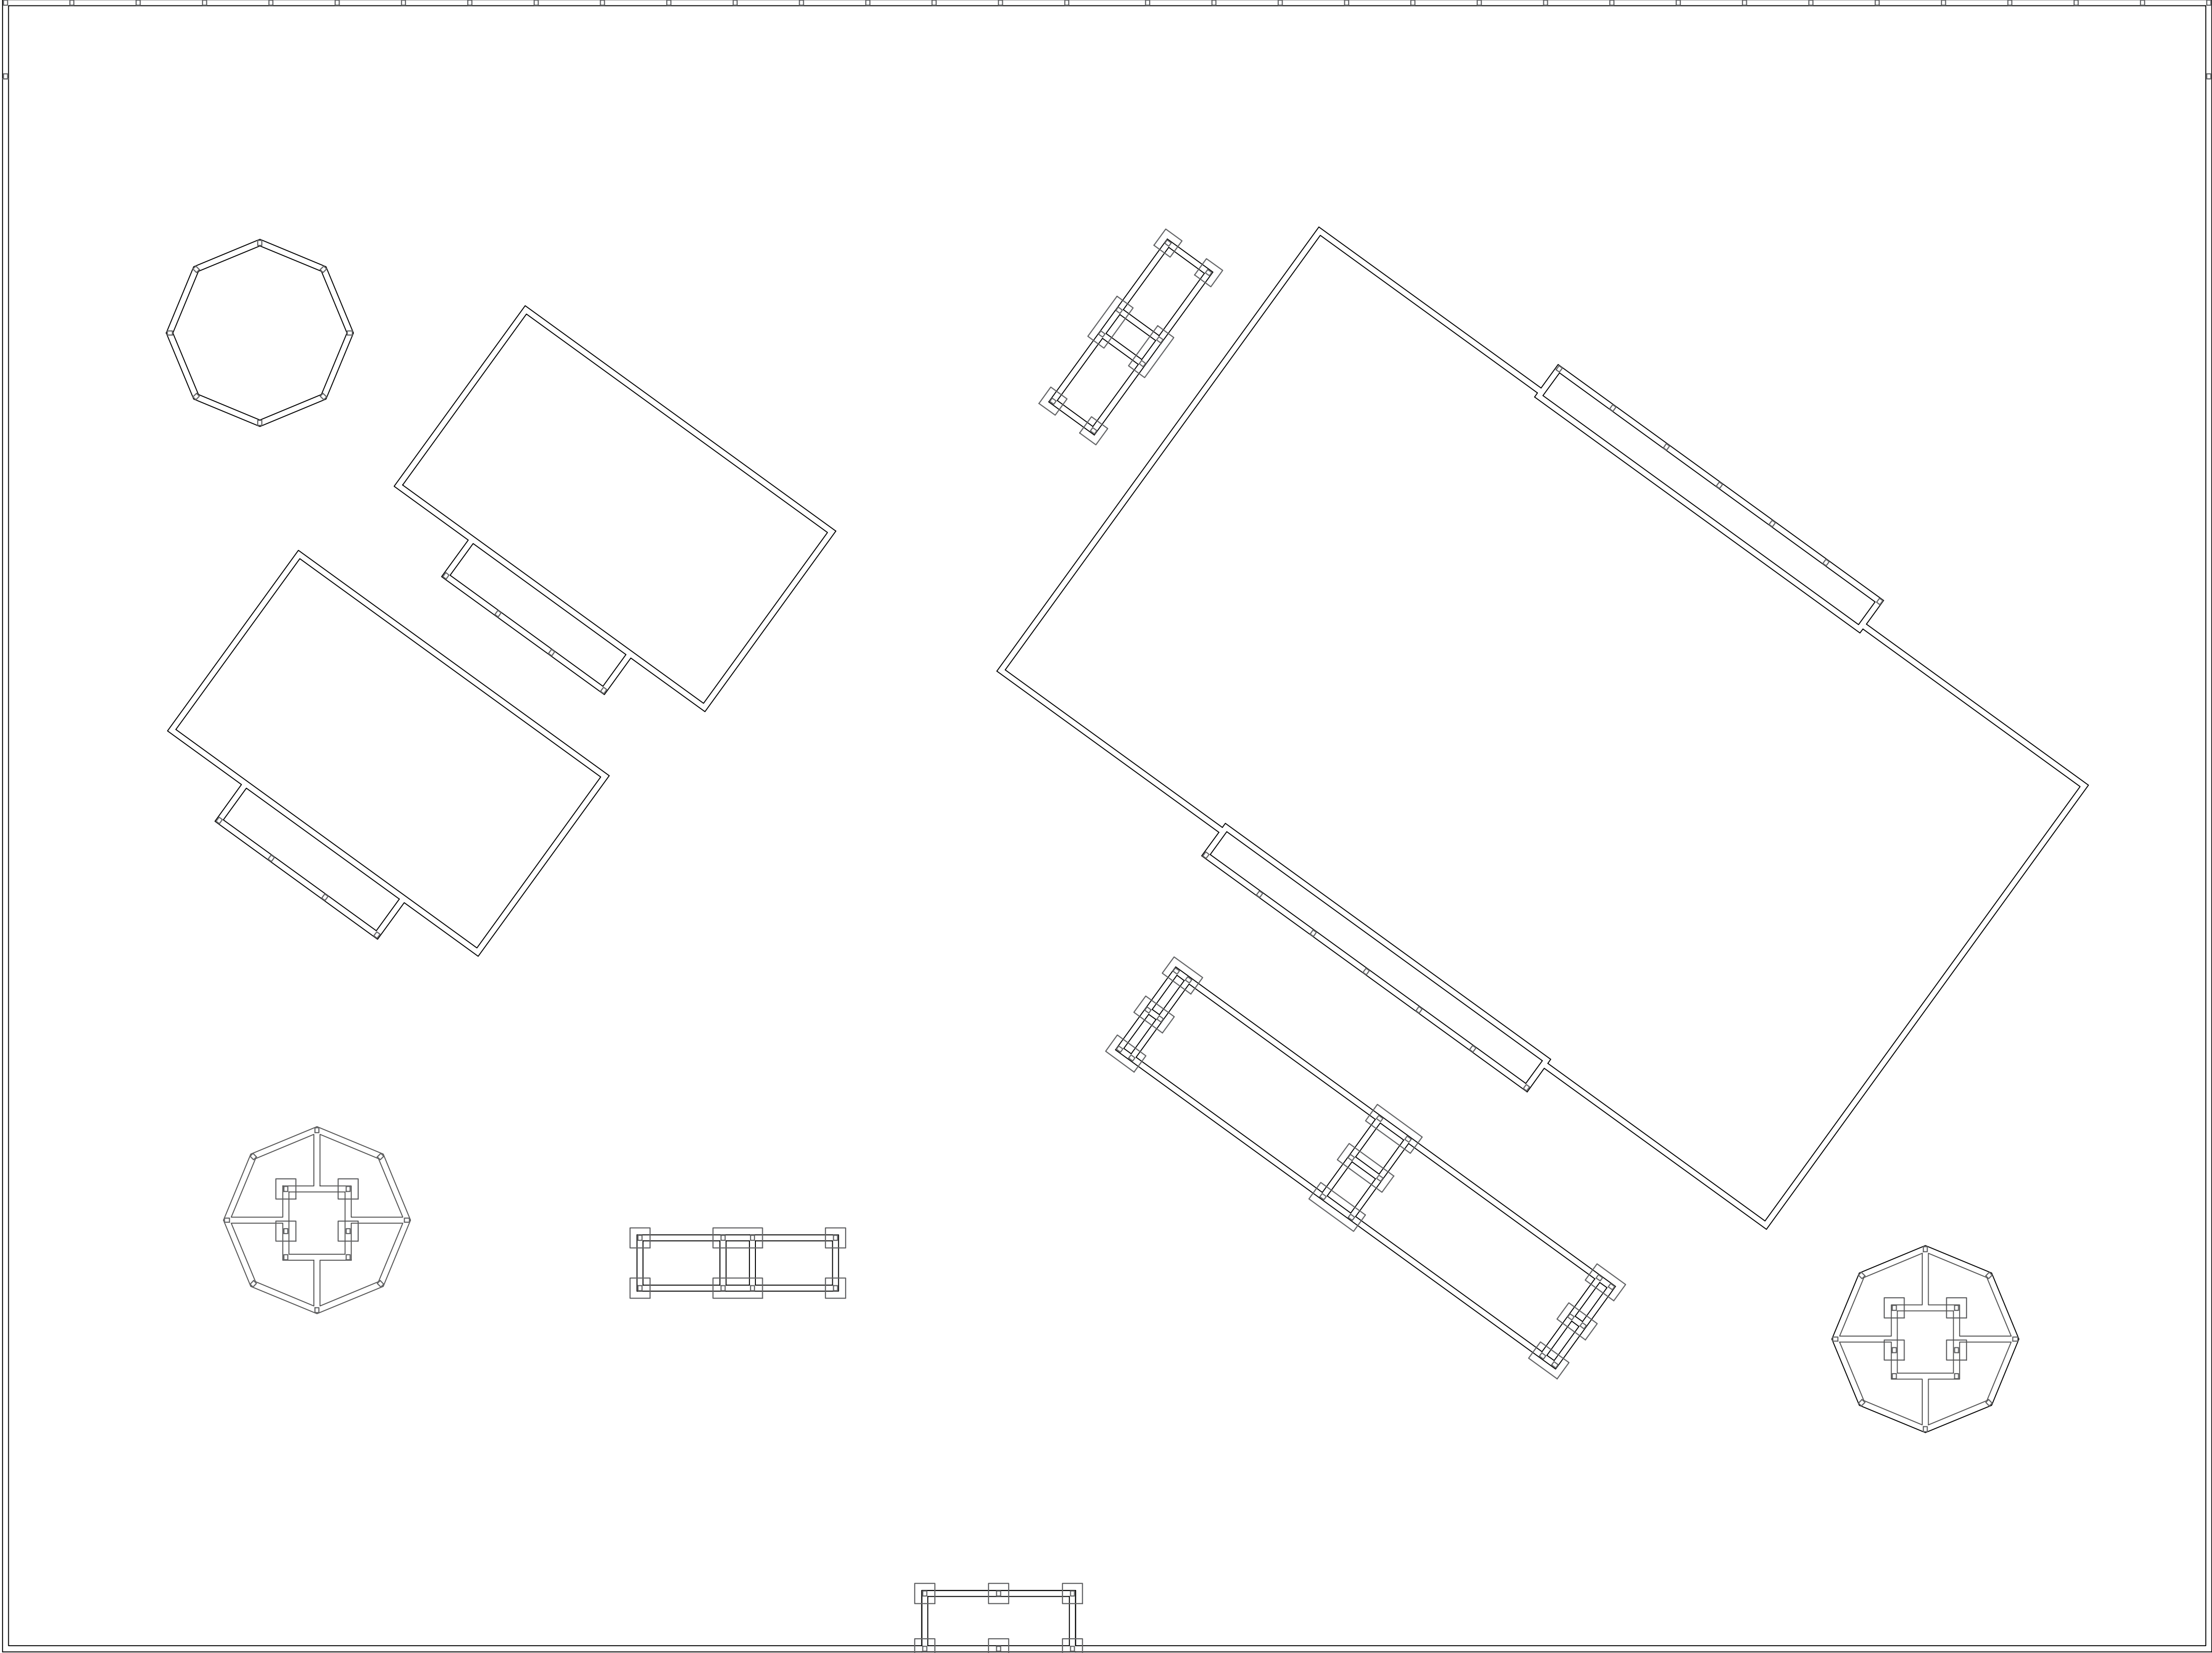

Projeto:

Projeto de Urbanismo Vila Olimpica

Desenhos:

PLANTA BAIXA DE LOCAÇÃO DOS ELEMENTOS ESTRUTURAIS

Observações:

- Conferir todas as medidas em obra antes da execução dos serviços.
- Não executar alterações sem autorização prévia do responsável técnico.
- Qualquer divergência entre projeto e condições de campo deverá ser comunicada ao responsável técnico para análise e aprovação.
- Todas as instalações deverão ser executadas por mão de obra qualificada, seguindo as normas técnicas vigentes e as recomendações dos fabricantes dos materiais empregados.
- O dimensionamento e posicionamentos indicados em projeto prevalecem sobre quaisquer informações complementares aqui descritas.

A locação foi dimensionadas e deverá ser executadas conforme projeto.

Esta prancha apresenta a disposição das sapatas, vigas baldrame e pilares da edificação.

- As vigas baldrame deverão ser executadas conforme dimensões de 0,30m x 0,30m, indicados em projeto estrutural.
- As sapatas deverão ser executadas nas dimensões especificadas, respeitando os níveis de assentamento definidos em projeto.
- Os pilares deverão ser posicionados conforme indicado nesta prancha e detalhados nos respectivos desenhos estruturais.
- Antes da concretagem, deverão ser conferidos alinhamentos, níveis, dimensões, armaduras e cobrimentos.
- O fundo das escavações deverá estar limpo, regularizado e livre de materiais inadequados à fundação.
- Qualquer divergência entre as condições encontradas em campo e as previstas em projeto deverá ser comunicada ao responsável técnico para análise e aprovação.
- Todos os serviços deverão atender às especificações do projeto estrutural e às normas técnicas vigentes.

Projeta:

Fernando Matias Mamede

RESPONSÁVEL TÉCNICO
Fernando Matias Mamede
Engenheiro Civil
Crea: 162056275-8

Proprietário:

Prefeitura Municipal de Coremas

PROPRIETÁRIO(A)

Endereço/Obra:

Rua Francisco Raimundo de Andrade, DNOCS, Coremas - PB, 58770-000

ÁREAS

m²

Área do Terreno10.733,41

Estacionamento519,11

Calçada249,64

Área verde4.281,11

Prancha:

02/14


Logo of Fernando Matias Mamede Engineering

Logo of Prefeitura Municipal de Coremas

Ponto de mercado
(0,00)

S1=S2=S5=S6=S12=S13=S15=S16=S17=S19=S21=S23=S24=S25=S27=S28=S30=S31=S32=S33=S34=S35
100 x 100 cm


S3=S4=S18=S22
100 x 247 cm

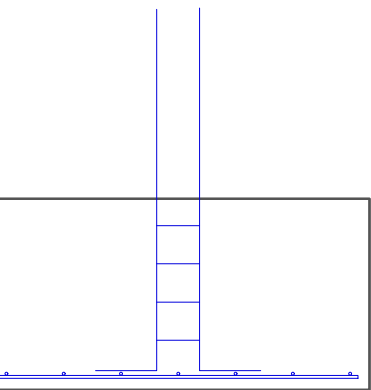

4 N2 - Ø10.0 C= 110




4 N3 - Ø5.0 C= 66

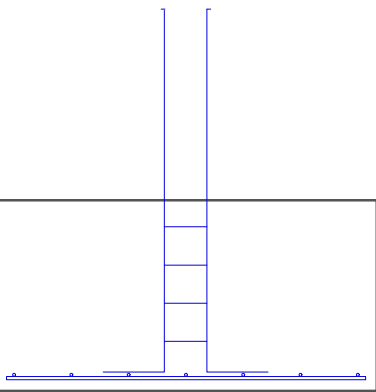


8 N2 - Ø10.0 C= 110




4 N3 - Ø5.0 C= 66

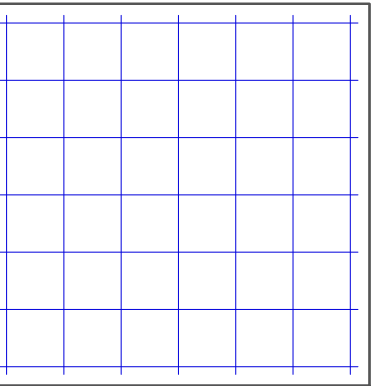

14 N1 - Ø8.0 C= 94

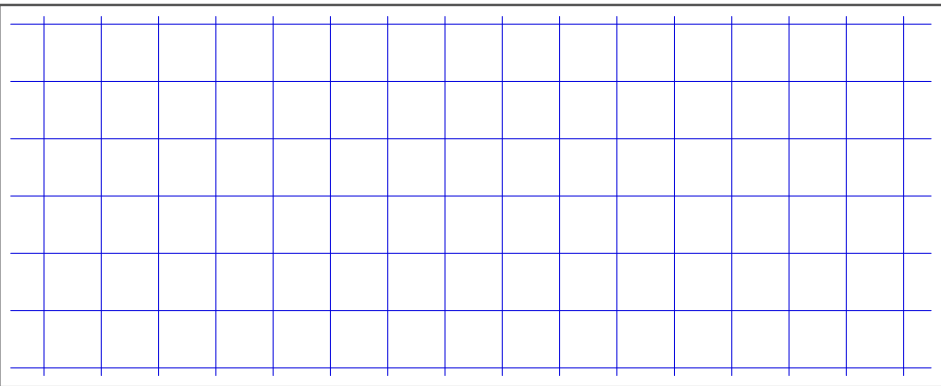


16 N1 - Ø8.0 C= 94

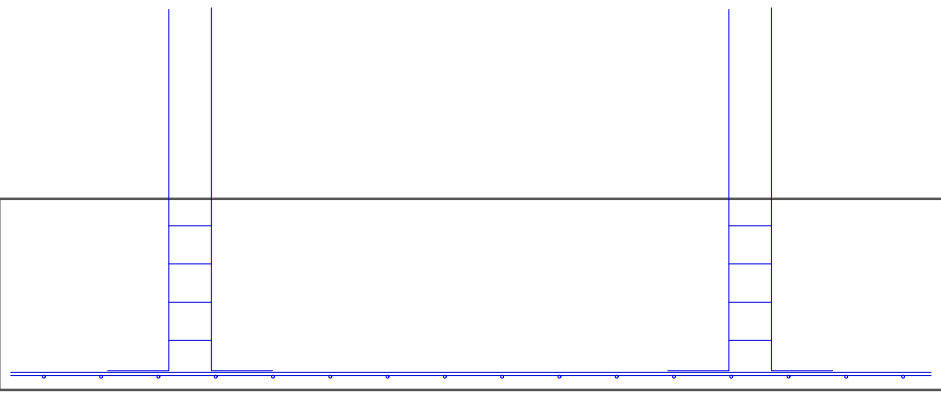

7 N4 - Ø8.0 C= 241


S7=S8=S9=S20=S26=S29
100 x 175 cm

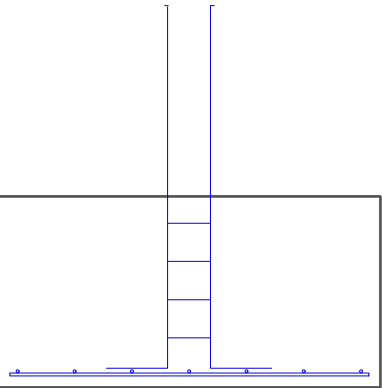


8 N2 - Ø10.0 C= 110



4 N3 - Ø5.0 C= 66

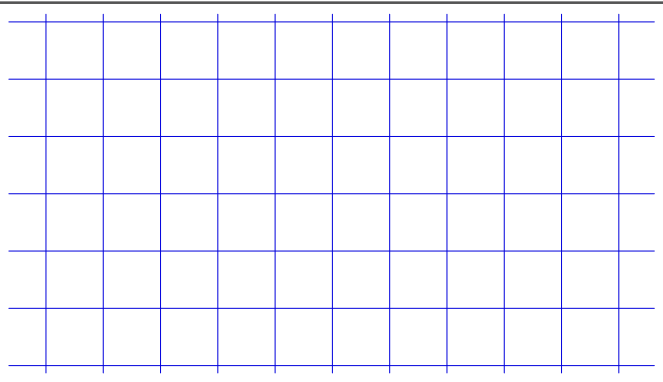


11 N1 - Ø8.0 C= 94

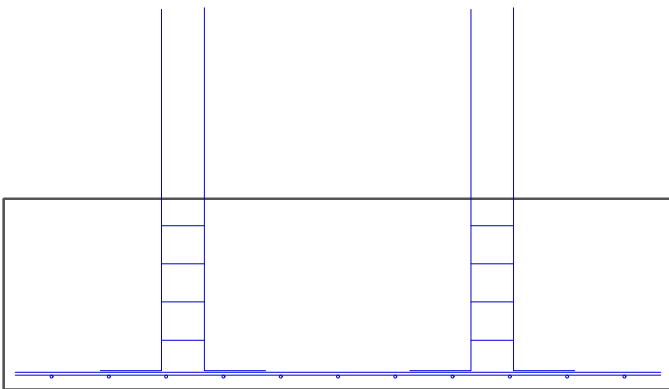

7 N5 - Ø8.0 C= 169


S10=S11=S14
100 x 275 cm

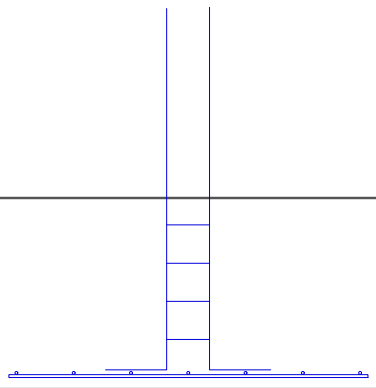


8 N2 - Ø10.0 C= 110



4 N3 - Ø5.0 C= 66

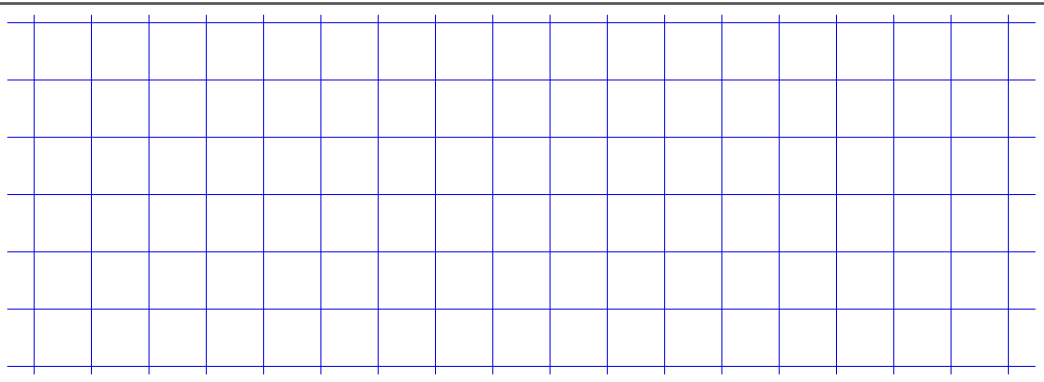

18 N1 - Ø8.0 C= 94

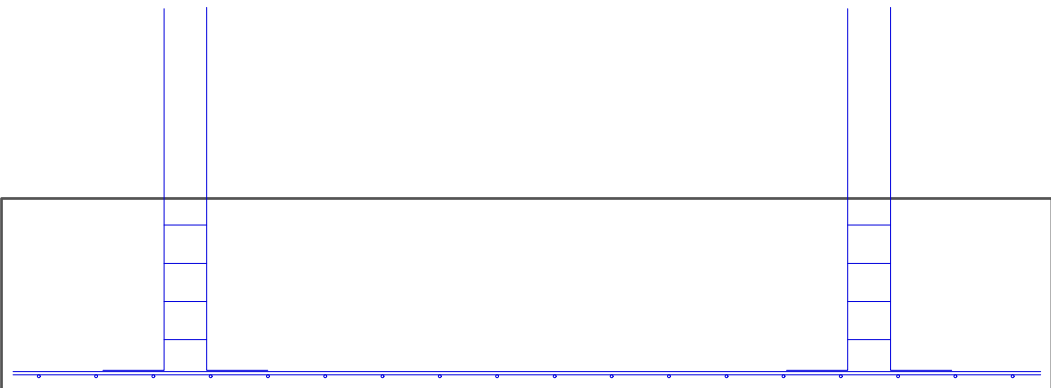

7 N6 - Ø8.0 C= 269

Projeto:

Projeto de Urbanismo Vila Olimpica

Desenhos:

PLANTA BAIXA DE LOCAÇÃO DOS ELEMENTOS ESTRUTURAIS

Observações:

- Conferir todas as medidas em obra antes da execução dos serviços.
- Não executar alterações sem autorização prévia do responsável técnico.
- Qualquer divergência entre projeto e condições de campo deverá ser comunicada ao responsável técnico para análise e aprovação.
- Todas as instalações deverão ser executadas por mão de obra qualificada, seguindo as normas técnicas vigentes e as recomendações dos fabricantes dos materiais empregados.
- O dimensionamento e posicionamentos indicados em projeto prevalecem sobre quaisquer informações complementares aqui descritas.

Esta prancha apresenta os detalhamentos das sapatas da edificação, contendo dimensões, níveis, armaduras e demais informações necessárias para sua execução.

- Todas as sapatas deverão ser executadas rigorosamente conforme as dimensões indicadas nos detalhamentos.
- As armaduras deverão ser montadas conforme bitolas, quantidades, espaçamentos, comprimentos de ancoragem e dobramentos especificados em projeto.
- Deverão ser respeitados os cobrimentos mínimos das armaduras conforme especificado no projeto estrutural e nas normas técnicas vigentes.
- Os arranques dos pilares deverão ser posicionados e fixados conforme os detalhamentos apresentados.
- Antes da concretagem, deverão ser conferidas as dimensões das formas, posicionamento das armaduras, cobrimentos, arranques e níveis de assentamento.
- O fundo das escavações deverá estar limpo, regularizado e livre de materiais orgânicos ou inadequados.
- Não será permitida a concretagem sem a prévia conferência das armaduras e das dimensões indicadas em projeto.
- Qualquer divergência identificada em campo deverá ser comunicada ao responsável técnico para análise e aprovação.
- Todos os serviços deverão atender às especificações do projeto estrutural e às normas técnicas vigentes.

Projetista:

Fernando Matias Mamede

RESPONSÁVEL TÉCNICO
Fernando Matias Mamede
Engenheiro Civil
Crea: 162056275-6

Proprietário:

Prefeitura Municipal de Coremas

PROPRIETÁRIO(A)


Endereço/Obra: Rua Francisco Raimundo de Andrade, DNOCS, Coremas - PB, 58770-000

ÁREAS	m²
Área do Terreno	10.733,41
Estacionamento	519,11
Calçada	249,64
Área verde	4.281,11


Prancha:

03/14


P1 = P2 = P3 = P4 = P5 = P6 = P7 = P8 = P9 = P10 = P11 = P12 = P13 = P14 = P15 = P16 = P17 = P18 = P19 = P20 = P21 = P22 = P23 = P24 = P25 = P26 = P27 = P28 = P29 = P30 = P31 = P32 = P33 = P34 = P35 = P36
20 x 20 cm

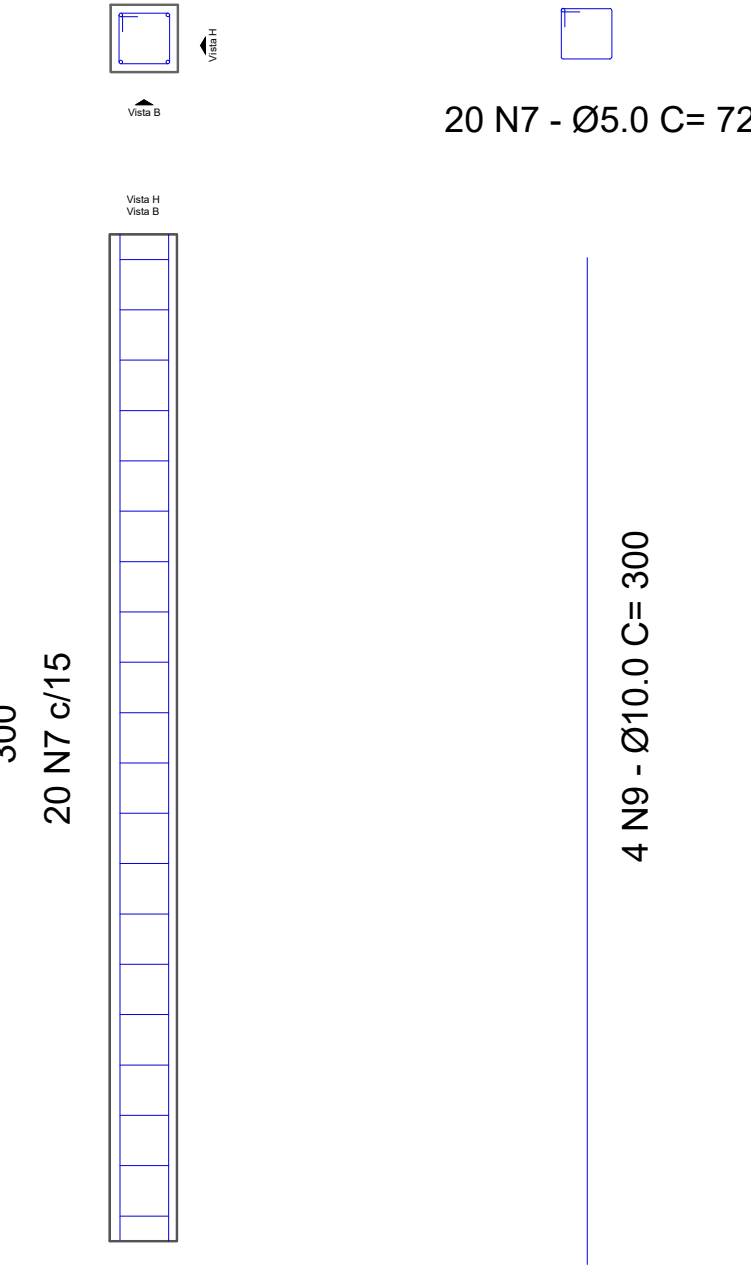


P37 = P39 = P40 = P43 = P44 = P49 = P50 = P53 = P82 = P84 = P85 = P92 = P93 = P100 = P103 = P104 = P106 = P107 = P116 = P119 = P120 = P127 = P128 = P129
20 x 25 cm

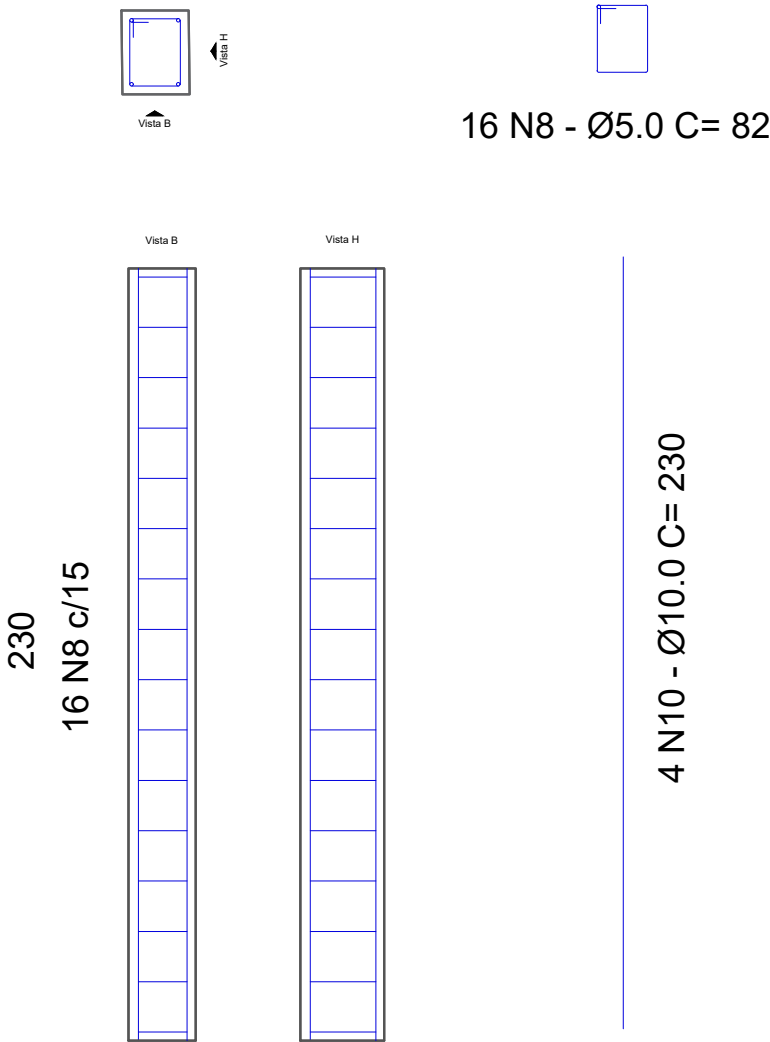


P88 = P89 = P101 = P102 = P114 = P115 = P125 = P126
20 x 25 cm

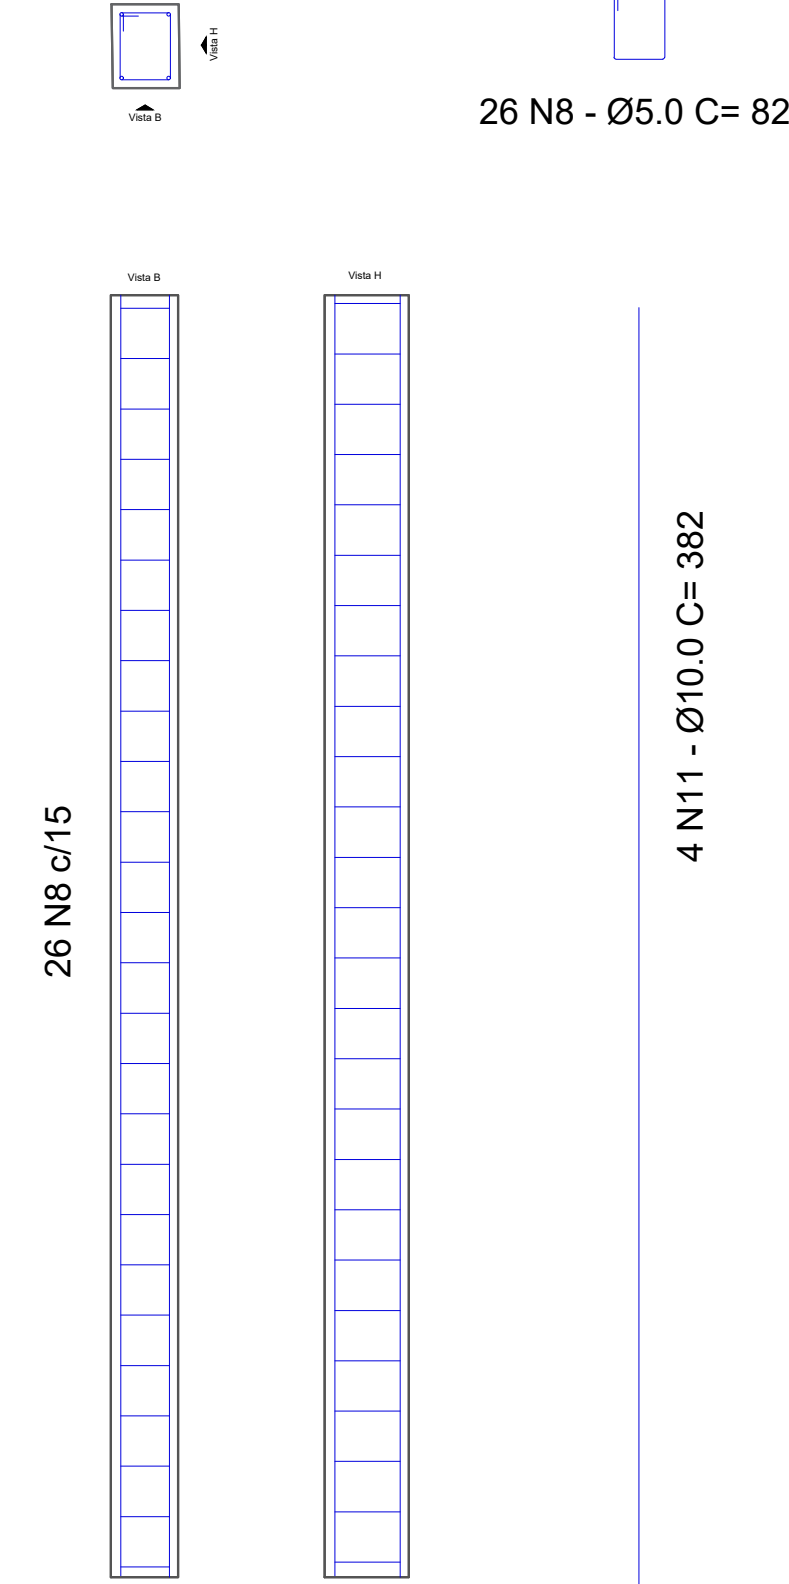


P94 = P95 = P121 = P122
20 x 25 cm

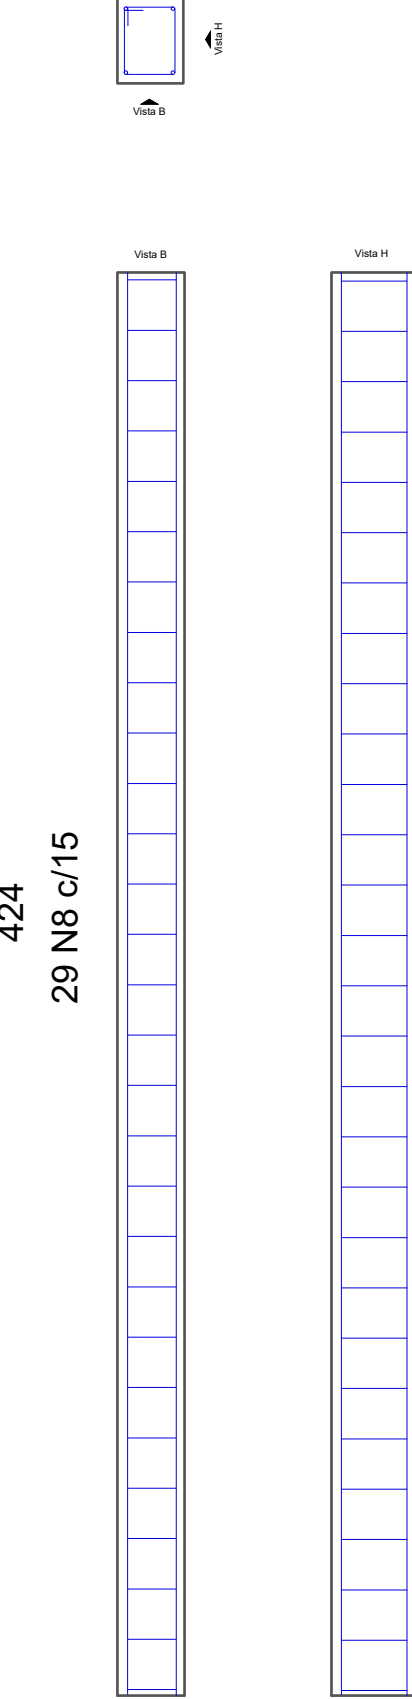


P38 = P41 = P42 = P45 = P46 = P47 = P51 = P54 = P96 = P97 = P98 = P99 = P110 = P111 = P112 = P113
20 x 25 cm

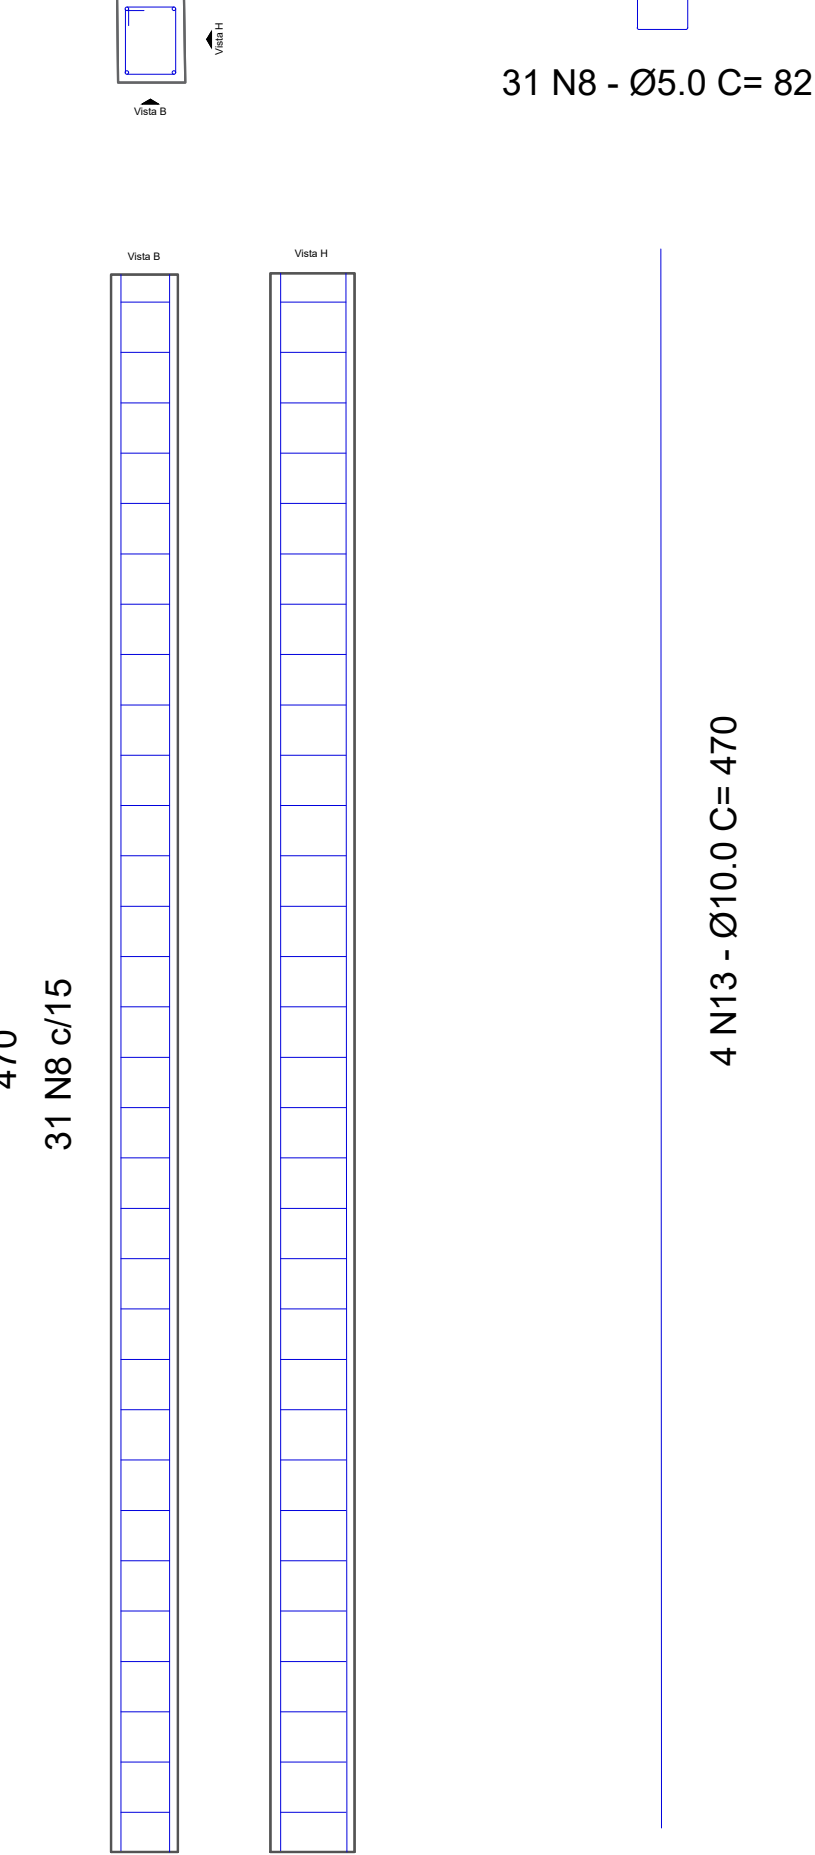


P48 = P52 = P55 = P56 = P57 = P58 = P59 = P60 = P61 = P62 = P63 = P64 = P65 = P66 = P67 = P68 = P69 = P70 = P72 = P74 = P77 = P80
20 x 25 cm

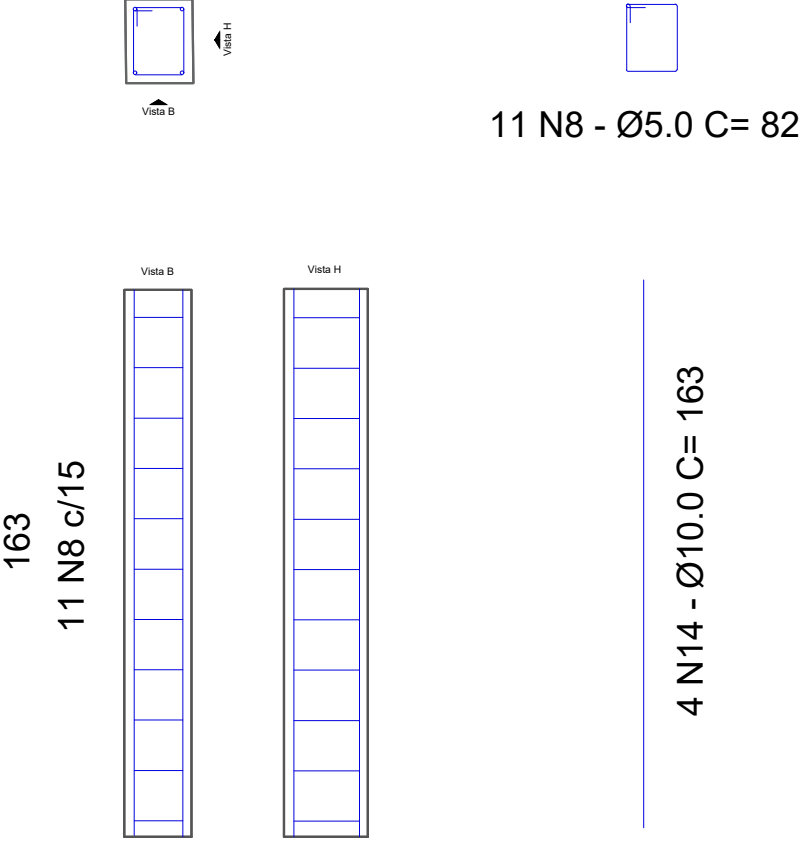


P71 = P773 = P75 = P76 = P78 = P79 = P105 = P109 = P117 = P118 = P123 = P124
20 x 25 cm

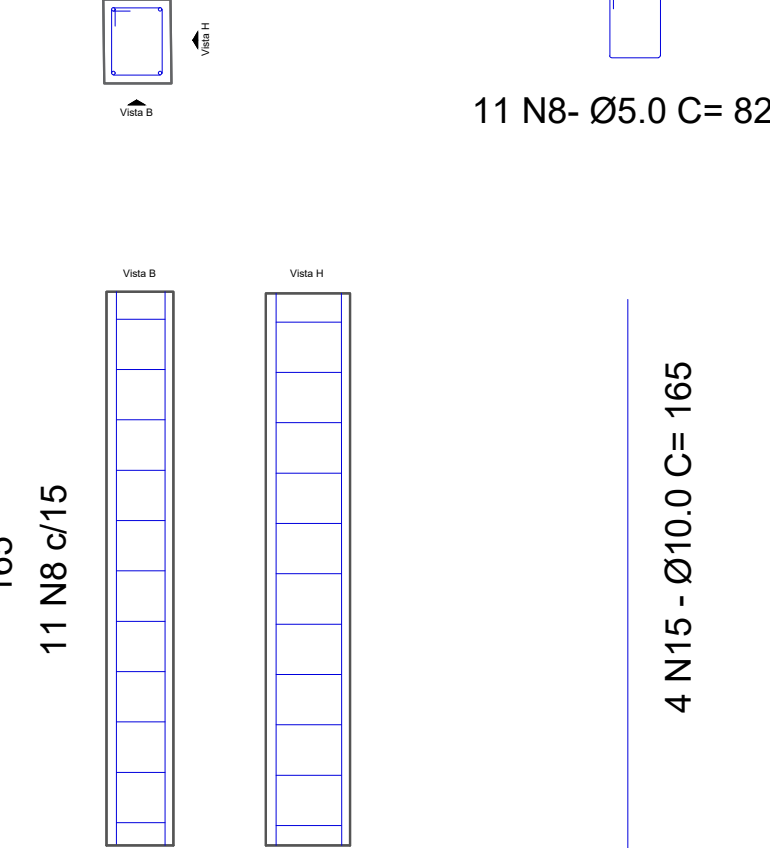


P81 = P83 = P86 = P87 = P90 = P91
20 x 25 cm

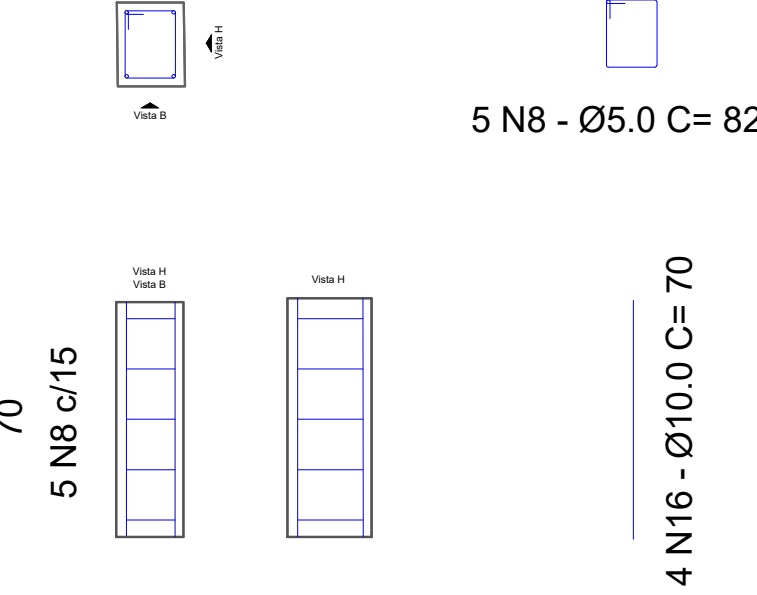

P130 = P131 = P133 = P134
20 x 25 cm

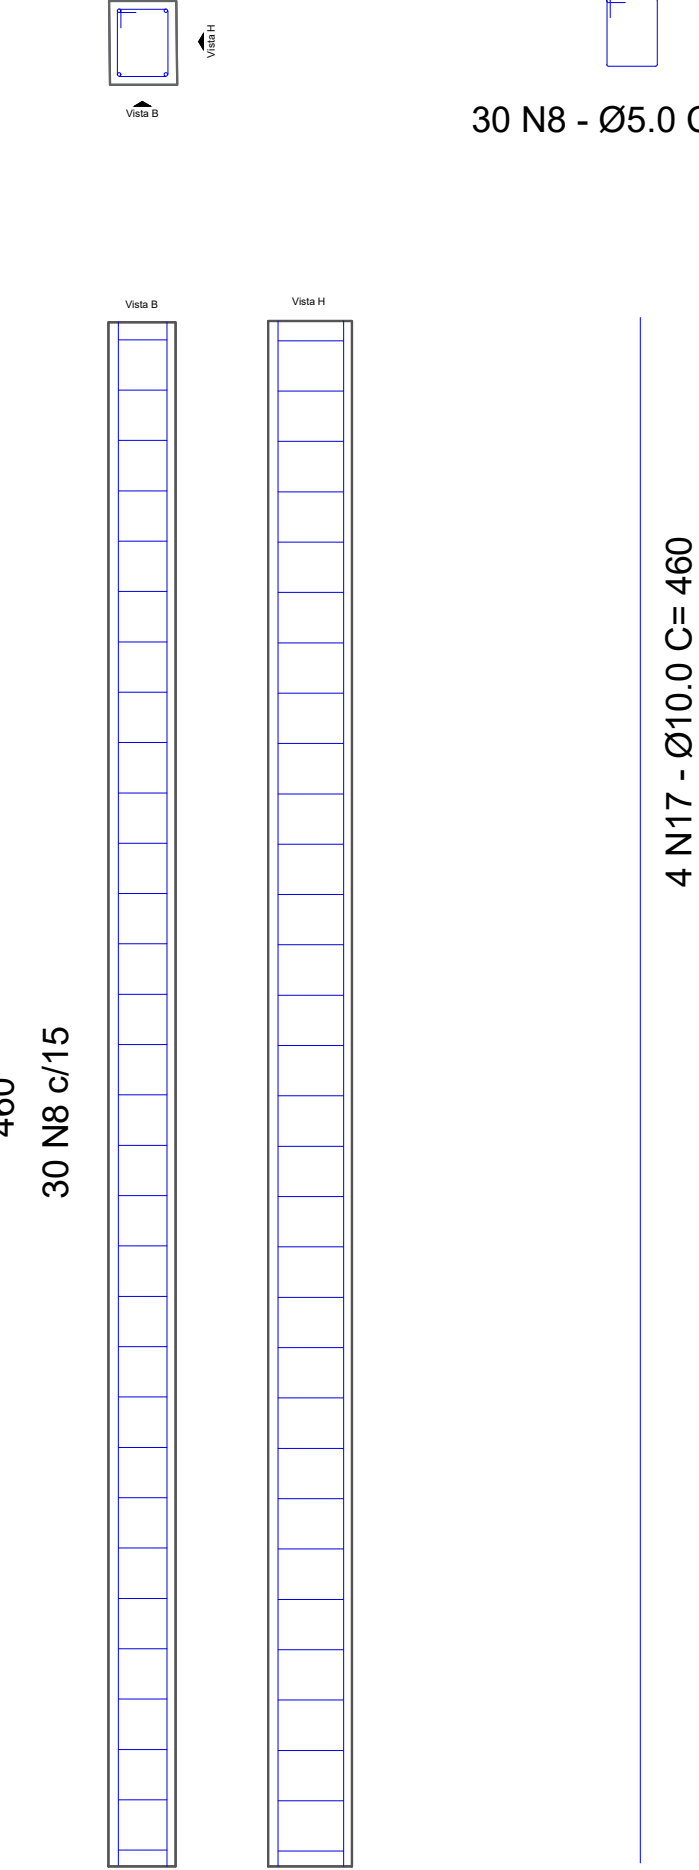

P132 = P135
20 x 25 cm

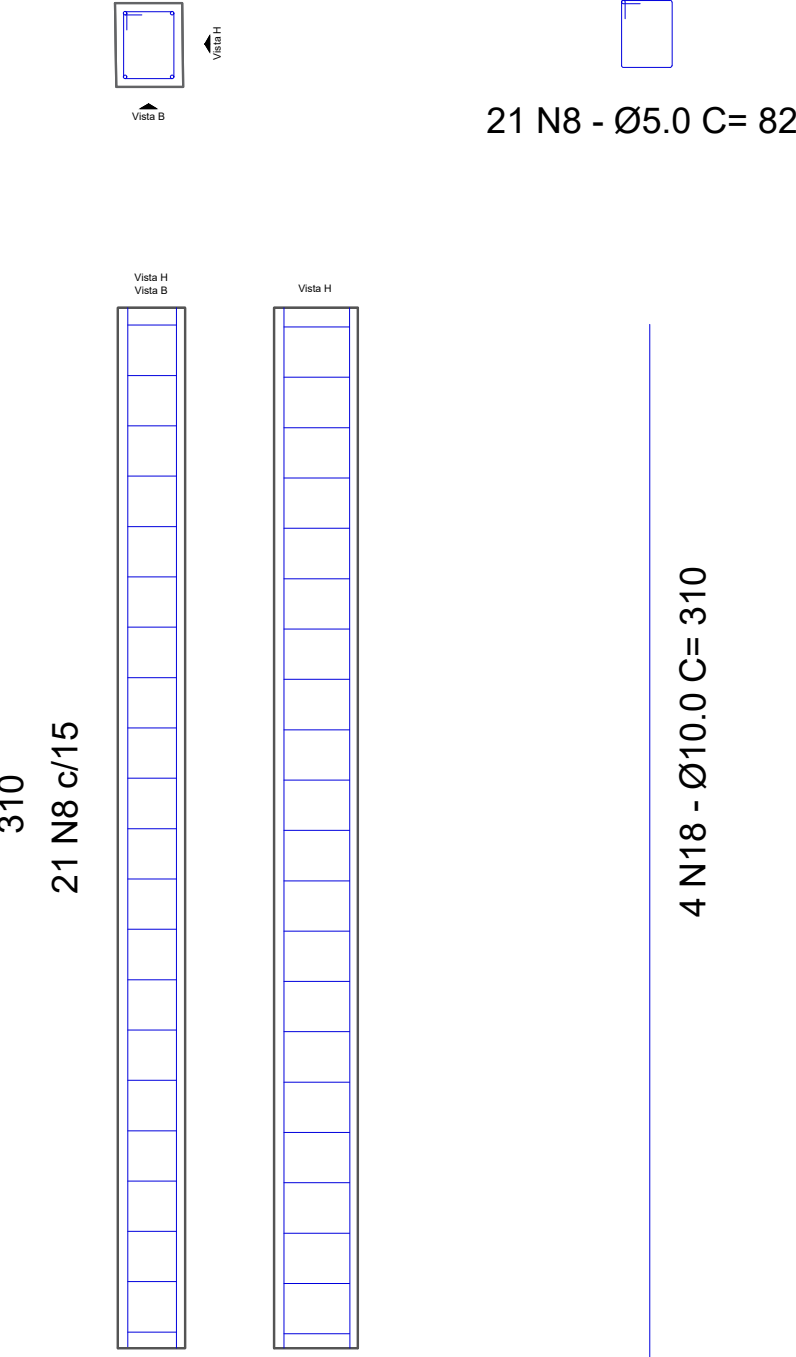

Projeto:

Projeto de Urbanismo Vila Olimpica

Desenhos:

PLANTA BAIXA DE LOCAÇÃO DOS ELEMENTOS ESTRUTURAIS

Observações:

- Conferir todas as medidas em obra antes da execução dos serviços.
- Não executar alterações sem autorização prévia do responsável técnico.
- Qualquer divergência entre projeto e condições de campo deverá ser comunicada ao responsável técnico para análise e aprovação.
- Todas as instalações deverão ser executadas por mão de obra qualificada, seguindo as normas técnicas vigentes e as recomendações dos fabricantes dos materiais empregados.
- O dimensionamento e posicionamentos indicados em projeto prevalecem sobre quaisquer informações complementares aqui descritas.

Esta prancha apresenta os detalhamentos dos pilares da edificação, contendo dimensões, armaduras longitudinais, armaduras transversais (estribos), emendas e demais informações necessárias para sua execução.

- Todos os pilares deverão ser executados rigorosamente conforme as dimensões indicadas nos detalhamentos estruturais.
- As armaduras longitudinais deverão ser montadas conforme as bitolas, quantidades, comprimentos de ancoragem e posicionamentos especificados em projeto.
- Os estribos deverão ser executados conforme diâmetros, espaçamentos, dimensões e dobramentos indicados nos detalhamentos.
- Deverão ser respeitados os cobrimentos mínimos das armaduras conforme especificado em projeto e nas normas técnicas vigentes.
- As emendas, transpasse das barras e ancoragens deverão seguir rigorosamente as especificações apresentadas nos detalhamentos estruturais.
- Os pilares deverão ser posicionados conforme os eixos estruturais definidos em projeto.
- Antes da concretagem, deverão ser conferidos alinhamento, prumo, dimensões das formas, posicionamento das armaduras, espaçamento dos estribos, cobrimentos e locação dos arranques.
- Não será permitida a alteração das armaduras, dimensões ou posicionamento dos pilares sem autorização do responsável técnico.
- Qualquer divergência identificada em campo deverá ser comunicada ao responsável técnico para análise e aprovação.
- Todos os serviços deverão atender às especificações do projeto estrutural e às normas técnicas vigentes.

Projetista:

Fernando Matias Mamede

RESPONSÁVEL TÉCNICO
Fernando Matias Mamede
Engenheiro Civil
Crea: 162056275-6

Proprietário:

Prefeitura Municipal de Coremas

PROPRIETÁRIO(A)


Endereço/Obra: Rua Francisco Raimundo de Andrade, DNOCS, Coremas - PB, 58770-000

ÁREAS
Área do Terreno 10.733,41
Estacionamento 519,11
Calçada 249,64
Área verde 4.281,11


Prancha:

04/14


V1=V2=V3
15 x 25 cm

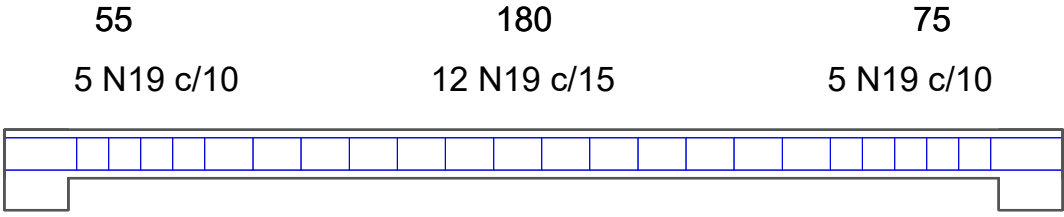


V4=V5
15 x 25 cm

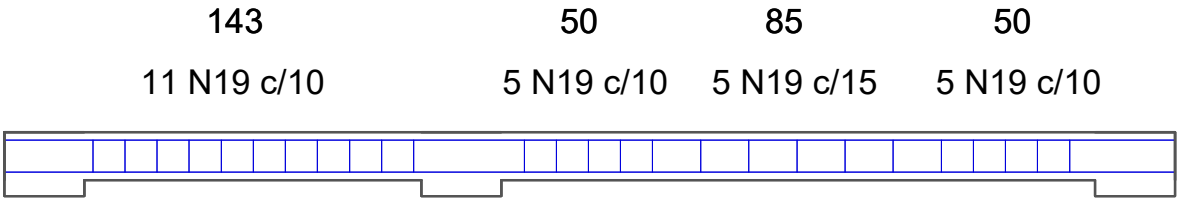


V6=V10
15 x 25 cm

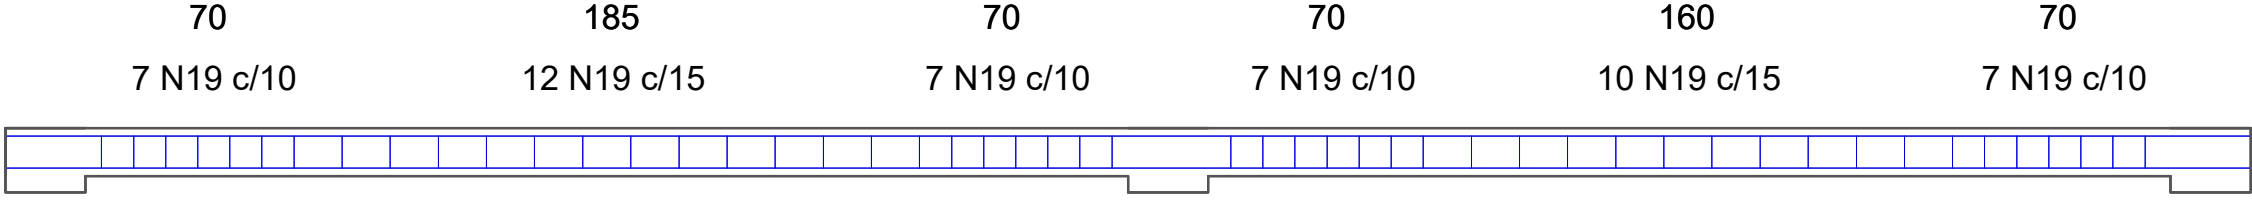


V7=V8=V9
15 x 25 cm

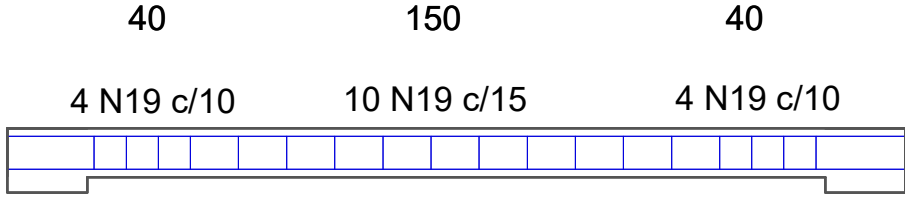


V12=V13
15 x 25 cm

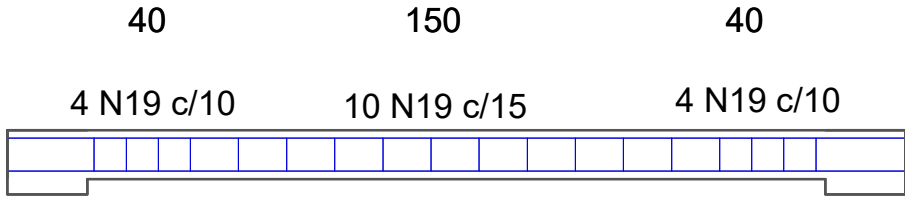


V11=V14
15 x 30 cm

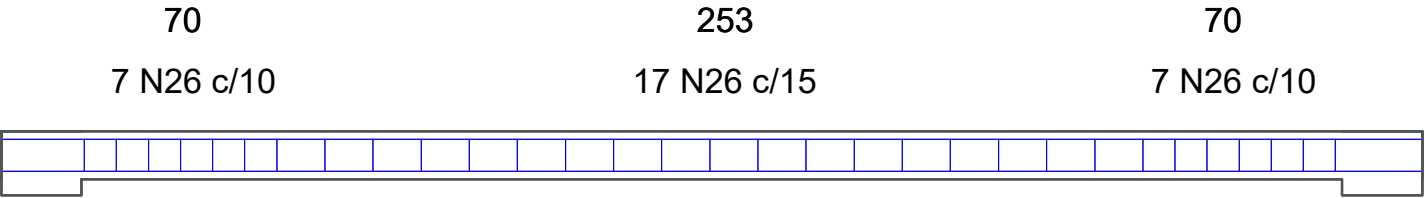


QUIOSQUE

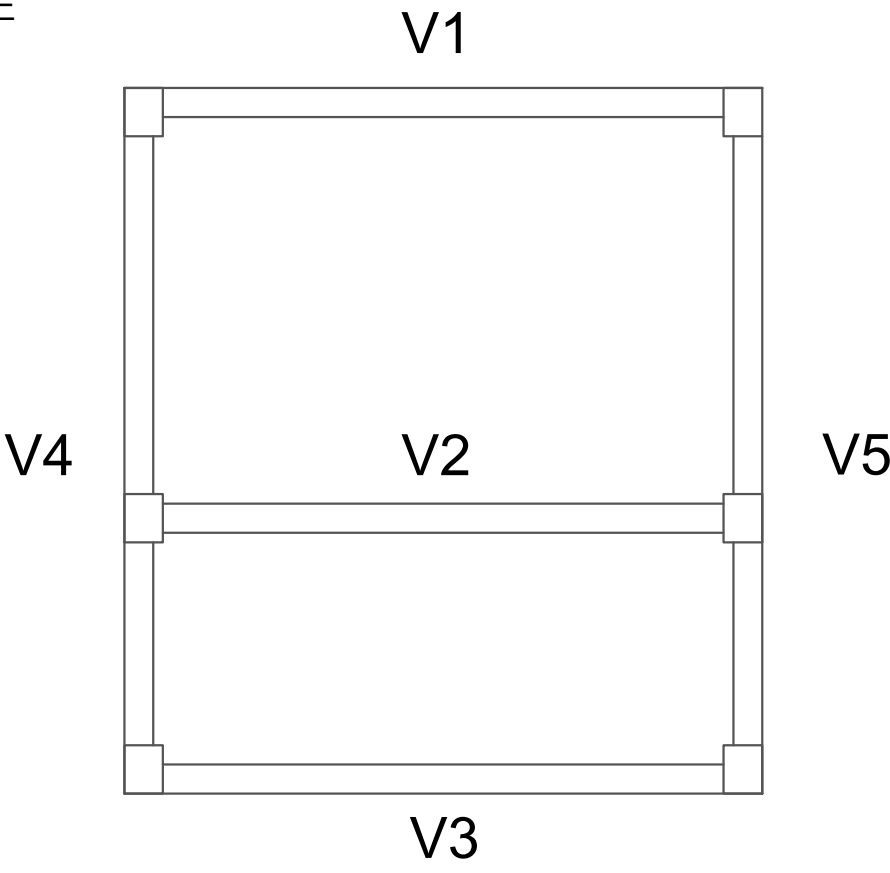

GUARITA

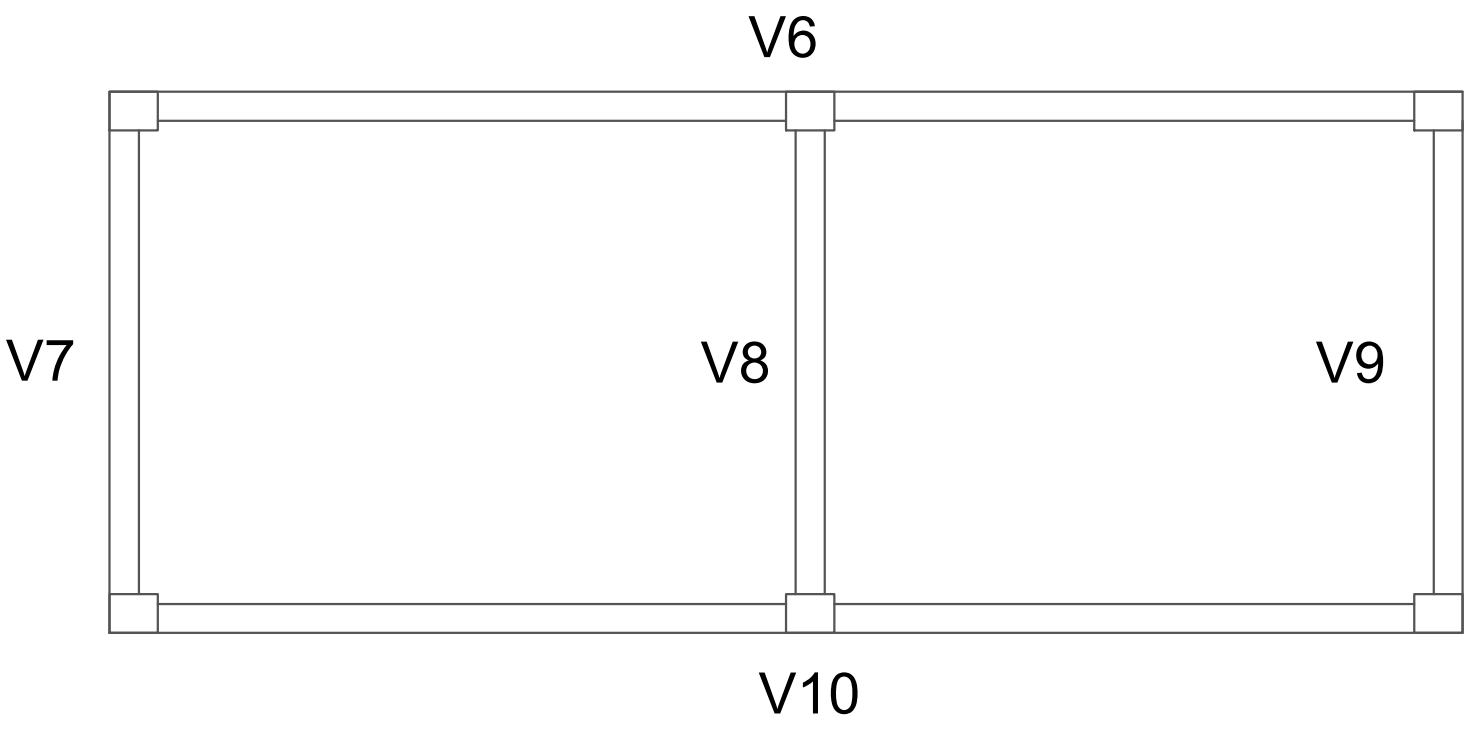

BANHEIROS

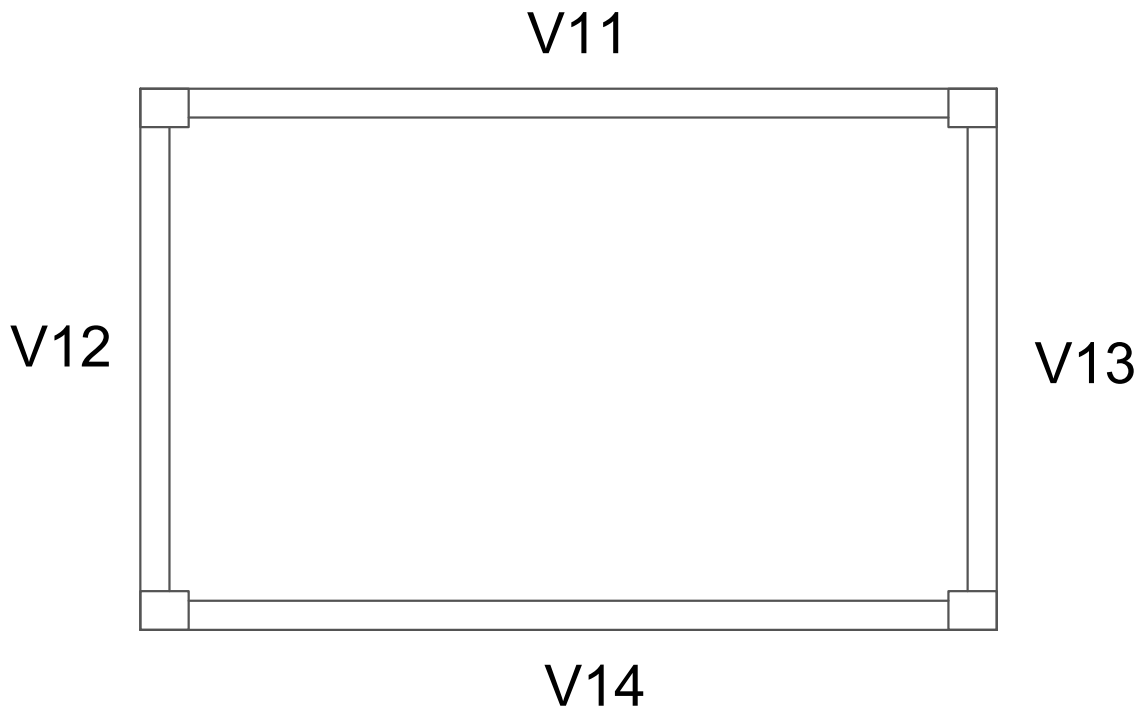

Projeto:

Projeto de Urbanismo Vila Olimpica

Desenhos:

PLANTA BAIXA DE LOCAÇÃO DOS ELEMENTOS ESTRUTURAIS

Observações:

- Conferir todas as medidas em obra antes da execução dos serviços.
- Não executar alterações sem autorização prévia do responsável técnico.
- Qualquer divergência entre projeto e condições de campo deverá ser comunicada ao responsável técnico para análise e aprovação.
- Todas as instalações deverão ser executadas por mão de obra qualificada, seguindo as normas técnicas vigentes e as recomendações dos fabricantes dos materiais empregados.
- O dimensionamento e posicionamentos indicados em projeto prevalecem sobre quaisquer informações complementares aqui descritas.

Esta prancha apresenta os detalhamentos das vigas da edificação, contendo dimensões, armaduras longitudinais, armaduras transversais (estribos), ancoragens, emendas e demais informações necessárias para sua execução.

- Todas as vigas deverão ser executadas rigorosamente conforme as dimensões indicadas nos detalhamentos estruturais.
- As armaduras longitudinais superiores e inferiores deverão ser montadas conforme as bitolas, quantidades, comprimentos, ancoragens e posicionamentos especificados em projeto.
- Os estribos deverão ser executados conforme diâmetros, espaçamentos, dimensões e dobramentos indicados nos detalhamentos.
- Deverão ser respeitados os cobrimentos mínimos das armaduras conforme especificado em projeto e nas normas técnicas vigentes.
- As emendas, transpasse das barras e ancoragens deverão seguir rigorosamente as especificações apresentadas nos detalhamentos estruturais.
- As passagens de tubulações, eletrodutos ou quaisquer outros elementos através das vigas somente poderão ser executadas quando previstas em projeto ou autorizadas pelo responsável técnico.
- Antes da concretagem, deverão ser conferidos alinhamento, nivelamento, dimensões das formas, posicionamento das armaduras, espaçamento dos estribos, cobrimentos e demais elementos previstos em projeto.
- Não será permitida a alteração das armaduras, dimensões ou posicionamento das vigas sem autorização do responsável técnico.
- Qualquer divergência identificada em campo deverá ser comunicada ao responsável técnico para análise e aprovação.
- Todos os serviços deverão atender às especificações do projeto estrutural e às normas técnicas vigentes.

Projetista:

Fernando Matias Mamede

RESPONSÁVEL TÉCNICO
Fernando Matias Mamede
Engenheiro Civil
Crea: 162056275-6



Proprietário:

Prefeitura Municipal de Coremas



PROPRIETÁRIO(A)


Endereço/Obra: Rua Francisco Raimundo de Andrade, DNOCS, Coremas - PB, 58770-000

ÁREAS	m²
Área do Terreno	10.733,41
Estacionamento	519,11
Calçada	249,64
Área verde	4.281,11


Prancha:

05/14



QUIOSQUE

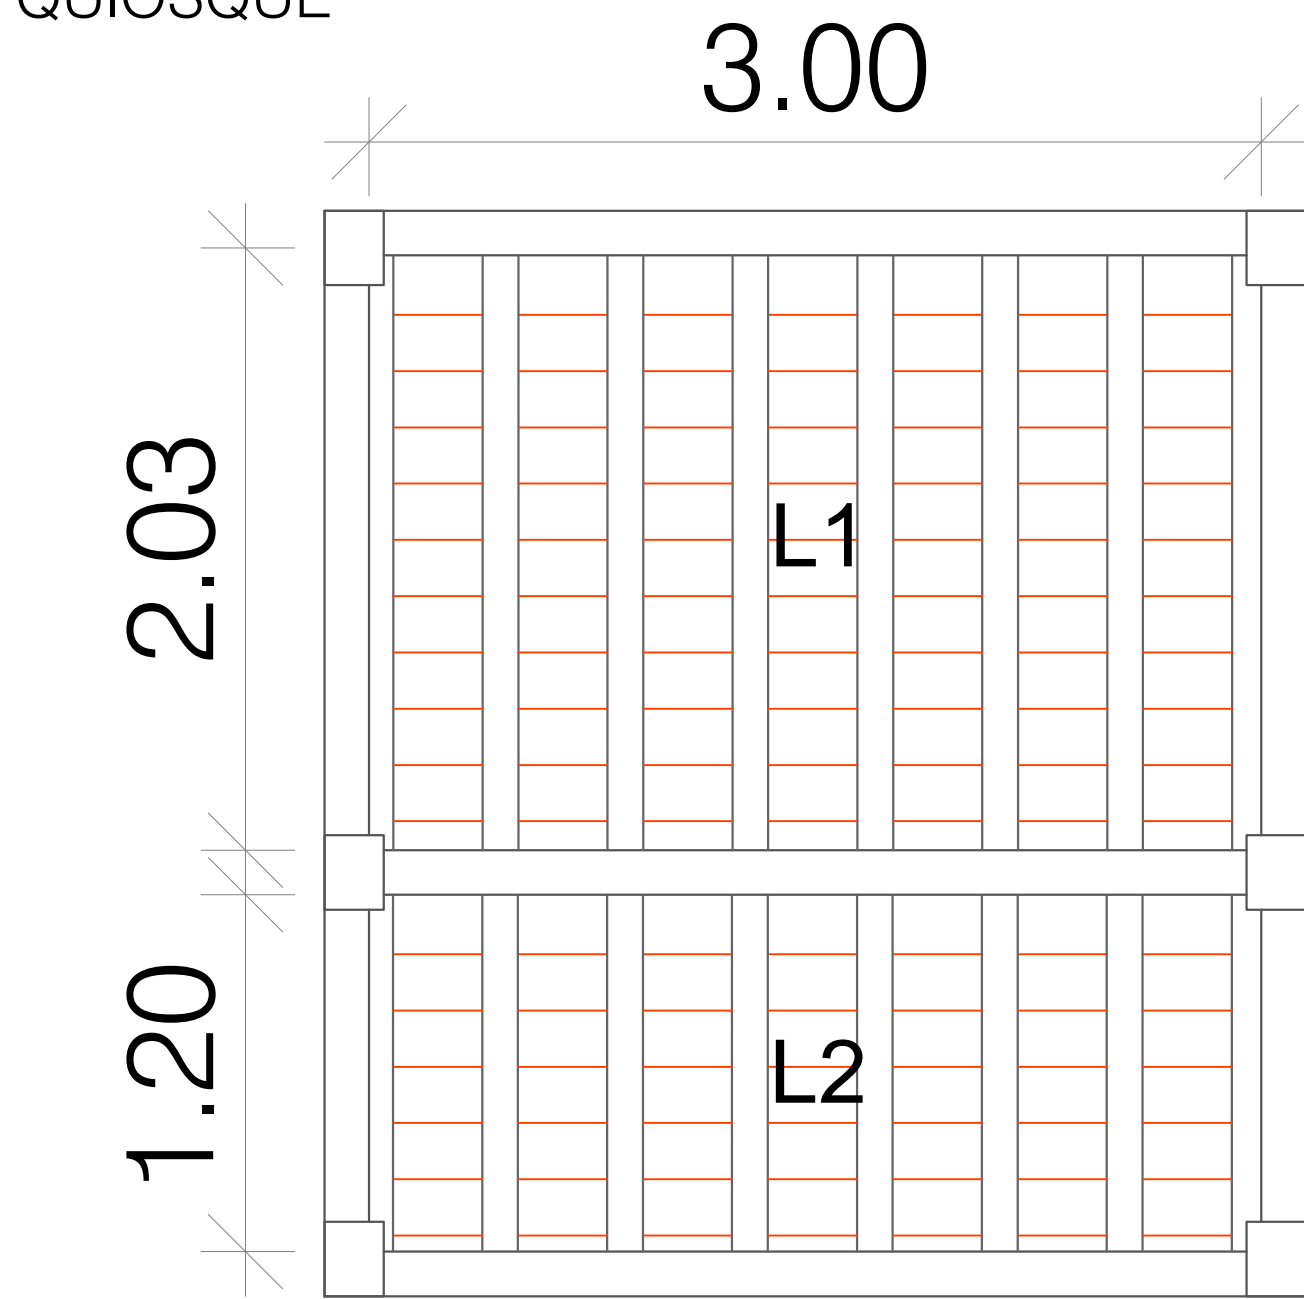

GUARITA

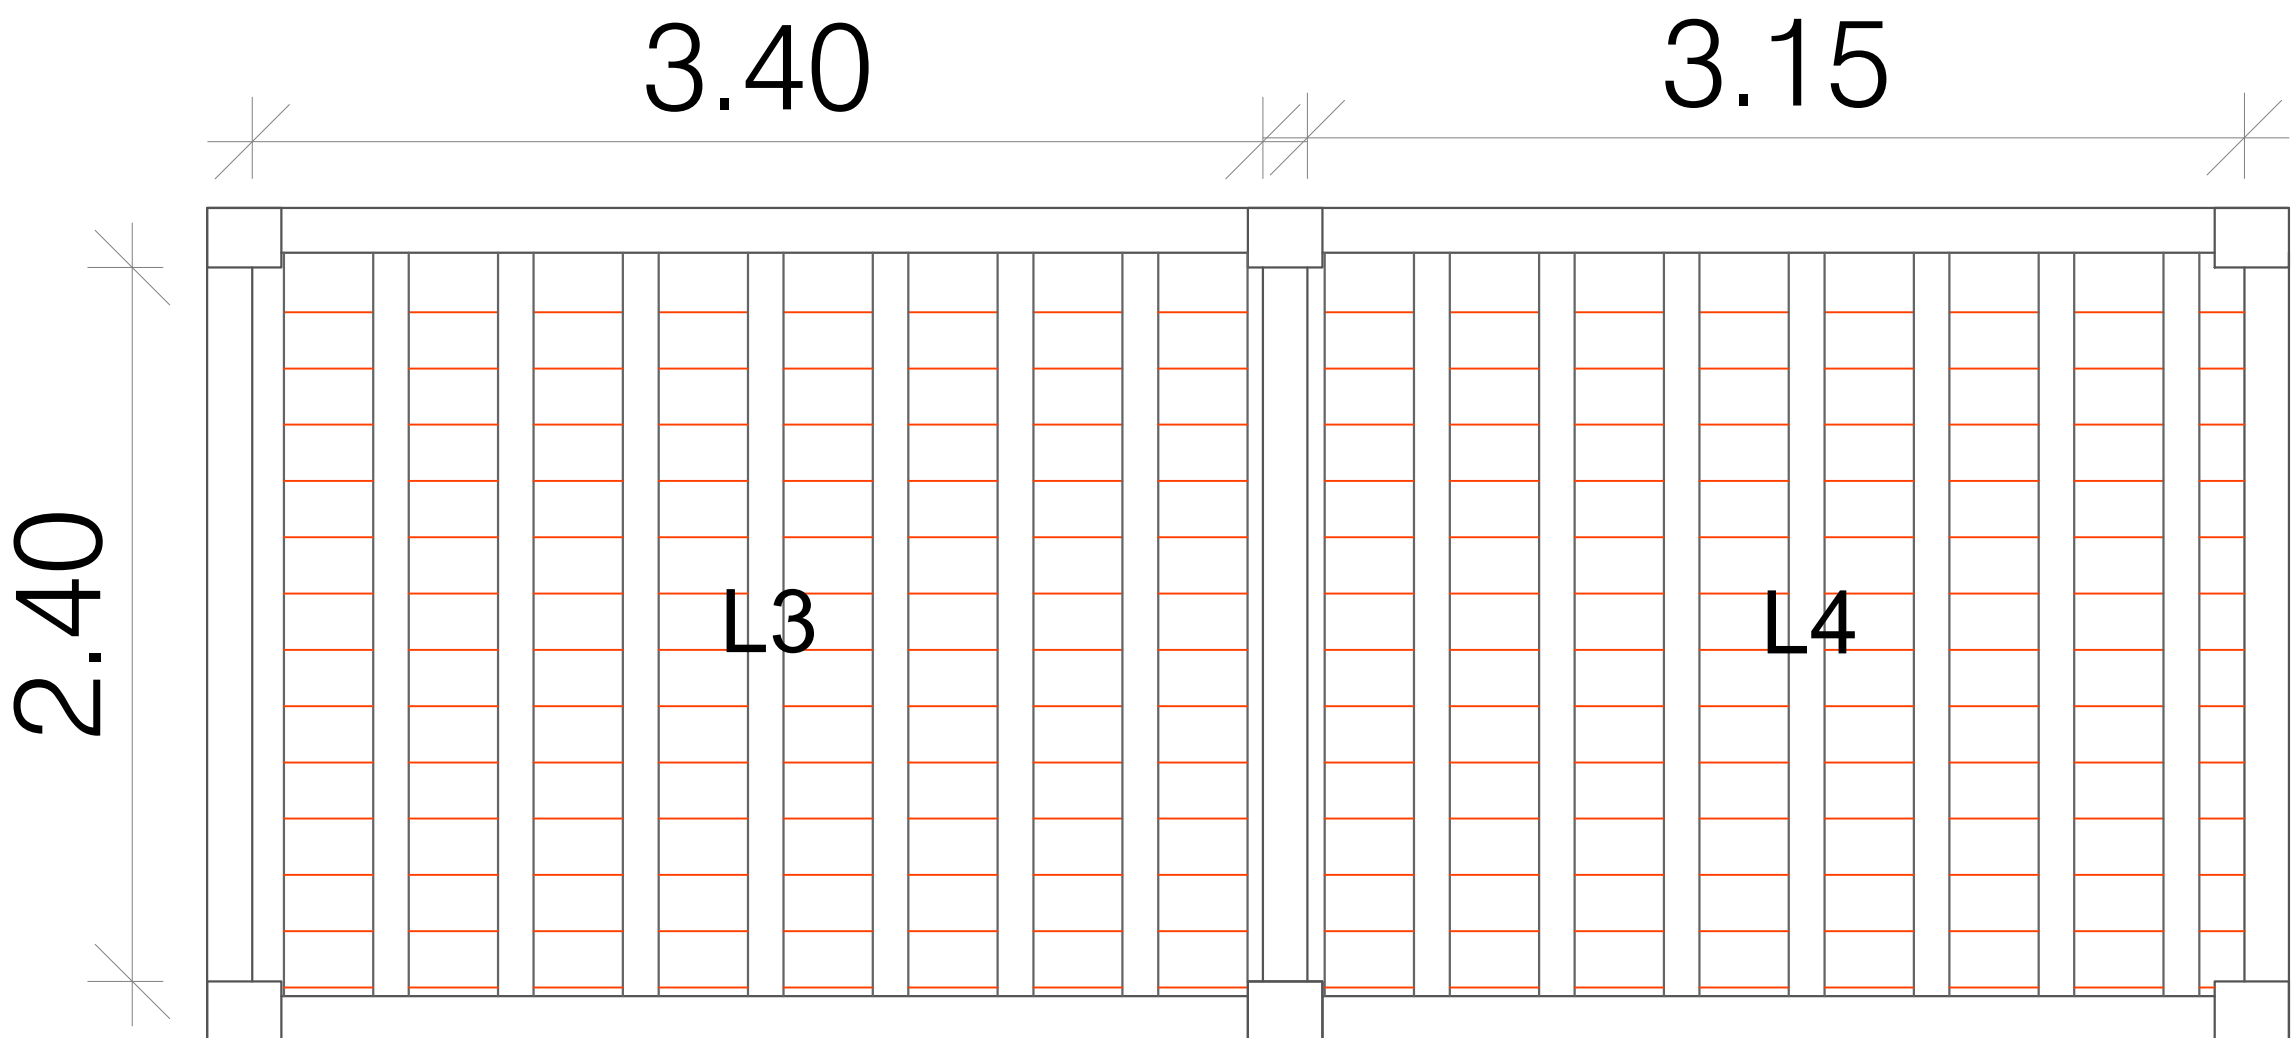

BANHEIROS

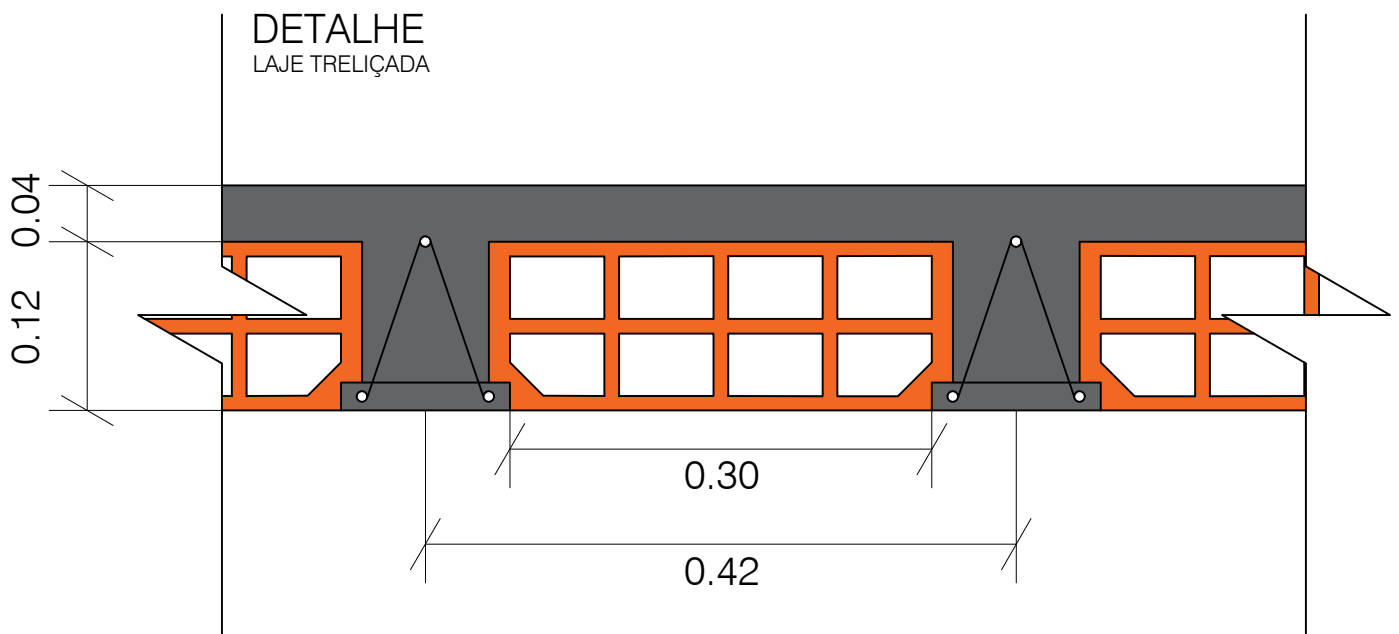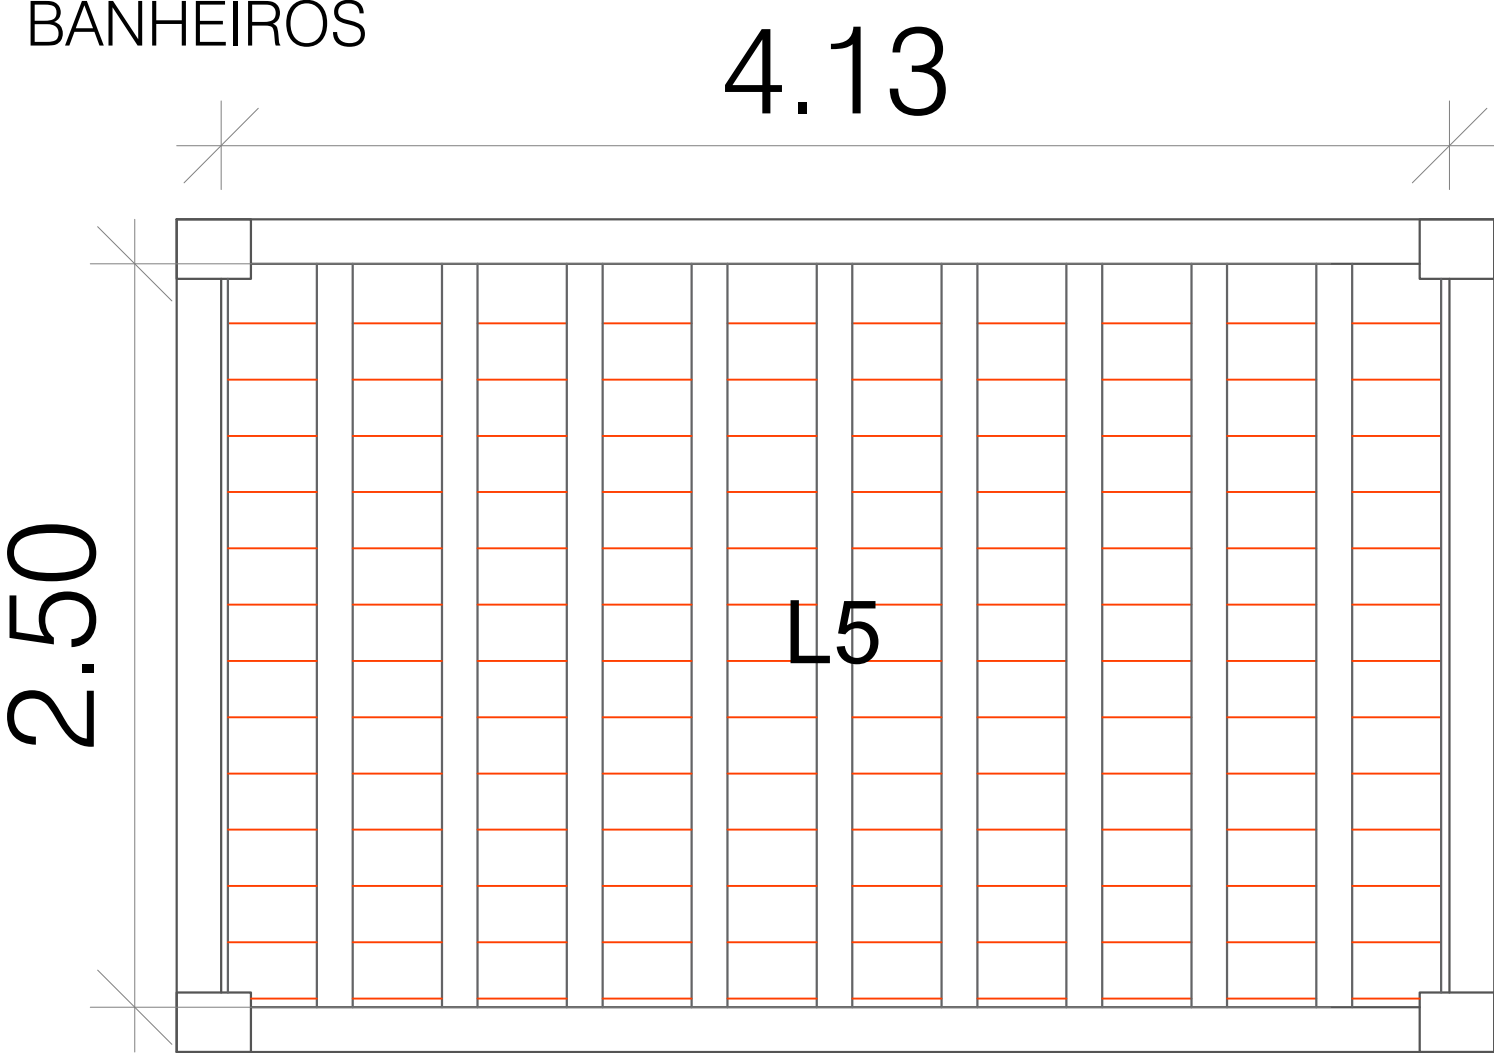

Projeto:

Projeto de Urbanismo Vila Olimpica

Desenhos:

PLANTA BAIXA DE LOCAÇÃO DOS ELEMENTOS ESTRUTURAIS

Observações:

- Conferir todas as medidas em obra antes da execução dos serviços.
- Não executar alterações sem autorização prévia do responsável técnico.
- Qualquer divergência entre projeto e condições de campo deverá ser comunicada ao responsável técnico para análise e aprovação.
- Todas as instalações deverão ser executadas por mão de obra qualificada, seguindo as normas técnicas vigentes e as recomendações dos fabricantes dos materiais empregados.
- O dimensionamento e posicionamentos indicados em projeto prevalecem sobre quaisquer informações complementares aqui descritas.

Esta prancha apresenta os detalhamentos das lajes da edificação, contendo informações de espessura, altura total, altura da capa de concreto, armaduras complementares, reforços e demais elementos necessários para sua execução.

- As lajes serão executadas em sistema treliçado com elementos de enchimento em bloco cerâmico, conforme especificado em projeto.
- A altura das vigotas treliçadas, a espessura da capa de concreto, a altura total da laje e os elementos de enchimento deverão seguir rigorosamente as especificações indicadas nos detalhamentos estruturais.
- As armaduras complementares, armaduras negativas, armaduras de distribuição, reforços localizados e demais elementos estruturais deverão ser executados conforme bitolas, quantidades, comprimentos e posicionamentos definidos em projeto.
- Os escoramentos deverão permanecer instalados durante o período mínimo necessário para garantir a adequada resistência do concreto, conforme orientação técnica e cronograma de execução.
- Antes da concretagem, deverão ser conferidos o posicionamento das vigotas, alinhamento, nivelamento, escoramento, armaduras complementares, instalações embutidas e demais elementos previstos em projeto.
- Não será permitida a abertura de furos, rasgos ou remoção de elementos estruturais sem autorização do responsável técnico.
- As passagens de instalações elétricas, hidráulicas e sanitárias deverão respeitar as posições previstas em projeto.
- Qualquer divergência identificada em campo deverá ser comunicada ao responsável técnico para análise e aprovação.
- Todos os serviços deverão atender às especificações do projeto estrutural e às normas técnicas vigentes.

Projetista:

Fernando Matias Mamede

RESPONSÁVEL TÉCNICO
Fernando Matias Mamede
Engenheiro Civil
Crea: 162056275-6

Proprietário:

Prefeitura Municipal de Coremas

PROPRIETÁRIO(A)

Endereço/Obra:


Rua Francisco Raimundo de Andrade, DNOCS, Coremas - PB, 58770-000

ÁREAS

Área do Terreno	10.733,41
Estacionamento	519,11
Calçada	249,64
Área verde	4.281,11

Prancha:

06/14

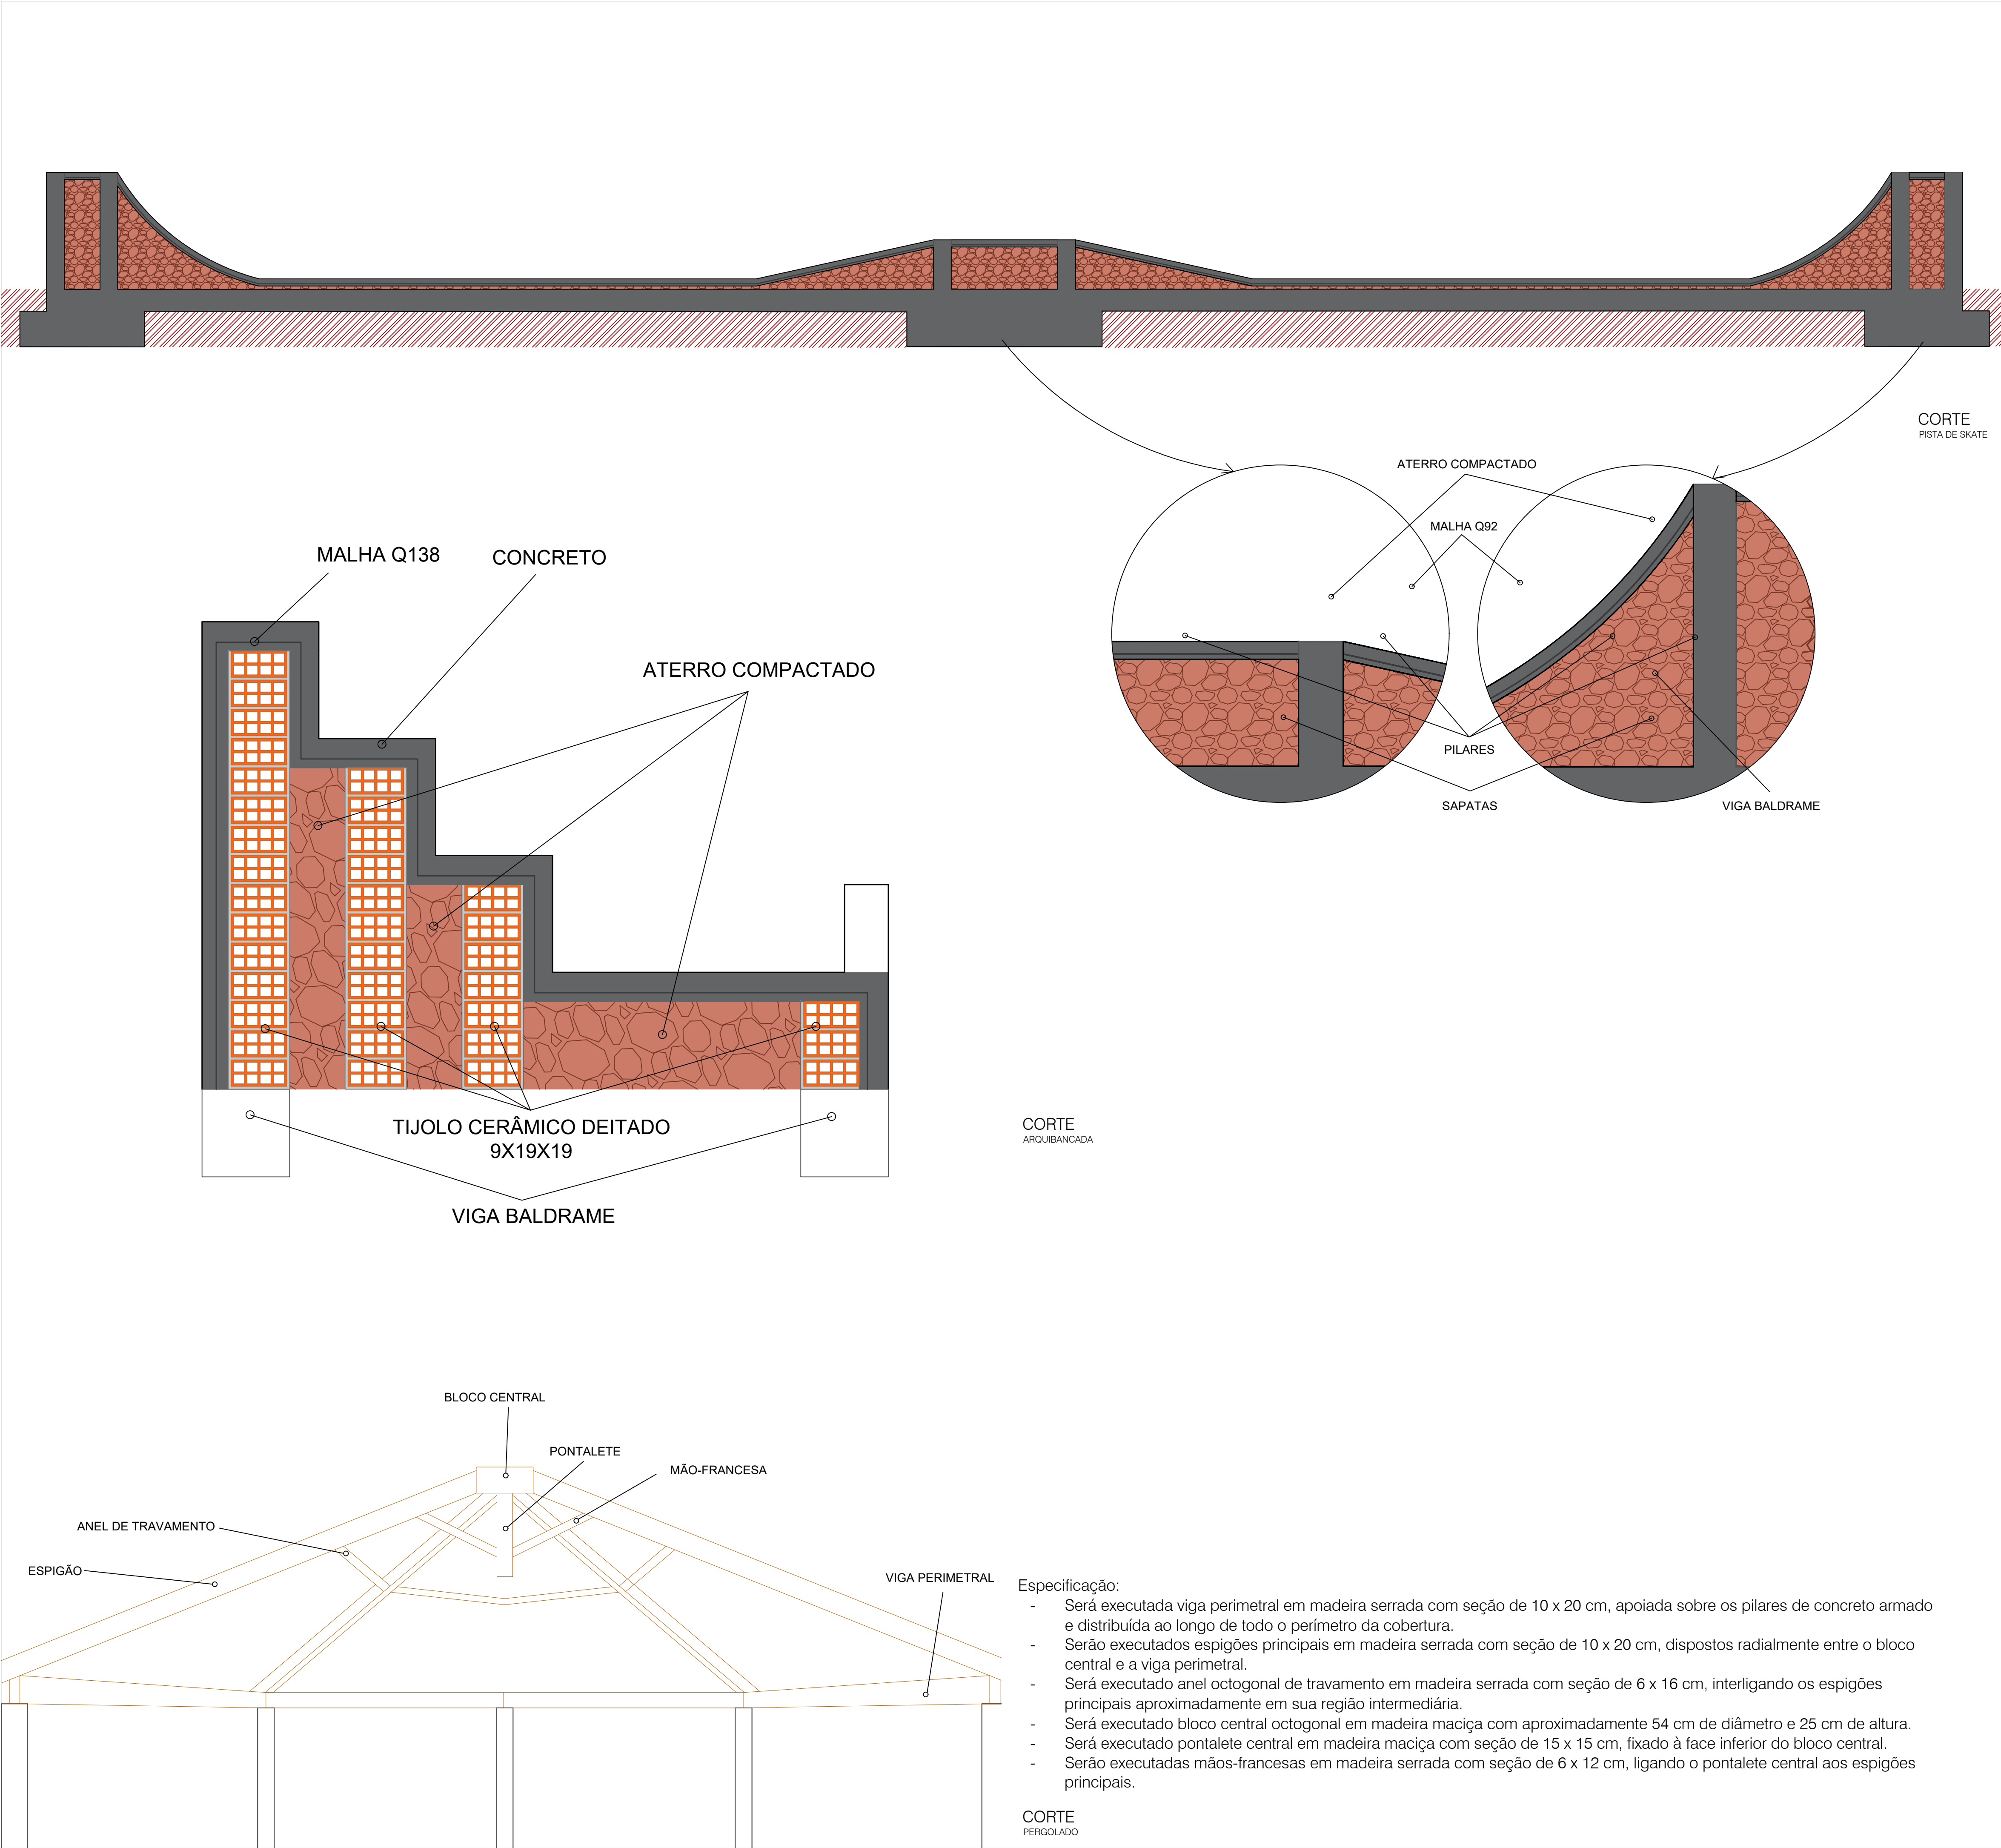

Projeto:

Projeto de Urbanismo Vila Olimpica

Desenhos:

PLANTA BAIXA DE LOCAÇÃO DOS ELEMENTOS ESTRUTURAIS

Observações:

- Conferir todas as medidas em obra antes da execução dos serviços.
- Não executar alterações sem autorização prévia do responsável técnico.
- Qualquer divergência entre projeto e condições de campo deverá ser comunicada ao responsável técnico para análise e aprovação.
- Todas as instalações deverão ser executadas por mão de obra qualificada, seguindo as normas técnicas vigentes e as recomendações dos fabricantes dos materiais empregados.
- O dimensionamento e posicionamentos indicados em projeto prevalecem sobre quaisquer informações complementares aqui descritas.

Esta prancha apresenta os detalhamentos construtivos da pista de skate e das arquibancadas, devendo sua execução seguir rigorosamente as dimensões, níveis, materiais e especificações indicados em projeto.

- A pista de skate deverá ser executada sobre aterro devidamente compactado.
- O aterro deverá ser realizado em camadas sucessivas de, no máximo, 20 cm de espessura, com compactação adequada de cada camada, até atingir os níveis definidos em projeto.
- Sobre o aterro compactado deverá ser executada uma capa de concreto com espessura de 10 cm.
- A capa de concreto deverá ser armada com tela soldada tipo Q92, posicionada conforme detalhamento apresentado em projeto.
- As superfícies deverão apresentar acabamento uniforme, respeitando os níveis, inclinações e geometrias indicadas nos detalhamentos.
- Os pilares de sustentação deverão ser executados conforme os detalhamentos específicos constantes na prancha de pilares.

- As arquibancadas deverão ser executadas conforme as dimensões e níveis indicados em projeto.
- Cada degrau será formado por alvenaria de vedação executada com tijolos cerâmicos assentados horizontalmente, conforme detalhamento apresentado.
- Os espaços internos entre os elementos de contenção deverão ser preenchidos com aterro compactado.
- O aterro deverá ser executado em camadas sucessivas de, no máximo, 20 cm de espessura, com compactação adequada de cada camada.
- Sobre o aterro compactado deverá ser executada uma capa de concreto com espessura de 10 cm.
- A capa de concreto das arquibancadas deverá ser armada com tela soldada tipo Q138, posicionada conforme detalhamento estrutural.

Projetista:

Fernando Matias Mamede

RESPONSÁVEL TÉCNICO

Fernando Matias Mamede

Engenheiro Civil

Crea: 162056275-6

Proprietário:

Prefeitura Municipal de Coremas

PROPRIETÁRIO(A)


Endereço/Obra:

Rua Francisco Raimundo de Andrade, DNOCS, Coremas - PB, 58770-000


ÁREAS	m²
Área do Terreno	10.733,41
Estacionamento	519,11
Calçada	249,64
Área verde	4.281,11

Prancha:

07/14

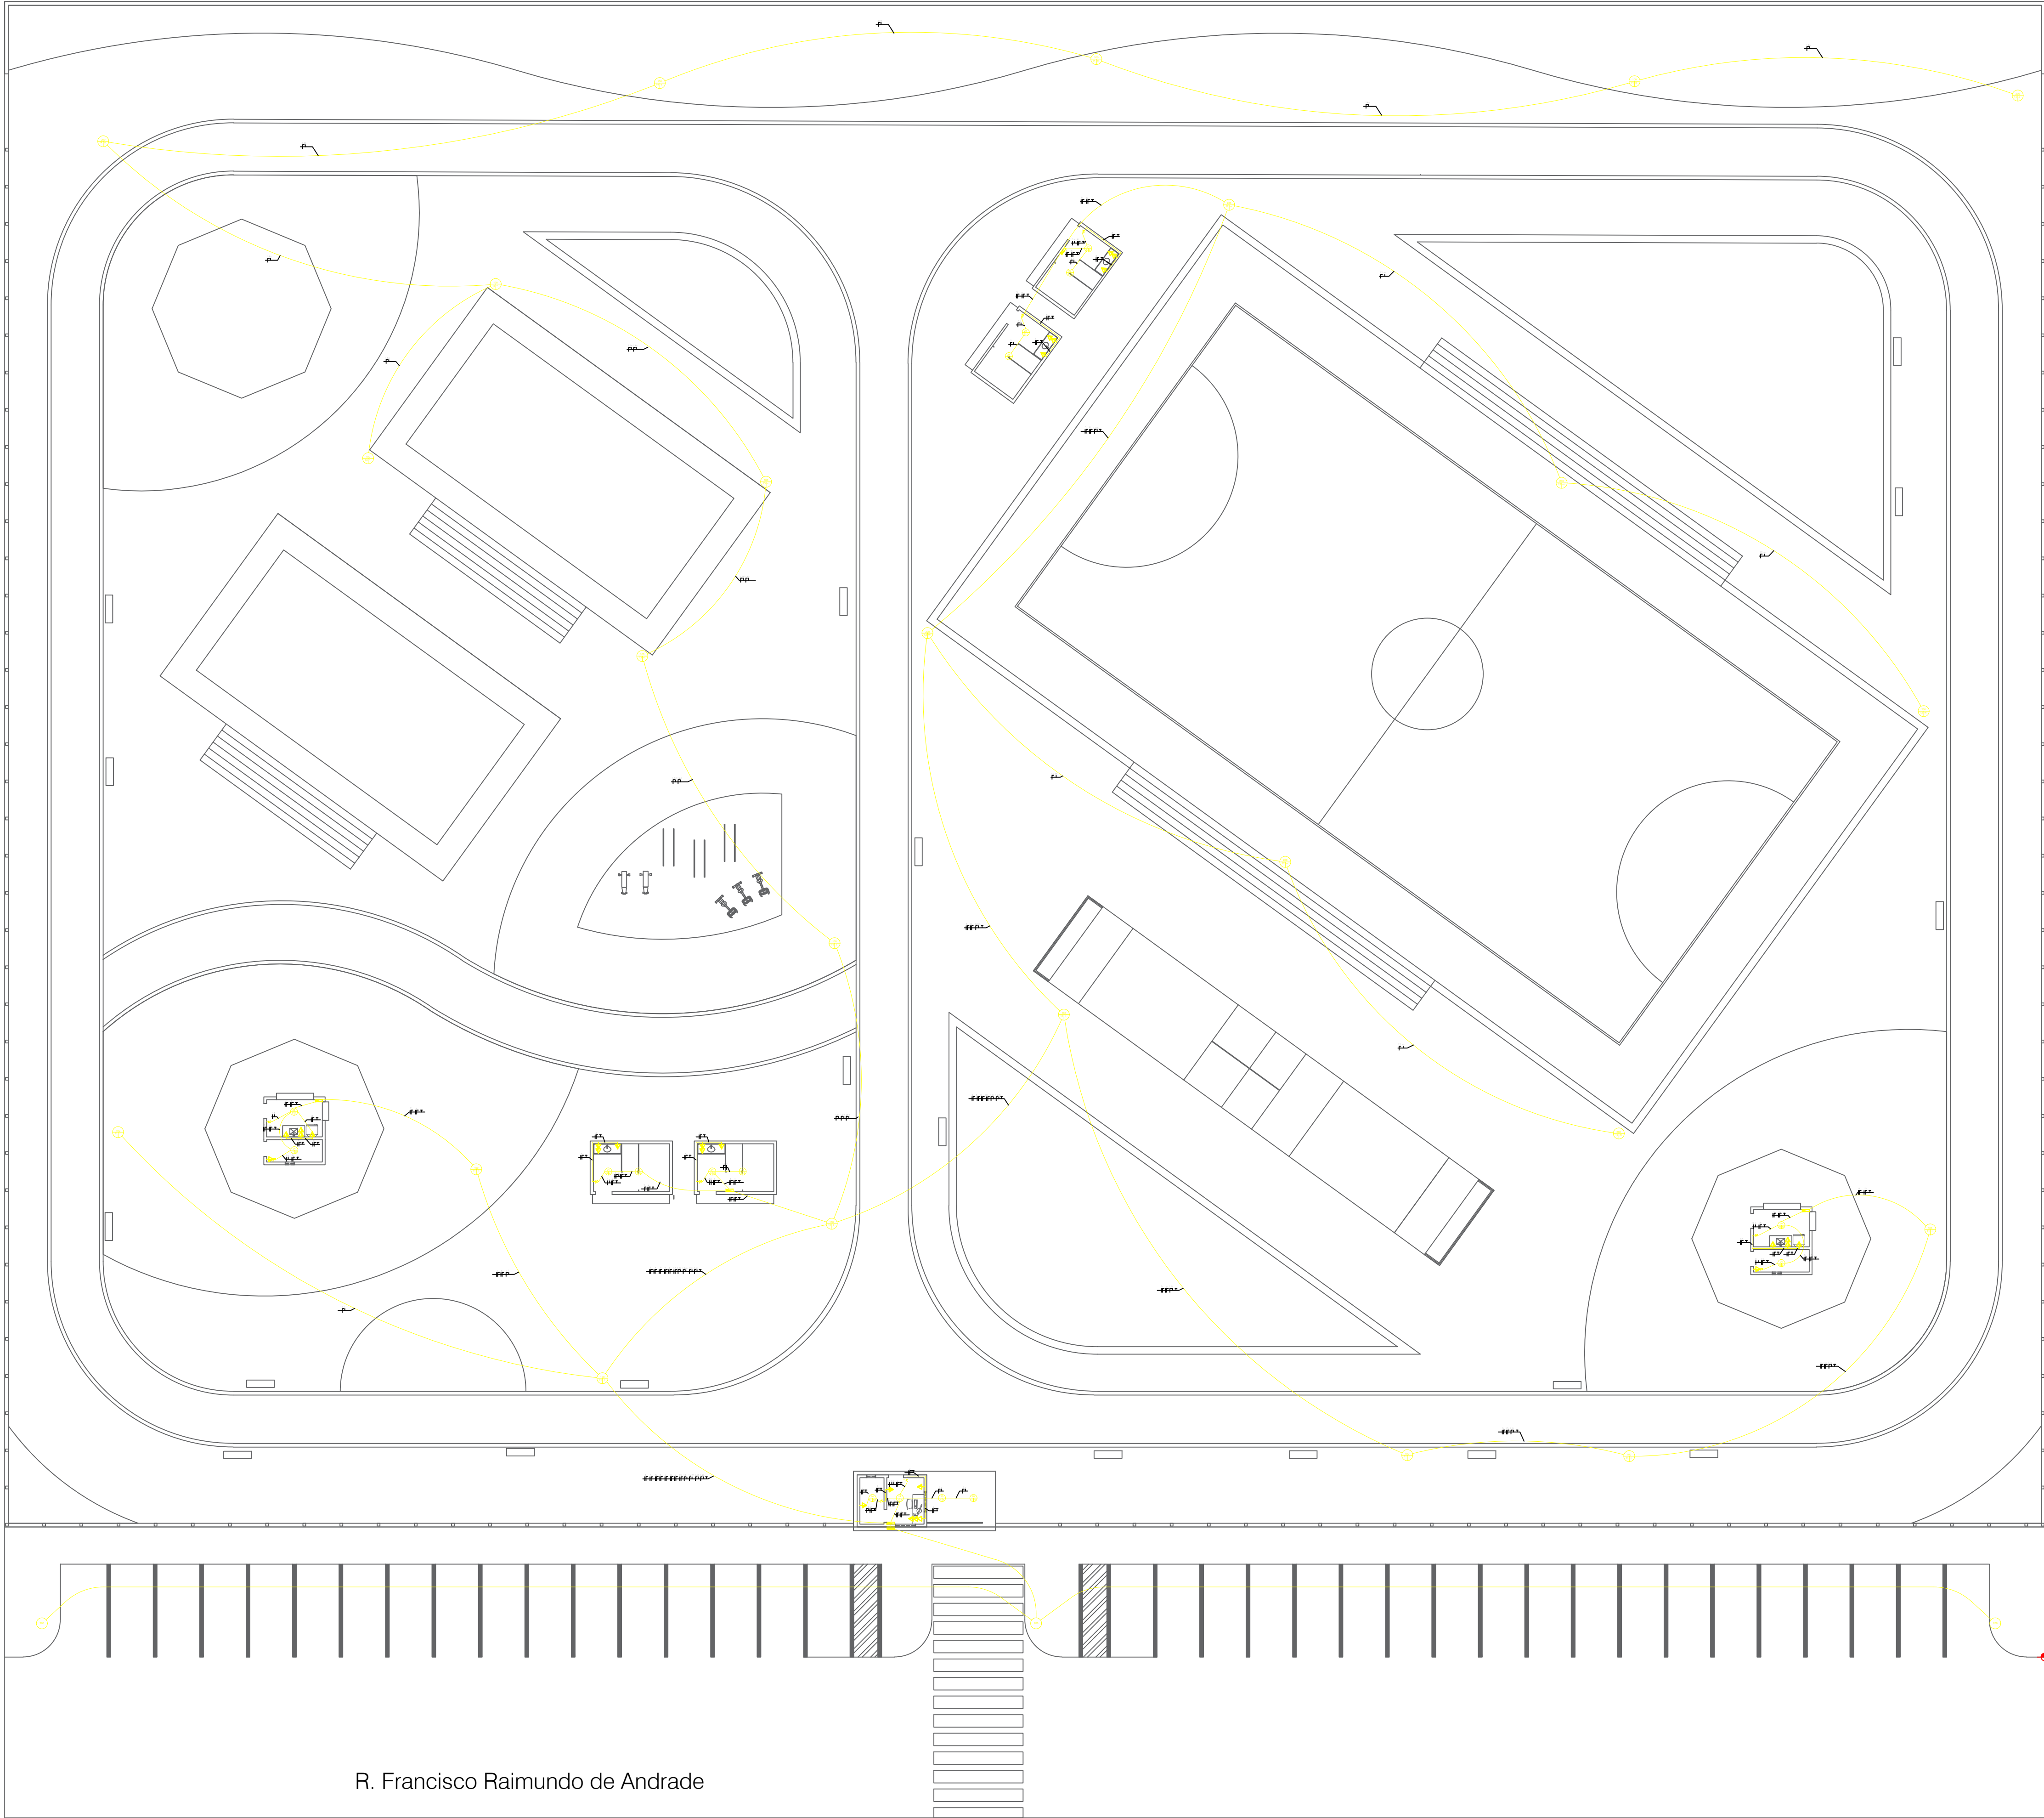

R. Francisco Raimundo de Andrade

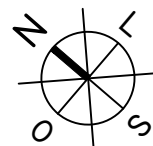

Projeto:


Projeto de Urbanismo Vila Olimpica

Desenhos:

PLANTA BAIXA COM DETALHAMENTO DOS PONTOS ELÉTRICOS

Circuito		QUADRO DE CARGAS - GERAL													Tomadas (V)		Comente (A)	Cond. (mm²)	Proteção (A)
		Iluminação (W)								Tomadas (W)					Pot (W)	Pot (VA)			
		18	24	100	200	300	600	1000	1800	100	200	300	600						
1	Iluminação Quilômetro		4							96	96	1	220	96	1	220	0,48	1,5	10
2	Tomadas Quilômetro						5			1500	1500	1	220	1500	1	220	0,87	2,5	10
3	Iluminação Banheiros 1			4						96	96	1	220	96	1	220	0,48	1,5	10
4	Tomadas Banheiros 1						6			600	600	1	220	600	1	220	2,73	2,5	10
5	Iluminação Banheiros 2			4						96	96	1	220	96	1	220	0,48	1,5	10
6	Tomadas Banheiros 2						5			600	600	1	220	600	1	220	2,73	2,5	10
7	Iluminação Quilômetro 1		2							48	48	1	220	48	1	220	0,22	1,5	10
8	Tomadas Quilômetro 1			2						500	500	1	220	500	1	220	2,27	2,5	10
9	Iluminação Quilômetro 2						5			48	48	1	220	48	1	220	0,22	1,5	10
10	Tomadas Quilômetro 2						5			500	500	1	220	500	1	220	2,27	2,5	10
11	Iluminação Portas - Entrada				9					900	900	1	220	900	1	220	4,09	2,5	10
12	Iluminação Portas - Quadra Futsal						6			1200	1200	1	220	1200	1	220	5,45	2,5	10
13	Iluminação Portas - Quadra Vôlei						4			400	400	1	220	400	1	220	1,82	2,5	10
14	Iluminação Portas - Fundos				2	3				800	800	1	220	800	1	220	3,64	2,5	10
TOTAL			16	15	9	27		1		7384	7384	1	220	7384	1	220	33,56	6,0	50

DIAGRAMA UNIFILAR

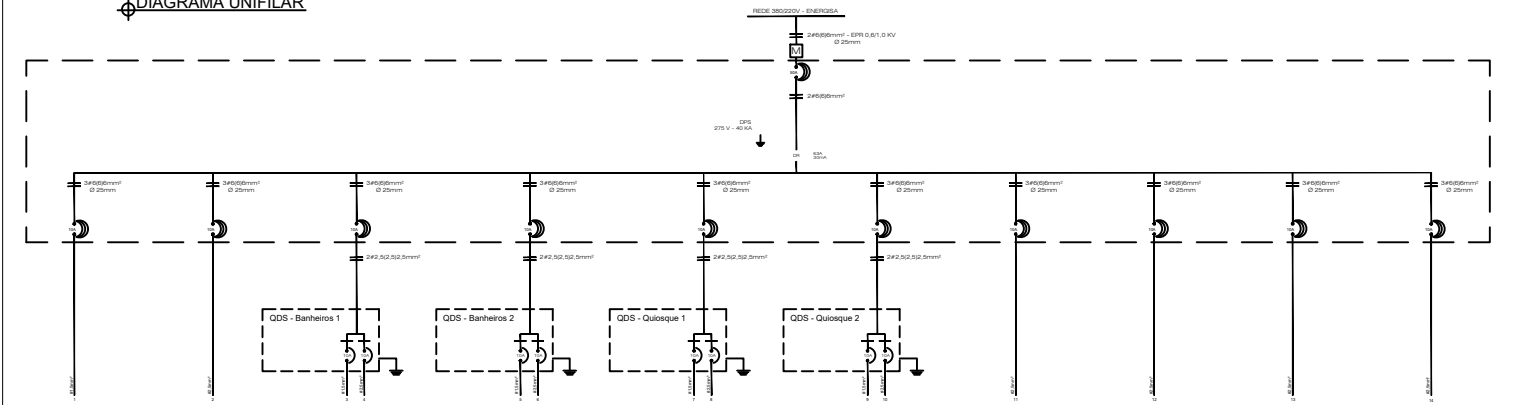

Observações:

- Conferir todas as medidas em obra antes da execução dos serviços.
- Não executar alterações sem autorização prévia do responsável técnico.
- Qualquer divergência entre projeto e condições de campo deverá ser comunicada ao responsável técnico para análise e aprovação.
- Todas as instalações deverão ser executadas por mão de obra qualificada, seguindo as normas técnicas vigentes e as recomendações dos fabricantes dos materiais empregados.
- O dimensionamento e posicionamentos indicados em projeto prevalecem sobre quaisquer informações complementares aqui descritas.

Esta prancha apresenta os detalhes das instalações elétricas devendo sua execução seguir rigorosamente as dimensões, níveis, materiais e especificações indicados em projeto.

- A alimentação da edificação será realizada através do quadro geral de distribuição (QDG), conforme indicado em projeto.
- Todos os circuitos deverão ser identificados e distribuídos conforme o diagrama unifilar e o quadro de cargas apresentados em projeto.
- As emendas de condutores somente poderão ser executadas no interior de caixas de passagem, caixas de derivação ou quadros elétricos.
- Todos os condutores deverão possuir isolamento adequado à tensão de operação e serem instalados sem danos mecânicos.
- Os condutores deverão possuir seção nominal conforme especificado em projeto.
- Os circuitos de iluminação, tomadas de uso geral (TUG), tomadas de uso específico (TUE) e equipamentos deverão respeitar as bitolas indicadas no quadro de cargas.
- Os eletrodutos deverão possuir diâmetros compatíveis com a quantidade e seção dos condutores instalados.
- Não será permitida a ocupação excessiva dos eletrodutos, devendo ser respeitadas as taxas máximas de ocupação previstas em norma.
- O quadro de distribuição deverá possuir barramentos independentes para neutro e aterramento.
- Todos os dispositivos de proteção deverão ser instalados conforme especificado em projeto.
- Os circuitos deverão ser protegidos por disjuntores termomagnéticos compatíveis com suas respectivas cargas.
- Quando especificado em projeto, deverão ser instalados dispositivos DR e DPS.
- Os quadros de distribuição deverão ser instalados nos locais indicados em projeto, garantindo fácil acesso para operação e manutenção.
- Não executar alterações sem autorização prévia do responsável técnico.
- Qualquer divergência entre projeto e condições de campo deverá ser comunicada ao responsável técnico para análise e aprovação.

Projetista:

Fernando Matias Mamede

RESPONSÁVEL TÉCNICO
Fernando Matias Mamede
Engenheiro Civil
Crea: 162056275-8

Proprietário:

Prefeitura Municipal de Coremas

PROPRIETÁRIO(A)


Endereço/Obra: Rua Francisco Raimundo de Andrade, DNOCS, Coremas - PB, 58770-000

ÁREAS	m²
Área do Terreno	10.733,41
Estacionamento	519,11
Calçada	249,64
Área verde	4.281,11


Prancha:

08/14


Detalhamento Elétrico - Banheiros 1

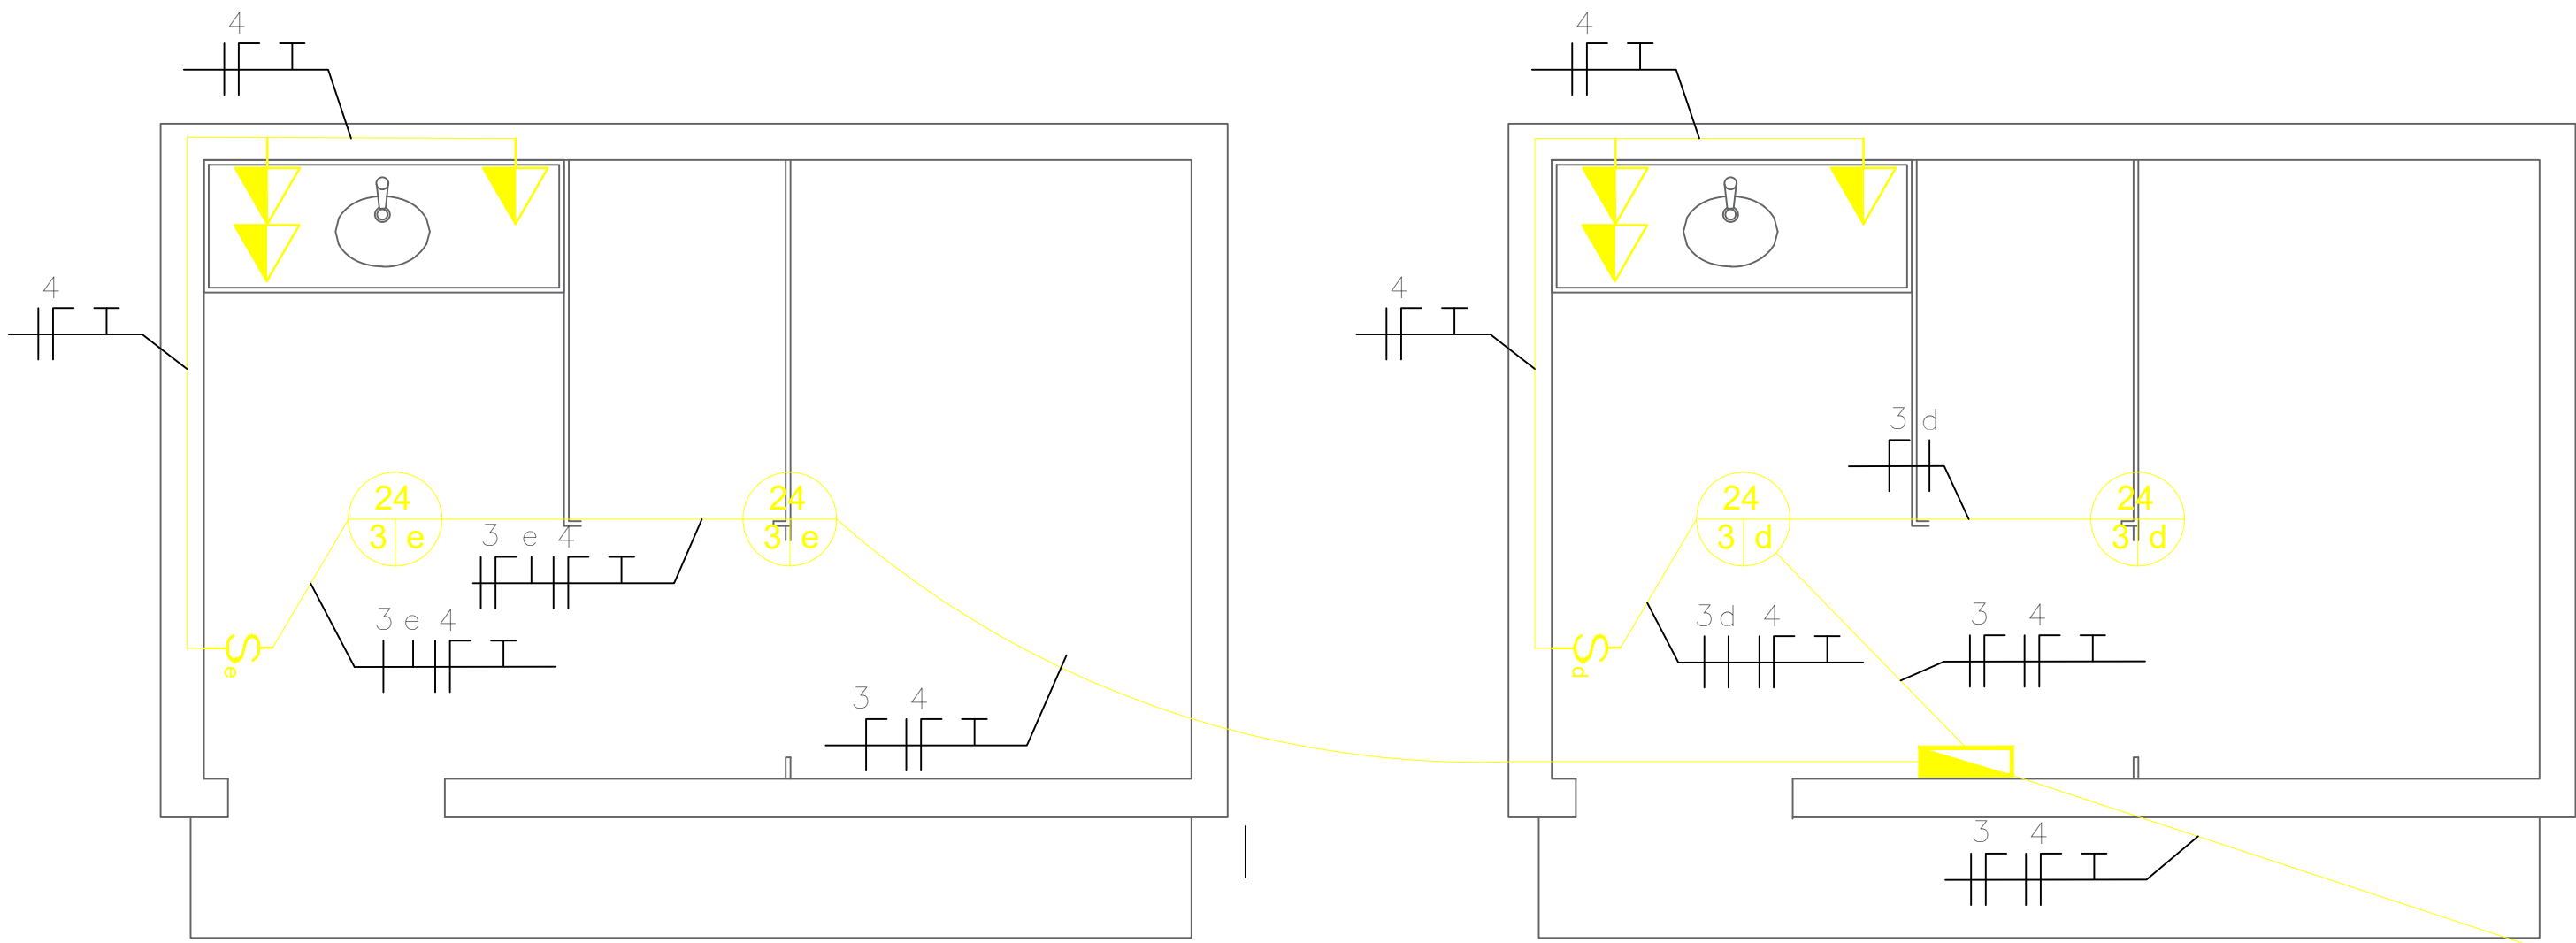


Detalhamento Elétrico - Quiosque 1

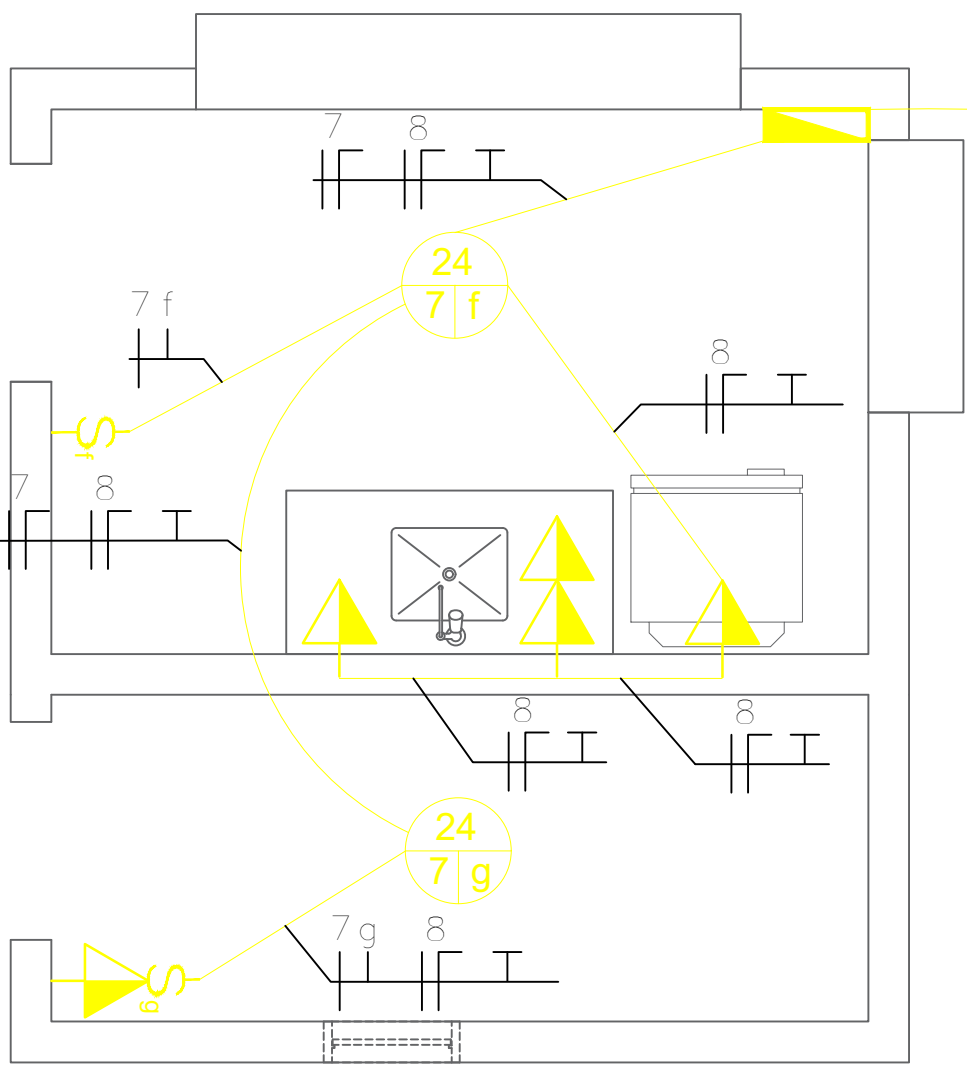


Detalhamento Elétrico - Banheiros 2

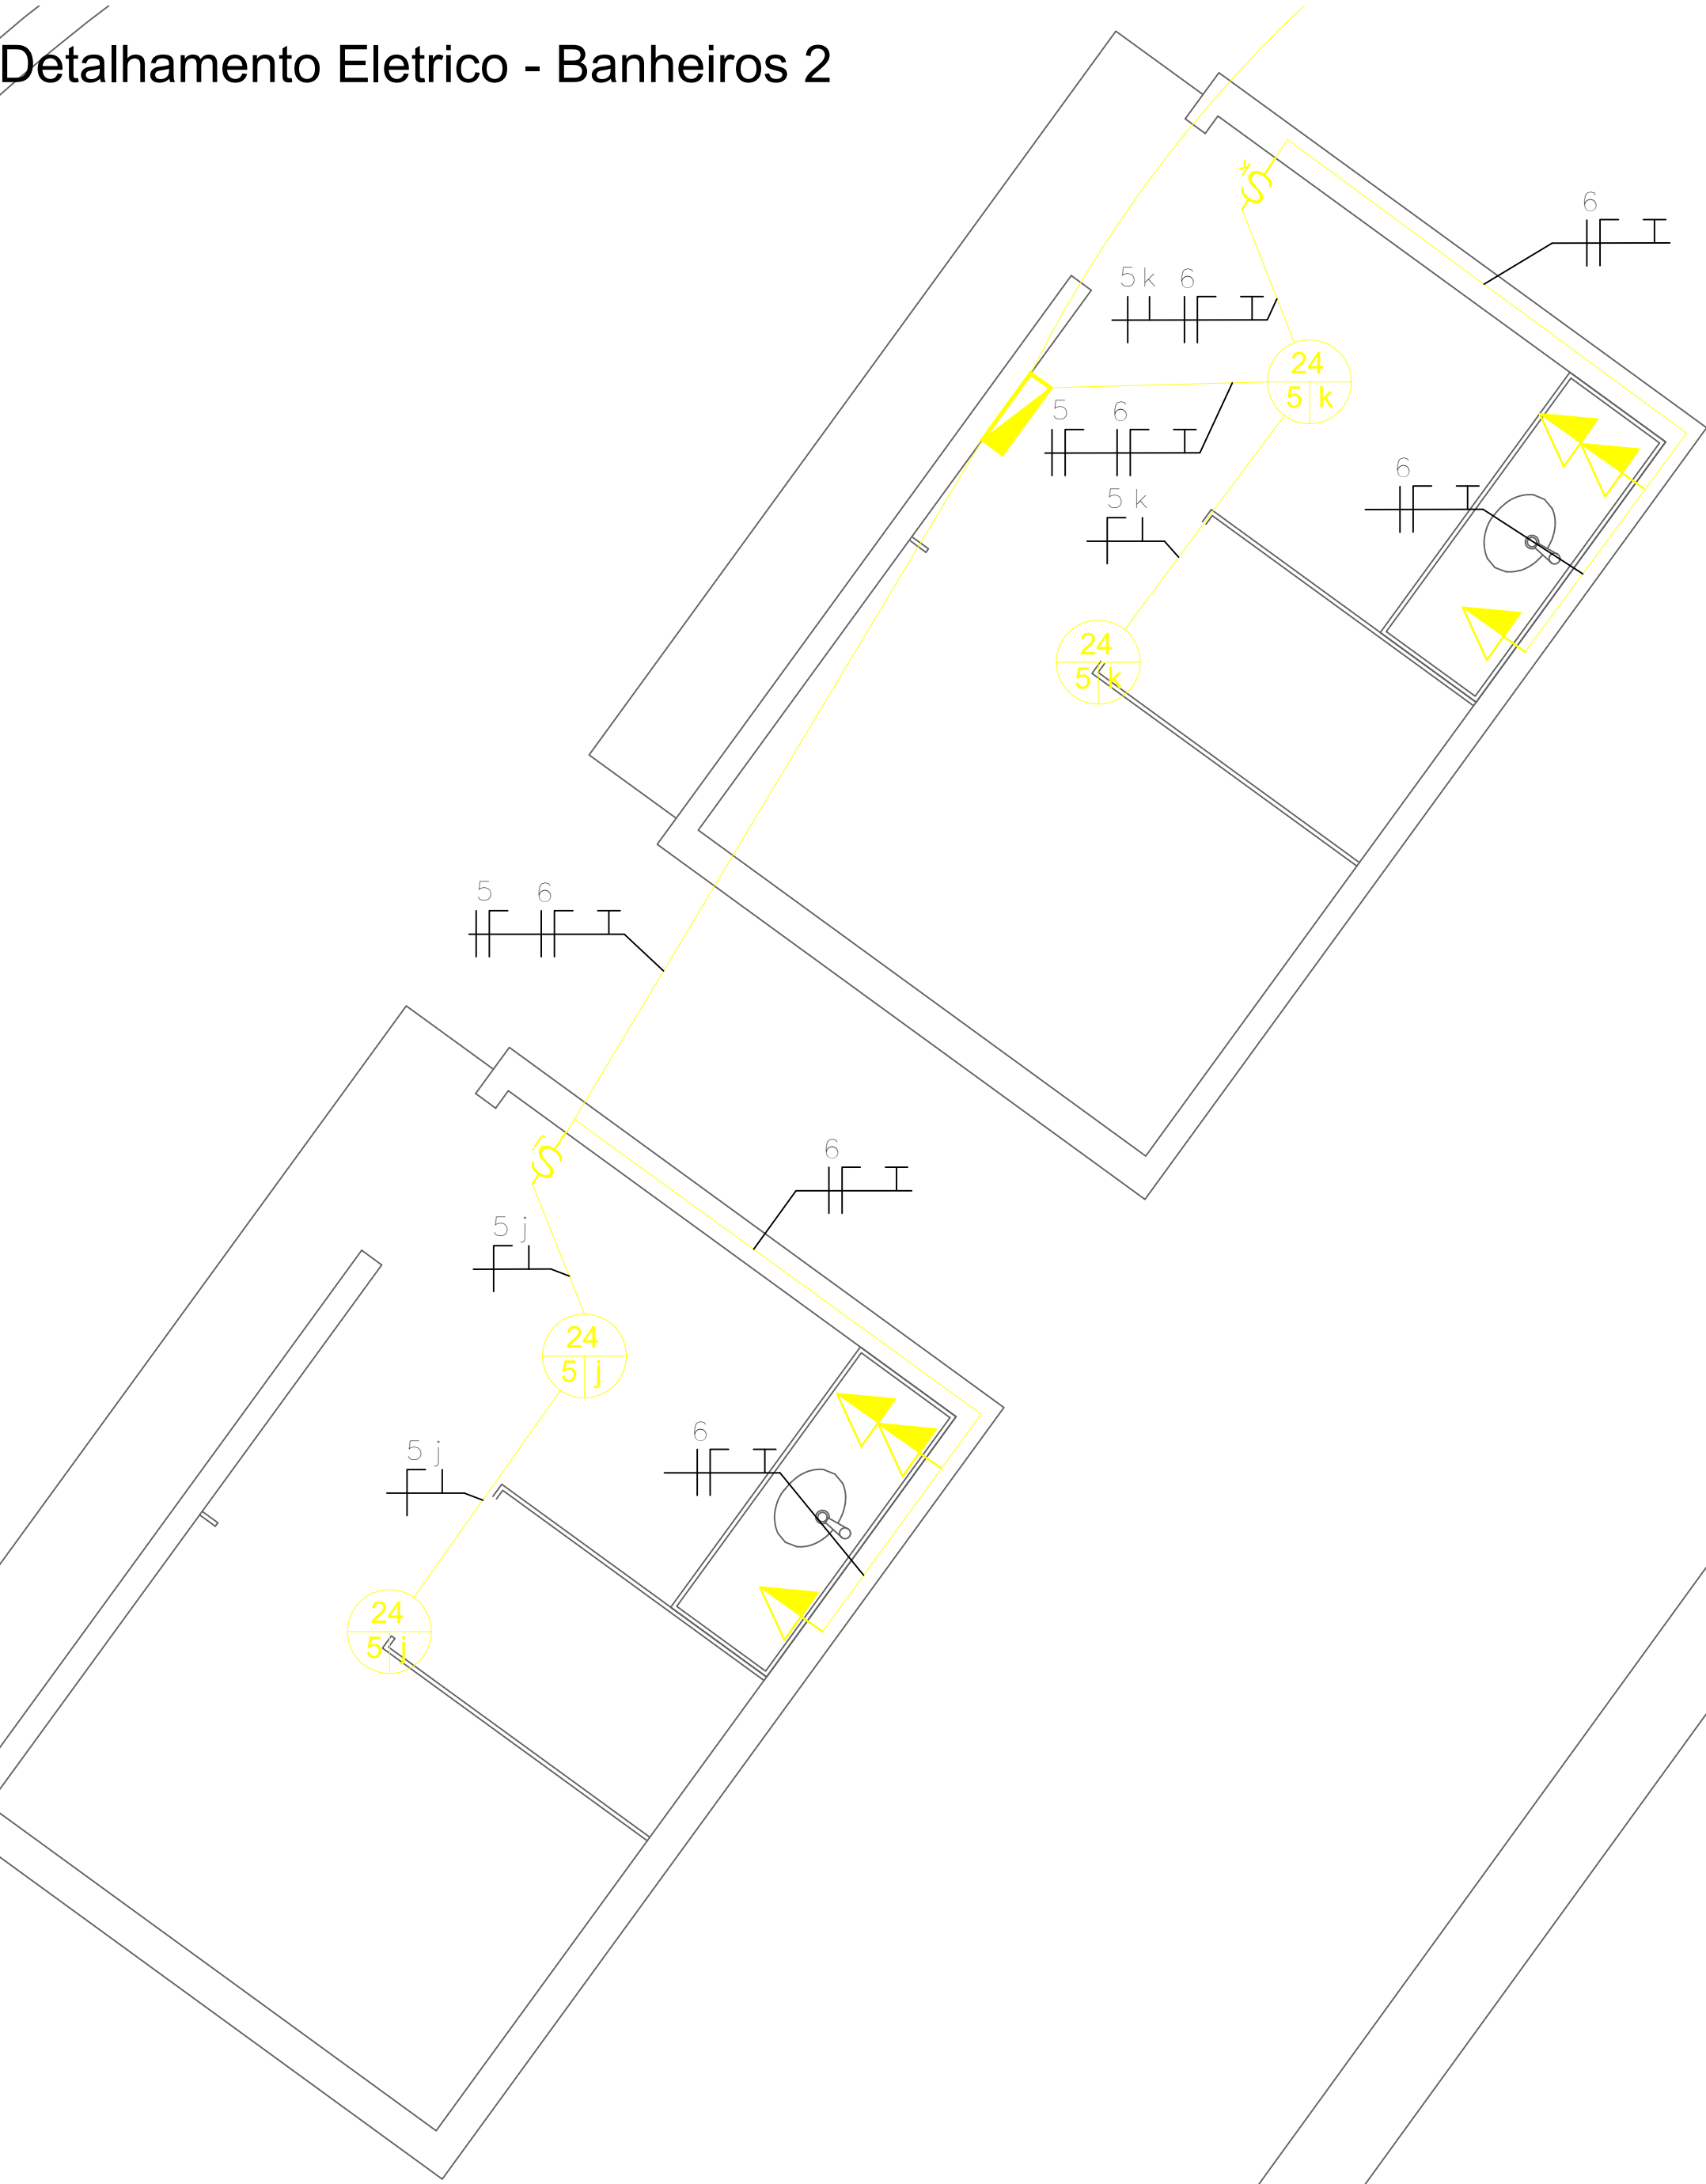

Detalhamento Elétrico - Quiosque 2

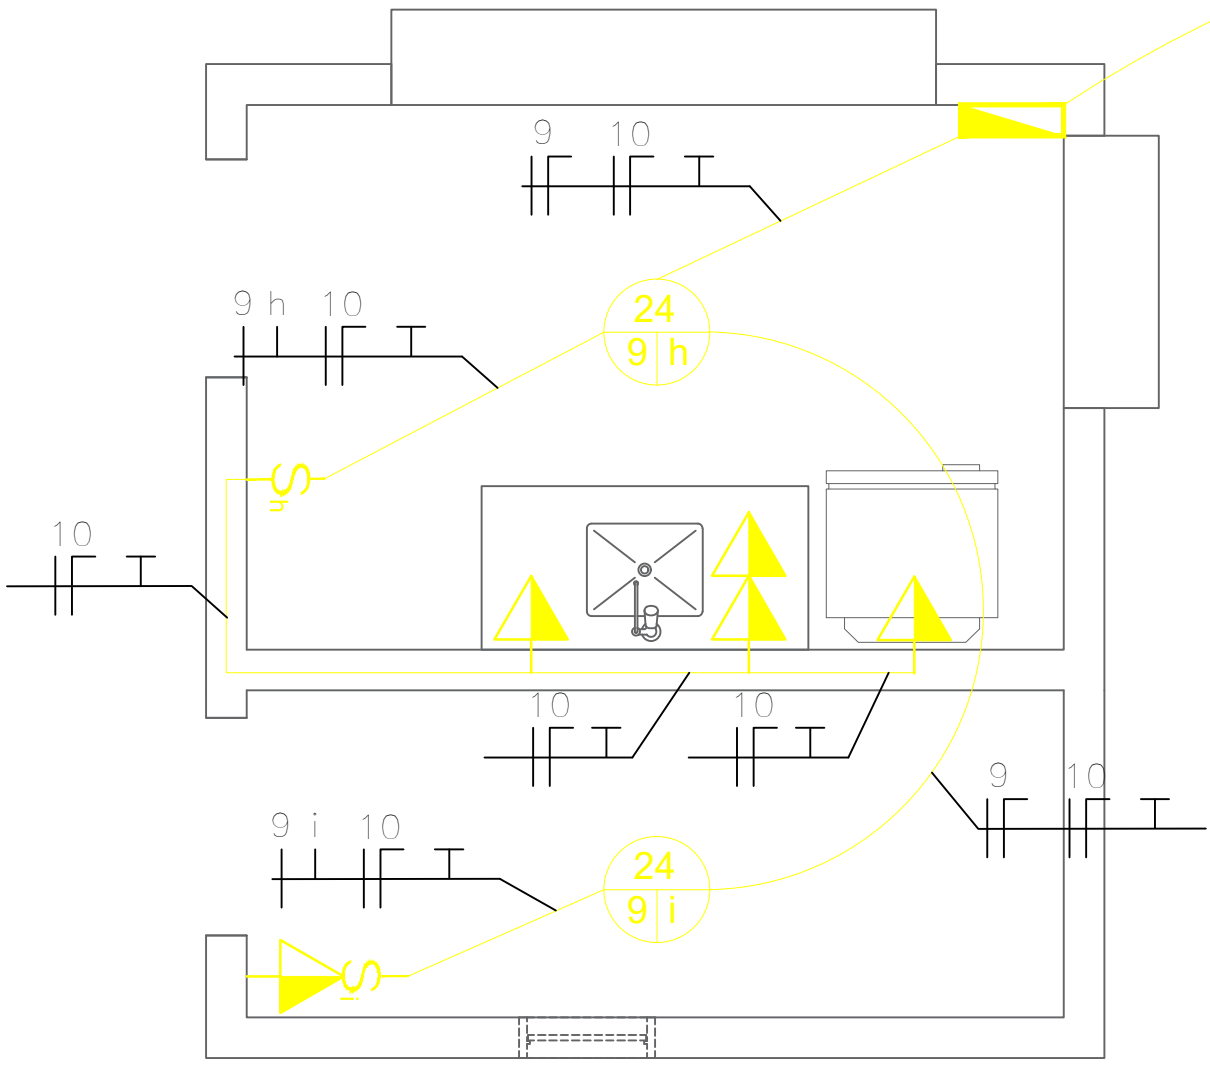

Detalhamento Elétrico - Guarita

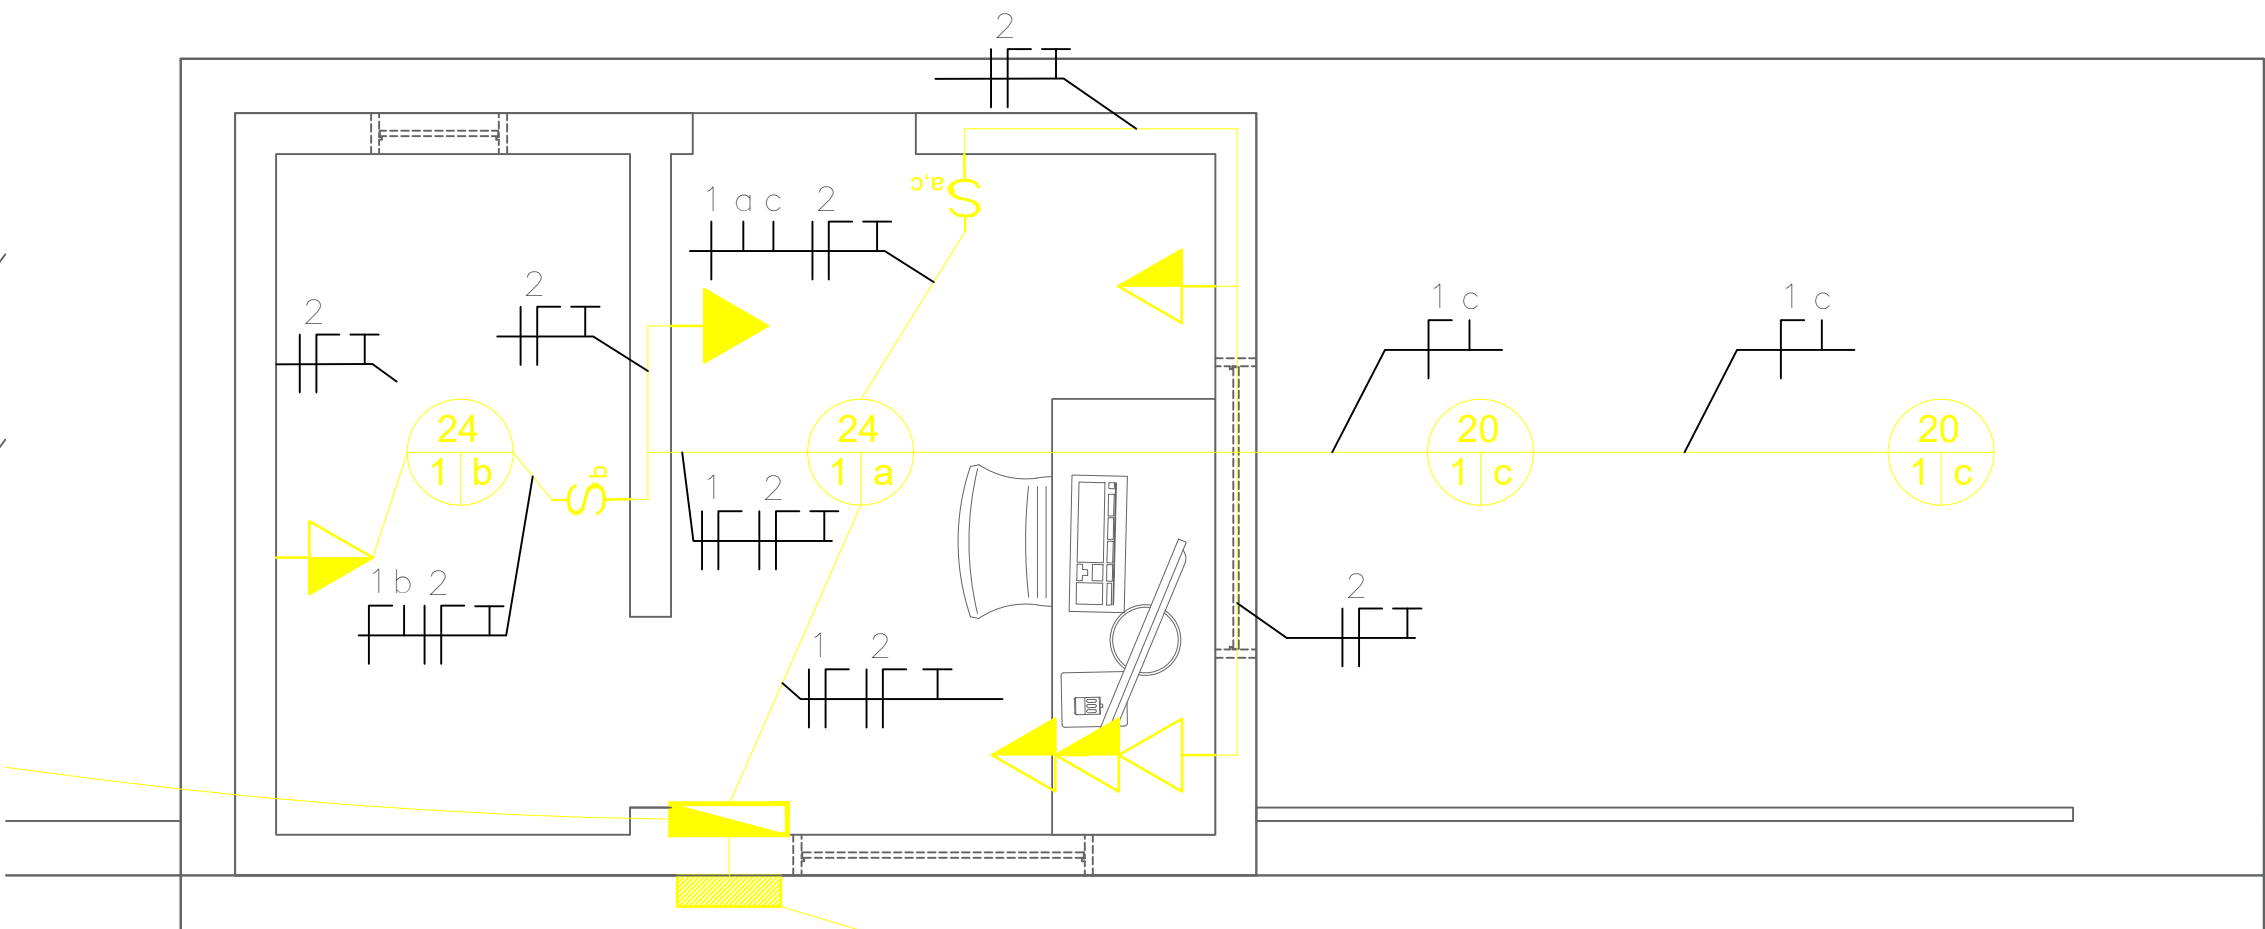

Projeto:

Desenhos:

Projeto de Urbanismo Vila Olimpica

PLANTA BAIXA COM DETALHAMENTO DOS PONTOS ELÉTRICOS

Circuito	Descrição	QUADRO DE CARGAS - GERAL										Pot (W)	Pot (VA)	FP	Tensão (V)	Corrente (A)	Cond. (mm²)	Proteção (A)
		Iluminação (W)		Tomadas (W)		Tubo (W)		Tubo (W)		Tubo (W)								
		18	24	100	200	100	600	1000	1800									
1	Iluminação Quilômetro		4			5				96	96	1	220		0,44	1,5	10	
2	Tomadas Quilômetro									1500	1500	1	220		0,87	2,5	10	
3	Iluminação Banheiros 1			4						96	96	1	220		0,44	1,5	10	
4	Tomadas Banheiros 1									600	600	1	220		2,73	2,5	10	
5	Iluminação Banheiros 2			4						96	96	1	220		0,44	1,5	10	
6	Tomadas Banheiros 2									600	600	1	220		2,73	2,5	10	
7	Iluminação Quiosque 1		2							48	48	1	220		0,22	1,5	10	
8	Tomadas Quiosque 1									600	600	1	220		2,73	2,5	10	
9	Iluminação Quiosque 2		2							48	48	1	220		0,22	1,5	10	
10	Tomadas Quiosque 2									600	600	1	220		2,73	2,5	10	
11	Iluminação Pontes - Frente				9					900	900	1	220		4,09	2,5	10	
12	Iluminação Pontes - Quadra Central						6			1200	1200	1	220		5,45	2,5	10	
13	Iluminação Pontes - Quadra Lateral									400	400	1	220		1,82	2,5	10	
14	Iluminação Pontes - Fundos				2	3				800	800	1	220		3,64	2,5	10	
TOTAL			16	15	9	27		1		7384	7384	1	220		33,56	6,0	50	

DIAGRAMA UNIFILAR

Observações:

- Conferir todas as medidas em obra antes da execução dos serviços.
- Não executar alterações sem autorização prévia do responsável técnico.
- Qualquer divergência entre projeto e condições de campo deverá ser comunicada ao responsável técnico para análise e aprovação.
- Todas as instalações deverão ser executadas por mão de obra qualificada, seguindo as normas técnicas vigentes e as recomendações dos fabricantes dos materiais empregados.
- O dimensionamento e posicionamentos indicados em projeto prevalecem sobre quaisquer informações complementares aqui descritas.

Esta prancha apresenta os detalhes das instalações elétricas devendo sua execução seguir rigorosamente as dimensões, níveis, materiais e especificações indicados em projeto.

- A alimentação da edificação será realizada através do quadro geral de distribuição (QDG), conforme indicado em projeto.
- Todos os circuitos deverão ser identificados e distribuídos conforme o diagrama unifilar e o quadro de cargas apresentados em projeto.
- As emendas de condutores somente poderão ser executadas no interior de caixas de passagem, caixas de derivação ou quadros elétricos.
- Todos os condutores deverão possuir isolamento adequado à tensão de operação e serem instalados sem danos mecânicos.
- Os condutores deverão possuir seção nominal conforme especificado em projeto.
- Os circuitos de iluminação, tomadas de uso geral (TUG), tomadas de uso específico (TUE) e equipamentos deverão respeitar as bitolas indicadas no quadro de cargas.
- Os eletrodutos deverão possuir diâmetros compatíveis com a quantidade e seção dos condutores instalados.
- Não será permitida a ocupação excessiva dos eletrodutos, devendo ser respeitadas as taxas máximas de ocupação previstas em norma.
- O quadro de distribuição deverá possuir barramentos independentes para neutro e aterramento.
- Todos os dispositivos de proteção deverão ser instalados conforme especificado em projeto.
- Os circuitos deverão ser protegidos por disjuntores termomagnéticos compatíveis com suas respectivas cargas.
- Quando especificado em projeto, deverão ser instalados dispositivos DR e DPS.
- Os quadros de distribuição deverão ser instalados nos locais indicados em projeto, garantindo fácil acesso para operação e manutenção.
- Não executar alterações sem autorização prévia do responsável técnico.
- Qualquer divergência entre projeto e condições de campo deverá ser comunicada ao responsável técnico para análise e aprovação.

Projetista:

RESPONSÁVEL TÉCNICO

Proprietário:

Endereço/Obra:

ÁREAS

Prancha:

Fernando Matias Mamede


Fernando Matias Mamede
Engenheiro Civil
Crea: 162056275-8

Prefeitura Municipal de Coremas

Rua Francisco Raimundo de Andrade, DNOCS, Coremas - PB, 58770-000

Área do Terreno	10.733,41
Estacionamento	519,11
Calçada	249,64
Área verde	4.281,11


09/14

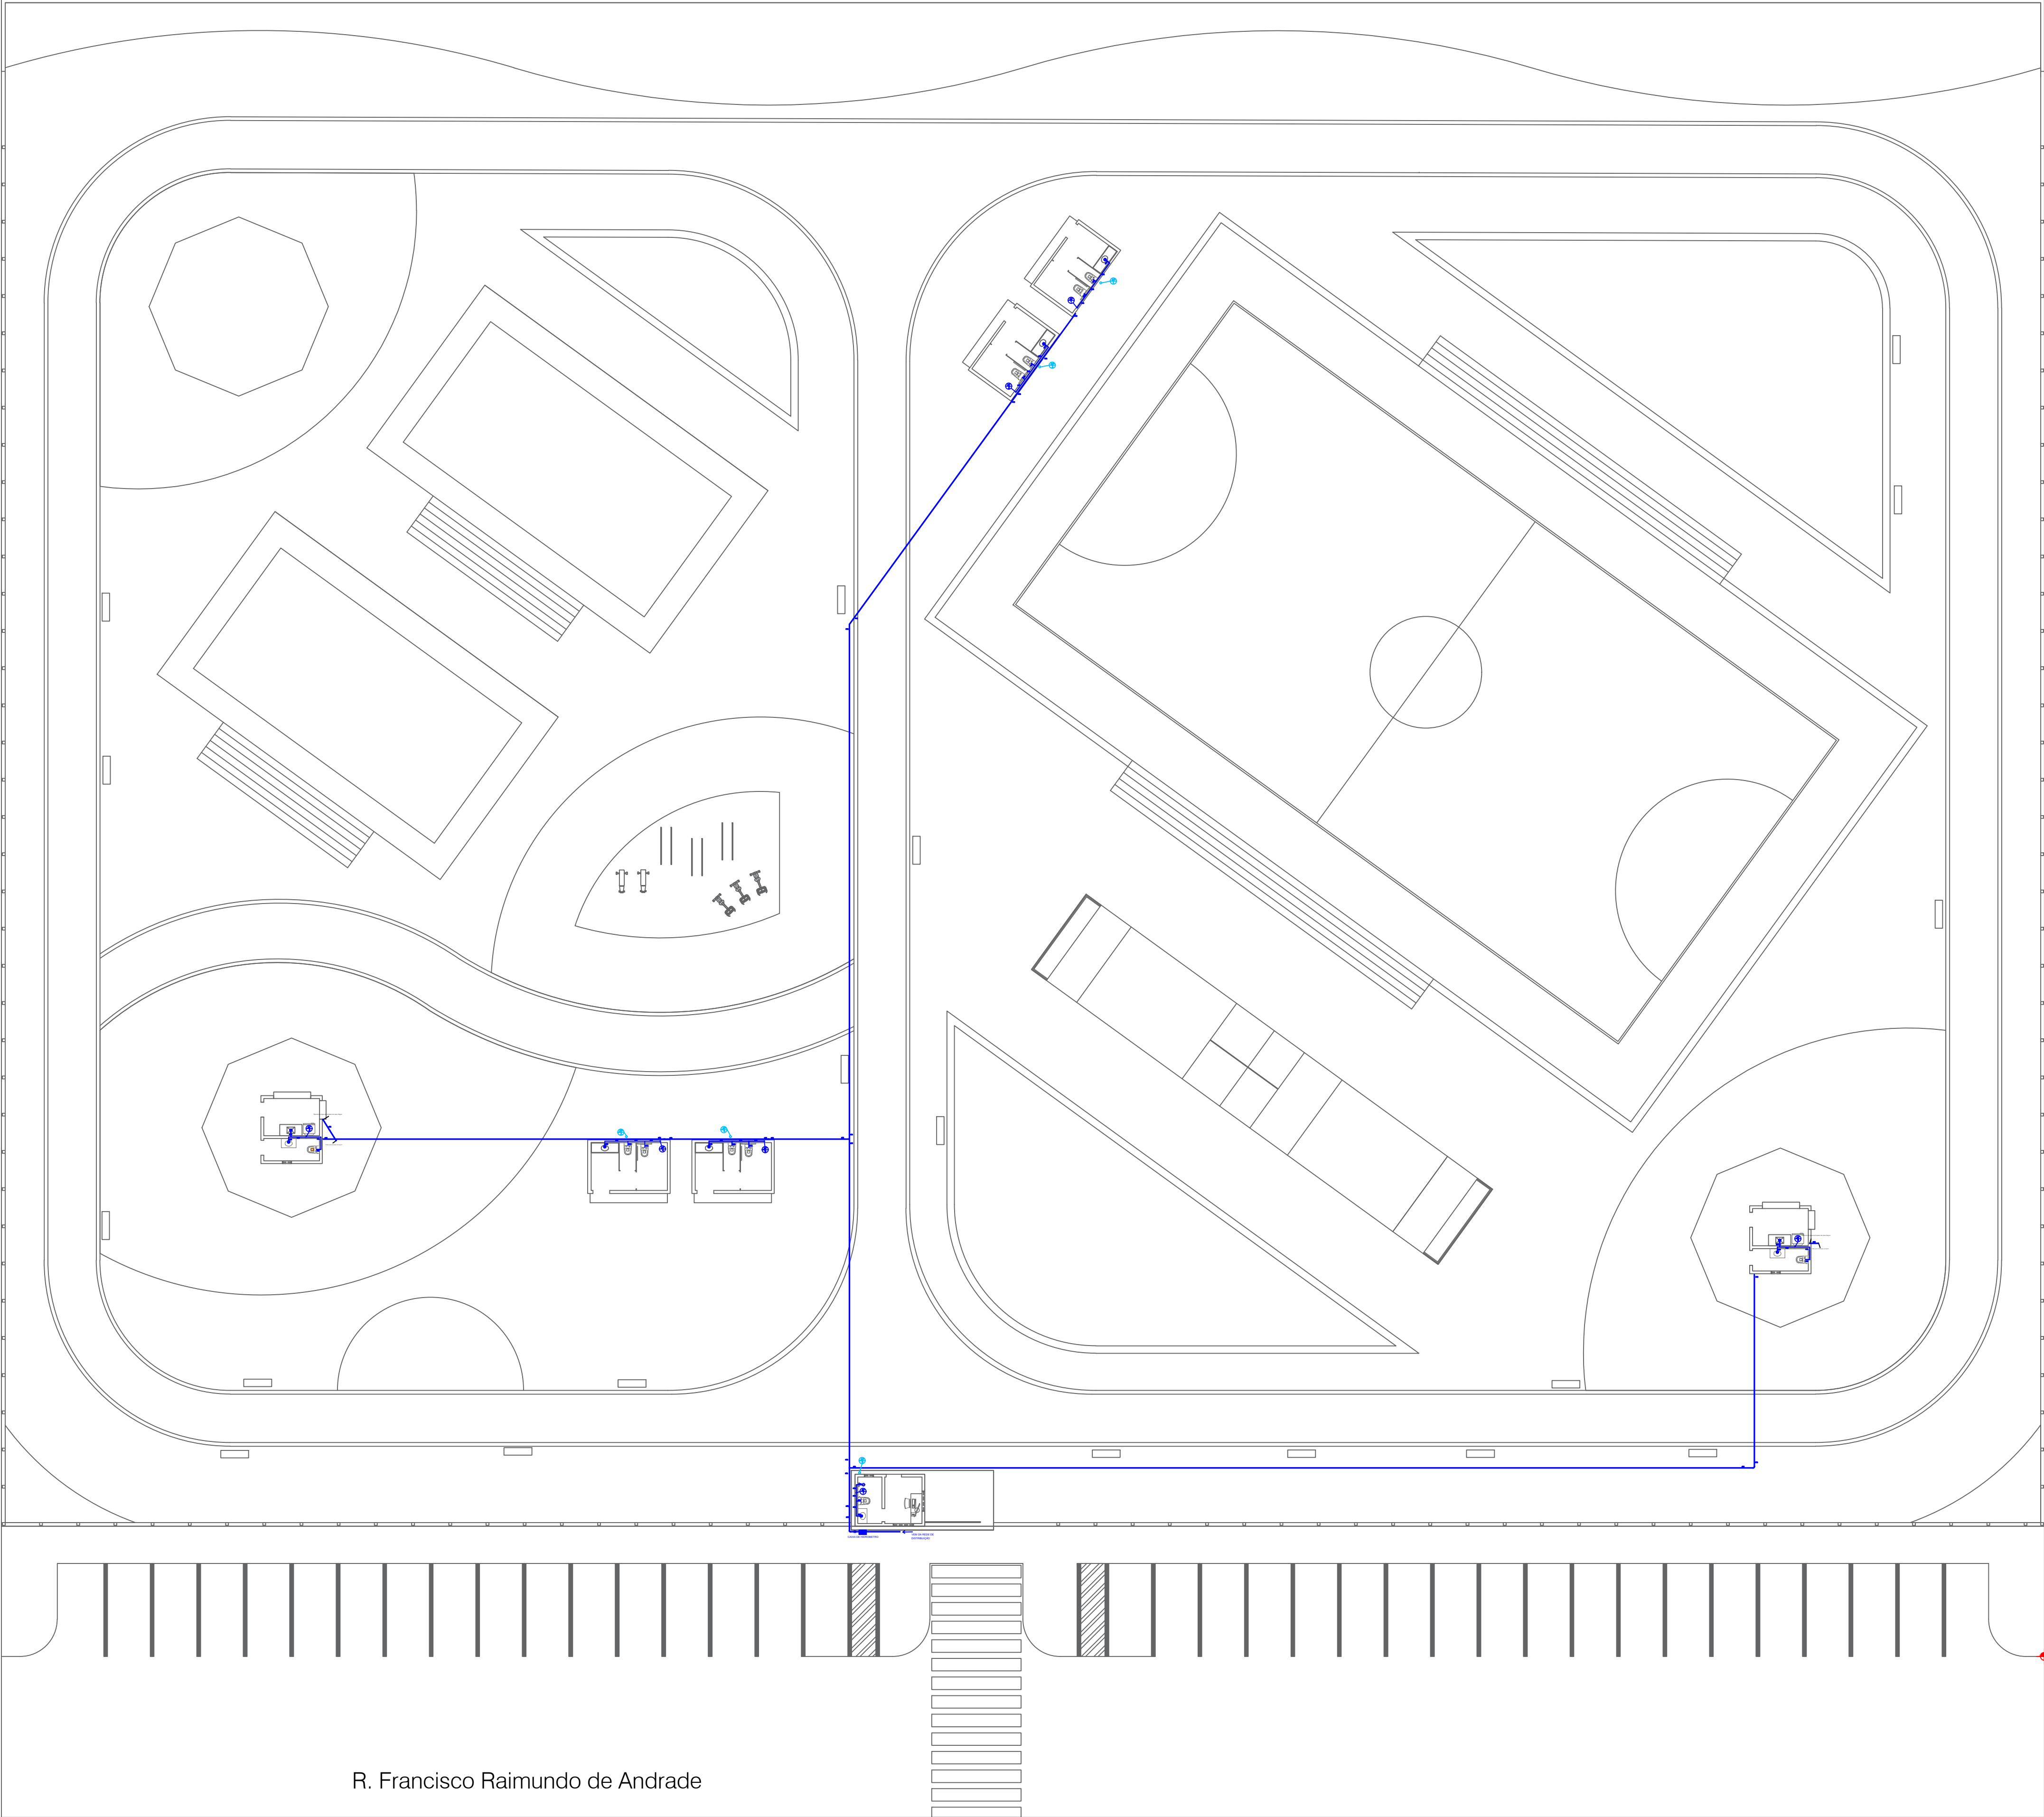

R. Francisco Raimundo de Andrade

PLANTA GERAL - COBERTA
COMPLEXO ESPORTIVO

ESC: 1/200

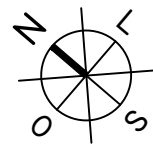

Projeto:

Projeto de Urbanismo Vila Olimpica

Desenhos:

PLANTA BAIXA COM DETALHAMENTO DOS PONTOS DE ÁGUAS FRIAS E PLUVIAIS

Observações:

- Conferir todas as medidas em obra antes da execução dos serviços.
- Não executar alterações sem autorização prévia do responsável técnico.
- Qualquer divergência entre projeto e condições de campo deverá ser comunicada ao responsável técnico para análise e aprovação.
- Todas as instalações deverão ser executadas por mão de obra qualificada, seguindo as normas técnicas vigentes e as recomendações dos fabricantes dos materiais empregados.
- O dimensionamento e posicionamentos indicados em projeto prevalecem sobre quaisquer informações complementares aqui descritas.

Esta prancha apresenta os detalhes das instalações de águas frias devendo sua execução seguir rigorosamente as dimensões, níveis, materiais e especificações indicados em projeto.

- Tubulação de abastecimento e distribuição principal: DN 32 mm.
- Tubulações de alimentação dos pontos de consumo: DN 25 mm.
- O reservatório superior será composto por:

Tubulação de alimentação controlada por torneira de boia;

Tubulação de abastecimento da rede de distribuição;

Tubulação de ventilação prolongada acima do nível máximo de água do reservatório;

Tubulação de limpeza (dreno) para esgotamento total do reservatório;

Extravasor (ladrão) interligado ao dreno, destinado à descarga do excedente de água em caso de falha do sistema de controle de nível.

• Todas as tubulações deverão ser executadas conforme os diâmetros, cotas e posicionamentos indicados em projeto.

• Deverão ser realizados testes de estanqueidade antes do fechamento de paredes, pisos e forros.

As instalações de águas pluviais foram dimensionadas e deverão ser executadas conforme as prescrições da ABNT NBR 10844.

- As águas provenientes da cobertura serão captadas por calhas e conduzidas através de condutores verticais e horizontais até o ponto de lançamento previsto em projeto.
- O extravasor do reservatório superior será direcionado para a rede de drenagem pluvial.
- As tubulações deverão obedecer aos diâmetros e declividades especificados em projeto.
- Deverá ser garantido o livre escoamento das águas pluviais, evitando acúmulo ou retorno de fluxo.
- As calhas, condutores e dispositivos de captação deverão permanecer livres de obstruções.

Projeta:

Fernando Matias Mamede

RESPONSÁVEL TÉCNICO

Fernando Matias Mamede

Engenheiro Civil

Crea: 162056275-8

Proprietário:

Prefeitura Municipal de Coremas

PROPRIETÁRIO(A)

Endereço/Obra:


Rua Francisco Raimundo de Andrade, DNOCS, Coremas - PB, 58770-000

ÁREAS	m²
Área do Terreno	10.733,41
Estacionamento	519,11
Calçada	249,64
Área verde	4.281,11

Prancha:

10/14


Detalhamento Hidráulico - Banheiros 1

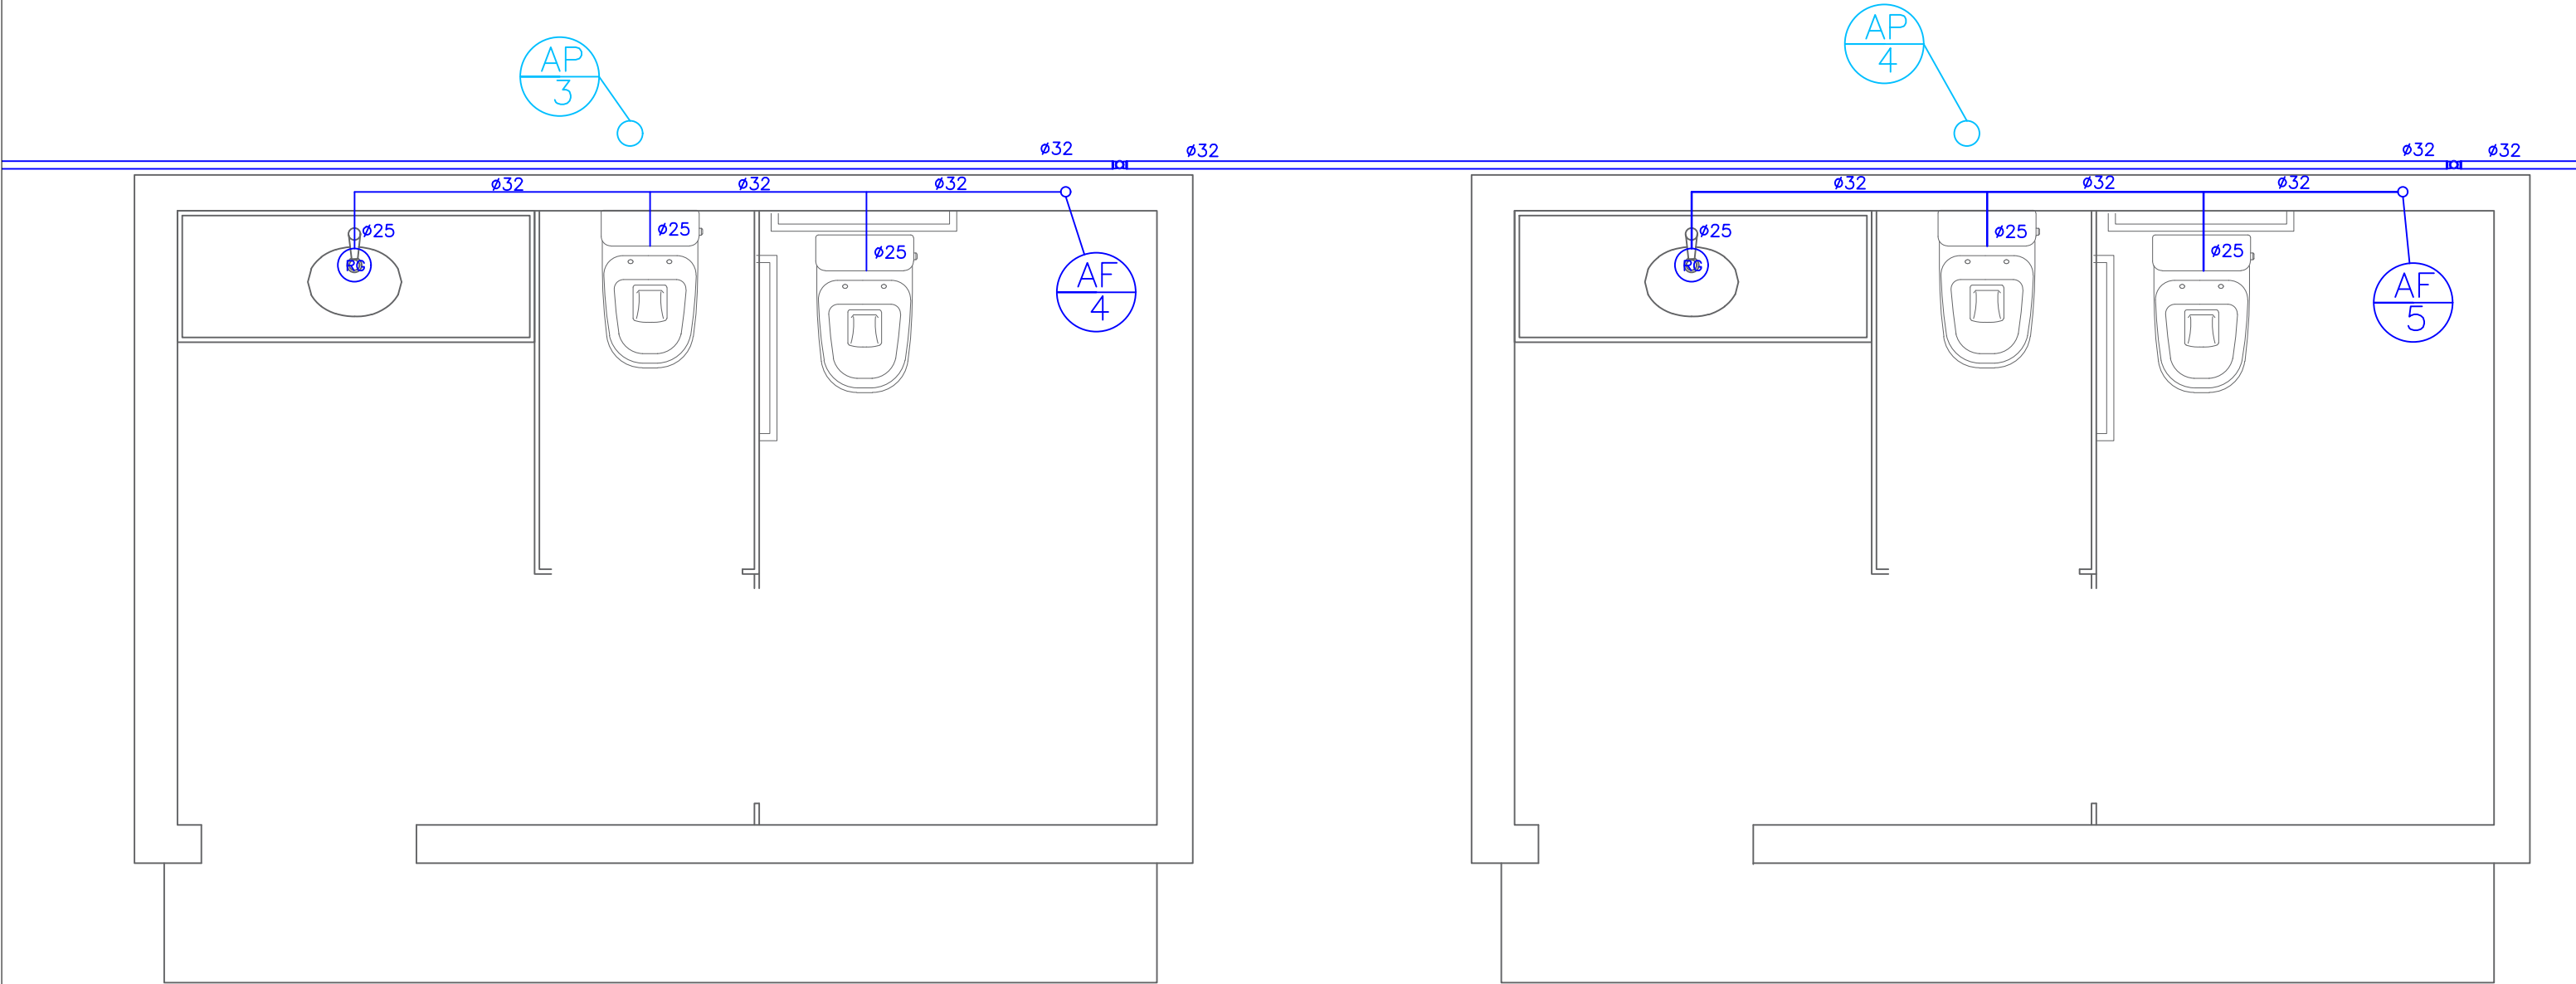


Detalhamento Hidráulico - Banheiros 2




Detalhamento Hidráulico - Quiosque 1

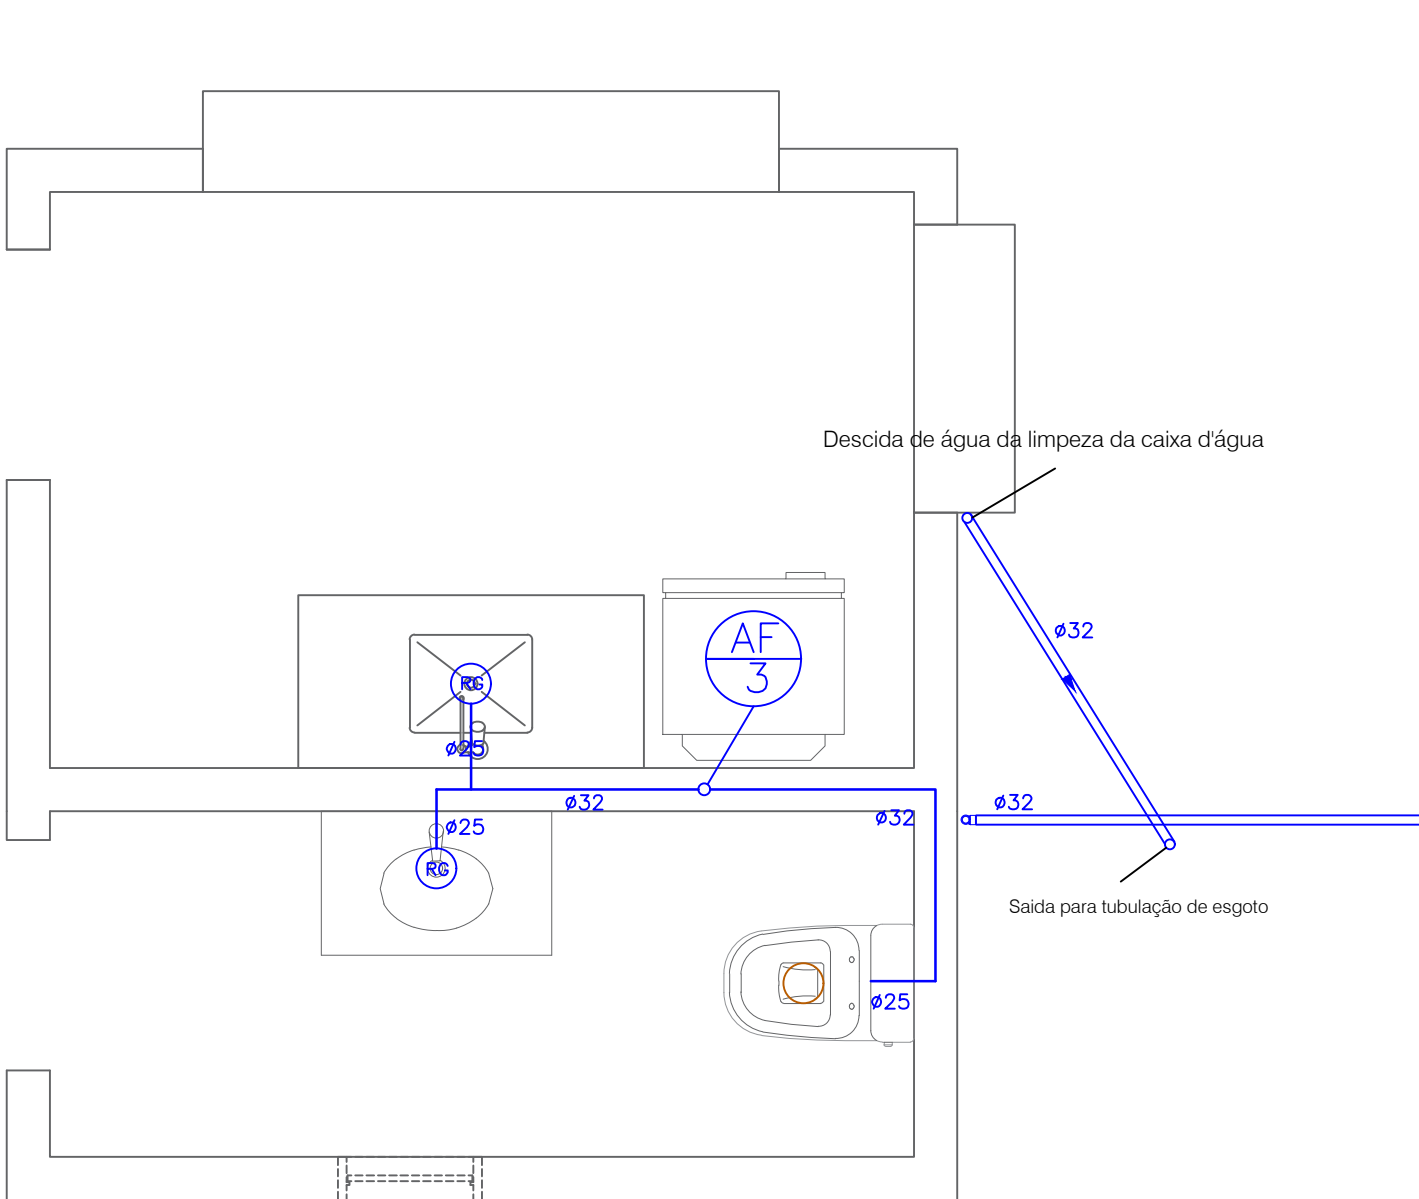

Detalhamento Hidráulico - Quiosque 2

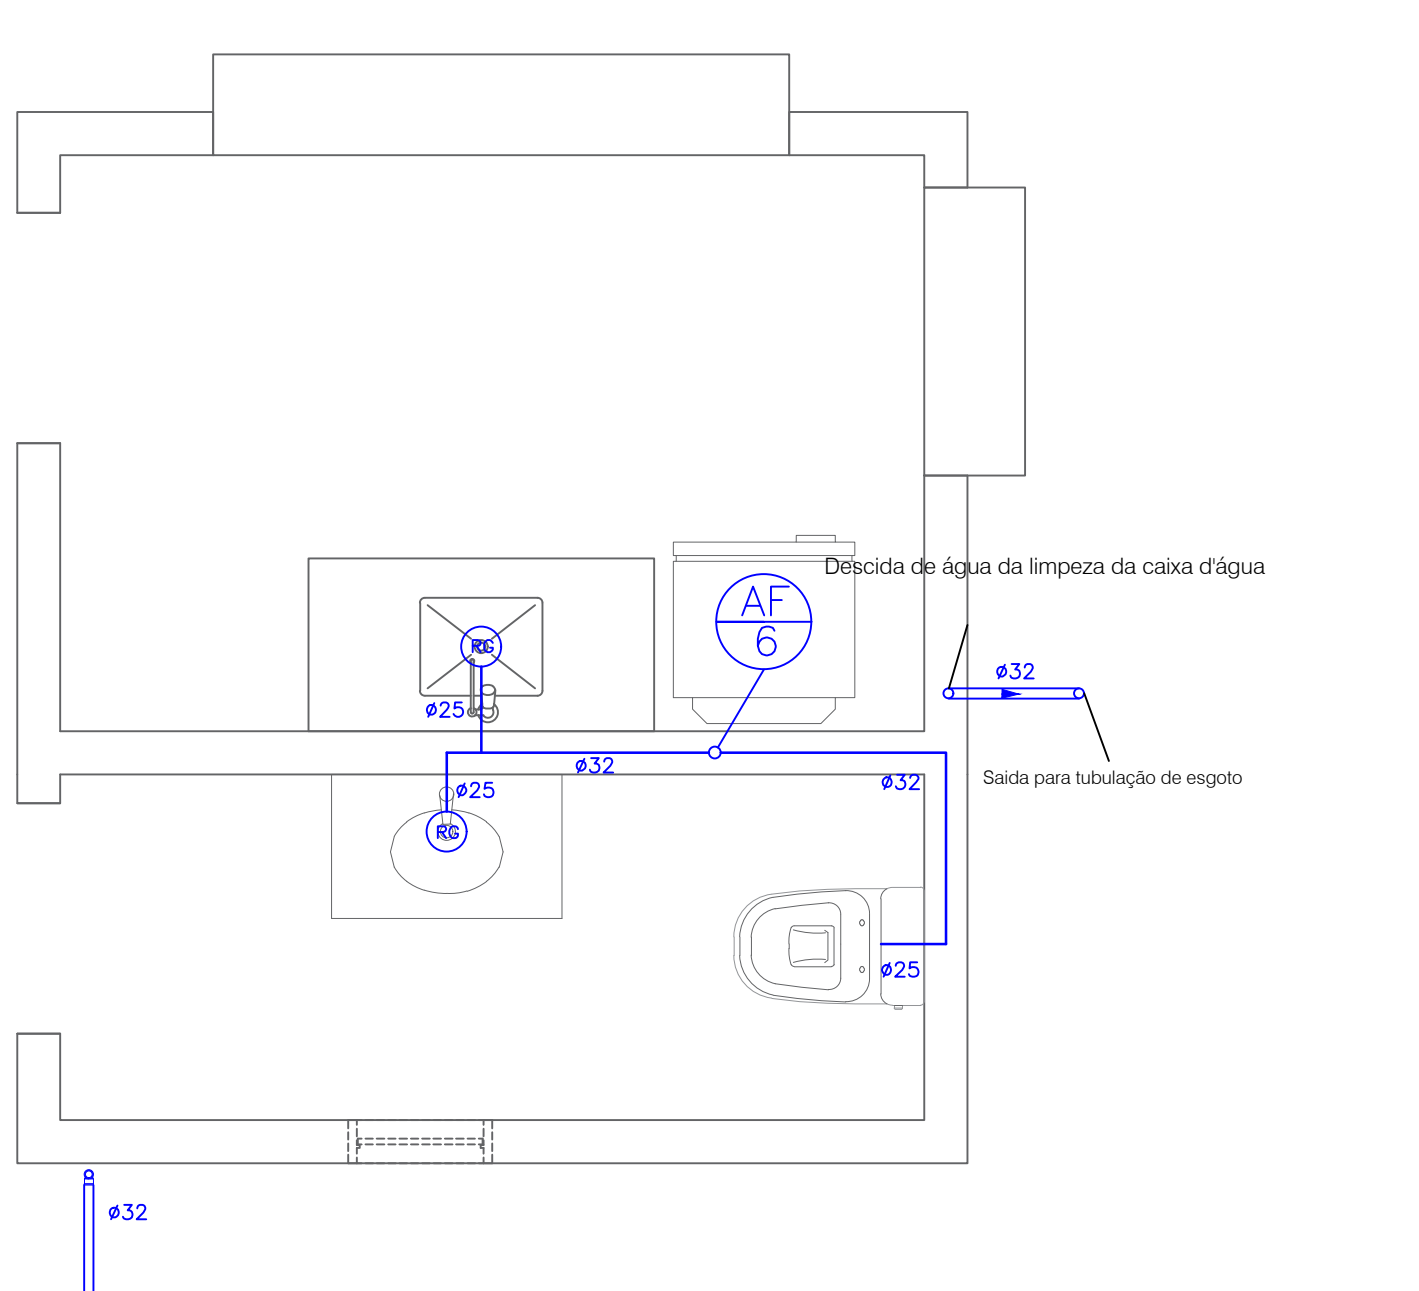

Detalhamento Hidráulico - Guarita

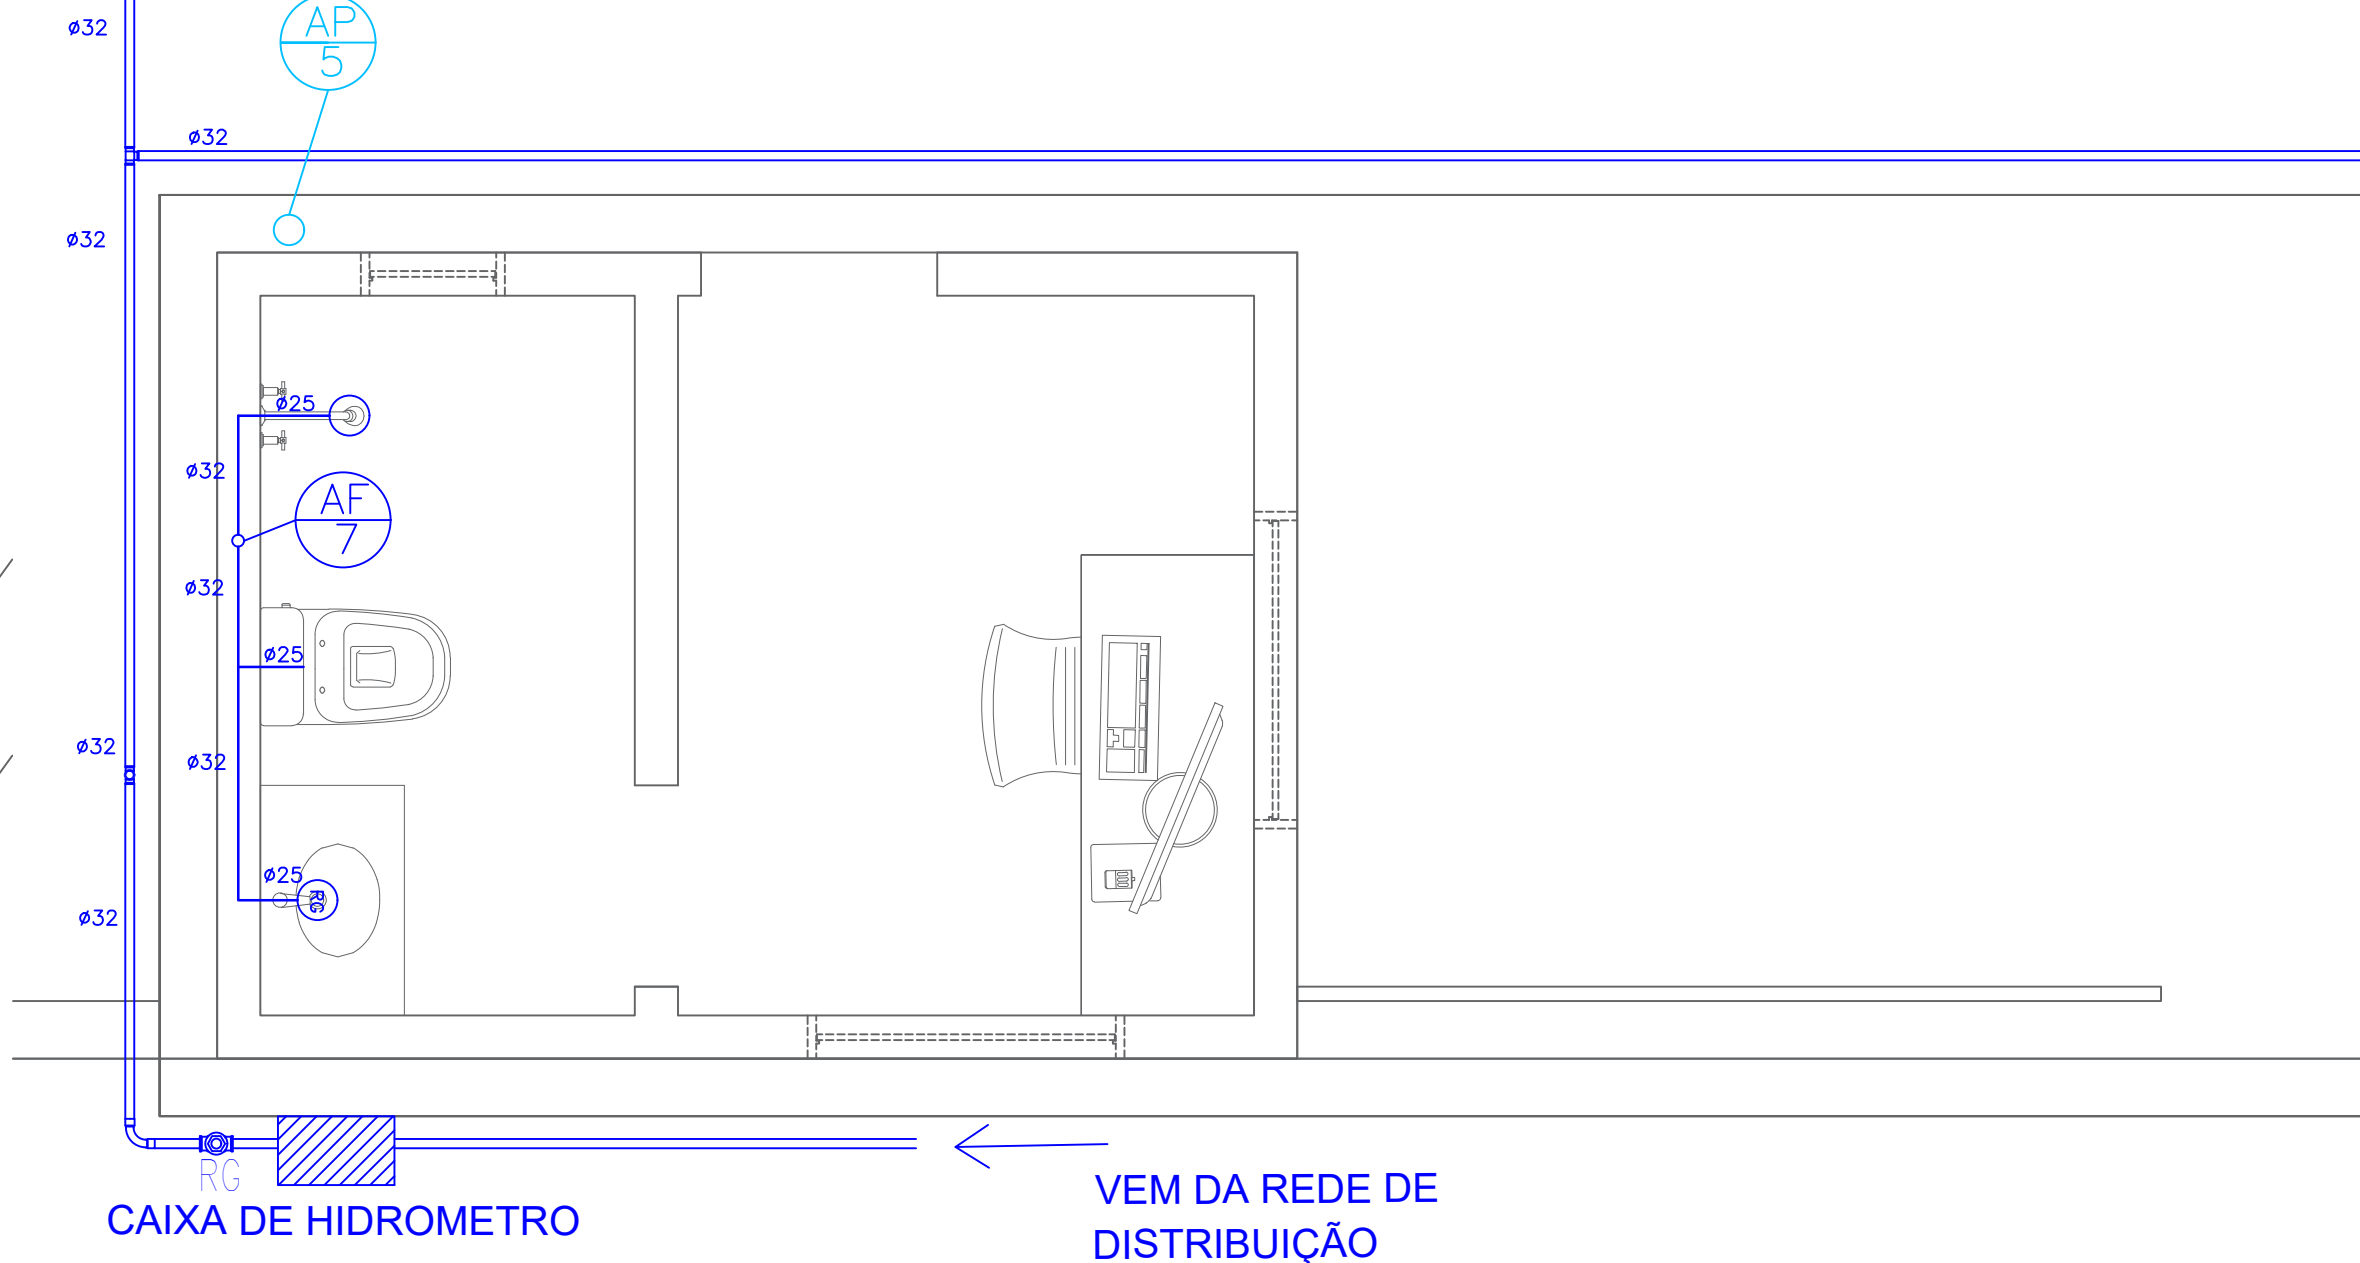

Projeto:

Projeto de Urbanismo Vila Olimpica

Desenhos:

PLANTA BAIXA COM DETALHAMENTO DOS PONTOS DE ÁGUAS FRIAS E PLUVIAIS

Observações:

- Conferir todas as medidas em obra antes da execução dos serviços.
- Não executar alterações sem autorização prévia do responsável técnico.
- Qualquer divergência entre projeto e condições de campo deverá ser comunicada ao responsável técnico para análise e aprovação.
- Todas as instalações deverão ser executadas por mão de obra qualificada, seguindo as normas técnicas vigentes e as recomendações dos fabricantes dos materiais empregados.
- O dimensionamento e posicionamentos indicados em projeto prevalecem sobre quaisquer informações complementares aqui descritas.

Esta prancha apresenta os detalhes das instalações de águas frias devendo sua execução seguir rigorosamente as dimensões, níveis, materiais e especificações indicados em projeto.

- Tubulação de abastecimento e distribuição principal: DN 32 mm.
- Tubulações de alimentação dos pontos de consumo: DN 25 mm.
- O reservatório superior será composto por:

Tubulação de alimentação controlada por torneira de boia;
Tubulação de abastecimento da rede de distribuição;
Tubulação de ventilação prolongada acima do nível máximo de água do reservatório;
Tubulação de limpeza (dreno) para esgotamento total do reservatório;
Extravasor (ladrão) interligado ao dreno, destinado à descarga do excedente de água em caso de falha do sistema de controle de nível.

- Todas as tubulações deverão ser executadas conforme os diâmetros, cotas e posicionamentos indicados em projeto.
- Deverão ser realizados testes de estanqueidade antes do fechamento de paredes, pisos e forros.

As instalações de águas pluviais foram dimensionadas e deverão ser executadas conforme as prescrições da ABNT NBR 10844.

- As águas provenientes da cobertura serão captadas por calhas e conduzidas através de condutores verticais e horizontais até o ponto de lançamento previsto em projeto.
- O extravasor do reservatório superior será direcionado para a rede de drenagem pluvial.
- As tubulações deverão obedecer aos diâmetros e declividades especificados em projeto.
- Deverá ser garantido o livre escoamento das águas pluviais, evitando acúmulo ou retorno de fluxo.
- As calhas, condutores e dispositivos de captação deverão permanecer livres de obstruções.

Projetista:

Fernando Matias Mamede

RESPONSÁVEL TÉCNICO
Fernando Matias Mamede
Engenheiro Civil
Crea: 162056275-8

Proprietário:

Prefeitura Municipal de Coremas

PROPRIETÁRIO(A)


Endereço/Obra: Rua Francisco Raimundo de Andrade, DNOCS, Coremas - PB, 58770-000

ÁREAS	m²
Área do Terreno	10.733,41
Estacionamento	519,11
Calçada	249,64
Área verde	4.281,11


Prancha:

11/14


Detalhamento Hidráulico - Banheiros 1

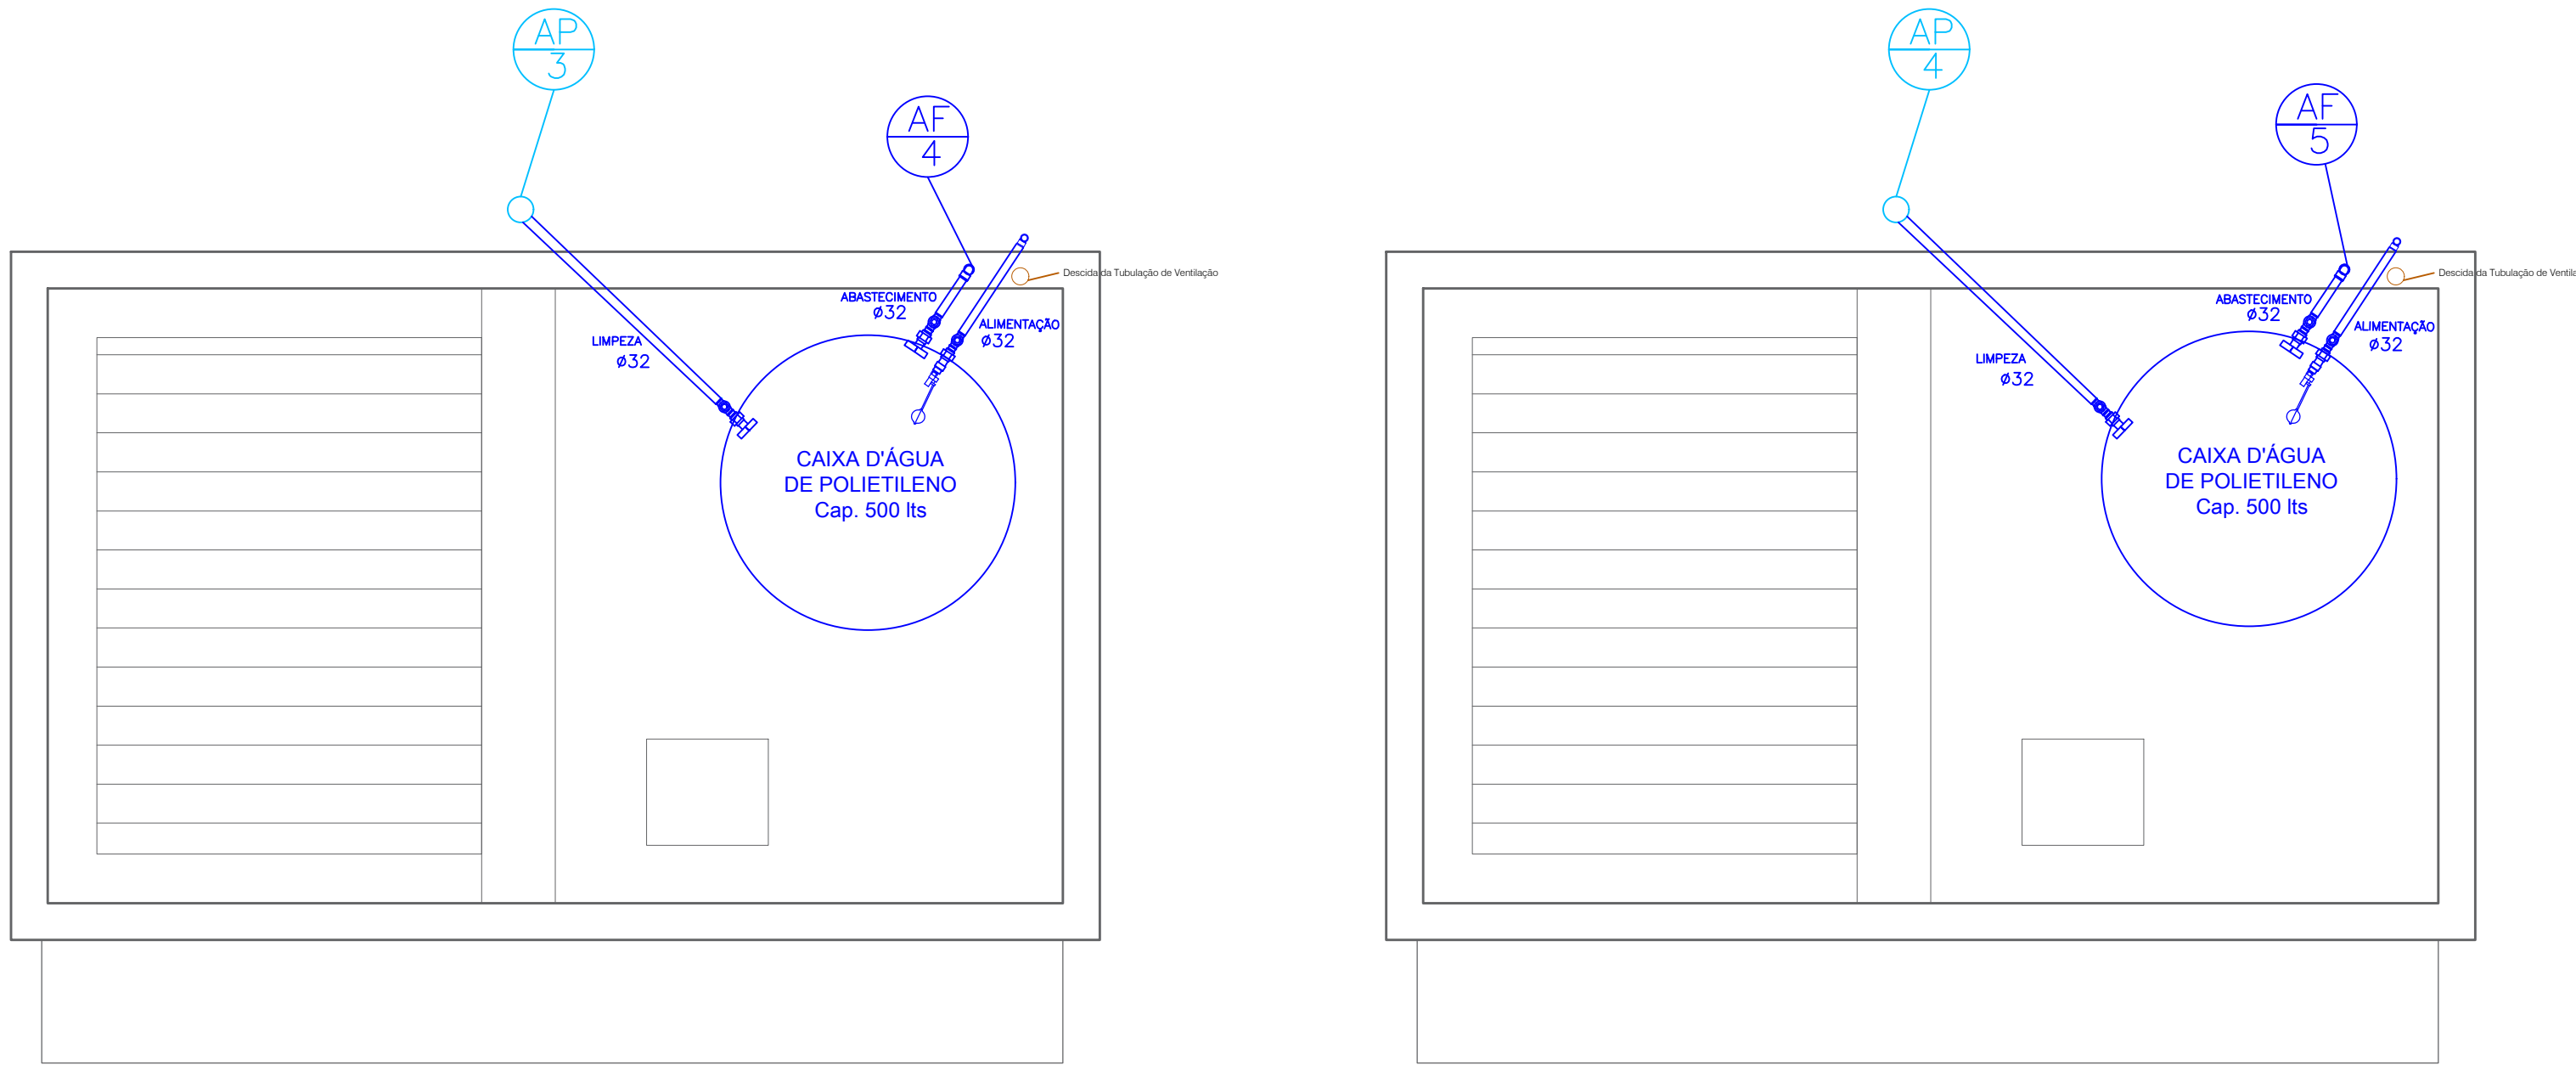


Detalhamento Hidráulico - Banheiros 2

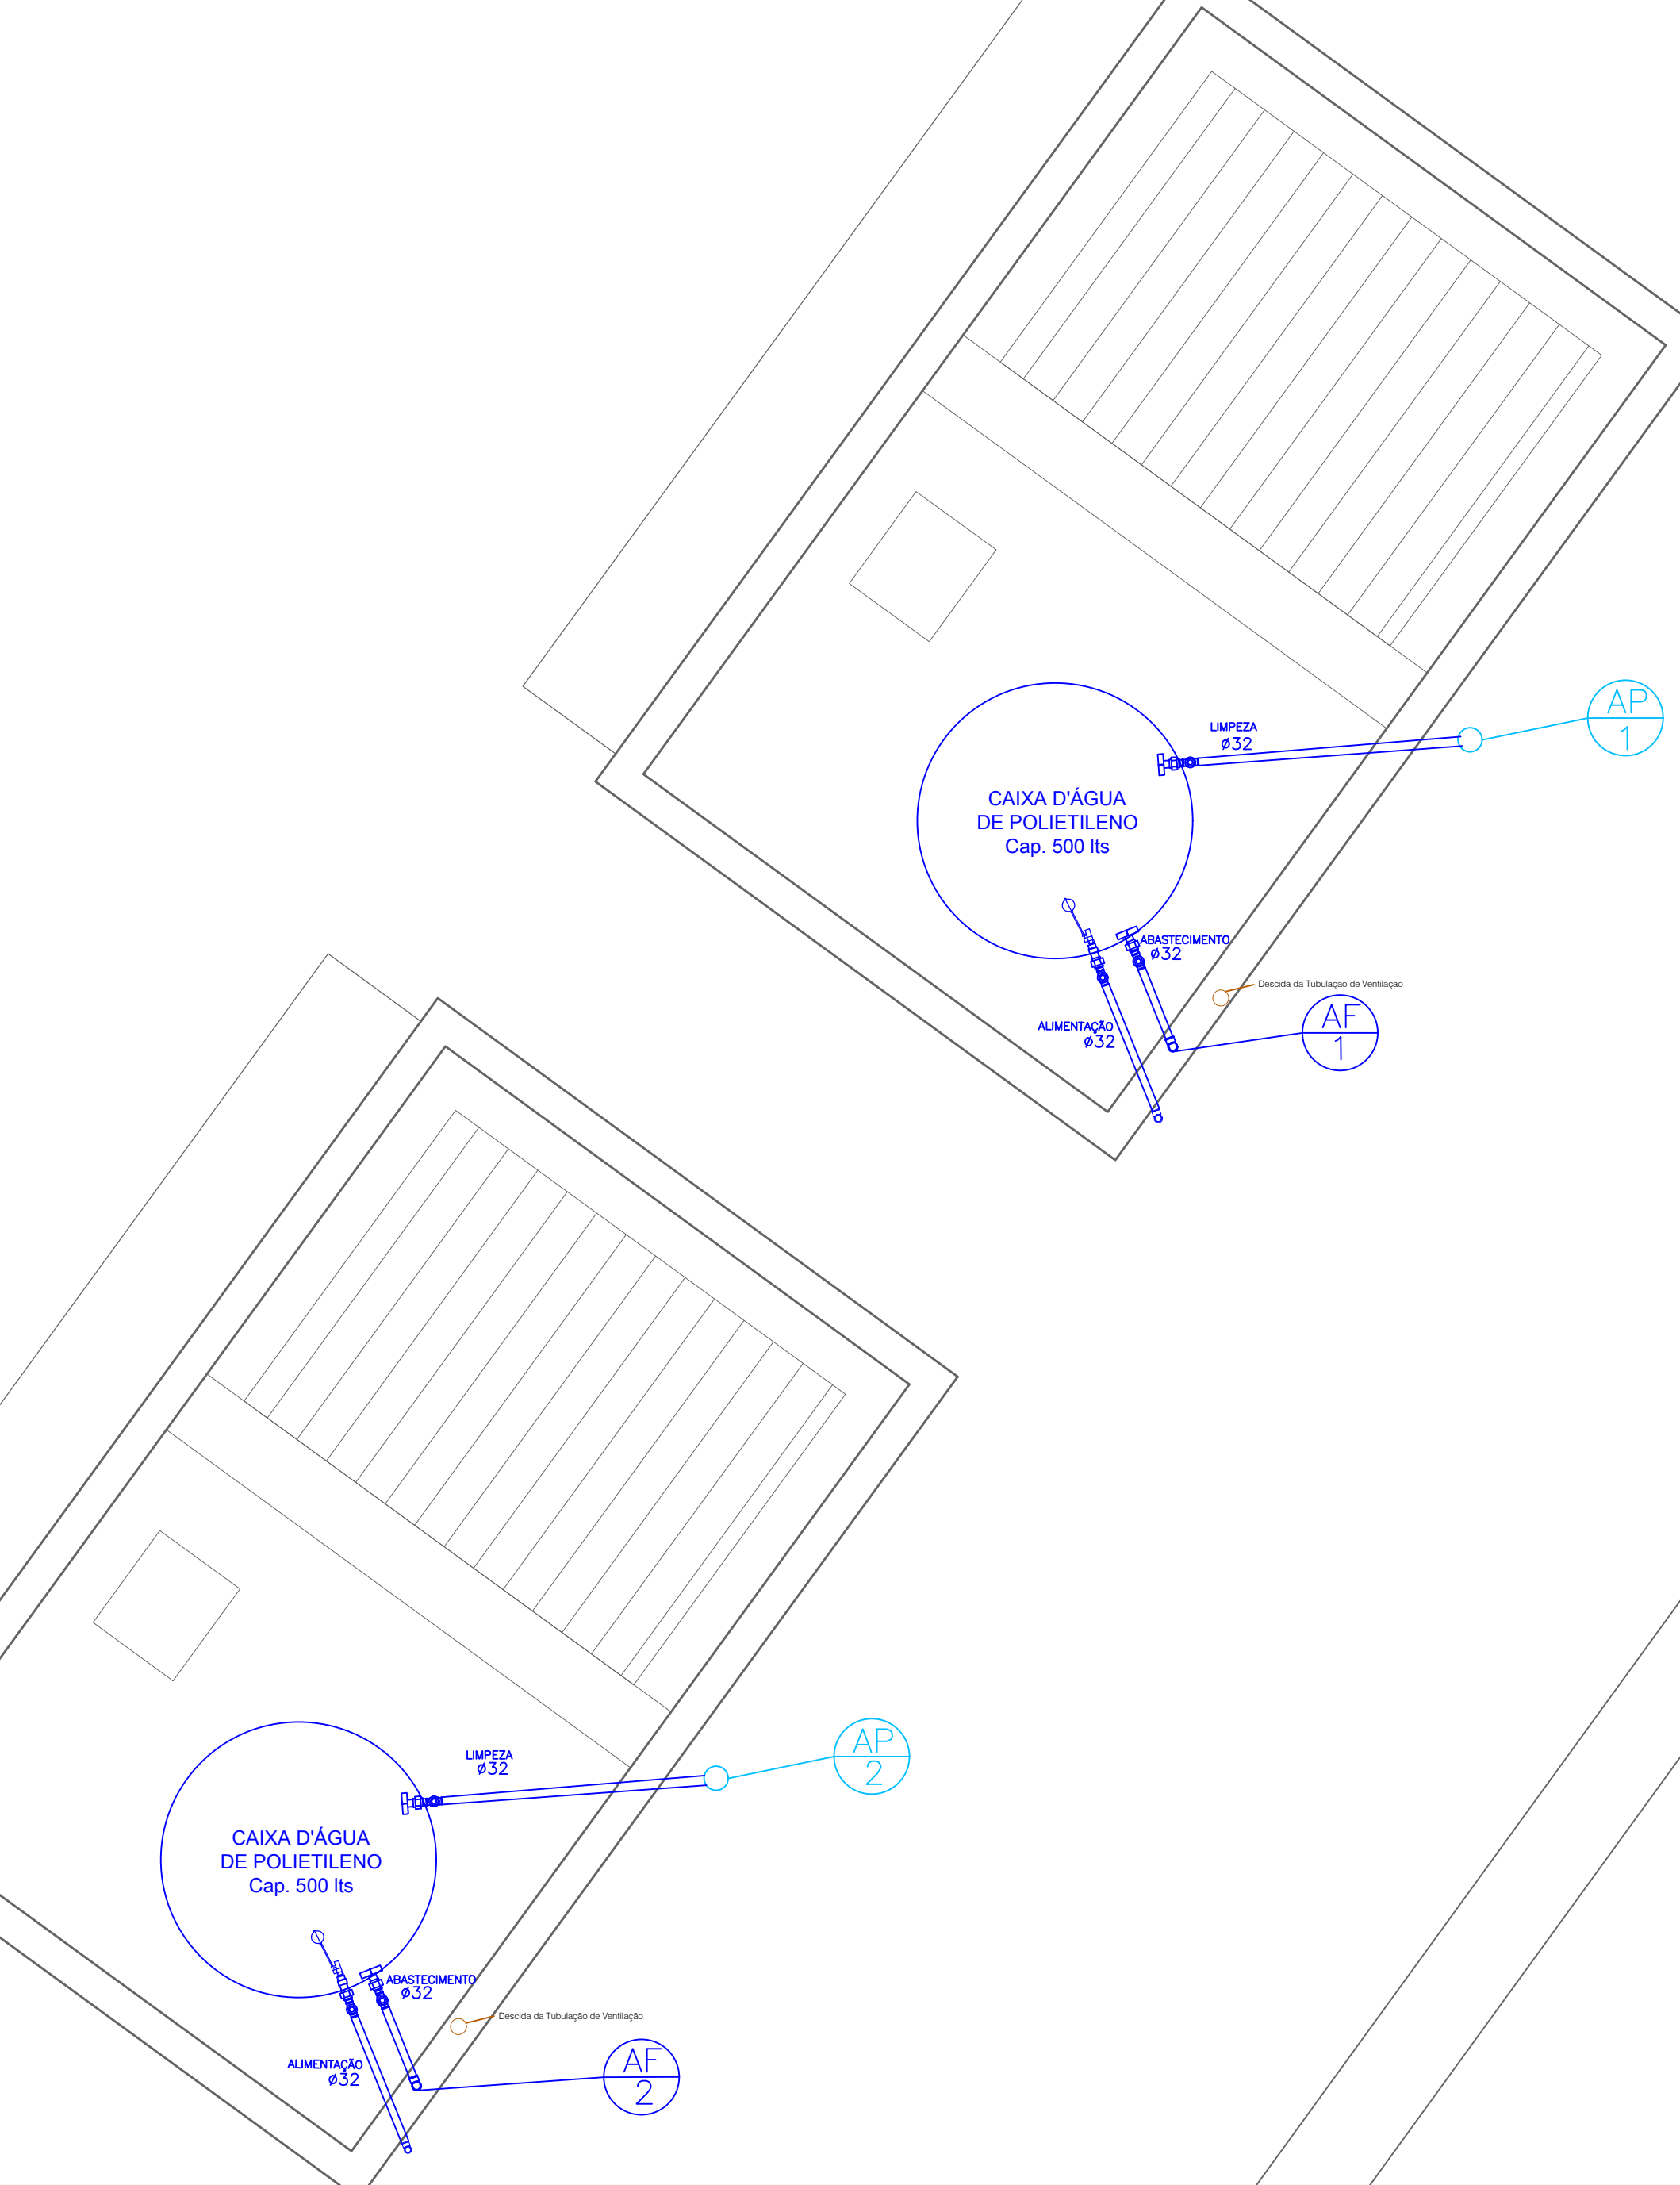


Detalhamento Hidráulico - Guarita

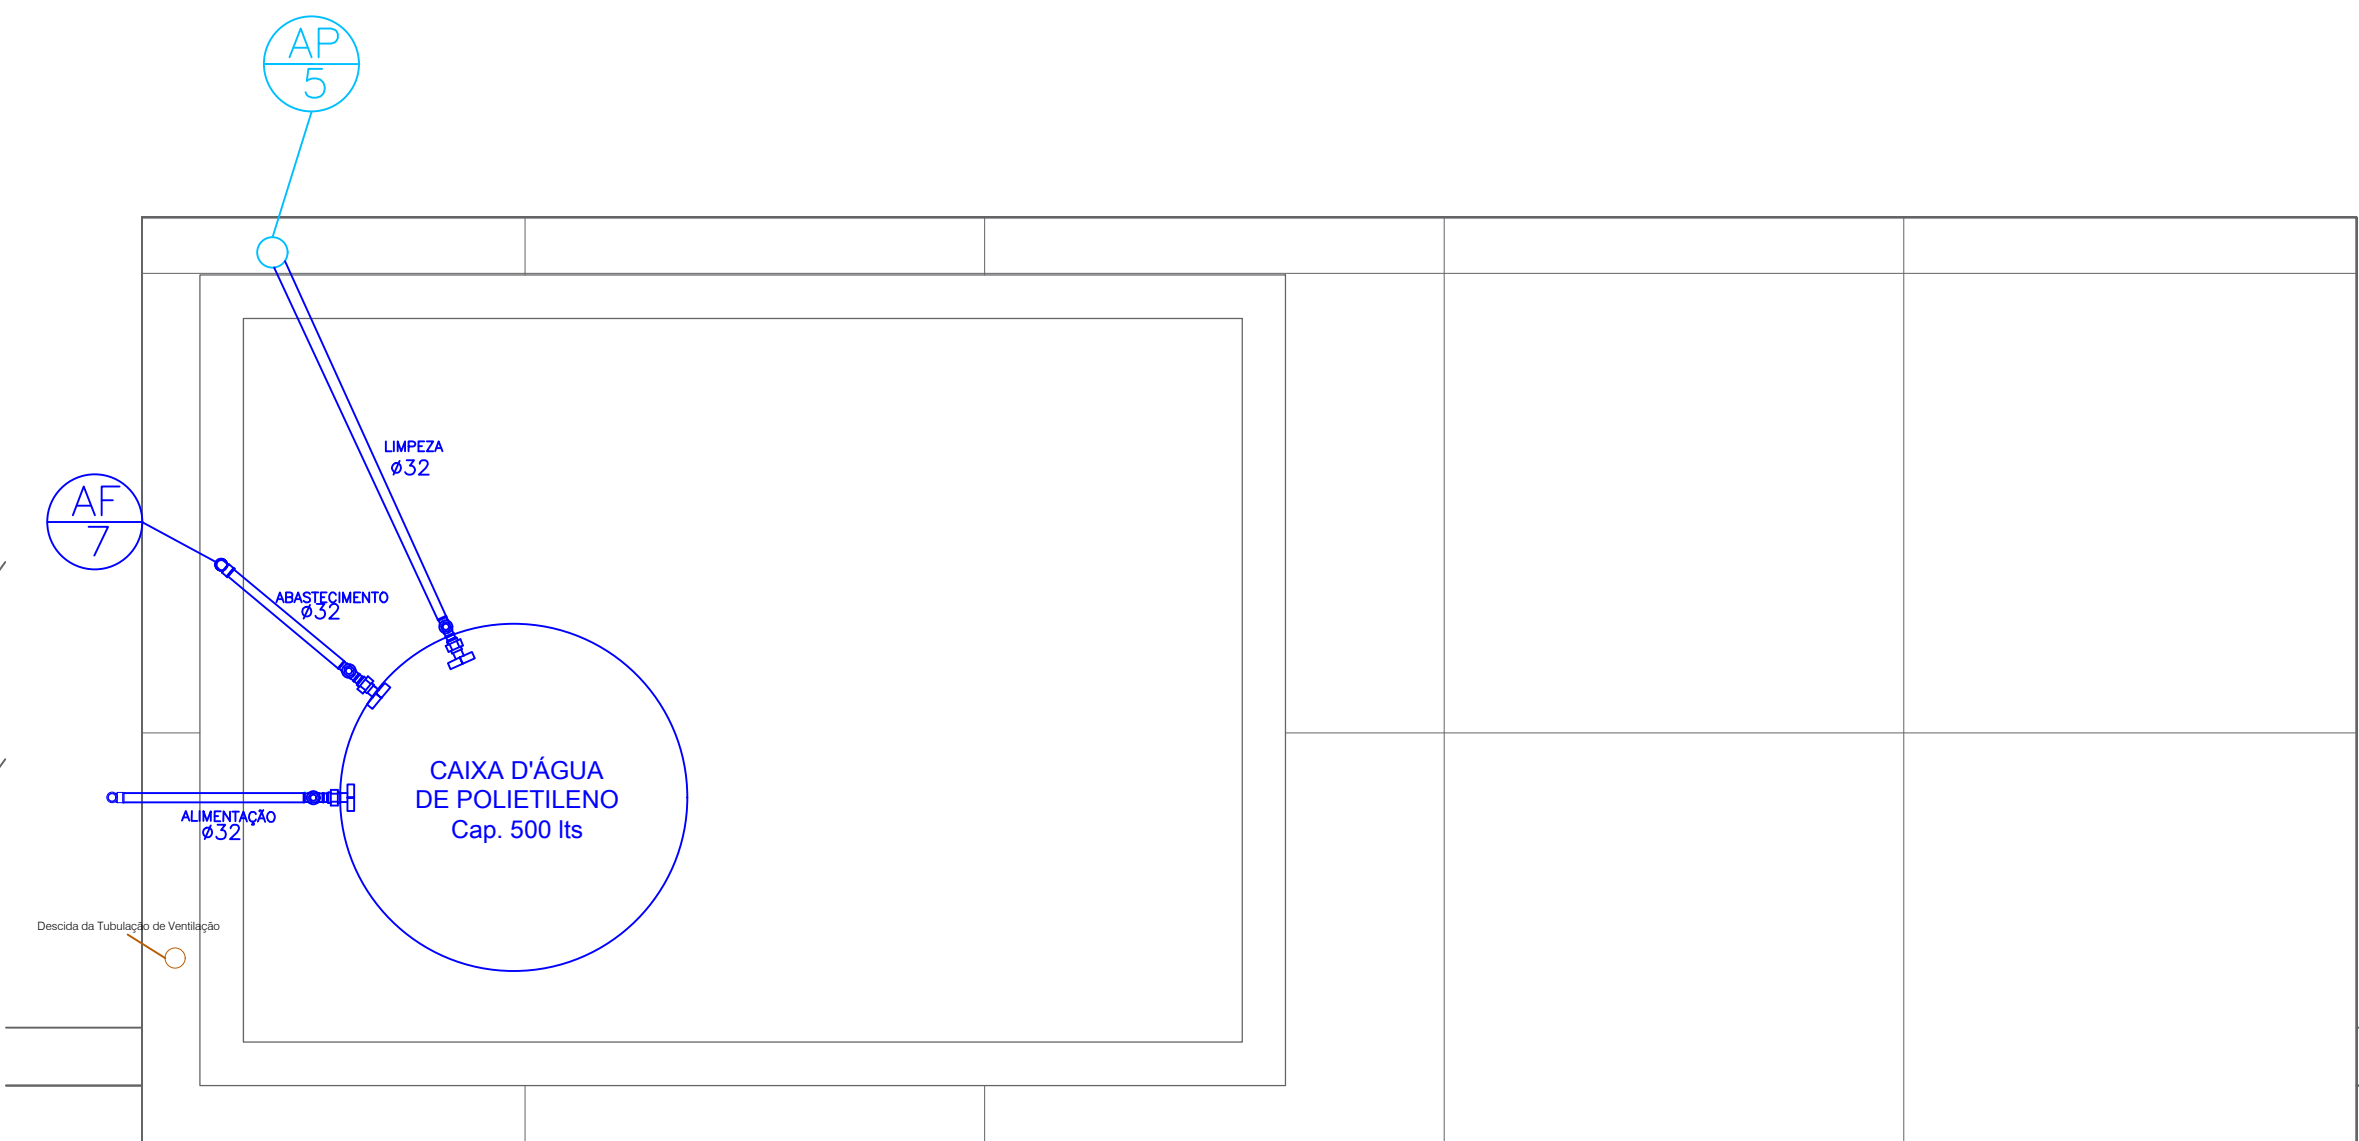

Detalhamento Hidráulico - Quiosque 1

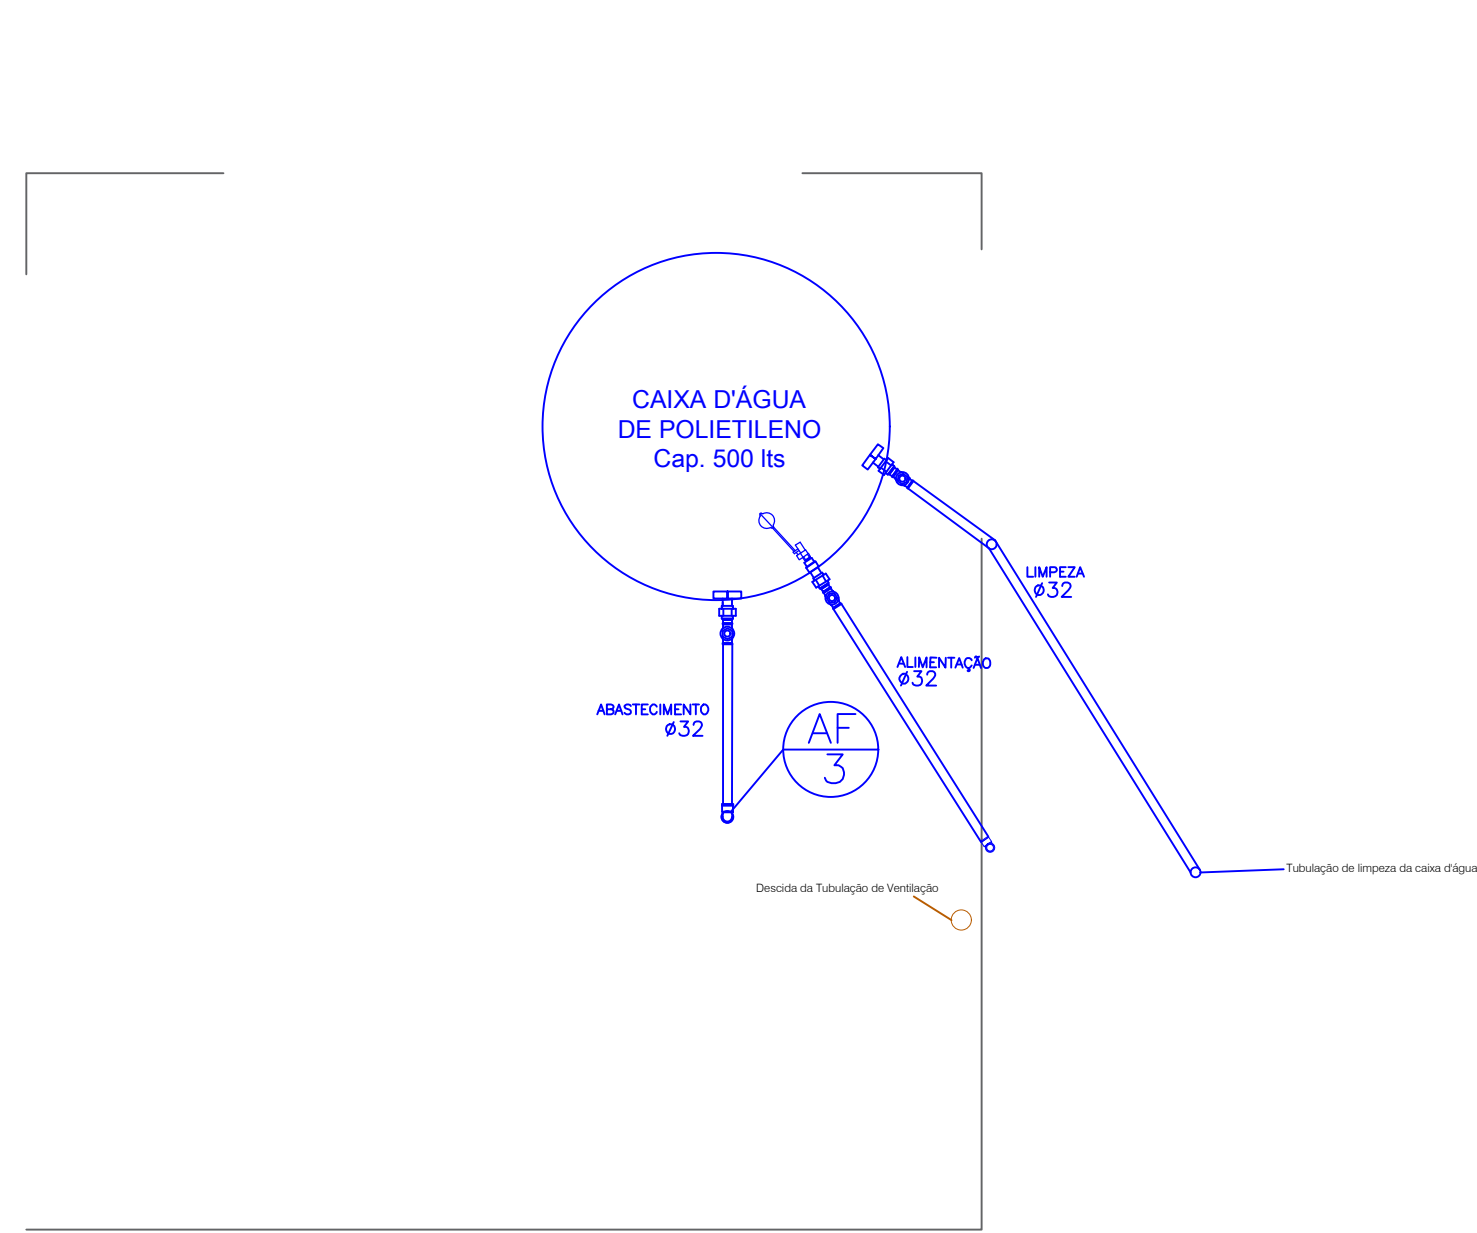

Detalhamento Hidráulico - Quiosque 2

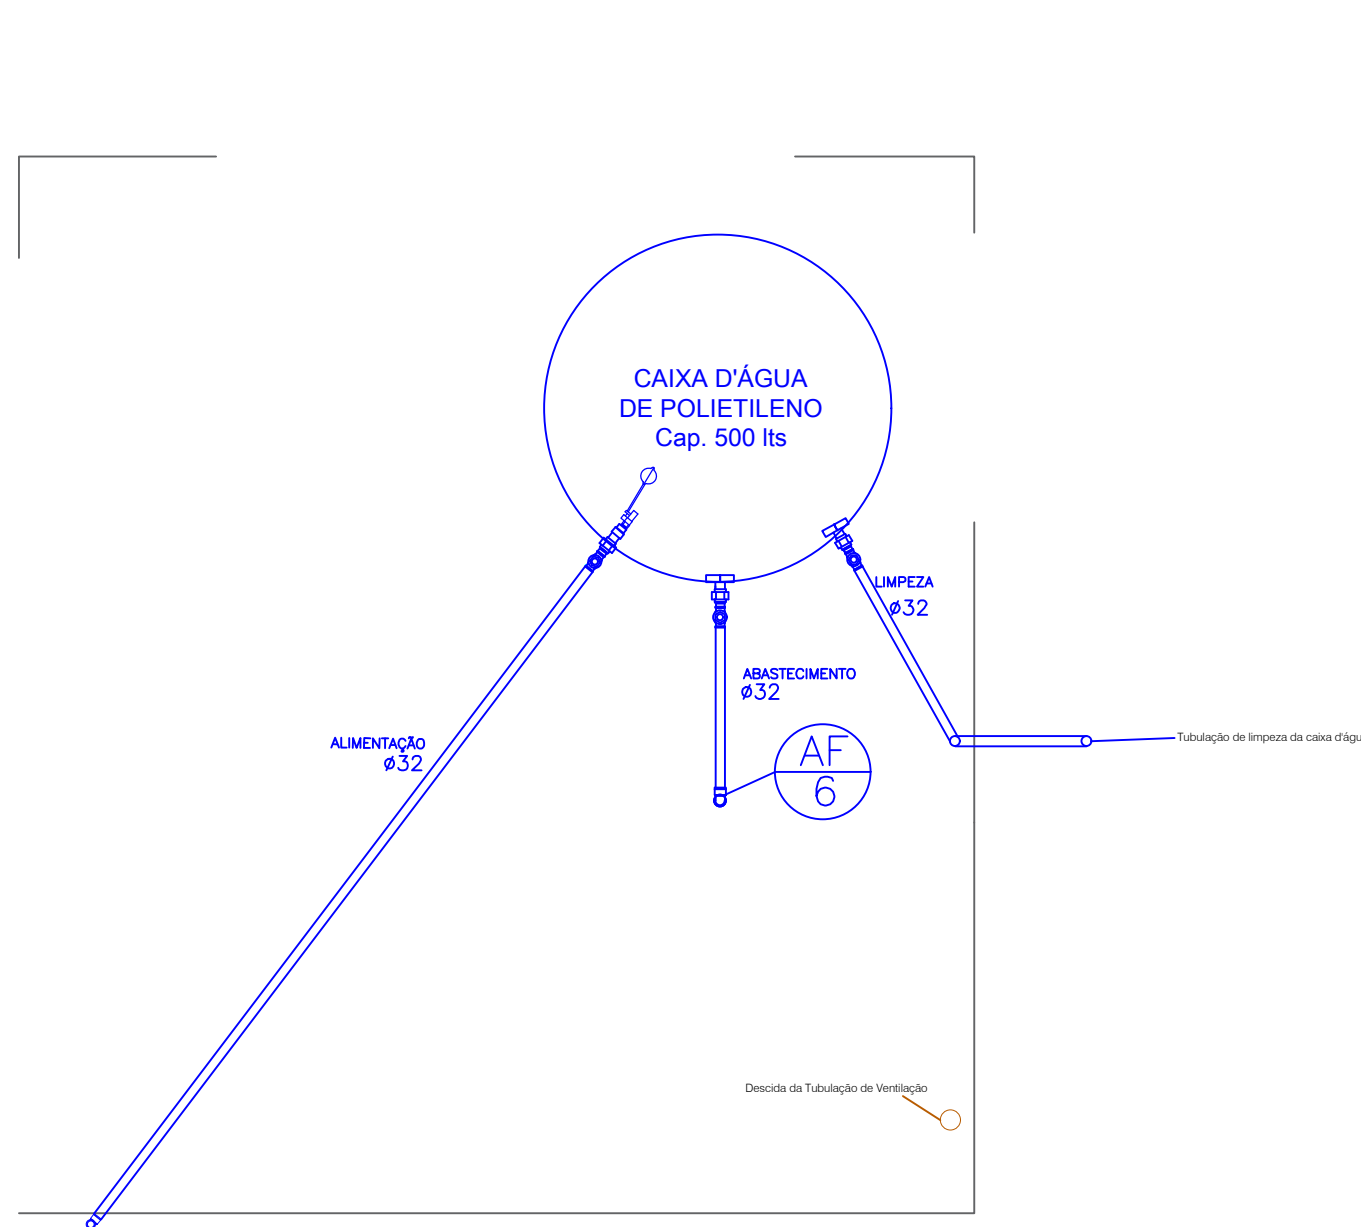

Projeto:

Projeto de Urbanismo Vila Olimpica

Desenhos:

PLANTA BAIXA COM DETALHAMENTO DOS PONTOS DE ÁGUAS FRIAS E PLUVIAIS

Observações:

- Conferir todas as medidas em obra antes da execução dos serviços.
- Não executar alterações sem autorização prévia do responsável técnico.
- Qualquer divergência entre projeto e condições de campo deverá ser comunicada ao responsável técnico para análise e aprovação.
- Todas as instalações deverão ser executadas por mão de obra qualificada, seguindo as normas técnicas vigentes e as recomendações dos fabricantes dos materiais empregados.
- O dimensionamento e posicionamentos indicados em projeto prevalecem sobre quaisquer informações complementares aqui descritas.

Esta prancha apresenta os detalhes das instalações de águas frias devendo sua execução seguir rigorosamente as dimensões, níveis, materiais e especificações indicados em projeto.

- Tubulação de abastecimento e distribuição principal: DN 32 mm.
- Tubulações de alimentação dos pontos de consumo: DN 25 mm.
- O reservatório superior será composto por:

Tubulação de alimentação controlada por torneira de boia;
Tubulação de abastecimento da rede de distribuição;
Tubulação de ventilação prolongada acima do nível máximo de água do reservatório;
Tubulação de limpeza (dreno) para esgotamento total do reservatório;
Extravassor (ladrão) interligado ao dreno, destinado à descarga do excedente de água em caso de falha do sistema de controle de nível.

- Todas as tubulações deverão ser executadas conforme os diâmetros, cotas e posicionamentos indicados em projeto.
- Deverão ser realizados testes de estanqueidade antes do fechamento de paredes, pisos e forros.

As instalações de águas pluviais foram dimensionadas e deverão ser executadas conforme as prescrições da ABNT NBR 10844.

- As águas provenientes da cobertura serão captadas por calhas e conduzidas através de condutores verticais e horizontais até o ponto de lançamento previsto em projeto.
- O extravassor do reservatório superior será direcionado para a rede de drenagem pluvial.
- As tubulações deverão obedecer aos diâmetros e declividades especificados em projeto.
- Deverá ser garantido o livre escoamento das águas pluviais, evitando acúmulo ou retorno de fluxo.
- As calhas, condutores e dispositivos de captação deverão permanecer livres de obstruções.

Proprietário:

Prefeitura Municipal de Coremas

Responsável Técnico:

Fernando Matias Mamede
Engenheiro Civil
Crea: 162056275-8

Proprietário(a):

Endereço/Obra:

Rua Francisco Raimundo de Andrade, DNOCS, Coremas - PB, 58770-000

ÁREAS

m²

Área do Terreno

10.733,41

Estacionamento

519,11

Calçada


249,64

Área verde

4.281,11


Prancha:

12/14

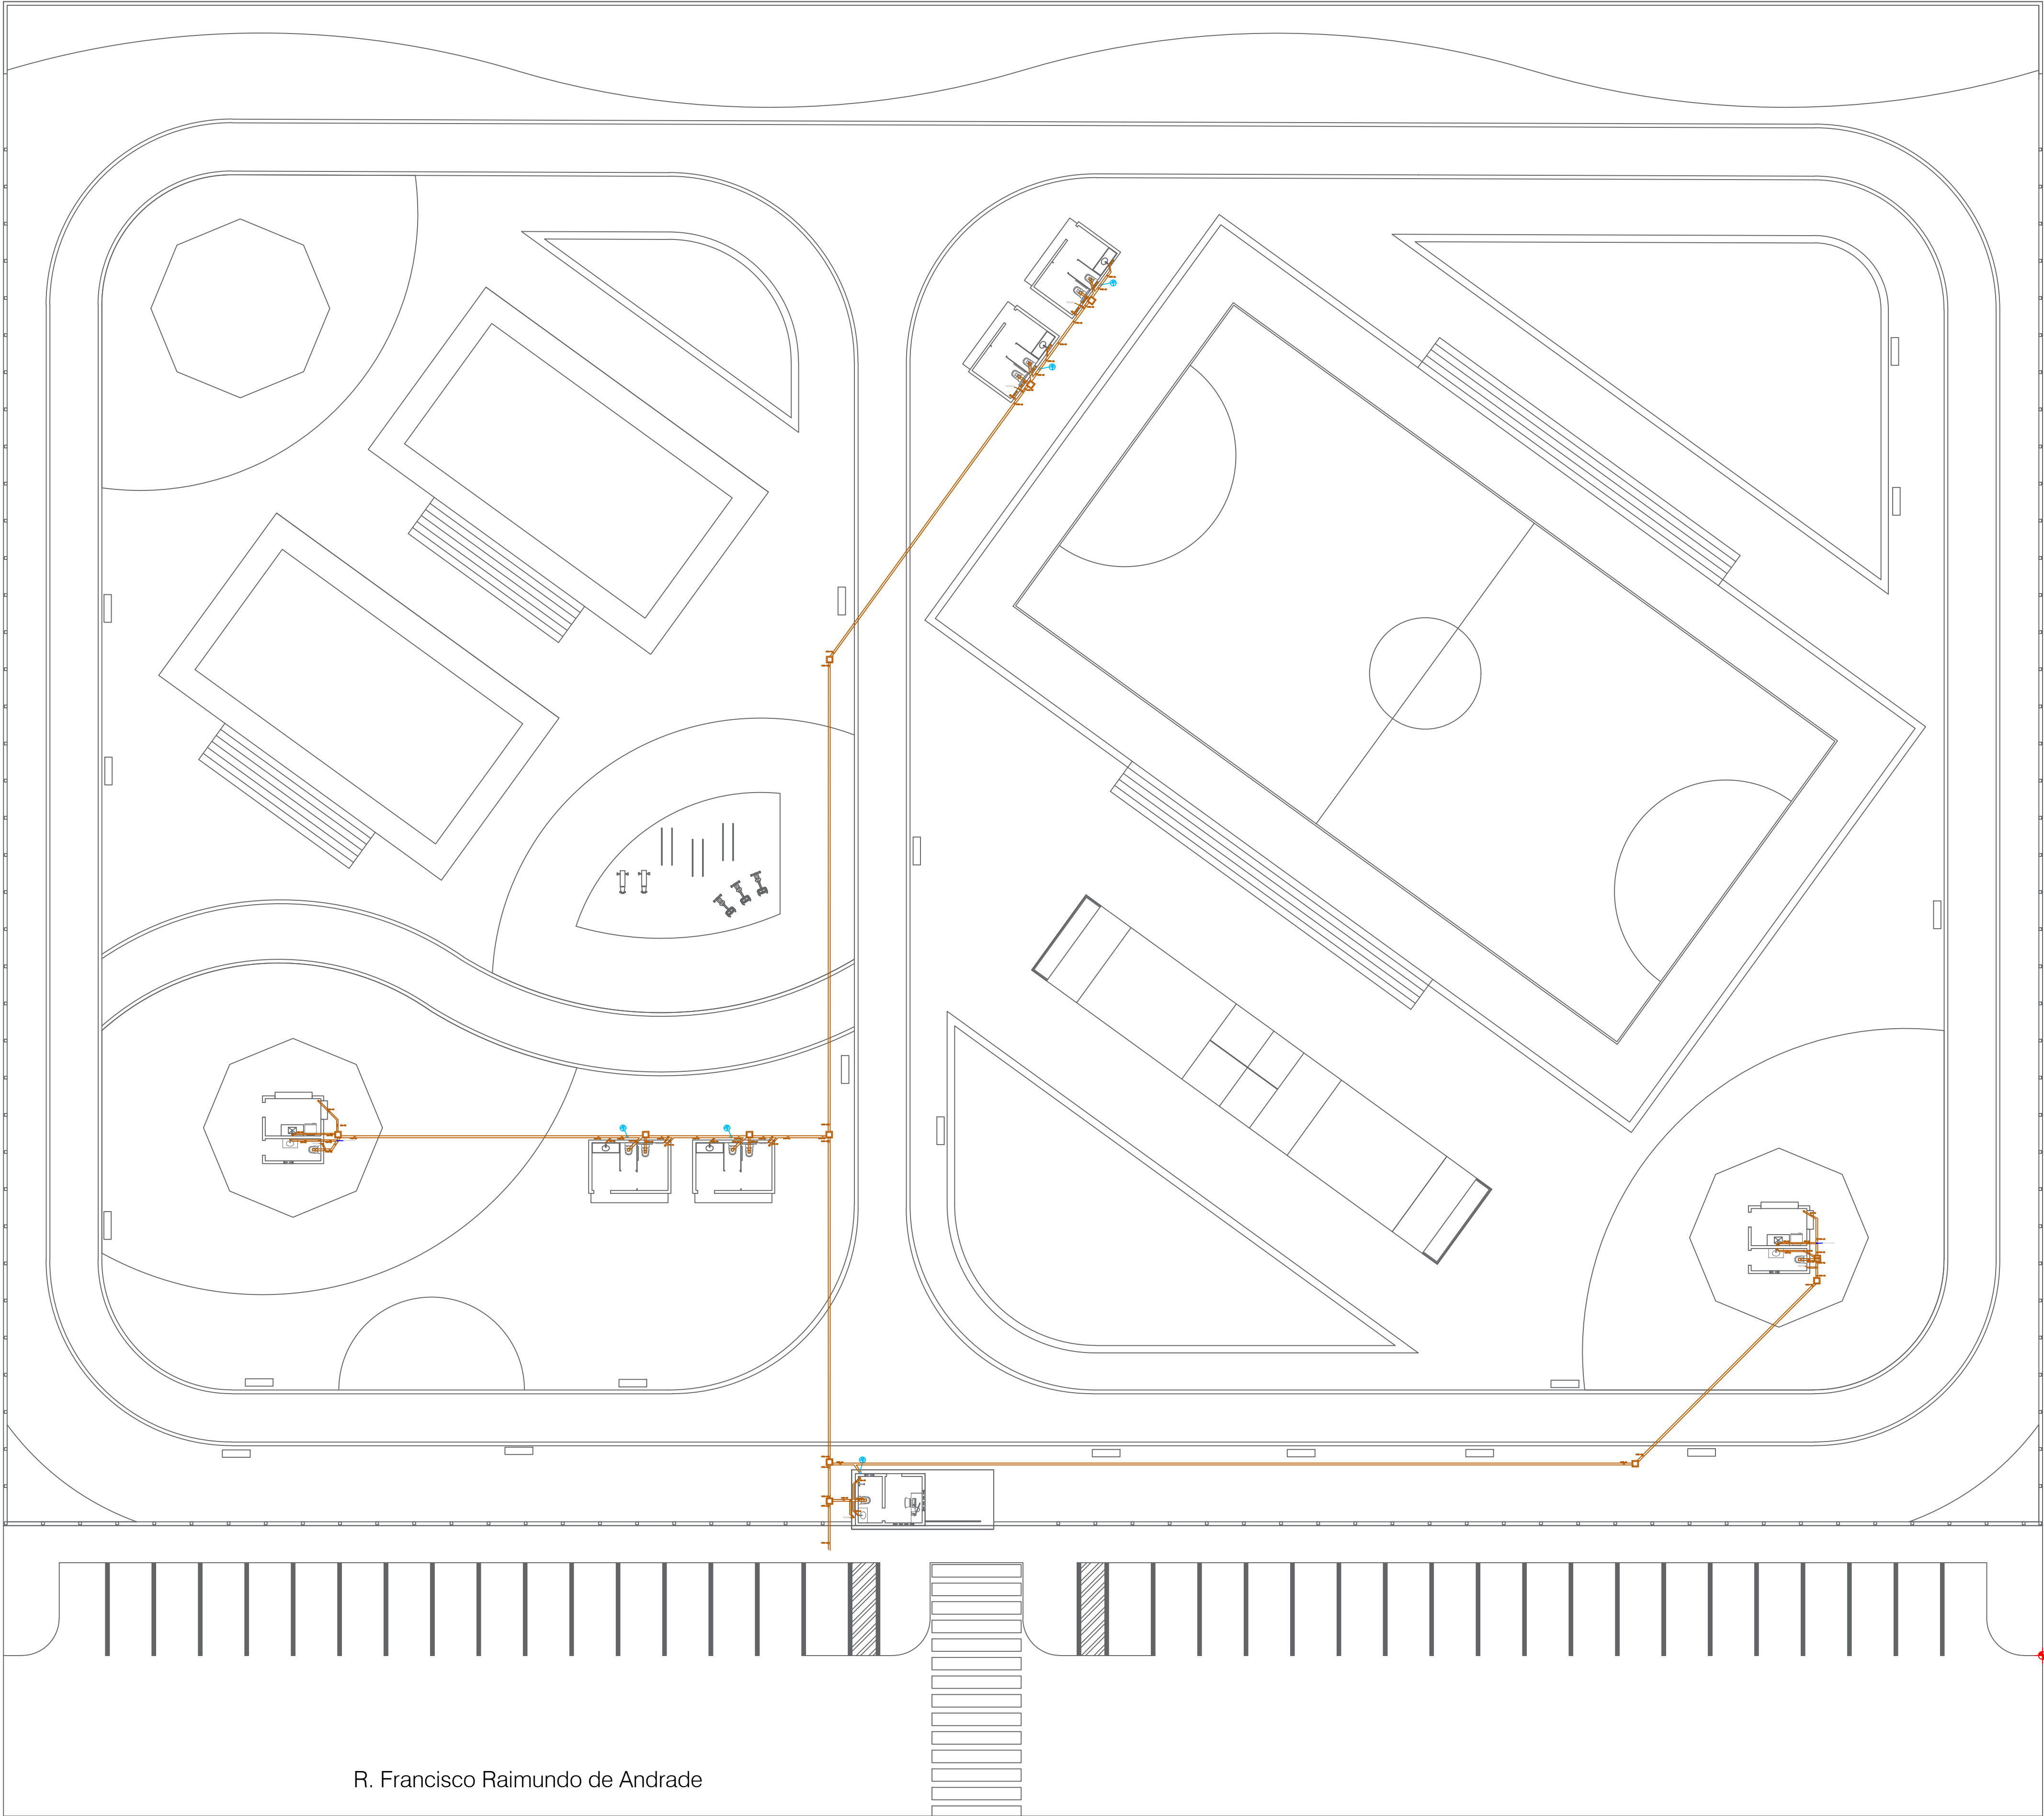

PLANTA GERAL - COBERTA
COMPLEXO ESPORTIVO

ESC: 1/200

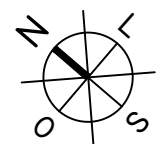

Projeto:

Projeto de Urbanismo Vila Olimpica

Desenhos:

PLANTA BAIXA COM DETALHAMENTO DOS PONTOS DE ESGOTO SANITÁRIO

- Conferir todas as medidas em obra antes da execução dos serviços.
- Não executar alterações sem autorização prévia do responsável técnico.
- Qualquer divergência entre projeto e condições de campo deverá ser comunicada ao responsável técnico para análise e aprovação.
- Todas as instalações deverão ser executadas por mão de obra qualificada, seguindo as normas técnicas vigentes e as recomendações dos fabricantes dos materiais empregados.
- Os diâmetros, declividades, cotas e posicionamentos indicados em projeto prevalecem sobre quaisquer informações complementares aqui descritas.

Esta prancha apresenta os detalhes das instalações de esgoto sanitário devendo sua execução seguir rigorosamente as dimensões, níveis, materiais e especificações indicados em projeto.

- Ramais de esgoto sanitário: DN 75 mm com declividade mínima de 1%.
- Ramais de bacias sanitárias: DN 100 mm com declividade mínima de 1%.
- Coletor principal de esgoto: DN 100 mm com declividade mínima de 1%.
- O sistema contará com caixas de inspeção nos locais indicados em projeto.
- O sistema será provido de ventilação sanitária através de tubulações de ventilação dimensionadas e posicionadas conforme projeto.
- Todas as conexões deverão ser executadas no sentido do fluxo, respeitando os diâmetros, declividades e cotas indicados em projeto.
- Antes da entrada em operação, deverá ser realizado teste de estanqueidade em toda a rede.

Projetista:

Fernando Matias Mamede

RESPONSÁVEL TÉCNICO
Fernando Matias Mamede
Engenheiro Civil
Crea: 162056275-8



Proprietário:

Prefeitura Municipal de Coremas

PROPRIETÁRIO(A)



Endereço/Obra: Rua Francisco Raimundo de Andrade, DNOCS, Coremas - PB, 58770-000

ÁREAS	m²
Área do Terreno	10.733,41
Estacionamento	519,11
Calçada	249,64
Área verde	4.281,11

Prancha:

13/14

Detalhamento Hidráulico - Banheiros 1

Detalhamento Hidráulico - Banheiros 2

Detalhamento Hidráulico - Quiosque 1

[illegible]

Detalhamento Hidráulico - Guarita

Hydraulic detail drawing of a guardhouse (Guarita) showing water supply and drainage systems. The drawing includes a floor plan with a toilet and sink. Orange lines represent the piping, with diameters and slopes indicated. A blue circle labeled 'AP 5' is connected to the main supply line. A note 'Tubulação de ventilação para o sistema' points to a vent pipe. The drawing is part of a larger set, with other sheets indicated by numbers 1, 2, 3, 100.

Projeto de Urbanismo Vila Olimpica			
Desenhos: PLANTA BAIXA COM DETALHAMENTO DOS PONTOS DE ESGOTO SANITÁRIO			
• Conferir todas as medidas em obra antes da execução dos serviços. • Não executar alterações sem autorização prévia do responsável técnico. • Qualquer divergência entre projeto e condições de campo deverá ser comunicada ao responsável técnico para análise e aprovação. • Todas as instalações deverão ser executadas por mão de obra qualificada, seguindo as normas técnicas vigentes e as recomendações dos fabricantes dos materiais empregados. • O dimensionamento e posicionamentos indicados em projeto prevalecem sobre quaisquer informações complementares aqui descritas. Esta prancha apresenta os detalhamentos das instalações de esgoto sanitário devendo sua execução seguir rigorosamente as dimensões, níveis, materiais e especificações indicados em projeto. • Ramais de esgoto sanitário: DN 75 mm com declividade mínima de 1%. • Ramais de bacias sanitárias: DN 100 mm com declividade mínima de 1%. • Coletor principal de esgoto: DN 100 mm com declividade mínima de 1%. • O sistema contará com caixas de inspeção nos locais indicados em projeto. • O sistema será provido de ventilação sanitária através de tubulações de ventilação dimensionadas e posicionadas conforme projeto. • Todas as conexões deverão ser executadas no sentido do fluxo, respeitando os diâmetros, declividades e cotas indicados em projeto. • Antes da entrada em operação, deverá ser realizado teste de estanqueidade em toda a rede.			
Projetista: Fernando Matias Mamede	RESPONSÁVEL TÉCNICO Fernando Matias Mamede Engenheiro Civil Crea: 162056275-8		
Proprietário: Prefeitura Municipal de Coremas	PROPRIETÁRIO(A)		
Endereço/Obra: Rua Francisco Raimundo de Andrade, DNOCS, Coremas - PB, 58770-000			Prancha: 14/14
ÁREAS Área do Terreno Estacionamento Calçada Área verde	m² 10.733,41 519,11 249,64 4.281,11		