





PLANTA BAIXA

MURO DE ARRIMO
ESCALA 1/45

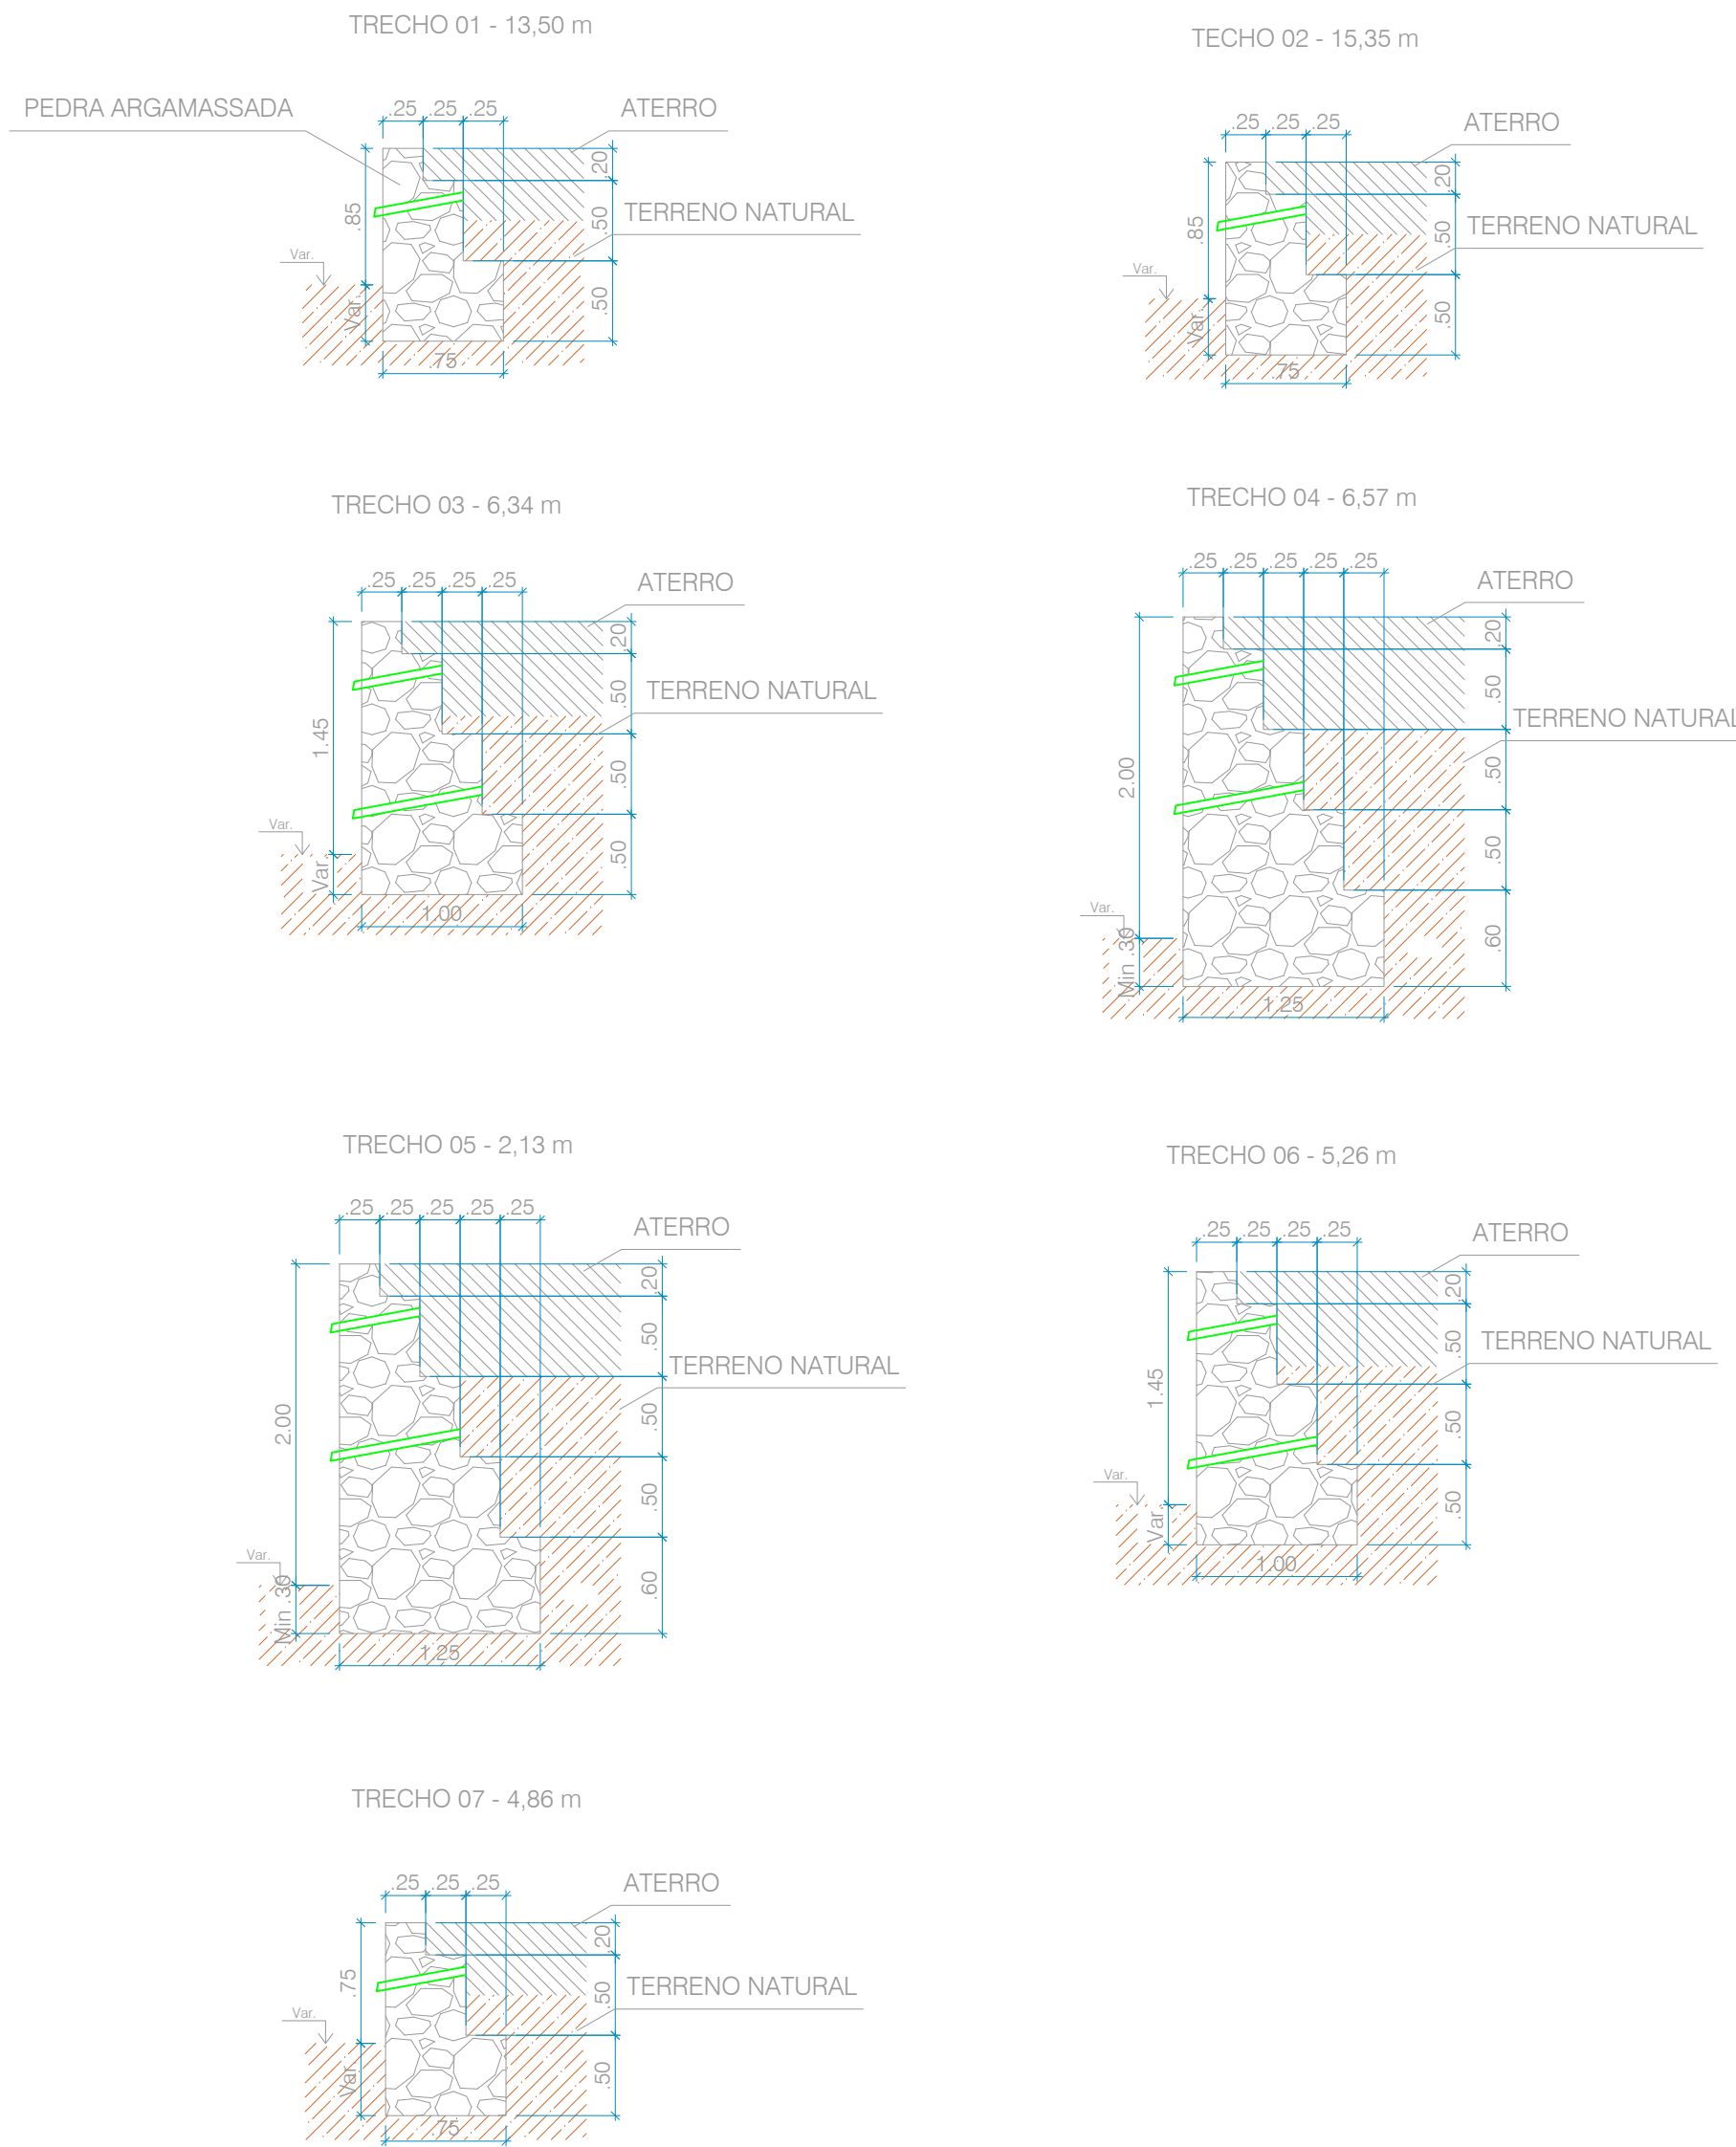


SEÇÃO TIPO

TRECHO 01, 02, 03, 04, 05, 06 e 07
ESCALA 1/45

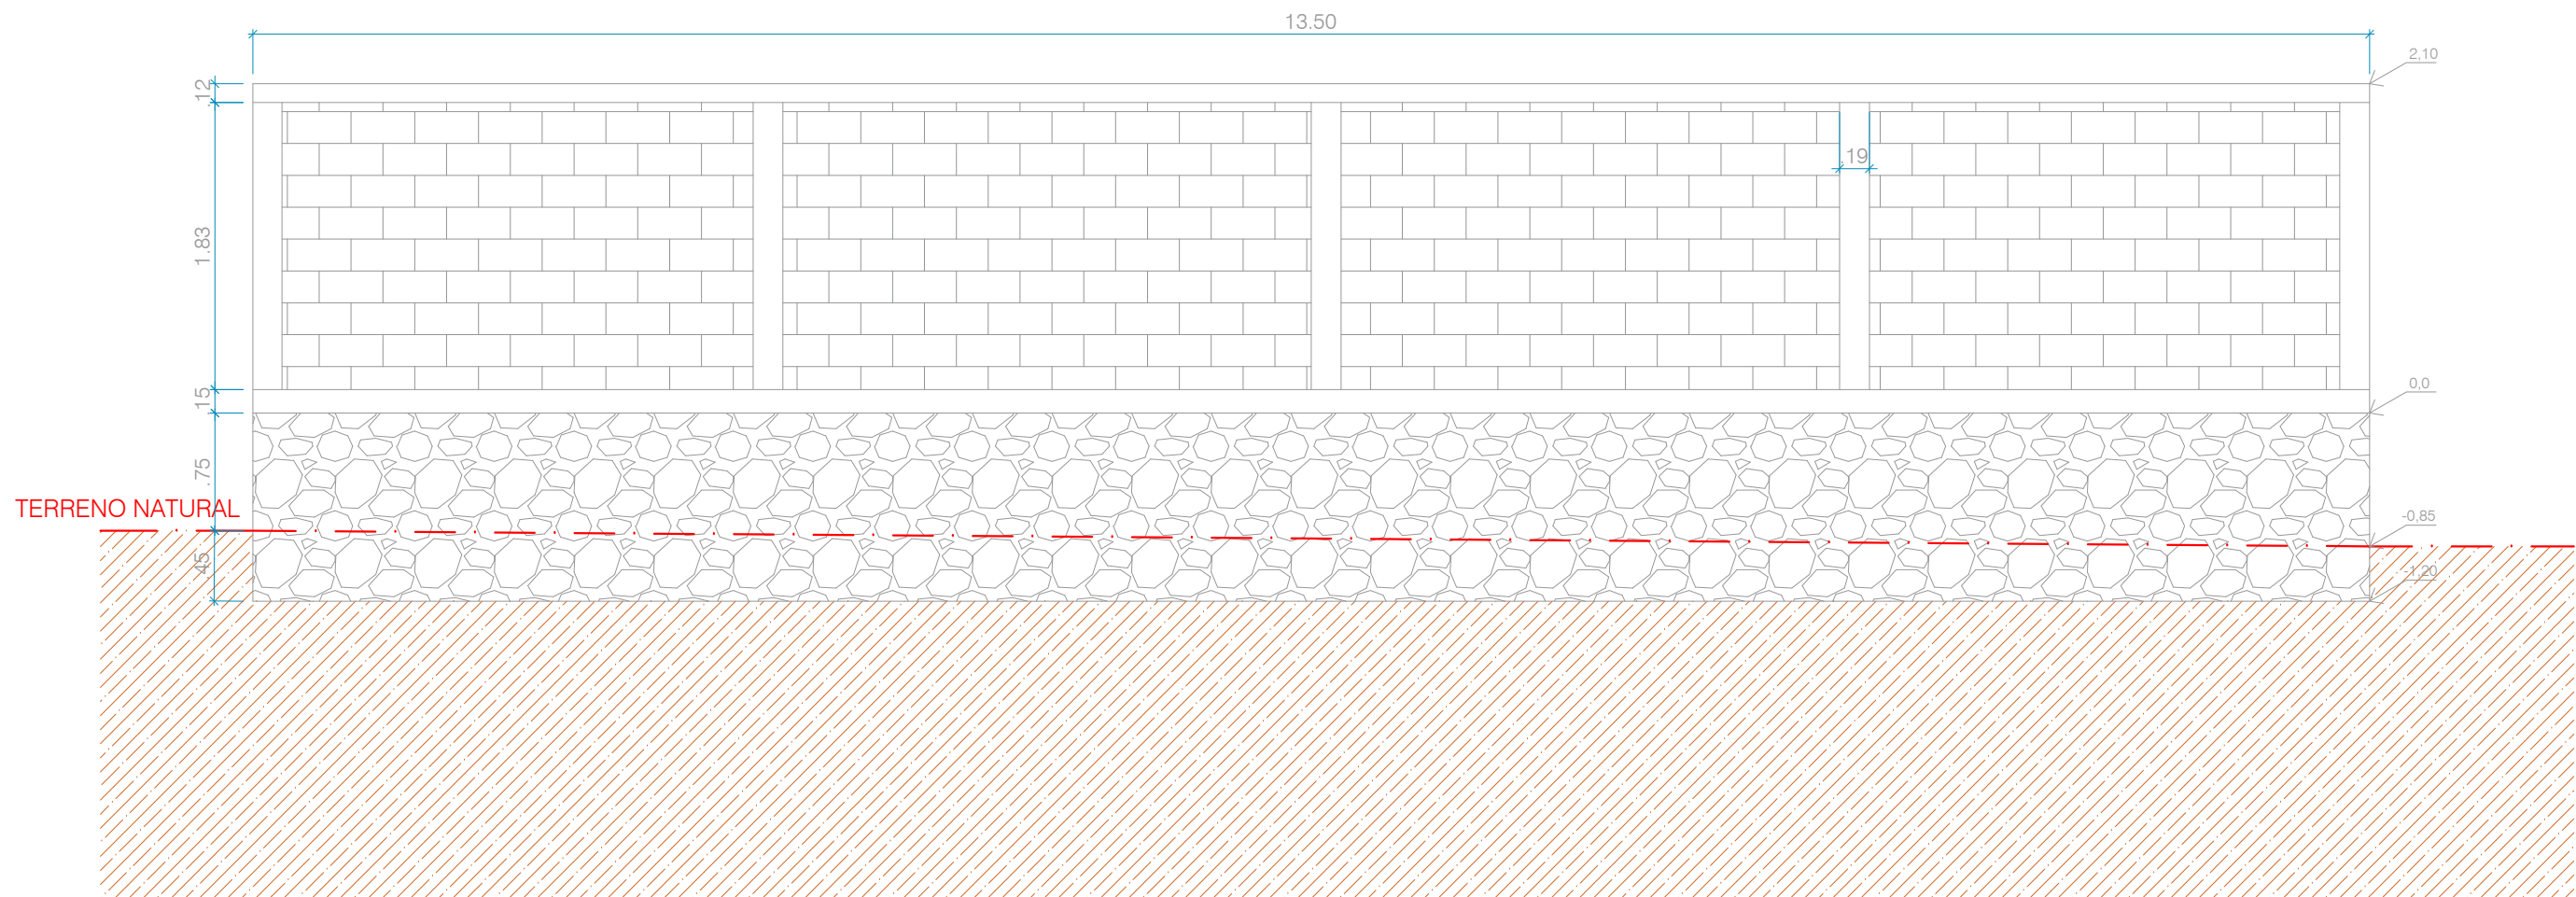


FÔRMA

TRECHO 01
ESCALA 1/45

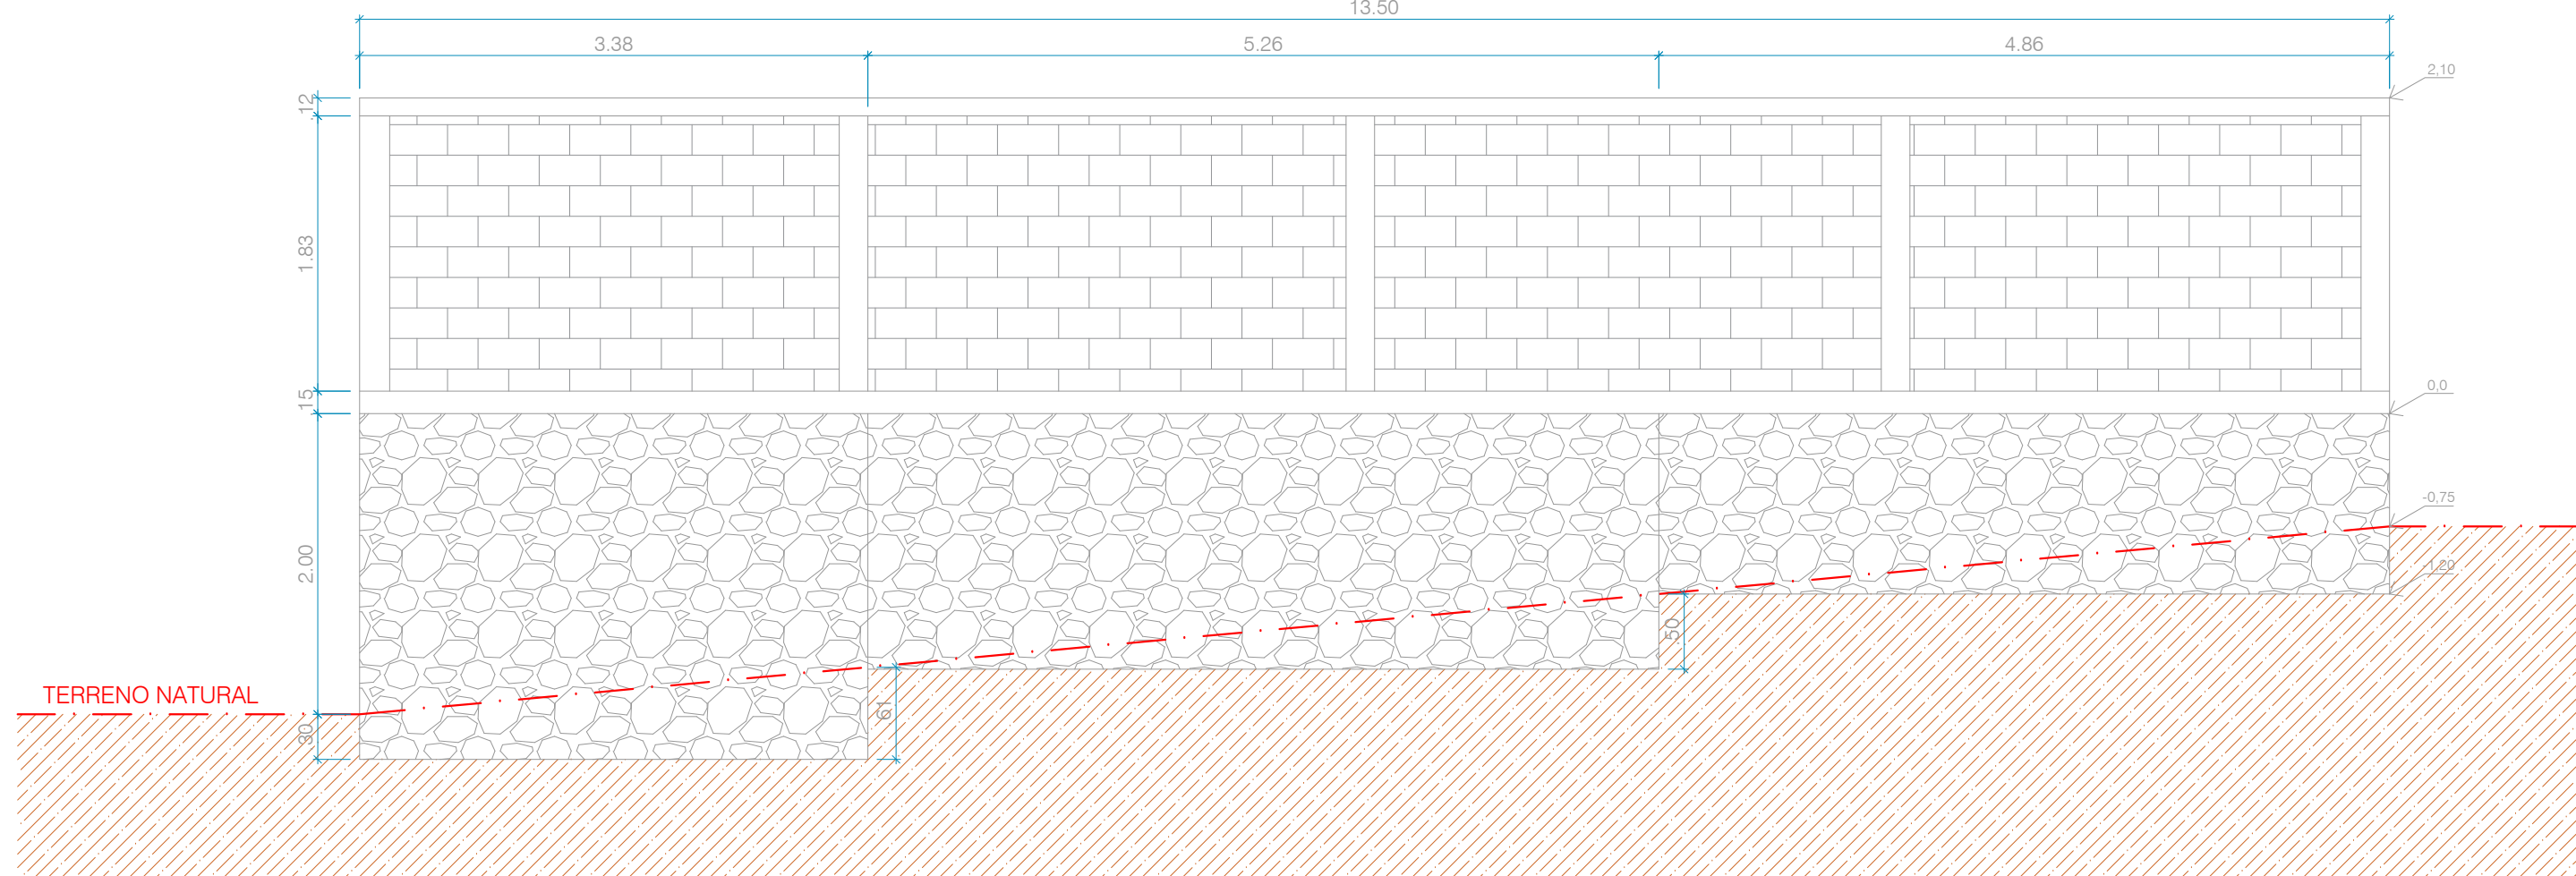

FÔRMA

TRECHO 05, 06 e 07
ESCALA 1/45

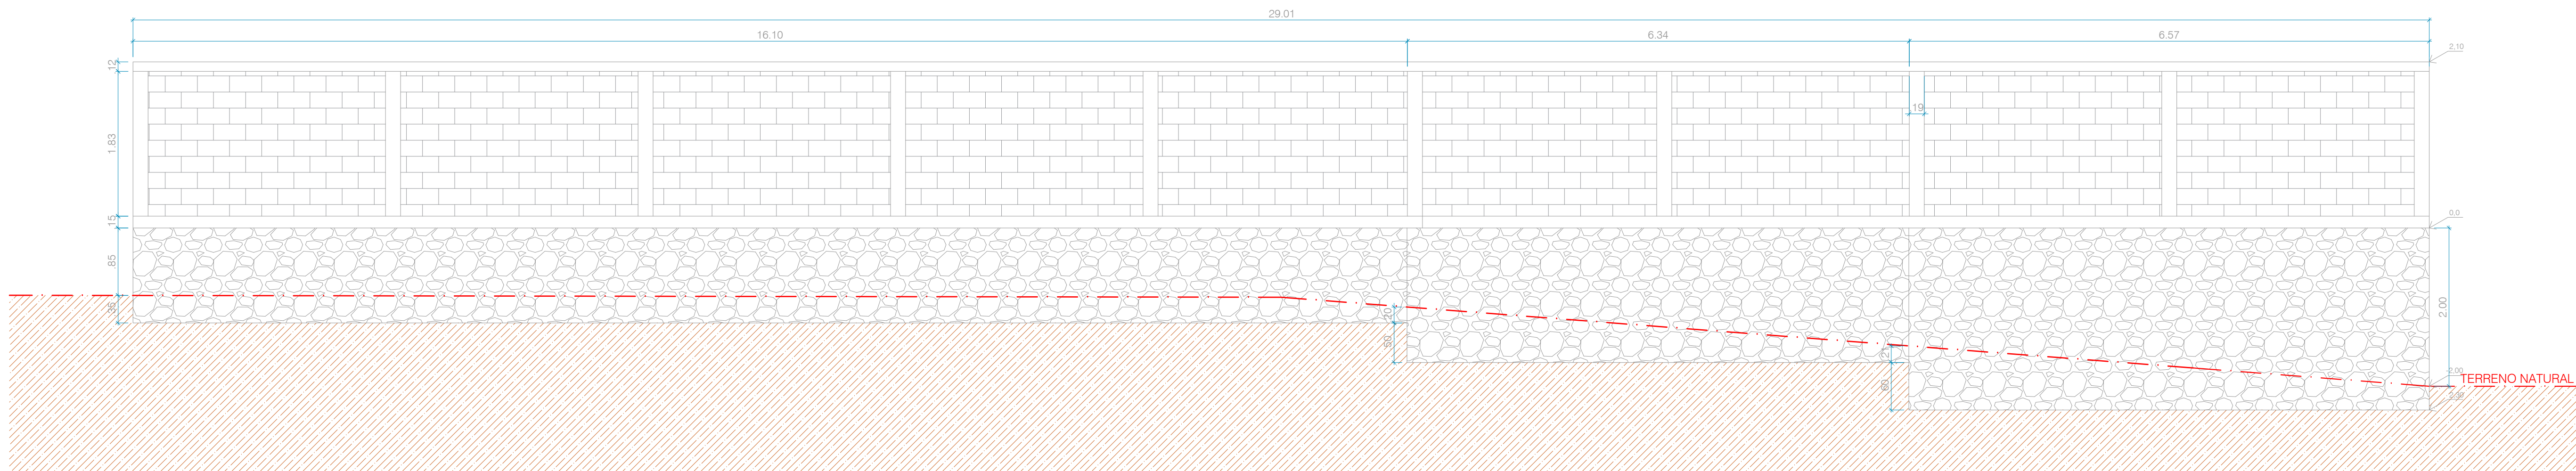

FÔRMA

TRECHO 02, 03 e 04
ESCALA 1/45

NORMAS INCIDENTES SOBRE O PROJETO:

NBR 6122 – PROJETO E EXECUÇÃO DE FUNDAÇÕES, 20/09/2010.
NBR 6118 – PROJETO DE ESTRUTURAS DE CONCRETO – PROCEDIMENTO, 07/08/2014.
NBR 6120 – CARGAS PARA CÁLCULO DE ESTRUTURAS DE EDIFICAÇÕES, 30/11/1980.
ERRATA EM 30/04/2000.
NBR 8681 – AÇÕES DE SEGURANÇA NAS ESTRUTURAS, PROCEDIMENTO, 31/03/2004.

EPE

PROJETO:
MURO DE ARRIMO DA ESCOLA LOGRADOURO
LOCAL:
ZONA URBANA, MUNICÍPIO DE COREMAS - PB
PROPRIETÁRIO:
PREFEITURA MUNICIPAL DE COREMAS - PB

FOLHA
01
06

ESCALA:
Indicada

DESENHOS:
Projeto Do Muro de Arrimo -
Planta Baixa e de Forma

RESPONSÁVEL TÉCNICO:
Kleber Sá de Oliveira
Crea: 160268278-0

ANOTAÇÕES:

ARQUIVO:
PROJETO_MURO DE
ARRIMO.dwg

DESENHO:
Diego Romualdo de Medeiros

DATA:
AGO - 2020