




CORTE AA
ESCALA 1:50

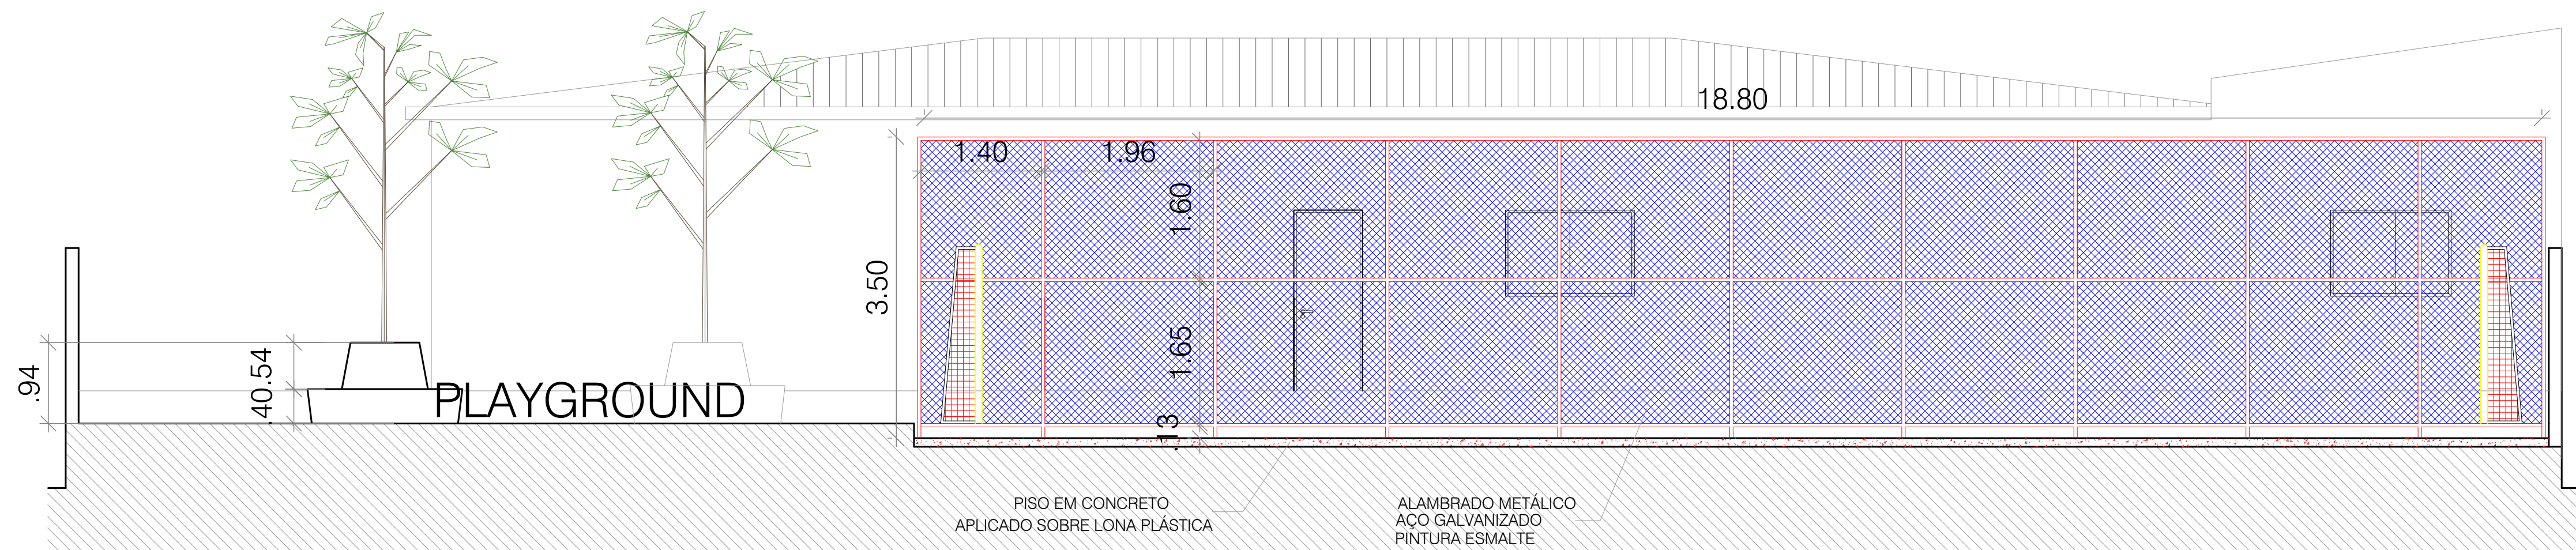

CORTE DD
ESCALA 1:50

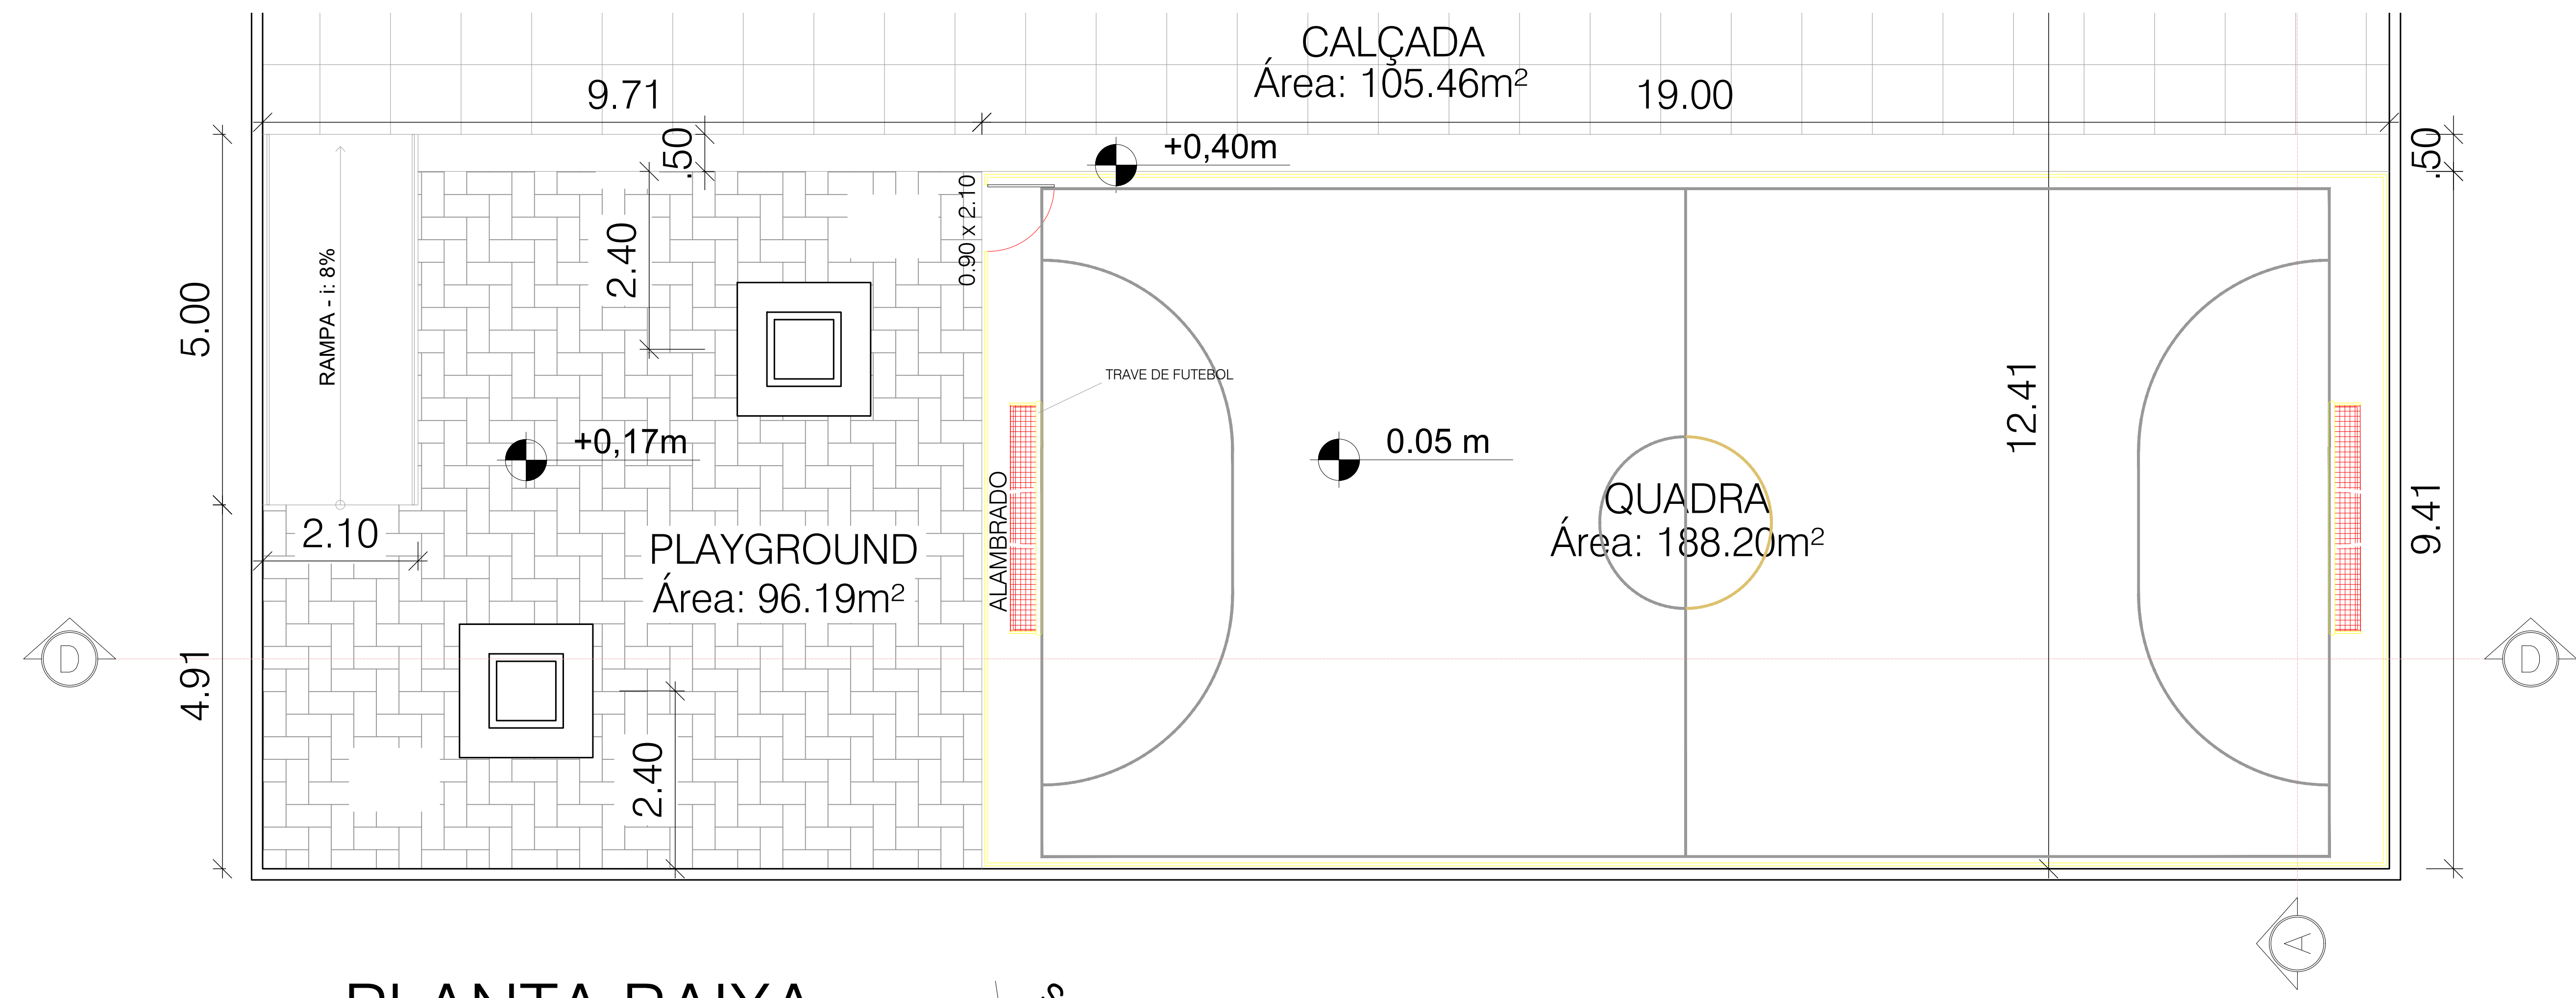

PLANTA BAIXA
ESCALA 1:50

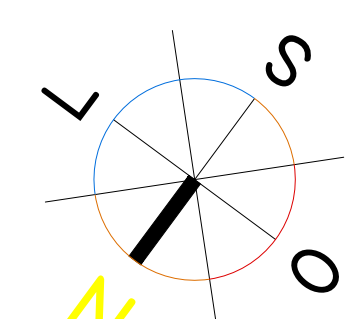

EPE		PROJETO: QUADRA DA ESCOLA LOGRADOURO	
		LOCAL: ZONA URBANA, MUNICÍPIO DE COREMAS - PB	
FOLHA: 06/06		PROPRIETÁRIO: PREFEITURA MUNICIPAL DE COREMAS - PB	
ESCALA: Indicada		RESPONSÁVEL TÉCNICO: Kleber Sá de Oliveira Crea: 160268278-0	
DESENHO: Diego Romualdo de Medeiros		ANOTAÇÕES:	
ARQUIVO:		DATA: AGO - 2020	