




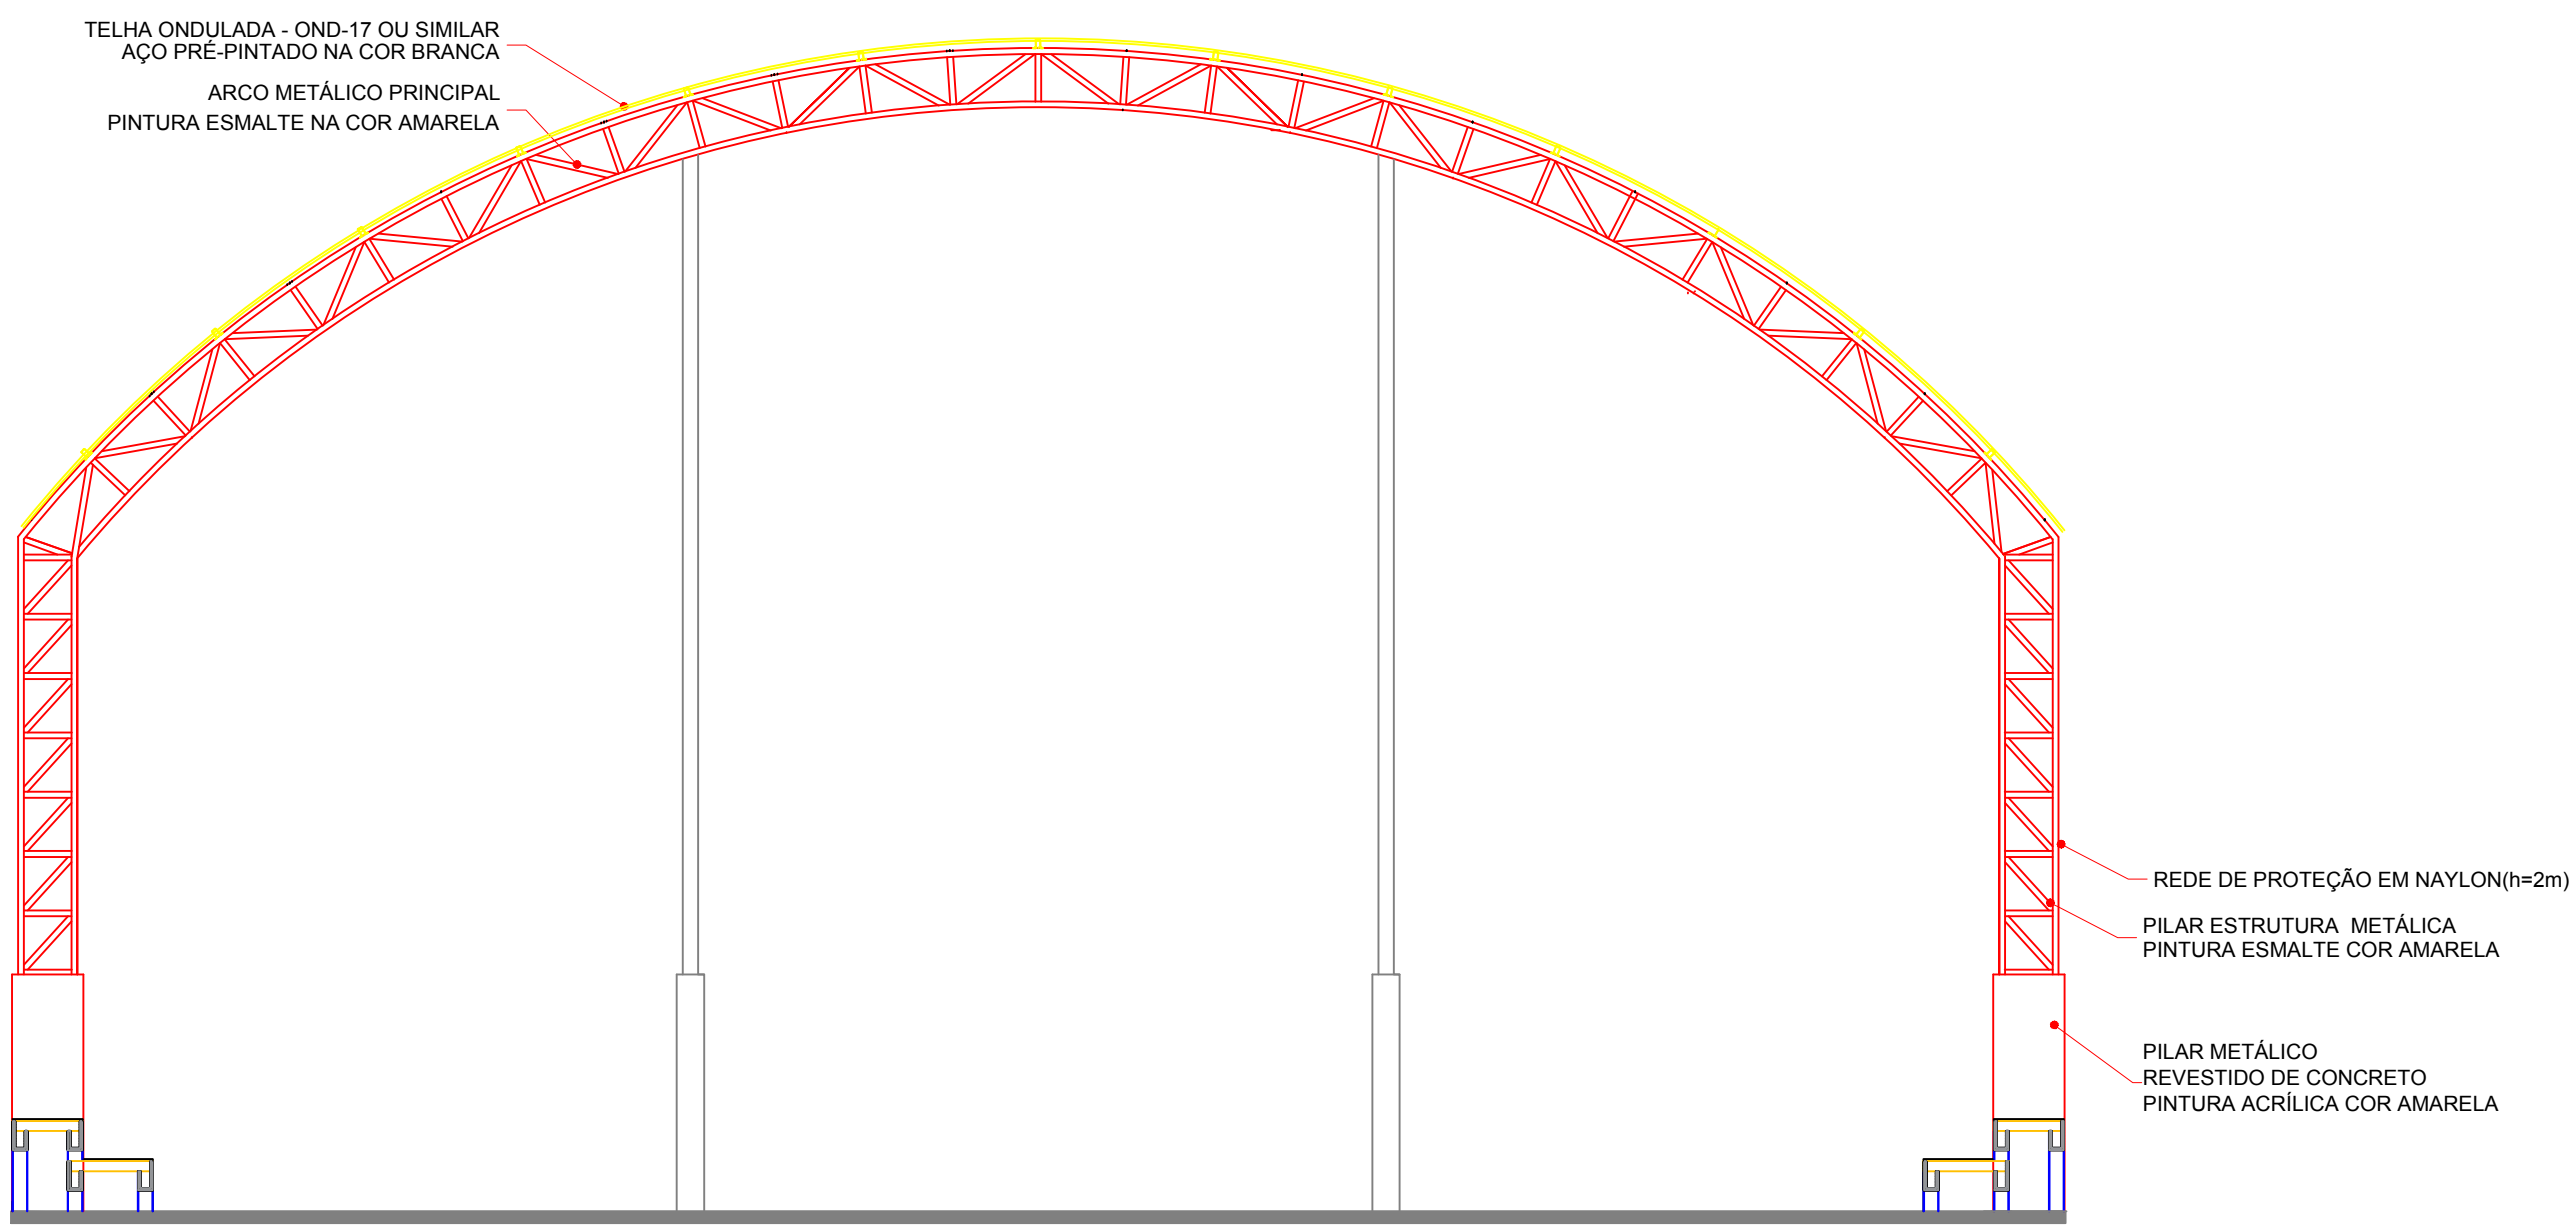

CORTE AA - QUADRA
ESCALA 1/50

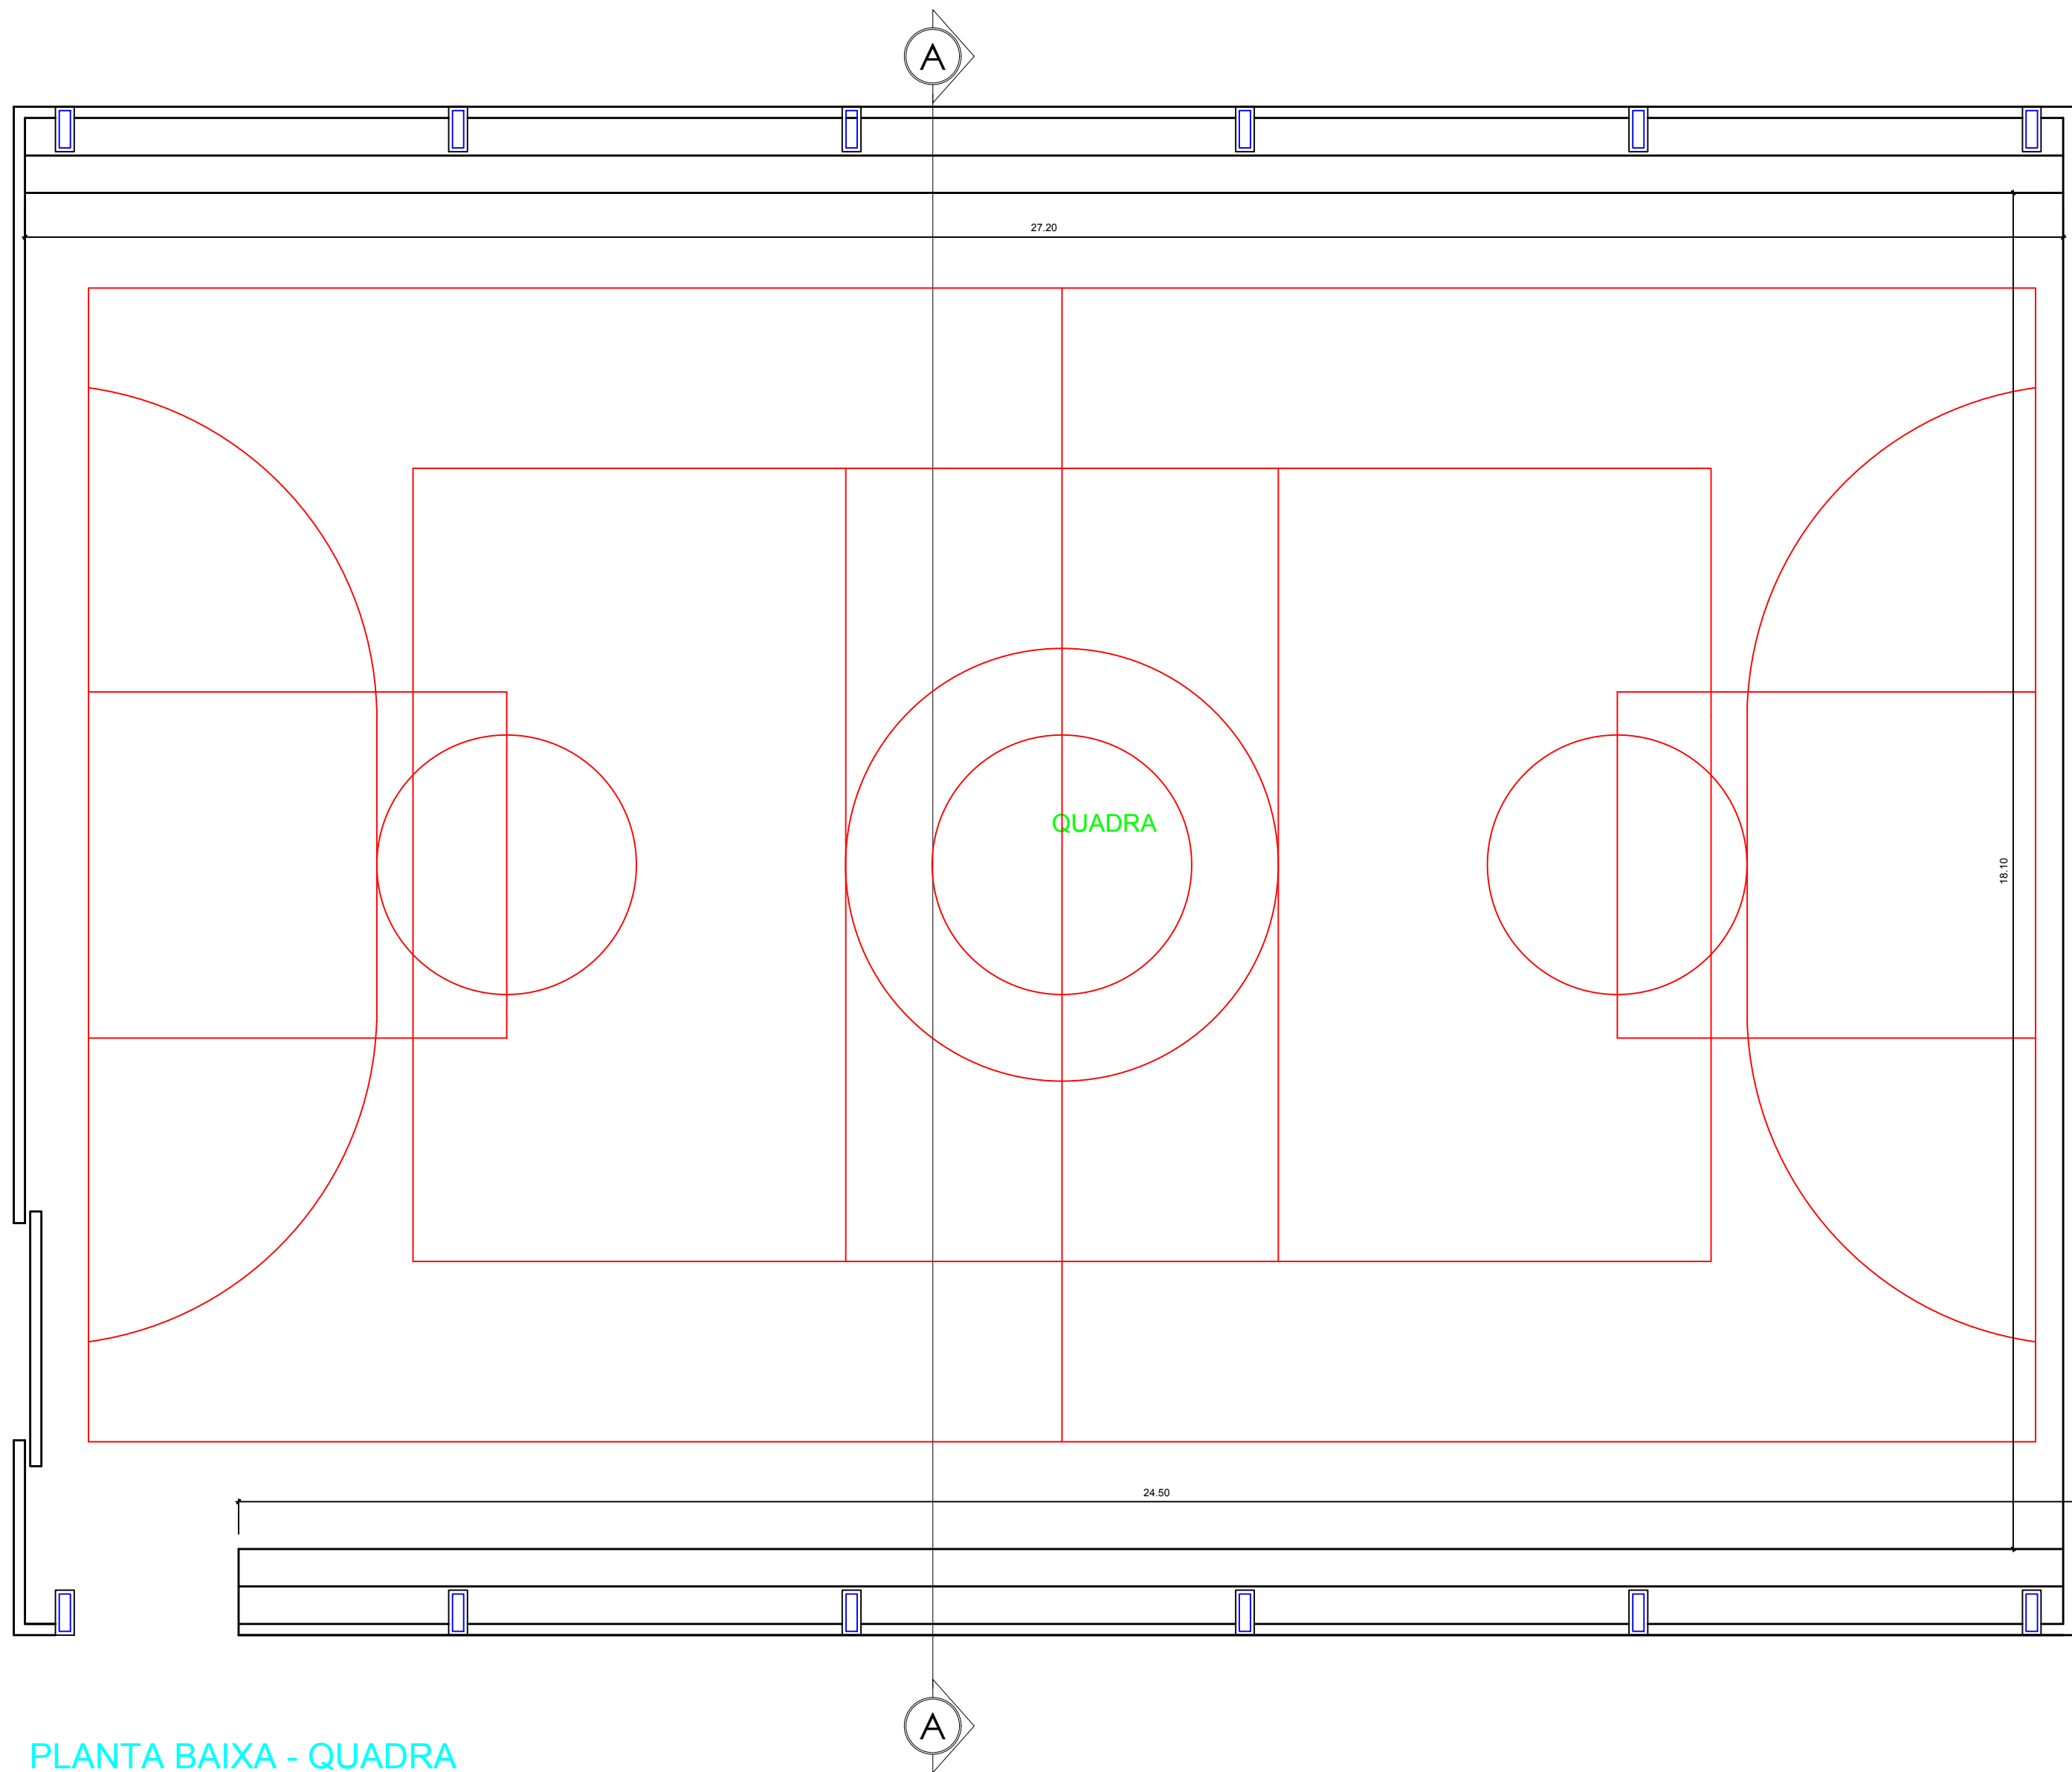

PLANTA BAIXA - QUADRA
ESCALA 1/50

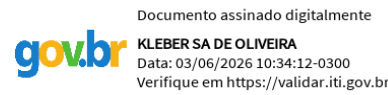

EPE		PROJETO: REFORMA DA ESCOLA FLÓRIDO NITÃO DINIZ	
		LOCAL: ZONA URBANA, MUNICÍPIO DE COREMAS - PB	
FOLHA: 01/01		PROPRIETÁRIO: PREFEITURA MUNICIPAL DE COREMAS - PB	
ARQUIVO: ESCOLA_DINIZS_COREMAS.DWG		DESENHO: Diego Romualdo de Medeiros	RESPONSÁVEL TÉCNICO: Kleber Sá de Oliveira CREA: 160268278-0
		ANOTAÇÕES:	
		DATA: DEZ - 2019	