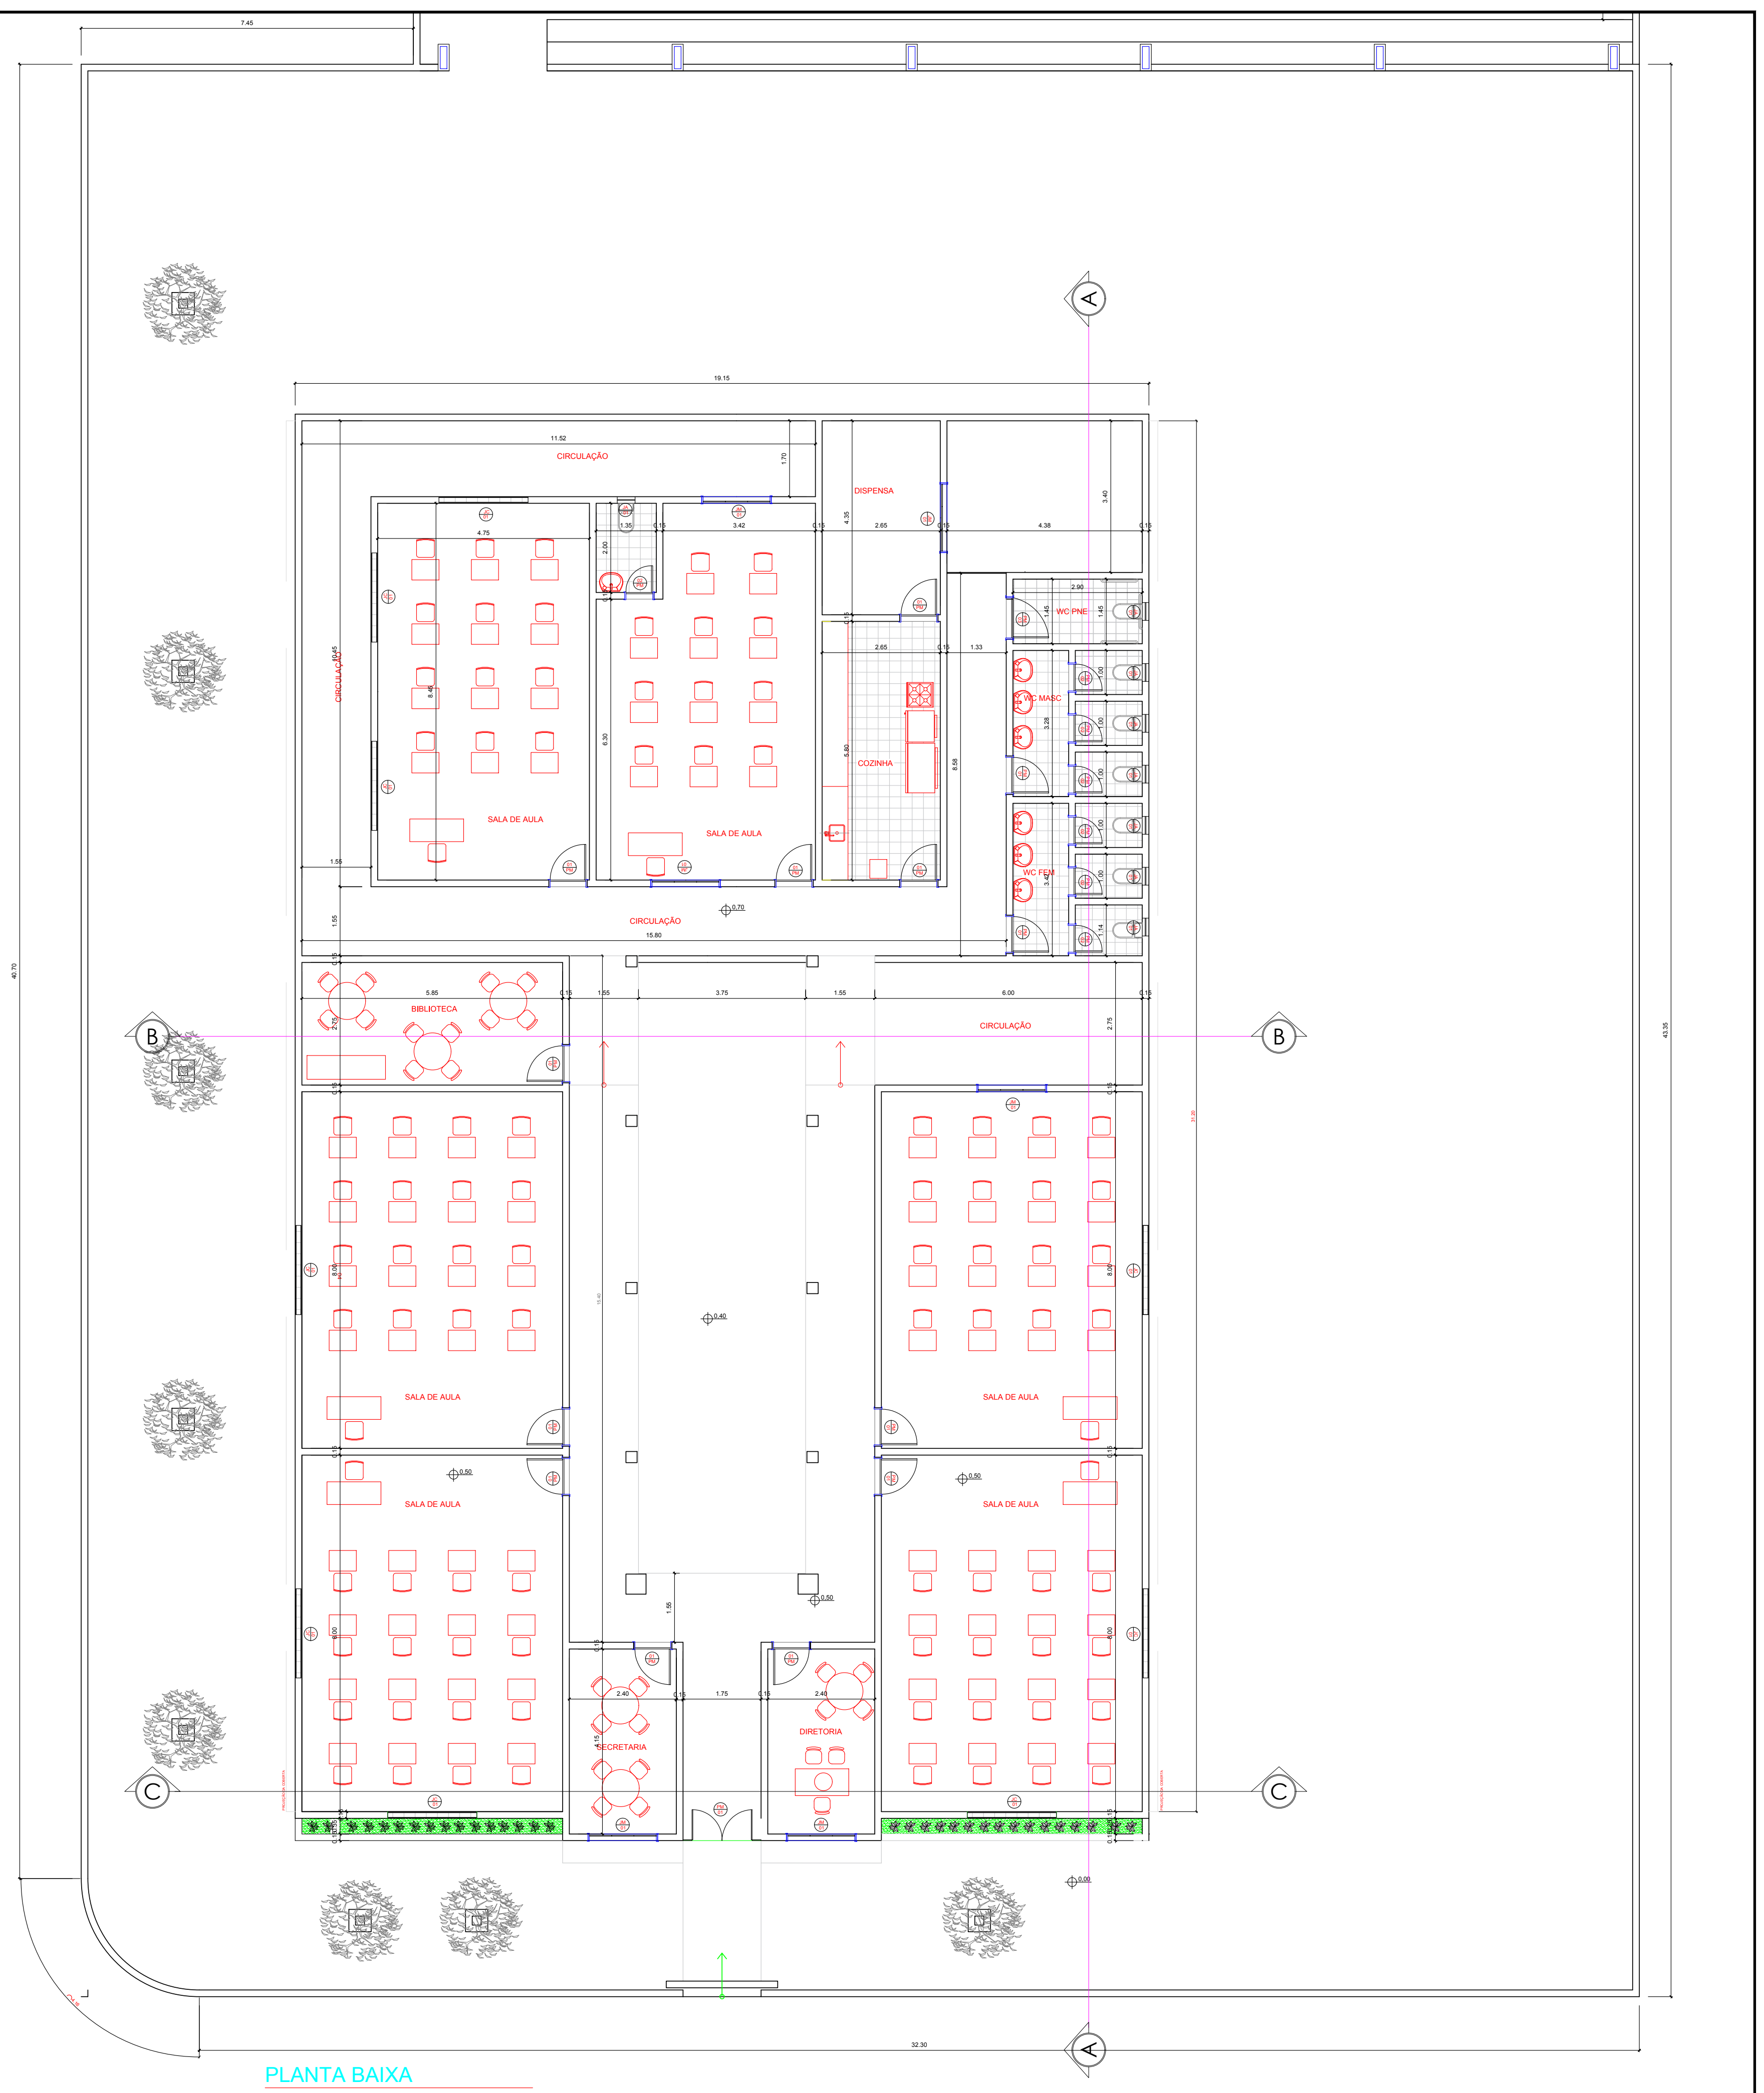
CIRCULAÇÃO
DISPENSA
SALA DE AULA
COZINHA
WC PNE
WC MASC
WC FEM
BIBLIOTECA
SECRETARIA
DIRETORIA
7.45
19.15
11.52
15.80
40.70
43.35
32.30
A
B
C

PLANTA BAIXA

ESCALA 1:50

QUADRO RESUMO DE ESQUADRIAS

ESQUADRIA	DIMENSÃO (LxH)cm	QUANT.	LOCAL	TIPO
PM 01	86,0 x 210,0	13	WC F/M, SALAS	PORTA DE MADEIRA
PM 02	60,0 x 210,0	7	WCS	PORTA DE MADEIRA
PM 03	90,0 x 210,0	1	WC PNE	PORTA DE MADEIRA
JA 01	40,0 x 40,0	8	WC FEM./MASC.	JANELA DE ALUMÍNIO
JM 01	110,0 x 40,0	6	SALAS/COZ./DISP.	JANELA DE MADEIRA
JC 01	150,0 x 100	1	SALAS	COBOGÓ

EPE

PROJETO:
REFORMA DA ESCOLA FLÓRIDO NITÃO DINIZ
LOCAL:
ZUNA URBANA, MUNCÍPIO DE COREMAS - PB
PROPRIETÁRIO:
PREFEITURA MUNICIPAL DE COREMAS - PB
RESPONSÁVEL TÉCNICO:
Kleber Sá de Oliveira
CREA: 160268278-0
ANOTAÇÕES:
DATA:
DEZ - 2019
FOLHA
01/02
ESCALA:
1:50
DESENHOS:
Planta Baixa
ARQUIVO:
ESCOLA_DNOCS_COREMAS.DWG
DESENHO:
Diego Romualdo de Medeiros

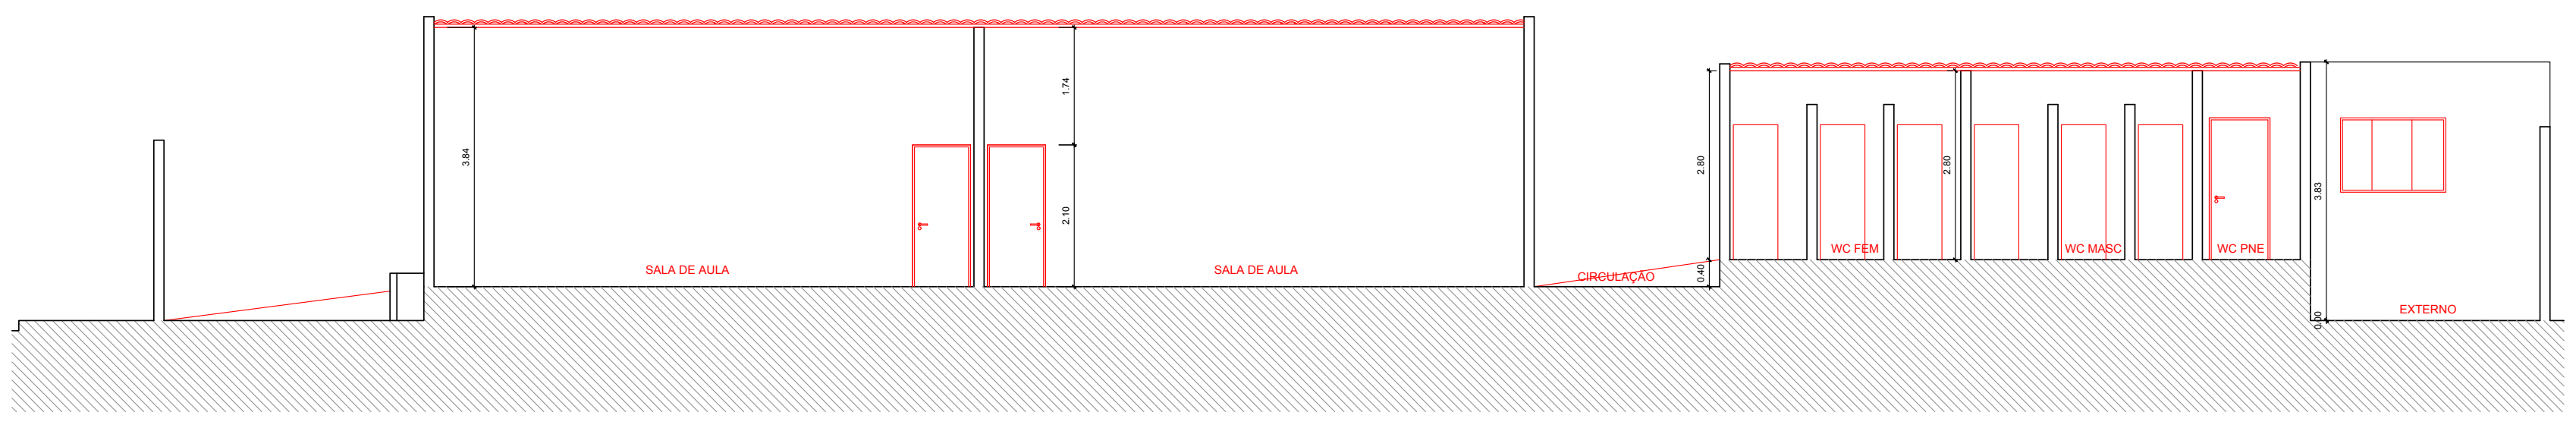
SALA DE AULA
SALA DE AULA
CIRCULAÇÃO
WC FEM
WC MASC
WC PNE
EXTERNO
3.84
1.74
2.10
2.80
3.83

CORTE AA

ESCALA 1/45

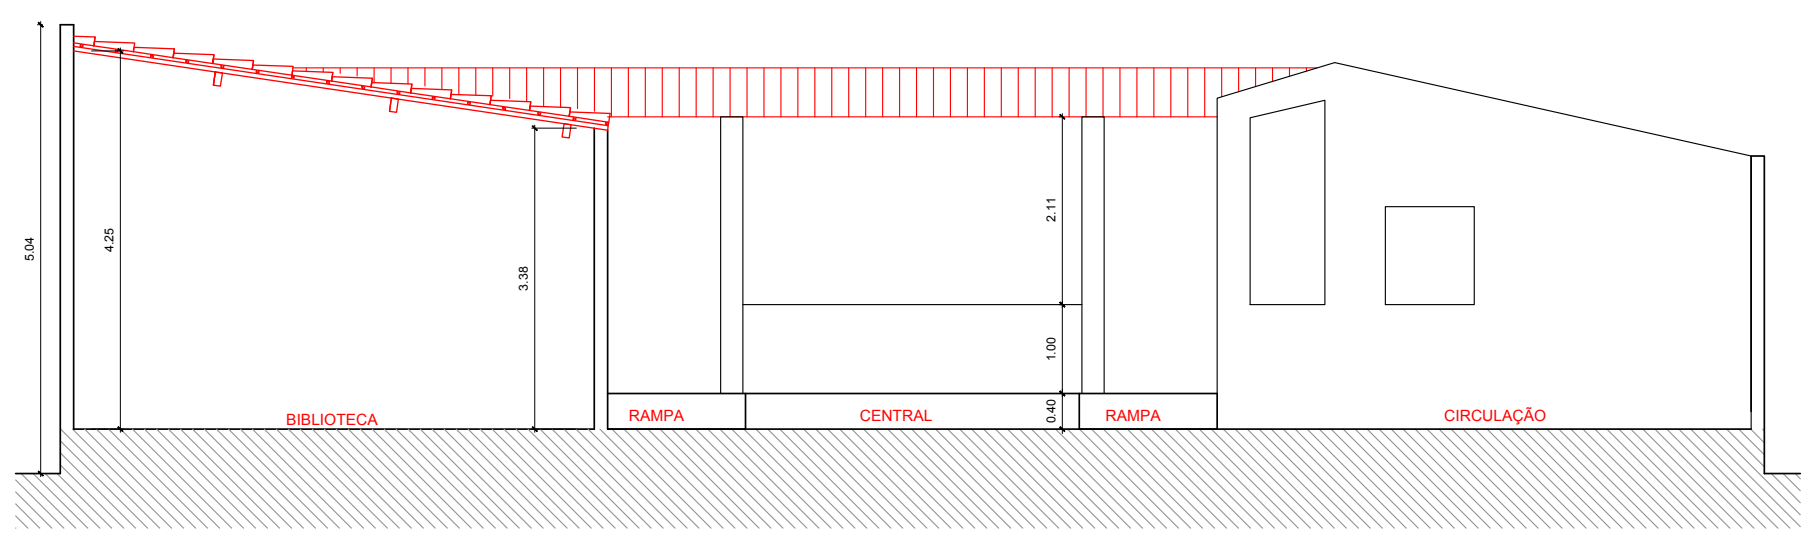
BIBLIOTECA
RAMPA
CENTRAL
RAMPA
CIRCULAÇÃO
5.04
4.25
3.38
2.11
1.00
0.40

CORTE BB

ESCALA 1/45

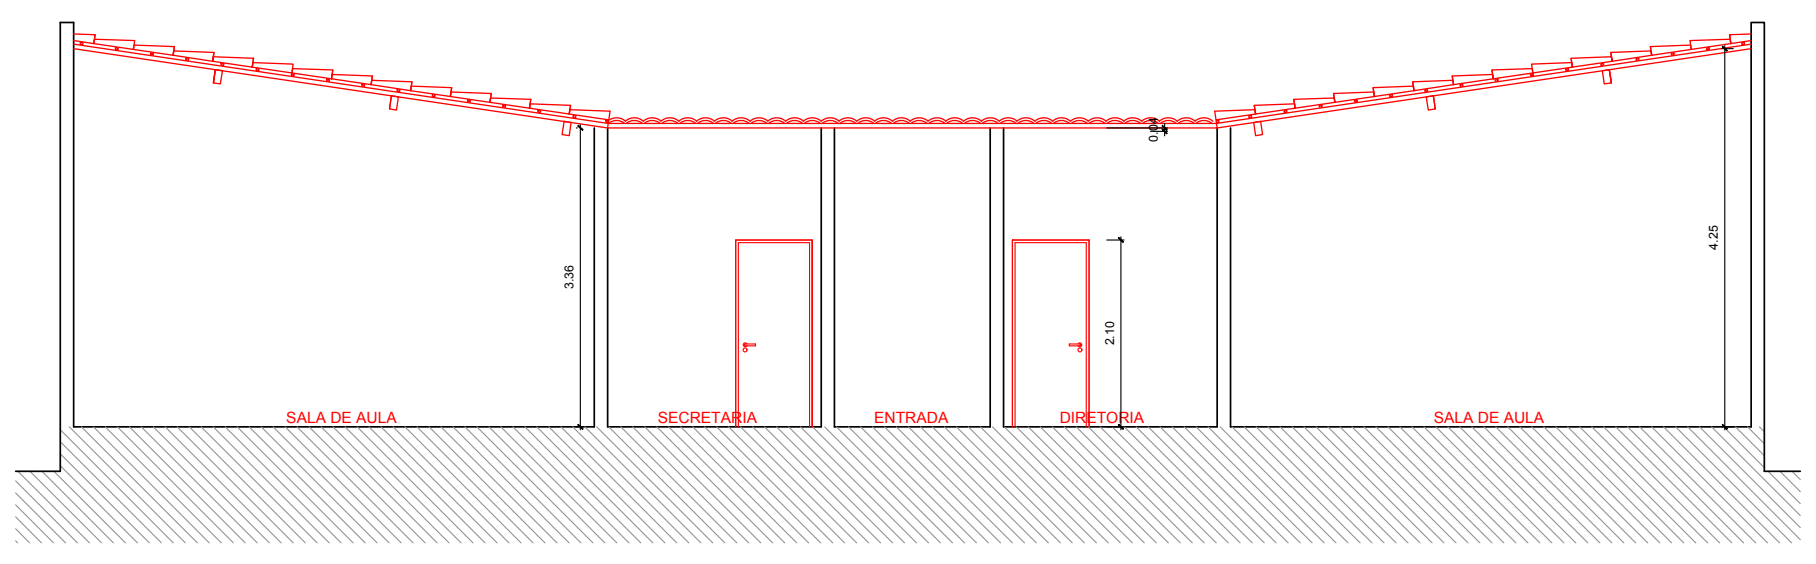
SALA DE AULA
SECRETARIA
ENTRADA
DIRETORIA
SALA DE AULA
3.36
2.10
4.25

CORTE CC

ESCALA 1/45

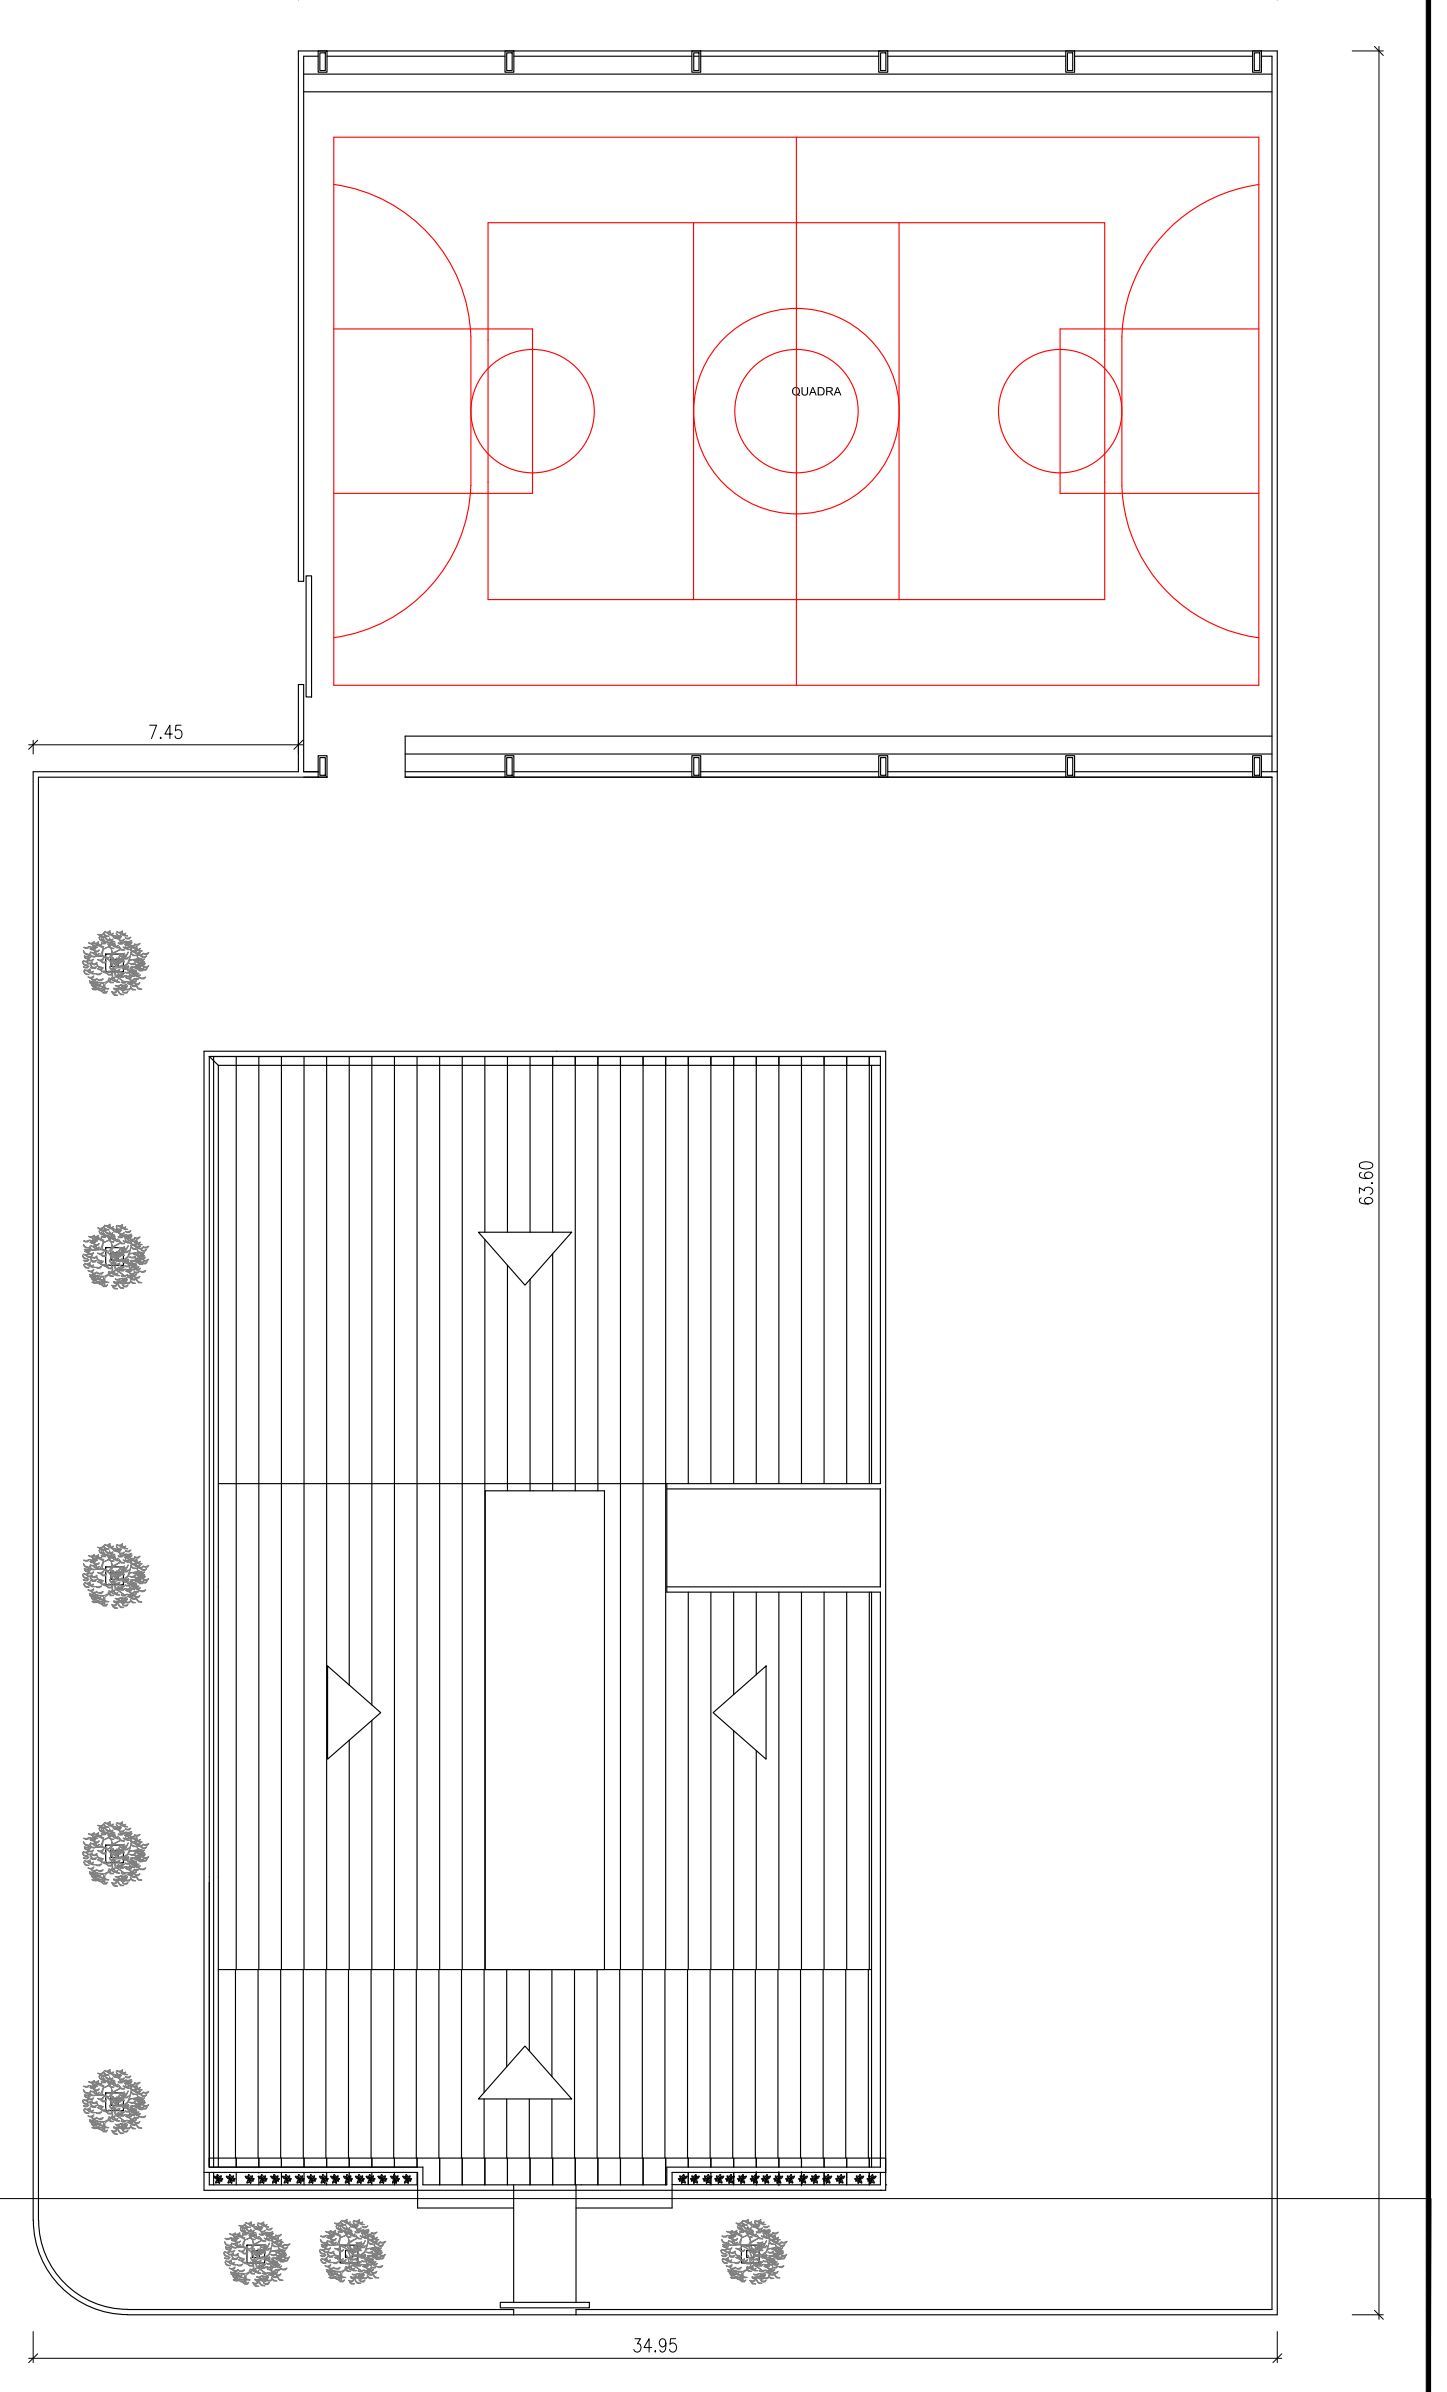
QUADRA
7.45
63.60
34.95

PLANTA DE COBERTA E LOCAÇÃO

ESCALA 1:125

EPE

PROJETO:
REFORMA DA ESCOLA FLÓRIDO NITÃO DINIZ
LOCAL:
ZUNA URBANA, MUNCÍPIO DE COREMAS - PB
PROPRIETÁRIO:
PREFEITURA MUNICIPAL DE COREMAS - PB
RESPONSÁVEL TÉCNICO:
Kleber Sá de Oliveira
CREA: 160268278-0
ANOTAÇÕES:
DATA:
DEZ - 2019
FOLHA
02/02
ESCALA:
1:50
1:125
DESENHOS:
Cortes
Locação e Coberta
ARQUIVO:
ESCOLA_DNOCS_COREMAS.DWG
DESENHO:
Diego Romualdo de Medeiros