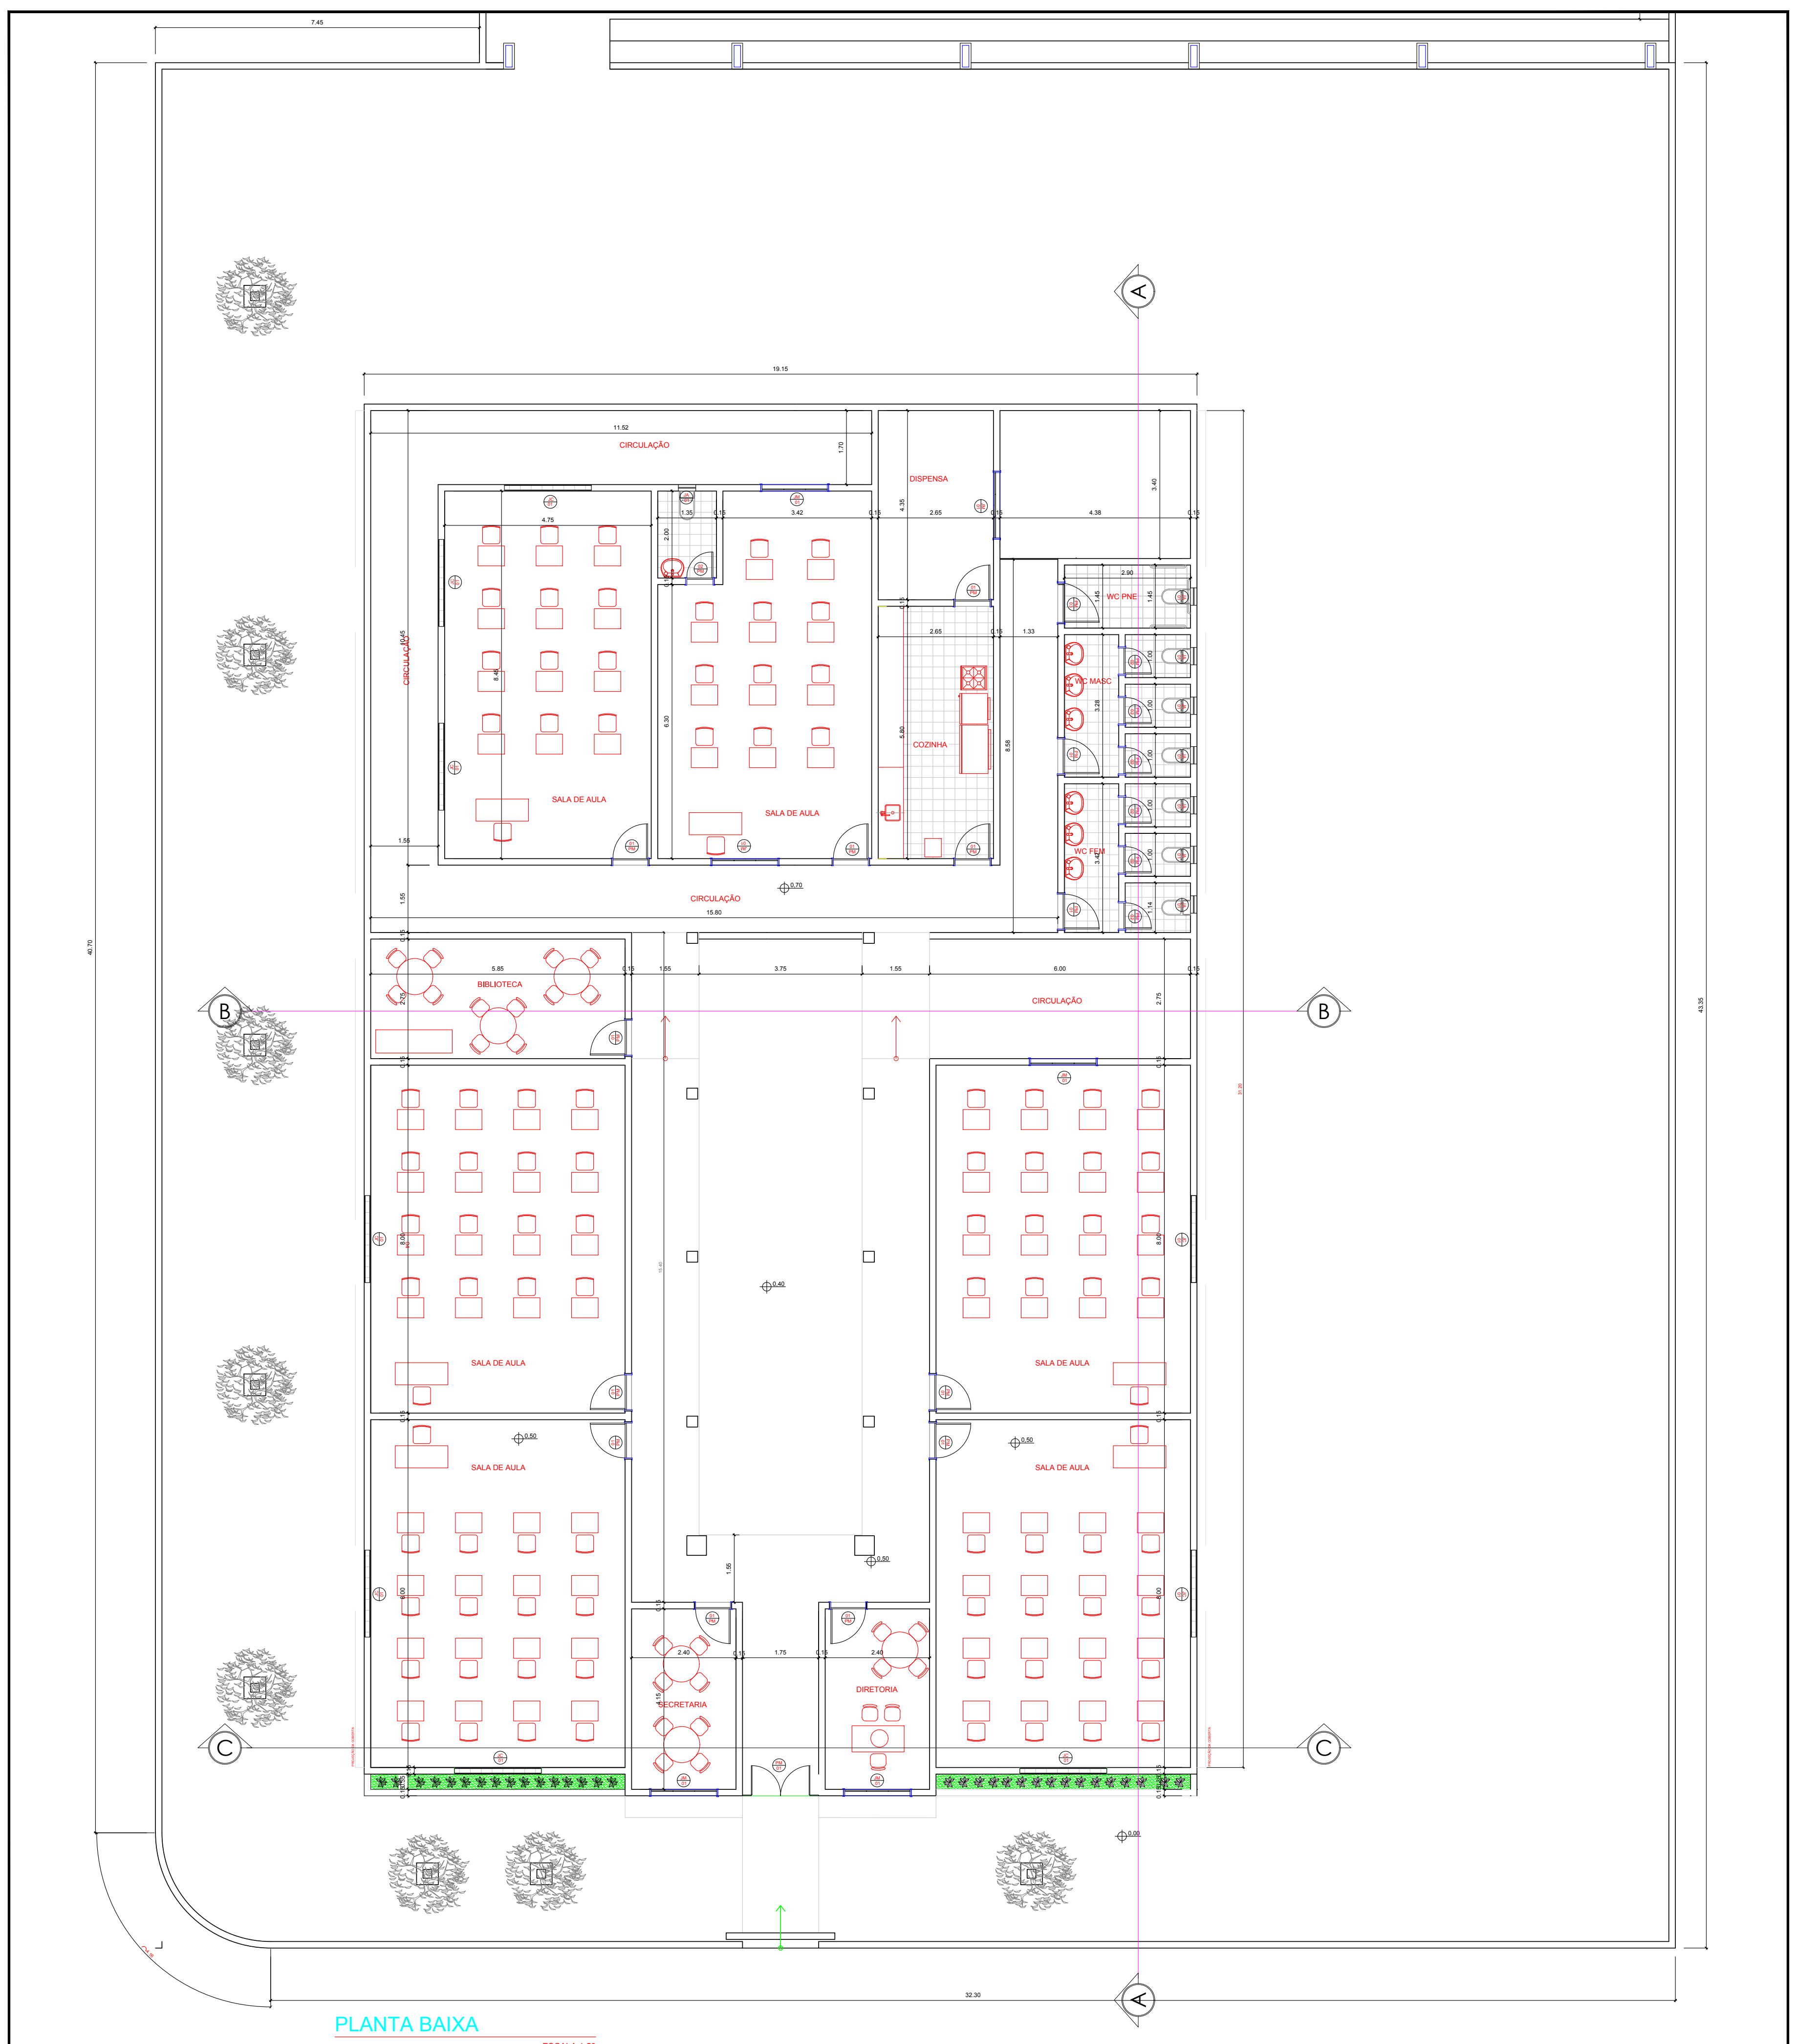
7.45
19.15
11.52
CIRCULAÇÃO
1.70
DISPENSA
4.35
2.65
4.38
3.40
4.75
3.42
1.35
2.00
CIRCULAÇÃO
8.45
6.30
SALA DE AULA
SALA DE AULA
5.80
COZINHA
8.58
2.90
WC PNE
1.45
1.33
WC MASC
3.28
WC FEM
3.40
1.00
1.14
1.55
CIRCULAÇÃO
15.80
0.70
5.85
BIBLIOTECA
1.55
3.75
1.55
6.00
CIRCULAÇÃO
2.75
B
B
A
A
C
C
SALA DE AULA
SALA DE AULA
SALA DE AULA
SALA DE AULA
8.00
0.40
0.50
1.55
2.40
1.75
2.40
SECRETARIA
DIRETORIA
0.00
4.16
40.70
43.35
32.30

PLANTA BAIXA

ESCALA 1:50

QUADRO RESUMO DE ESQUADRIAS

ESQUADRIA	DIMENSÃO (LxH)cm	QUANT.	LOCAL	TIPO
PM 01	86,0 x 210,0	13	WC F/M, SALAS	PORTA DE MADEIRA
PM 02	60,0 x 210,0	7	WCS	PORTA DE MADEIRA
PM 03	90,0 x 210,0	1	WC PNE	PORTA DE MADEIRA
JA 01	40,0 x 40,0	8	WC FEM./MASC.	JANELA DE ALUMÍNIO
JM 01	110,0 x 40,0	6	SALAS/COZ./DISP.	JANELA DE MADEIRA
JC 01	150,0 x 100	1	SALAS	COBOGÓ

EPE

PROJETO:
REFORMA DA ESCOLA FLÓRIDO NITÃO DINIZ

LOCAL:
ZUNA URBANÁ, MUNCÍPIO DE COREMAS - PB

PROPRIETÁRIO:
PREFEITURA MUNICIPAL DE COREMAS - PB

RESPONSÁVEL TÉCNICO:
Kleber Sá de Oliveira
CREA: 160268278-0

ANOTAÇÕES:

DATA:
DEZ - 2019

FOLHA
01/02

ESCALA:
1:50

DESENHOS:
Planta Baixa

DESENHO:
Diego Romualdo de Medeiros

ARQUIVO:
ESCOLA_DNOCS_COREMAS.DWG

Kleber Sá de Oliveira
Engenheiro Civil
CREA 1602682780

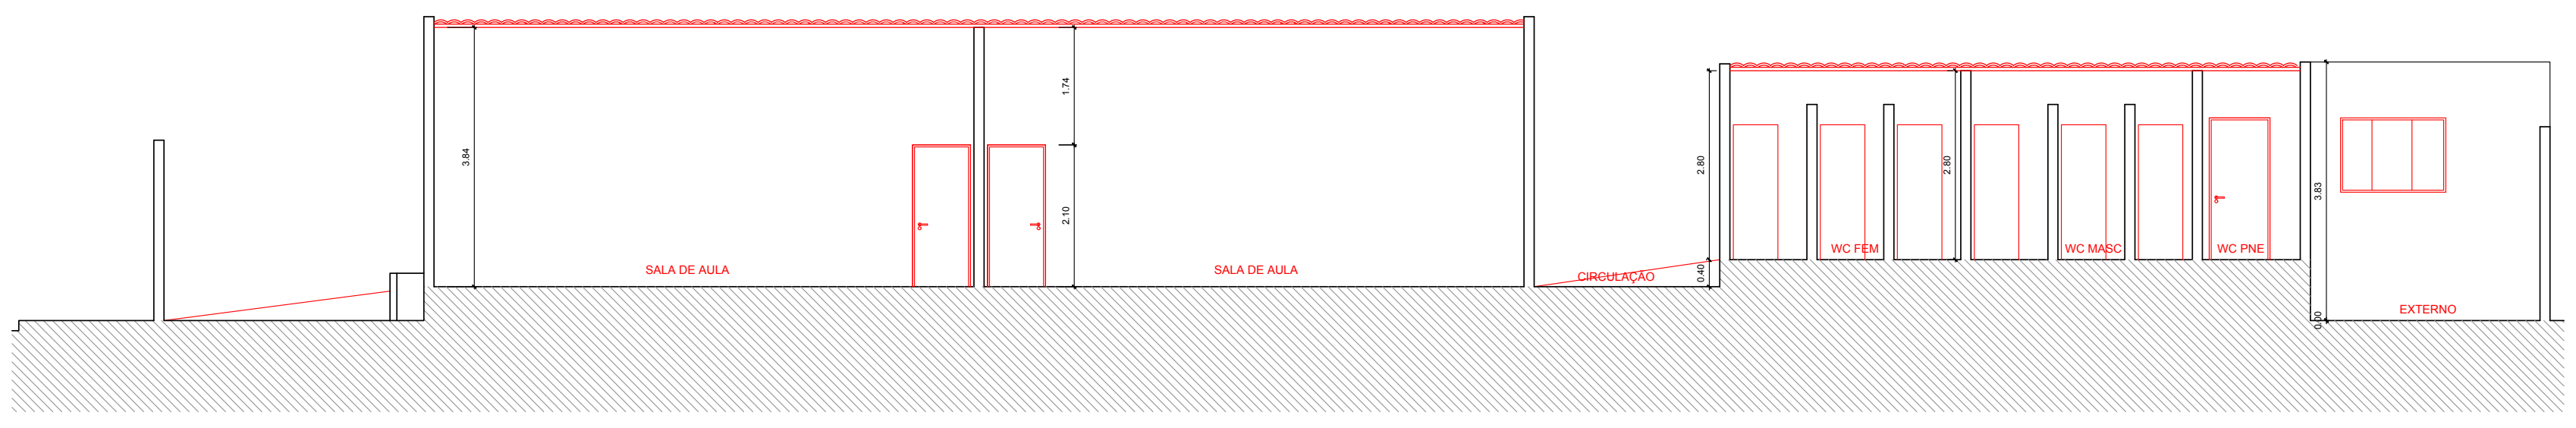
3.84
1.74
2.10
SALA DE AULA
SALA DE AULA
CIRCULAÇÃO
0.40
2.80
2.80
WC FEM
WC MASC
WC PNE
3.83
0.60
EXTERNO

CORTE AA

ESCALA 1/45

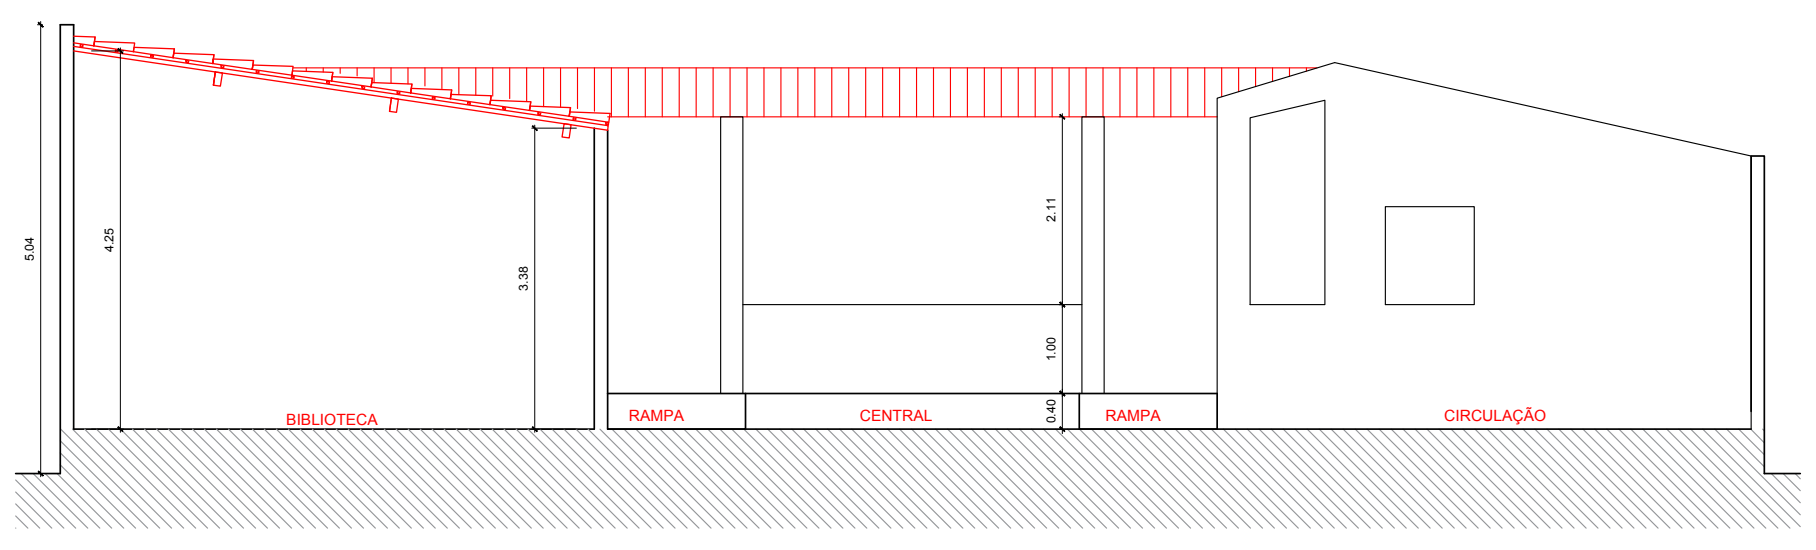
5.04
4.25
3.38
2.11
1.00
0.40
BIBLIOTECA
RAMPA
CENTRAL
RAMPA
CIRCULAÇÃO

CORTE BB

ESCALA 1/45

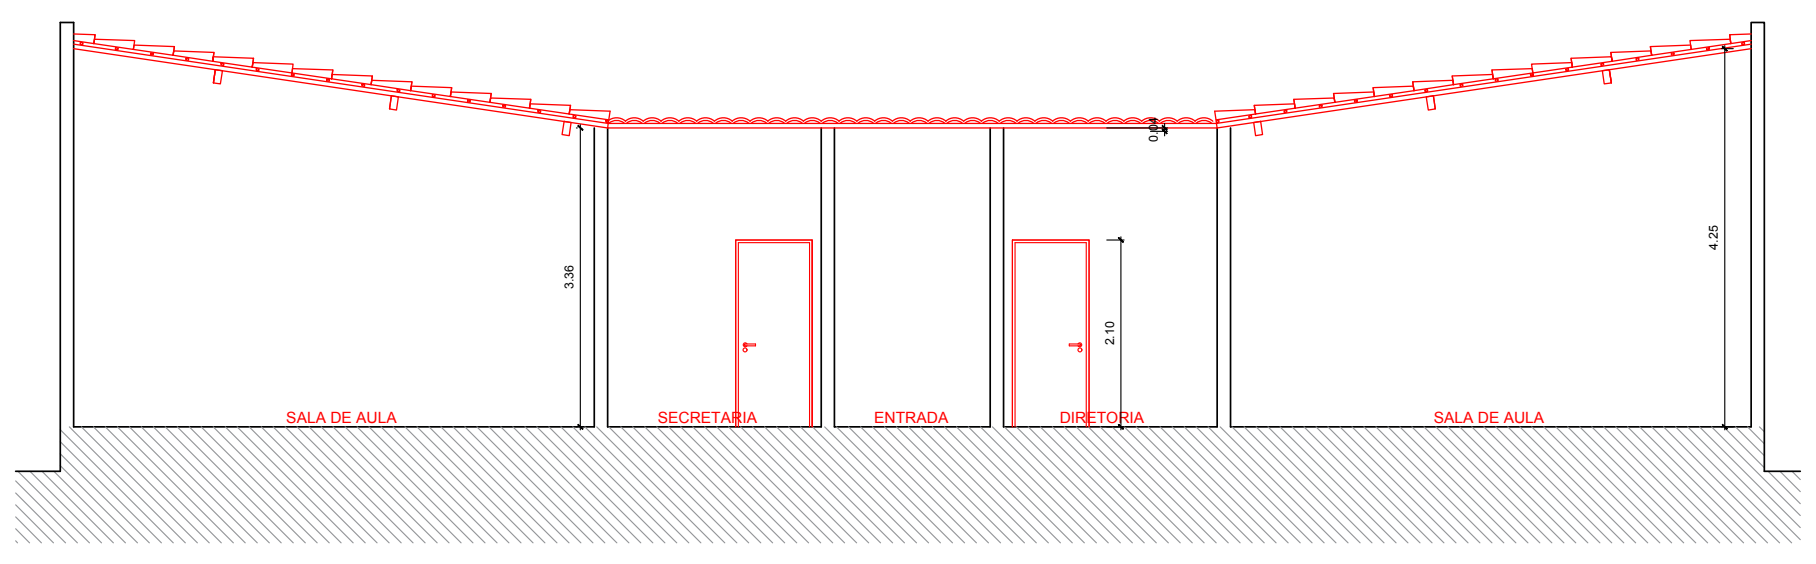
3.36
2.10
4.25
SALA DE AULA
SECRETARIA
ENTRADA
DIRETORIA
SALA DE AULA

CORTE CC

ESCALA 1/45

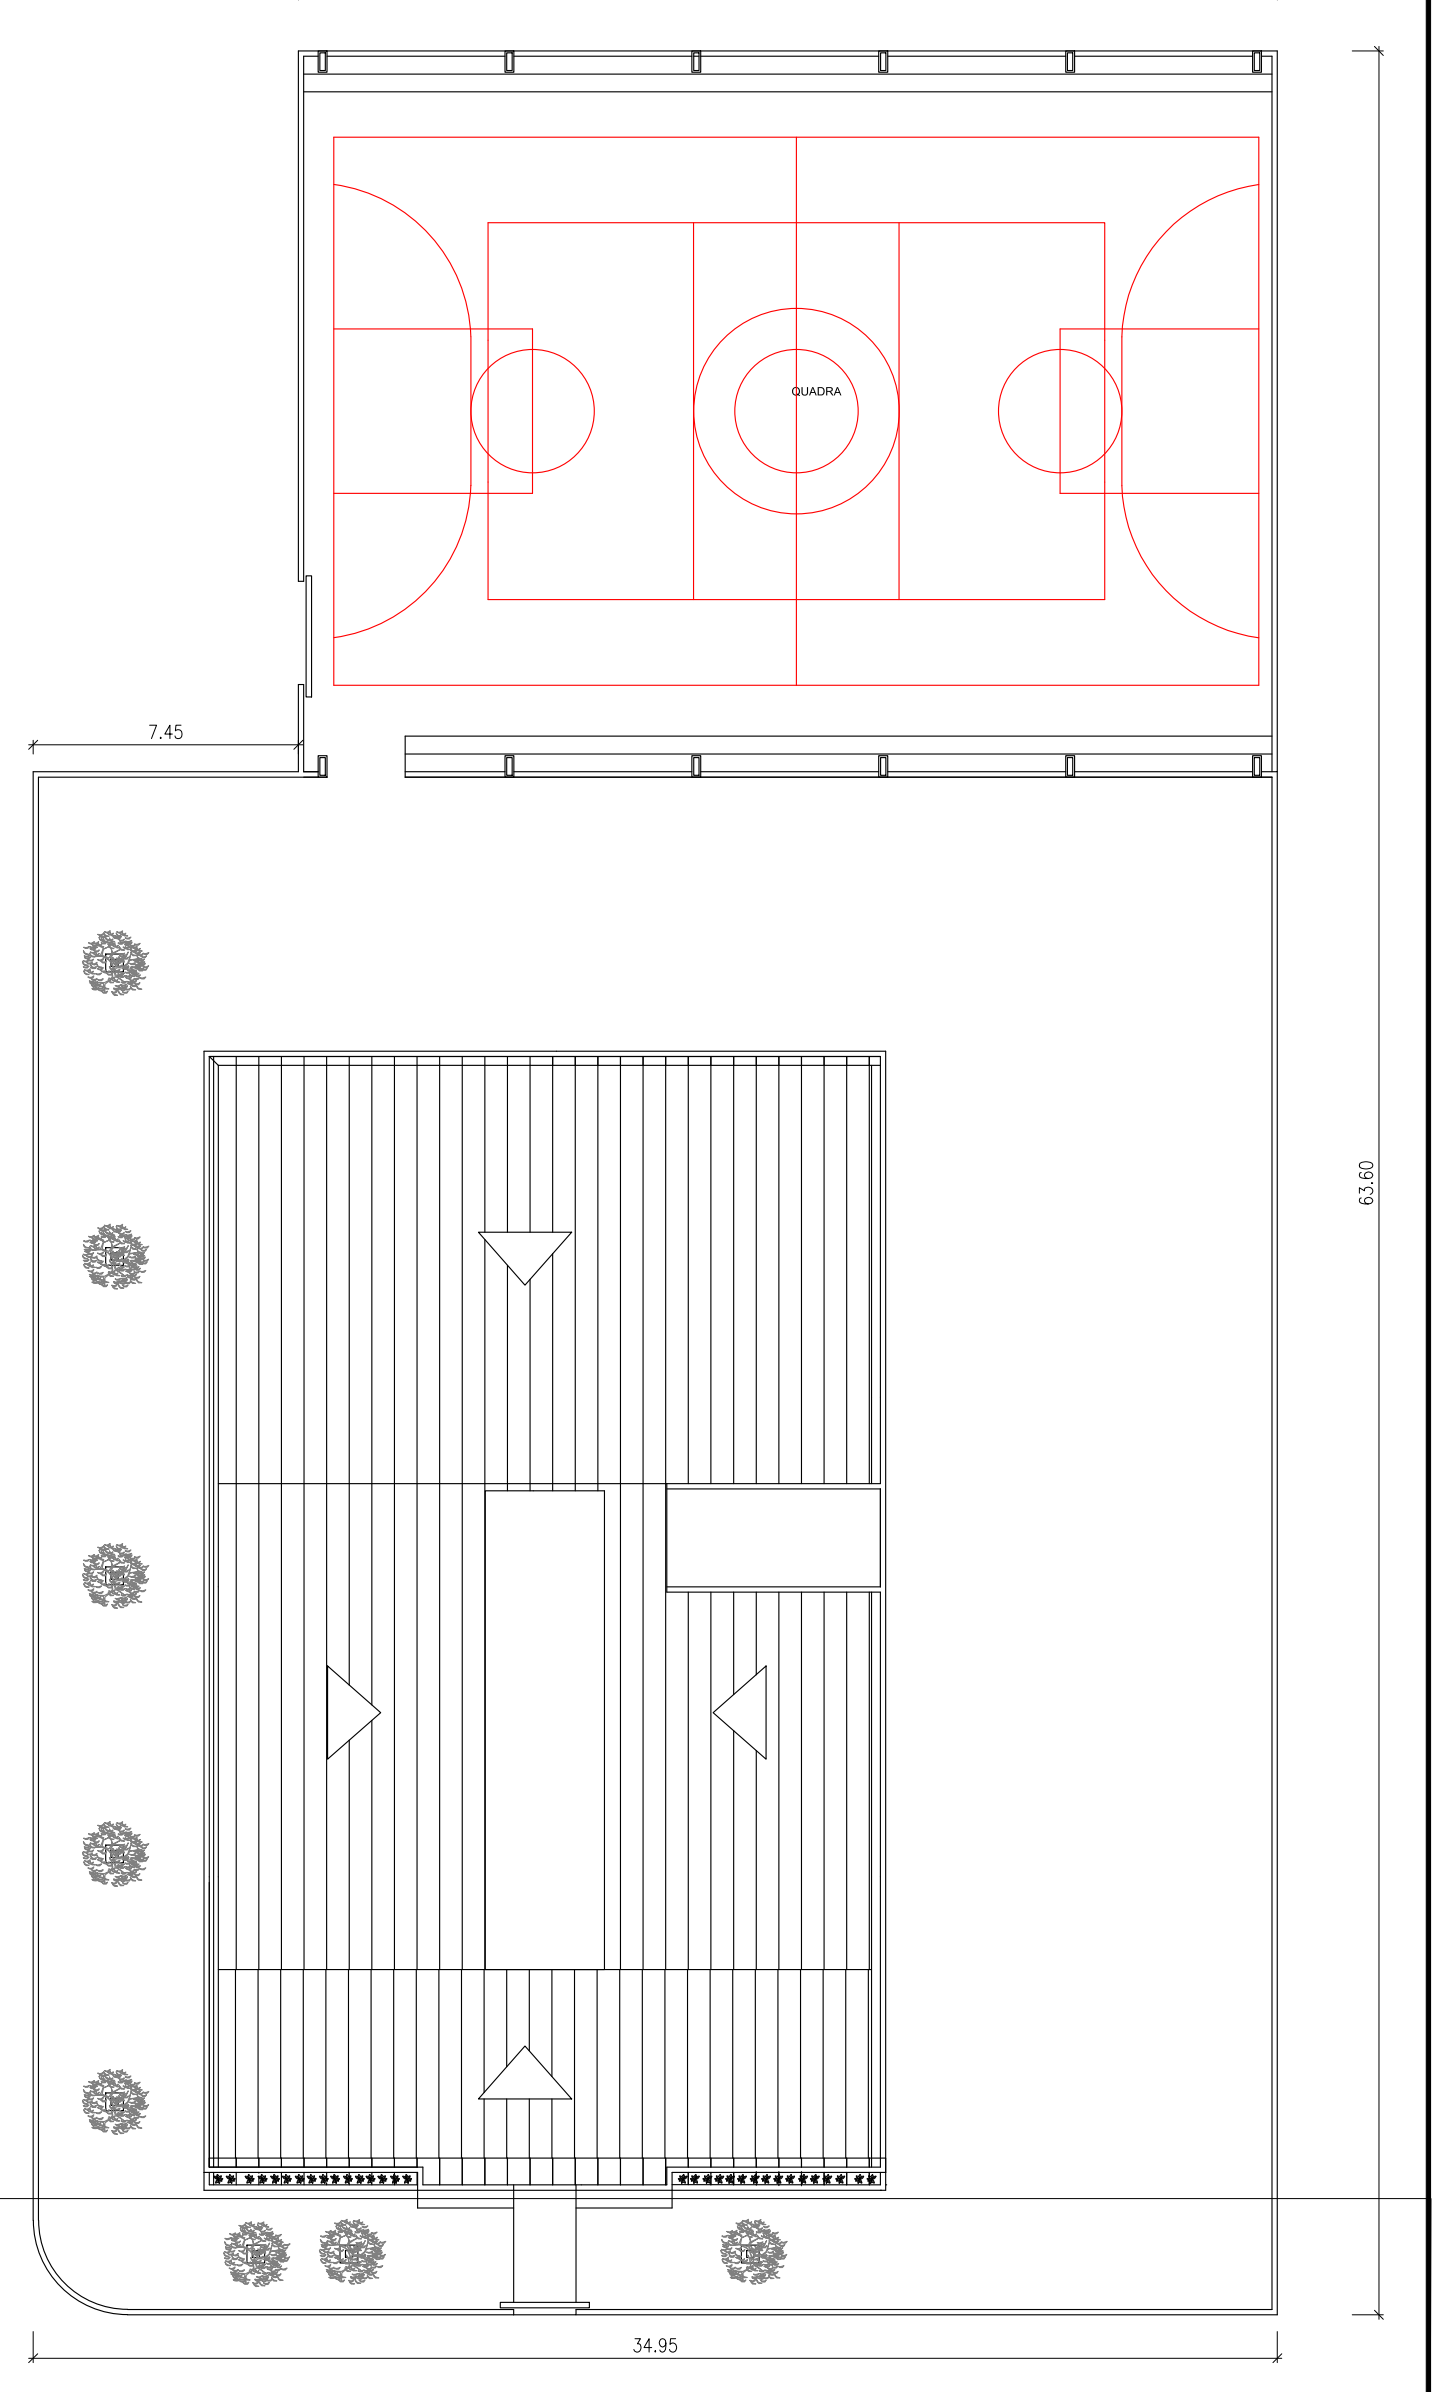
QUADRA
7.45
63.60
34.95

PLANTA DE COBERTA E LOCAÇÃO

ESCALA 1:125

EPE

PROJETO:
REFORMA DA ESCOLA FLÓRIDO NITÃO DINIZ

LOCAL:
ZUNA URBANA, MUNCÍPIO DE COREMAS - PB

PROPRIETÁRIO:
PREFEITURA MUNICIPAL DE COREMAS - PB

RESPONSÁVEL TÉCNICO:
Kleber Sá de Oliveira
CREA: 160268278-0

ANOTAÇÕES:

DATA:
DEZ - 2019

FOLHA
02/02

ESCALA:
1:50
1:125

DESENHOS:
Cortes
Locação e Coberta

DESENHO:
Diego Romualdo de Medeiros

ARQUIVO:
ESCOLA_DNOCS_COREMAS.DWG

Kleber Sá de Oliveira
Engenheiro Civil
CREA 1602682780