



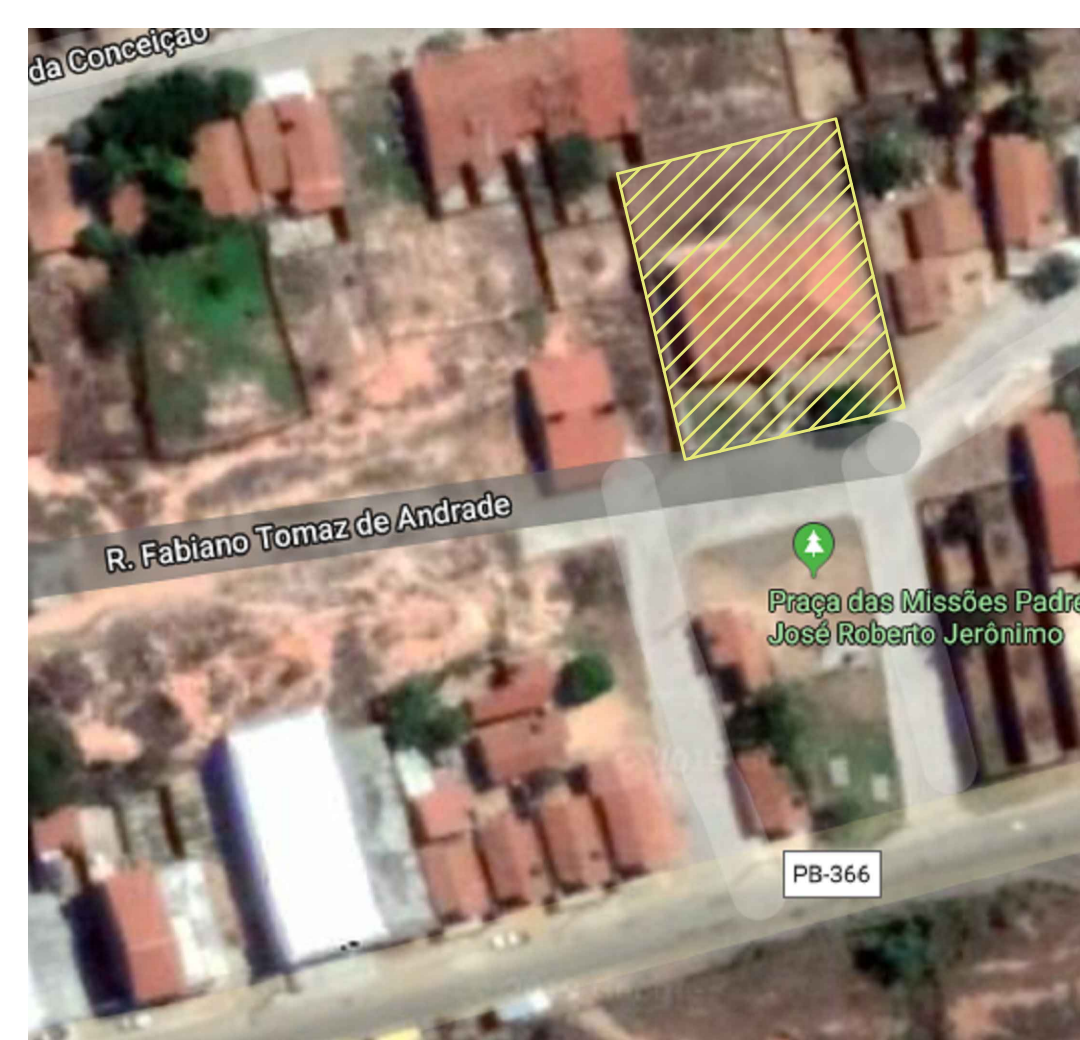

Planta de localização

* Conferir medidas no local

Projeto:		Corteiro Intelectual e Cidadão	
PROJETO ARQUITETÔNICO - REFORMA ESCOLA LOGRADOURO			
Cliente:		Prefeitura Municipal de Coremas	
Arquiteto (a):		Kírya Cristinne 00	
Conteúdo:		Planta de localização Planta de cobertura	Folha: 01 04
Folha:		Indicada	Carimbo:
Data:		DEZEMBRO/2019	Kírya Cristinne Arquiteta

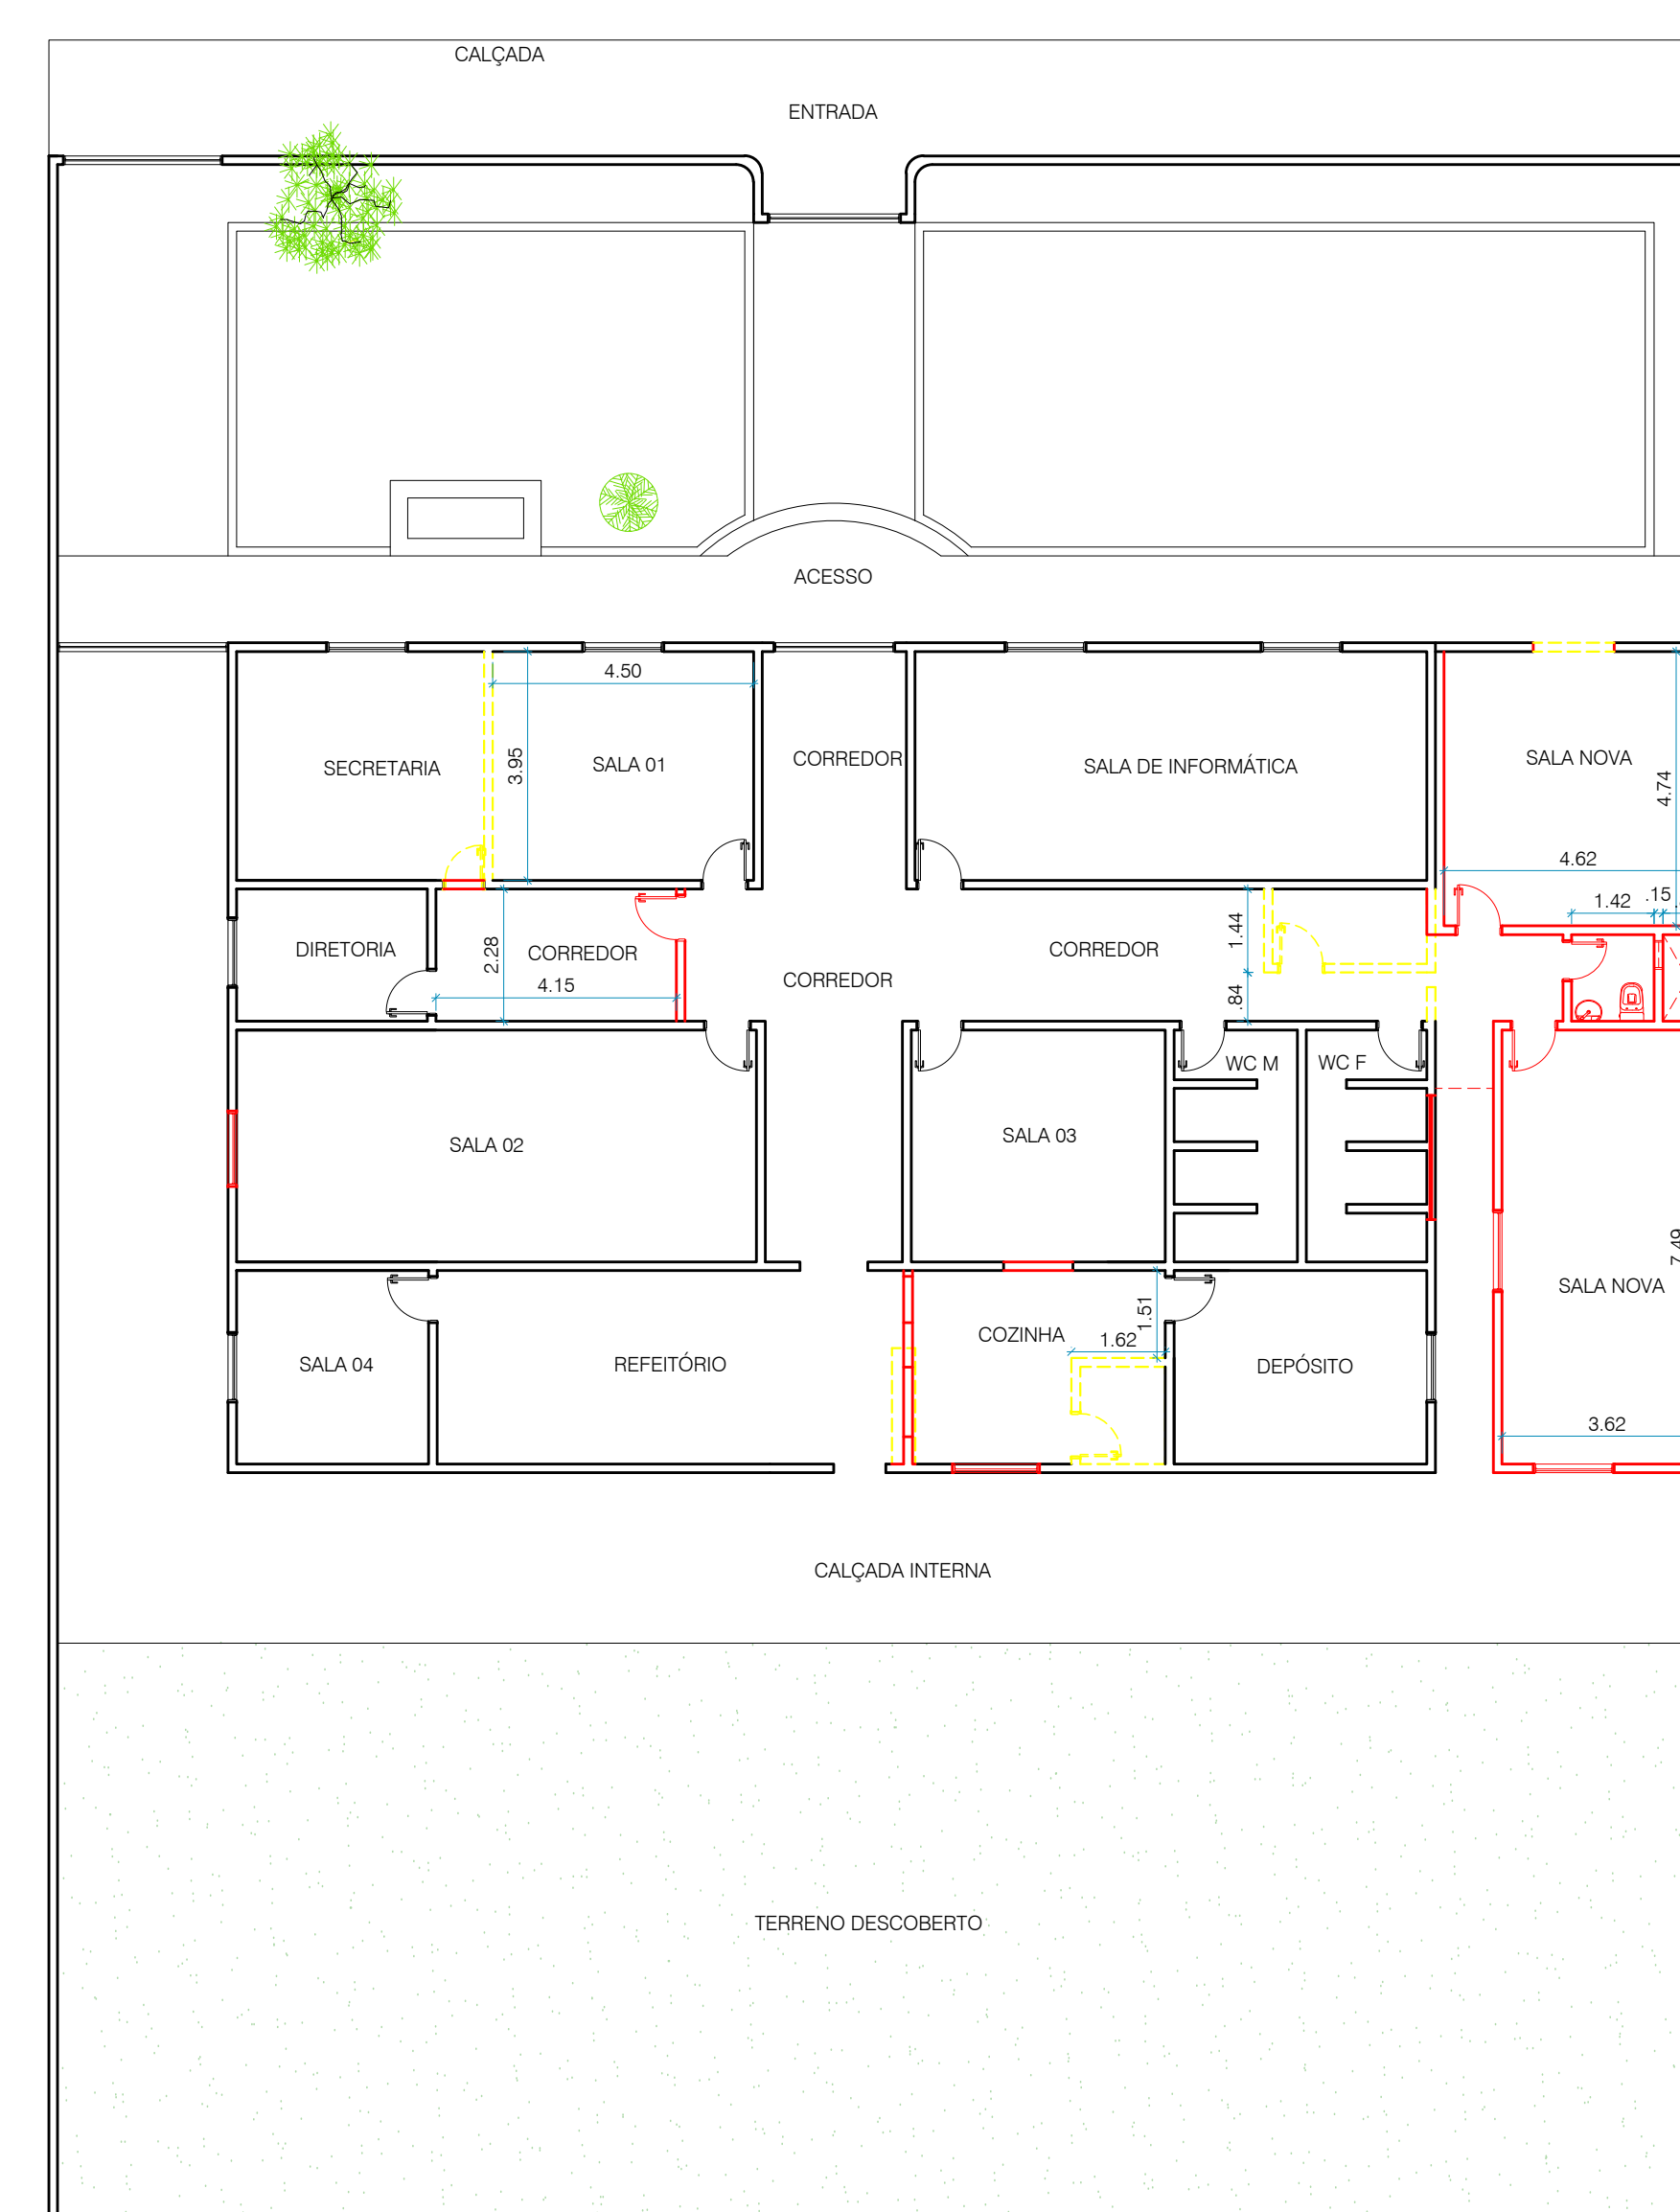

PLANTA BAJXA - REFORMA
ESCALA 1:125

LEGENDA de PAREDES

- == à Construir
- à Demolir
- === Existente


* Conferir medidas no local

Projeto		Código de Identificação do Projeto	
PROJETO ARQUITETÔNICO - REFORMA ESCOLA LOGRADOURO			
Cliente		Prestador	
Prefeitura Municipal de Coremas			
Assinado por		Assinado em	
Kiryia Cristinne		00	
Comissão		Prestação	
Planta de reforma		02/04	
Descrição		Gerenciado por	
Indicada		Kiryia Cristinne Fale conosco	
Data			
DEZEMBRO/2019			




* Conferir medidas no local


Projeto:		CENÁRIO IMPOSSÍVEL NO LUCAR	
PROJETO ARQUITETÔNICO - REFORMA ESCOLA LOGRADUORO			
Cliente:		PREFEITURA MUNICIPAL DE COREMAS	
Arquiteto (s):		KIRYA CRISTIANE	
Data:		00	
Conteúdo:		Planta baixa 03₀₄	
Assunto:		Indicada	
Data:		DEZEMBRO/2019 KIRYA CRISTIANE LUC. 00001	

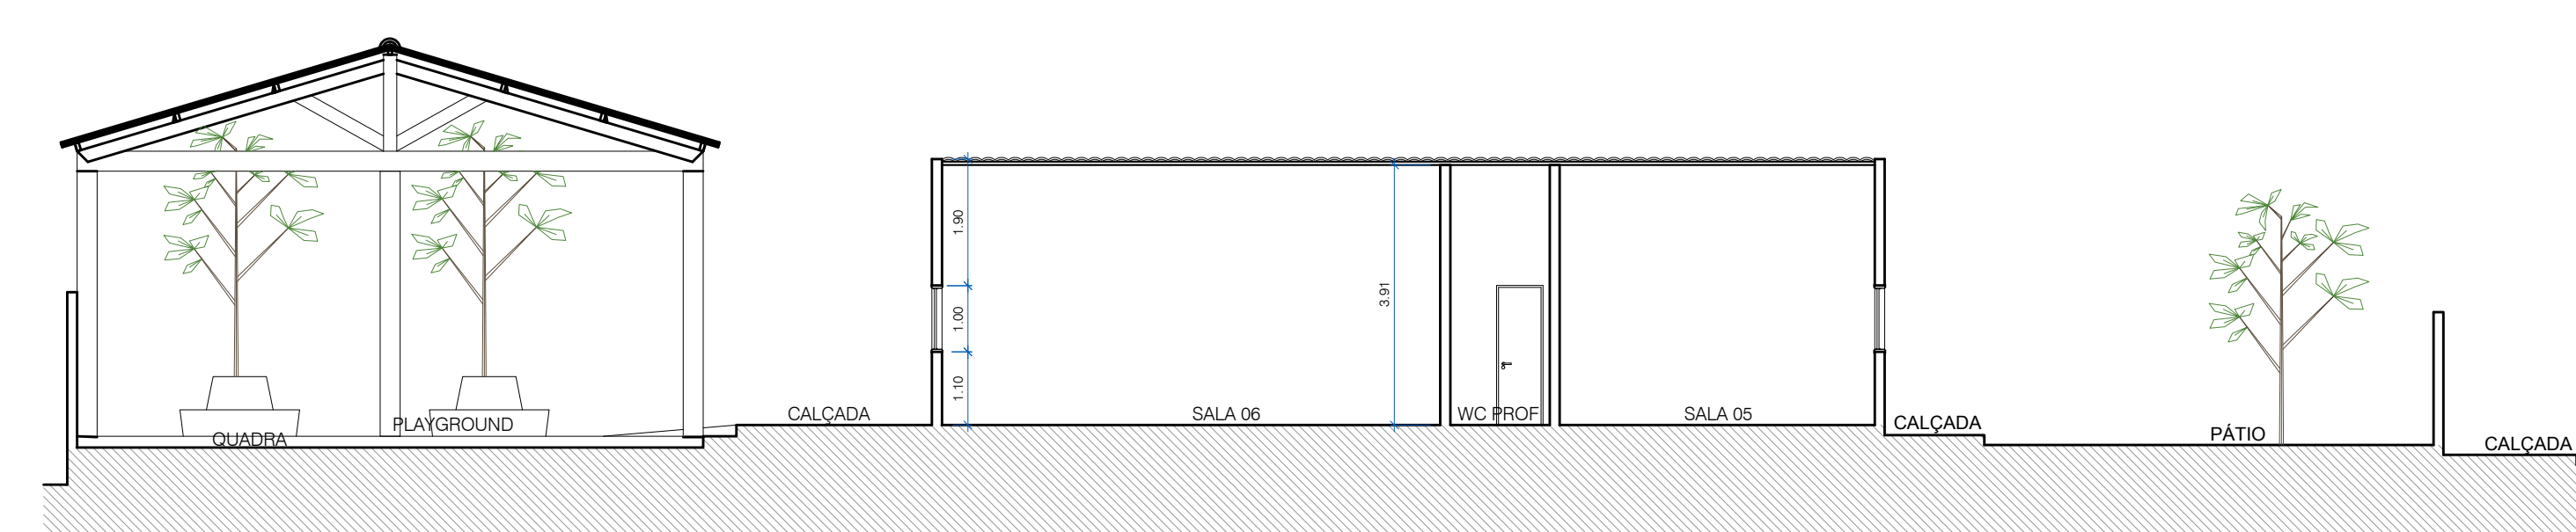


CORTE DO

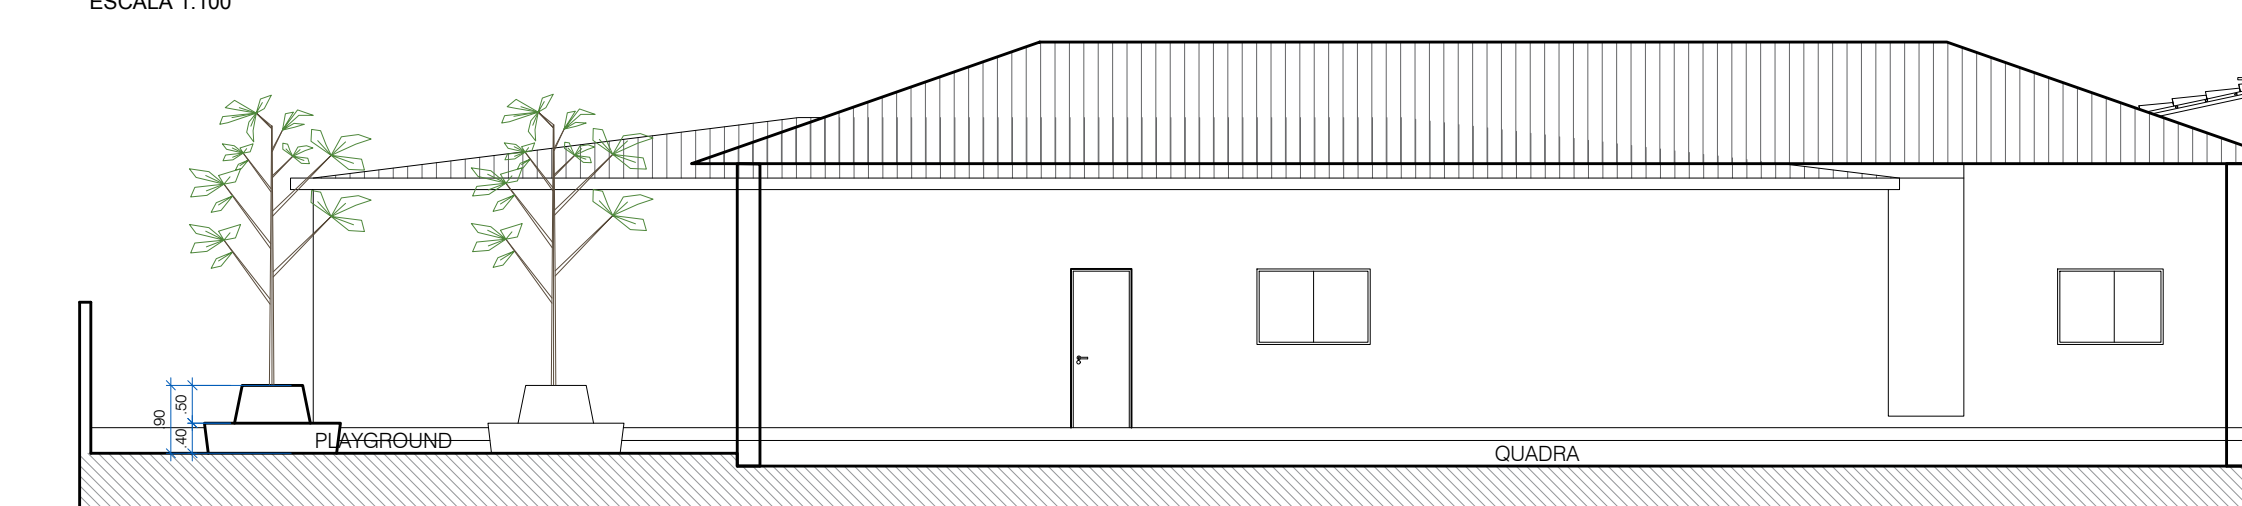

CORTE CC

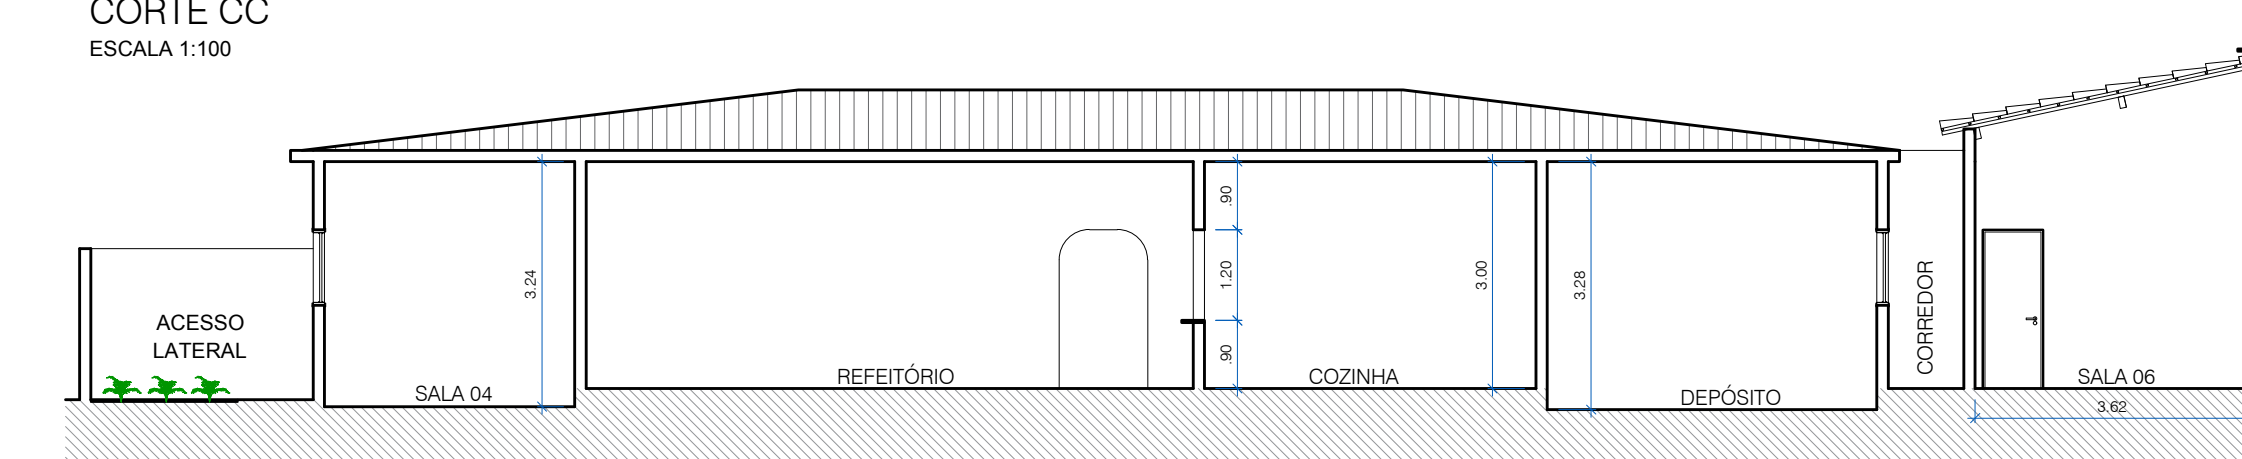

CORTE BB

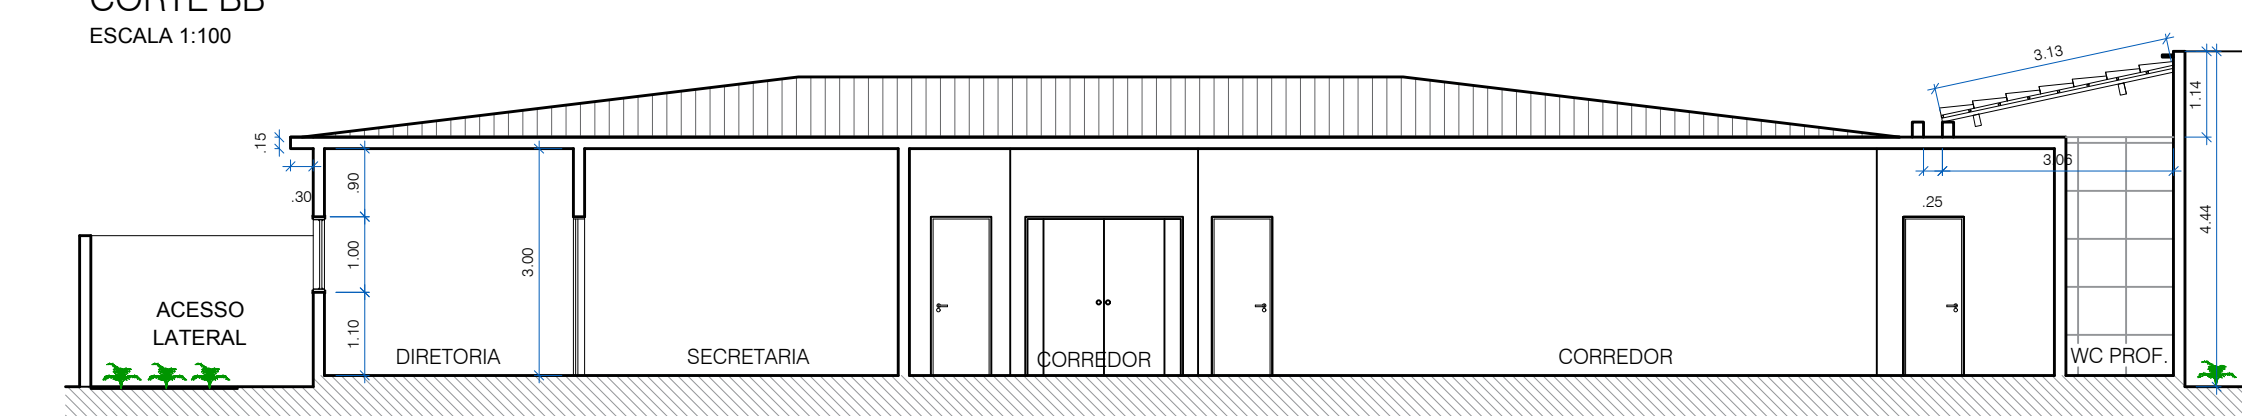

CORTE AA

* Conferir medidas no local

Projeto		Código	
PROJETO ARQUITETÔNICO - REFORMA ESCOLA LOGRADOURO			
Cliente		Prestador	
Prefeitura Municipal de Coremas			
Assinatura do		Assinatura do	
Kirya Cristinne		00	
Cidade		UF	
Corões		04/04	
Data		Assinatura	
Indicada		Kirya Cristinne	
Data		Assinatura	
DEZEMBRO/2019		Kirya Cristinne	
		Assinatura	