


VISTA DOS DRENO


TRECHO 01

ESCALA 1/35

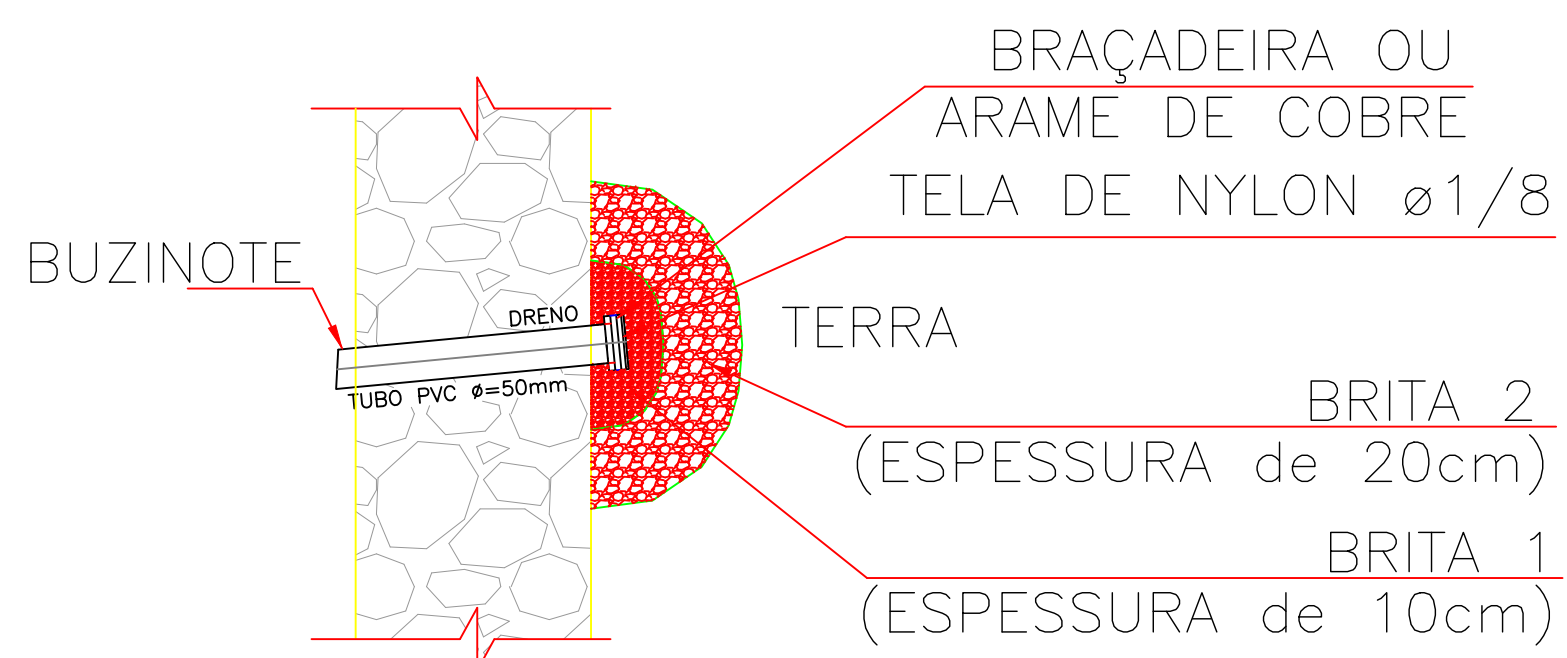

DET. DO DRENO


ESCALA 1/15

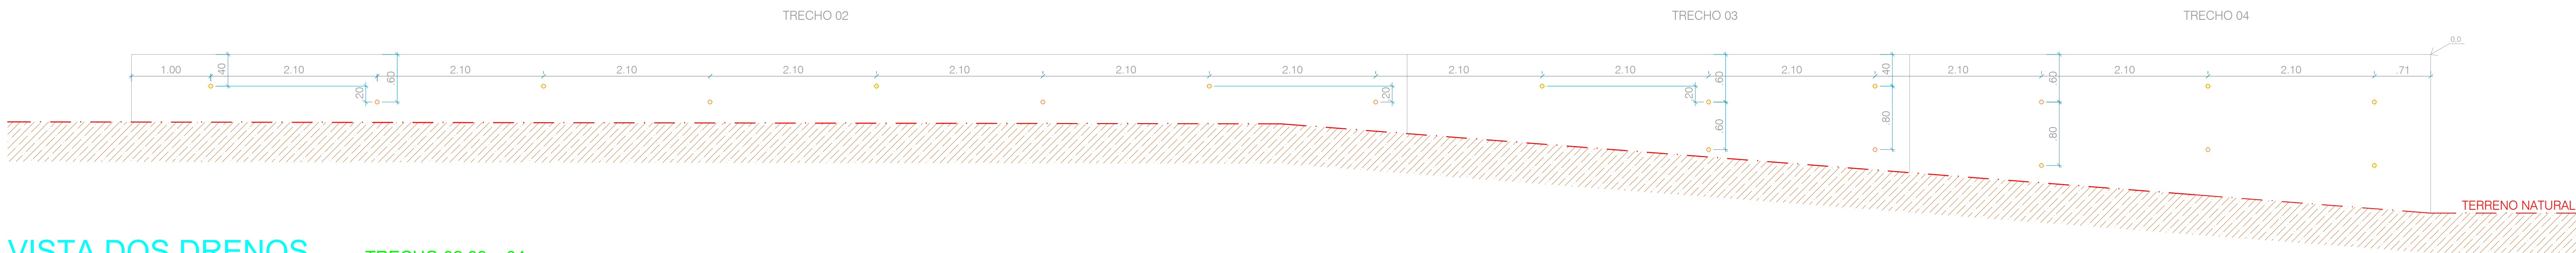

VISTA DOS DRENOS

TRECHO 02,03 e 04

ESCALA 1/35

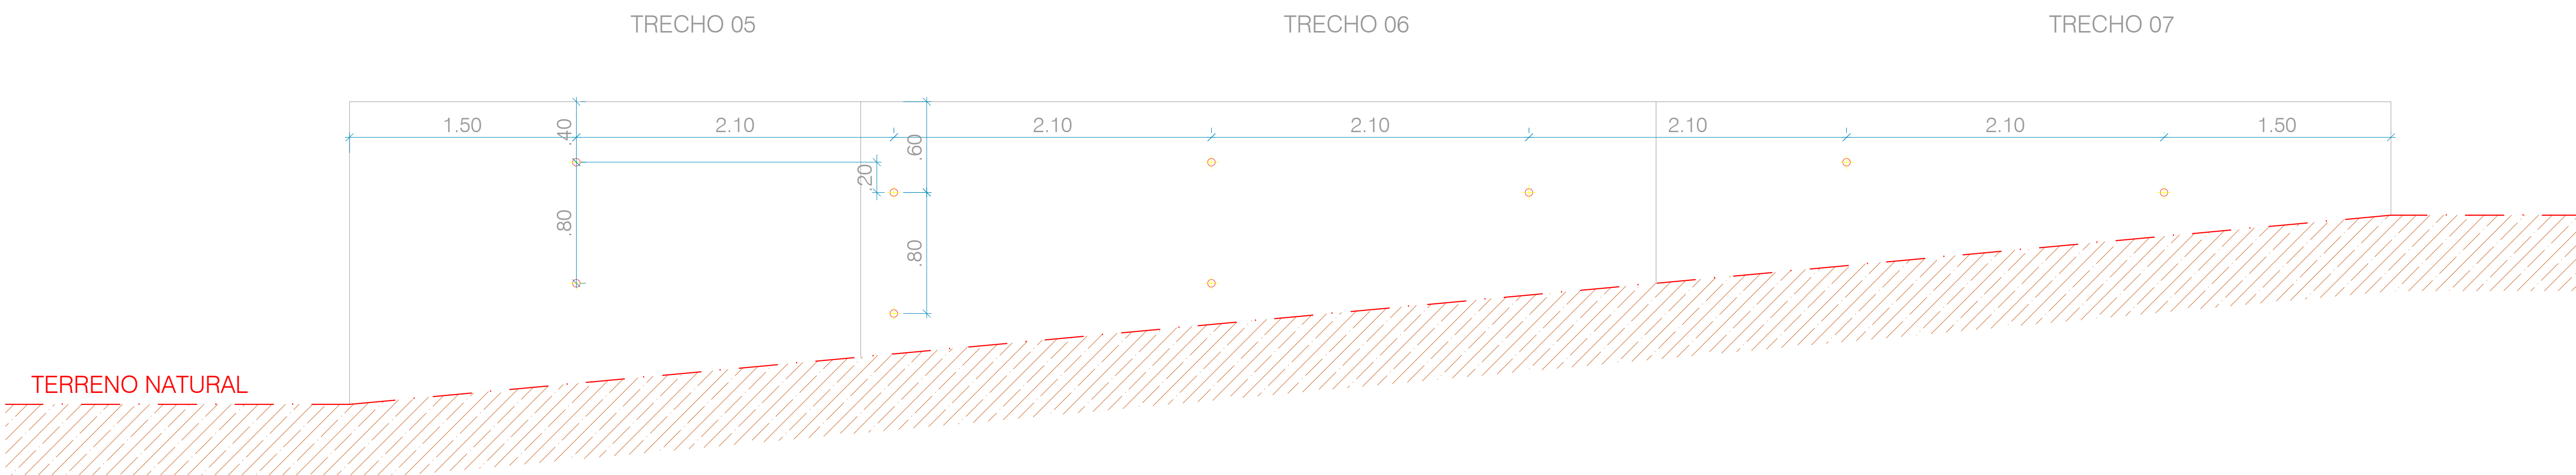

VISTA DOS DRENOS

TRECHO 05,06 e 07

ESCALA 1/35

EPE		PROJETO: MURO DE ARRIMO DA ESCOLA LOGRADOURO	
		LOCAL: ZUNA URBANA, MUNICÍPIO DE COREMAS - PB	
FOLHA 04/06		PROPRIETÁRIO: PREFEITURA MUNICIPAL DE COREMAS - PB	
ESCALA: Indicada		RESPONSÁVEL TÉCNICO: Kleber Sá de Oliveira Crea: 160268278-0	
ARQUIVO: PROJETO_MURO DE ARRIMO.dwg		DESENHO: Diego Romualdo de Medeiros	
		ANOTAÇÕES:	
		DATA: AGO - 2020	