



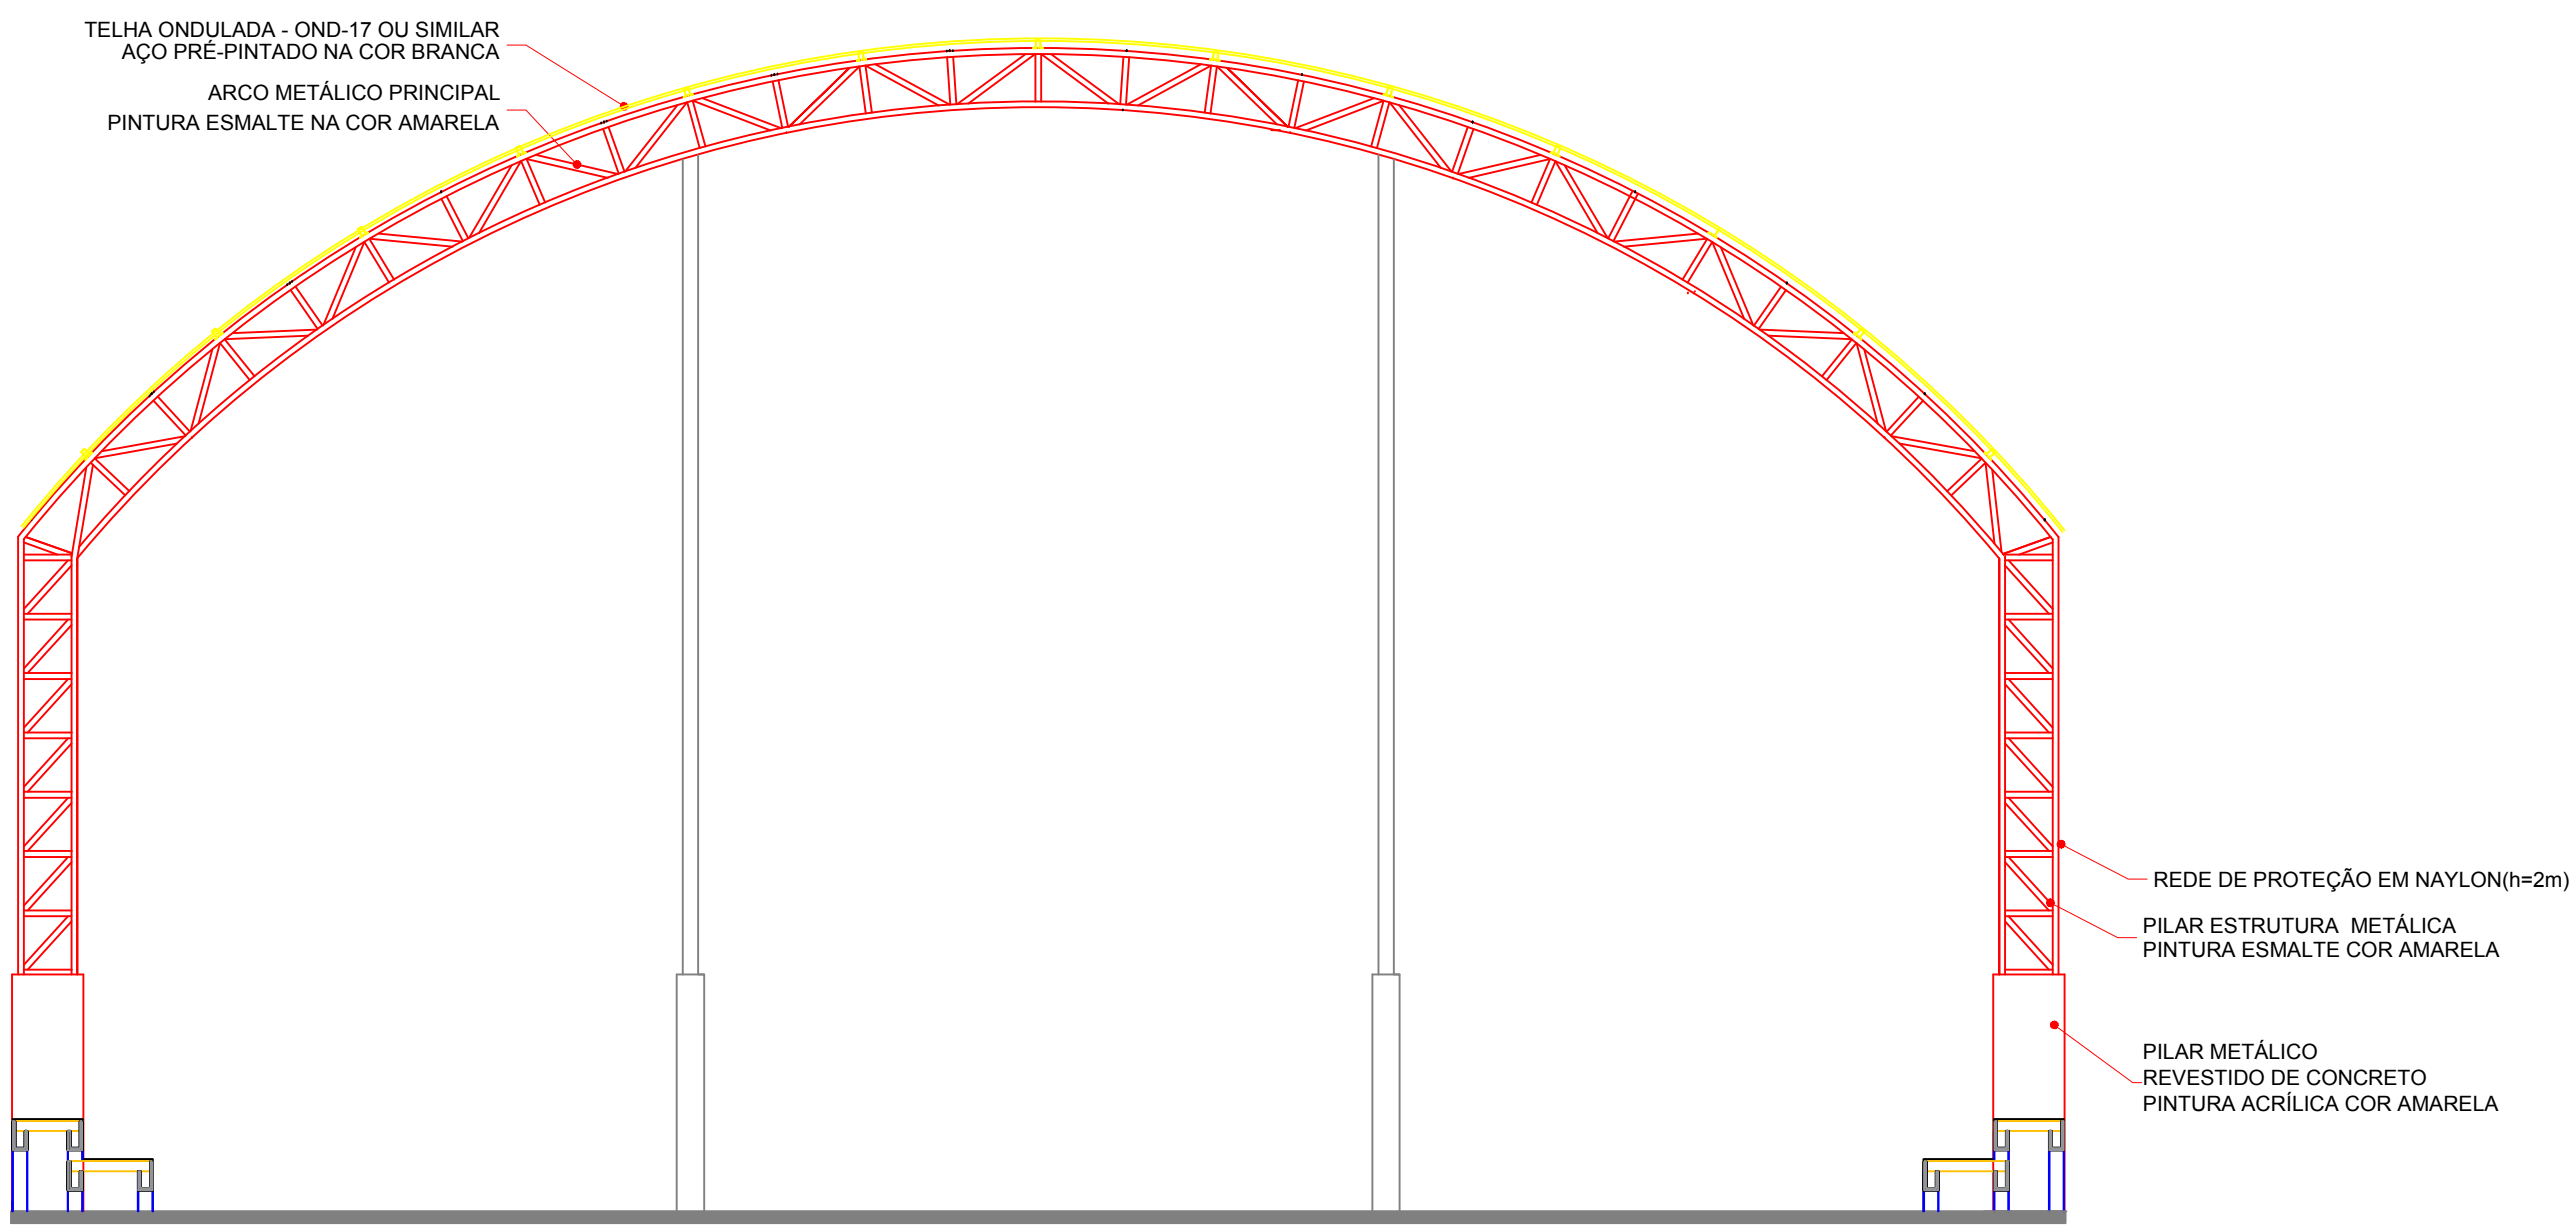

CORTE AA - QUADRA
ESCALA 1:50

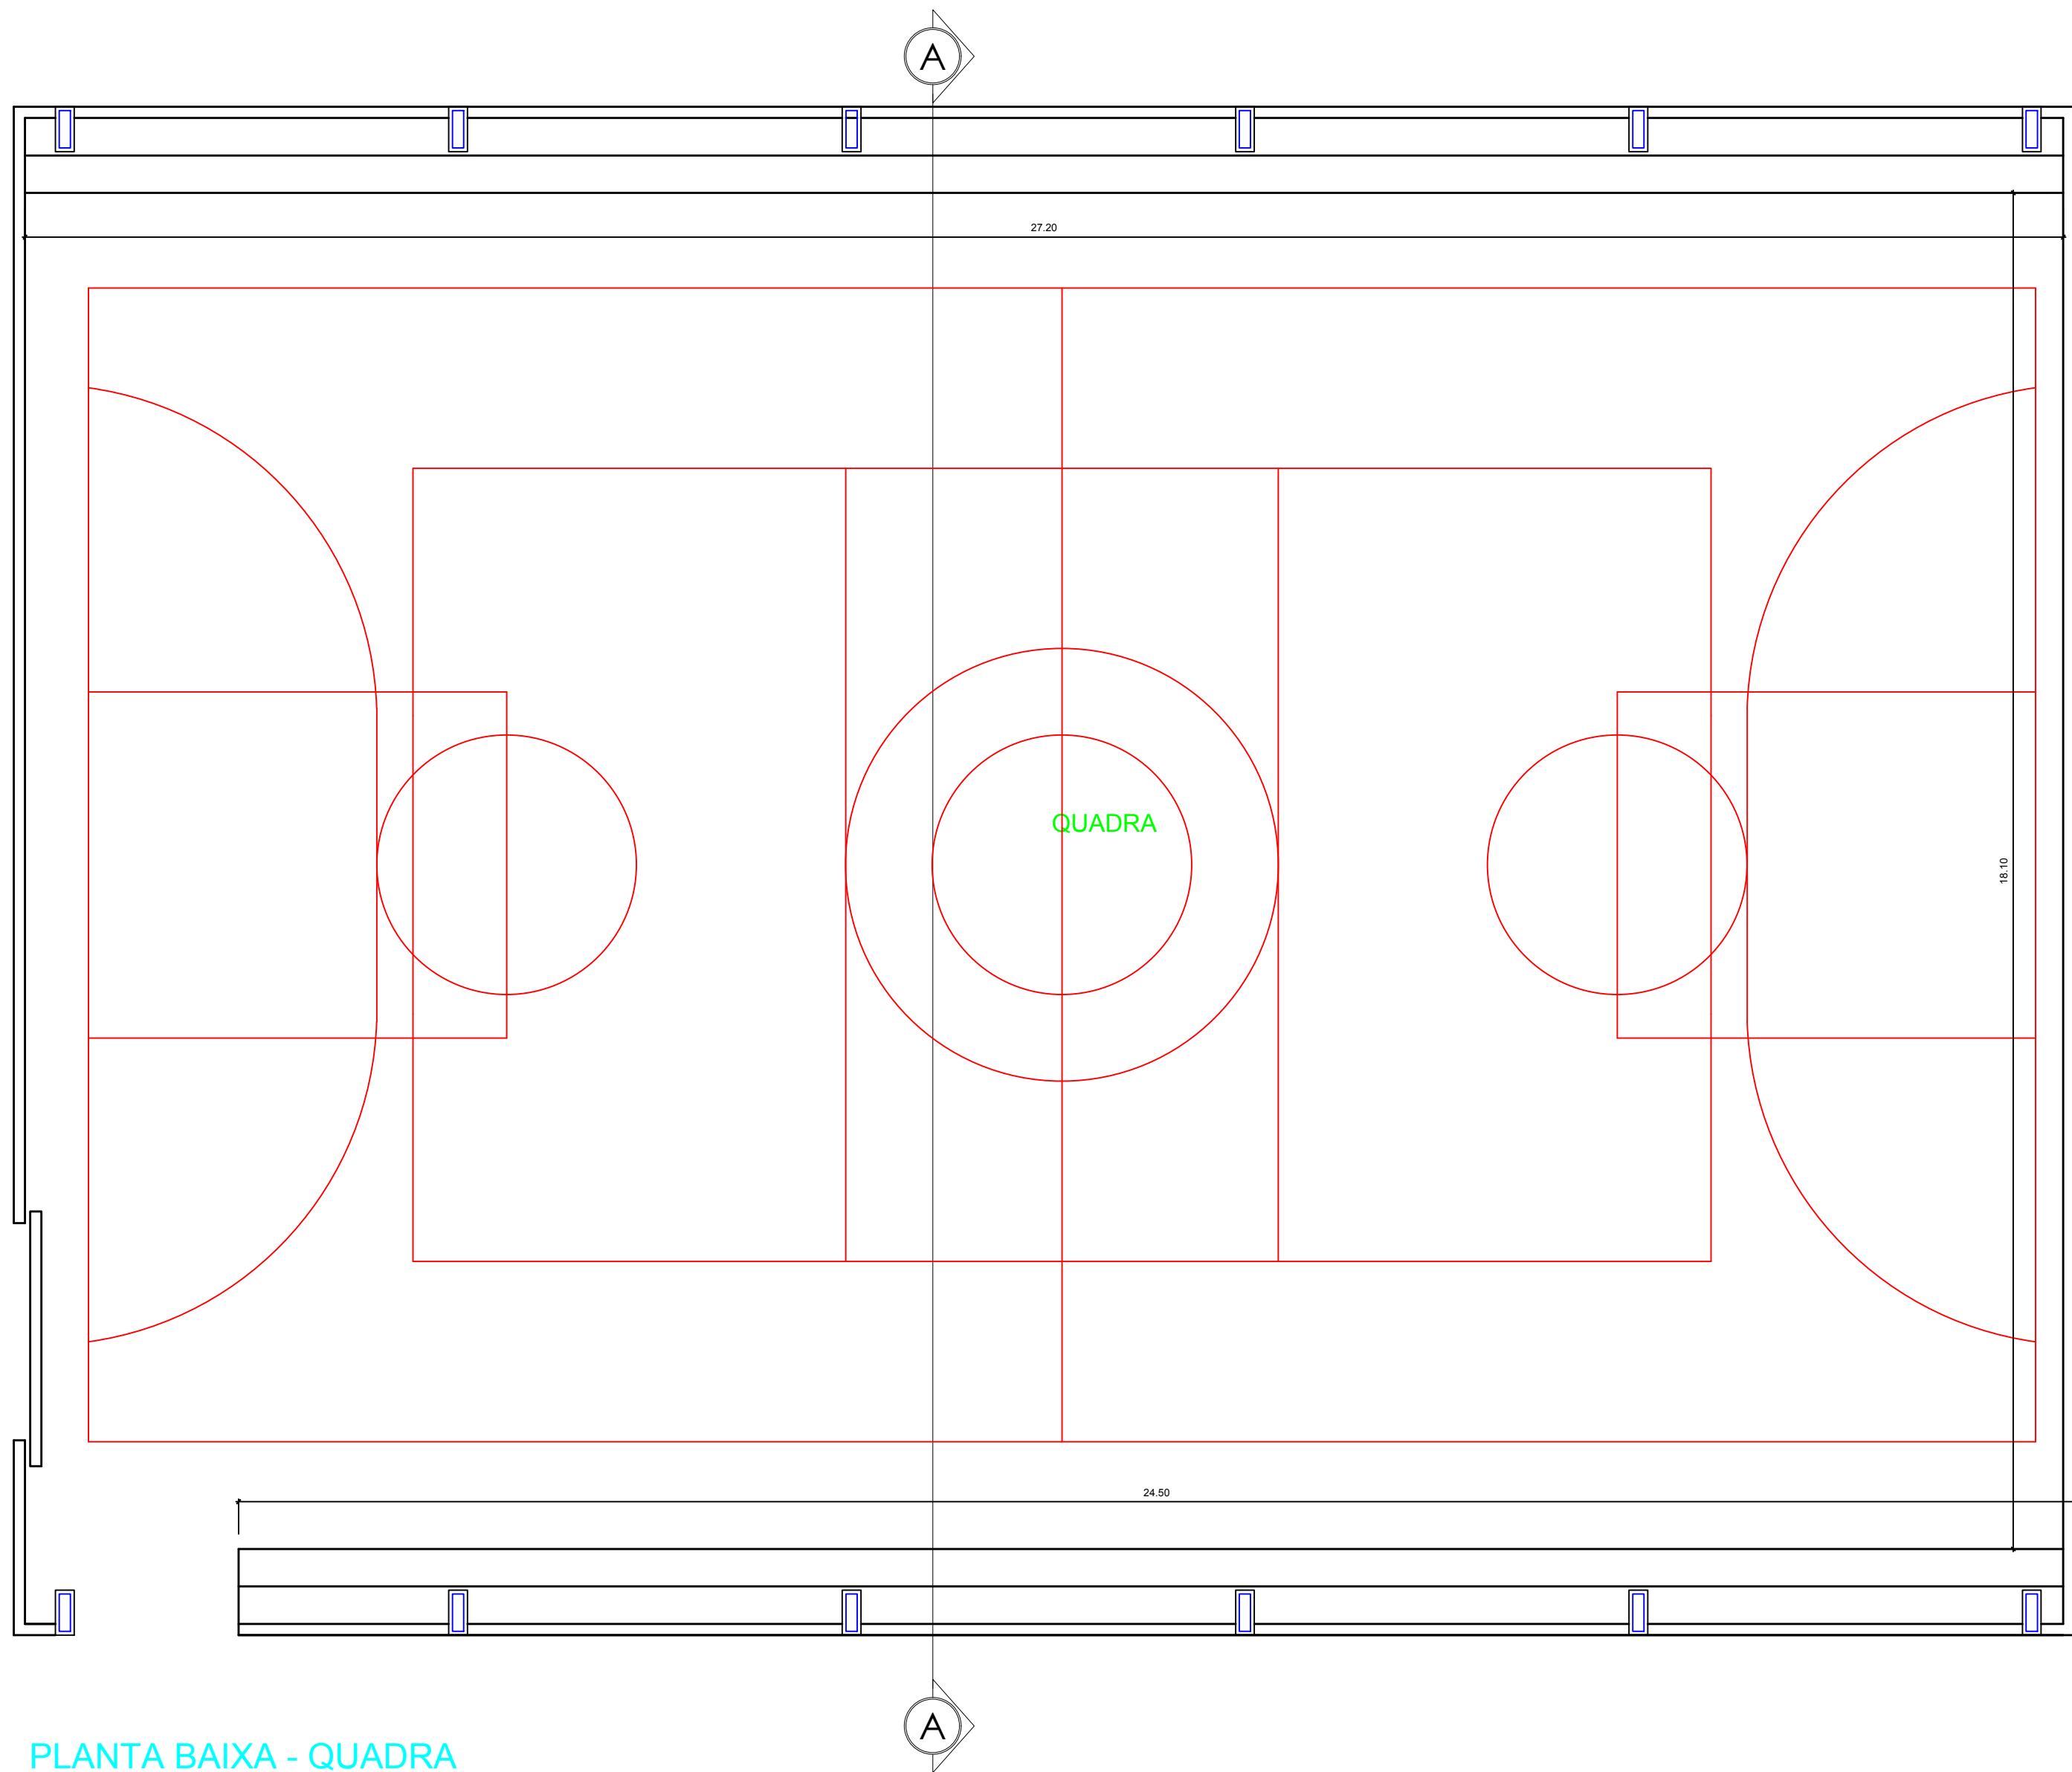

PLANTA BAIXA - QUADRA
ESCALA 1:50

EPE		PROJETO: REFORMA DA ESCOLA FLÓRIDO NITÃO DINIZ	
		LOCAL: ZONA URBANA, MUNICÍPIO DE COREMAS - PB	
FOLHA: 01/01		DESENHOS: Planta Baixa - Quadra Coberta Corte - Quadra Coberta	RESPONSÁVEL TÉCNICO: Kleber Sá de Oliveira CREA: 160268278-0
ARQUIVO: ESCOLA_DINIZS_COREMAS.DWG		DESENHO: Diego Romualdo de Medeiros	DATA: DEZ - 2019