
| REV. | DESCRIÇÃO | MODIFICADO POR | DATA |
|---|---|---|---|
| | | | |
| | | | |
| | | | |
| | | | |
| | | | |

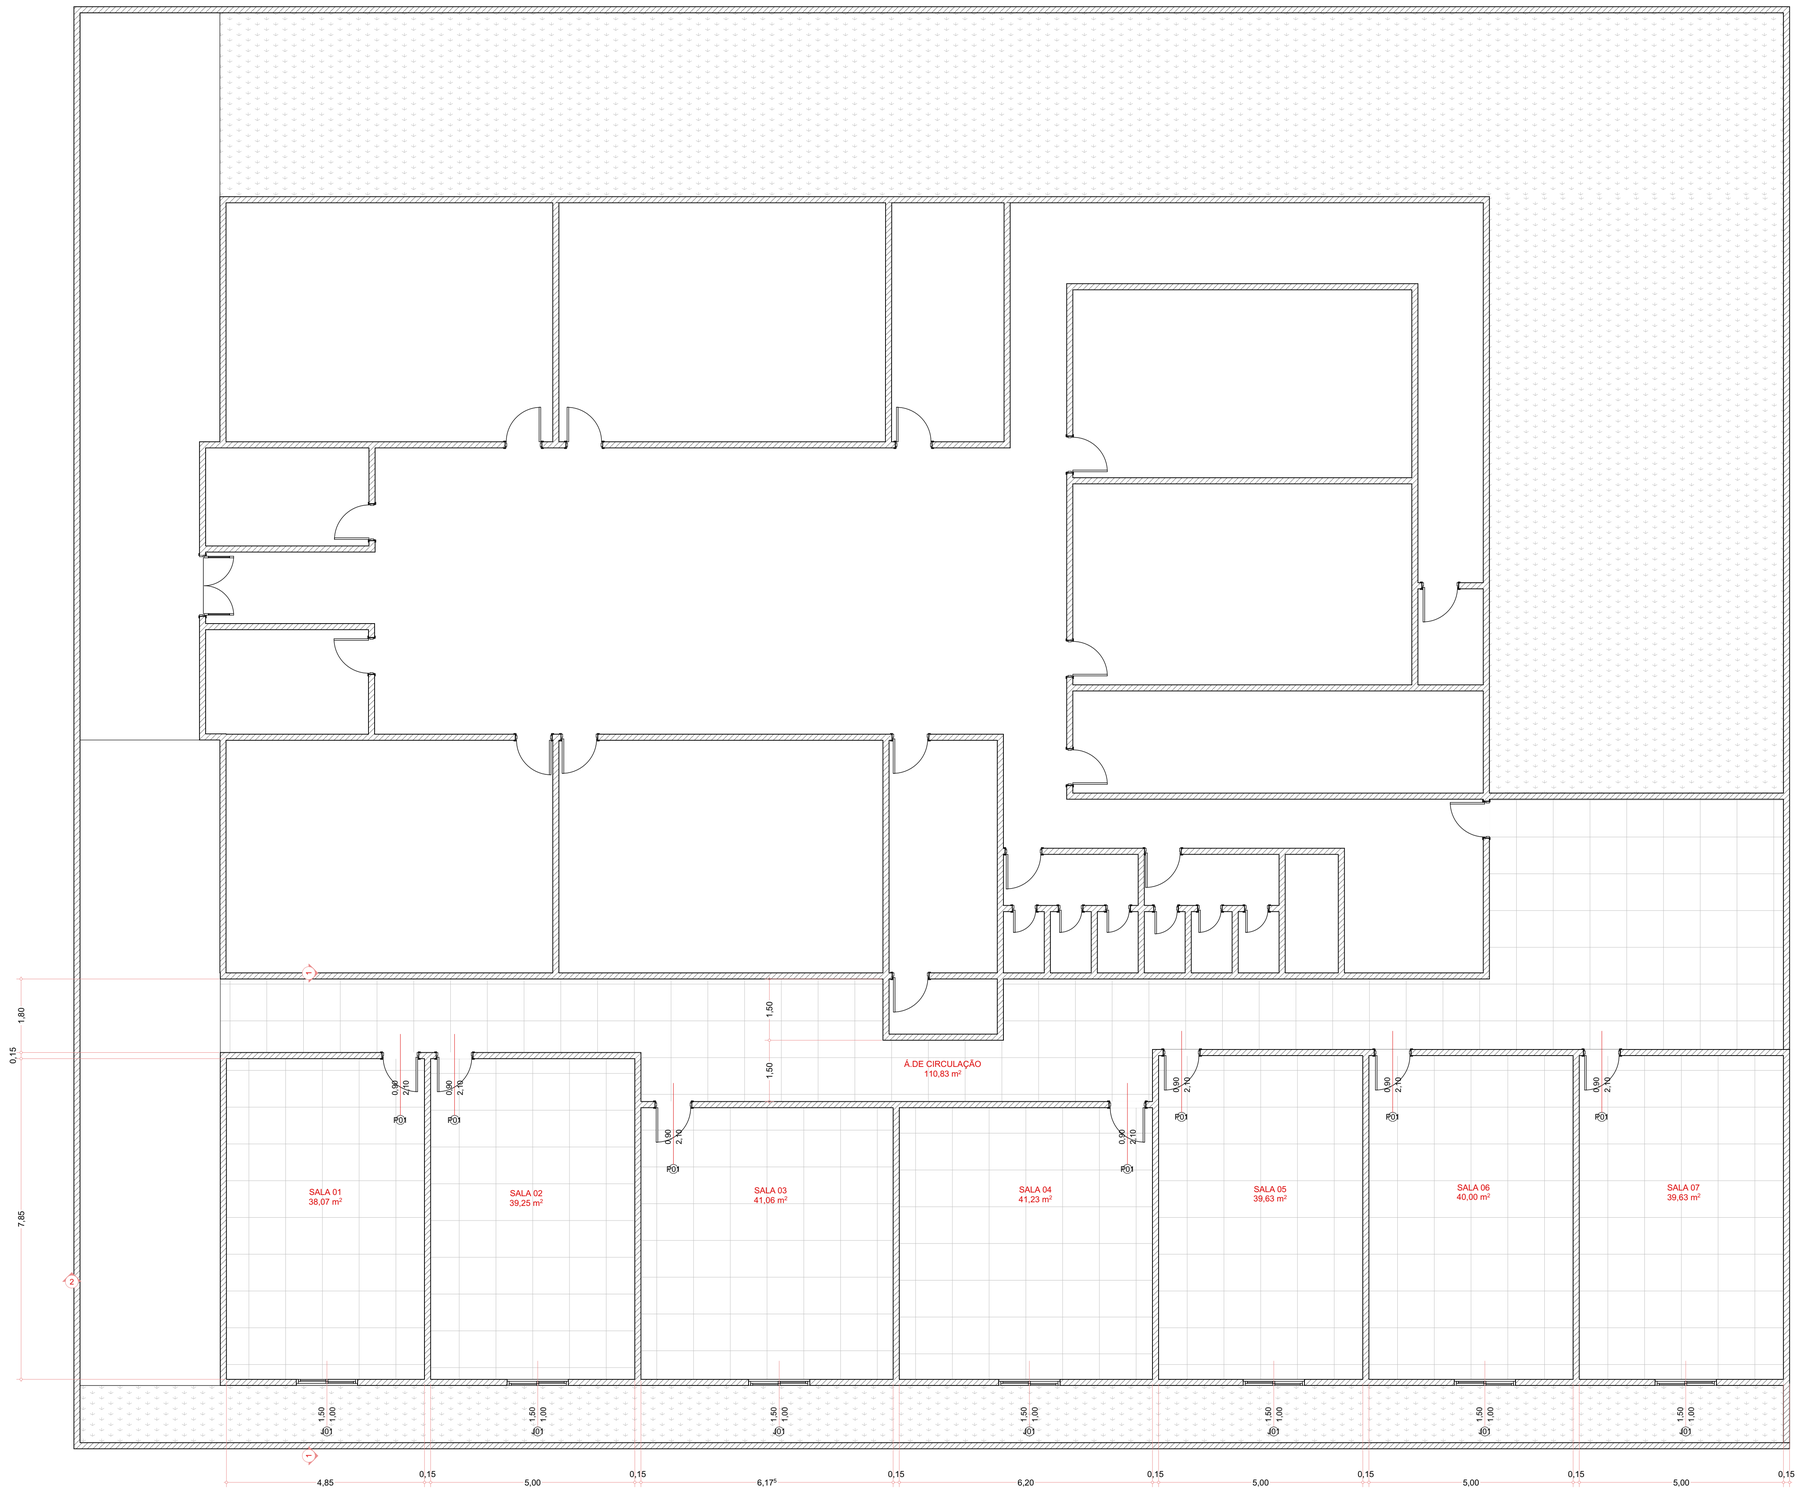


*MEM | PL - ZONAS NORMATIVAS

| AMB. | CATEGORIA | Á PERM | Á. TÉRREO | Á. TERRENO |
|---|---|---|---|---|
| 0 | | | | |
| Á.DE CIRCULAÇÃO | OUTRO | 110,83 | 110,83 | --- |
| SALA 01 | OUTRO | 38,07 | 38,07 | --- |
| SALA 02 | OUTRO | 39,25 | 39,25 | --- |
| SALA 03 | OUTRO | 41,06 | 41,06 | --- |
| SALA 04 | OUTRO | 41,23 | 41,23 | --- |
| SALA 05 | OUTRO | 39,63 | 39,63 | --- |
| SALA 06 | OUTRO | 40,00 | 40,00 | --- |
| SALA 07 | OUTRO | 39,63 | 39,63 | --- |

*LEG | PORTA - JANELA

| ID | ABERTURA | MATERIAL | Q. |
|---|---|---|---|
| JANELA | | | |
| J01 | - | MADEIRA | 7 |
| PORTA | | | |
| P01 | ABRIR | MADEIRA | 7 |
| | | | 14 |

PROJETO

# PROJETO FLORIDO

ENDEREÇO
R.Maria do Socorro da Silva-DNOCS COREMAS PARAIBA BRASIL

CIDADE
COREMAS

ESTADO
PARAIBA

CLIENTE
PREFEITURA DE COREMAS

ARQUITETO
MAURICIO ANDERSON
CAU-00A2491800

FASE PROJETO
Planta baixa

ESCALA
1:75, 1:1

DIMENSÃO DA FOLHA
A1

CONTEÚDO

## P. TEC. | PLANTA BAIXA


DATA
22/07/2026

FOLHA
01

ARQUIVO DIGITAL
projeo florido nitão.pln


REVISÃO

| REV. | DESCRIÇÃO | MODIFICADO POR | DATA |
|---|---|---|---|
| | | | |
| | | | |
| | | | |
| | | | |
| | | | |

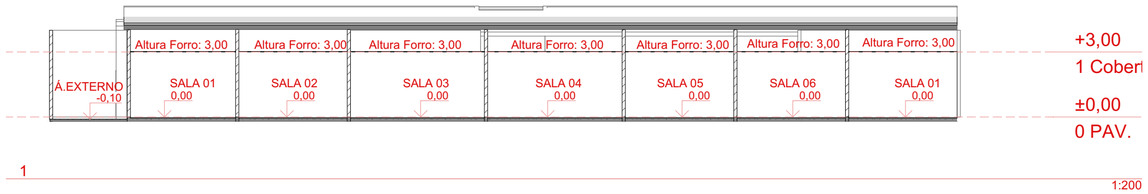


1

1:200

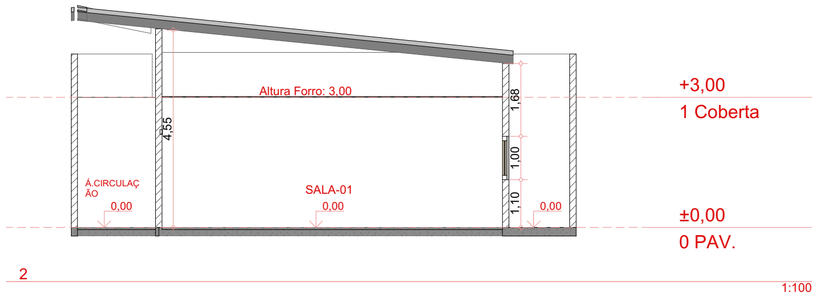


2

1:100

PROJETO

# PROJETO FLORIDO

ENDEREÇO

R.Maria do Socorro da Silva-DNOCS COREMAS PARAIBA BRASIL

CIDADE
COREMAS

ESTADO
PARAIBA

CLIENTE

PREFEITURA DE COREMAS

ARQUITETO

MAURICIO ANDERSON
CAU-00A2491800

FASE PROJETO
Planta baixa

ESCALA
1:100, 1:200

DIMENSÃO DA FOLHA
A1

CONTEÚDO

## Leiaute


DATA
22/07/2026

FOLHA
02

ARQUIVO DIGITAL
projeo florido nitão.pln

REVISÃO

| REV. | DESCRIÇÃO | MODIFICADO POR | DATA |
|---|---|---|---|
| | | | |
| | | | |
| | | | |
| | | | |
| | | | |

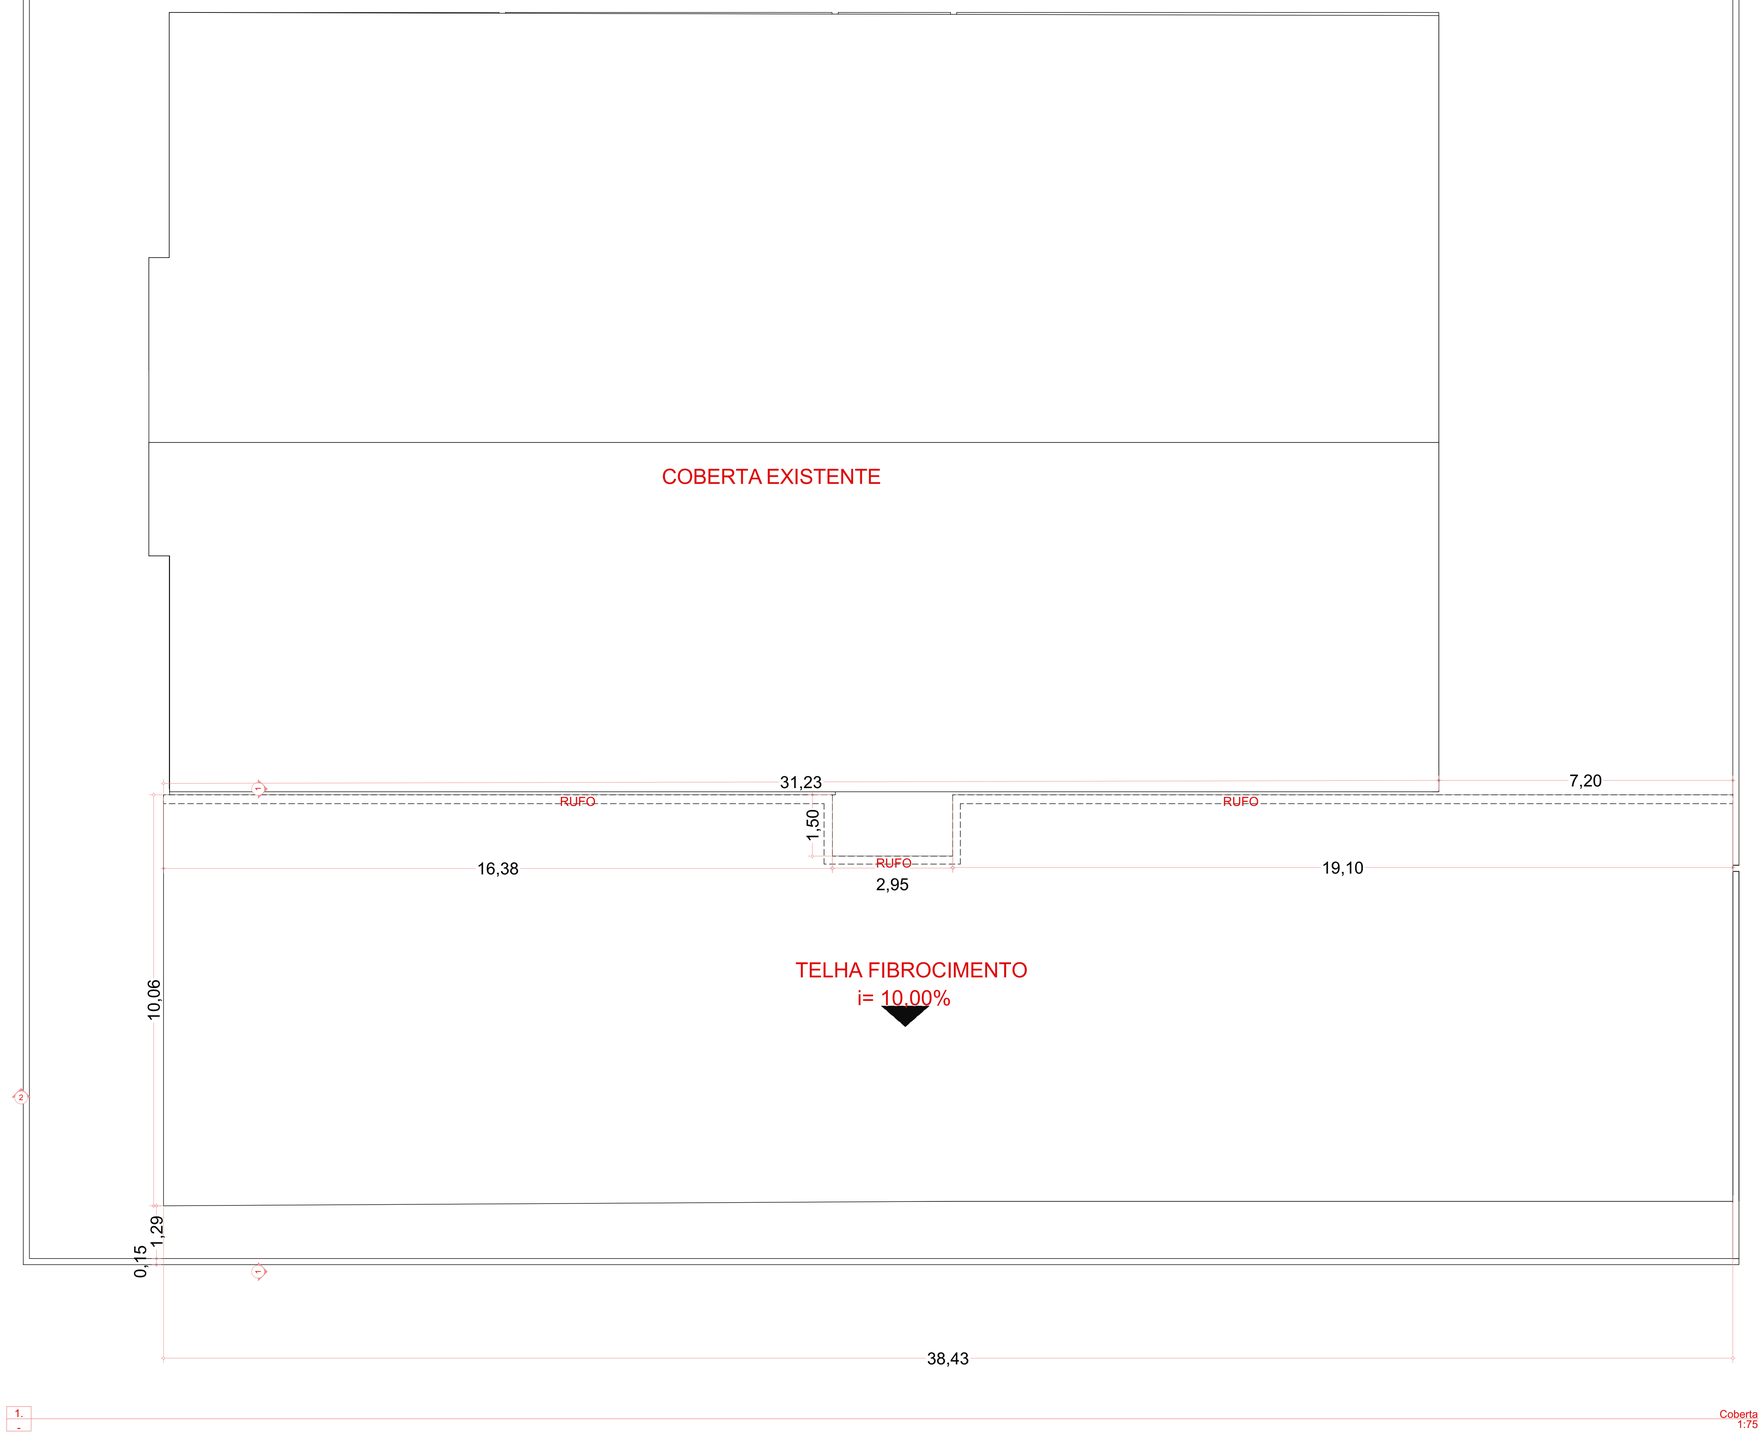


PROJETO

# PROJETO FLORIDO

ENDEREÇO
R.Maria do Socorro da Silva-DNOCS COREMAS PARAIBA BRASIL

CIDADE
COREMAS

ESTADO
PARAIBA

CLIENTE
PREFEITURA DE COREMAS

ARQUITETO
MAURICIO ANDERSON
CAU-00A2491800

FASE PROJETO
Planta baixa

ESCALA
1:75

DIMENSÃO DA FOLHA
A1

CONTEÚDO

## COBERTA


DATA
22/07/2026

FOLHA
03

ARQUIVO DIGITAL
projeo florido nitão.pln

REVISÃO

| REV. | DESCRIÇÃO | MODIFICADO POR | DATA |
|---|---|---|---|
| | | | |
| | | | |
| | | | |
| | | | |
| | | | |

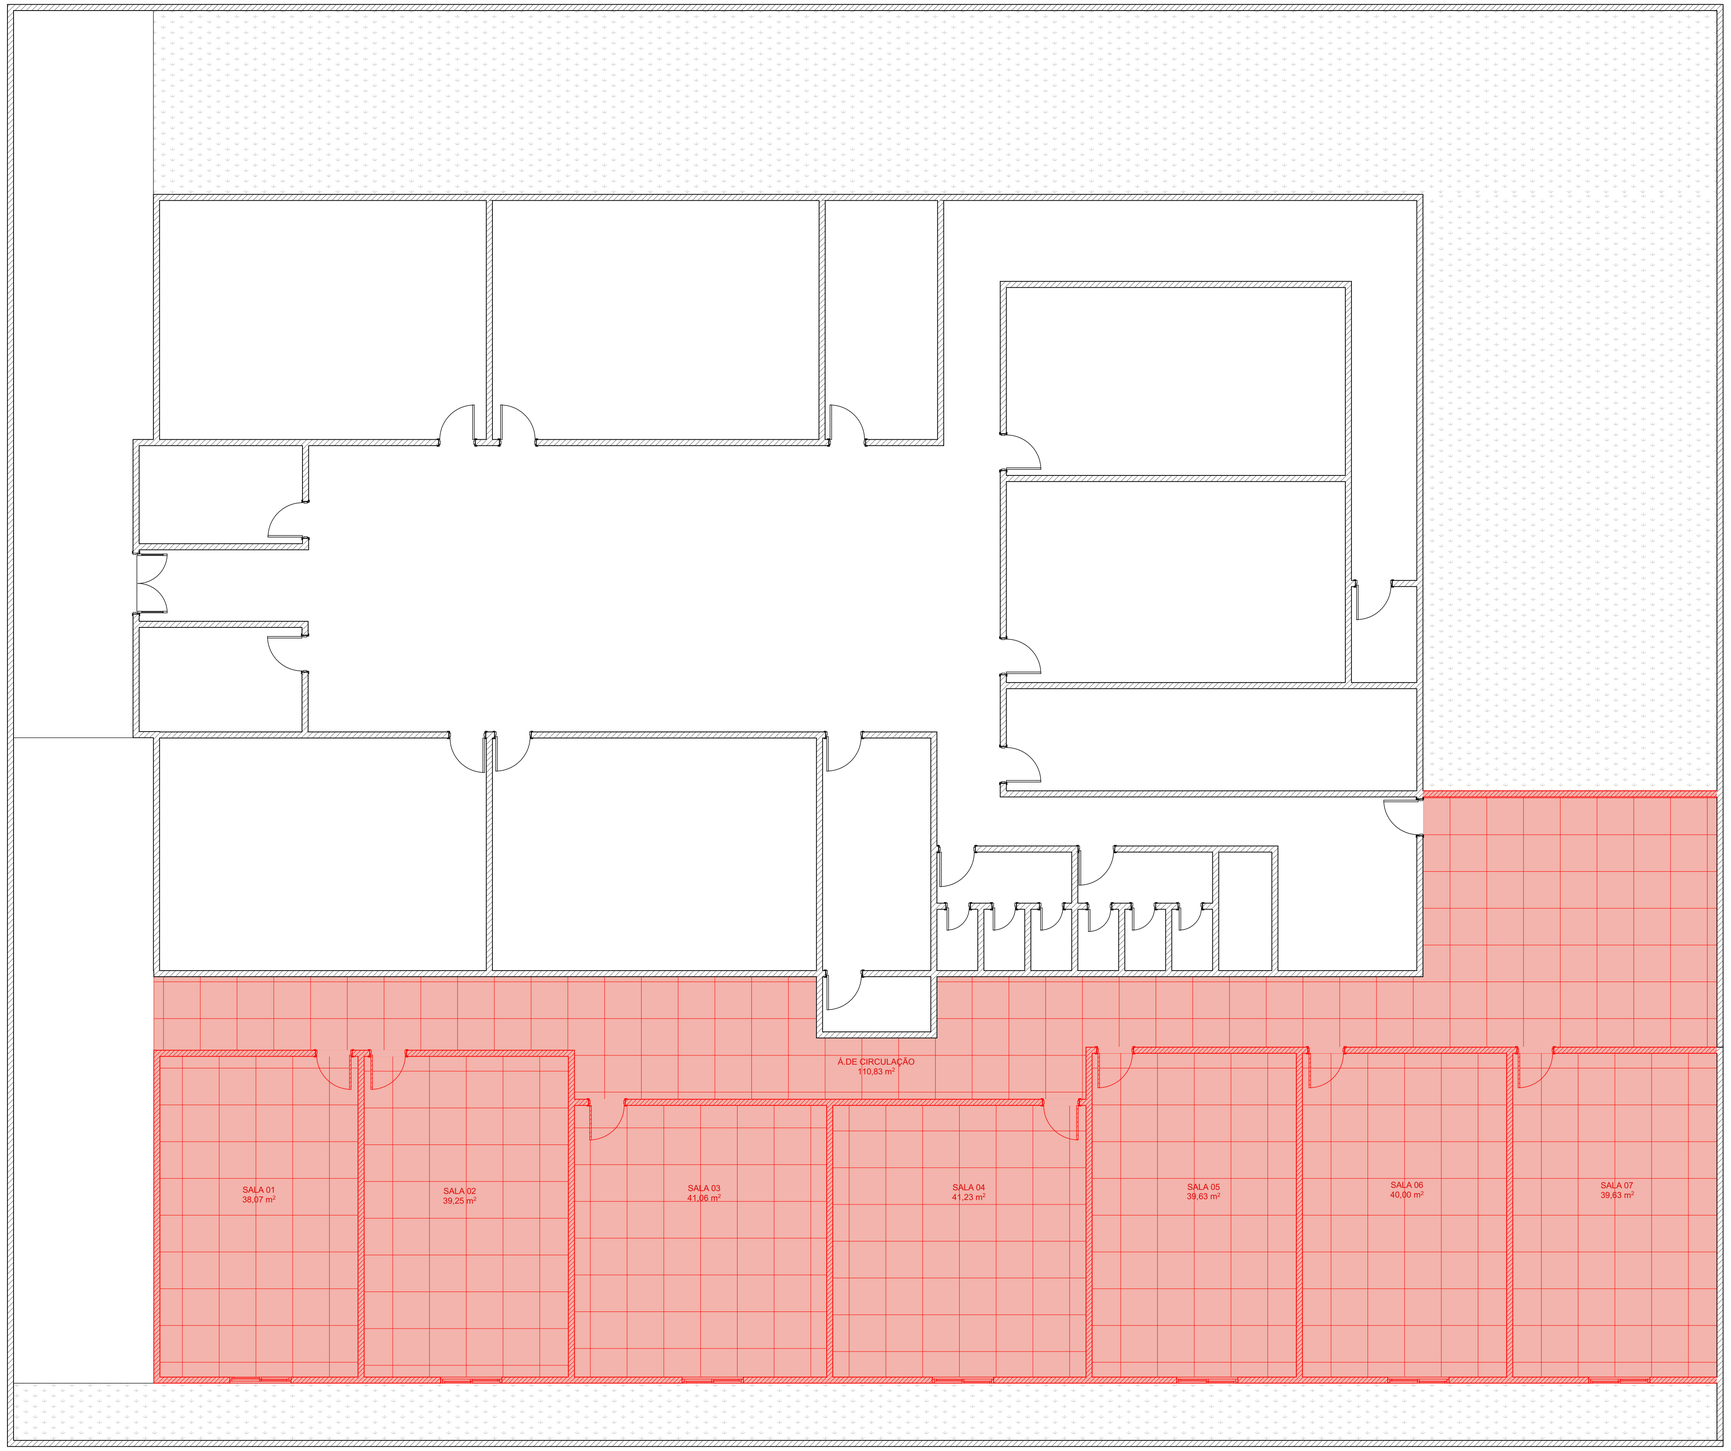


02

DEMOLIR E CONSTRUIR
1:75

N

| *LEG \| DC - PAREDE | |
|---|---|
| | ÁREA (M²) |
| Existente | 1.499,04 |
| A Construir | 492,81 |
| | 1.991,85 m² |

PROJETO

# PROJETO FLORIDO

ENDEREÇO
R.Maria do Socorro da Silva-DNOCS COREMAS PARAIBA BRASIL

CIDADE
COREMAS

ESTADO
PARAIBA

CLIENTE
PREFEITURA DE COREMAS

ARQUITETO
MAURICIO ANDERSON
CAU-00A2491800

FASE PROJETO
Planta baixa

ESCALA
1:75, 1:1

DIMENSÃO DA FOLHA
A1

CONTEÚDO
Leiaute


DATA
22/07/2026

FOLHA
01

ARQUIVO DIGITAL
projeo florido nitão.pln

REVISÃO

| REV. | DESCRIÇÃO | MODIFICADO POR | DATA |
|---|---|---|---|
| | | | |
| | | | |
| | | | |
| | | | |
| | | | |

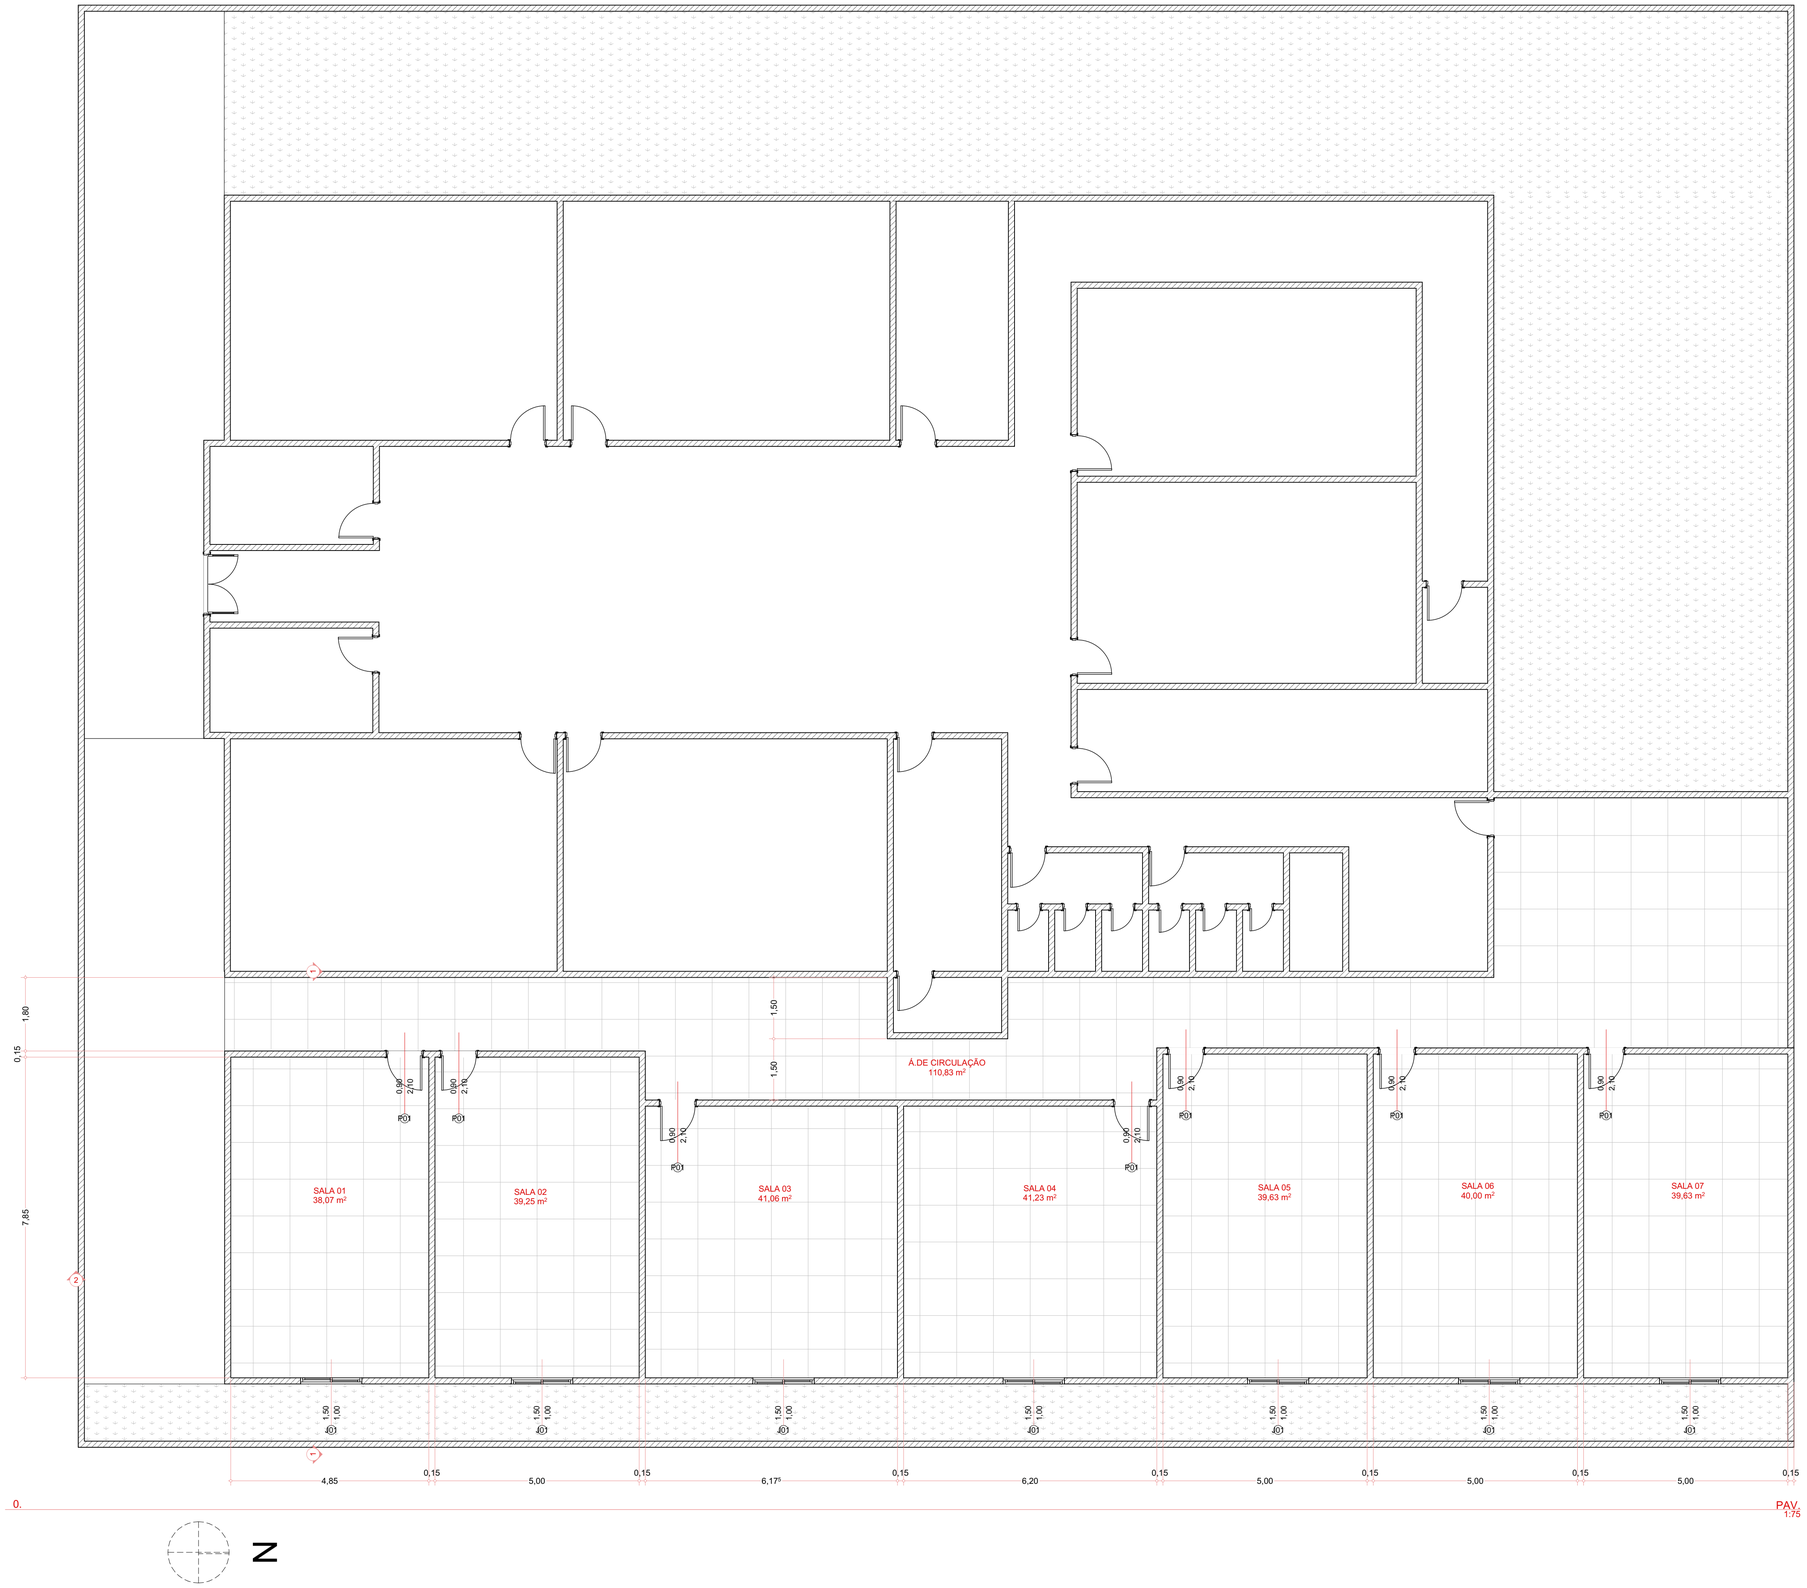


PROJETO

# PROJETO FLORIDO

ENDEREÇO
R.Maria do Socorro da Silva-DNOCS COREMAS PARAIBA BRASIL

CIDADE
COREMAS

ESTADO
PARAIBA

CLIENTE
PREFEITURA DE COREMAS

ARQUITETO
MAURICIO ANDERSON
CAU-00A2491800

FASE PROJETO
Planta baixa

ESCALA
1:75

DIMENSÃO DA FOLHA
A1

CONTEÚDO

## Leiaute

DATA
22/07/2026

FOLHA
02

ARQUIVO DIGITAL
projeo florido nitão.pln

REVISÃO