

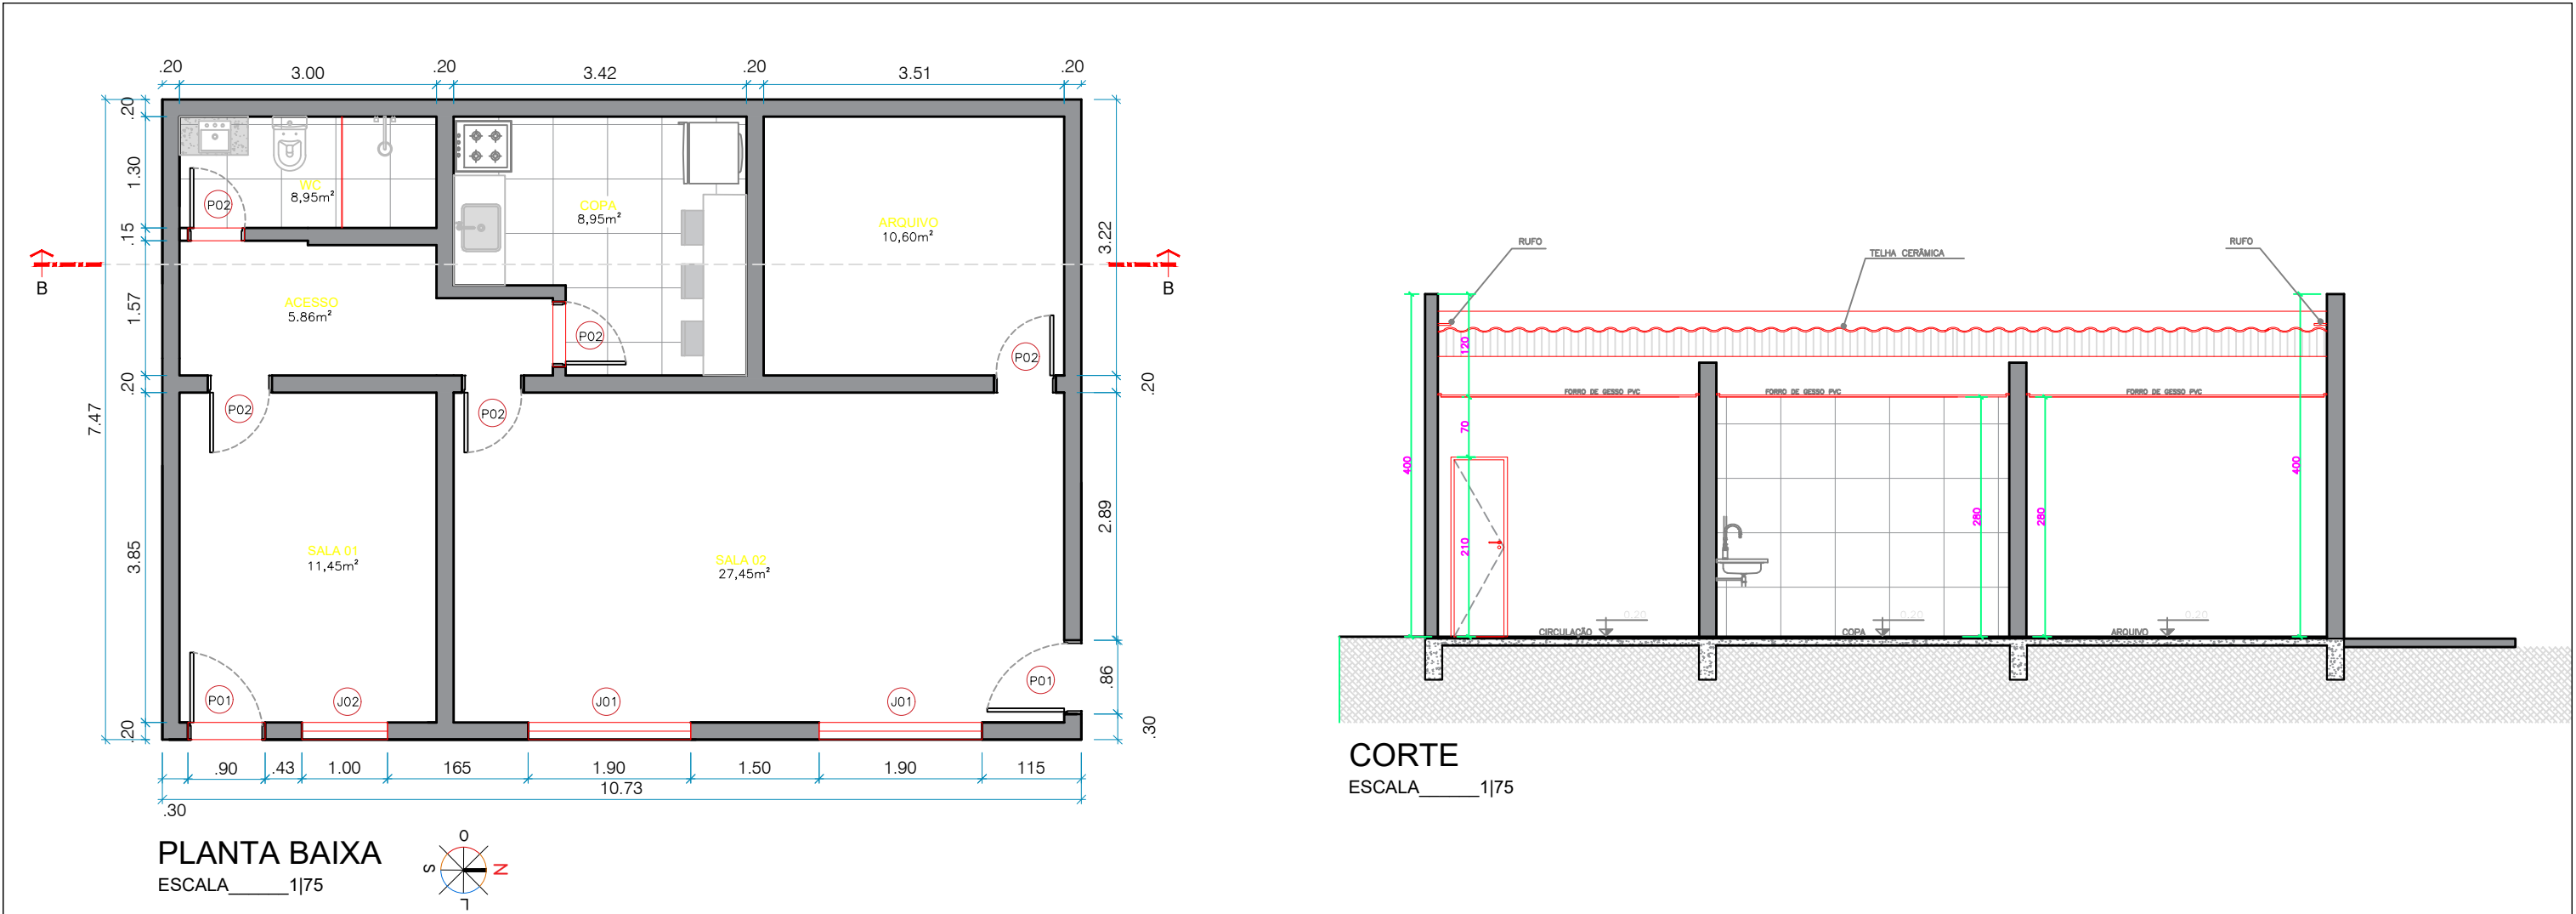


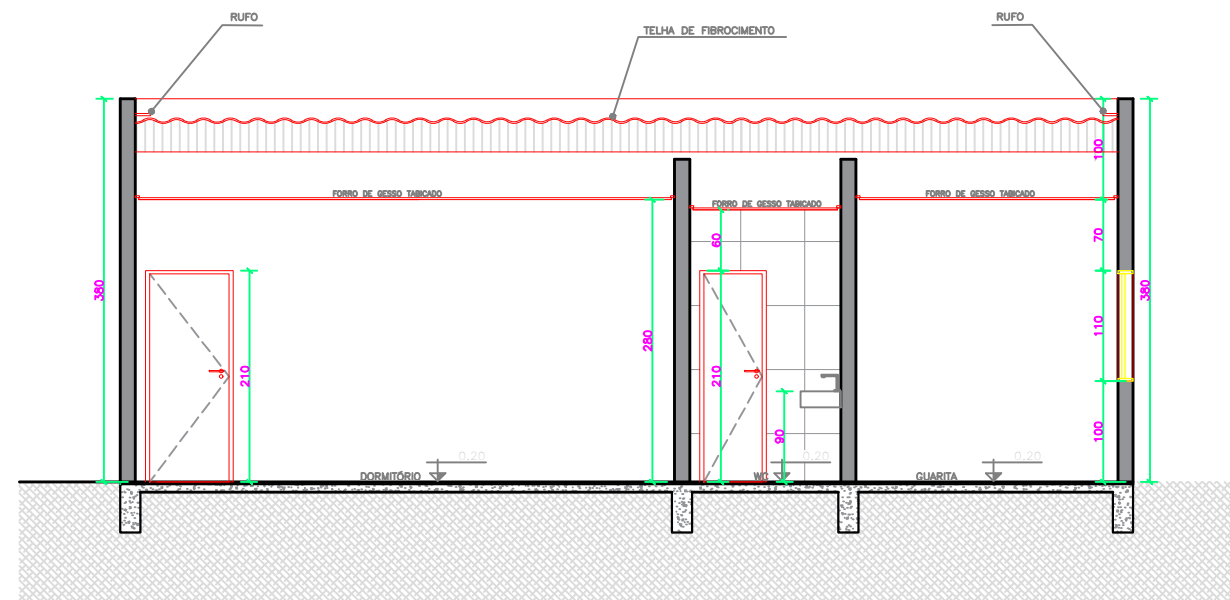

ACABAMENTOS - ESCRITÓRIO			
REVESTIMENTO	Especificação	LOCAL	ÁREA
Cemâmico	Piso Cerâmico Marmorizado Brilhante Borda Reta Interno 54x54cm Phanteon Lef	PISO GERAL	73,03m²
	Cobertura de parede 280cm com Cerâmico Marmorizado Brilhante Borda Reta Interno 54x54cm Phanteon Lef	COPA, WC	60,15m²
Pintura	Parede pintada e emassada com tinta para ambientes externos com acabamento fosco na cor branca	FACHADA NORTE, LESTE E SUL	105m²
	Parede pintada e emassada com Tinta Látex Coralar + Econômico Sem Cheiro 18 L Branco Gelo	ACESSO, SALA 01, 02 E ARQUIVO	135m²
	Fechamento com forro em reguas de pvc, frisado para ambientes comerciais	GESSO GERAL	73,03m²

ACABAMENTOS - ESCRITÓRIO			
ESQUADRIA	Especificação	LOCAL	QTE
PORTA	Porta de Madeira Lisa Nevada MGM 210cmx90cm Melamínico Mogno	SALA 01 E SALA 02	02
	Porta de Madeira Lisa Nevada MGM 210cmx70cm Melamínico Mogno	SALA 02, ARQUIVO COPA E WC	05
JANELA	Restauração das janelas existentes 190x110cm e 100x110cm com lixamento e nova pintura na cor cinza sem brilho	SALA 01 E 02	03

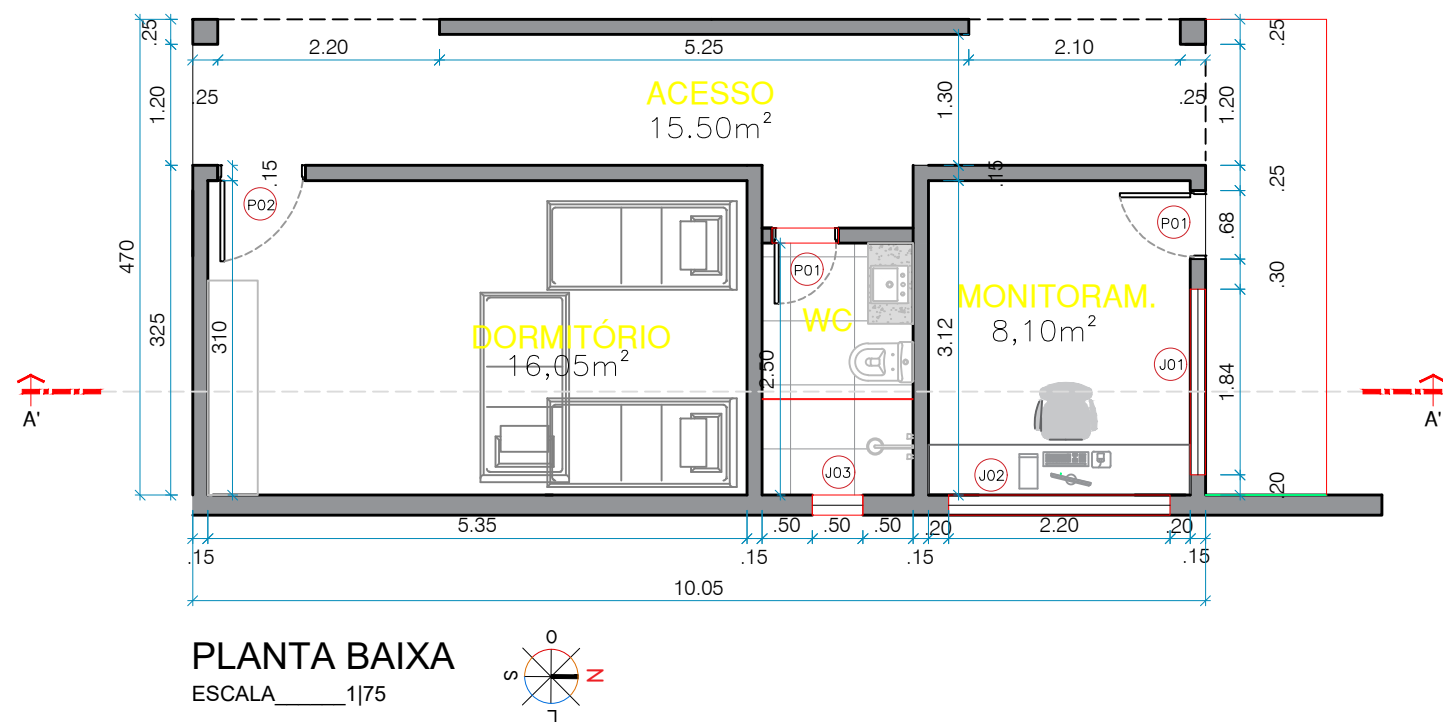

ACABAMENTOS - GUARITA			
REVESTIMENTO	Especificação	LOCAL	ÁREA
Cemâmico	Piso Cerâmico Marmorizado Brilhante Borda Reta Interno 54x54cm Phanteon Lef	PISO GERAL	47.44m²
	Cobertura de parede 280cm com Cerâmico Marmorizado Brilhante Borda Reta Interno 54x54cm Phanteon Lef	BANHEIRO	23m²
Pintura	Parede pintada e emassada com tinta para ambientes externos com acabamento fosco na cor branca	FACHADA NORTE, SUL E OESTE	115m²
	Parede pintada e emassada com Tinta Látex Coralar + Econômico Sem Cheiro 18 L Branco Gelo	ACESSO, SALA 01, 02 E ARQUIVO	112m²
	Fechamento com forro em reguas de pvc, frisado para ambientes comerciais	GESSO GERAL	46m²

ACABAMENTOS - GUARITA			
ESQUADRIA	Especificação	LOCAL	QTE
PORTA	Porta de Madeira Lisa Nevada MGM 210cmx70cm Melamínico Mogno	MONITORAMENTO BANHEIRO	02
	Porta de Madeira Lisa Nevada MGM 210cmx70cm Melamínico Mogno	DORMITÓRIO	01
JANELA	J01 - Janela de aluminio com vidro 185 x 110cm J02 - Janela de aluminio com vidro fumê 220 x 110cm J03 - Janela basculante horizontal de vidro 50 x 40cm	SALA 01 E 02 BANHEIRO	03



WC 8,95m²

ACESSO 5,86m²

COPA 8,95m²

ARQUIVO 10,60m²

SALA 01 11,45m²


SALA 02 27,45m²

PLANTA BAIXA


PONTOS ELETRICOS _____ 1/75




 PREFEITURA DE COREMAS TRABALHO E RESPEITO PELA DIGNIDADE	Projeto: Projeto Arquitetônico - Detalhe guarita		Arquiteta: Cayo Nogueira CAU nº A17524-6	
	Proprietário: Prefeitura Municipal de Coremas PB		Escala: indicada	Prancha: 03/04
				Data: MAI/2025

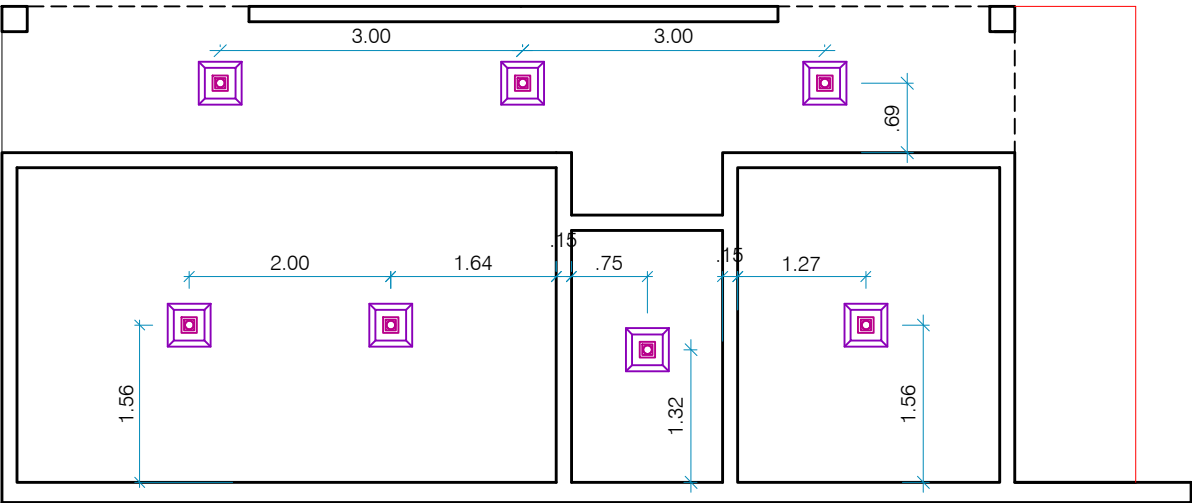


PLANTA BAIXA
PONTOS LUMINICOS _____ 1/75

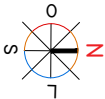

PONTOS LUMINICOS			
SIMBOLO	ESPECIFICAÇÃO	UNI	LOCAL
	Plafon quadrado sobrepor 40x40 30w branco frio	07	MONITORAMENTO, DORMITORIO E WC
	Conjunto 4x2 com 1 Interruptor Simples Liz 10 A 250 V Branco	03	SALA 01, 02, ARQUIVO, COPA, BANHEIRO
	Tomada Dupla 4x2 10A Branca Habitat Fame MÉDIA= 1,20m	02	MONITORAMENTO, DORMITORIO
	Tomada Dupla 4x2 10A Branca Habitat Fame BAIXA=0,50m	05	MONITORAMENTO, DORMITORIO

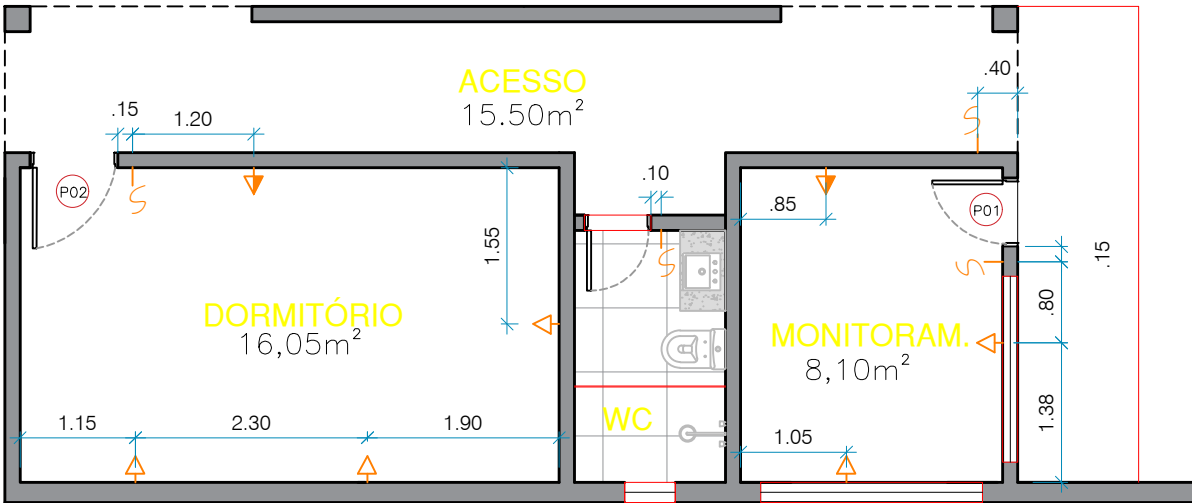

PLANTA BAIXA
PONTOS ELÉTRICOS _____ 1/75

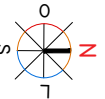

* Conferir medidas no local




PLANTA DE COBERTA

1:200

versão	data	alterações efetuadas
original		projeto original
CARIMBO PROTOCOLO GERAL		VERSÃO V02
CARIMBO SECRETARIO	CARIMBO DIRETORIA	CARIMBO FISCAL
CARIMBO APROVAÇÃO	CARIMBO DIVERSOS	
ASSINATURAS		
PROPRIETÁRIO	ARQUITETO	RT
PREFEITURA DE COREMAS TRABALHANDO E RESPEITANDO O MEIO AMBIENTE 01 02 INDICADA INDICADA INDICADA INDICADA PROJETO DE REFORMA - GARAGEM MUNICIPAL 03-2025 MAIO 2025 COREMAS-PB CAYO NOGUEIRA KIRYA CRISTINNE CARIMBO ATENÇÃO		



PLANTA BAIXA
GARAGEM MUNICIPAL ESC: 1/150

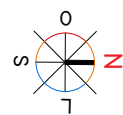

versão	data	alterações efetuadas
original		projeto original


CARIMBO PROTOCOLO GERAL		CARIMBO PREFEITURA	VERSÃO V02

CARIMBO SECRETARIO	CARIMBO DIRETORIA	CARIMBO FISCAL

CARIMBO APROVAÇÃO	CARIMBO COORDENADOR

ASSINATURAS			
PROPRIETÁRIO	ARQUITETO	RT	


	DESCRIÇÃO	PROJETO DE REFORMA - GARAGEM MUNICIPAL		
	RAÃO SOCIAL			
	CPF			
	ESTADO	EXECUTIVO	DATA	03-2025
	ENDEREÇO		CIDADE	COREMAS-PB
PROPRIETÁRIO	CAYO NOGUEIRA KIRYA CRISTINE	FONE		
AUTOR	PLANTA BAIXA	CAI	CARIMBO ATIVIDADE	
PROPOSTA				
02				
02				
ESCALA	INDICADA	REVISÃO	REVISÃO	

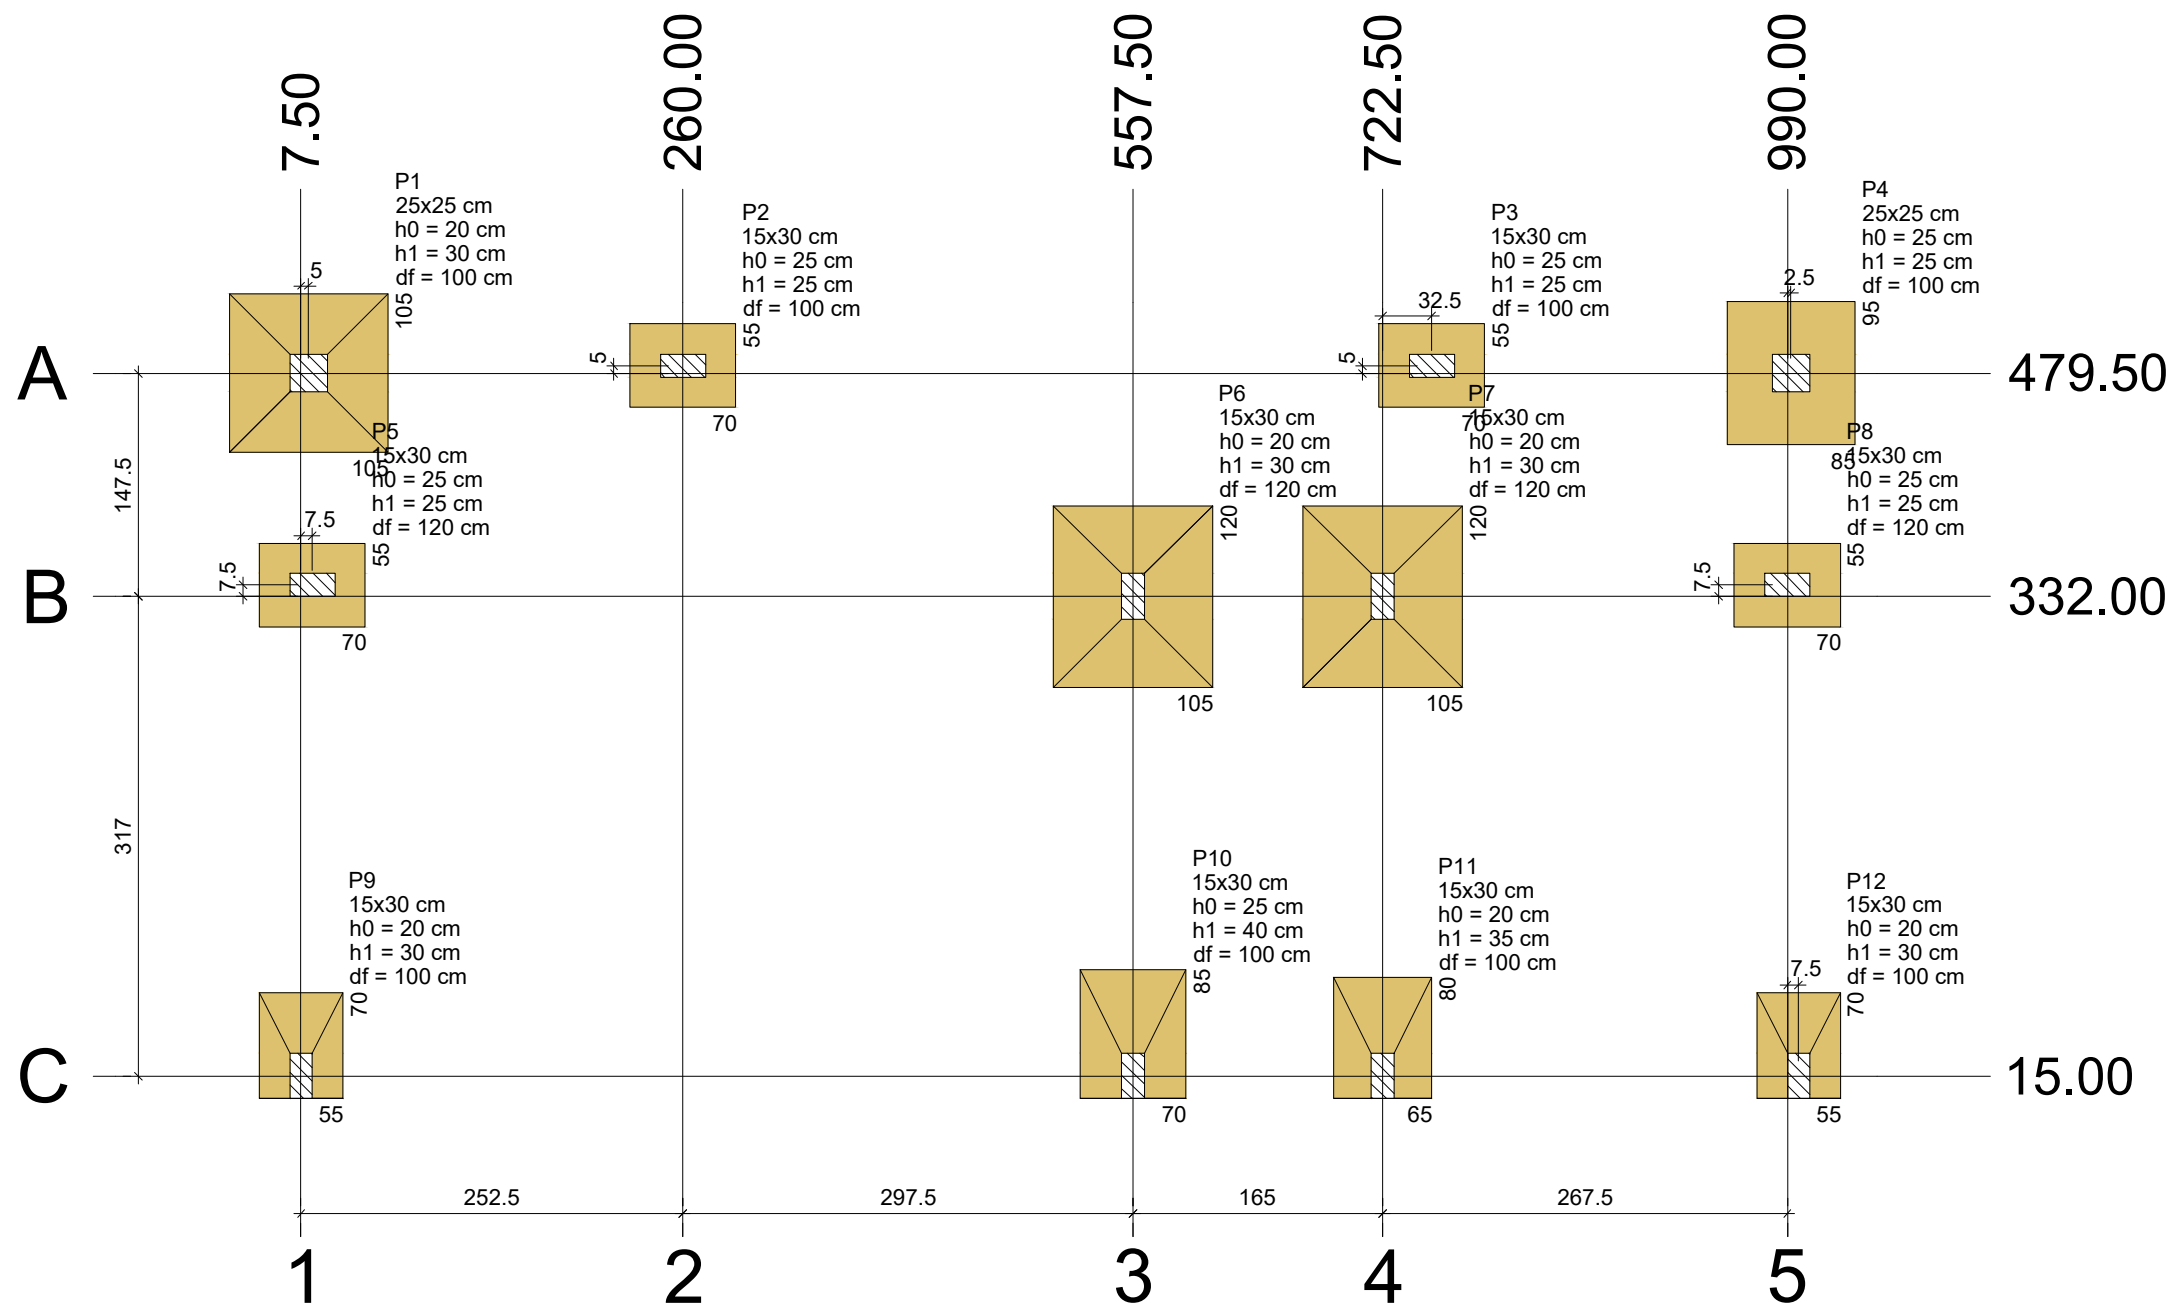

Planta de localização
escala 1:50

Pilar													
Nome	Seção (cm)	X (cm)	Y (cm)	Carga Máx. (tf)	Carga Mín. (tf)	Mx Máximo (kgf.m)		My Máximo (kgf.m)		Fx Máximo (tf)		Fy Máximo (tf)	
						Positivo	Negativo	Positivo	Negativo	Positivo	Negativo	Positivo	Negativo
P1	25x25	12.50	479.50	3.3	1.7	700	-400	100	-200	0.0	-0.3	0.4	-0.5
P2	15x30	260.00	484.50	3.0	2.7	200	-300	300	-200	0.4	0.0	0.1	-0.2
P3	15x30	755.00	484.50	3.0	2.6	200	-300	100	-200	0.0	-0.4	0.1	-0.2
P4	25x25	992.50	479.50	3.3	1.7	600	-700	300	-200	0.3	0.0	0.5	-0.4
P6	15x30	557.50	332.00	4.9	2.9	1300	-300	100	-200	0.0	-0.3	0.0	-1.3
P7	15x30	722.50	332.00	4.5	2.6	1200	-300	200	0	0.2	0.0	0.2	-1.0
P8	15x30	990.00	339.50	2.7	1.4	300	-300	200	-300	0.1	-0.1	0.3	-0.3
P9	15x30	7.50	15.00	2.7	2.3	0	-400	0	0	0.0	-0.1	0.4	0.0
P10	15x30	557.50	15.00	5.6	3.6	0	-1000	0	0	0.2	0.0	1.0	0.0
P11	15x30	722.50	15.00	4.7	2.7	0	-800	0	0	0.1	-0.1	0.8	0.0
P12	15x30	997.50	15.00	2.3	1.8	0	0	0	0	0.1	0.0	0.2	-0.3
P5	15x30	15.00	339.50	2.8	1.6	300	-100	200	-300	0.2	-0.2	0.2	-0.5


Os esforços indicados nesta tabela são os valores máximos obtidos pela envoltória de todas as combinações definidas para as fundações. Para análises complementares, deve-se consultar o relatório de esforços na fundação, que apresenta os valores calculados para cada combinação.

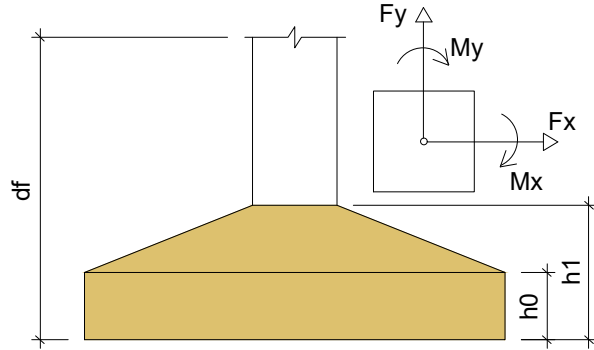

Fundação				
Lado B (cm)	Lado H (cm)	h0 / ha (cm)	h1 / hb (cm)	df (cm)
105	105	20	30	100
55	70	25	25	100
55	70	25	25	100
95	85	25	25	100
105	120	20	30	120
105	120	20	30	120
55	70	25	25	120
70	55	20	30	100
85	70	25	40	100
80	65	20	35	100
70	55	20	30	100
55	70	25	25	120

Locação no eixo X	
Coordenadas (cm)	Nome
7.50	P9
12.50	P1
15.00	P5
260.00	P2
557.50	P6, P10
722.50	P7, P11
755.00	P3
990.00	P8
992.50	P4
997.50	P12

Locação no eixo Y	
Coordenadas (cm)	Nome
484.50	P2, P3
479.50	P1, P4
339.50	P5, P8
332.00	P6, P7
15.00	P9, P10, P11, P12

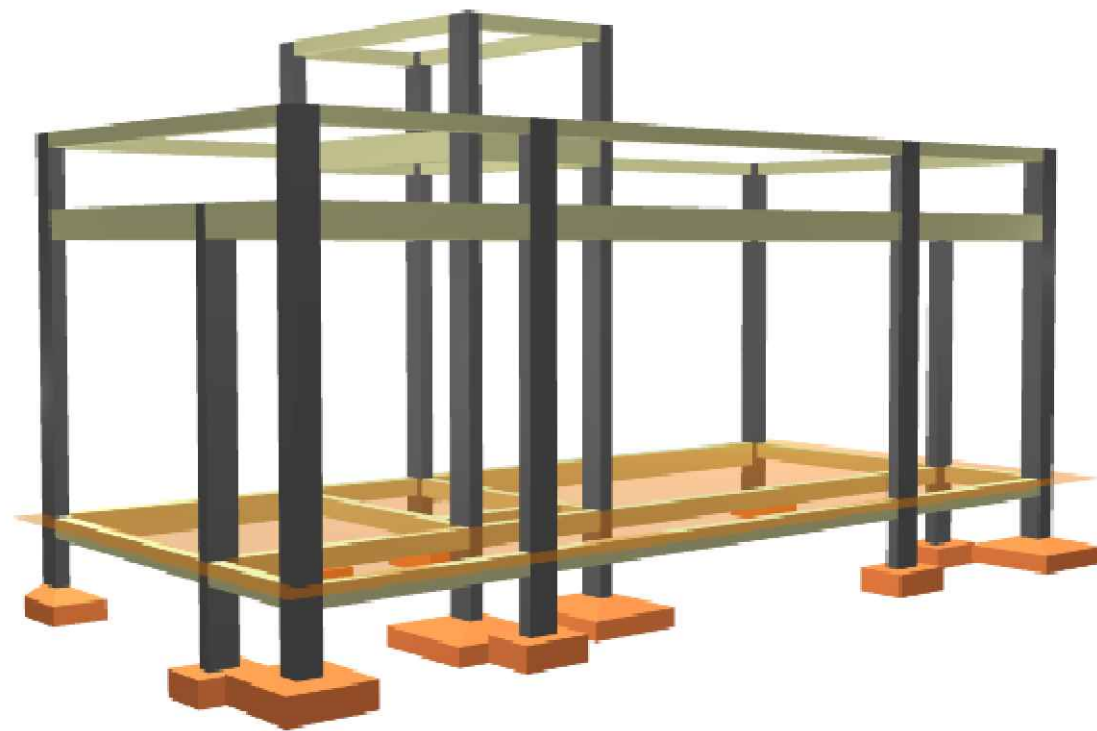


PROPRIETÁRIO: PREFEITURA MUNICIPAL DE COREMAS- PB

LINCOLN CARTAXO DE LIRA JÚNIOR:06897861405
Assinado de forma digital por LINCOLN CARTAXO DE LIRA JÚNIOR:06897861405
Dados: 2025.07.14 11:26:54 -03'00'

PROJETO: LINCOLN CARTAXO DE LIRA JÚNIOR CREA 160.814.689-8

FOLHA	PROJETO: GARAGEM COREMAS (ESTRUTURAL ANEXO I)			
01/09	CONVENIENTE: PREFEITURA MUNICIPAL DE COREMAS-PB CONCIDENTE: PREFEITURA MUNICIPAL DE COREMAS-PB LOCALIDADE: COREMAS- PB			
DESENHO	DATA	RESPONSÁVEL	RUBRICA	DADOS
CÓPIA	JUN/2025	LINCOLN CARTAXO		
VISTO				
ESCALAS	DESENHOS			CONVÊNIO
INDICADO	- PLANTA DE LOCAÇÃO			ARQUIVO

Aprovações:

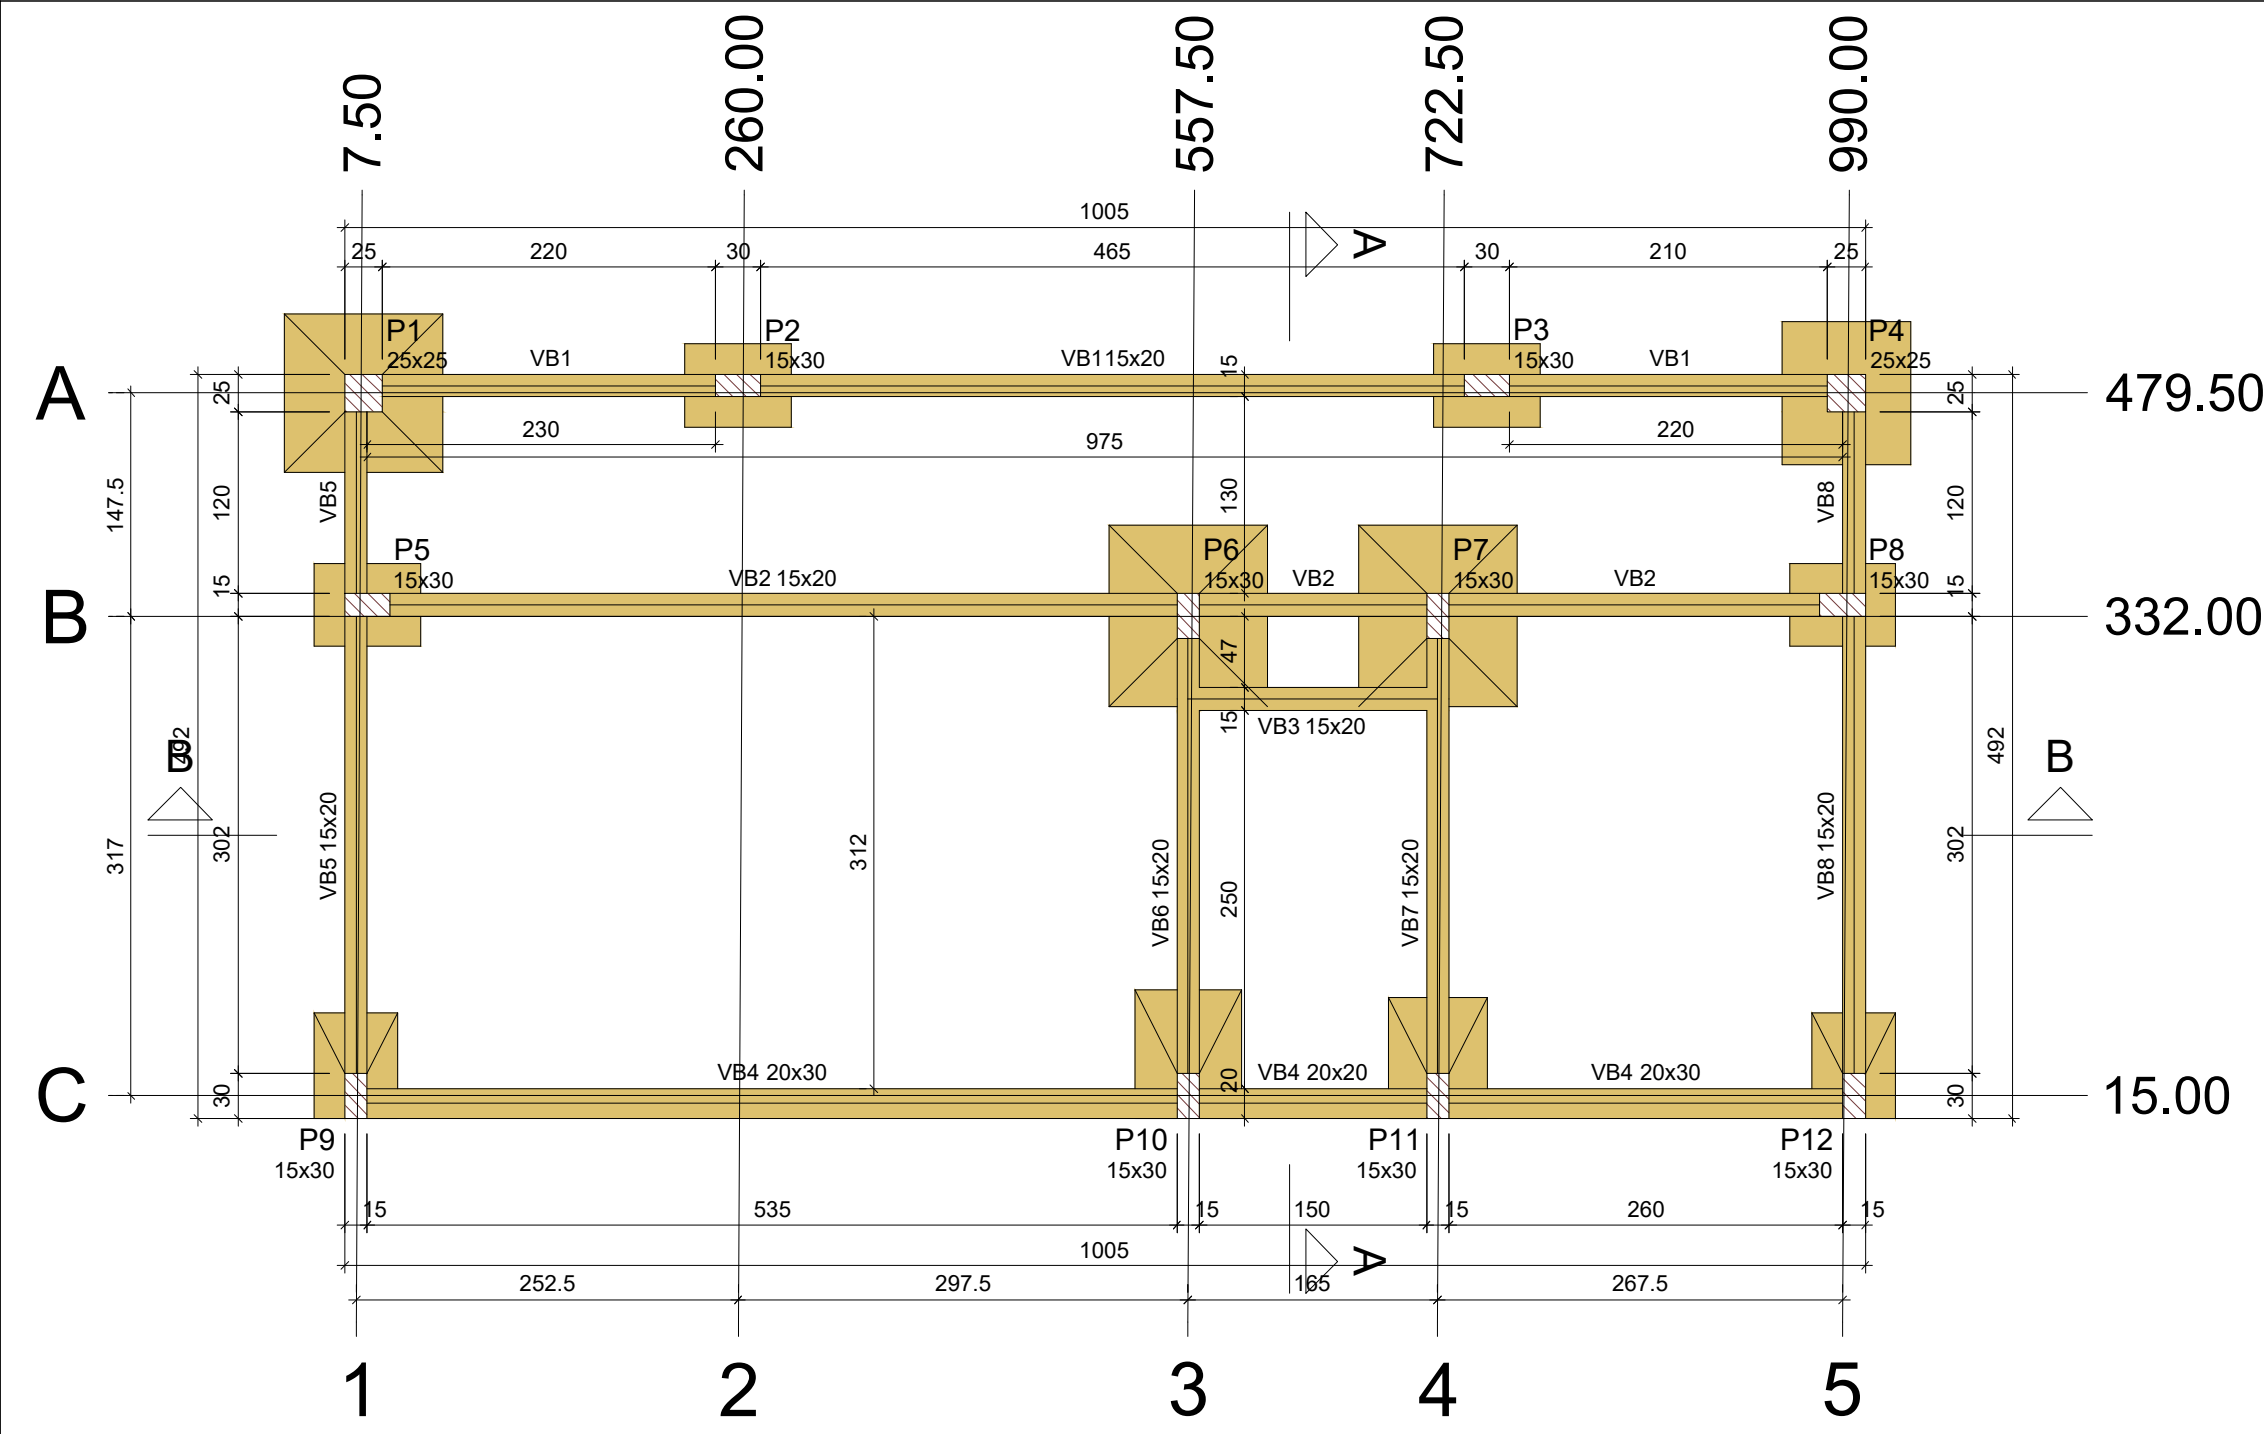

Forma do pavimento +0 (Nível 0)
escala 1:50


Vigas			
Nome	Seção (cm)	Elevação (cm)	Nível (cm)
VB1	15x20	0	0
VB2	15x20	0	0
VB3	15x20	0	0
VB4	20x30	0	0
	20x20	0	0
	20x30	0	0
VB5	15x20	0	0
VB6	15x20	0	0
VB7	15x20	0	0
VB8	15x20	0	0

Características dos materiais	
fck (kgf/cm²)	Ecs (kgf/cm²)
250	241500

Legenda dos pilares	
	Pilar que passa
	Pilar com mudança de seção

Legenda das vigas e paredes	
	Viga

Pilares			
Nome	Seção (cm)	Elevação (cm)	Nível (cm)
P1	25x25	0	0
P2	15x30	0	0
P3	15x30	0	0
P4	25x25	0	0
P6	15x30	0	0
P7	15x30	0	0
P8	15x30	0	0
P9	15x30	0	0
P10	15x30	0	0
P11	15x30	0	0
P12	15x30	0	0
P5	15x30	0	0

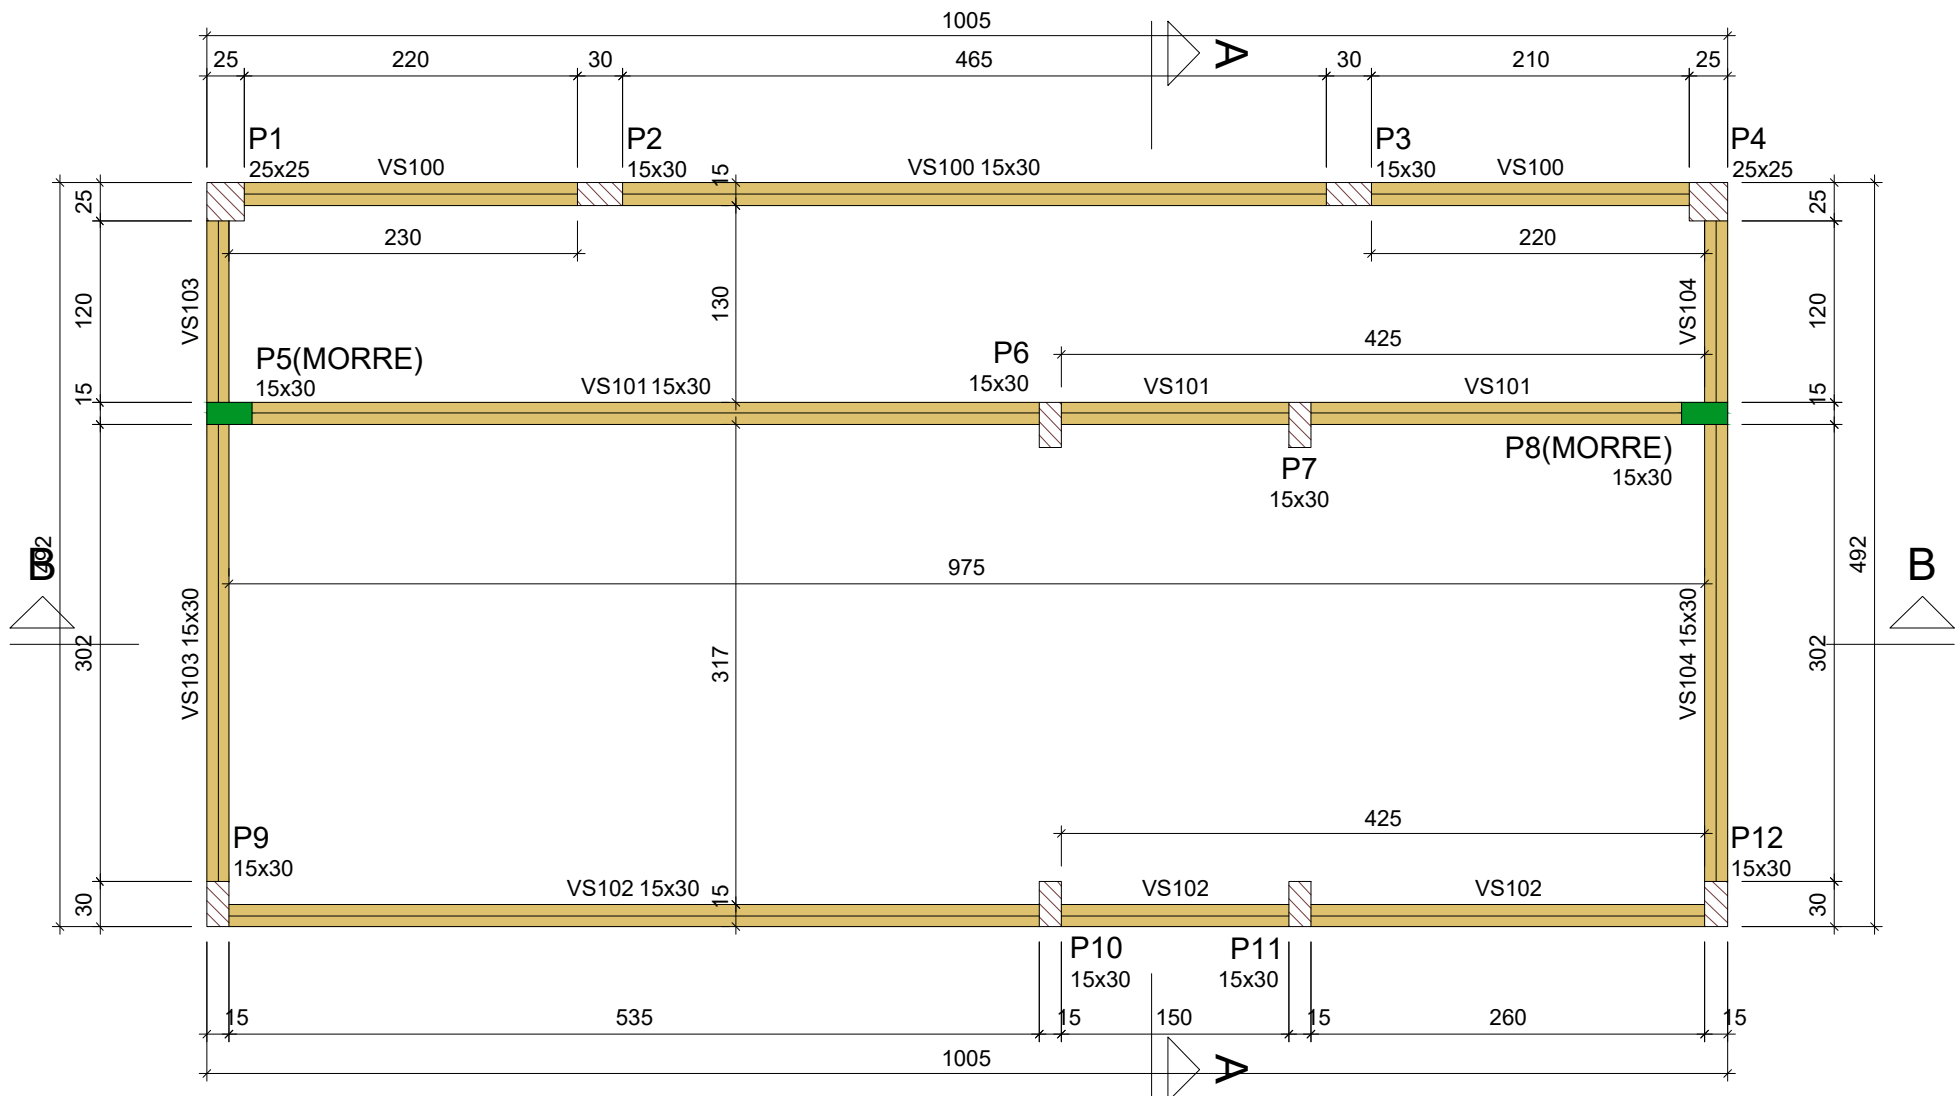

Forma do pavimento +305 (Nível 305)
escala 1:50


Vigas			
Nome	Seção (cm)	Elevação (cm)	Nível (cm)
VS100	15x30	0	305
VS101	15x30	0	305
VS102	15x30	0	305
VS103	15x30	0	305
VS104	15x30	0	305

Características dos materiais	
fck (kgf/cm²)	Ecs (kgf/cm²)
250	241500

Legenda das vigas e paredes	
	Viga

Legenda dos pilares	
	Pilar que morre
	Pilar que passa

Pilares			
Nome	Seção (cm)	Elevação (cm)	Nível (cm)
P1	25x25	0	305
P2	15x30	0	305
P3	15x30	0	305
P4	25x25	0	305
P6	15x30	0	305
P7	15x30	0	305
P8	15x30	0	305
P9	15x30	0	305
P10	15x30	0	305
P11	15x30	0	305
P12	15x30	0	305
P5	15x30	0	305

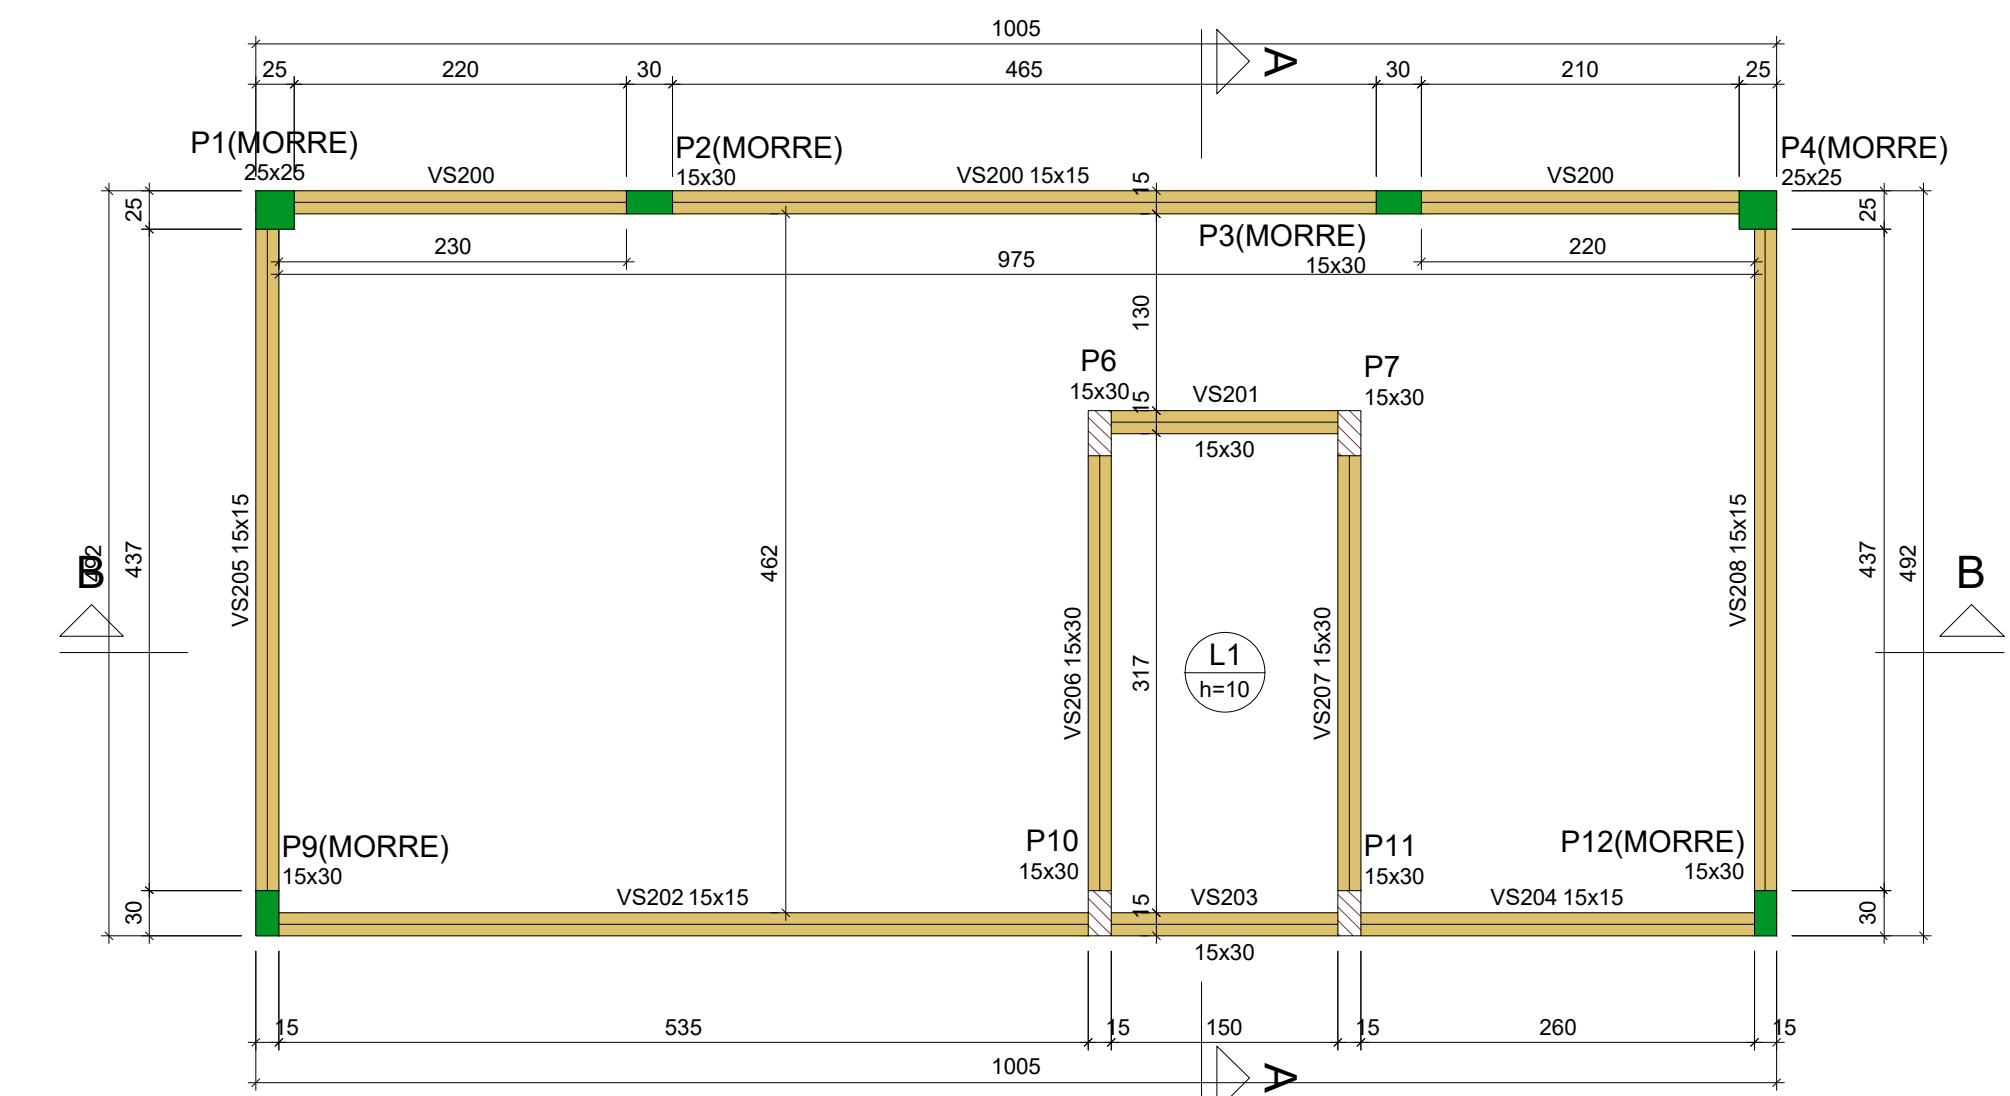

Forma do pavimento +380 (Nível 380)
escala 1:50

Lajes								
Dados					Sobrecarga (kgf/m²)			
Nome	Tipo	Altura (cm)	Elevação (cm)	Nível (cm)	Peso próprio (kgf/m²)	Adicional	Acidental	Água
L1	Maciça	10	0	380	250	100	50	950

Área de lajes			
Tipo	Altura (cm)	Bloco de Enchimento	Área (m²)
Maciça	10	-	4.75

Vigas			
Nome	Seção (cm)	Elevação (cm)	Nível (cm)
VS200	15x15	0	380
VS201	15x30	0	380
VS202	15x15	0	380
VS203	15x30	0	380
VS204	15x15	0	380
VS205	15x15	0	380
VS206	15x30	0	380
VS207	15x30	0	380
VS208	15x15	0	380

Legenda dos pilares	
	Pilar que morre
	Pilar que passa

Legenda das vigas e paredes	
	Viga

Características dos materiais	
fck (kgf/cm²)	Ecs (kgf/cm²)
250	241500


Pilares			
Nome	Seção (cm)	Elevação (cm)	Nível (cm)
P1	25x25	0	380
P2	15x30	0	380
P3	15x30	0	380
P4	25x25	0	380
P6	15x30	0	380
P7	15x30	0	380
P9	15x30	0	380
P10	15x30	0	380
P11	15x30	0	380
P12	15x30	0	380

PROPRIETÁRIO: PREFEITURA MUNICIPAL DE COREMAS- PB	
LINCOLN CARTAXO DE LIRA JUNIOR:06897861405	Assinado de forma digital por LINCOLN CARTAXO DE LIRA JUNIOR:06897861405 Dados: 2025.07.14 11:26:34 -03'00'
PROJETO: LINCOLN CARTAXO DE LIRA JÚNIOR CREA 160.814.689-8	

FOLHA	PROJETO: GARAGEM COREMAS (ESTRUTURAL ANEXO I)
02/09	CONVENIENTE: PREFEITURA MUNICIPAL DE COREMAS-PB
	CONCENDENTE: PREFEITURA MUNICIPAL DE COREMAS-PB
	LOCALIDADE: COREMAS- PB

DESENHO	DATA	RESPONSÁVEL	RUBRICA	DADOS
CÓPIA	JUN/2025	LINCOLN CARTAXO		
VISTO				
ESCALAS	DESENHOS			CONVÊNIO
INDICADO	- PLANTA DE FORMAS -- Pav. +0; -- Pav. +305; -- Pav. +380.			ARQUIVO

Aprovações:

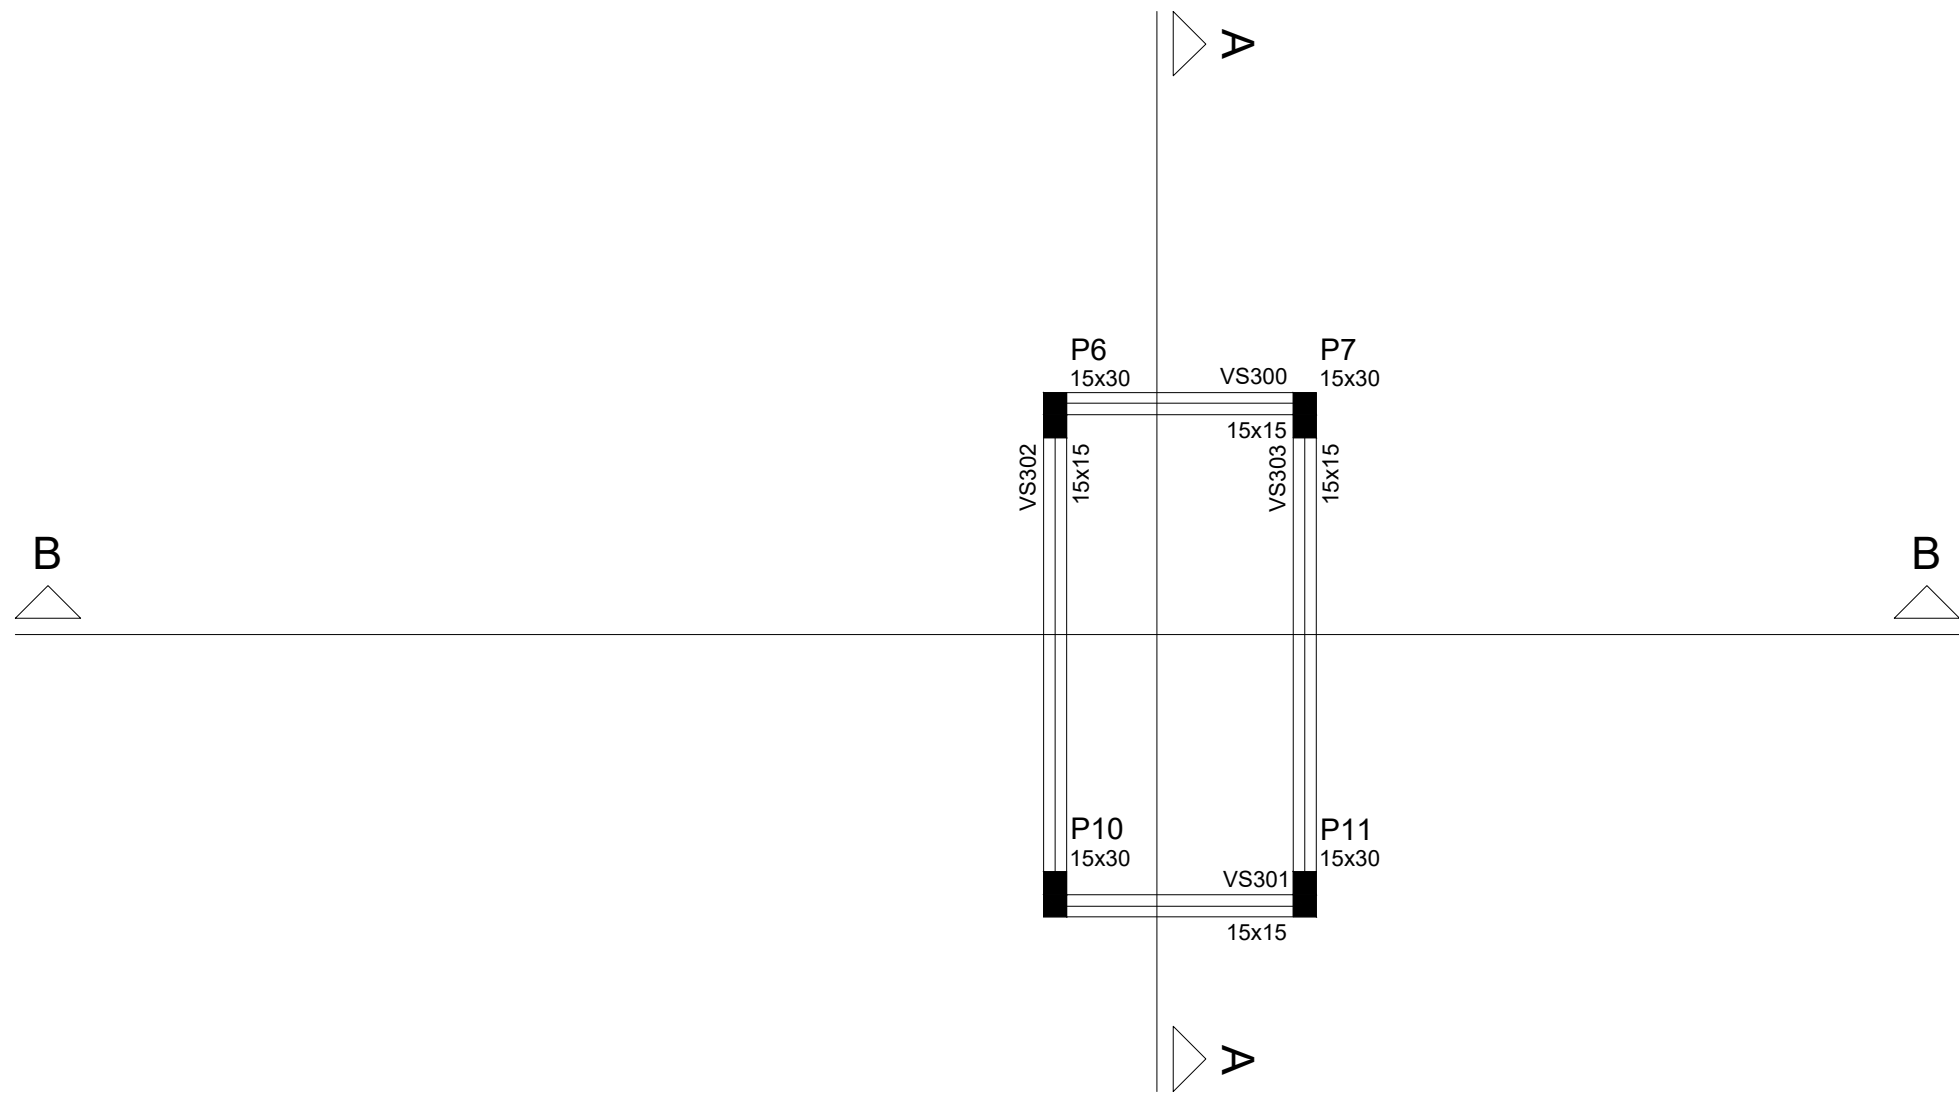


Forma do pavimento +490
escala 1:50

Vigas			
Nome	Seção (cm)	Elevação (cm)	Nível (cm)
VS300	15x15	0	490
VS301	15x15	0	490
VS302	15x15	0	490
VS303	15x15	0	490



Características dos materiais	
fck (kgf/cm²)	Ecs (kgf/cm²)
250	238000

Pilares			
Nome	Seção (cm)	Elevação (cm)	Nível (cm)
P6	15 x 30	0	490
P7	15 x 30	0	490
P10	15 x 30	0	490
P11	15 x 30	0	490


Legenda dos Pilares	
	Pilar que morre
	Pilar que passa
	Pilar que nasce
	Pilar com mudança de seção

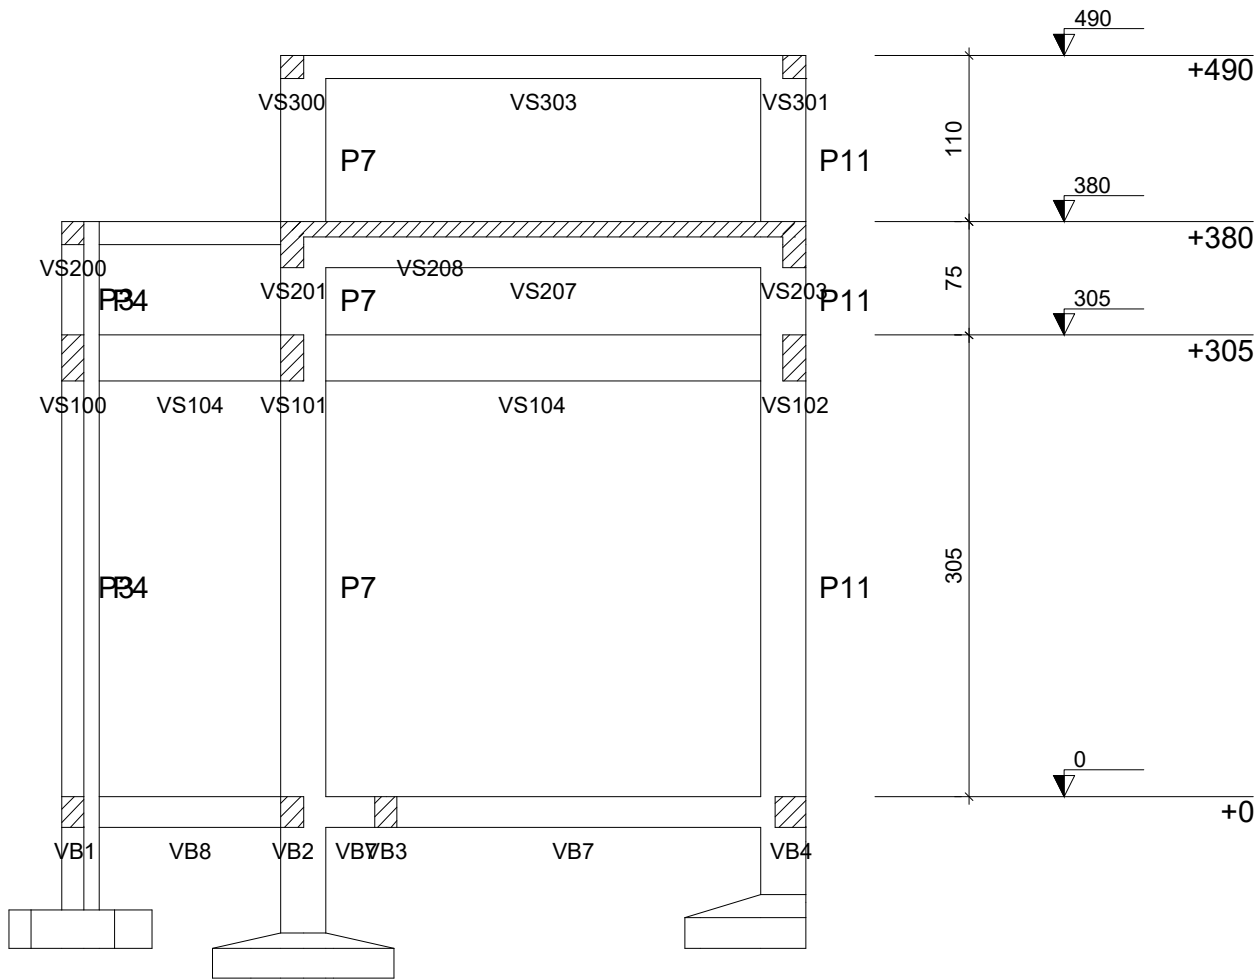

Corte A-A
escala 1:50

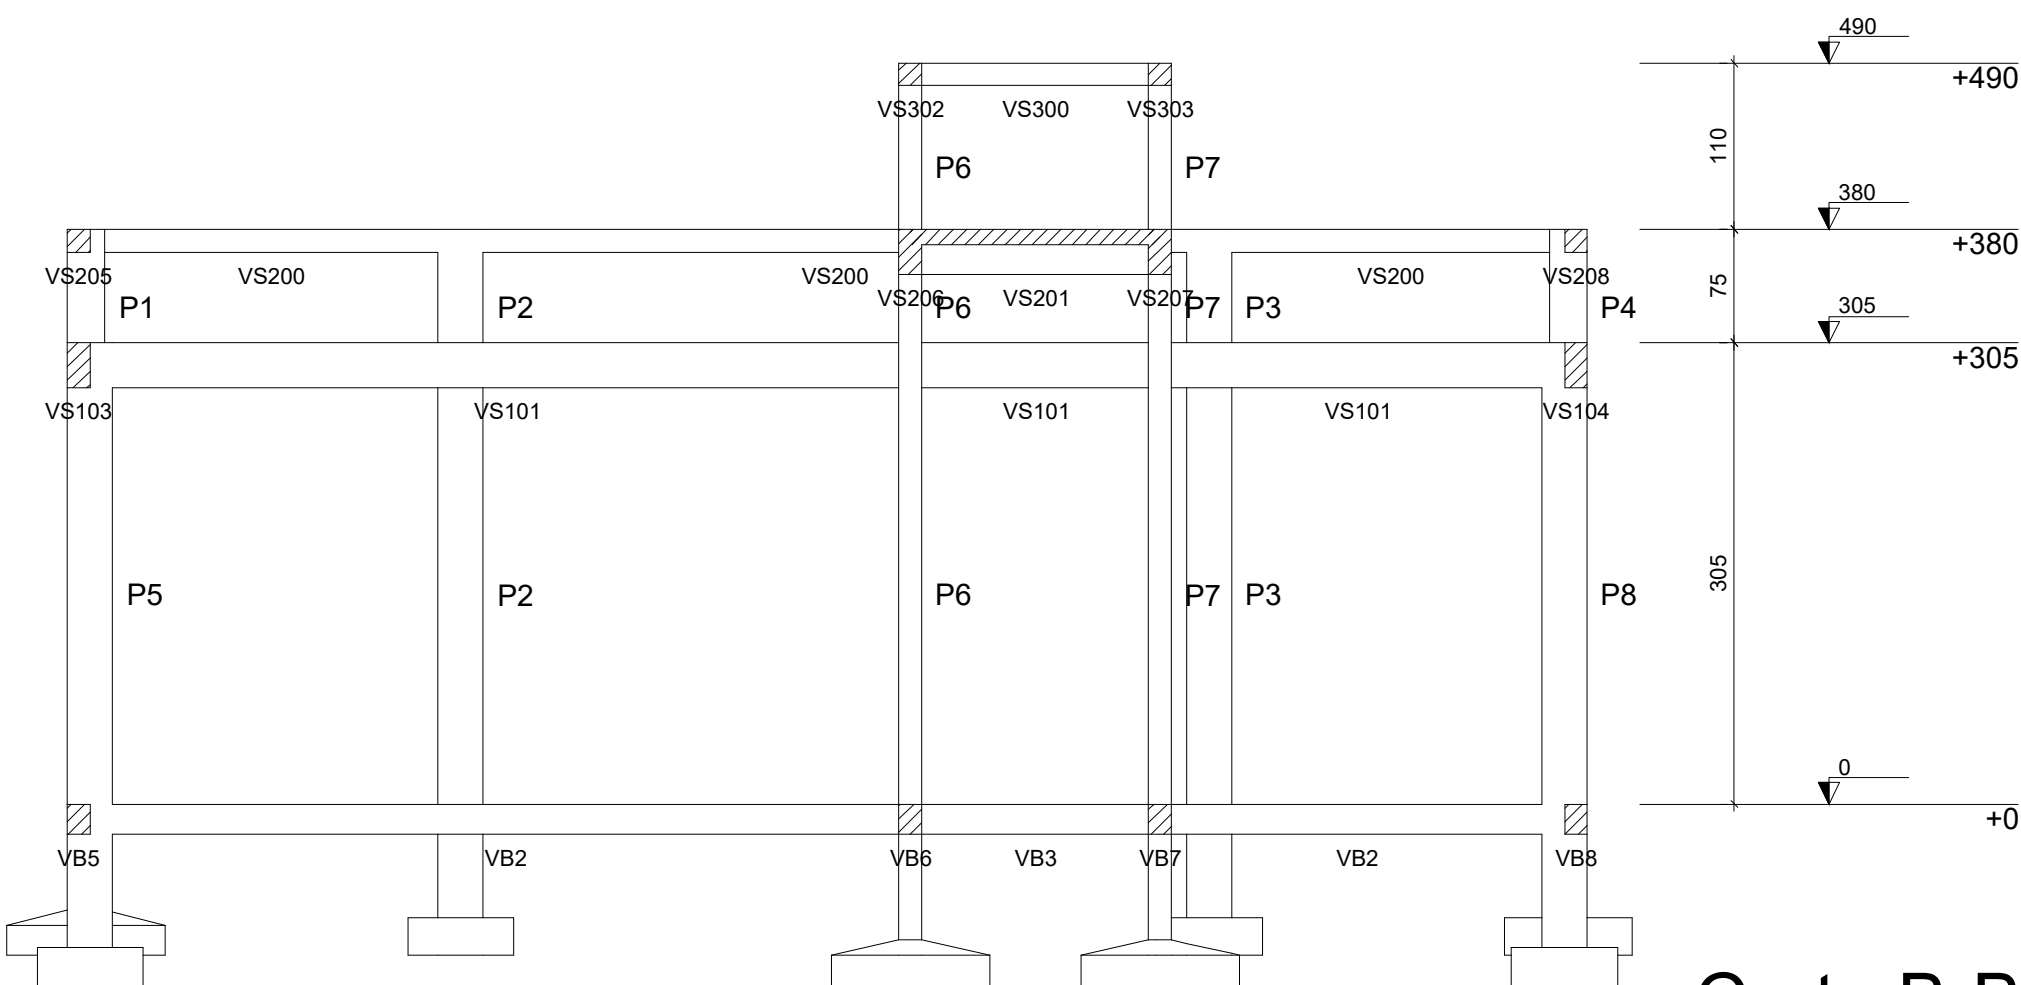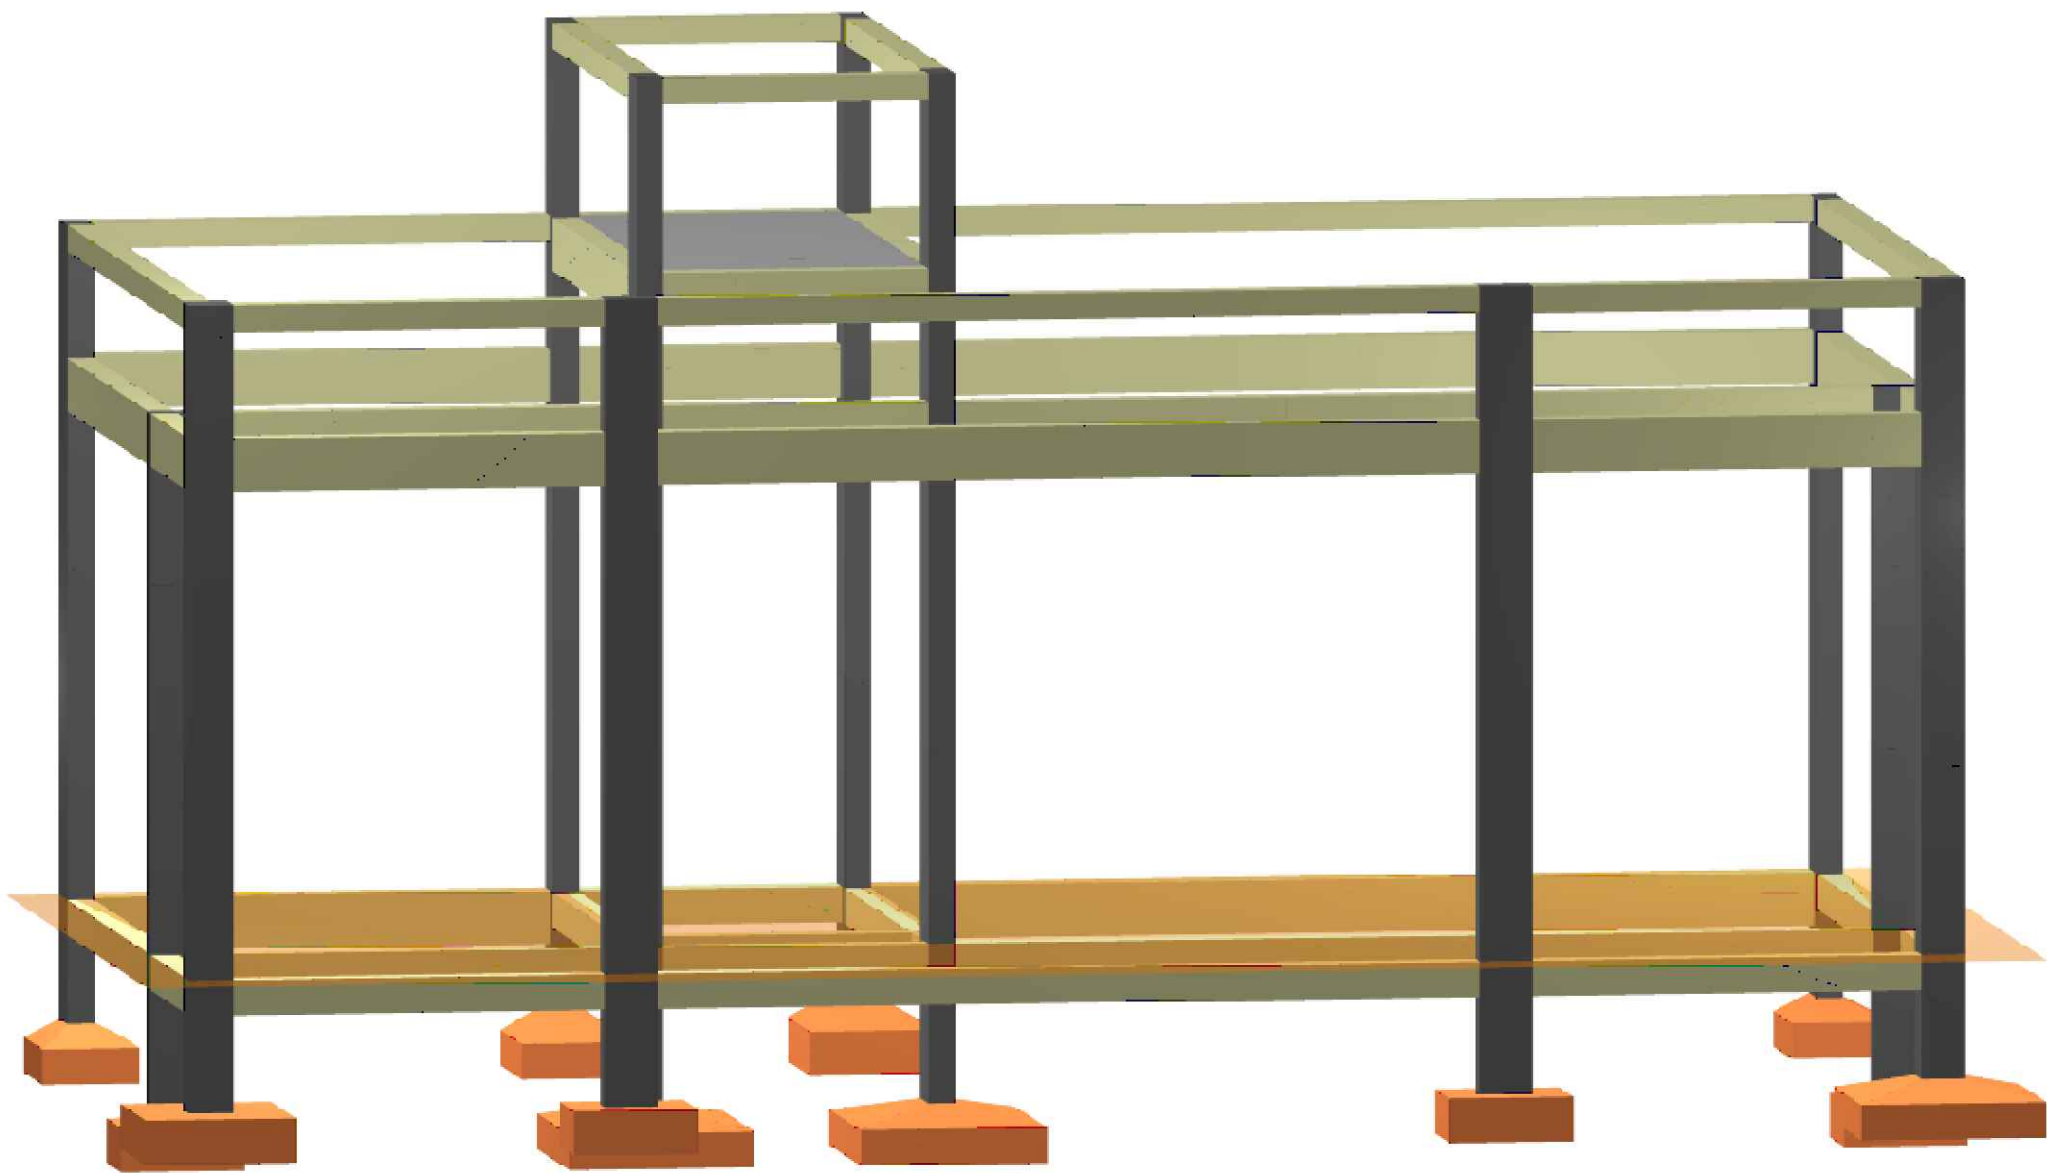

Corte B-B
escala 1:50

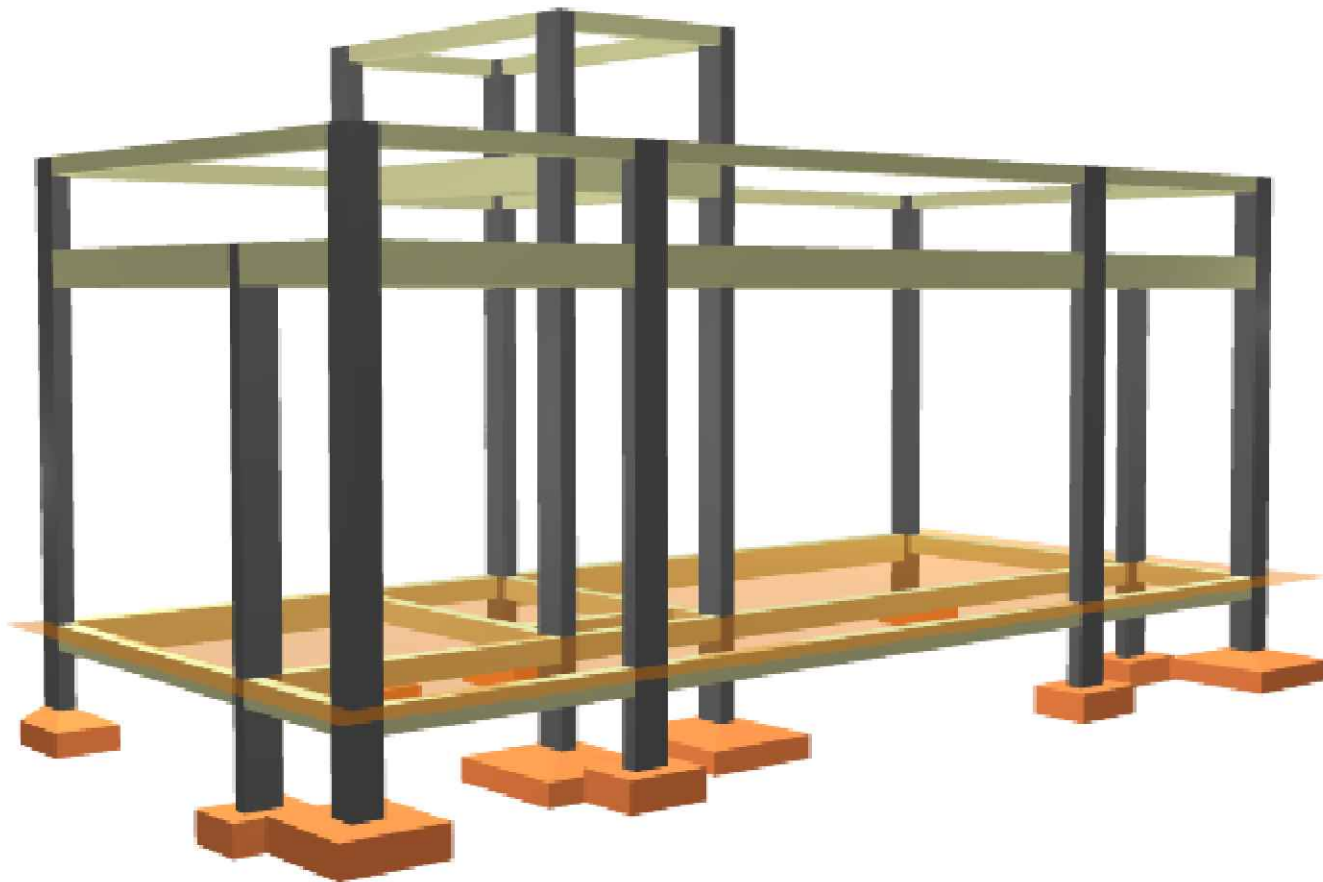



PROPRIETÁRIO: PREFEITURA MUNICIPAL DE COREMAS- PB

LINCOLN CARTAXO DE LIRA JUNIOR:06897861405 Assinado de forma digital por LINCOLN CARTAXO DE LIRA JUNIOR:06897861405 Dados: 2025.07.14 11:27:07 -03'00'

PROJETO: LINCOLN CARTAXO DE LIRA JÚNIOR CREA 160.814.689-8

FOLHA	PROJETO: GARAGEM COREMAS (ESTRUTURAL ANEXO I)		
03/09	CONVENIENTE: PREFEITURA MUNICIPAL DE COREMAS-PB		
	CONCIDENTE: PREFEITURA MUNICIPAL DE COREMAS-PB		
	LOCALIDADE: COREMAS- PB		
DESENHO	DATA	RESPONSÁVEL	RUBRICA
JUN/2025	LINCOLN CARTAXO		
CÓPIA			
VISTO			
ESCALAS	DESENHOS	CONVÊNIO	
INDICADO	- PLANTA DE FORMAS -- Pav. +490. - CORTES -- Corte A-A; -- Corte B-B.	ARQUIVO	

Aprovações:

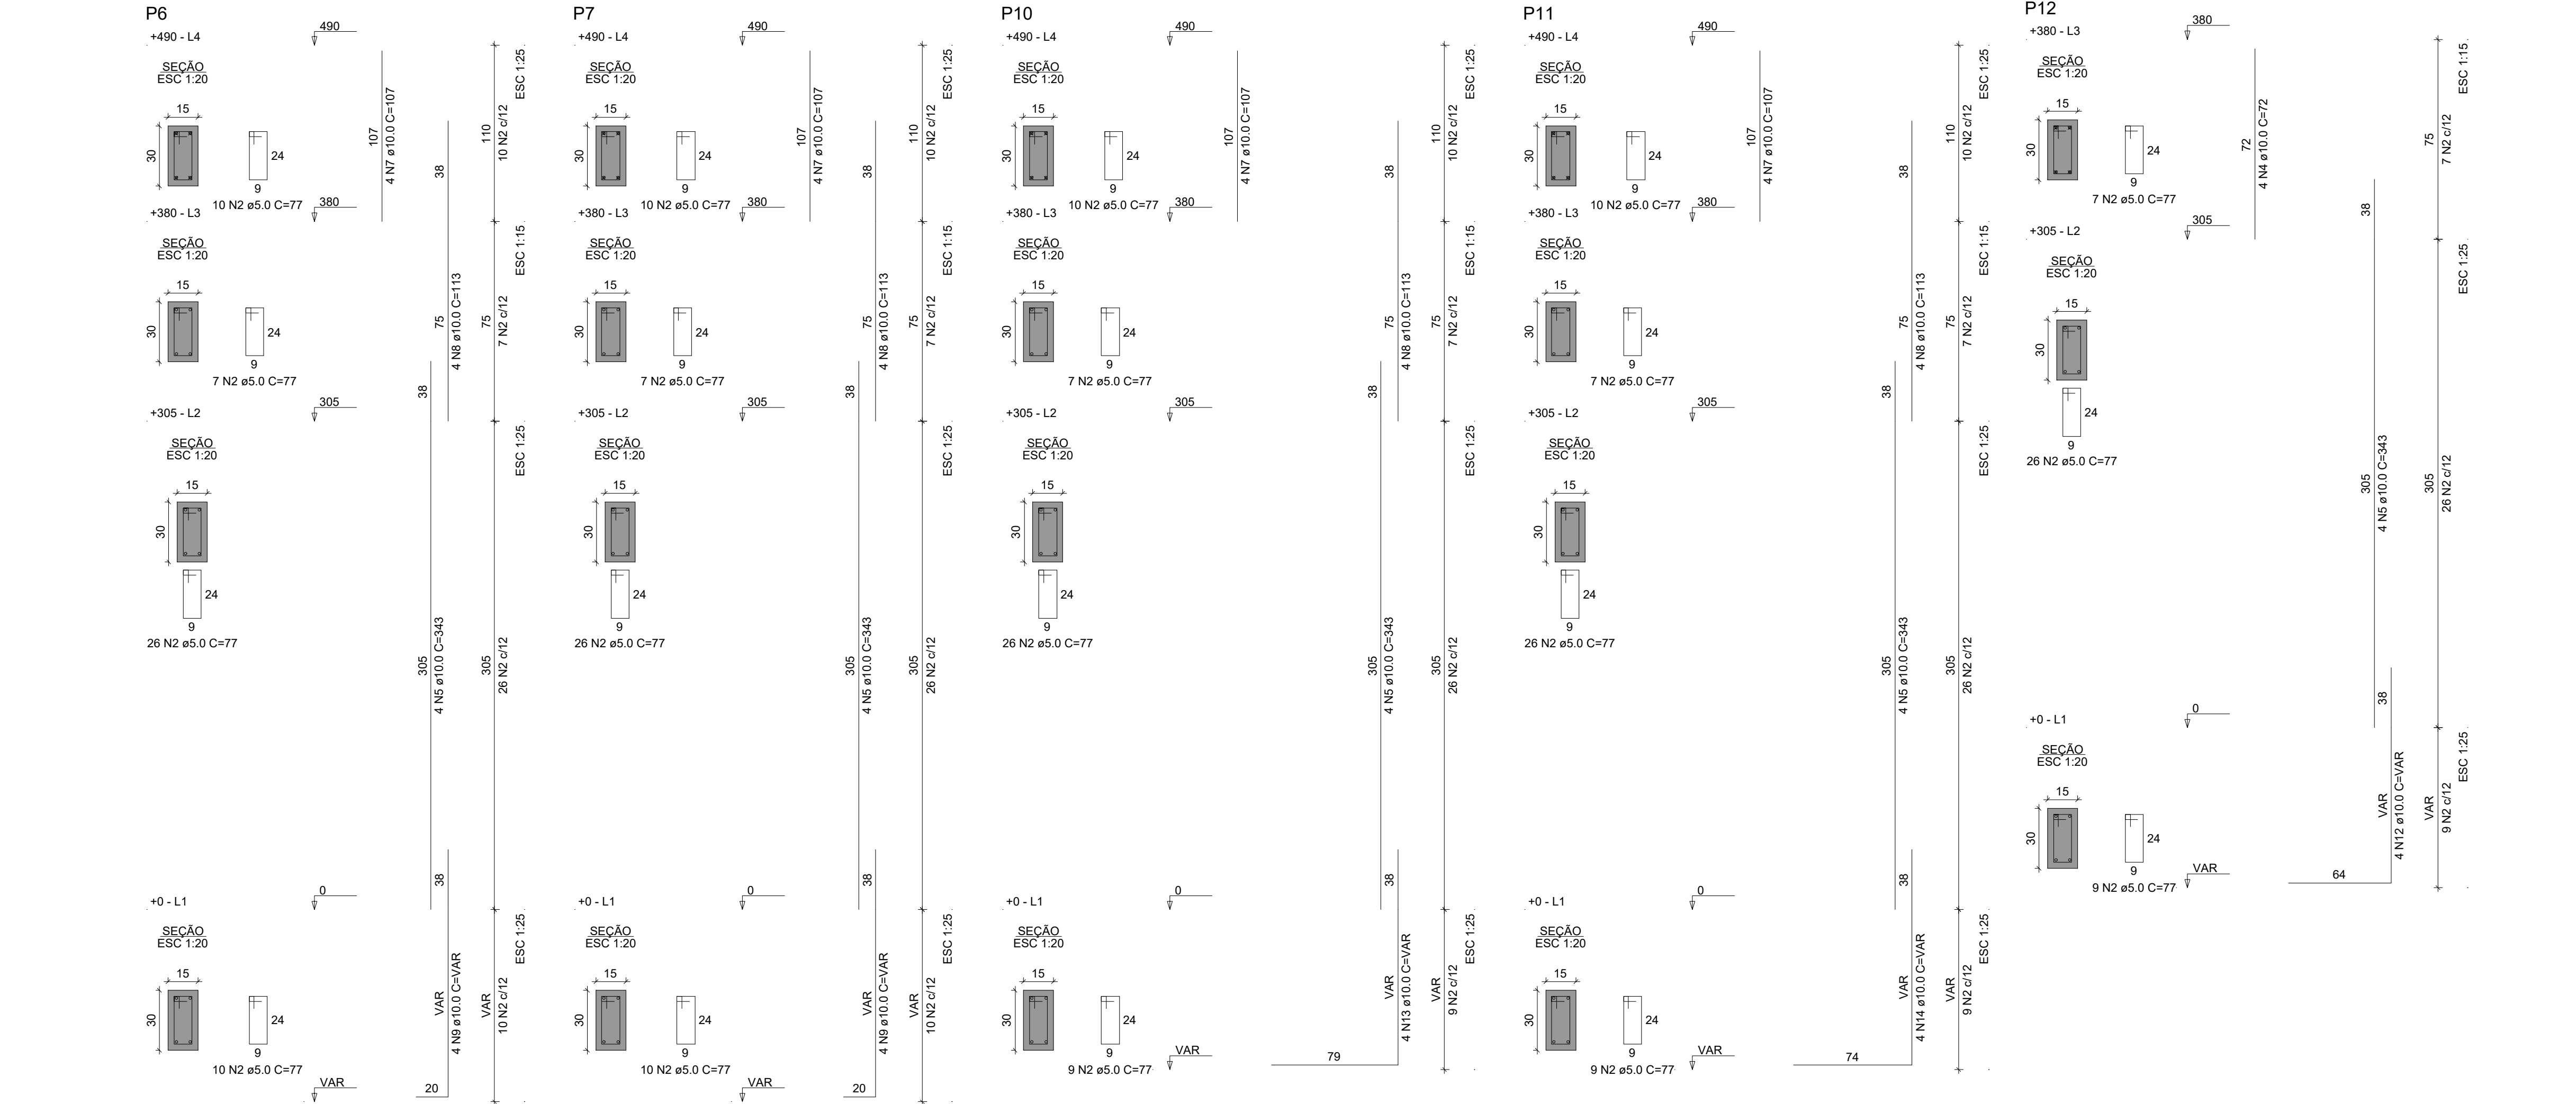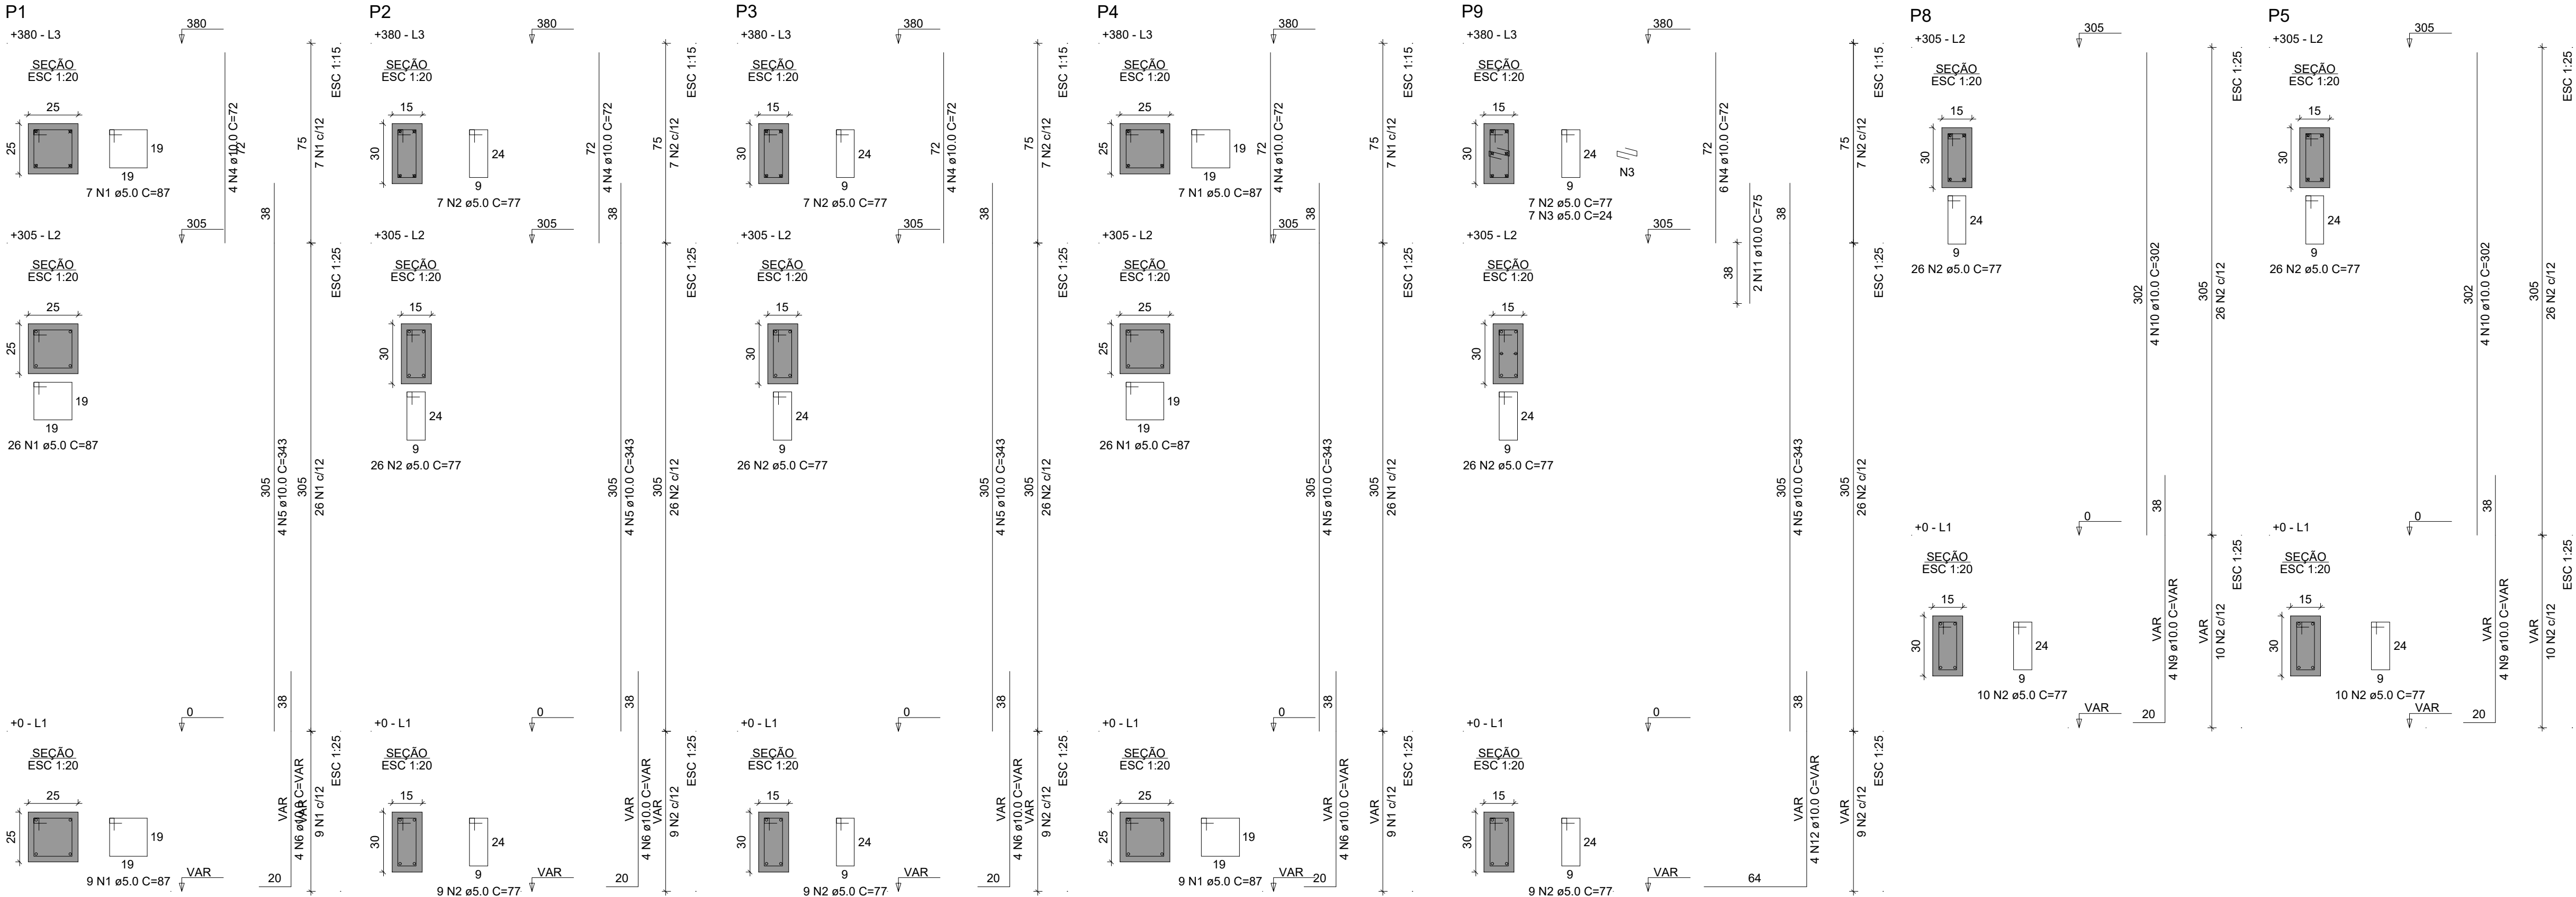

RELAÇÃO DO AÇO

P1-L3	P1-L2	P1-L1
P2-L3	P2-L2	P2-L1
P3-L3	P3-L2	P3-L1
P4-L3	P4-L2	P4-L1
P6-L4	P6-L3	P6-L2
P6-L1	P7-L4	P7-L3
P7-L2	P7-L1	P8-L2
P8-L1	P9-L3	P9-L2
P9-L1	P10-L4	P10-L3
P10-L2	P10-L1	P11-L4
P11-L3	P11-L2	P11-L1
P12-L3	P12-L2	P12-L1
P5-L2	P5-L1	

AÇO	N	DIAM (mm)	QUANT	C.UNIT (cm)	C.TOTAL (cm)
CA60	1	5.0	84	87	7308
	2	5.0	450	77	34650
CA50	3	5.0	7	24	168
	4	10.0	26	72	1872
	5	10.0	40	343	13720
	6	10.0	16	VAR	VAR
	7	10.0	16	107	1712
	8	10.0	16	113	1808
	9	10.0	16	VAR	VAR
	10	10.0	8	302	2416
	11	10.0	2	75	150
	12	10.0	8	VAR	VAR
	13	10.0	4	VAR	VAR
	14	10.0	4	VAR	VAR

RESUMO DO AÇO

AÇO	DIAM (mm)	C.TOTAL (m)	PESO + 10% (kg)
CA50	10.0	301.5	204.4
CA60	5.0	421.3	71.4
PESO TOTAL (kg)			
CA50		204.4	
CA60		71.4	

Volume de concreto (C-25) = 2.93 m³
Área de forma = 56.13 m²

PROPRIETÁRIO: PREFEITURA MUNICIPAL DE COREMAS- PB
LINCOLN CARTAXO DE LIRA JUNIOR:06897861405 Assinado de forma digital por LINCOLN CARTAXO DE LIRA JUNIOR:06897861405
Dados: 2025.07.14 11:28:00 -03'00'

PROJETO: LINCOLN CARTAXO DE LIRA JÚNIOR CREA 160.814.689-8


FOLHA: 05/09
PROJETO: GARAGEM COREMAS (ESTRUTURAL ANEXO I)
CONVENIENTE: PREFEITURA MUNICIPAL DE COREMAS-PB
CONCIDENTE: PREFEITURA MUNICIPAL DE COREMAS-PB
LOCALIDADE: COREMAS- PB

DESENHO	DATA	RESPONSÁVEL	RUBRICA	DADOS
COPIA	JUN/2025	LINCOLN CARTAXO		
VISTO				
ESCALAS	DESENHOS	CONVÊNIO		
INDICADO	PILARES	ARQUIVO		

Aprovações:


VB1

ESC 1:50

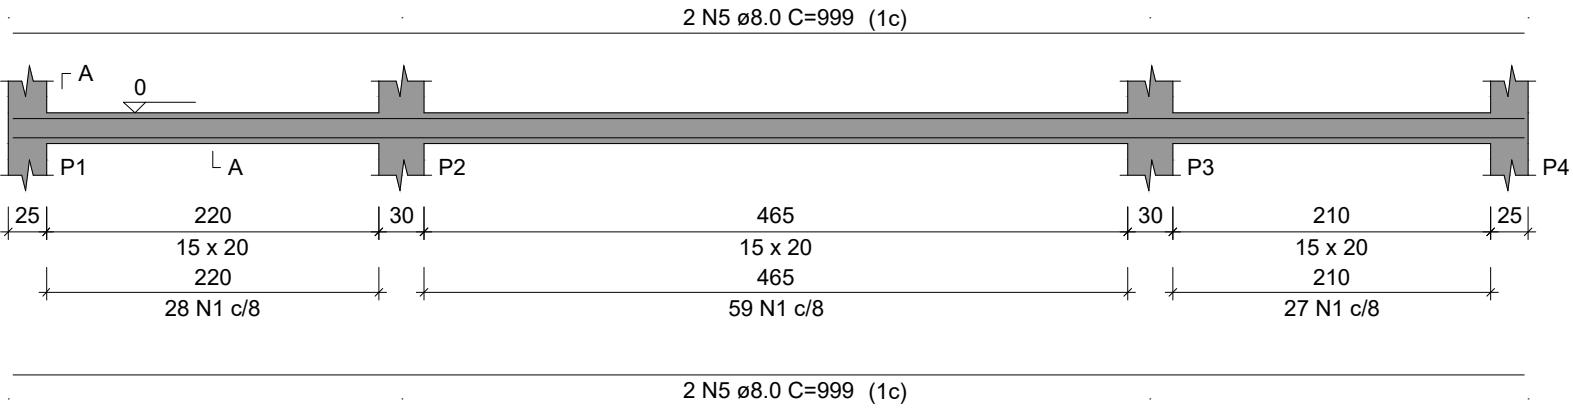


SEÇÃO A-A

ESC 1:25

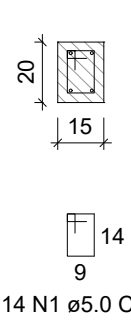


VB2

ESC 1:50

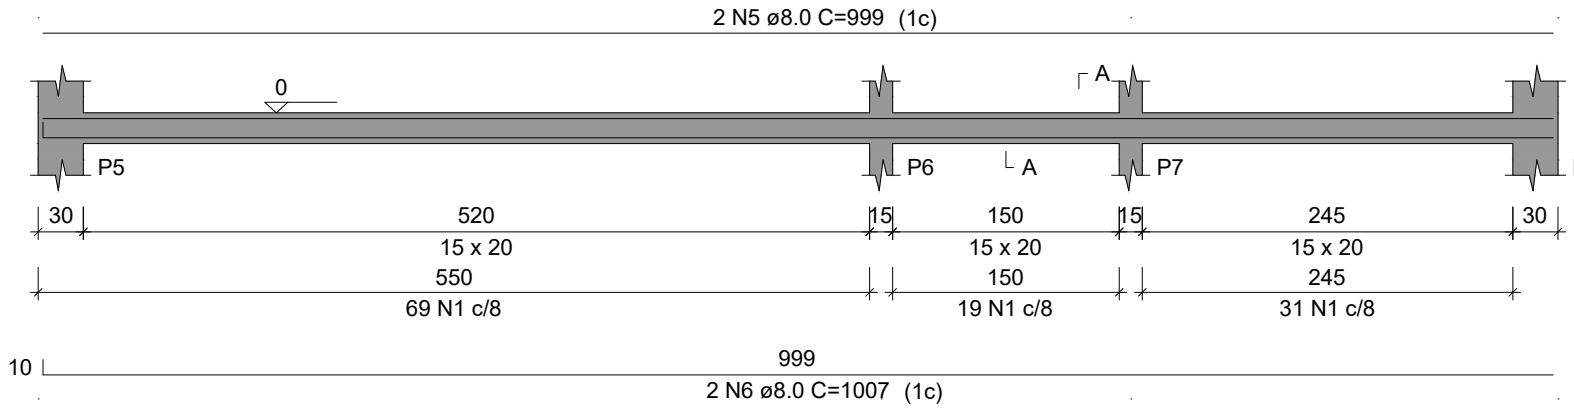


SEÇÃO A-A

ESC 1:25

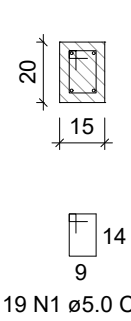


VB3

ESC 1:50

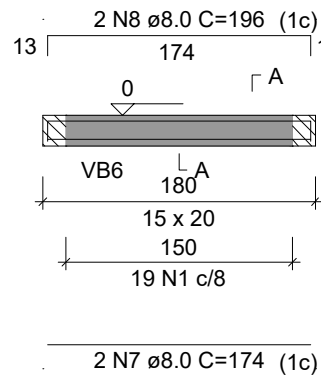


SEÇÃO A-A

ESC 1:25

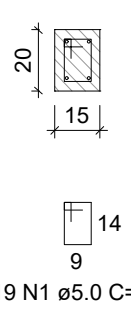


VB4

ESC 1:50

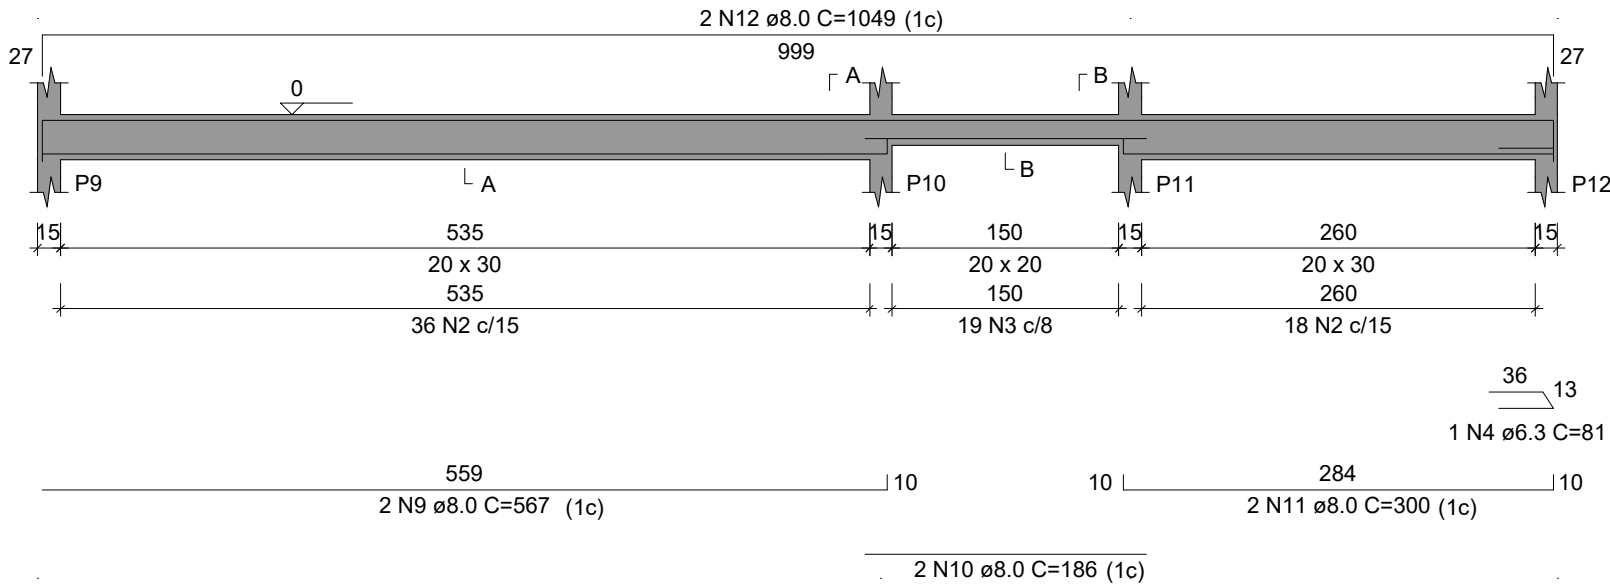


SEÇÃO A-A

ESC 1:25

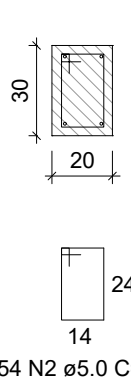


SEÇÃO B-B

ESC 1:25

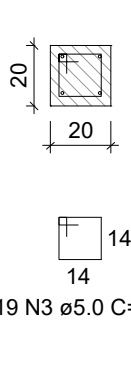


VB5

ESC 1:50

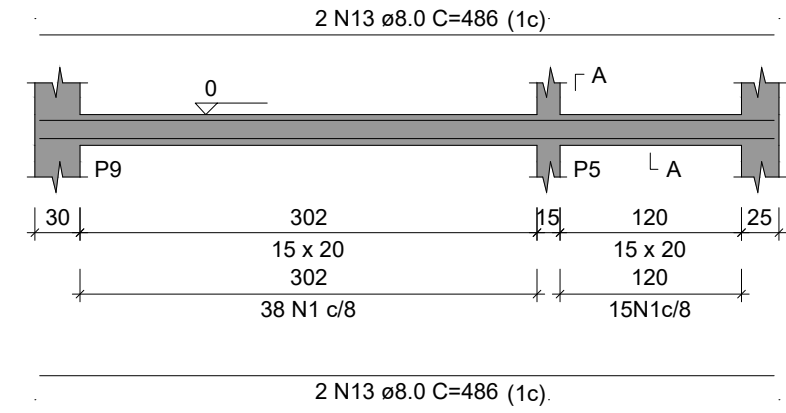


SEÇÃO A-A

ESC 1:25

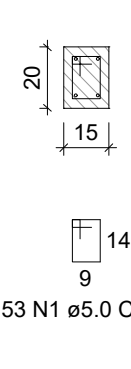


VB6

ESC 1:50

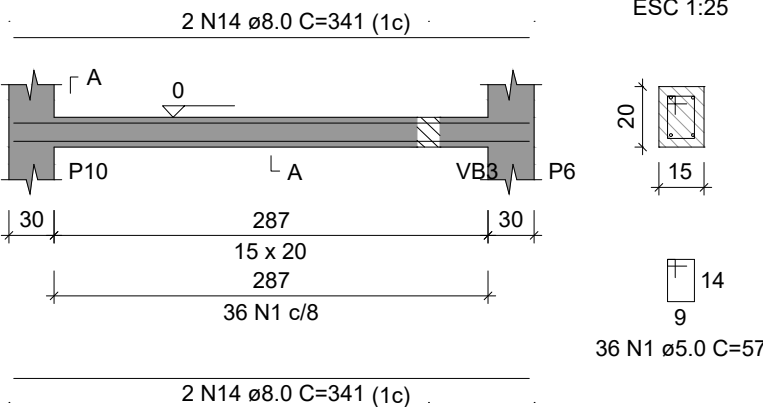


SEÇÃO A-A

ESC 1:25

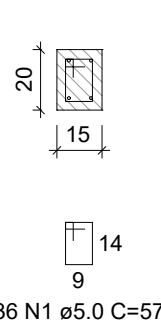


VB7

ESC 1:50

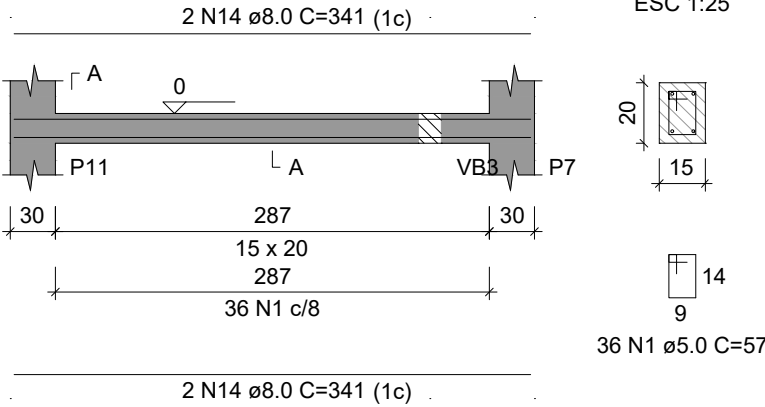


SEÇÃO A-A

ESC 1:25

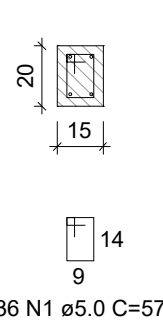


VB8

ESC 1:50

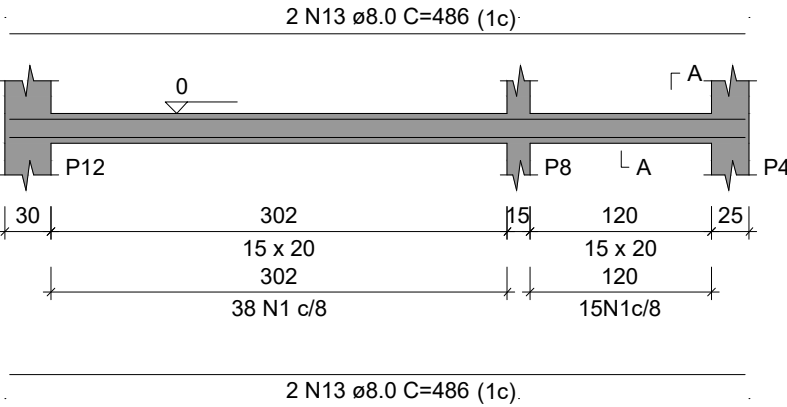

SEÇÃO A-A

ESC 1:25

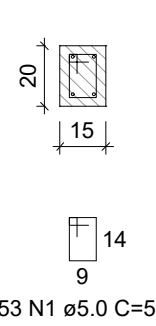

RELAÇÃO DO AÇO

VB1 VB2 VB3
VB4 VB5 VB6
VB7 VB8

RESUMO DO AÇO

AÇO	N	DIAM (mm)	QUANT	C.UNIT (cm)	C.TOTAL (cm)
CA60	1	5.0	430	57	24510
	2	5.0	54	87	4698
	3	5.0	19	67	1273
	4	6.3	1	81	81
	5	8.0	6	999	5994
	6	8.0	2	1007	2014
	7	8.0	2	174	348
	8	8.0	2	196	392
	9	8.0	2	567	1134
	10	8.0	2	186	372
	11	8.0	2	300	600
	12	8.0	2	1049	2098
	13	8.0	8	486	3888
	14	8.0	8	341	2728

AÇO	DIAM (mm)	C.TOTAL (m)	PESO + 10% (kg)
CA50	6.3	0.8	0.2
	8.0	195.7	84.9
	5.0	304.8	51.7
PESO TOTAL (kg)			
CA50	85.2		
CA60	51.7		

Volume de concreto (C-25) = 1.73 m³

Área de forma = 28.98 m²

PROPRIETÁRIO: PREFEITURA MUNICIPAL DE COREMAS- PB
LINCOLN CARTAXO DE LIRA JUNIOR:06897861405
Assinado de forma digital por LINCOLN CARTAXO DE LIRA JUNIOR:06897861405
Dados: 2025.07.14 11:27:48 -03'00'

PROJETO: LINCOLN CARTAXO DE LIRA JÚNIOR CREA 160.814.689-8

FOLHA

06/09

PROJETO: GARAGEM COREMAS (ESTRUTURAL ANEXO I)

CONVENIENTE: PREFEITURA MUNICIPAL DE COREMAS-PB


CONCENDENTE: PREFEITURA MUNICIPAL DE COREMAS-PB

LOCALIDADE: COREMAS- PB

DATA	RESPONSÁVEL	RUBRICA	DADOS
DESENHO JUN/2025	LINCOLN CARTAXO		
CÓPIA			
VISTO			
ESCALAS	DESENHOS		CONVÊNIO
INDICADO	- VIGAS BALDRAME		
			ARQUIVO


Aprovações:

VS100
ESC 1:50

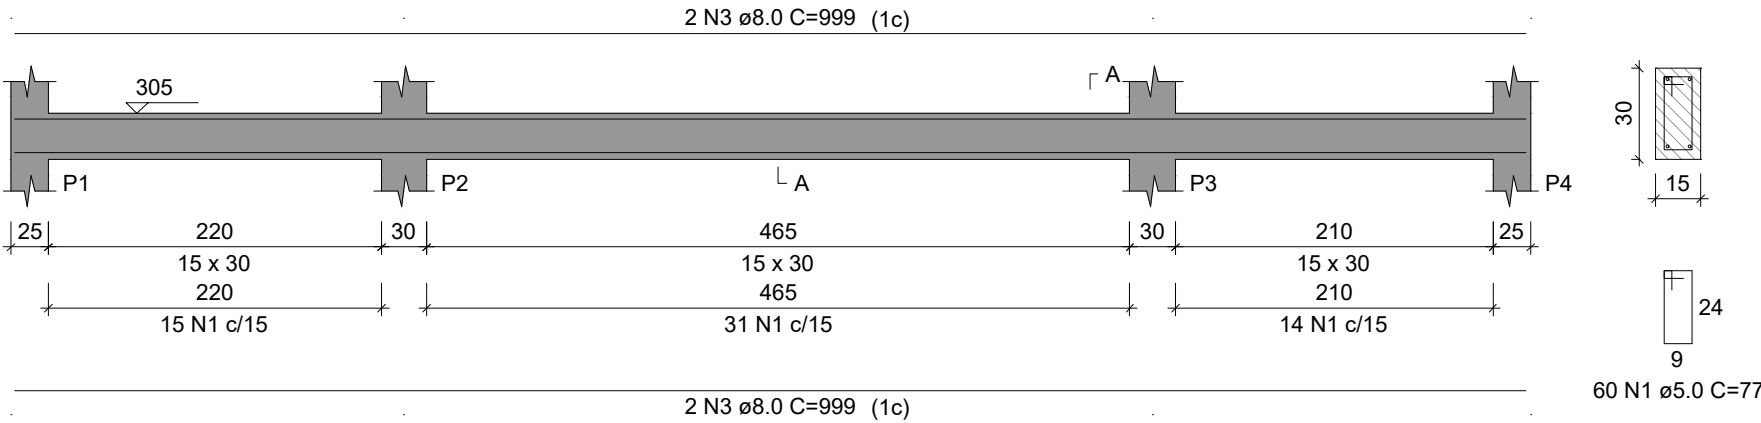


SEÇÃO A-A
ESC 1:25

VS101
ESC 1:50

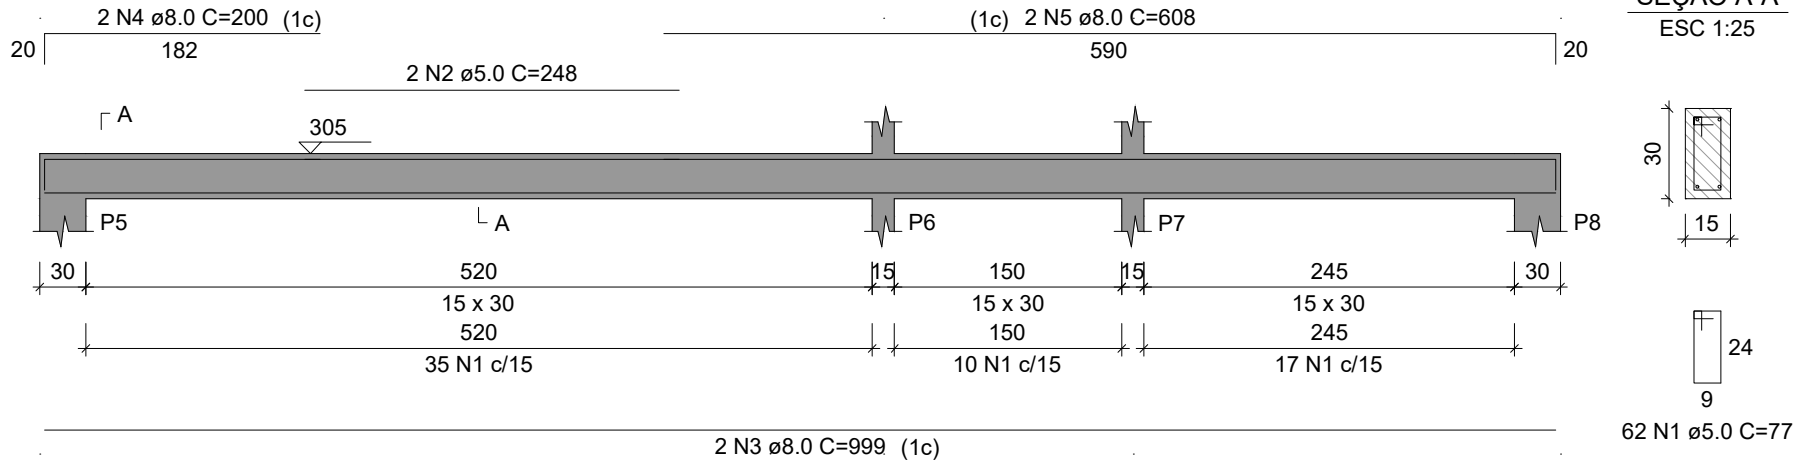


SEÇÃO A-A
ESC 1:25

VS102
ESC 1:50

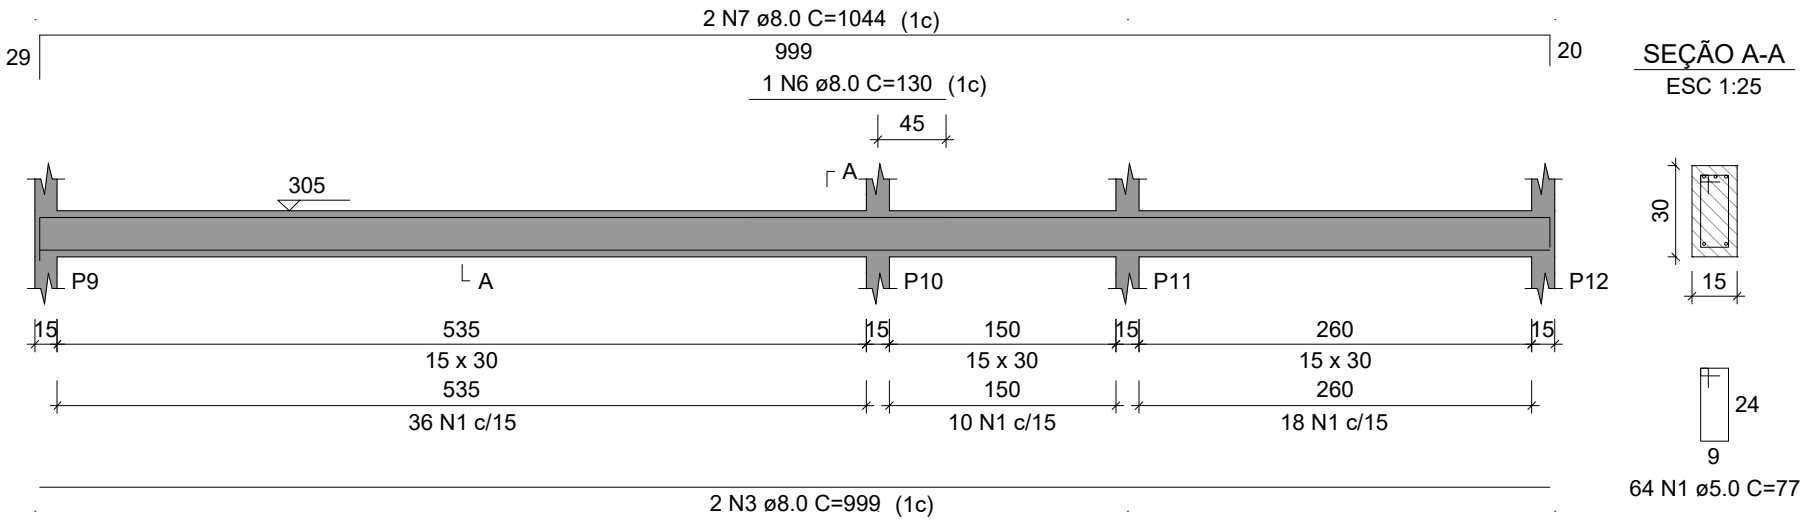


SEÇÃO A-A
ESC 1:25

VS103
ESC 1:50

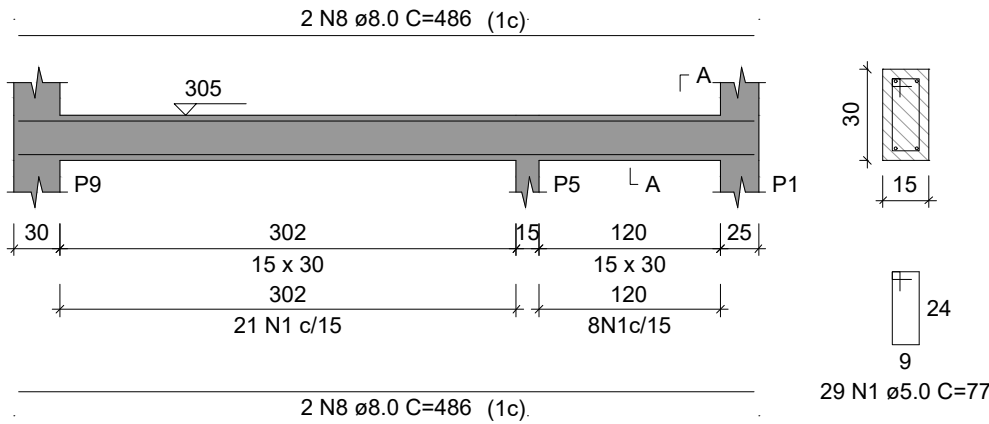

SEÇÃO A-A
ESC 1:25

VS104
ESC 1:50

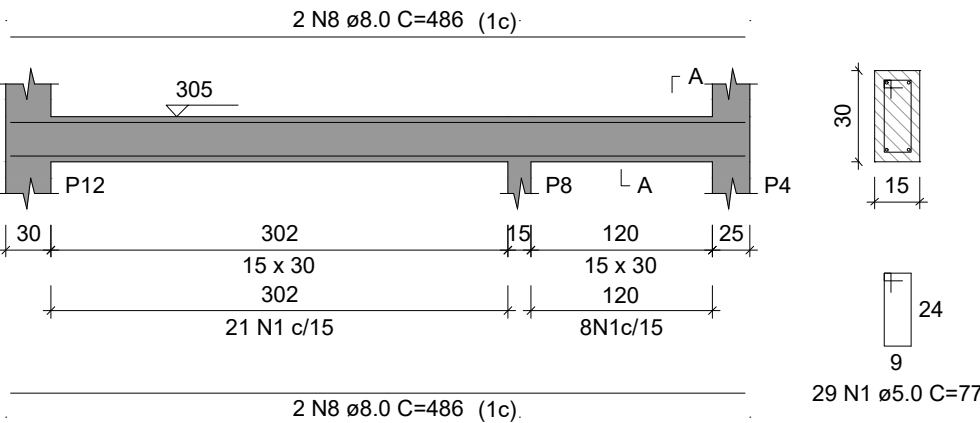

SEÇÃO A-A
ESC 1:25

RELAÇÃO DO AÇO

AÇO	N	DIAM (mm)	QUANT	C.UNIT (cm)	C.TOTAL (cm)
CA60	1	5.0	244	77	18788
	2	5.0	2	248	496
CA50	3	8.0	8	999	7992
	4	8.0	2	200	400
	5	8.0	2	608	1216
	6	8.0	1	130	130
	7	8.0	2	1044	2088
	8	8.0	8	486	3888

RESUMO DO AÇO

AÇO	DIAM (mm)	C.TOTAL (m)	PESO + 10% (kg)
CA50	8.0	157.1	68.2
CA60	5.0	192.8	32.7
PESO TOTAL (kg)			
CA50	68.2		
CA60	32.7		

Volume de concreto (C-25) = 1.80 m³
Área de forma = 29.99 m²

PROPRIETÁRIO: PREFEITURA MUNICIPAL DE COREMAS- PB

LINCOLN CARTAXO DE LIRA JÚNIOR:06897861405
Assinado de forma digital por LINCOLN CARTAXO DE LIRA JÚNIOR:06897861405
Dados: 2025.07.14 11:27:36 -03'00'

PROJETO: LINCOLN CARTAXO DE LIRA JÚNIOR CREA 160.814.689-8

FOLHA PROJETO: GARAGEM COREMAS (ESTRUTURAL ANEXO I)

CONVENENTE: PREFEITURA MUNICIPAL DE COREMAS-PB

CONCENDENTE: PREFEITURA MUNICIPAL DE COREMAS-PB


LOCALIDADE: COREMAS- PB

DESENHO	DATA	RESPONSÁVEL	RUBRICA	DADOS
CÓPIA	JUN/2025	LINCOLN CARTAXO		
VISTO				

ESCALAS	DESENHOS	CONVÊNIO
INDICADO	- VIGAS (Nv. +305)	ARQUIVO

Aprovações:


ESC 1:50

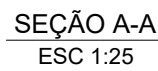


ESC 1:50




ESC 1:50

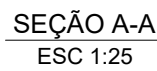


ESC 1:50

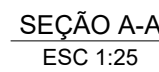


ESC 1:50

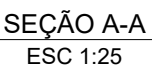


ESC 1:50

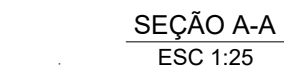

ESC 1:50

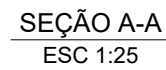

ESC 1:50

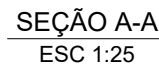


ESC 1:50




Volume de concreto (C-25) = 1.11 m³
Área de forma = 20.70 m²


VS300

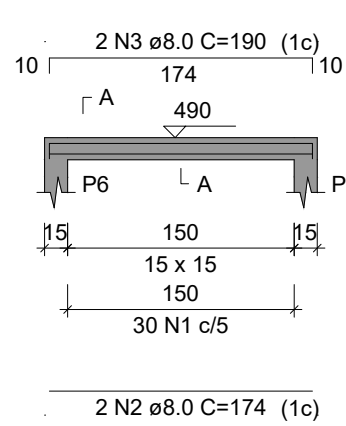


VS301

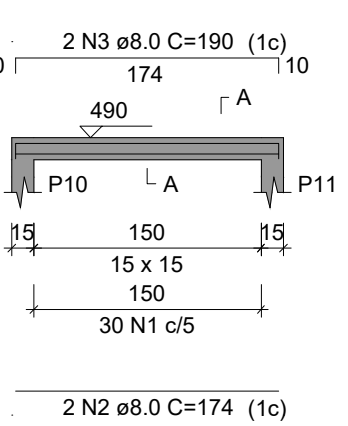

VS302

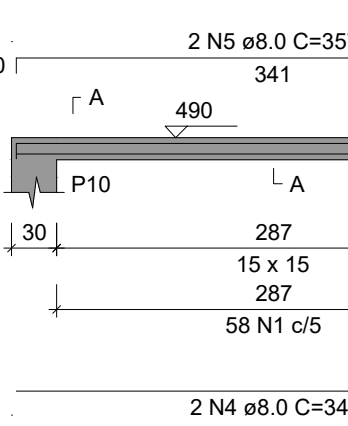

VS303

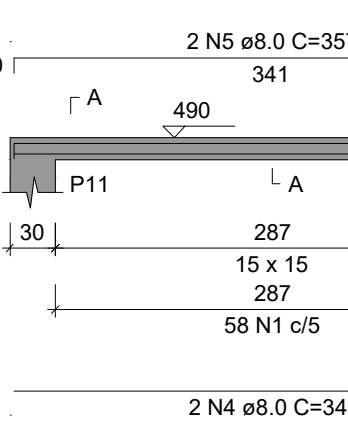

RELAÇÃO DO AÇO

AÇO	N	DIAM (mm)	QUANT	C.UNIT (cm)	C.TOTAL (cm)
CA60	1	5.0	176	47	8272
CA50	2	8.0	4	174	696
	3	8.0	4	190	760
	4	8.0	4	341	1364
	5	8.0	4	357	1428

RESUMO DO AÇO

AÇO	DIAM (mm)	C.TOTAL (m)	PESO + 10% (kg)
CA50	8.0	42.5	18.4
CA60	5.0	82.7	14
PESO TOTAL (kg)			
CA50	18.4		
CA60	14		

Volume de concreto (C-25) = 0.24 m³
Área de forma = 4.74 m²


PROPRIETÁRIO: PREFEITURA MUNICIPAL DE COREMAS- PB

LINCOLN CARTAXO DE LIRA JUNIOR:06897861405
Assinado de forma digital por LINCOLN CARTAXO DE LIRA JUNIOR:06897861405
Dados: 2025.07.14 11:28:26 -03'00'


PROJETO: LINCOLN CARTAXO DE LIRA JÚNIOR CREA 160.814.689-8

FOLHA	PROJETO: GARAGEM COREMAS (ESTRUTURAL ANEXO I)			
09/09	CONVENIENTE: PREFEITURA MUNICIPAL DE COREMAS-PB			
	CONCENDENTE: PREFEITURA MUNICIPAL DE COREMAS-PB			
	LOCALIDADE: COREMAS- PB			
	DATA	RESPONSÁVEL	RUBRICA	DADOS
DESENHO	JUN/2025	LINCOLN CARTAXO		
CÓPIA				
VISTO				
ESCALAS	DESENHOS			CONVÊNIO
INDICADO	- VIGAS (Nv. +490) - LAJE (Nv. +380)			ARQUIVO

Aprovações:

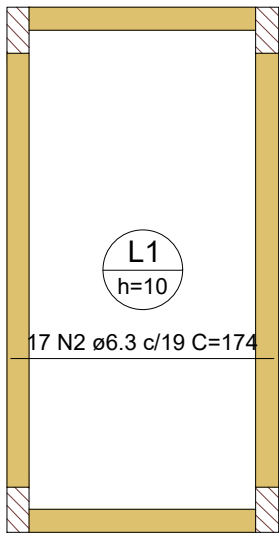

Armação positiva das lajes do pavimento +380 (Eixo X)
escala 1:50

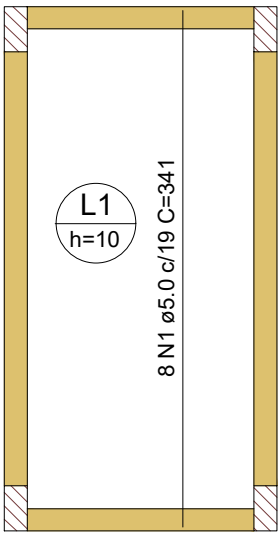

Armação positiva das lajes do pavimento +380 (Eixo Y)
escala 1:50


RELAÇÃO DO AÇO

AÇO	N	DIAM (mm)	QUANT	C.UNIT (cm)	C.TOTAL (cm)
CA60	1	5.0	8	341	2728
CA50	2	6.3	17	174	2958

RESUMO DO AÇO

AÇO	DIAM (mm)	C.TOTAL (m)	PESO + 10% (kg)
CA50	6.3	29.6	8
CA60	5.0	27.3	4.6
PESO TOTAL (kg)			
CA50	8		
CA60	4.6		

Volume de concreto (C-25) = 0.48 m³
Área de forma = 4.80 m²

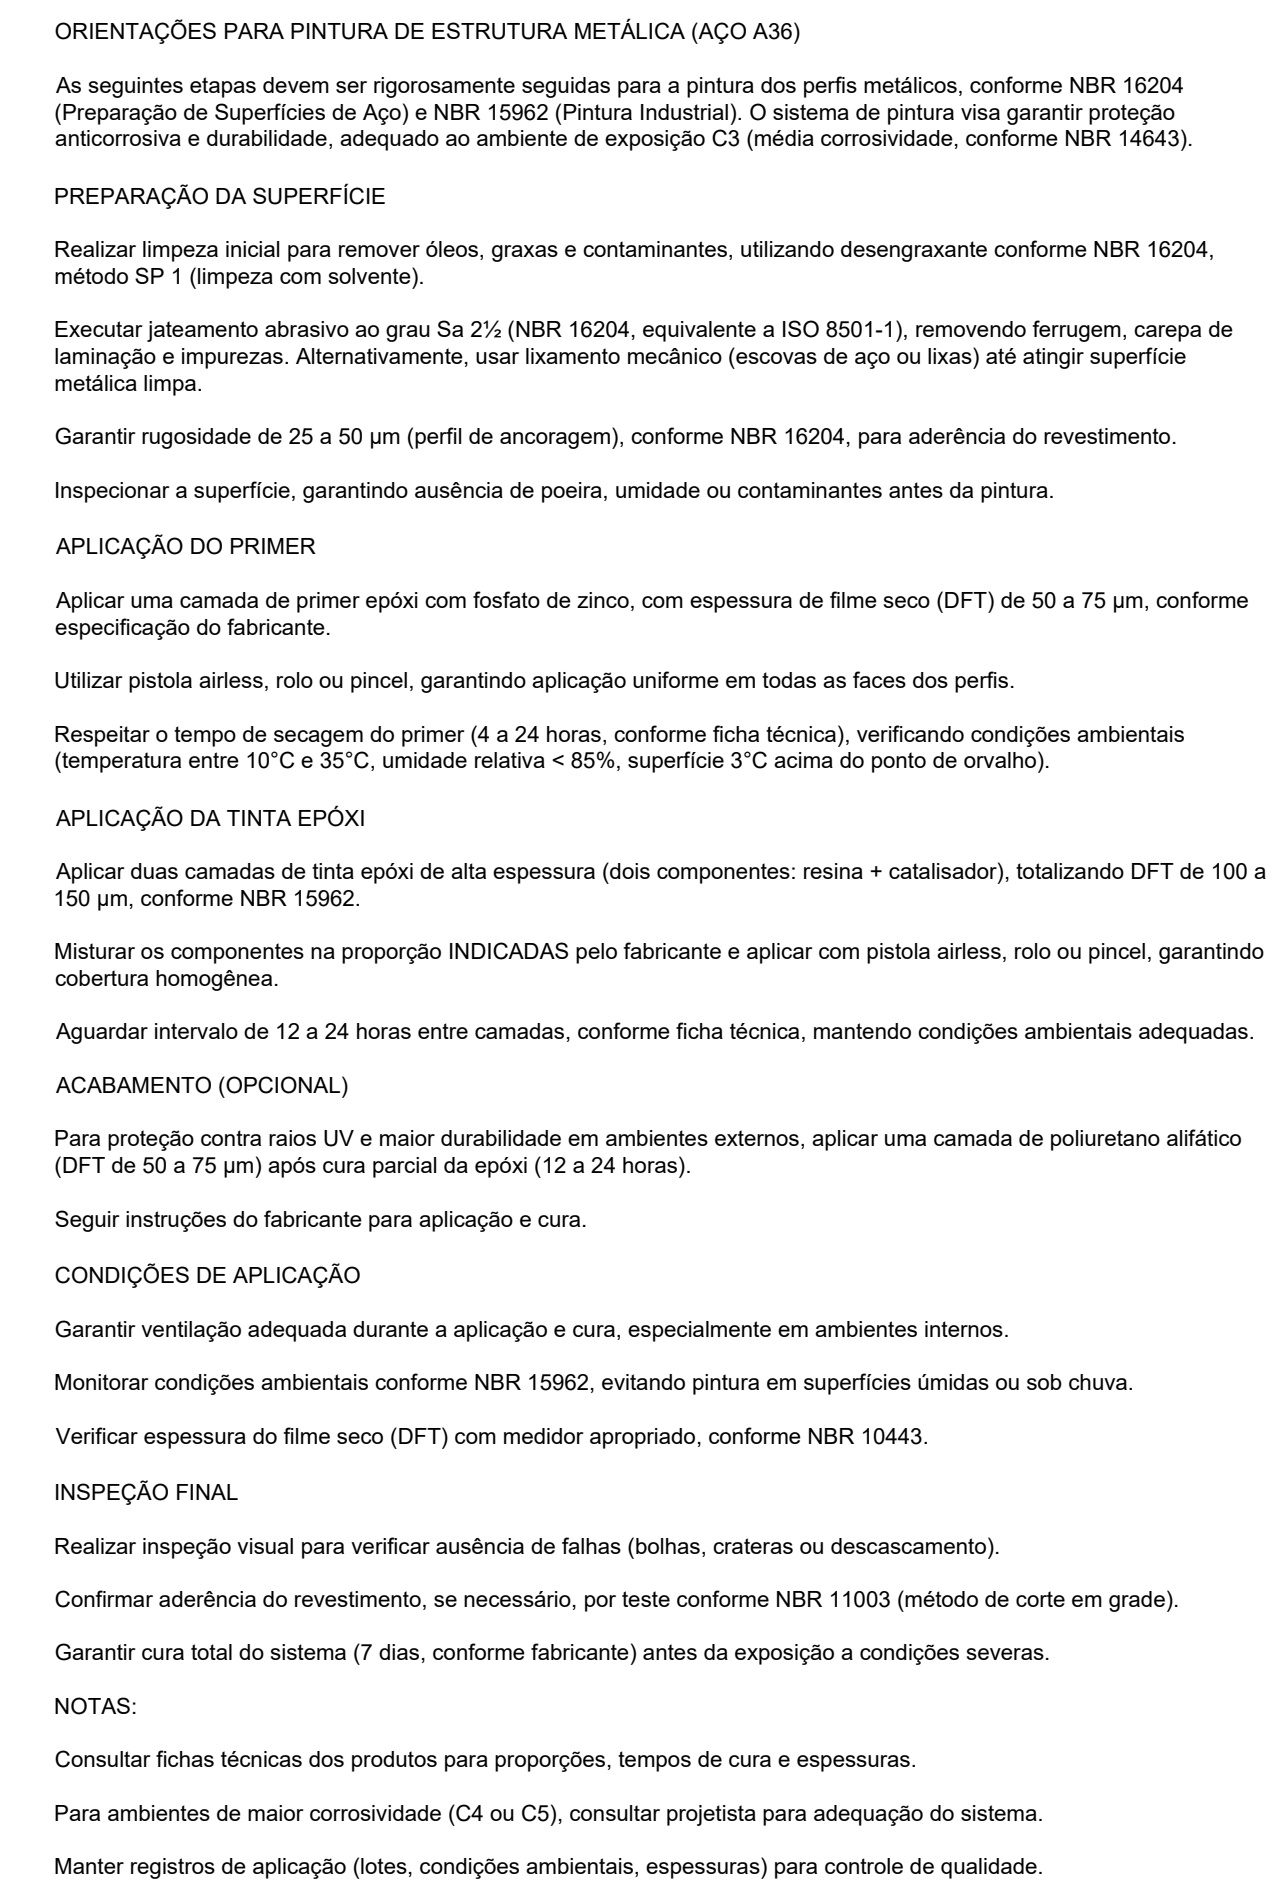

Cargas consideradas em projeto:

- Peso próprio da telha: 4,5 kgf/m²;
- Peso próprio de instalações elétricas e luminárias: 0,21 kgf/m²;
- Forro: NÃO INCLUSO

SAPATAS IDEIAIS: ESSE PROJETO ESTRUTURAL FOI CONCEBIDO IDEALIZANDO QUE EXISTEM FUNDAÇÕES PARA OS 12 PILARES QUE SERÃO REFORÇADOS, COM ARMAÇÕES, FCK E DIMENSÕES SEMELHANTES AO MOSTRADO ABAIXO, CASO CONTRÁRIO, FAZ-SE NECESSÁRIO DEMOLIÇÃO E RECONSTRUÇÃO DAS FUNDAÇÕES E DOS PILARES


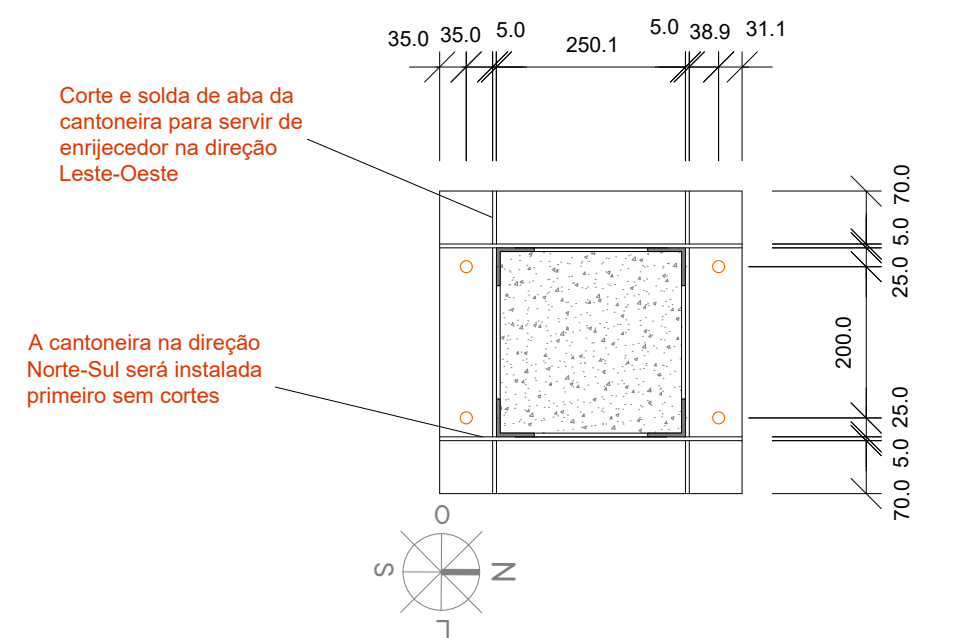


Diagrama de uma viga de concreto armado com uma junta de reparo. A viga é mostrada em seção transversal e longitudinal. A junta é feita com uma barra de aço (chumbador) de Ø16 mm, SAE 1020, fixada com cola epóxi (Vesedit, Quartzolit ou similar). A resistência média do adesivo é $f_{bk} \geq 6 \text{ MPa}$. A espessura da camada de cola é de 20,0 mm. A resistência do concreto leveado é considerada no cálculo como 20 MPa. A cantoneira 75x75x5 servirá como chapa de base.

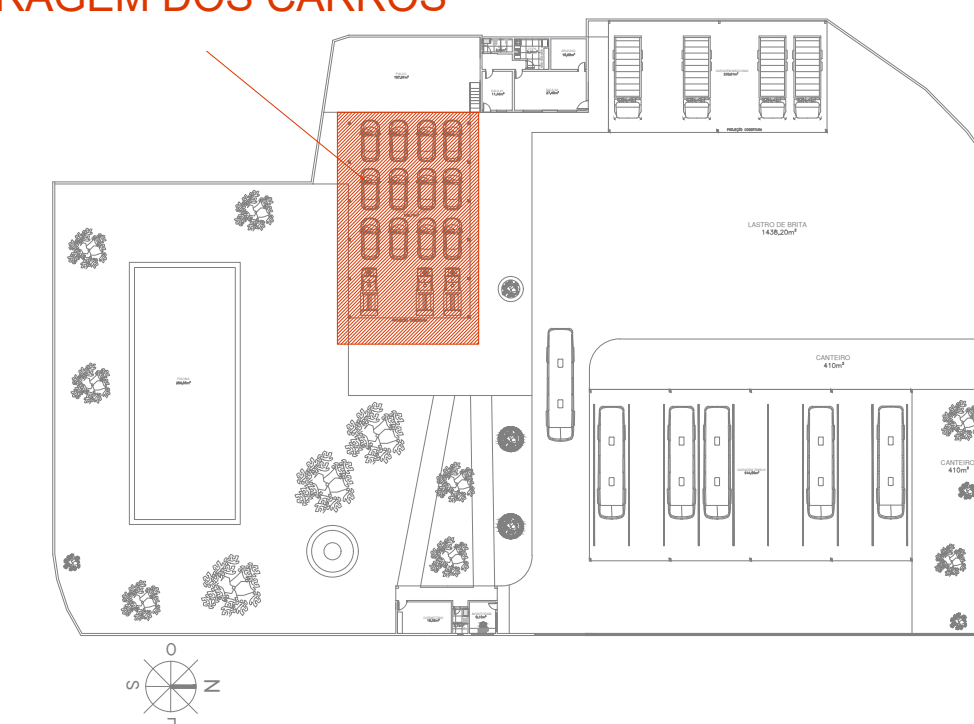

Detalhe Isométrico do Pilar com terças


PROPRIETÁRIO: PREFEITURA MUNICIPAL DE COREMAS - PB

LINCOLN CARTAXO DE LIRA Assinado de forma digital por LINCOLN
JUNIOR:06897861405 CARTAXO DE LIRA JUNIOR:06897861405
Dados: 2025.08.11 13:51:57 -03'00'

PROJETO: LINCOLN CARTAXO DE LIRA JÚNIOR CREA 160.814-689-8

CONSTRUÇÃO: PROJETO DE REFORMA - GARAGEM DE CARROS




FOLHA		PROJETO: PROJETO DE REFORMA - GARAGEM DE CARROS			
01/03		LOCALIDADE: MUNICÍPIO DE COREMAS - PB			
	DATA	RESPONSÁVEL	RUBRICA	DADOS	
DESENHO	JUN/2025	LINCOLN CARTAXO			
CÓPIA					
VERED					
ESCALAS	DESENHOS			CONVÊNIO	
INDICADAS	- Planta de Locação da Garagem dos carros - Detalhe para conferência comparativa da fundação existente com a idealizada - Detalhe de chapa base e chumbamento - Planta de situação			ARQUIVO	

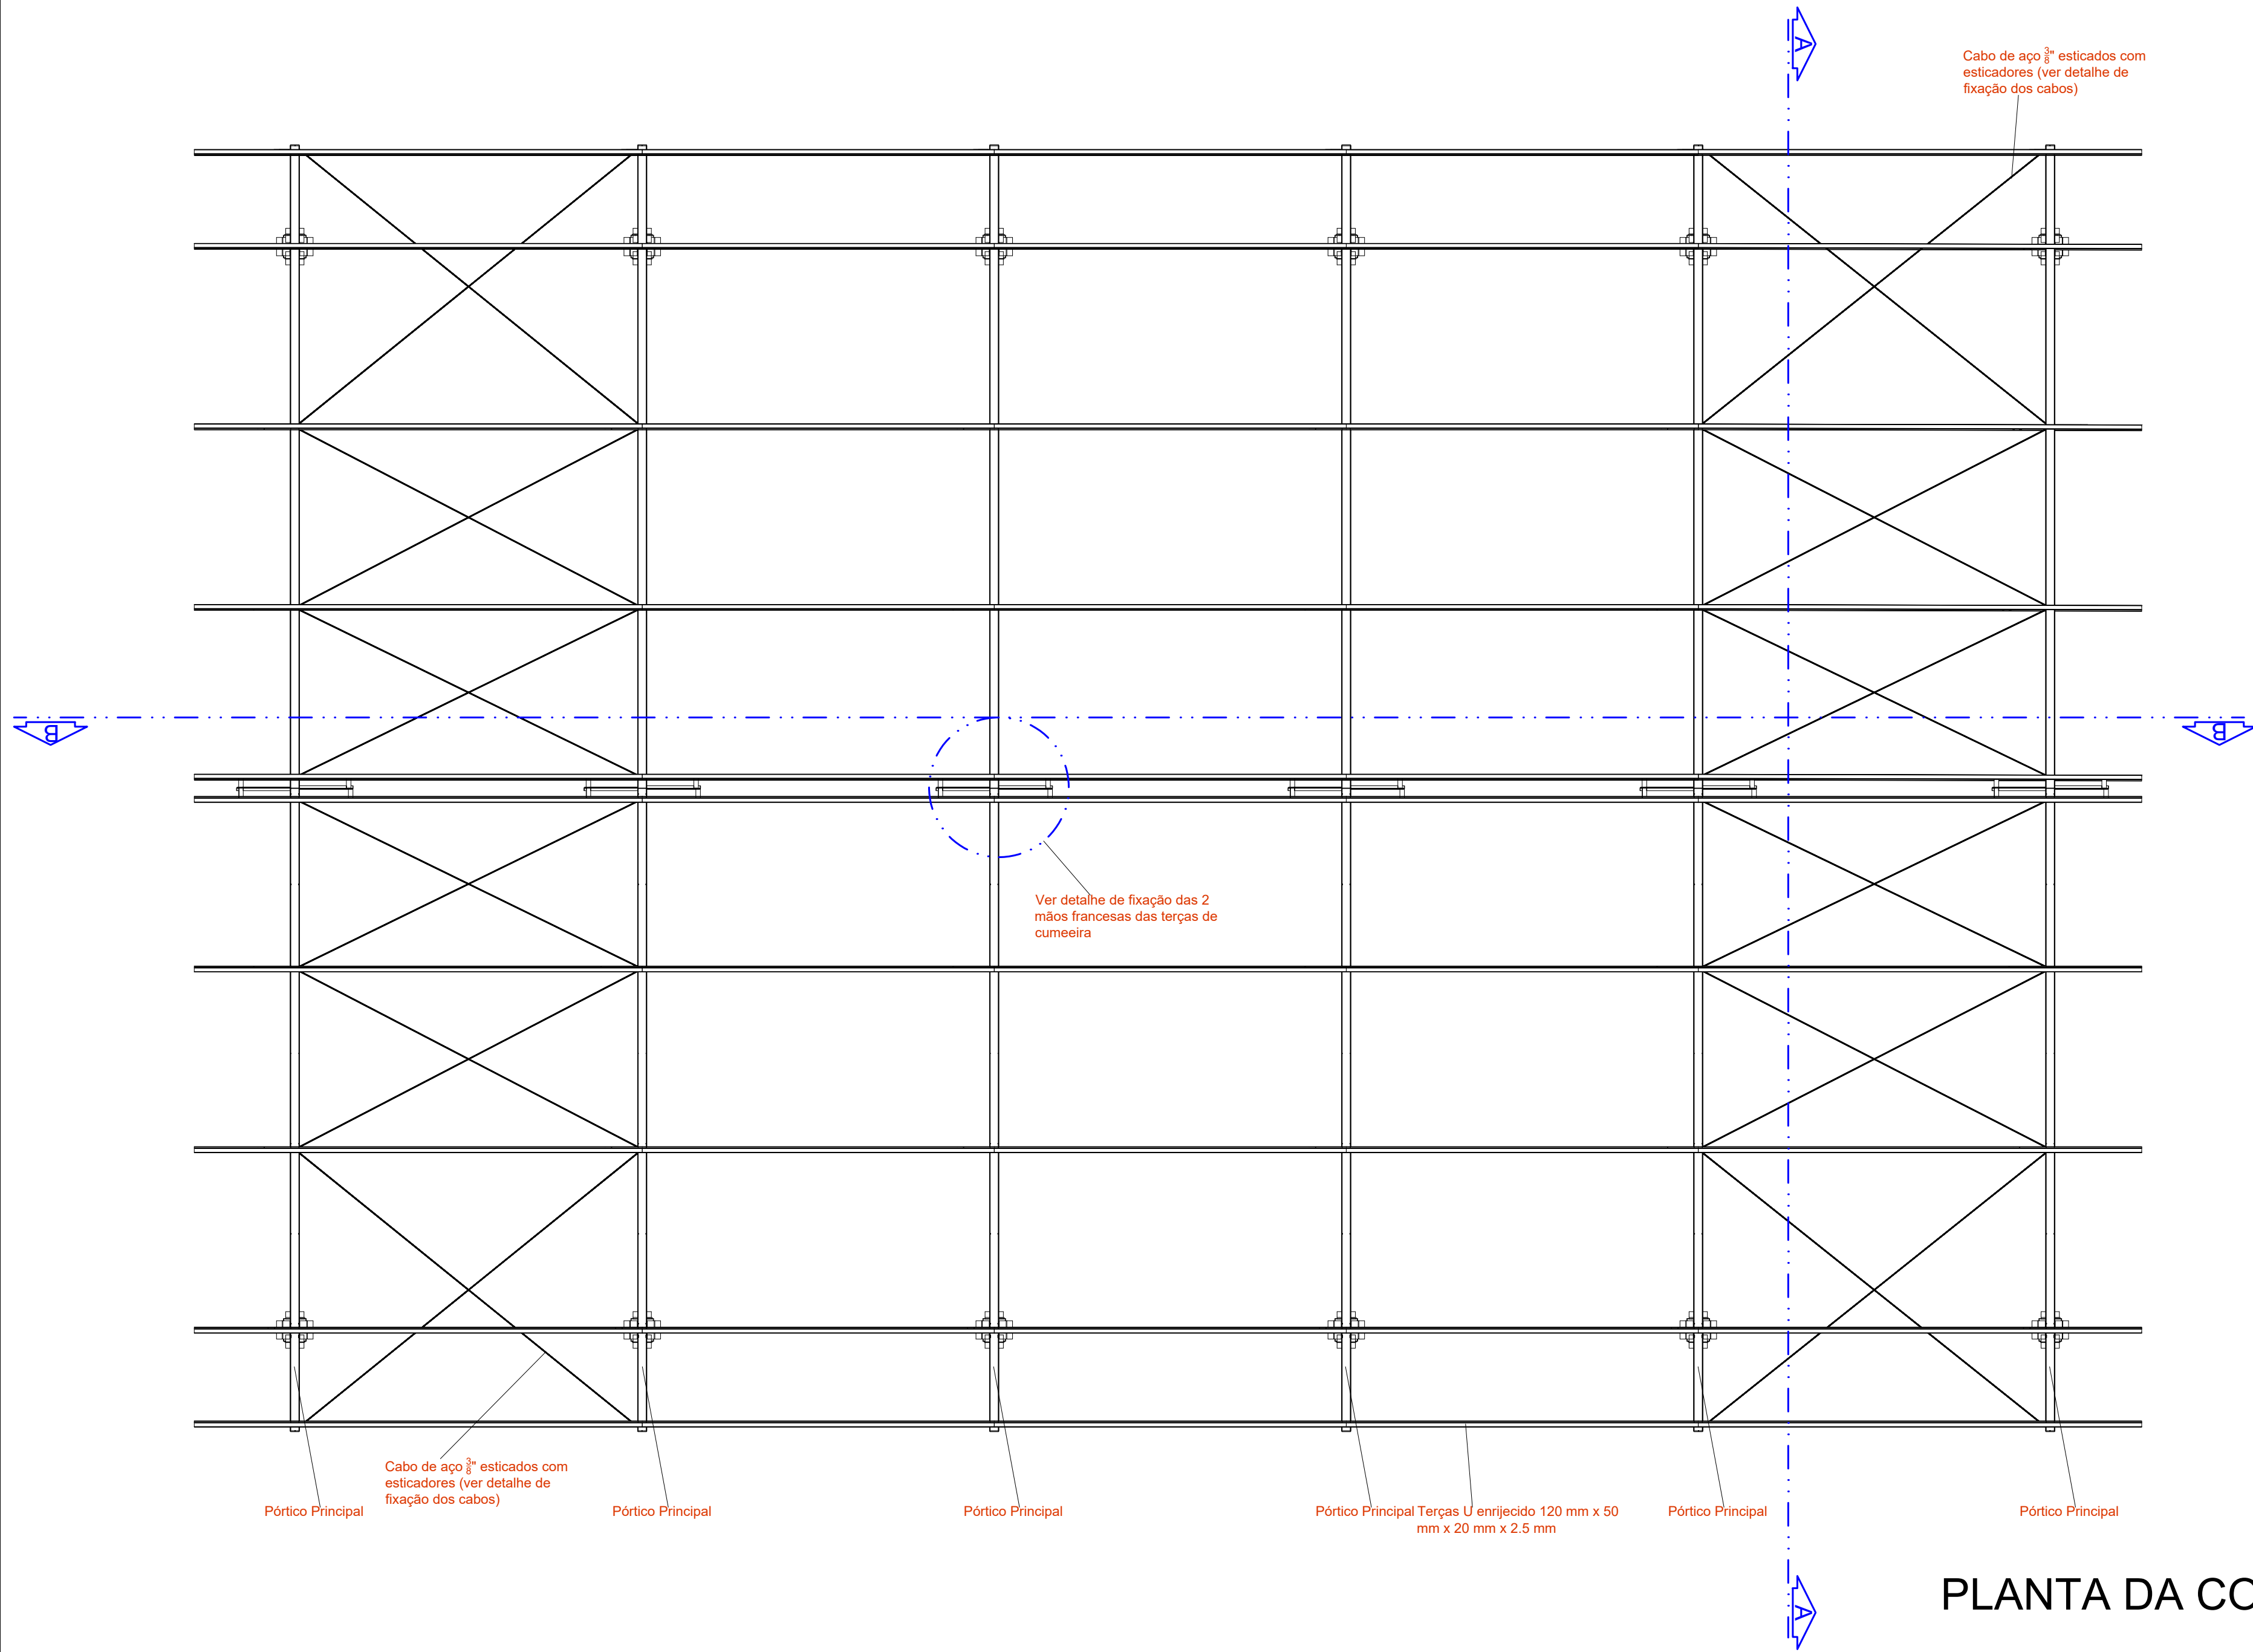

DETALHE DE FIXAÇÃO DOS CABOS

ESC 1:10

Comprimentos mínimos de Filetes de Soldas paralelos ao perfil:			
Peça	Tipo de Solda	Perna (mm)	Comprimento MÍNIMO
Diagonal 2xL em Banzo	Eletrodo E70 18	6 mm	2 x 6 cm (Em cada Cant.)
Montante 2xL em Banzo	Eletrodo E70 18	6 mm	2 x 3 cm (Em cada Cant.)

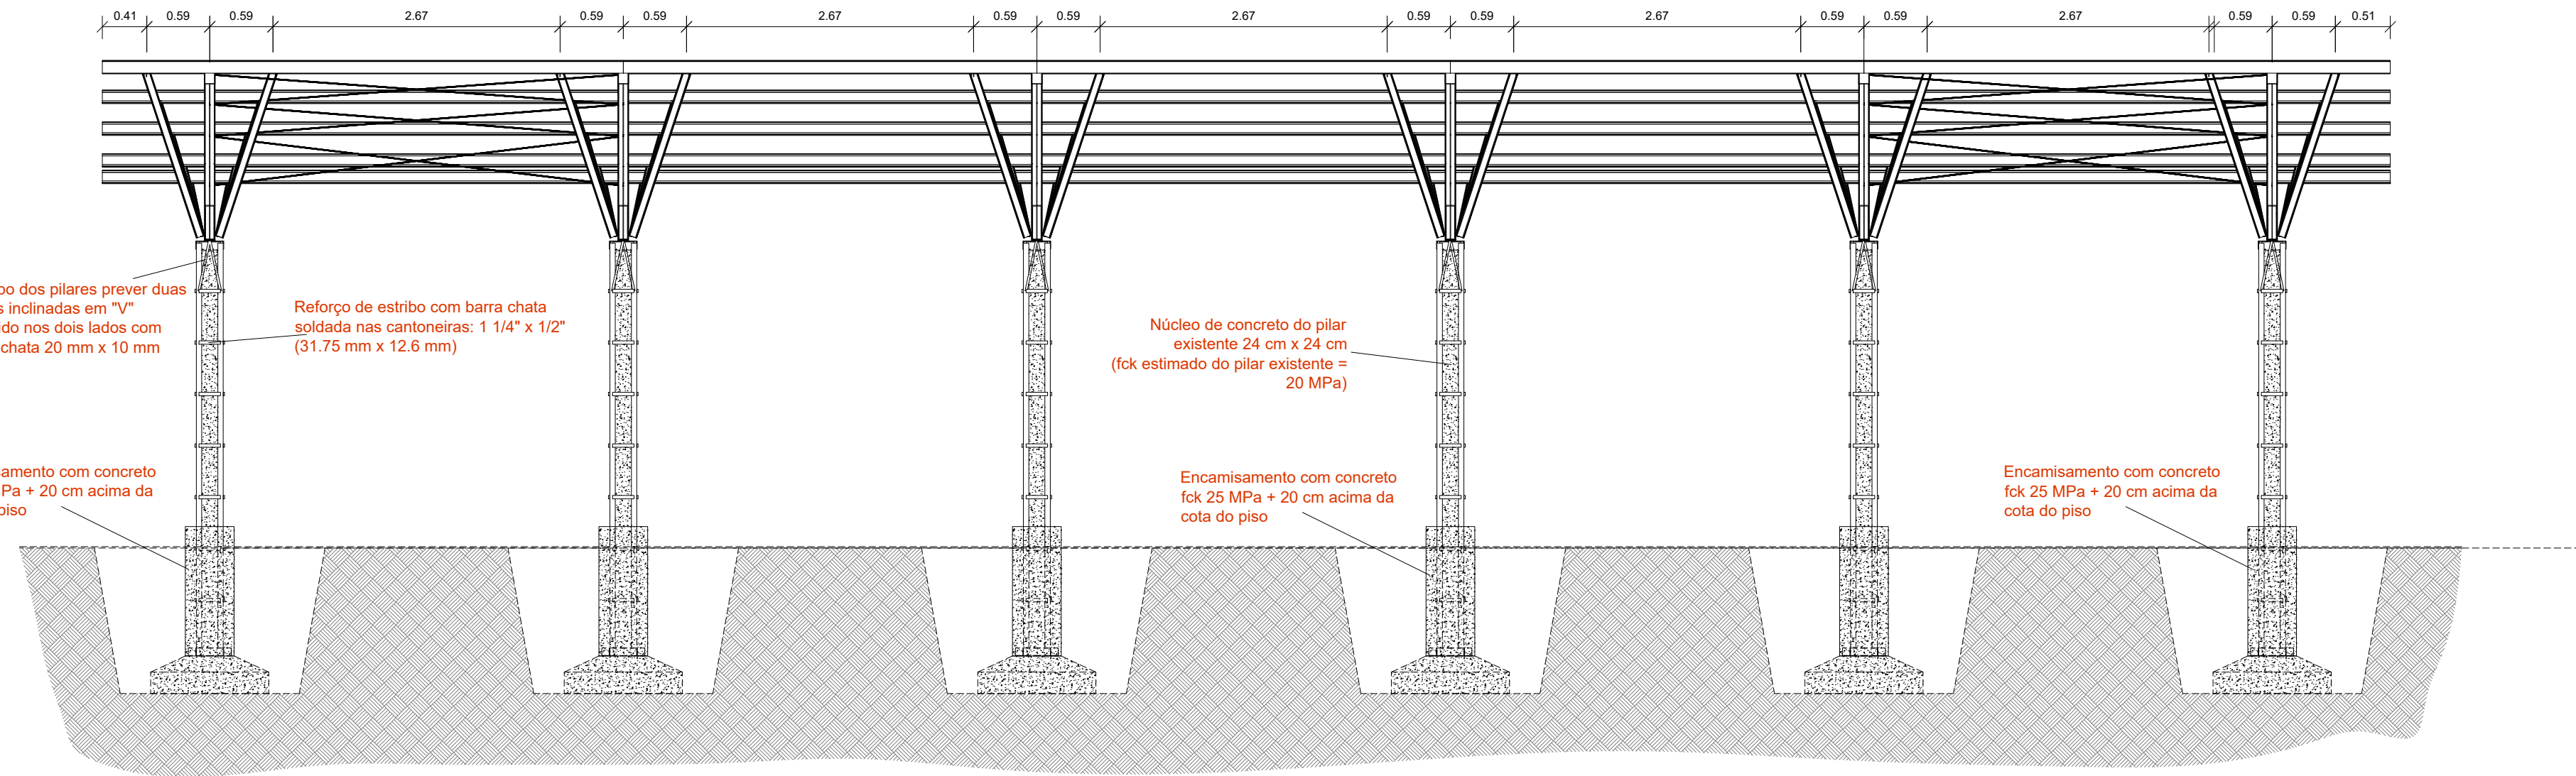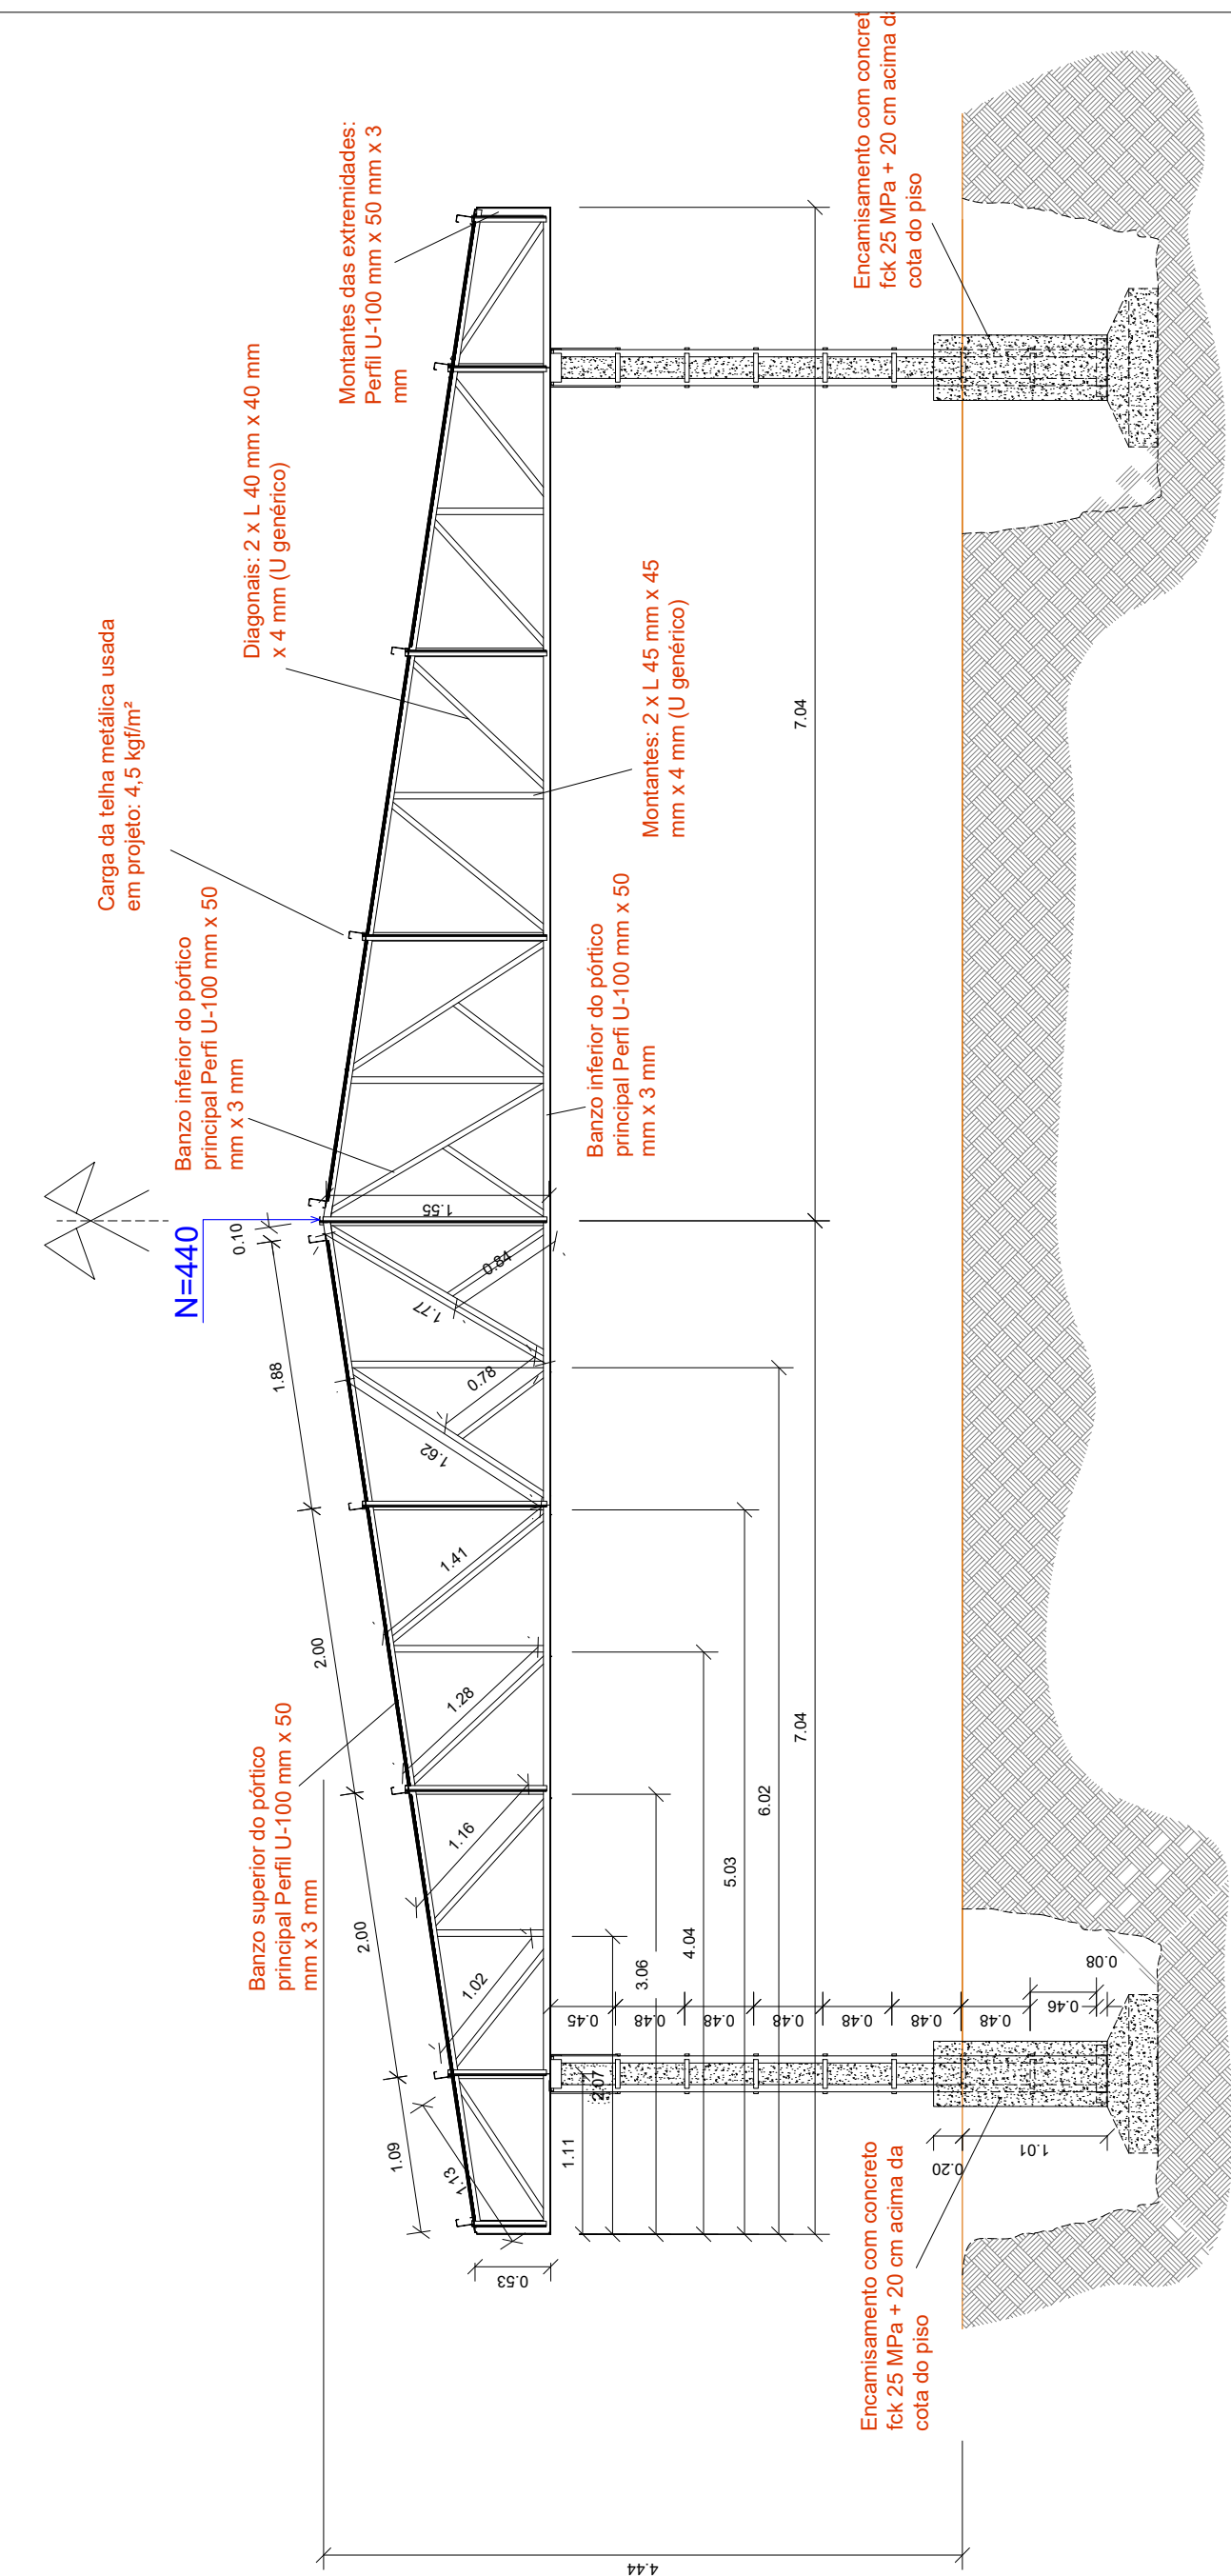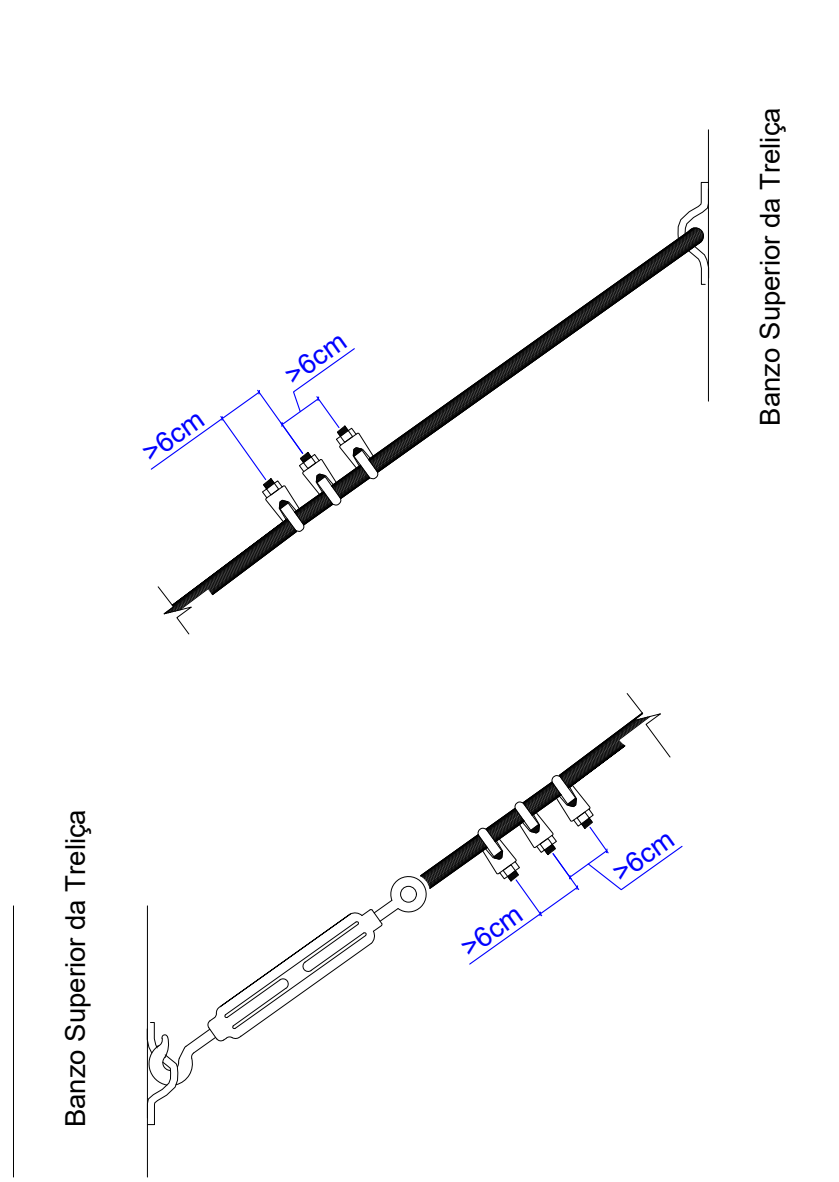

Mãos francesas das terças: 2 perfis em "V", Perfil U 80 mm x 40 mm x 5 mm


Apoio das 2 terças de cumeeira: Cantoneira L 50 mm x 50 mm x 5mm

DETALHE DE FIXAÇÃO DAS 2 MÃOS FRANCESAS DAS TERÇAS DE CUMEEIRA

S/ ESC

PROPRIETÁRIO: PREFEITURA MUNICIPAL DE COREMAS - PB			
LINCOLN CARTAXO DE LIRA JÚNIOR:06897861405		Assinado de forma digital por LINCOLN CARTAXO DE LIRA JÚNIOR:06897861405 Dados: 2025.08.11 13:52:57 -03'00'	
PROJETO: LINCOLN CARTAXO DE LIRA JÚNIOR CREA 160.814.689-B			
CONSTRUÇÃO: PROJETO DE REFORMA - GARAGEM DE CARROS			
FOLHA	PROJETO:	PROJETO DE REFORMA - GARAGEM DE CARROS	
02/03	LOCALIDADE:	MUNICÍPIO DE COREMAS - PB	
DATA	RESPONSÁVEL	RUBRICA	DADOS
DESIGNO	JUN 2025	LINCOLN CARTAXO	
CÓPIA			
VIETO			
ESCALAS	DESENHOS	CONVÊNIO	
INDICADAS	- PLANTA DE COBERTA - CORTE AA - CORTE BB - DETALHE DE FIXAÇÃO DAS 2 MÃOS FRANCESAS DAS TERÇAS DE CUMEEIRA	ARQUIVO	
Aprovações:			
LCL PROJETOS			
Av. Monteiro da França, 160, II. 030A Maracá, 35050-320 - João Pessoa (PB) Tel: +55 (81) 99654 4447 e-mail: lclprojetos@gmail.com			

Mãos francesas das terças: 2 perfis em
Perfil U 80 mm x 40 mm x 5 mm (Estão
em todos os apoios TERÇAS - BANZO)

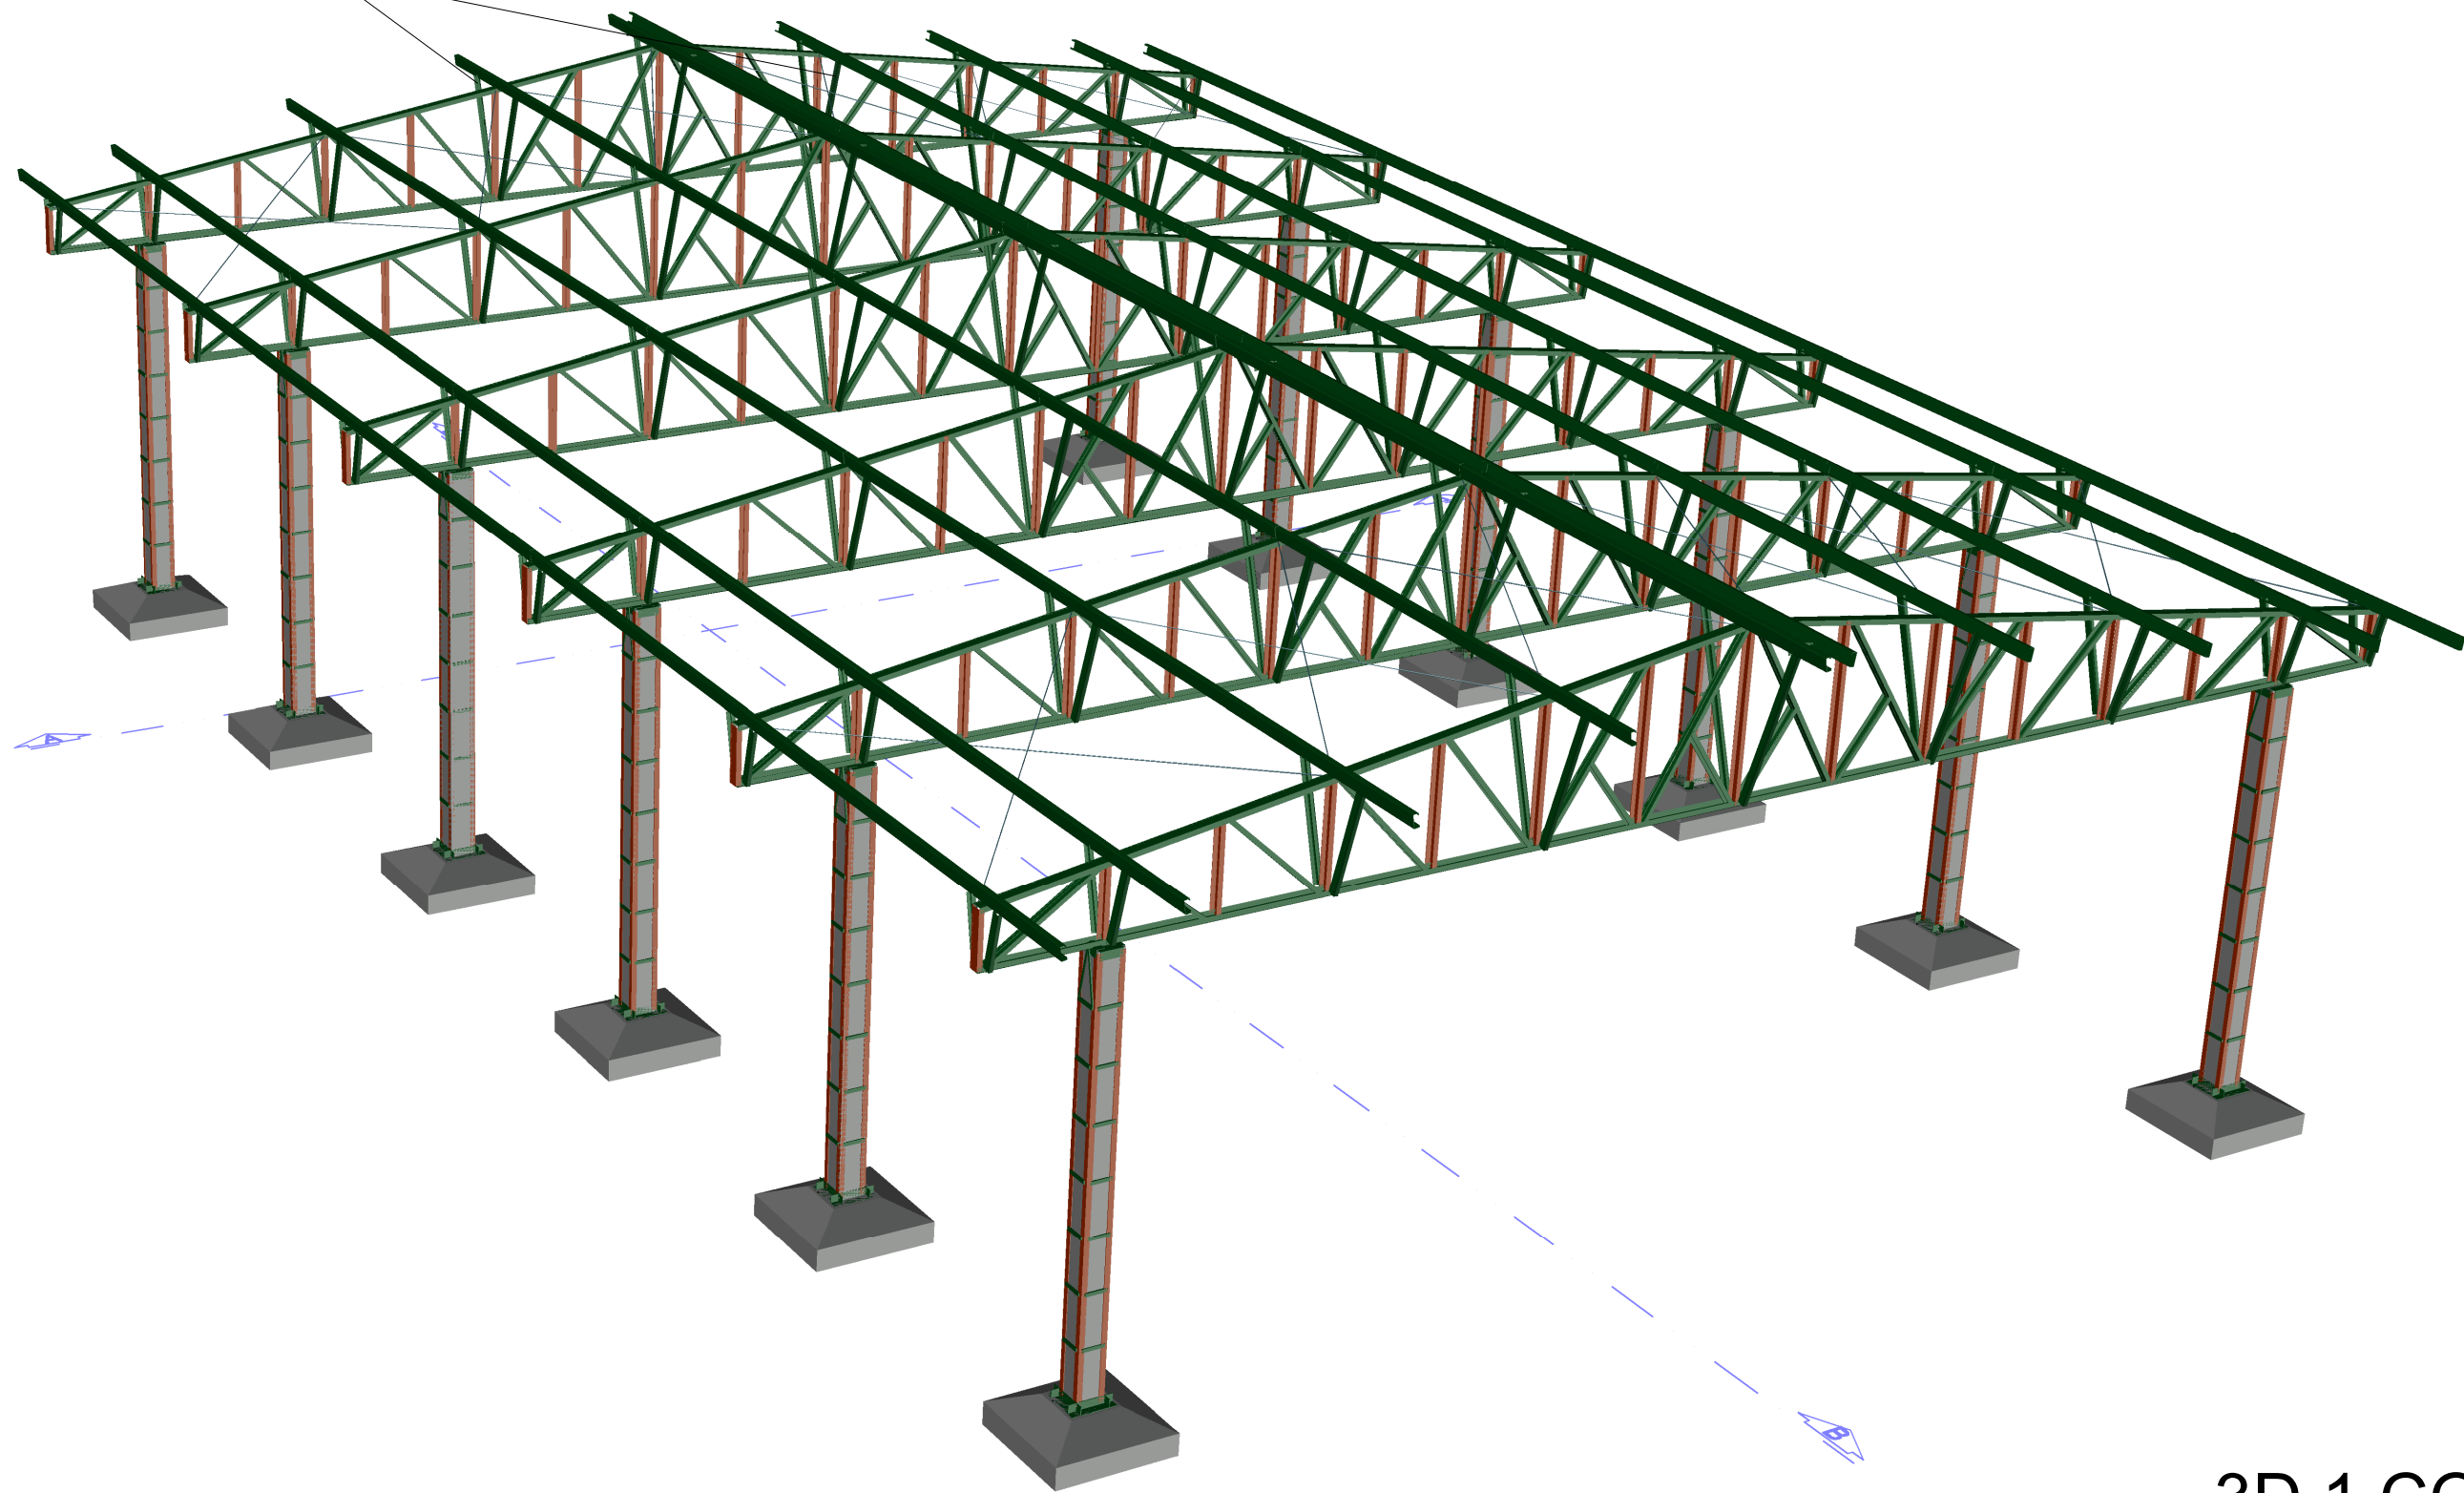


3D 1 COBERTA
ESC 1:50

1.1.1.5.- Tabela resumo

Tabela resumo																
Material		Série	Perfil	Comprimento			Volume			Peso						
Tipo	Designação			Perfil	Série	Material	(m)	Perfil	Série	Material	(m³)	Perfil	Série	Material	(kg)	(kg)
Aço laminado	A-36 250Mpa	L	L 50 x 50 x 5		186.528		0.090				702.84					
			L 75 x 75 x 5		19.200		0.014				110.63					
			L 45 x 45 x 4, Duplo U união genérica		83.865		0.059				459.52					
			L 40 x 40 x 4, Duplo U união genérica		136.694		0.084				661.00					
		Flat bars	FL 1 1/4" x 1/2" (31.75 mm x 12.6 mm)		67.200	426.287		0.027	0.246		212.71	1933.98				
			FL 20 x 10		23.535		0.005				36.95					
		Cabo de Aço	Cabo de Aço 3/8"		108.042	90.735		0.032		0.008	60.43	249.66				
						108.042	625.063		0.008	0.286		60.43			2244.08	
		Aço dobrado	A-36	U	U-100 mm x 50 mm x 3 mm		175.543		0.100			785.66				
					UF-80x5		104.083		0.073			575.10				
Aço dobrado	A-36	C	U enrijecido -120 mm x 50 mm x 20 mm x 2.5 mm		213.000	213.000	0.130	0.130	0.303	1017.49	1017.49					
							492.626							2378.25		

1.1.1.6.- Quantitativos de superfícies

Perfis de aço: Quantitativos das superfícies a pintar					
Tipo	Série	Perfil	Superfície unitária (m²/m)	Comprimento (m)	Superfície (m²)
Aço laminado	L	L 50 x 50 x 5	0.200	186.528	37.306
		L 75 x 75 x 5	0.300	19.200	5.760
		L 45 x 45 x 4, Duplo U união genérica	0.360	83.865	30.191
		L 40 x 40 x 4, Duplo U união genérica	0.320	136.694	43.742
		FL 1 1/4" x 1/2" (31.75 mm x 12.6 mm)	0.089	67.200	5.974
	Flat bars		FL 20 x 10	0.060	23.535
Cabo de Aço		Cabo de Aço 3/8"	0.030	108.042	3.233
				Subtotal	127.618
Aço dobrado	U	U-100 mm x 50 mm x 3 mm	0.386	175.543	67.775
		UF-80x5	0.292	104.083	30.345
	C	U enrijecido - 120 mm x 50 mm x 20 mm x 2.5 mm	0.492	213.000	104.762
				Subtotal	202.881
				Total	330.499

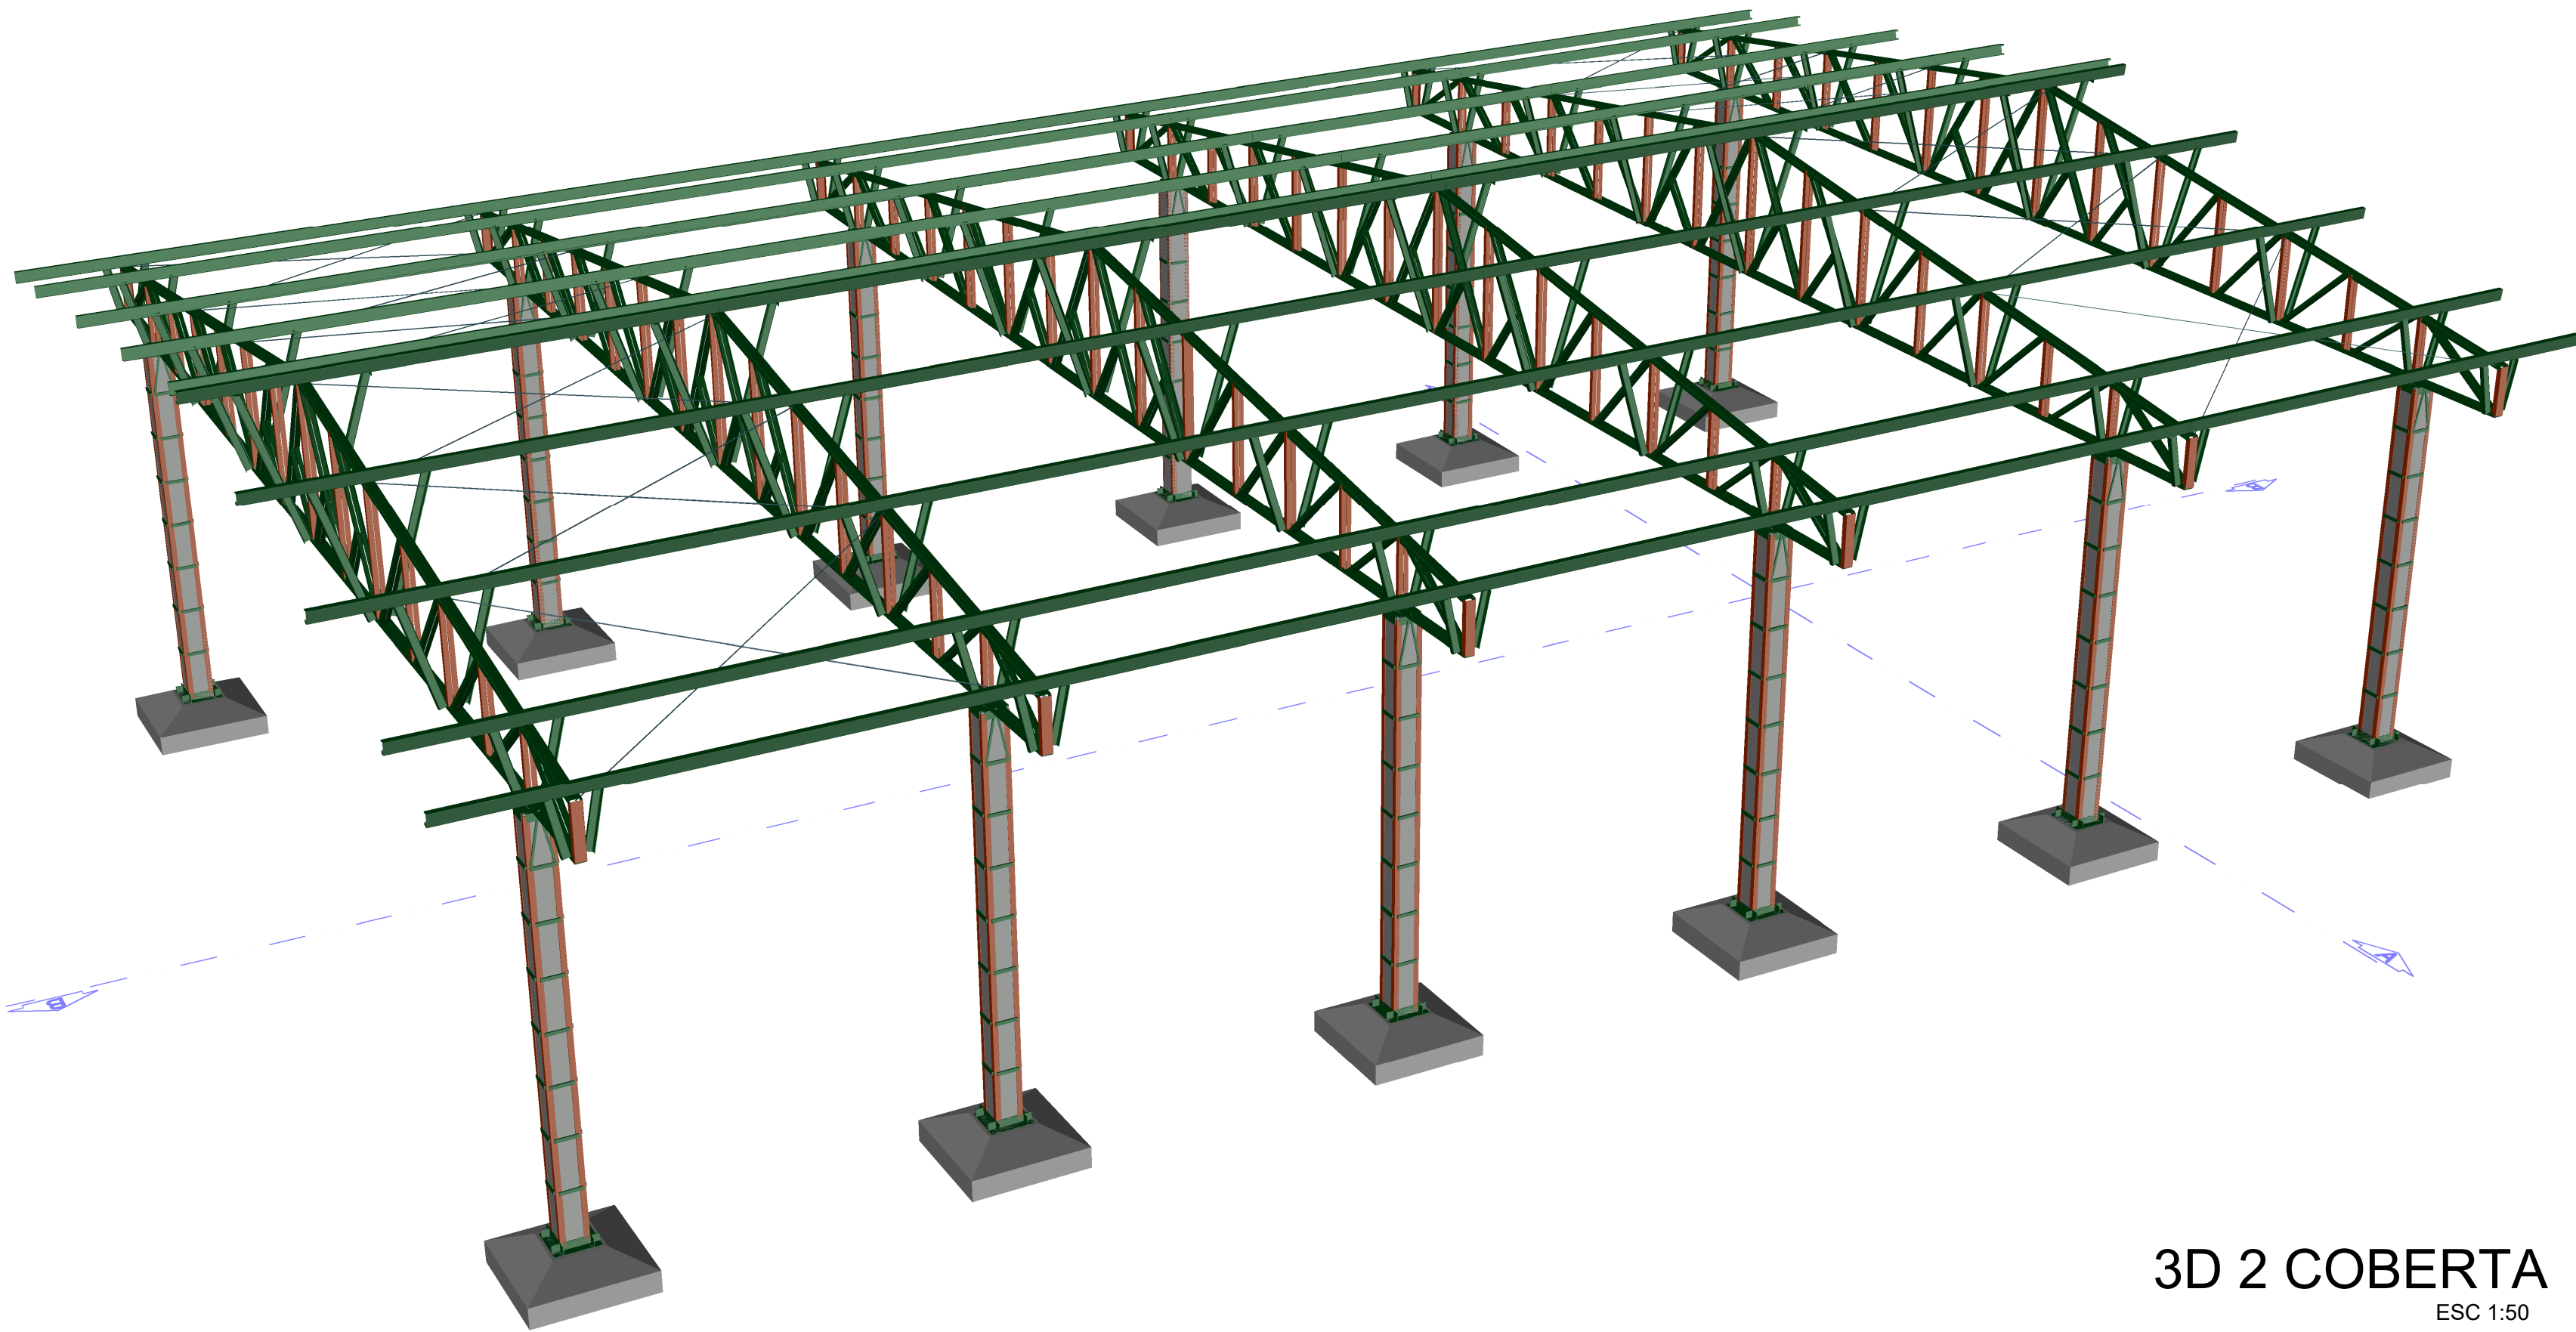

3D 2 COBERTA
ESC 1:50

PROPRIETÁRIO: PREFEITURA MUNICIPAL DE COREMAS - PB
LINCOLN CARTAXO DE LIRA JUNIOR:06897861405
Assinado de forma digital por LINCOLN CARTAXO DE LIRA JUNIOR:06897861405
Dados: 2025.08.11 13:54:09 -03'00'

PROJETO: LINCOLN CARTAXO DE LIRA JÚNIOR CREA 160.814.689-B


CONSTRUÇÃO: PROJETO DE REFORMA - GARAGEM DE CARROS

PROJETO: PROJETO DE REFORMA - GARAGEM DE CARROS


LOCALIDADE: MUNICÍPIO DE COREMAS - PB

DATA	RESPONSÁVEL	RUBRICA	DIADOS
JUN/2025	LINCOLN CARTAXO		
COPIA			
VIETO			
ESCALAS	DESENHOS	CONVÊNIO	
INDICADAS	• 3D 1 DA COBERTA		
	• 3D 2 DA COBERTA		
	• RESUMO DE MATERIAIS		
		ARQUIVO	


Aprovações:

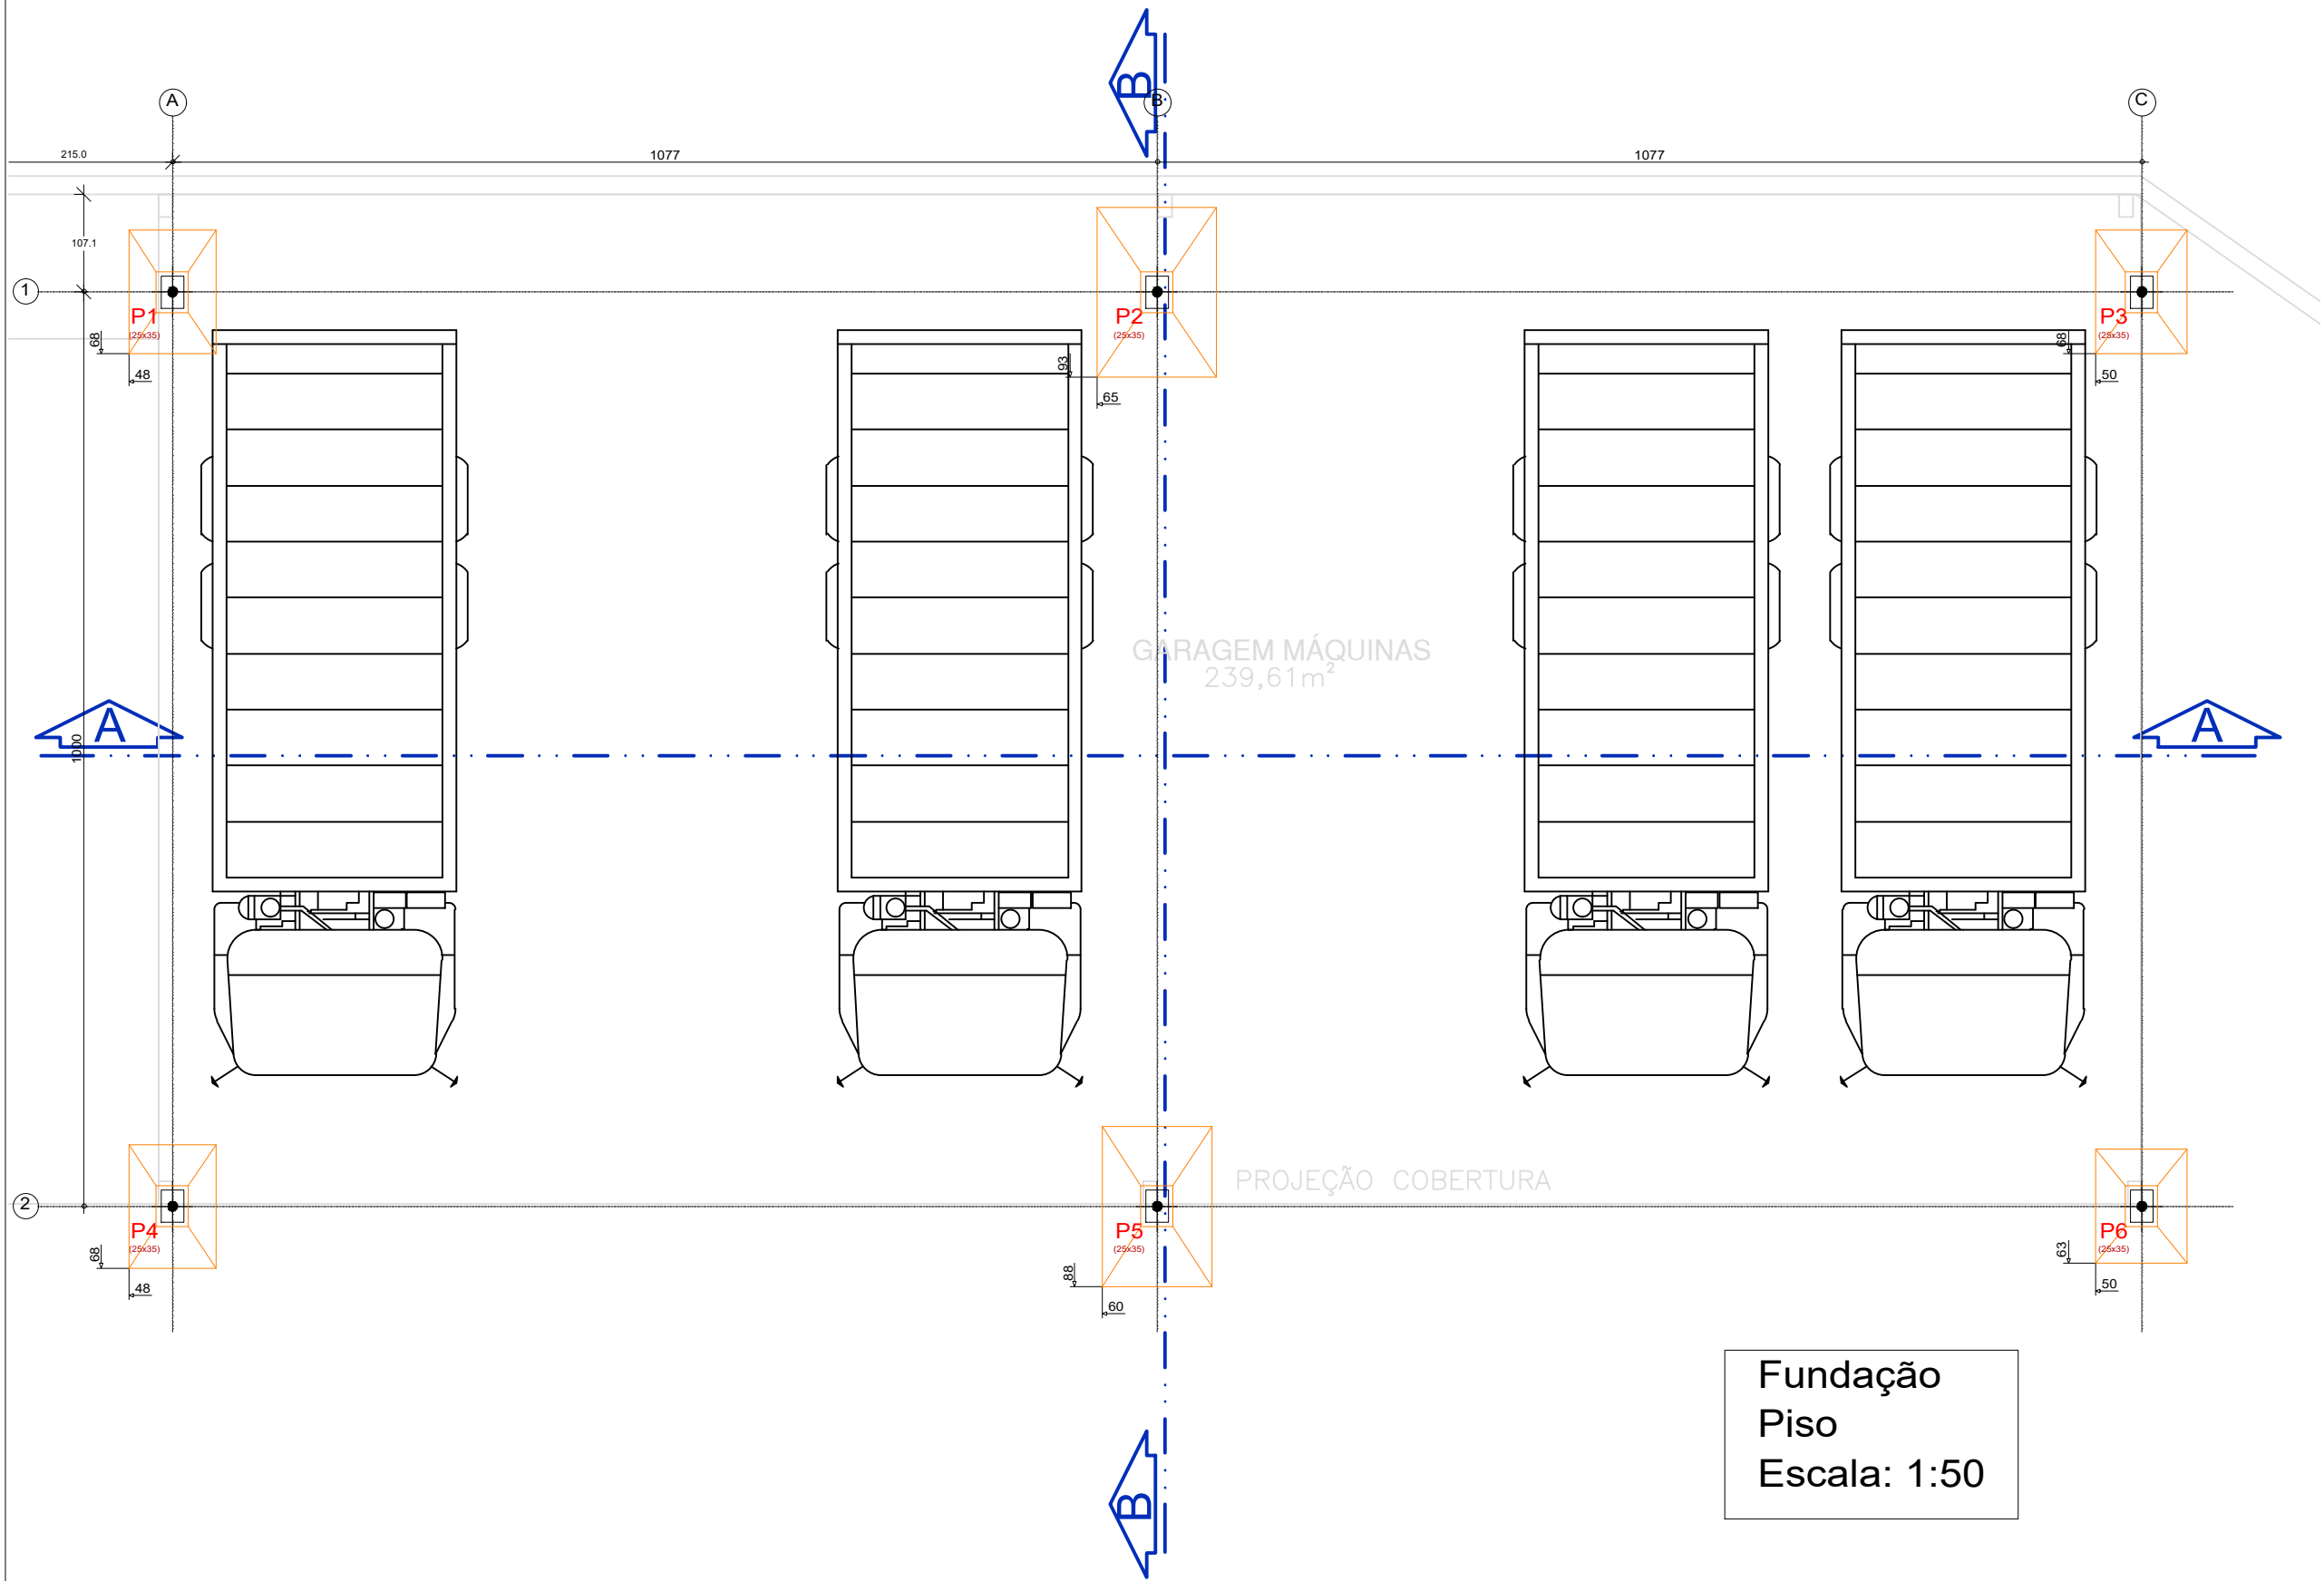


S1 e S4

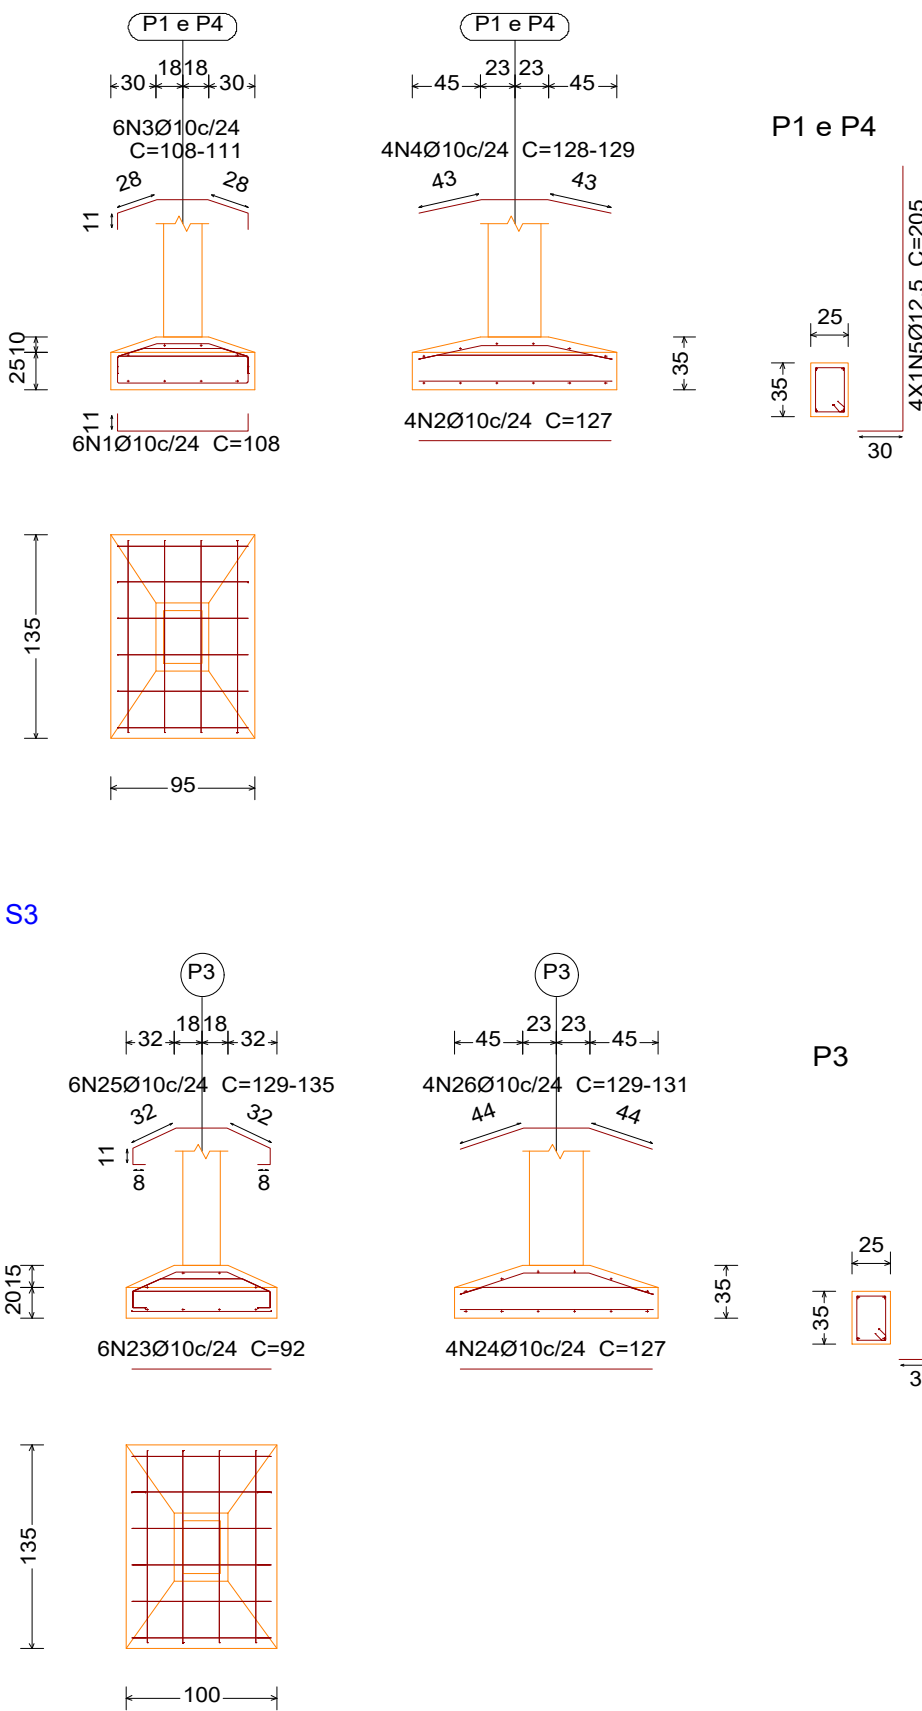


S2

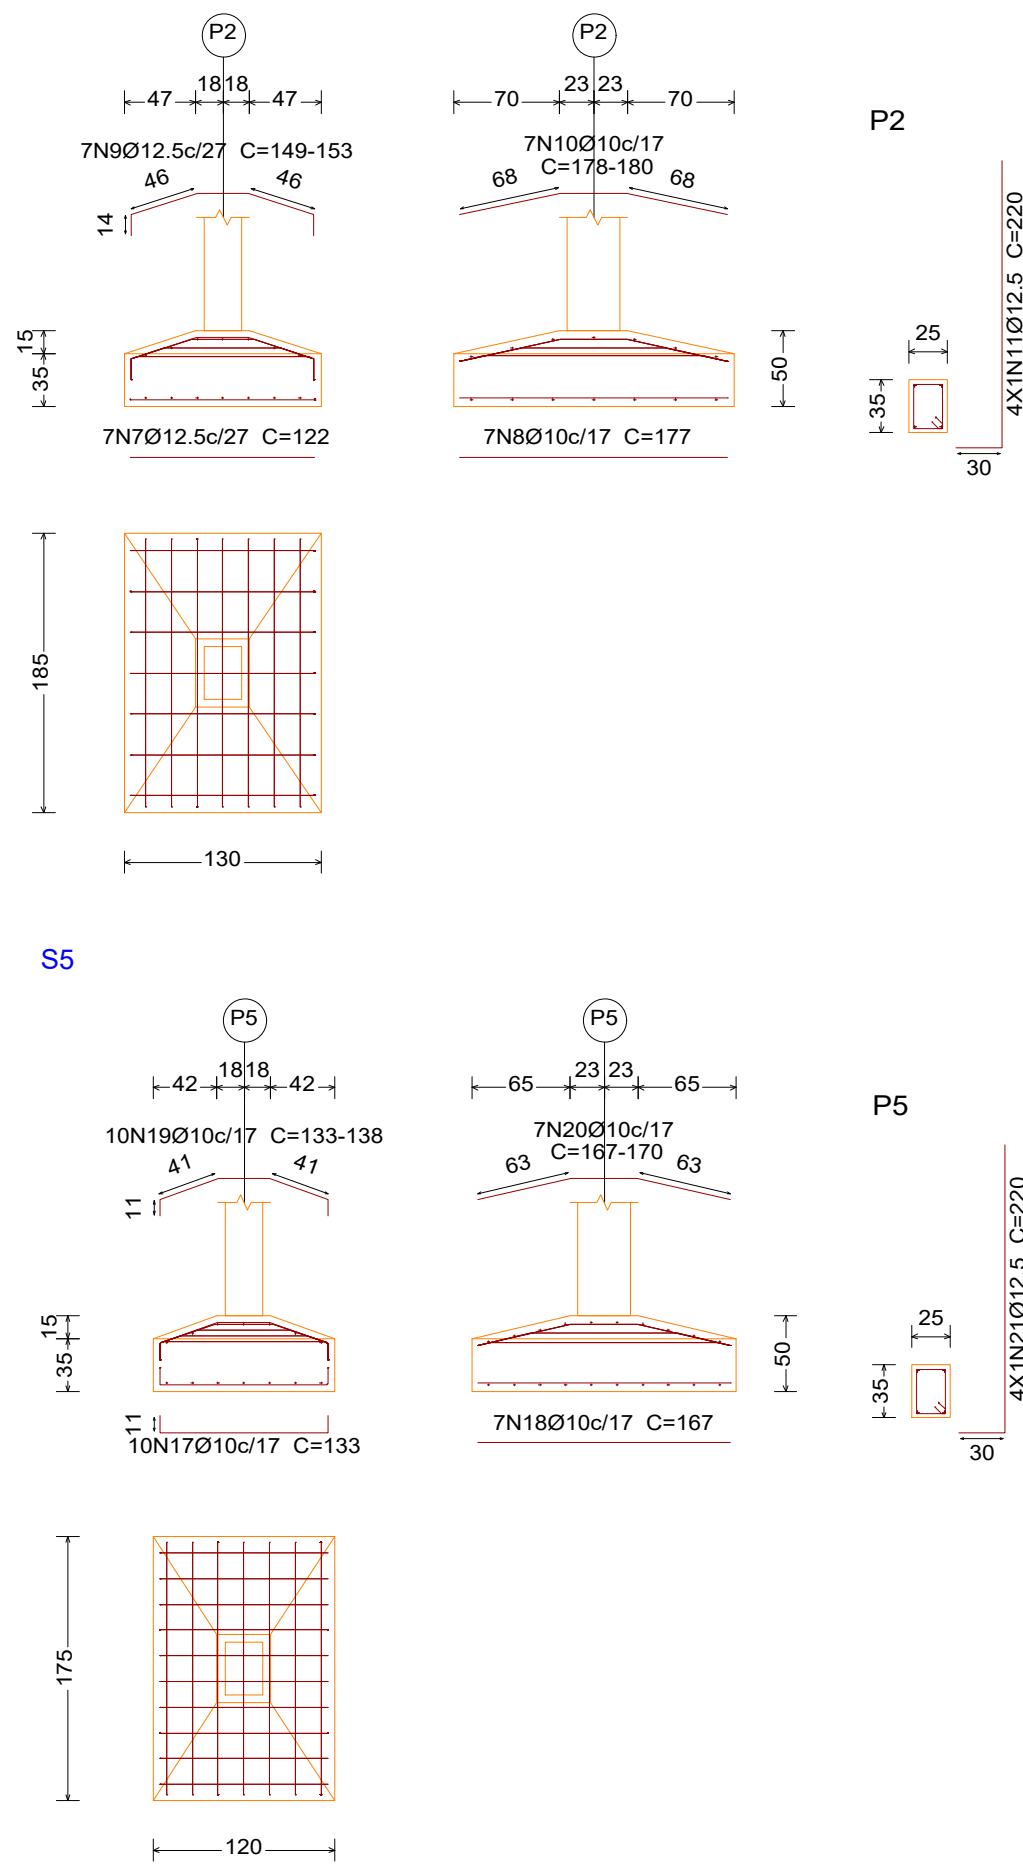


S3

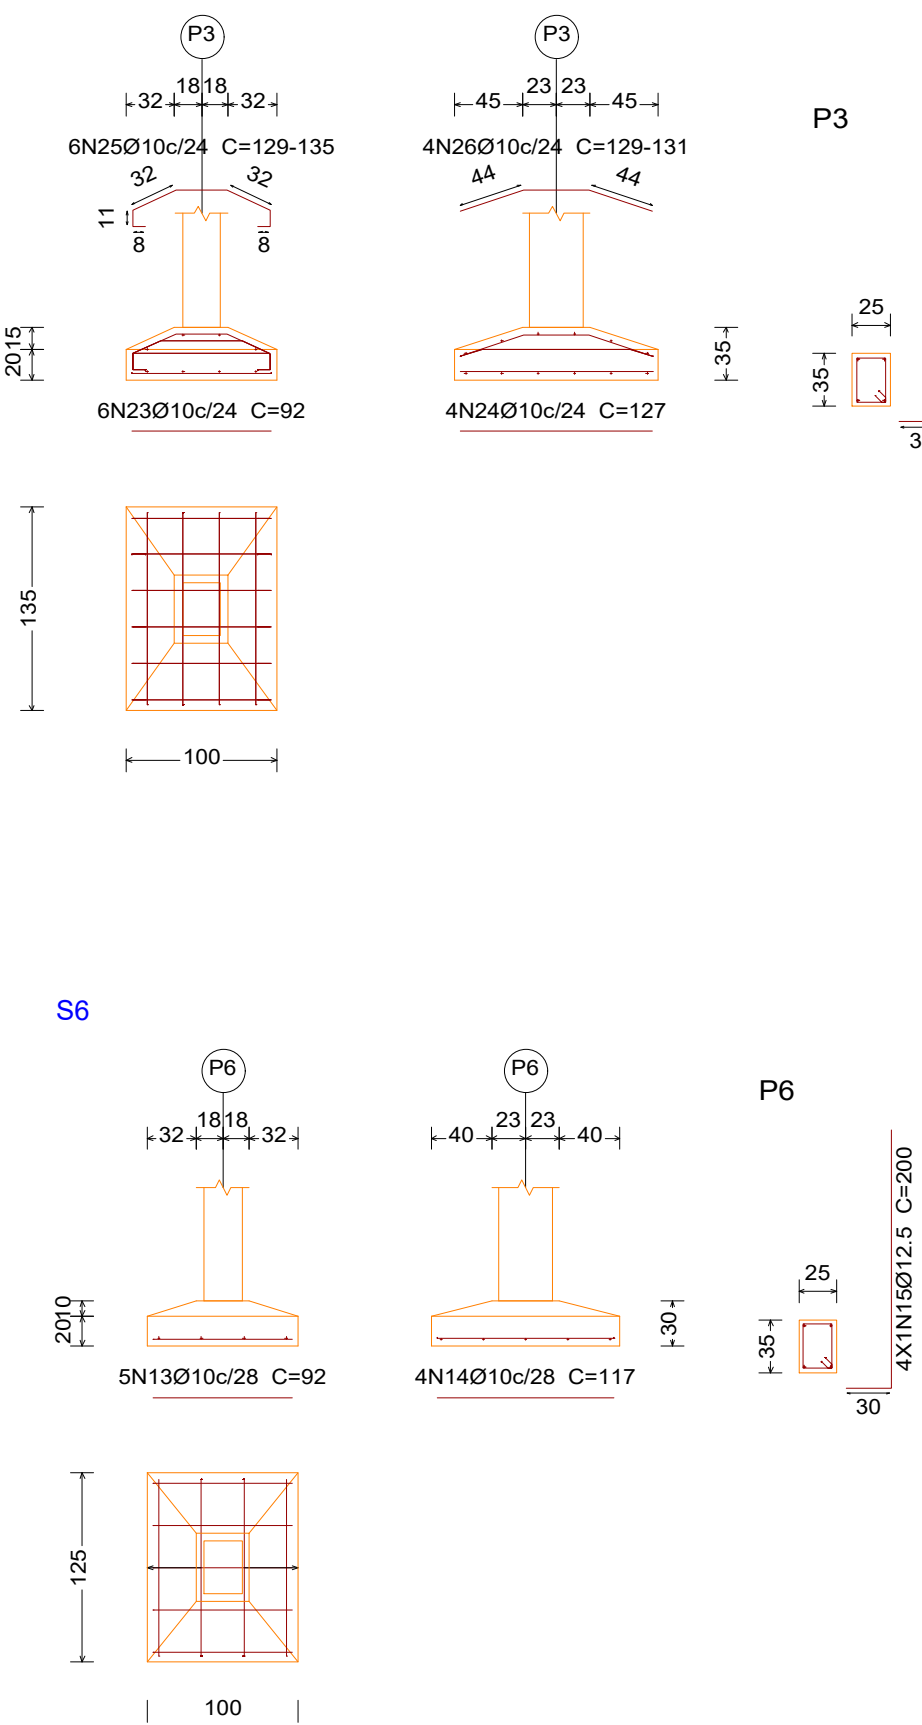





S5

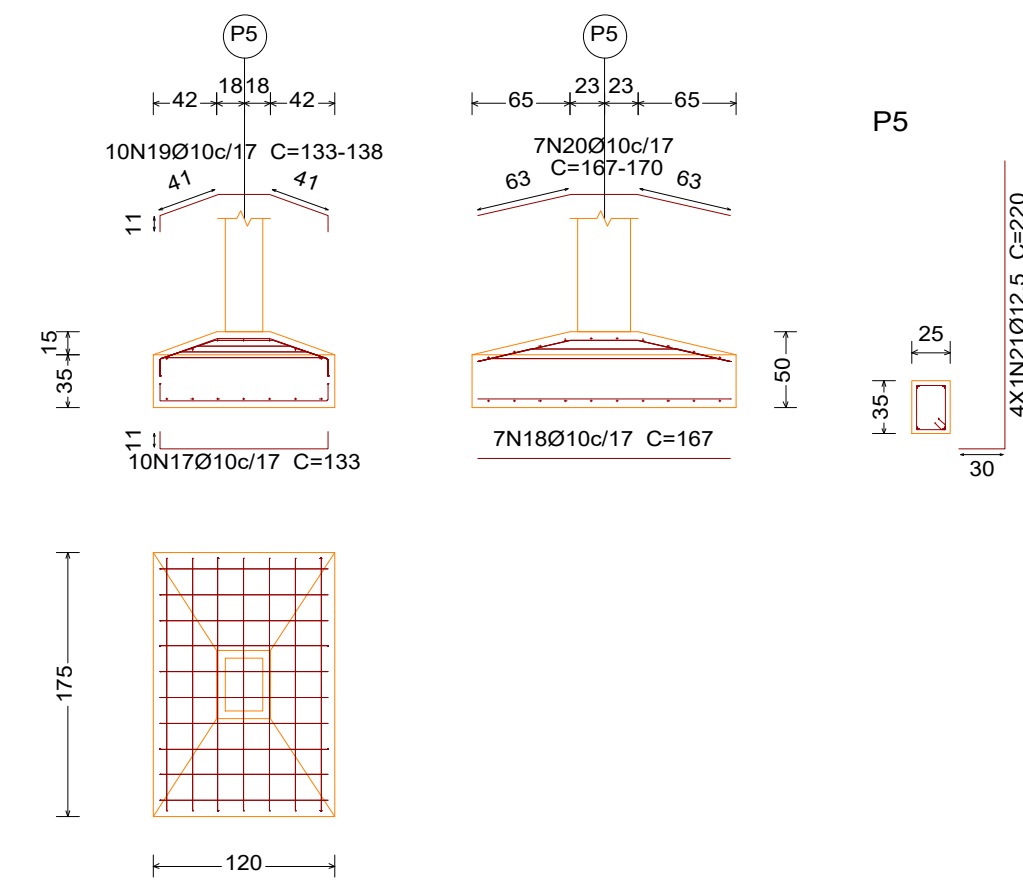

S6

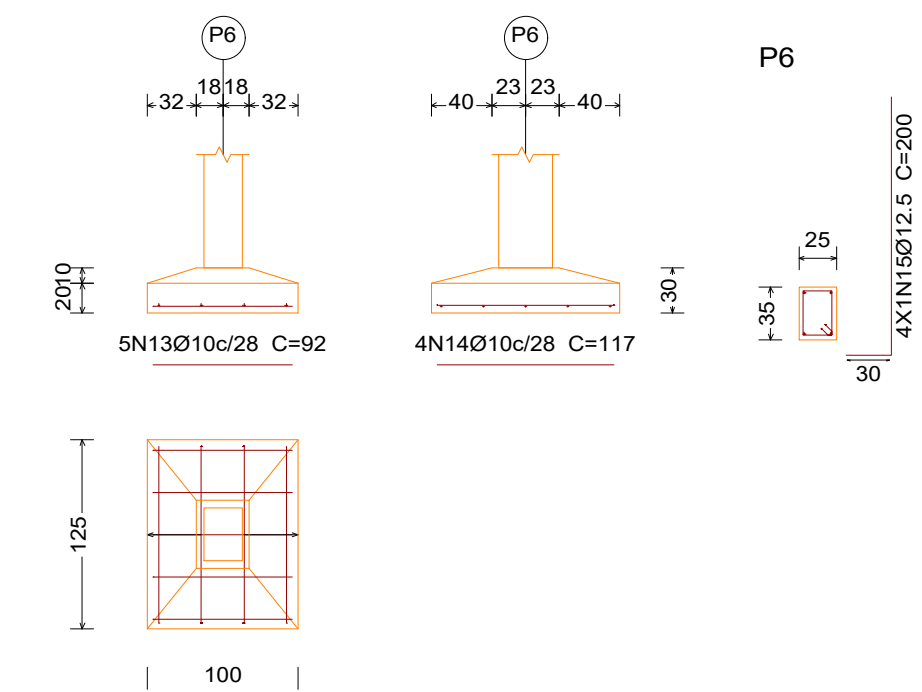


FUNDAÇÕES FORAM
DIMENSIONADAS PARA SOLO
COM TENSÃO ADMISSÍVEL
MAIOR OU IGUAL A 1.5 kgf/cm²

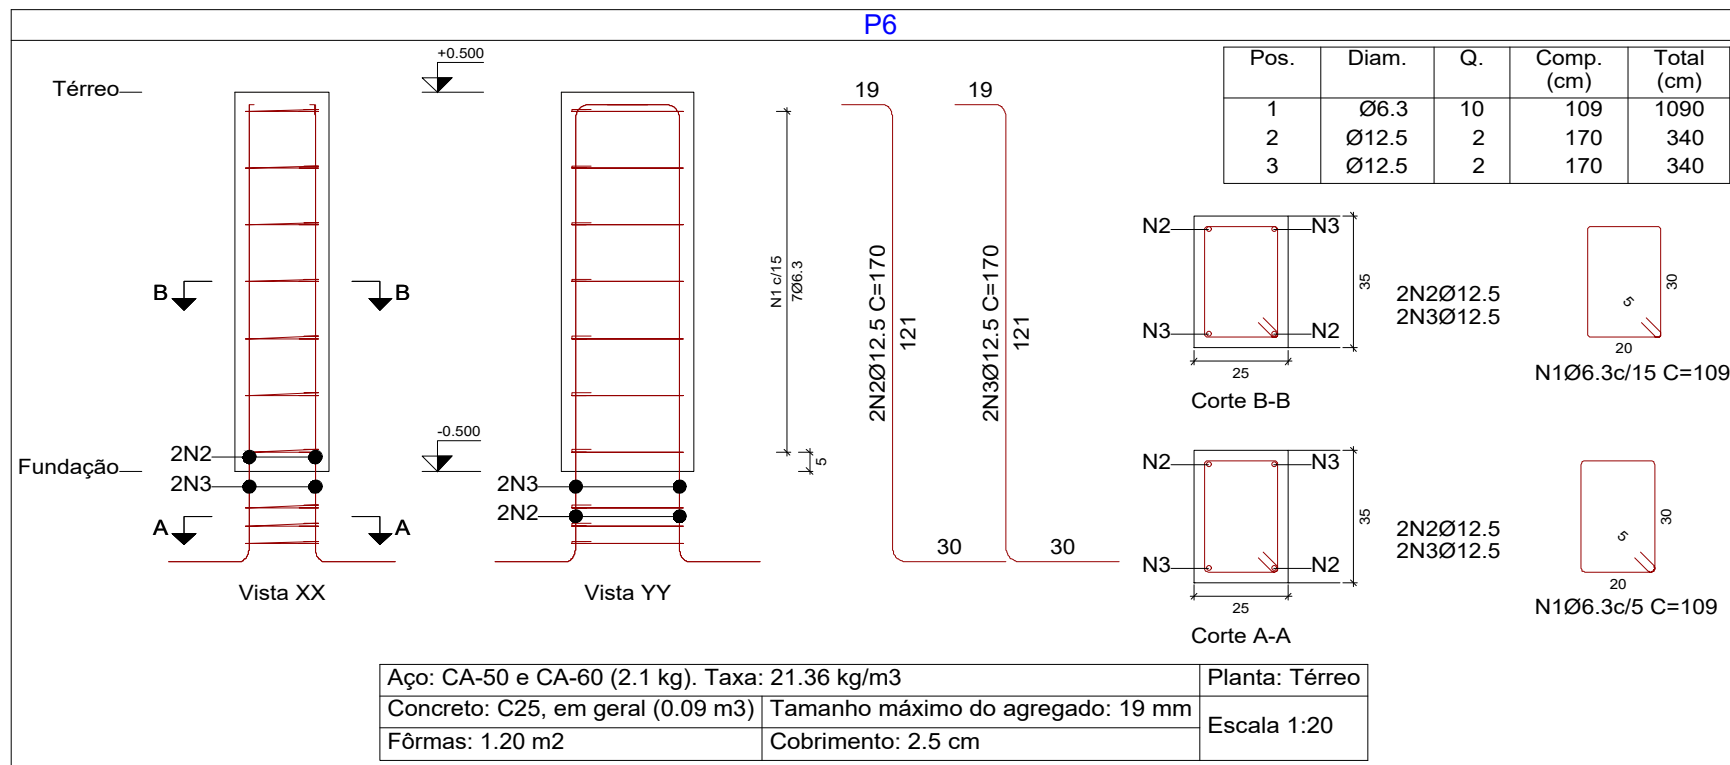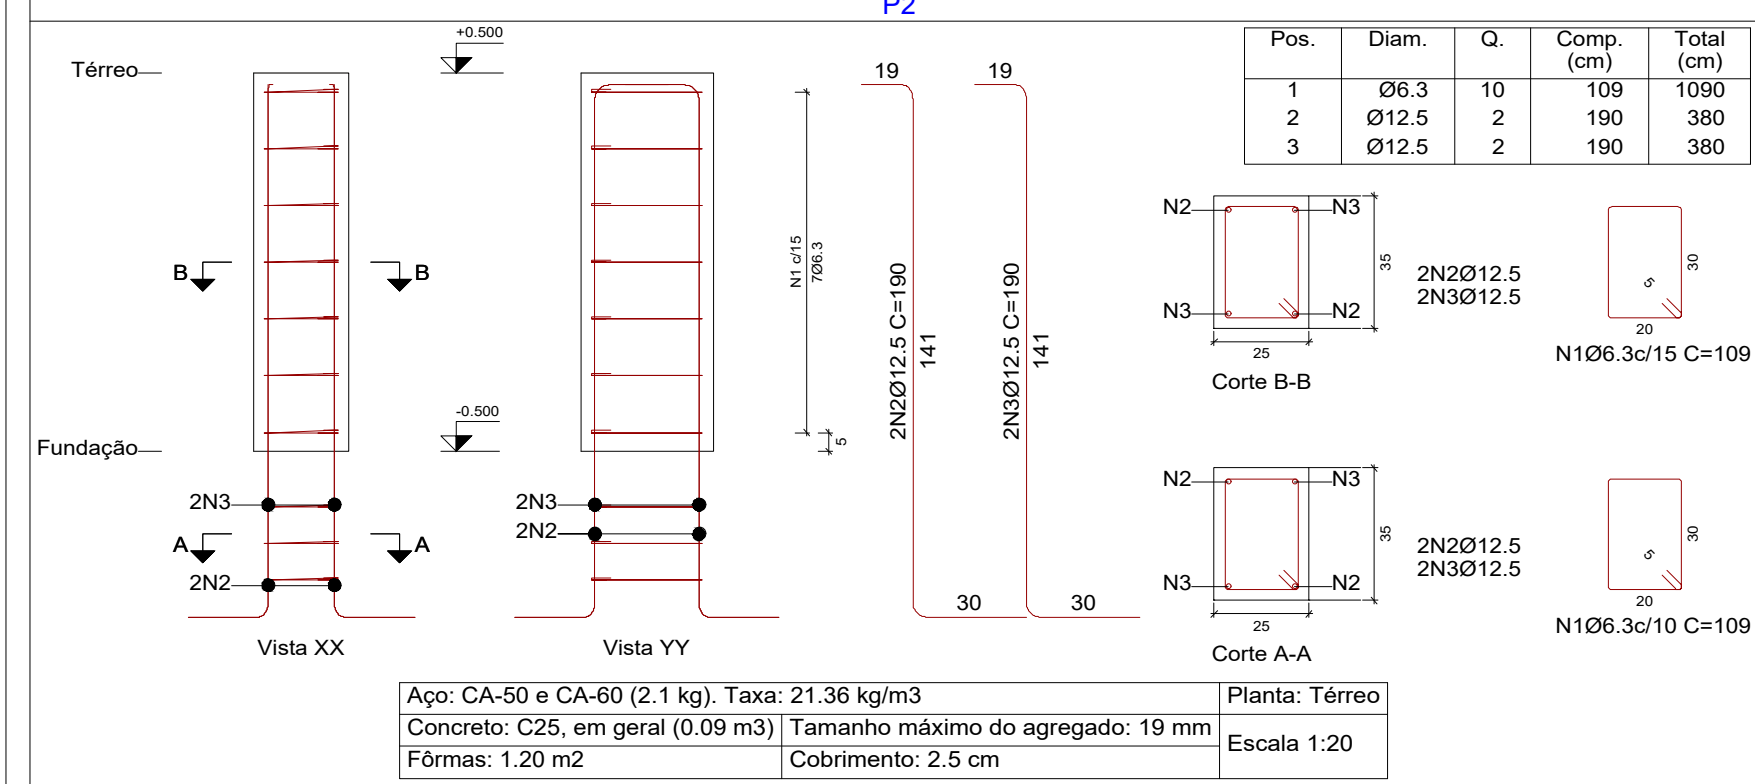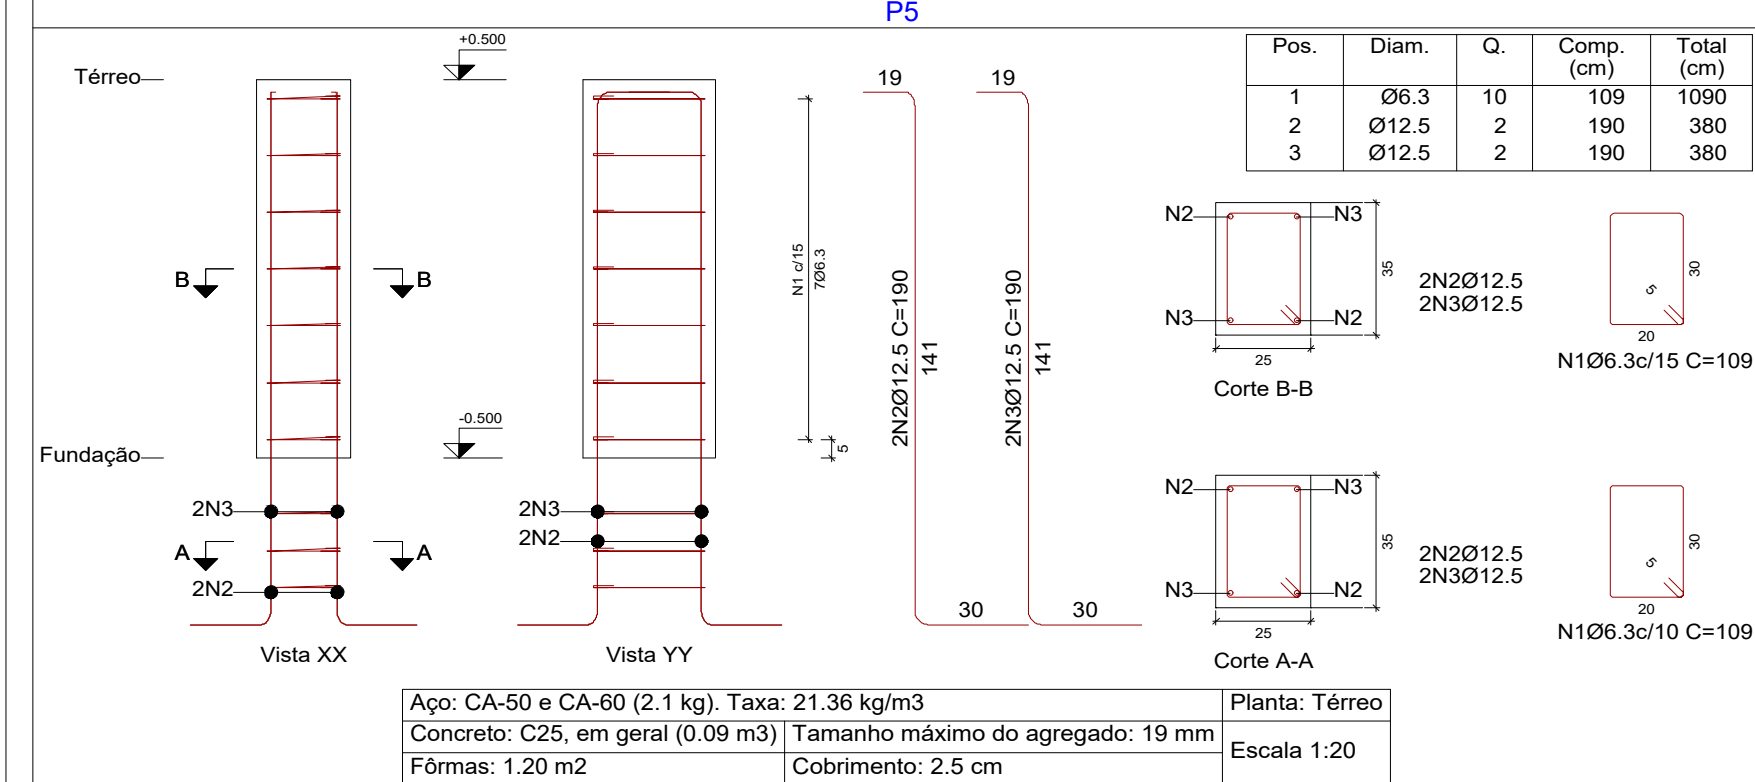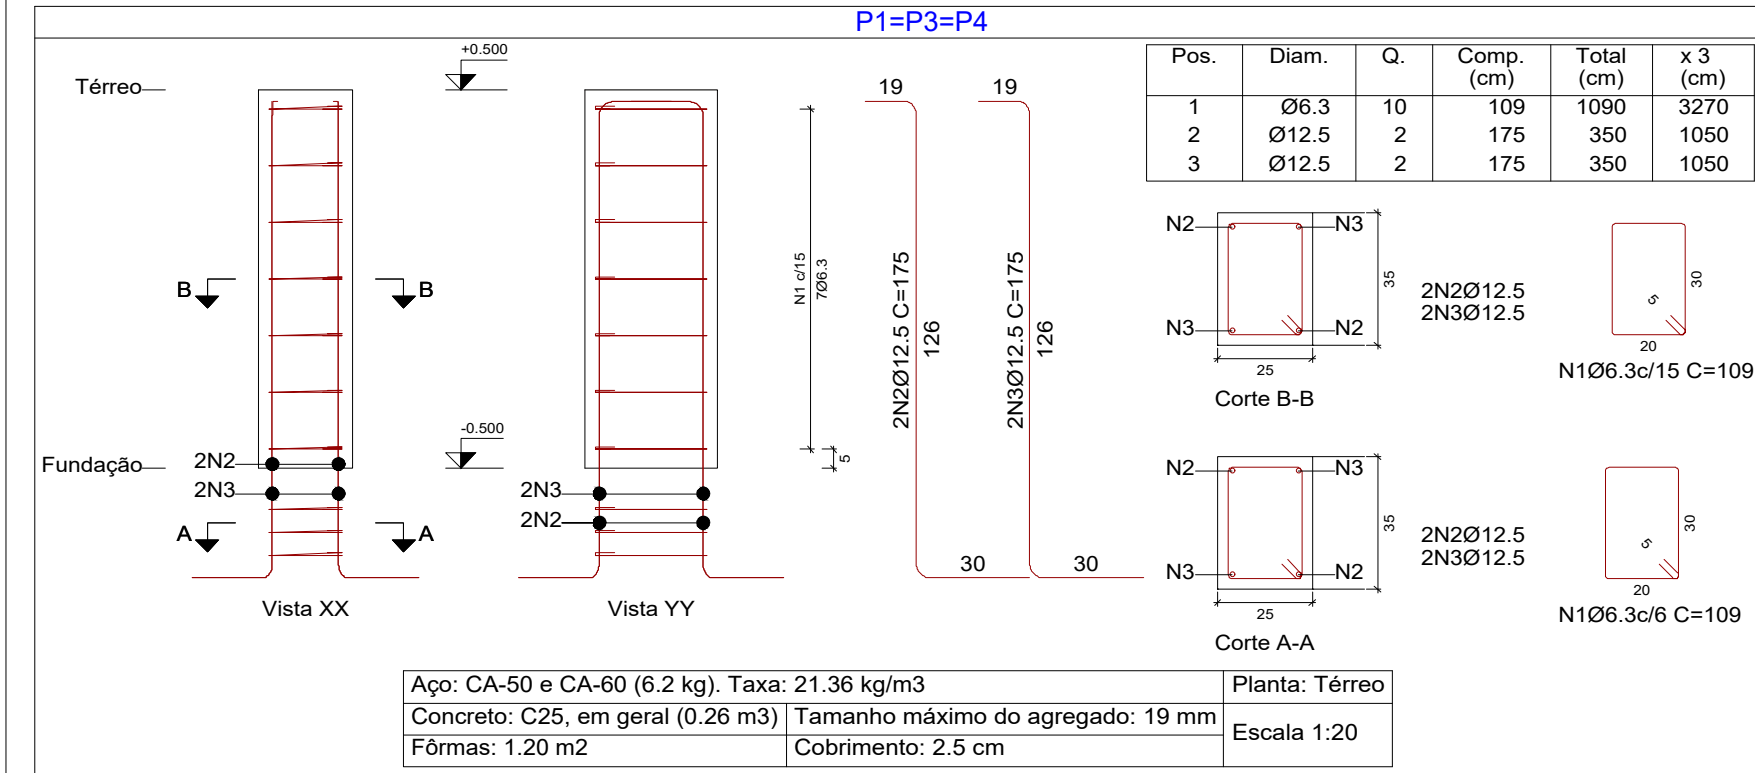

Elemento	Pos.	Diam.	Q.	Esquema (cm)	Comp. (cm)	Total (cm)	CA-50 (kg)	CA-60 (kg)
P1=P3=P4	1	Ø6.3	10		109	1090	2.7	
	2	Ø12.5	2	Consultar o desenho	175	350	3.4	
	3	Ø12.5	2	Consultar o desenho	175	350	3.4	
Total+10%:					(x3):	10.5		
P5	1	Ø6.3	10		109	1090	2.7	
	2	Ø12.5	2	Consultar o desenho	190	380	3.7	
	3	Ø12.5	2	Consultar o desenho	190	380	3.7	
Total+10%:						11.1		
P6	1	Ø6.3	10		109	1090	2.7	
	2	Ø12.5	2	Consultar o desenho	170	340	3.3	
	3	Ø12.5	2	Consultar o desenho	170	340	3.3	
Total+10%:						10.2		
P2	1	Ø6.3	10		109	1090	2.7	
	2	Ø12.5	2	Consultar o desenho	190	380	3.7	
	3	Ø12.5	2	Consultar o desenho	190	380	3.7	
Total+10%:						11.1		
							Ø6.3:	18.0 0.0
							Ø12.5:	45.9 0.0
							Total:	63.9 0.0

Elemento	Pos.	Diam.	Q.	Dob. (cm)	Reta (cm)	Dob. (cm)	Comp. (cm)	Total (cm)	CA-50 (kg)	CA-60 (kg)
S1=S4	1	Ø10	6	11	95	11	108	648	4.0	
	2	Ø10	4		VAR.		508	508	3.1	
	3	Ø10	6		VAR.		660	660	4.1	
	4	Ø10	4		VAR.		516	516	3.2	
	5	Ø12.5	4	30	175		205	820	7.9	
	6	Ø6.3	3		110		330	330	0.8	
Total+10%:									25.4	
(x2):									50.8	
S2	7	Ø12.5	7		122		122	854	8.2	
	8	Ø10	7		VAR.		177	1239	7.6	
	9	Ø12.5	7		VAR.		177	1239	7.6	
	10	Ø10	7		VAR.		177	1239	7.6	
	11	Ø12.5	4	30	190		220	880	8.5	
	12	Ø6.3	3		110		330	330	0.8	
Total+10%:									47.4	
S6	13	Ø10	5		92		92	460	2.8	
	14	Ø10	4		117		117	468	2.9	
	15	Ø12.5	4	30	170		200	800	7.7	
	16	Ø6.3	3		110		330	330	0.8	
Total+10%:									15.6	
(x2):									31.2	
S5	17	Ø10	10	11	111	11	133	1330	8.2	
	18	Ø10	7		167		167	1169	7.2	
	19	Ø10	10		VAR.		1360	1360	8.4	
	20	Ø10	7		VAR.		1183	1183	7.3	
	21	Ø12.5	4	30	190		220	880	8.5	
	22	Ø6.3	3		110		330	330	0.8	
Total+10%:									44.4	
S3	23	Ø10	6		92		92	552	3.4	
	24	Ø10	4		127		127	508	3.1	
	25	Ø10	6		VAR.		798	798	4.9	
	26	Ø10	4		VAR.		520	520	3.2	
	27	Ø12.5	4	30	174		204	816	7.9	
	28	Ø6.3	3		110		330	330	0.8	
Total+10%:									25.6	
(x2):									51.2	0.0
									Ø10:	105.1 0.0
									Ø12.5:	73.5 0.0
									Total:	183.8 0.0

Resumo Aço	Comp. total (m)	Peso+10% (kg)	Total
Fundação			
CA-50	Ø6.3	19.8	5
	Ø10	155.1	105
	Ø12.5	69.3	73
			183

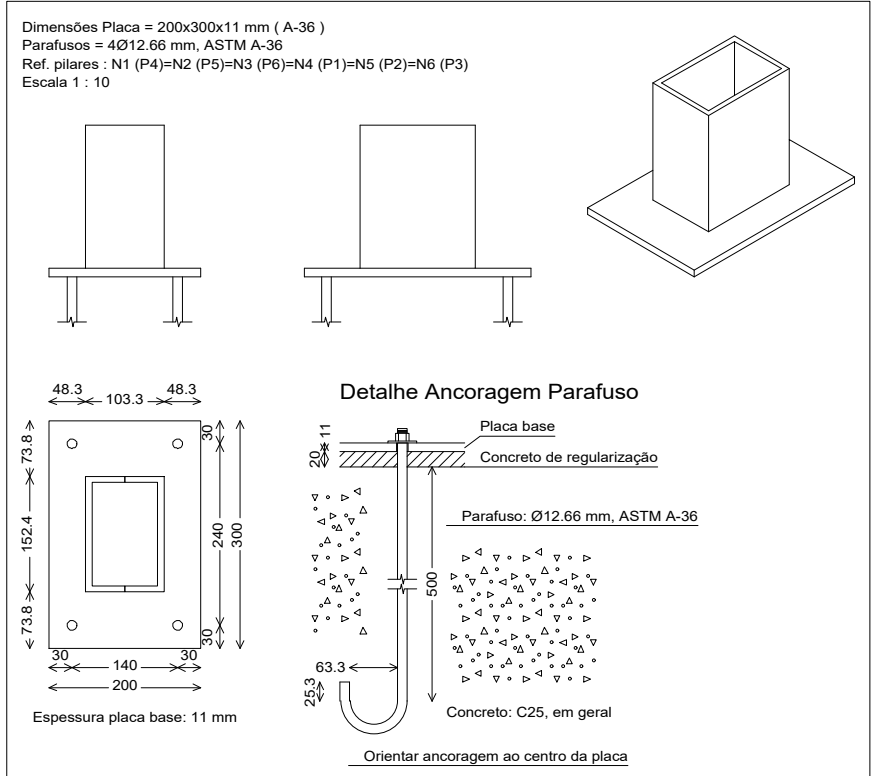

PROPRIETÁRIO: PREFEITURA MUNICIPAL DE COREMAS - PB
LINCOLN CARTAXO DE LIRA JUNIOR:06897861405
Assinado de forma digital por LINCOLN CARTAXO DE LIRA JUNIOR:06897861405
Dados: 2025.08.11 14:06:26 -03'00'

PROJETO: LINCOLN CARTAXO DE LIRA JÚNIOR CREA 160.814.689-8

CONSTRUÇÃO: PROJETO DE ESTRUTURAL - GARAGEM DAS MÁQUINAS - COREMAS/PB

FOLHA: (1)/03
PROJETO: PROJETO DE ESTRUTURAL - GARAGEM DAS MÁQUINAS - COREMAS/PB

LOCALIDADE: MUNICÍPIO DE COREMAS - PB

DATA: JUL/2025
RESPONSÁVEL: LINCOLN CARTAXO
RUBRICA:


DESENHOS:

- Planta de Locação
- Detalhamento das Sapatas
- Detalhamento de arranjos dos pilares
- Detalhamento de chumbamento e chapa base


INDICADAS:

ARQUIVO:

Aprovações:

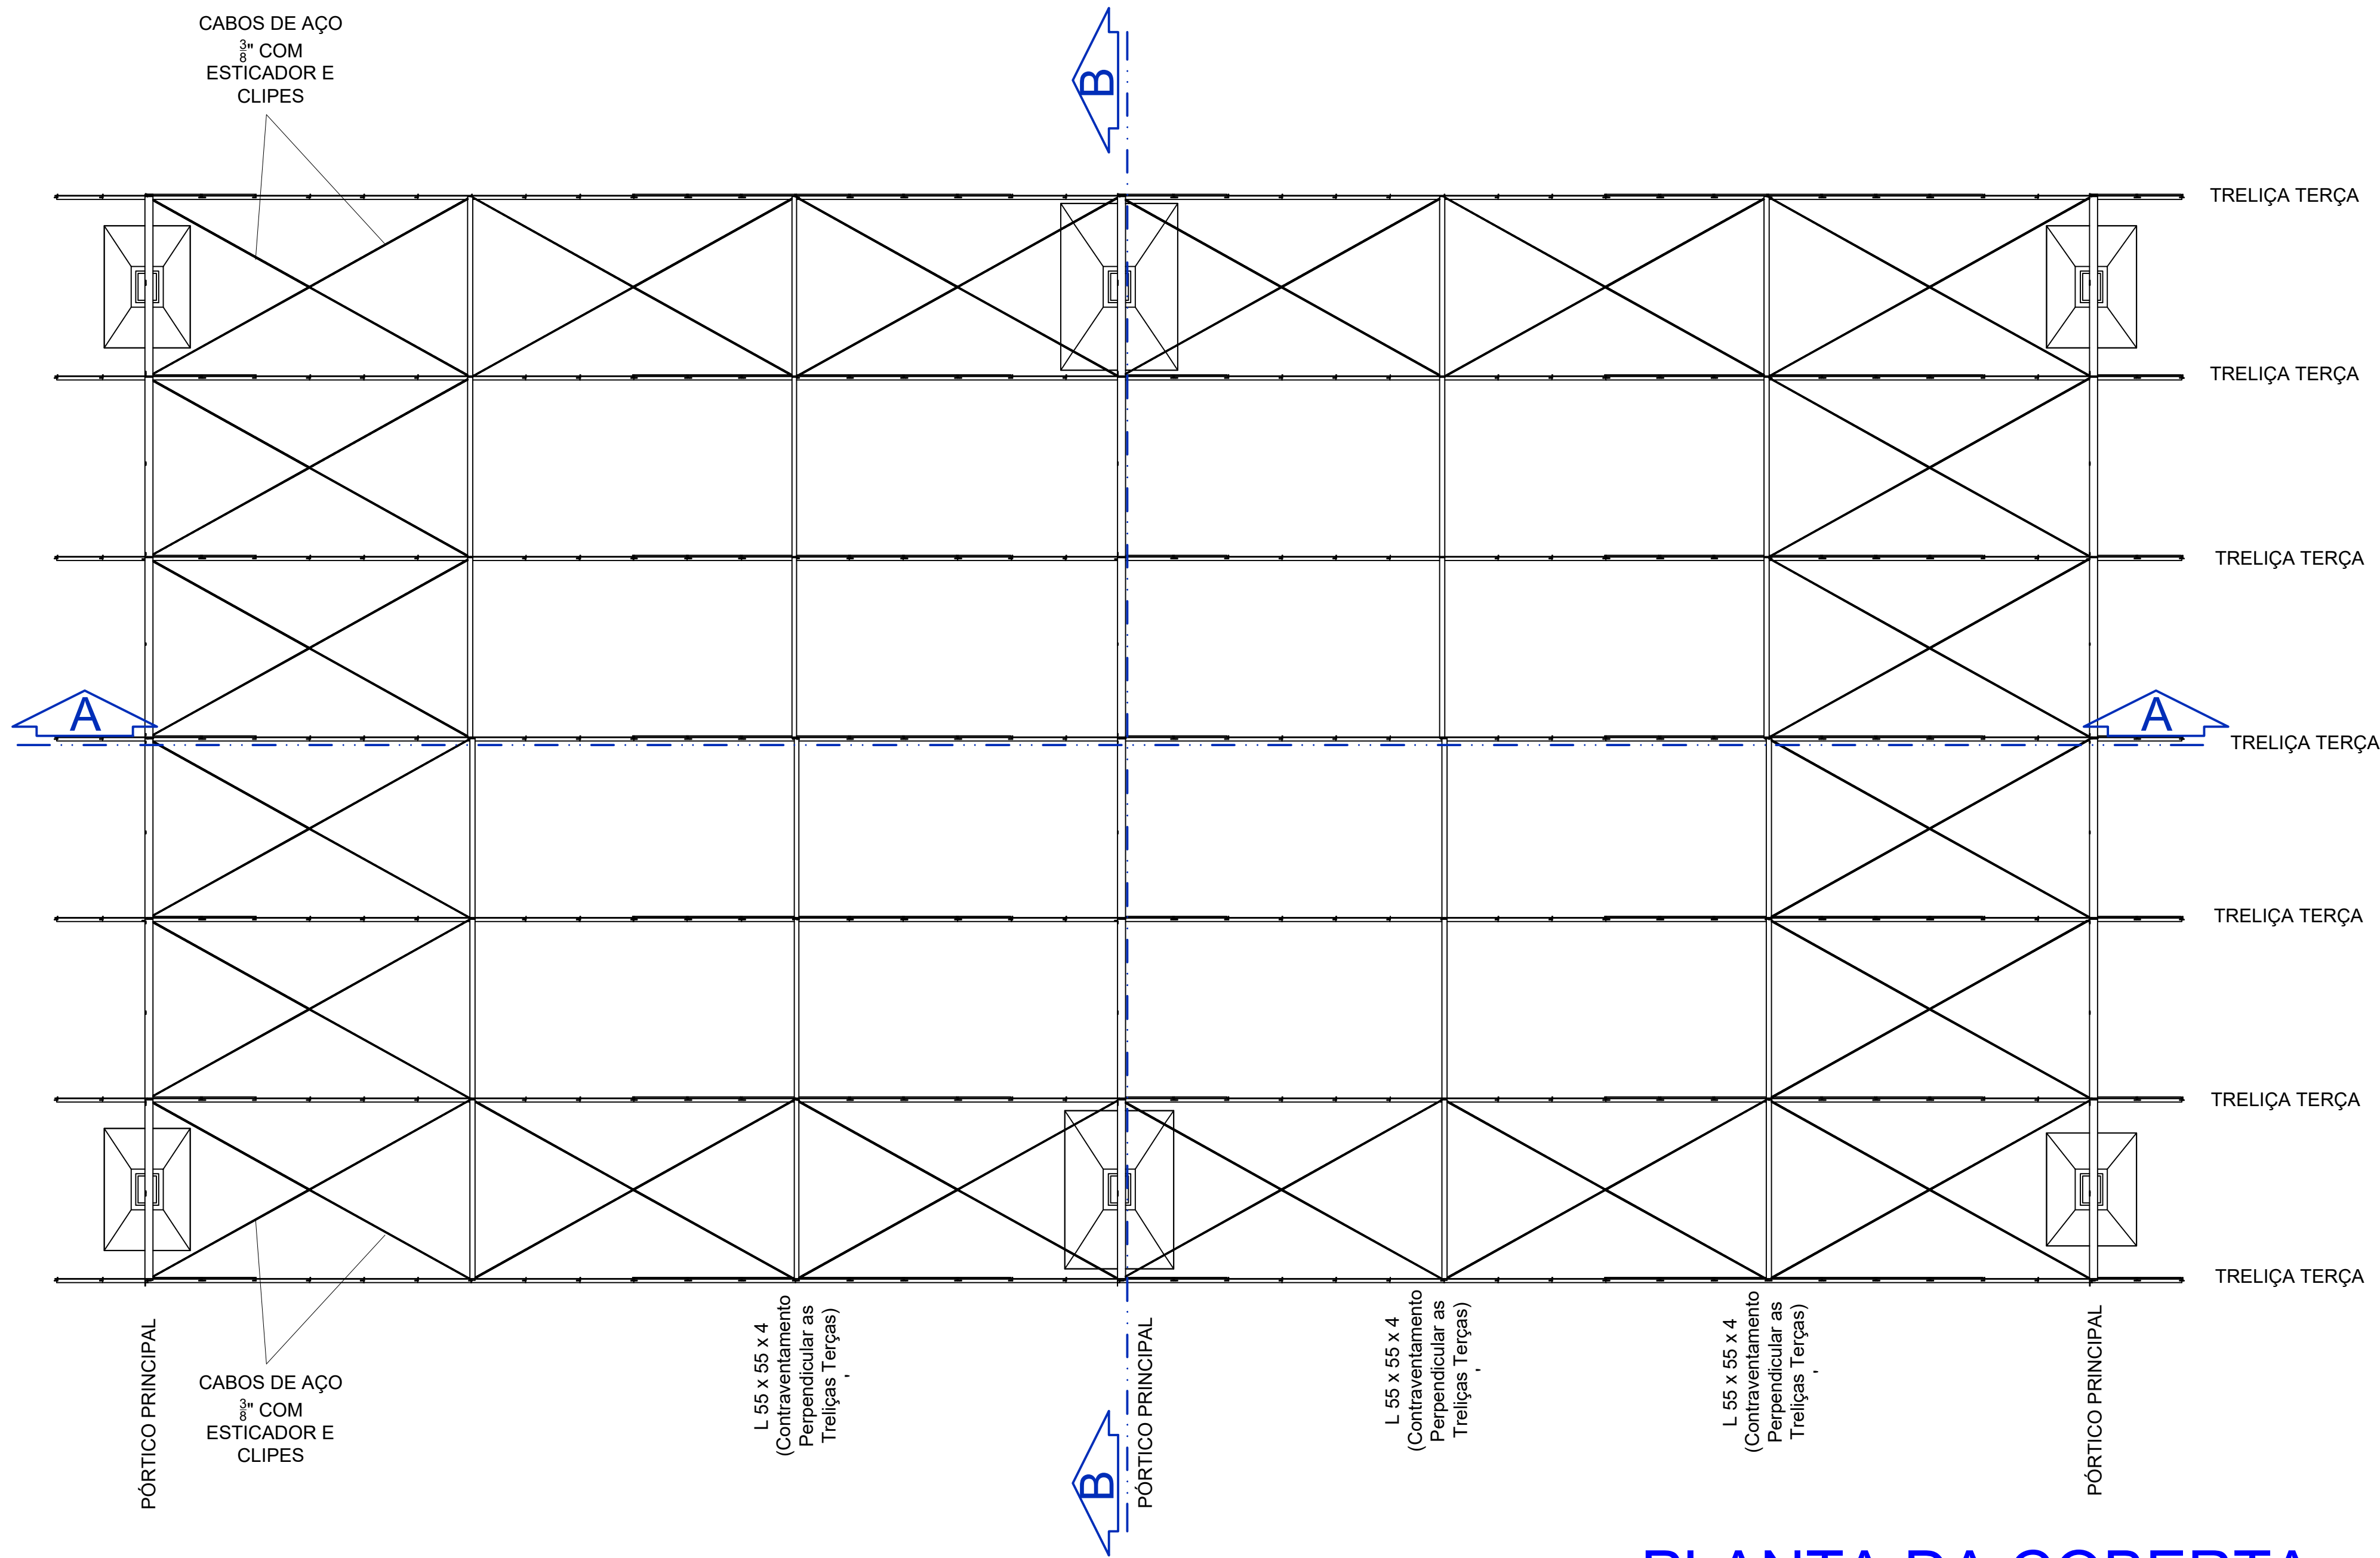

PLANTA DA COBERTA
Escala 1/75

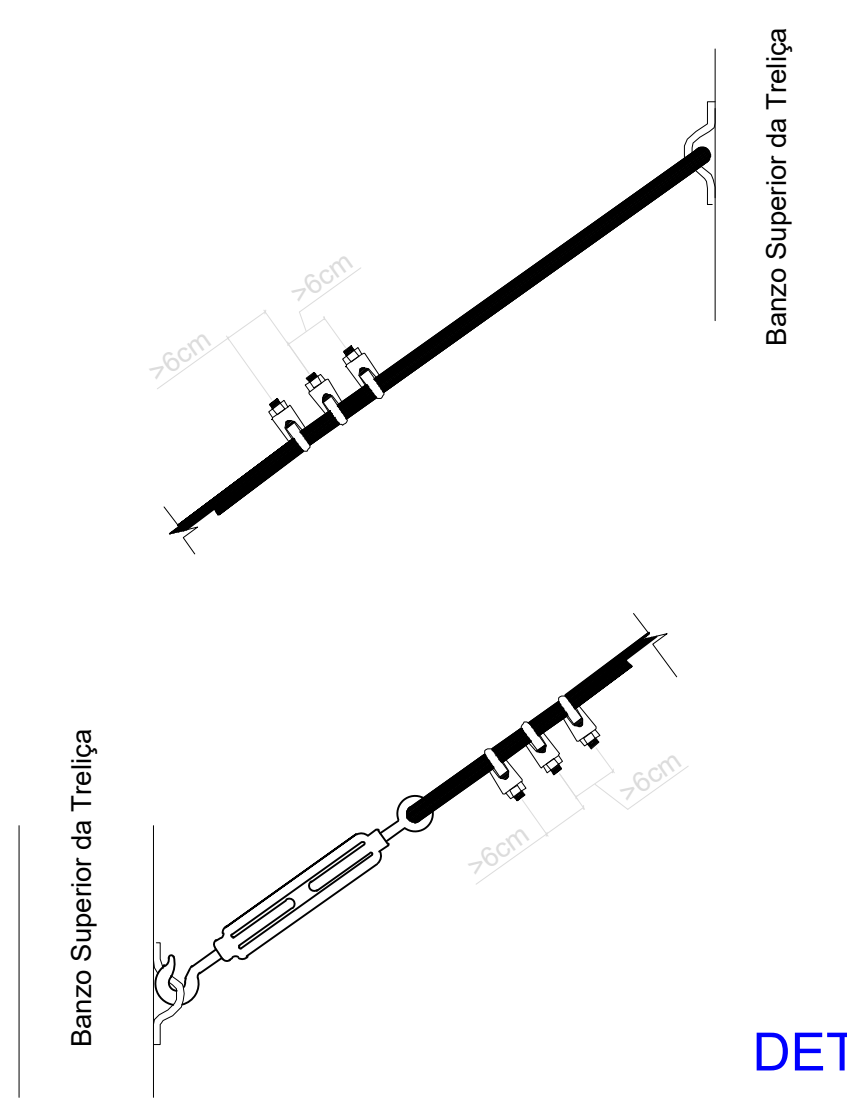

DETALHE DO ESTICADOR
Escala 1/10

ORIENTAÇÕES PARA PINTURA DE ESTRUTURA METÁLICA (AÇO A36)

As seguintes etapas devem ser rigorosamente seguidas para a pintura dos perfis metálicos, conforme NBR 16204 (Preparação de Superfícies de Aço) e NBR 15962 (Pintura Industrial). O sistema de pintura visa garantir proteção anticorrosiva e durabilidade, adequado ao ambiente de exposição C3 (média corrosividade, conforme NBR 14643).

PREPARAÇÃO DA SUPERFÍCIE

Realizar limpeza inicial para remover óleos, graxas e contaminantes, utilizando desengraxante conforme NBR 16204, método SP 1 (limpeza com solvente).

Executar jateamento abrasivo ao grau Sa 2½ (NBR 16204, equivalente a ISO 8501-1), removendo ferrugem, carepa de laminação e impurezas. Alternativamente, usar lixamento mecânico (escovas de aço ou lixas) até atingir superfície metálica limpa.

Garantir rugosidade de 25 a 50 µm (perfil de ancoragem), conforme NBR 16204, para aderência do revestimento.

Inspeccionar a superfície, garantindo ausência de poeira, umidade ou contaminantes antes da pintura.

APLICAÇÃO DO PRIMER

Aplicar uma camada de primer epóxi com fosfato de zinco, com espessura de filme seco (DFT) de 50 a 75 µm, conforme especificação do fabricante.

Utilizar pistola airless, rolo ou pincel, garantindo aplicação uniforme em todas as faces dos perfis.

Respeitar o tempo de secagem do primer (4 a 24 horas, conforme ficha técnica), verificando condições ambientais (temperatura entre 10°C e 35°C, umidade relativa < 85%, superfície 3°C acima do ponto de orvalho).

APLICAÇÃO DA TINTA EPÓXI

Aplicar duas camadas de tinta epóxi de alta espessura (dois componentes: resina + catalisador), totalizando DFT de 100 a 150 µm, conforme NBR 15962.

Misturar os componentes na proporção INDICADAS pelo fabricante e aplicar com pistola airless, rolo ou pincel, garantindo cobertura homogênea.

Aguardar intervalo de 12 a 24 horas entre camadas, conforme ficha técnica, mantendo condições ambientais adequadas.

ACABAMENTO (OPCIONAL)

Para proteção contra raios UV e maior durabilidade em ambientes externos, aplicar uma camada de poliuretano alifático (DFT de 50 a 75 µm) após cura parcial da epóxi (12 a 24 horas).

Seguir instruções do fabricante para aplicação e cura.

CONDIÇÕES DE APLICAÇÃO

Garantir ventilação adequada durante a aplicação e cura, especialmente em ambientes internos.

Monitorar condições ambientais conforme NBR 15962, evitando pintura em superfícies úmidas ou sob chuva.

Verificar espessura do filme seco (DFT) com medidor apropriado, conforme NBR 16204, AÇO 3/8" x 443.

INSPEÇÃO FINAL

Realizar inspeção visual para verificar ausência de falhas (bolhas, crateras ou descascamento).

Confirmar aderência do revestimento, se necessário, por teste conforme NBR 11003 (método de corte em grade).

Garantir cura total do sistema (7 dias, conforme fabricante) antes da exposição a condições severas.

NOTAS:


Consultar fichas técnicas dos produtos para proporções, tempos de cura e espessuras.

Para ambientes de maior corrosividade (C4 ou C5), consultar projetista para adequação do sistema.


Manter registros de aplicação (lotes, condições ambientais, espessuras) para controle de qualidade.

Cargas consideradas em projeto:

- Peso próprio da telha: 4,5 kg/m² (TP 40 que vence vãos entre terças de 2,40 m);
- Peso próprio de instalações elétricas e luminárias: 0,21 kg/m²
- Fofo: NÃO INCLUSO

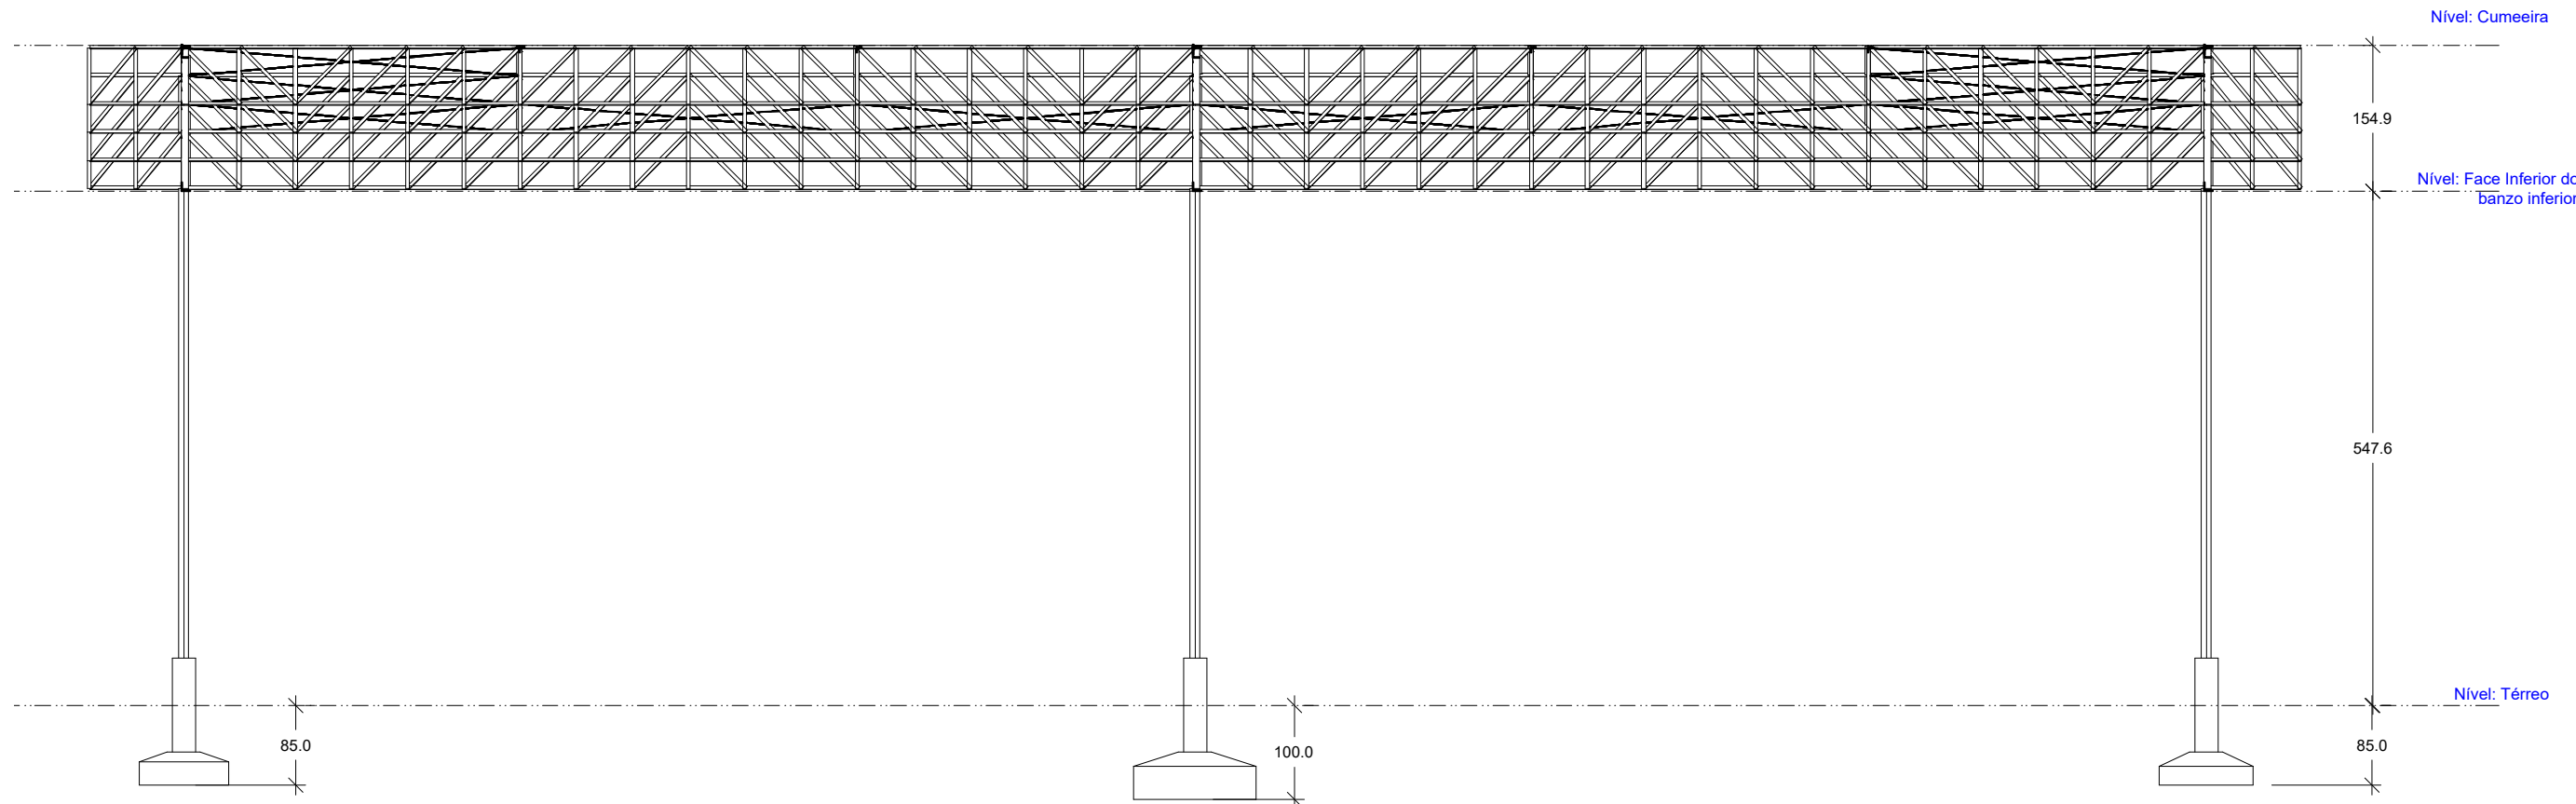

CORTE AA
Escala 1/75

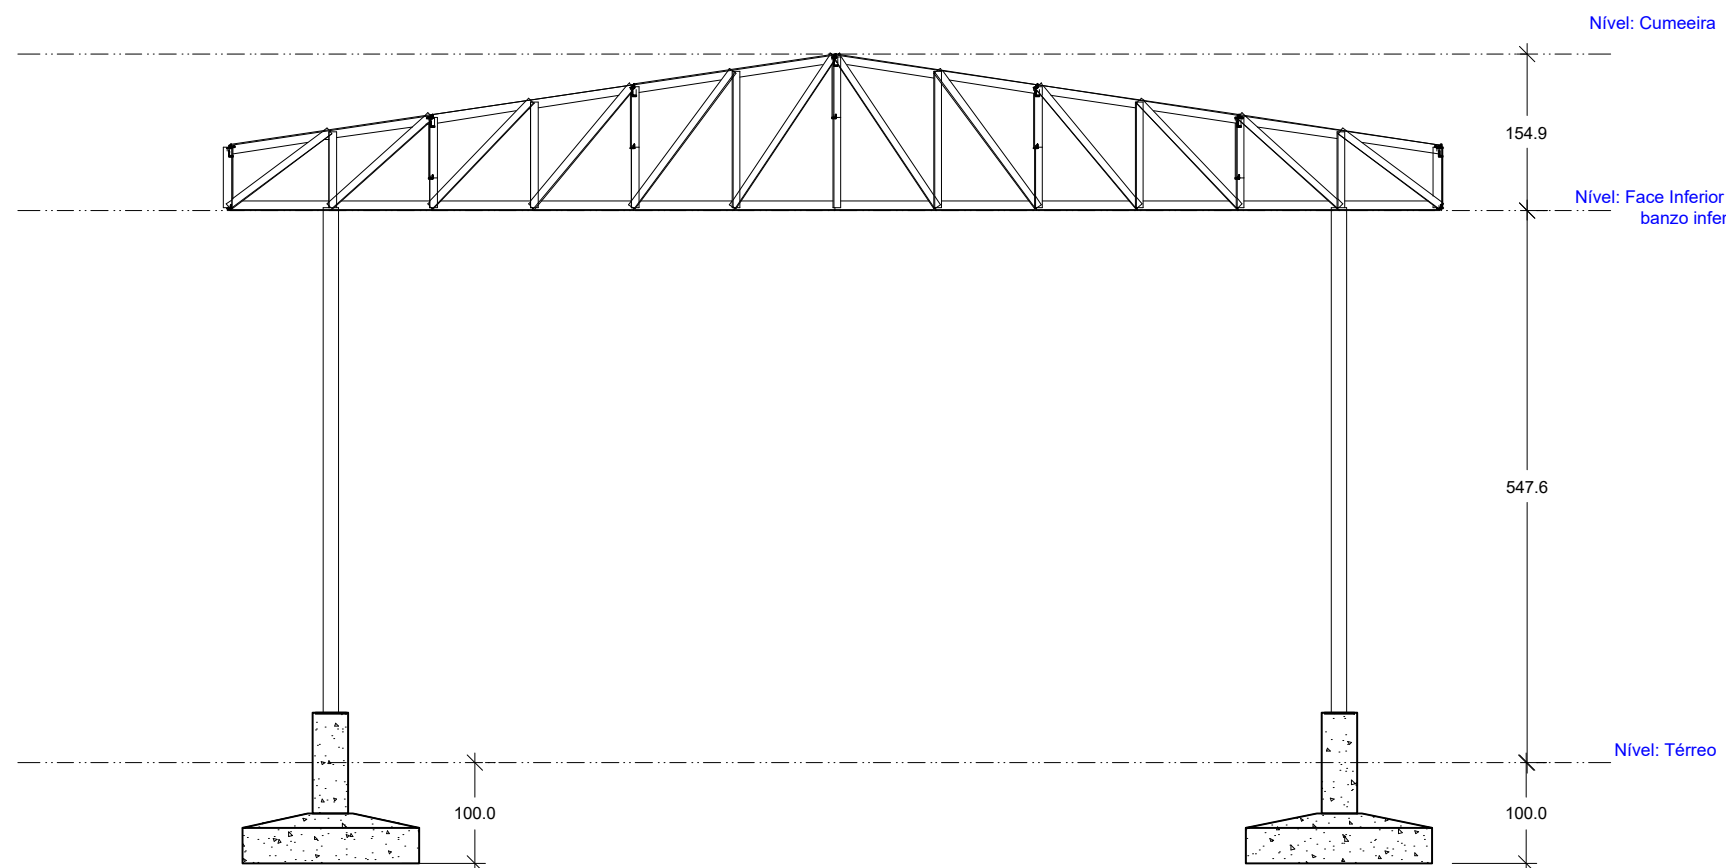


CORTE BB
Escala 1/75

PROPRIETÁRIO: PREFEITURA MUNICIPAL DE COREMAS - PB
LINCOLN CARTAXO DE LIRA JÚNIOR:06897861405
Assinado de forma digital por LINCOLN CARTAXO DE LIRA JÚNIOR:06897861405
Dados: 2025.08.11 14:07:09 -03'00'


CONSTRUÇÃO: PROJETO DE ESTRUTURAL - GARAGEM DAS MÁQUINAS - COREMAS/PB

FOLHA	PROJETO:	PROJETO DE ESTRUTURAL - GARAGEM DAS MÁQUINAS - COREMAS/PB
(2)/03	LOCALIDADE:	MUNICÍPIO DE COREMAS - PB
DESENHO:	RESPONSÁVEL:	RUBRICA:
JUL/2025	LINCOLN CARTAXO	
CÓPIA:		
VERBO:		
ESCALAS:	DESENHOS:	CONVÊNIO:
INDICADAS:	• Planta de Coberta • Det. Esticador de contraventamento em "X" • Corte AA • Corte BB	
		ARQUIVO:

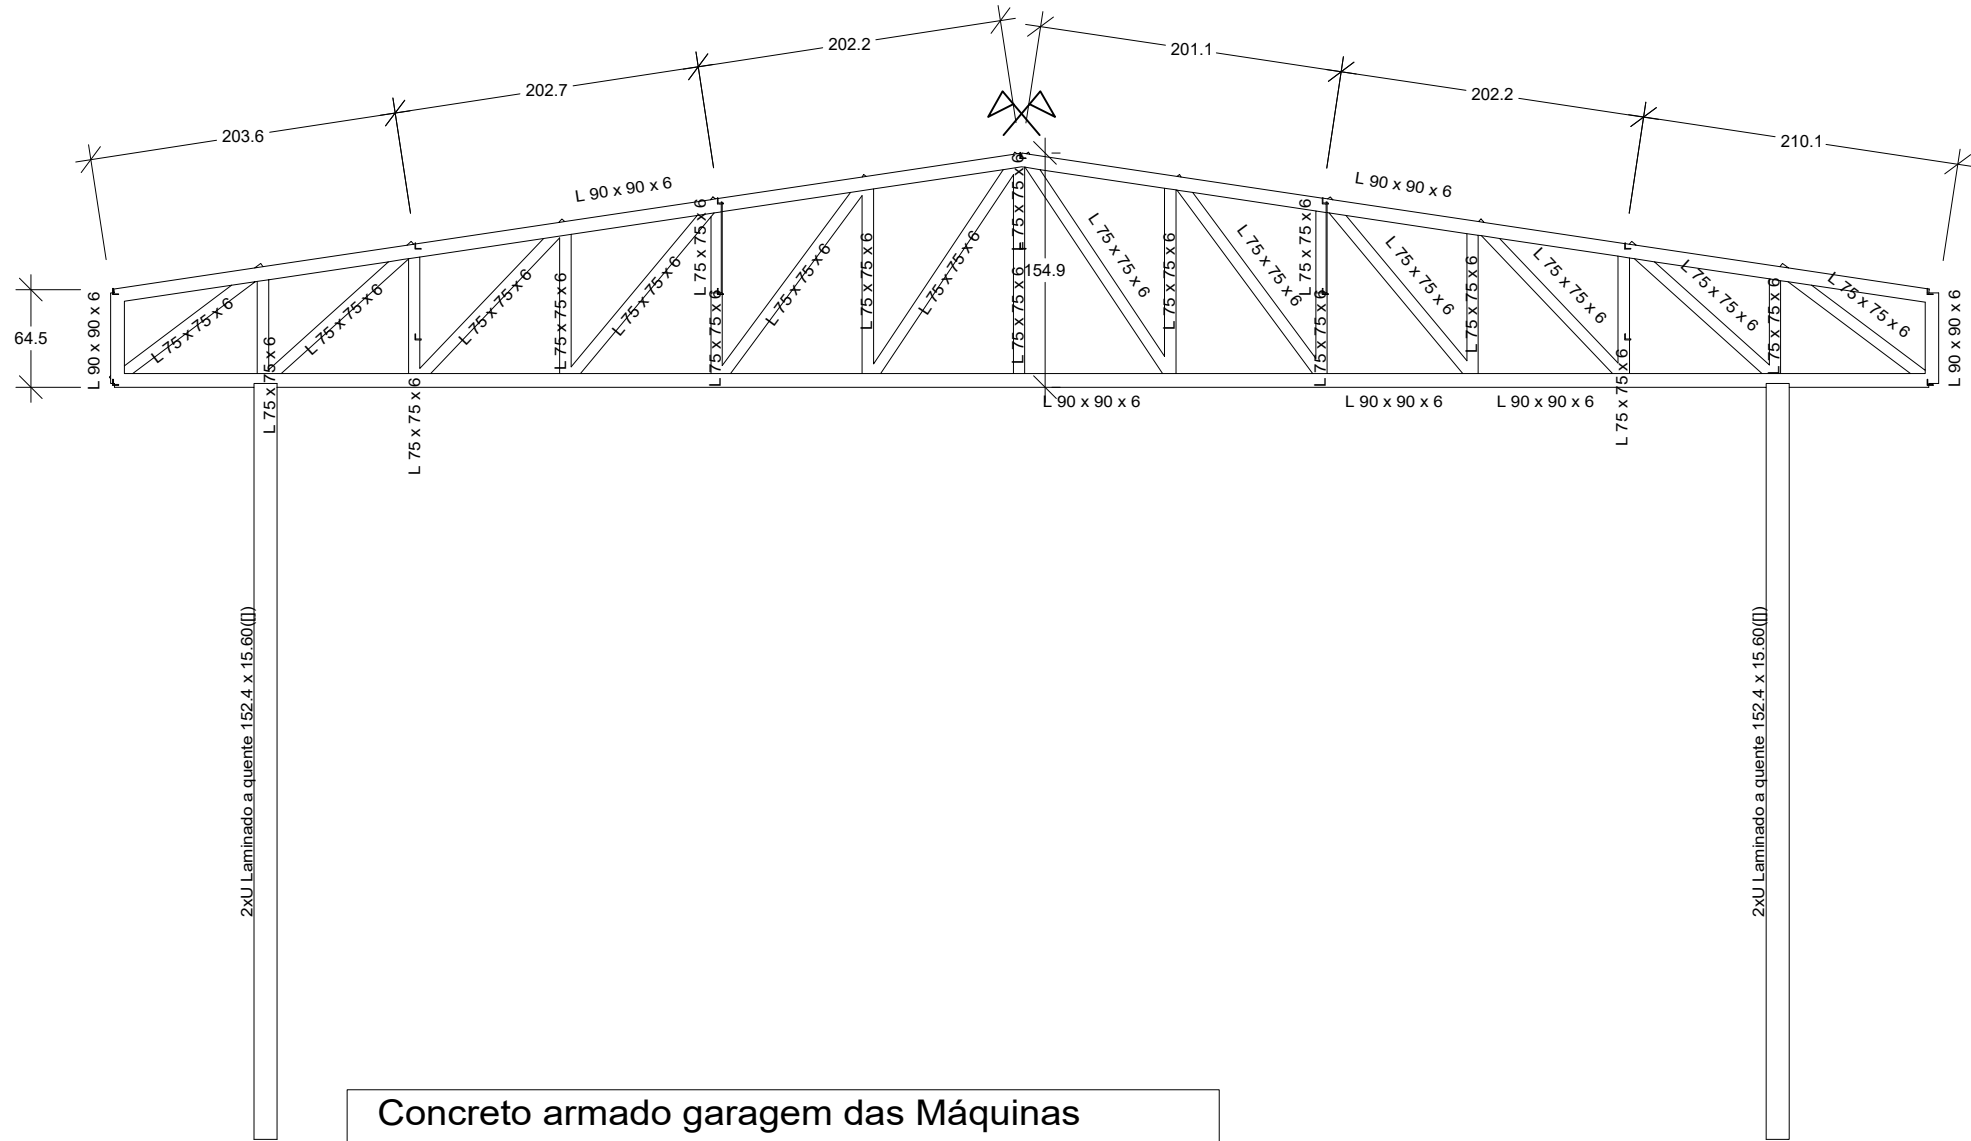


Concreto armado garagem das Máquinas
Estrutura 1
Norma de aço laminado: ABNT NBR 8800:2008
Aço laminado: A-36 250Mpa
Escala: 1:13

Estrutura 1: 2D: Pórtico Central

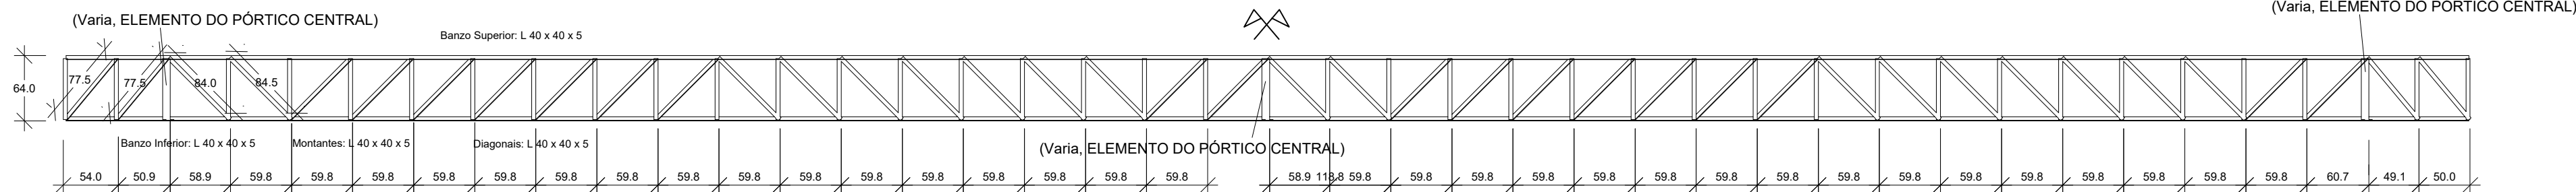

Estrutura 1: 2D: Treliza Terça

Concreto armado garagem das Máquinas
Estrutura 1
Norma de aço laminado: ABNT NBR 8800:2008
Aço laminado: A-36 250Mpa
Escala: 1:13

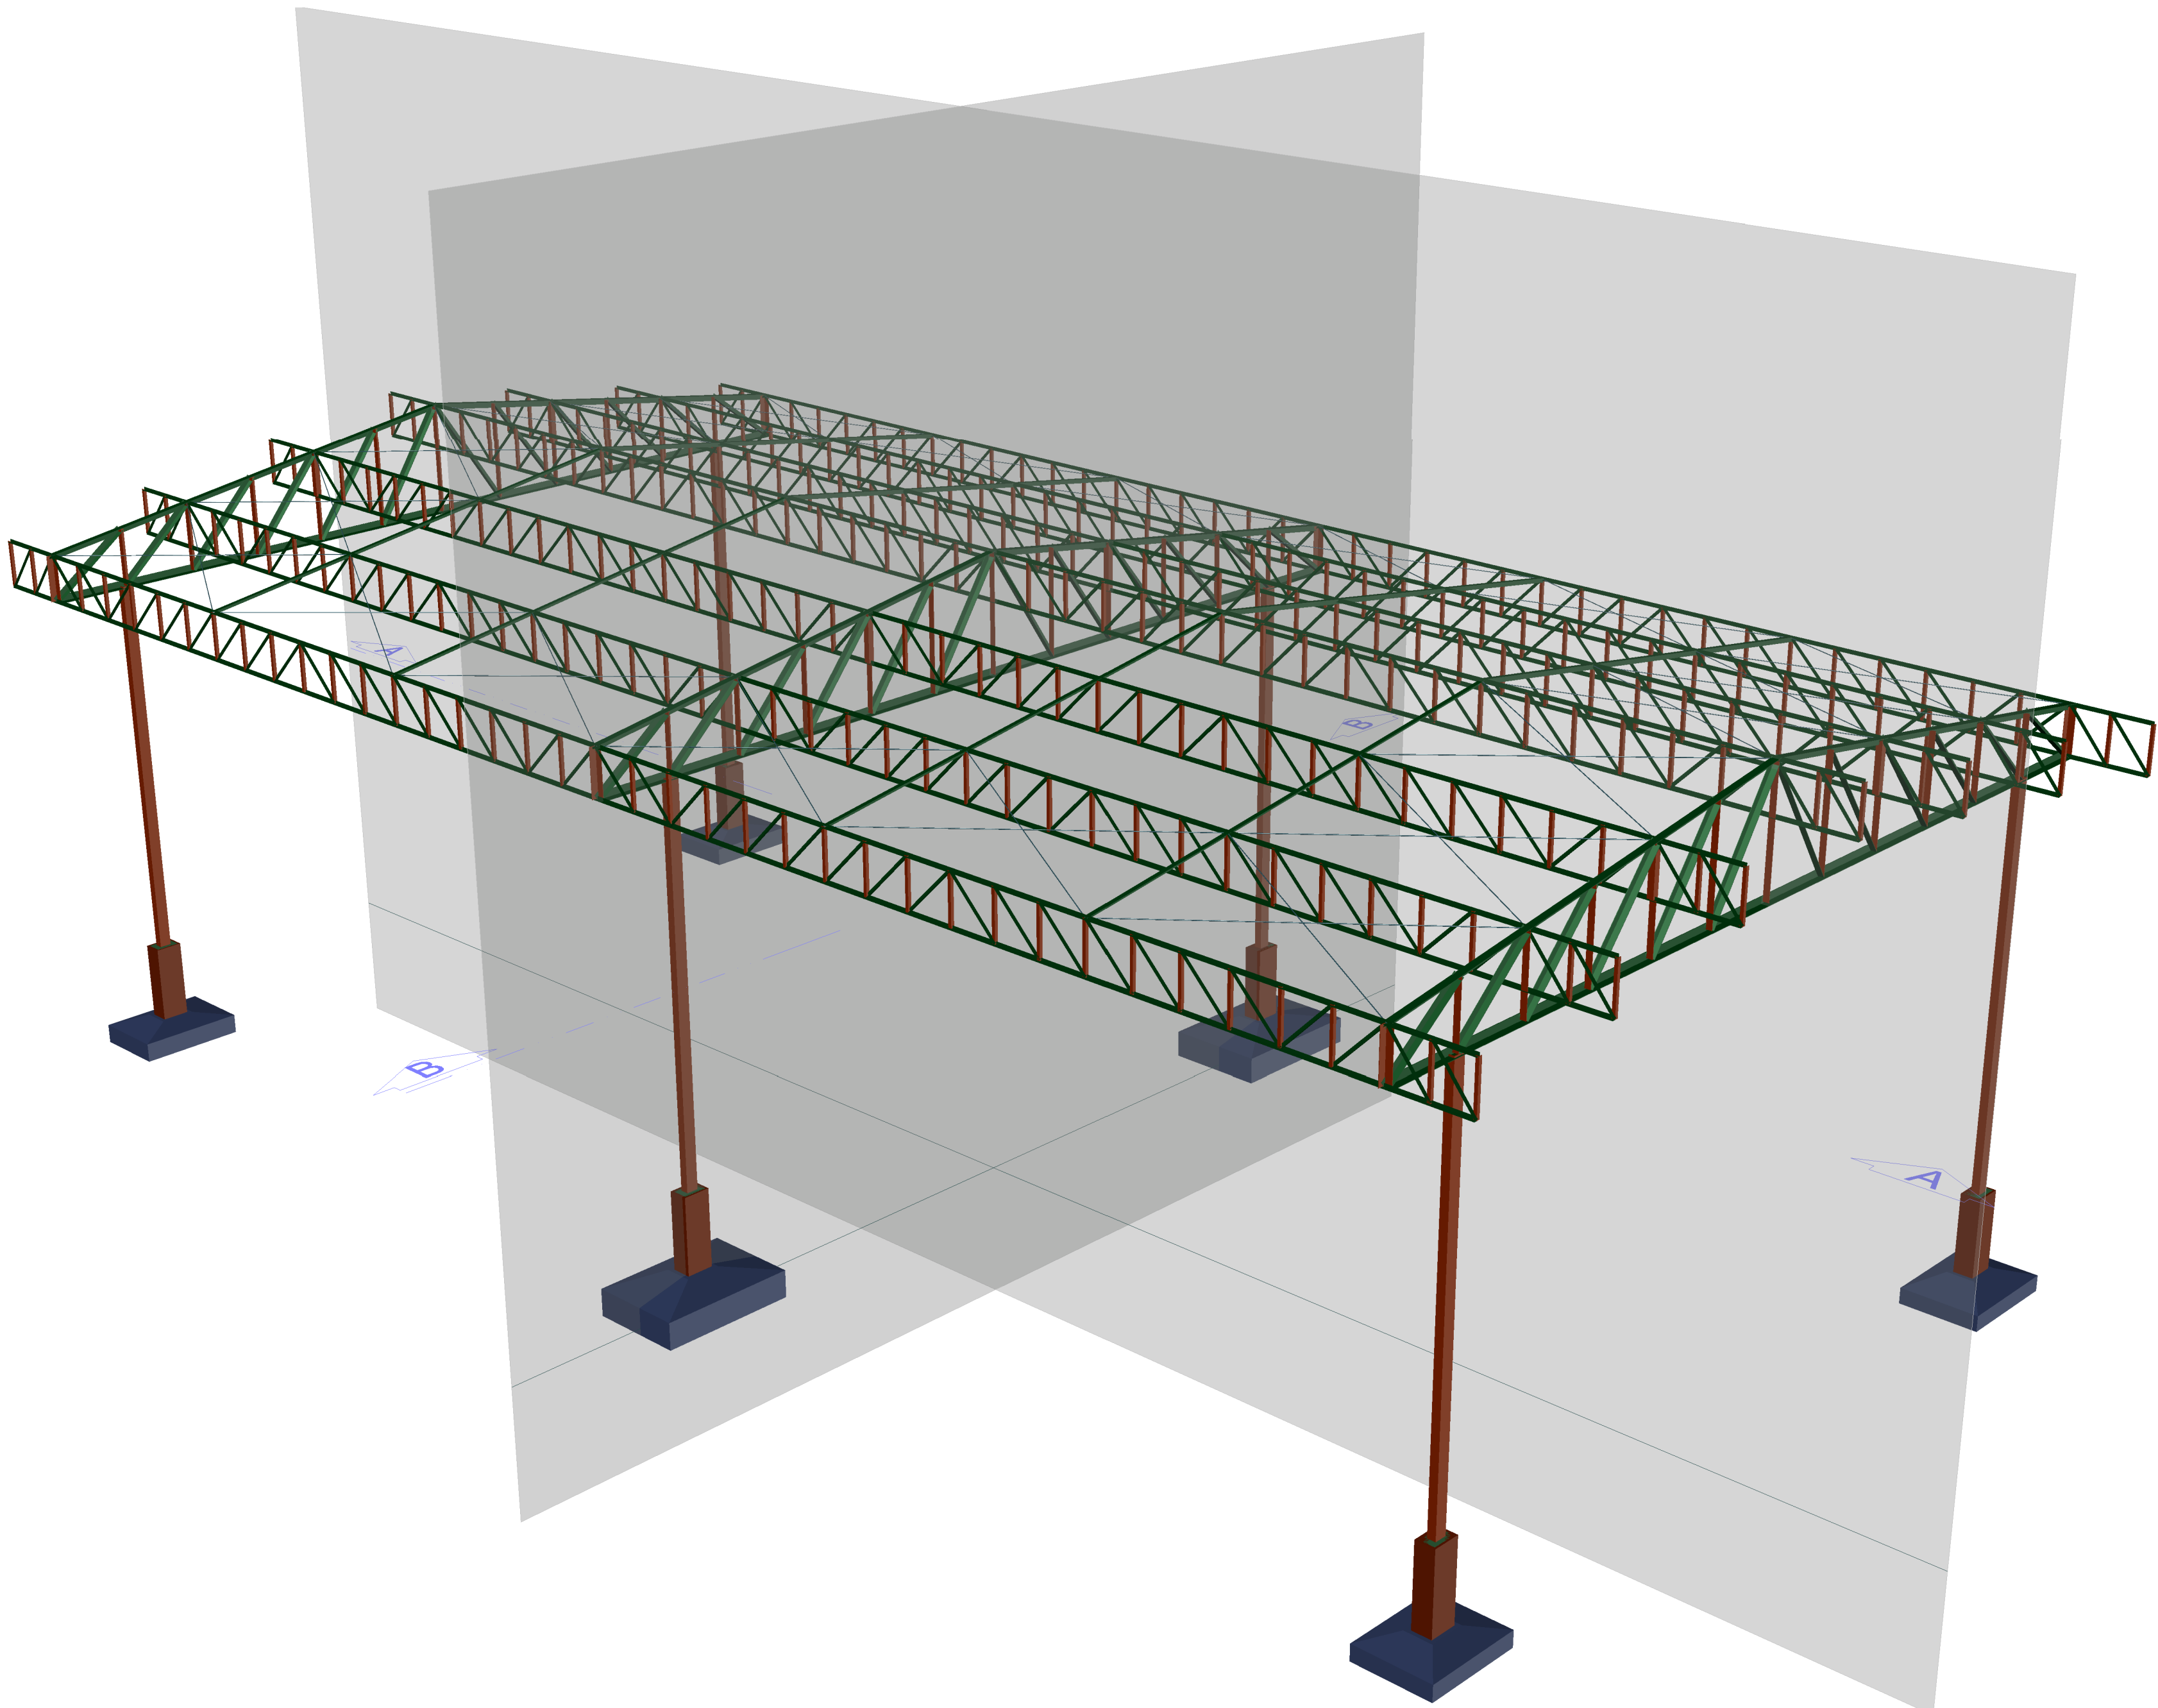

2.1.1.1.- Tabela resumo

Tabela resumo									
Material		Série	Perfil	Comprimento		Volume		Peso	
Tipo	Designação			Perfil (m)	Material (m²)	Perfil (m)	Material (m³)	Perfil (kg)	Material (kg)
U	U Laminado a quente 152.4 x 15.80, Caixa dupla soldada			20.000	0.115			90.15	
			75 x 75 x 6			2079		620.48	
			90 x 90 x 6		73.003	0.080		620.45	
			40 x 40 x 5		724.561	0.275		270.66	
			55 x 55 x 4		40.037	0.022	0.054	164.42	55.63
L	Cabo de aço 3/8"			164.818	0.013			110.62	
				154.881	0.013	0.392		4360.63	
Aço laminado 4-25 223964									

2.1.1.2.- Quantitativos de superfícies

Aço laminado: Quantitativos das superfícies a pintar				
Série	Perfil	Superfície unitária (m²/m)	Comprimento (m)	Superfície (m²)
U	U Laminado a quente 152.4 x 15.80, Caixa dupla soldada	0.511	30.000	15.343
L	L 75 x 75 x 6	0.300	90.541	27.162
	L 90 x 90 x 6	0.360	75.003	27.361
	L 40 x 40 x 5	0.160	724.561	115.930
	L 55 x 55 x 4	0.220	48.537	10.678
Cabo de aço circular	Cabo de aço 3/8"	0.031	164.818	5.178
Total			201.652	

2.2.- Placas de base

2.2.1.- Quantitativos placas de base

Pilares	Aço	Peso kgf	Totais kgf
N1 (P4), N2 (P5), N3 (P6), N4 (P1), N5 (P2), N6 (P3)	A-36 6 x 5.18	31.09	31.09
Totais		31.09	31.09

2.2.2.- Quantitativos parafusos placas de base

Pilares	Parafusos	Aço	Comprimento m	Peso kgf	Totais m	Totais kgf
N1 (P4), N2 (P5), N3 (P6), N4 (P1), N5 (P2), N6 (P3)	24012.66 mm L=69 cm ASTM A-36 (liso)		24 x 0.69	24 x 0.68	16.52	16.52
Totais					16.52	16.52

Fundação

Elemento	Fôrmas (m²)	Volume (m³)	Barras (kg)
Sapatas isoladas	12.32	3.326	183
Total	-	3.326	183

Térreo

Elemento	Fôrmas (m²)	Volume (m³)	Barras (kg)
Pilares	7.20	0.540	12
Total	-	0.540	12
Índices (por m²)	-	1.019	22.64
Superfície total: 0.53 m²			

Total obra

Elemento	Fôrmas (m²)	Volume (m³)	Barras (kg)
Sapatas isoladas	12.32	3.330	183
Total	-	3.330	183

Elemento	Fôrmas (m²)	Volume (m³)	Barras (kg)
Pilares	7.20	0.540	12
Total	-	0.540	12
Índices (por m²)	-	1.019	22.64
Superfície total: 0.53 m²			

Fundação

Referência	Comprimento (m)	Peso (kg)
Ø6.3	19.80	5
Ø10	155.11	105
Ø12.5	69.34	73
Total + 10%		183

Térreo

Referência	Comprimento (m)	Peso (kg)
Ø6.3	45.78	12
Total + 10%		12

Total obra


Referência	Comprimento (m)	Peso (kg)
Ø6.3	19.80	5
Ø10	155.11	105
Ø12.5	69.34	73
Total + 10%		183
Pilares em concreto	45.78	12
Total + 10%		12

PROPRIETÁRIO: PREFEITURA MUNICIPAL DE COREMAS - PB
LINCOLN CARTAXO DE LIRA JUNIOR:06897861405
Assinado de forma digital por LINCOLN CARTAXO DE LIRA JUNIOR:06897861405
Dados: 2025.08.11 14:07:48 -03'00'

PROJETO: LINCOLN CARTAXO DE LIRA JÚNIOR CREA 160.814.689-8


CONSTRUÇÃO: PROJETO DE ESTRUTURAL - GARAGEM DAS MÁQUINAS - COREMAS/PB

FOLHA		PROJETO: PROJETO DE ESTRUTURAL - GARAGEM DAS MÁQUINAS - COREMAS/PB		
(3)/03		LOCALIDADE: MUNICÍPIO DE COREMAS - PB		
DATA		RESPONSÁVEL	RUBRICA	DADOS
DESENHO: JUL/2025		LINCOLN CARTAXO		
CÓPIA:				
VIETO				
ESCALAS		DESENHOS		CONVÊNIO
INDICADAS		• Especificações de perfis do Pórtico Principal • Especificações de perfis da Treliza Terça • 3D (perspectiva) • Resumo de materiais		
				A

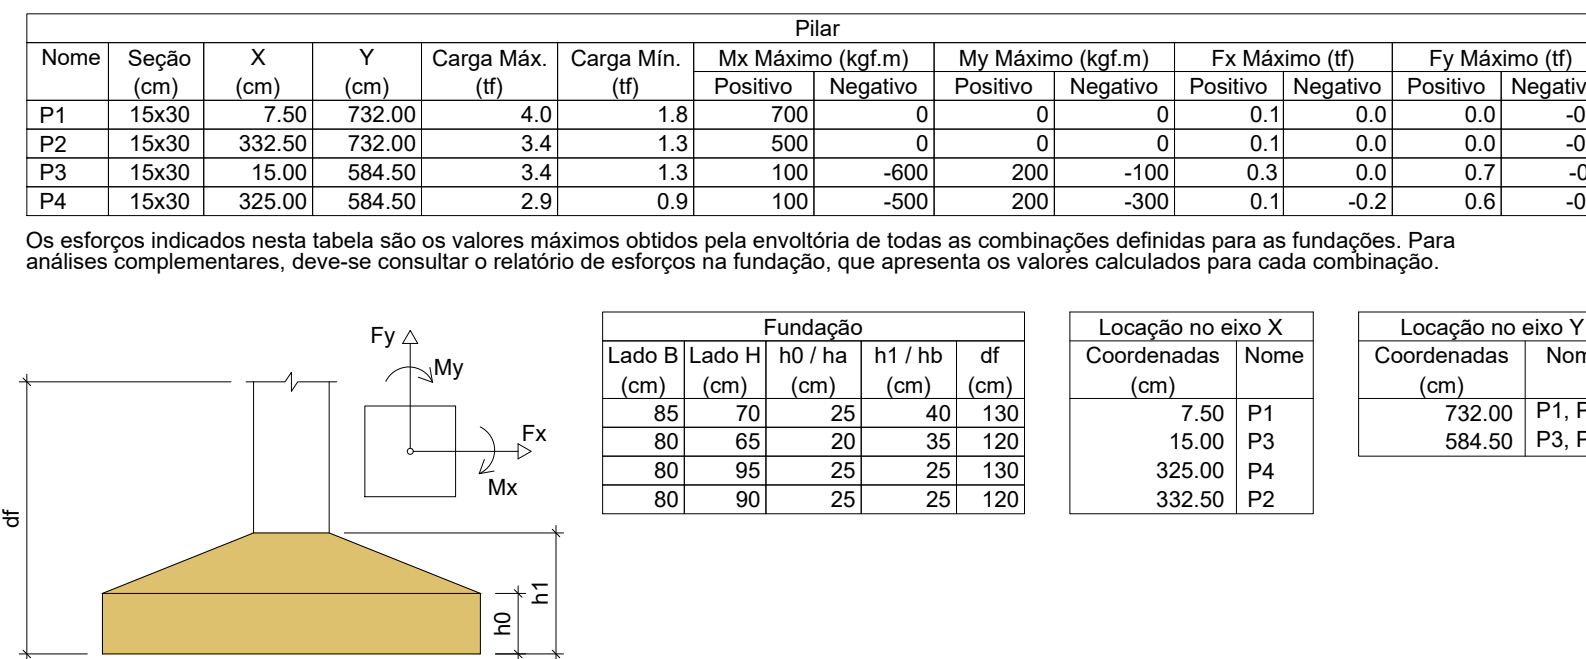


Planta de locação







escala 1:50

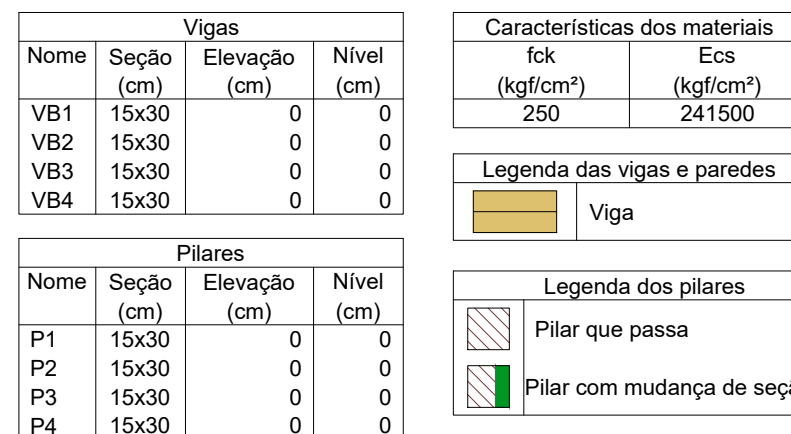


Forma do pavimento +0 (Nível 0)
escala 1:50

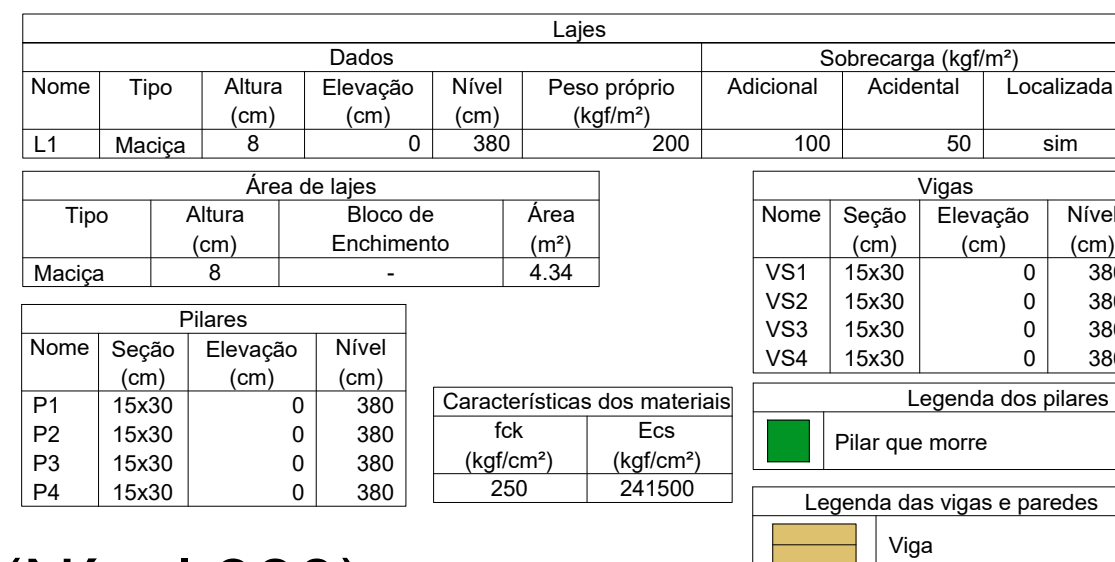

Forma do pavimento +380 (Nível 380)
escala 1:50

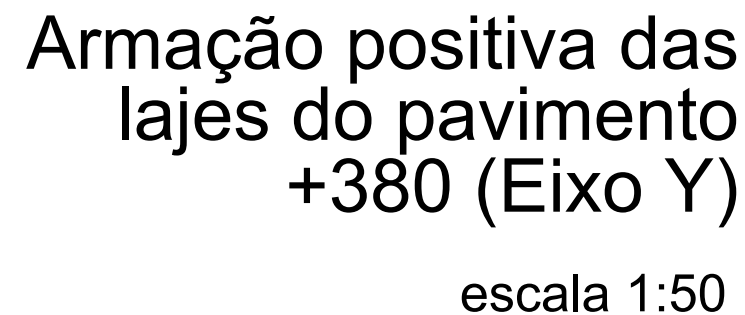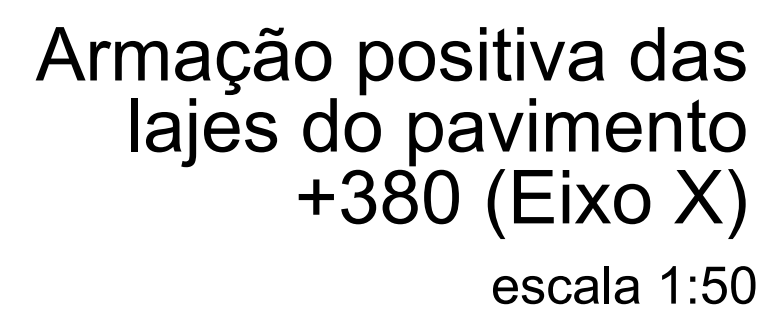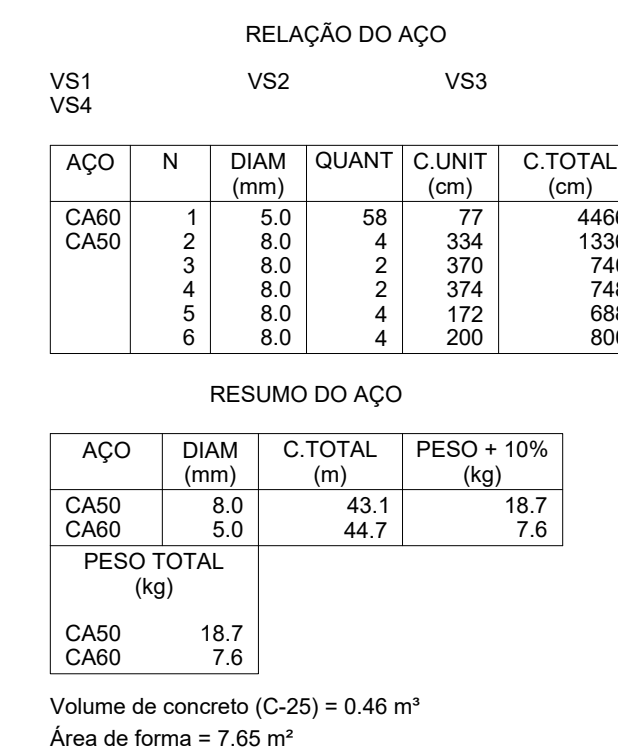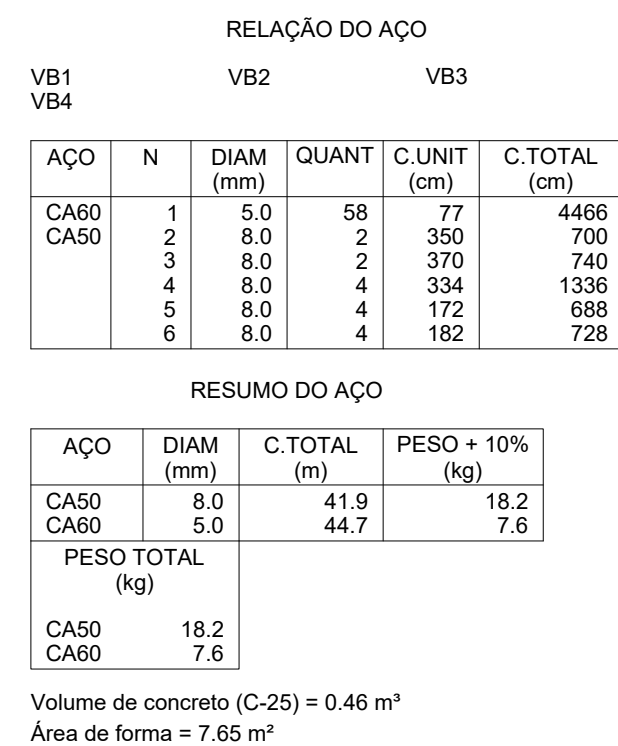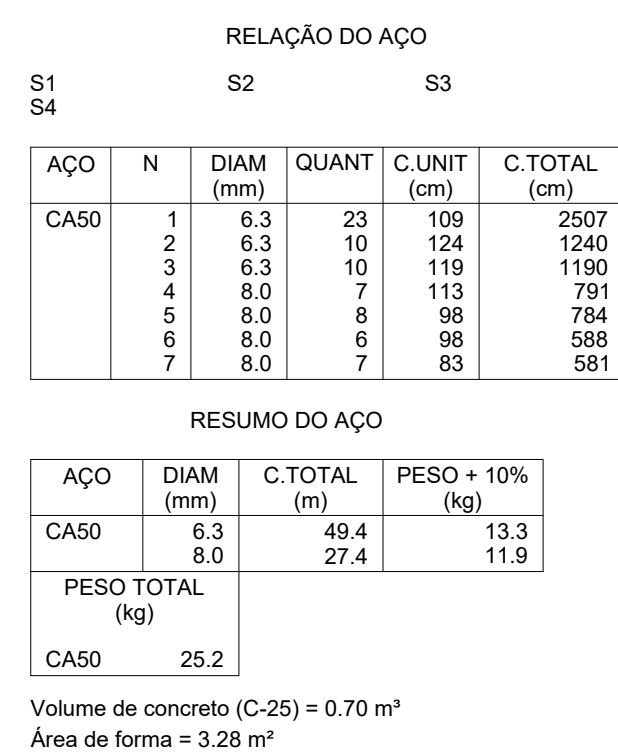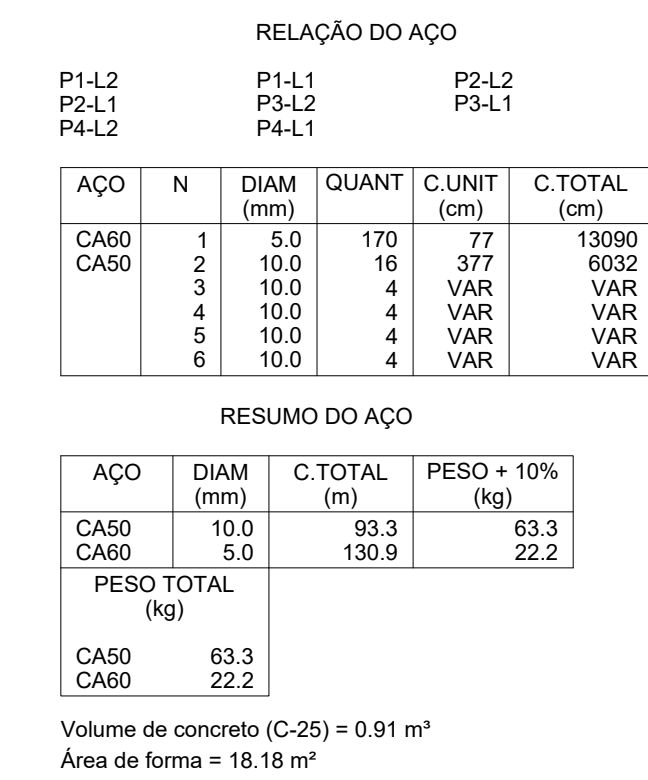

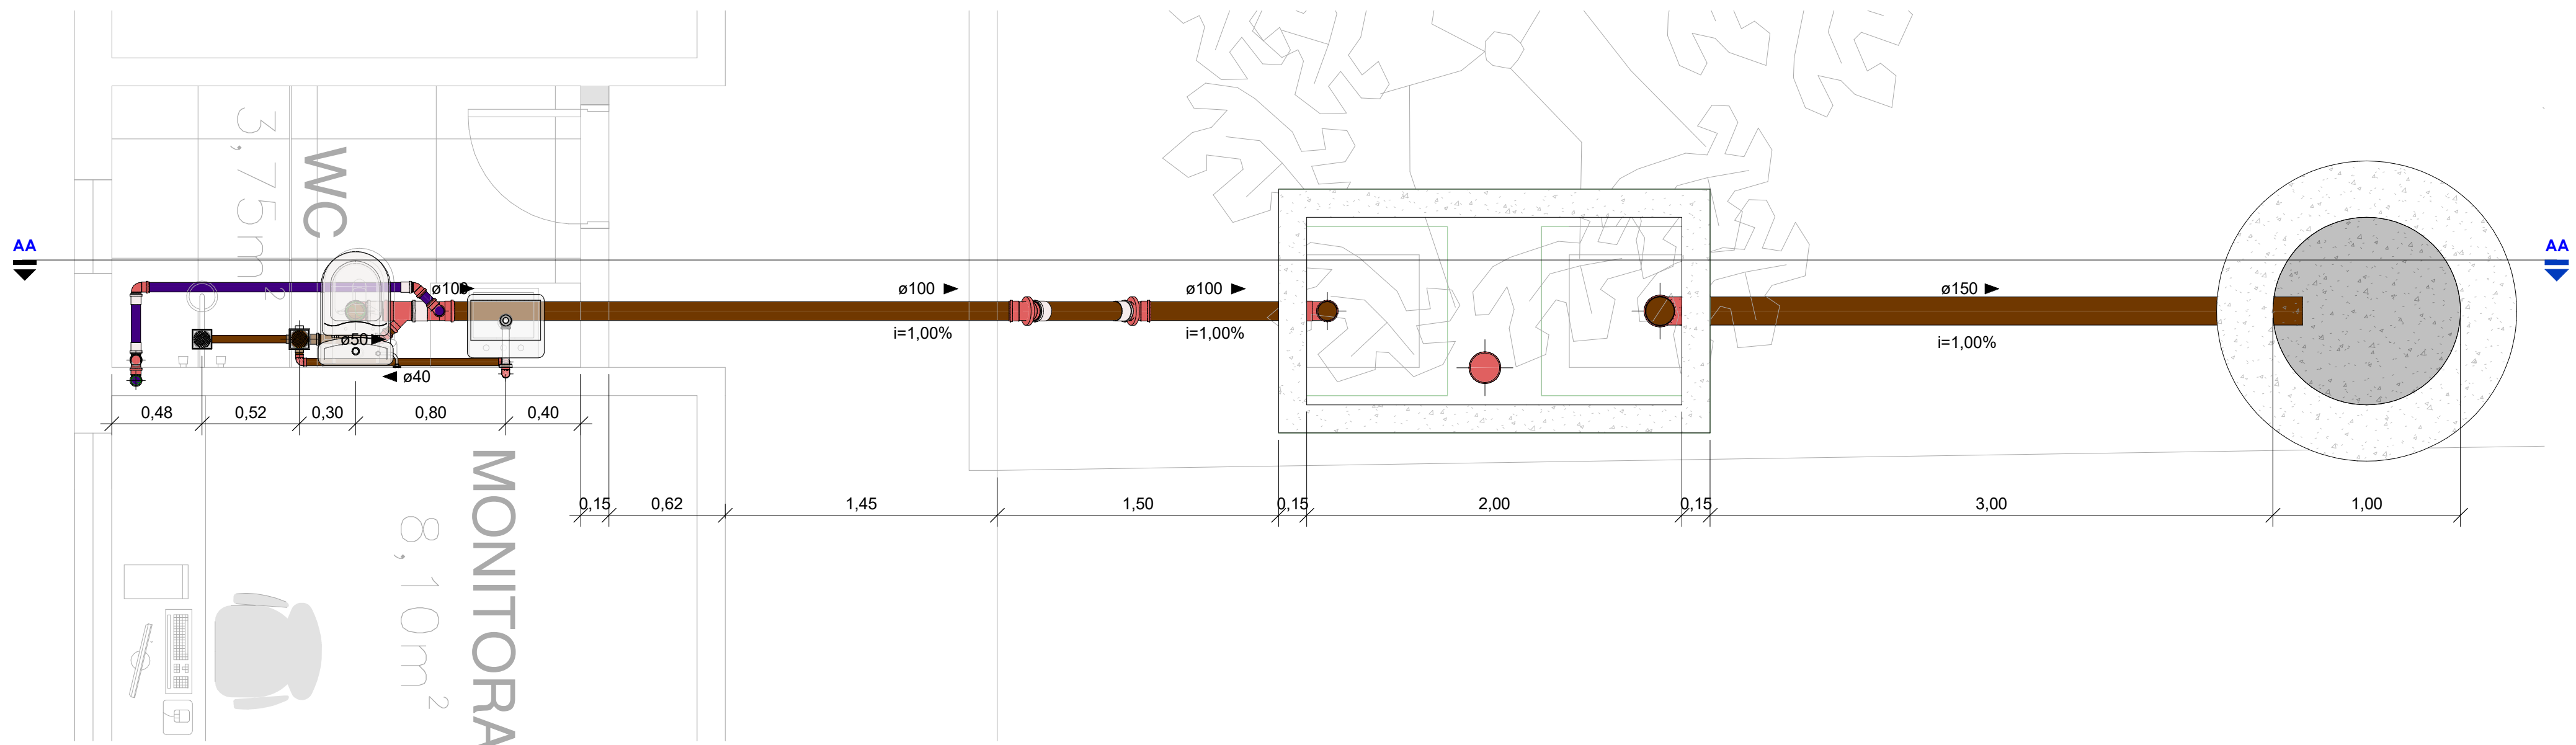

PLANTA BAIXA _DORMITÓRIO_WC_MONITORAMENTO_ - ESC

1/25

MEMORIAL TÉCNICO F.S 01

NORMAS SEGUIDAS

NBR: 13969 - Unidades de Tratamento Complementar e Disposição Final dos Efluentes Líquidos - Projeto, Construção e Operação;
NBR 17076 - Projeto de sistema de tratamento de esgoto de menor porte. Requisitos;
NBR: 7229 - Projeto, Construção e Operação de Sistemas de Tanques Sépticos

DADOS PARA ELABORAÇÃO

Número de Contribuintes (N): 5 Pessoas
Contribuição de Despejos (a): 80
Período de Detenção (T): 1,00
Intervalo de Limpeza (Anos): 1 anos
Temperatura Ambiente > 20 °C
Taxa de Acumulação de Lodo Fresco (Lf): 97
Volume Mínimo (L): 1.449 L ou 1,449 m³

DIMENSÕES TANQUE SÉPTICO


B (Base): 1,00 m
L (Largura): 2,00 m
H (Altura): 1,00 m
Volume Real (L): 2.000 L ou 2,0 m³

ÁREA DE INFILTRAÇÃO SUMIDOURO

Volume de Contribuição (V): 400 L/pessoa.dia
Coeficiente de Infiltração (C1): 105,00 (Área bem selecionada e limpa, variando a areia grossa com cascalho).
Área de Infiltração Mínima (m²): 3,81 m²


DIMENSÕES SUMIDOURO

Diâmetro (m): 1,00 m
Profundidade Útil (m): 2,00 m
Dimensões: Informadas em Planta Baixa
Área de Infiltração Lateral (m²): 6,30 m²
Área de Infiltração Fundo (m²): 0,80 m²
Área de Infiltração Total (m²): 7,1 m²

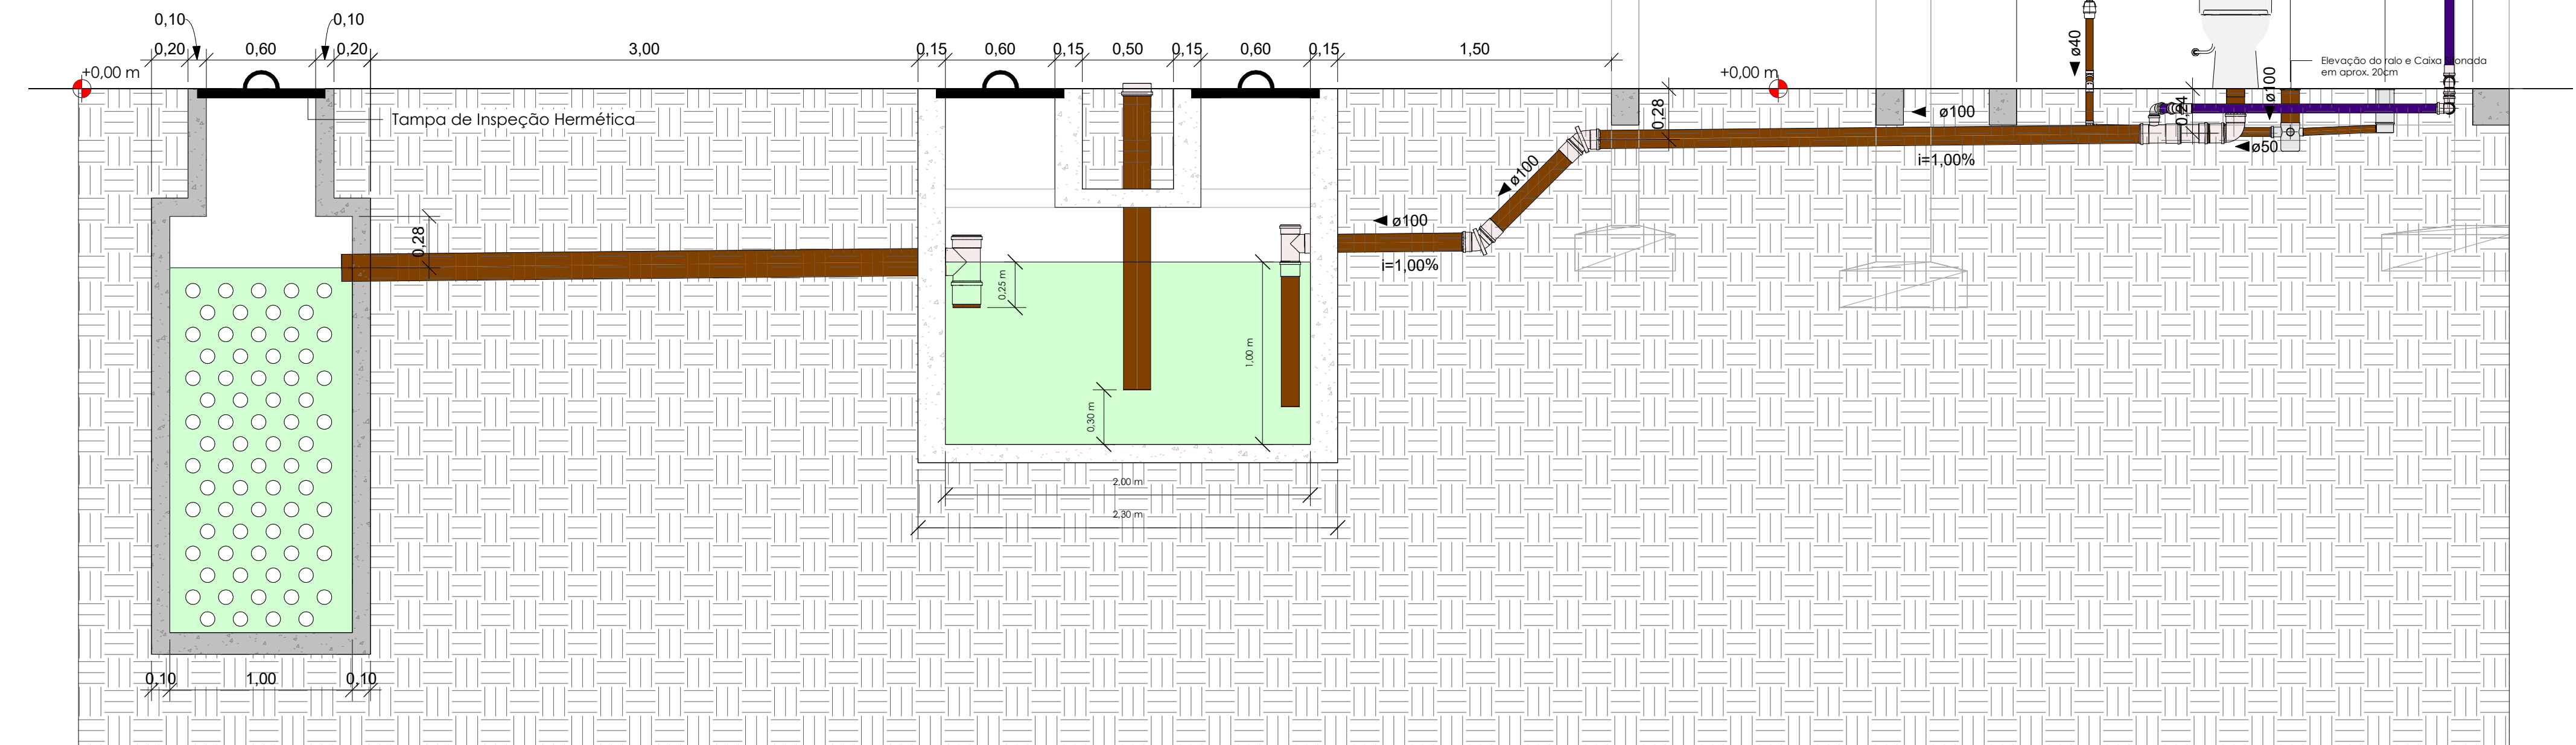

CORTE AA

ESC 1/25

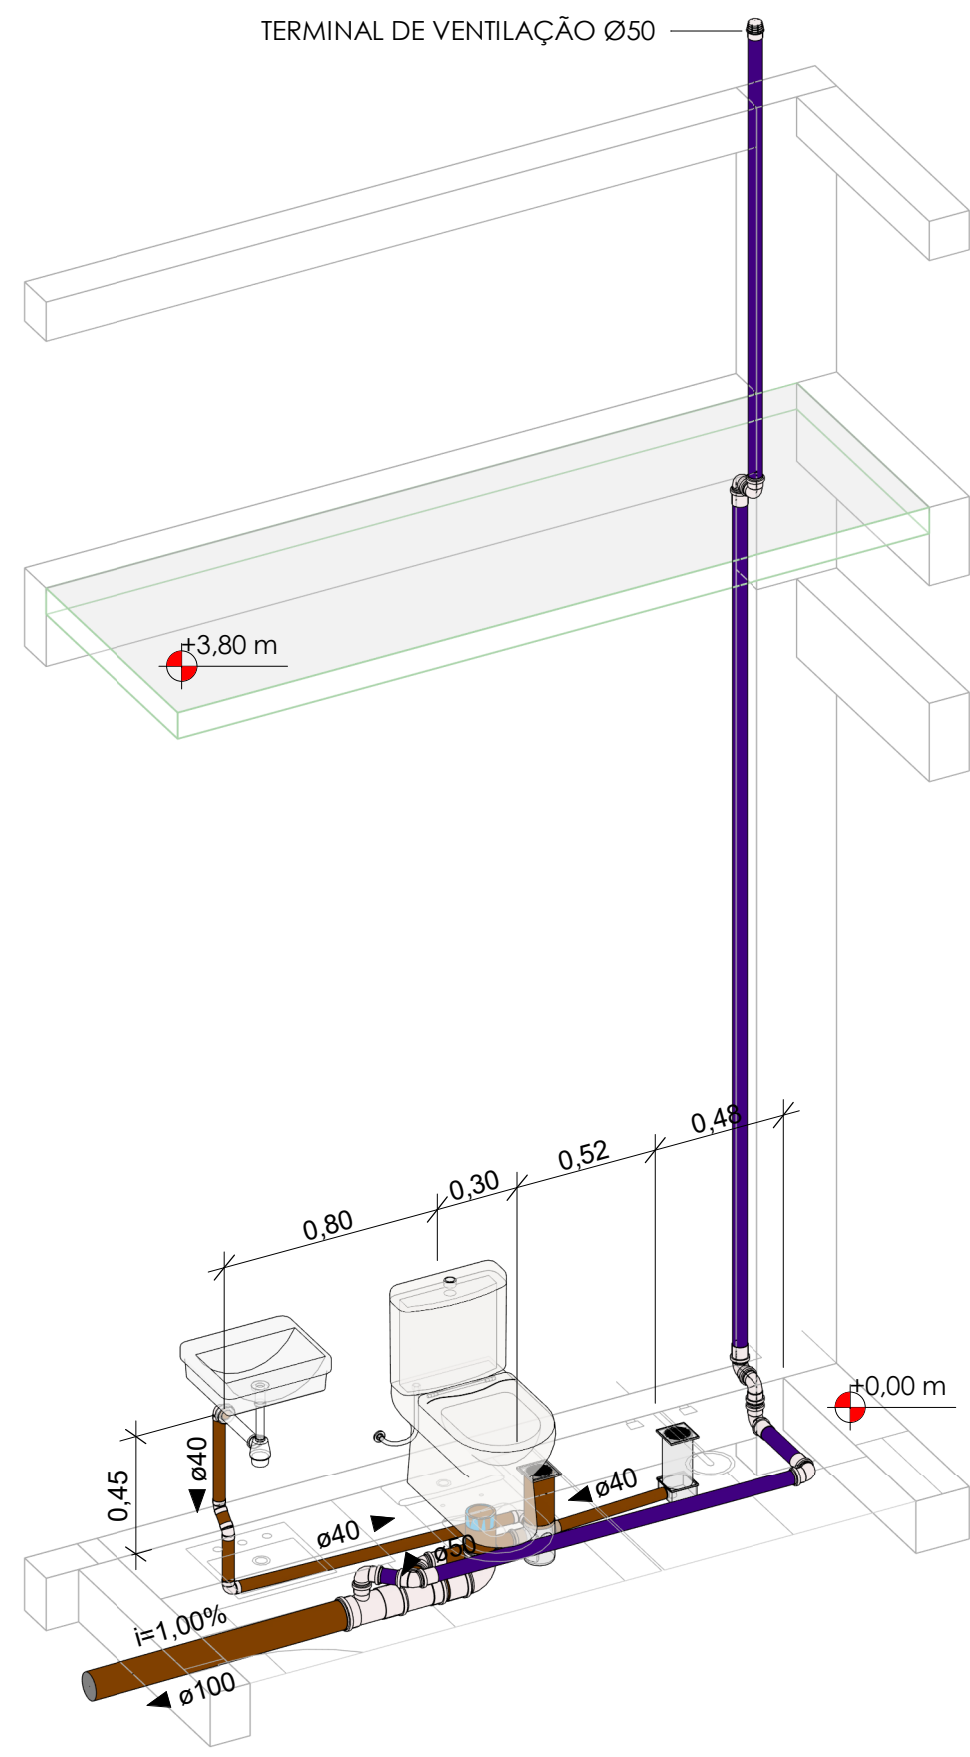

ISOMÉTRICA 02 - WC_MONITORAMENTO - ESC

1/25

LEGENDA:

- TUBULAÇÃO PVC BRANCO - ESGOTO
- TUBULAÇÃO PVC BRANCO SN - VENTILAÇÃO ESGOTO
- TUBULAÇÃO PVC MARROM - ÁGUA FRIA
- TUBO DE QUEDA DE ESGOTO
nn: número da coluna
xx: diâmetro nominal da coluna
- COLUNA DE VENTILAÇÃO
nn: número da coluna
xx: diâmetro nominal da coluna
- COLUNA DE ÁGUA FRIA (BARRILETE)
nn: número da coluna
xx: diâmetro nominal da coluna

CONFORME SUGERIDO PELA ABNT NBR 17076, É NECESSÁRIO UM ESTUDO TÉCNICO DO SOLO PARA VERIFICAÇÃO DA ABSORÇÃO DO SOLO EXISTENTE. O PRESENTE PROJETO NÃO CONTEMPLA OS DADOS DO SOLO LOCAL DESTE EMPREENDIMENTO. VISTO QUE NÃO FOI ENCAMINHADO PELA PREFEITURA, TAIS CÁLCULOS AQUI DESCRITOS SÃO INTERPRETADOS COMO MODELO PADRÃO E QUE NÃO CARACTERIZAM A SITUAÇÃO REAL.

PROPRIETÁRIO: PREFEITURA MUNICIPAL DE COREMAS - PB
LINCOLN CARTAXO DE LIRA JÚNIOR
CNPJ: 06.897.786/1405
Dados: 2025.06.19 17:30:04 -03'00'

PROJETO: LINCOLN CARTAXO DE LIRA JÚNIOR CREA 160.814.689-8


PROJETO: INSTALAÇÕES SANITÁRIAS DA REFORMA DA GARAGEM DE COREMAS
CONCEDENTE: PREFEITURA MUNICIPAL DE COREMAS - PB
CONVENIENTE: MUNICÍPIO DE COREMAS - PB
LOCAL: COREMAS - PB

DATA	19/06/2025	LINCOLN CARTAXO	RUBRICA	DADOS
CÓPIA				CREA 160.814.689-8
VISTO				

PRANCHA: 01 / 03
DESCRIÇÃO: PLANTA BAIXA - DORMITÓRIO, WC, MONITOR. FOSSA E SUMIDOURO, CORTE, MEMORIAL TÉCNICO E ISOMÉTRICA
ESCALA: INDICADA




Av. Gov. Flavio R. Coutinho, 500, sl. 601
Jd. Oceania, 58037-005 - João Pessoa (PB)
Tel +55 99924.4447
e-mail: contato@lclprojetos.com

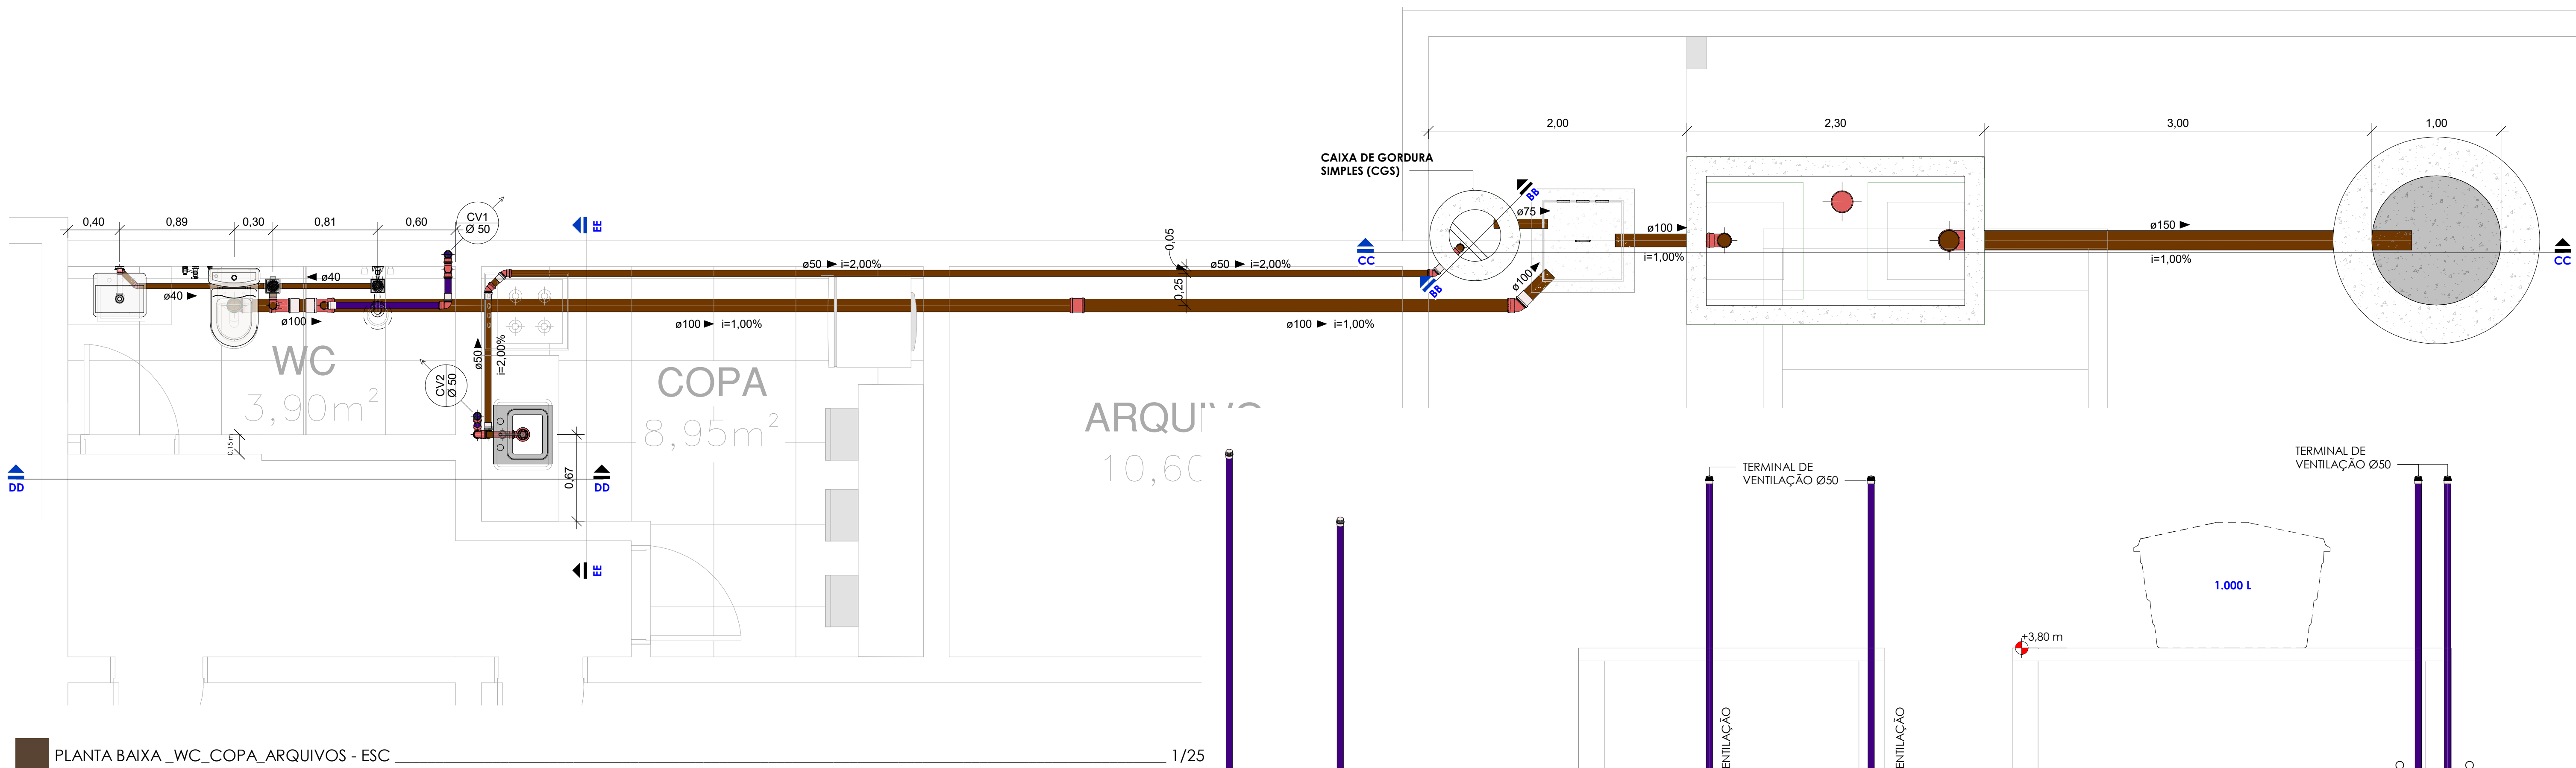


PLANTA BAIXA _WC_COPA_ARQUIVOS - ESC.

1/25

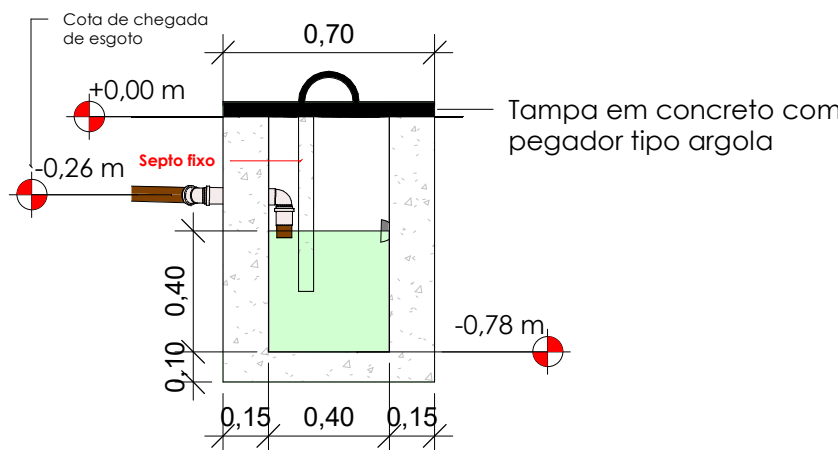


CORTE BB

ESC 1/25

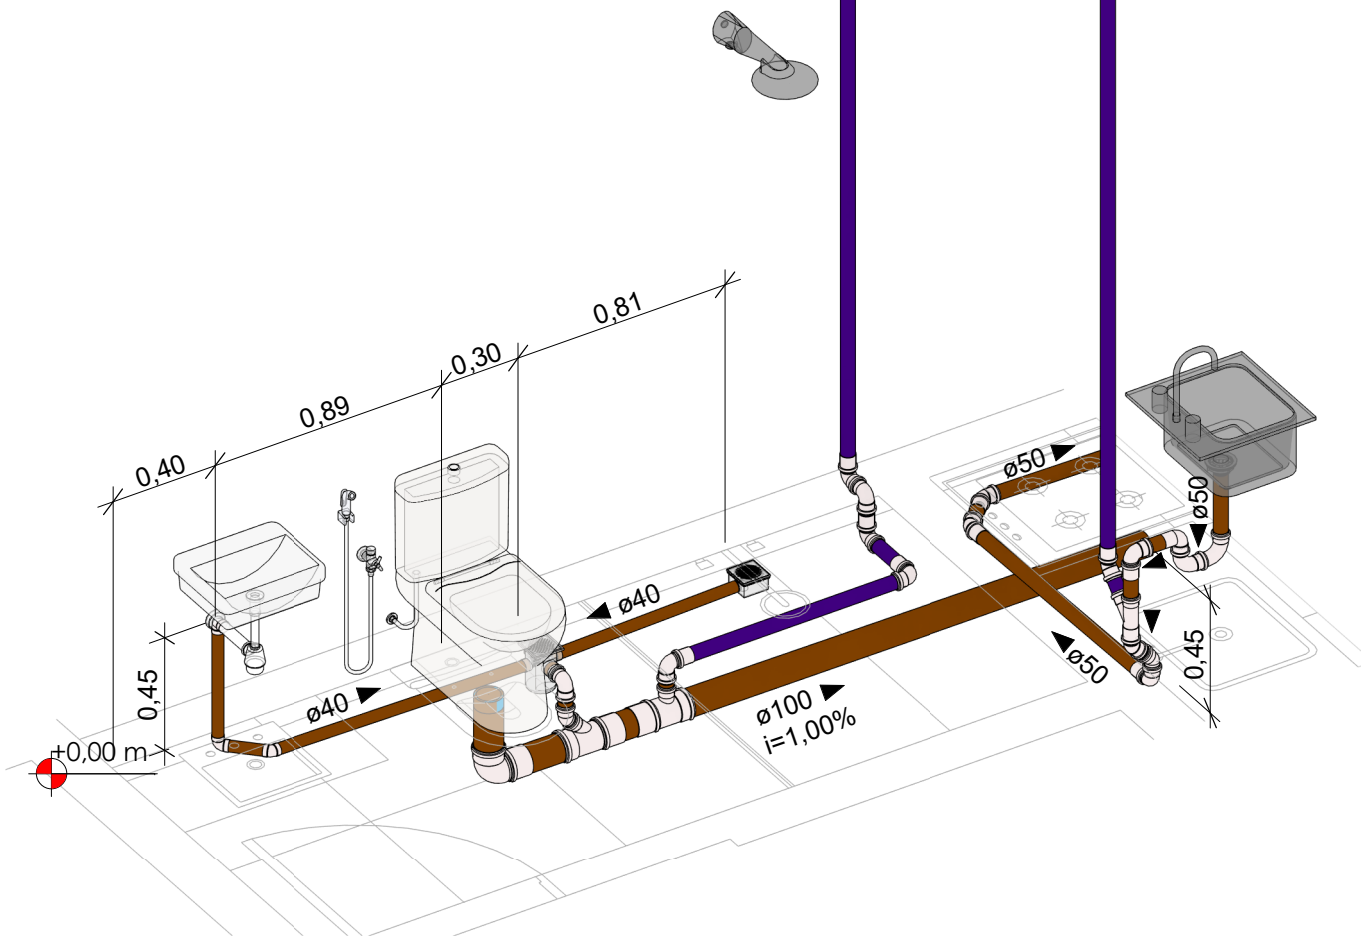


ISOMÉTRICAS 01 - WC_COPA - ESC

1/25

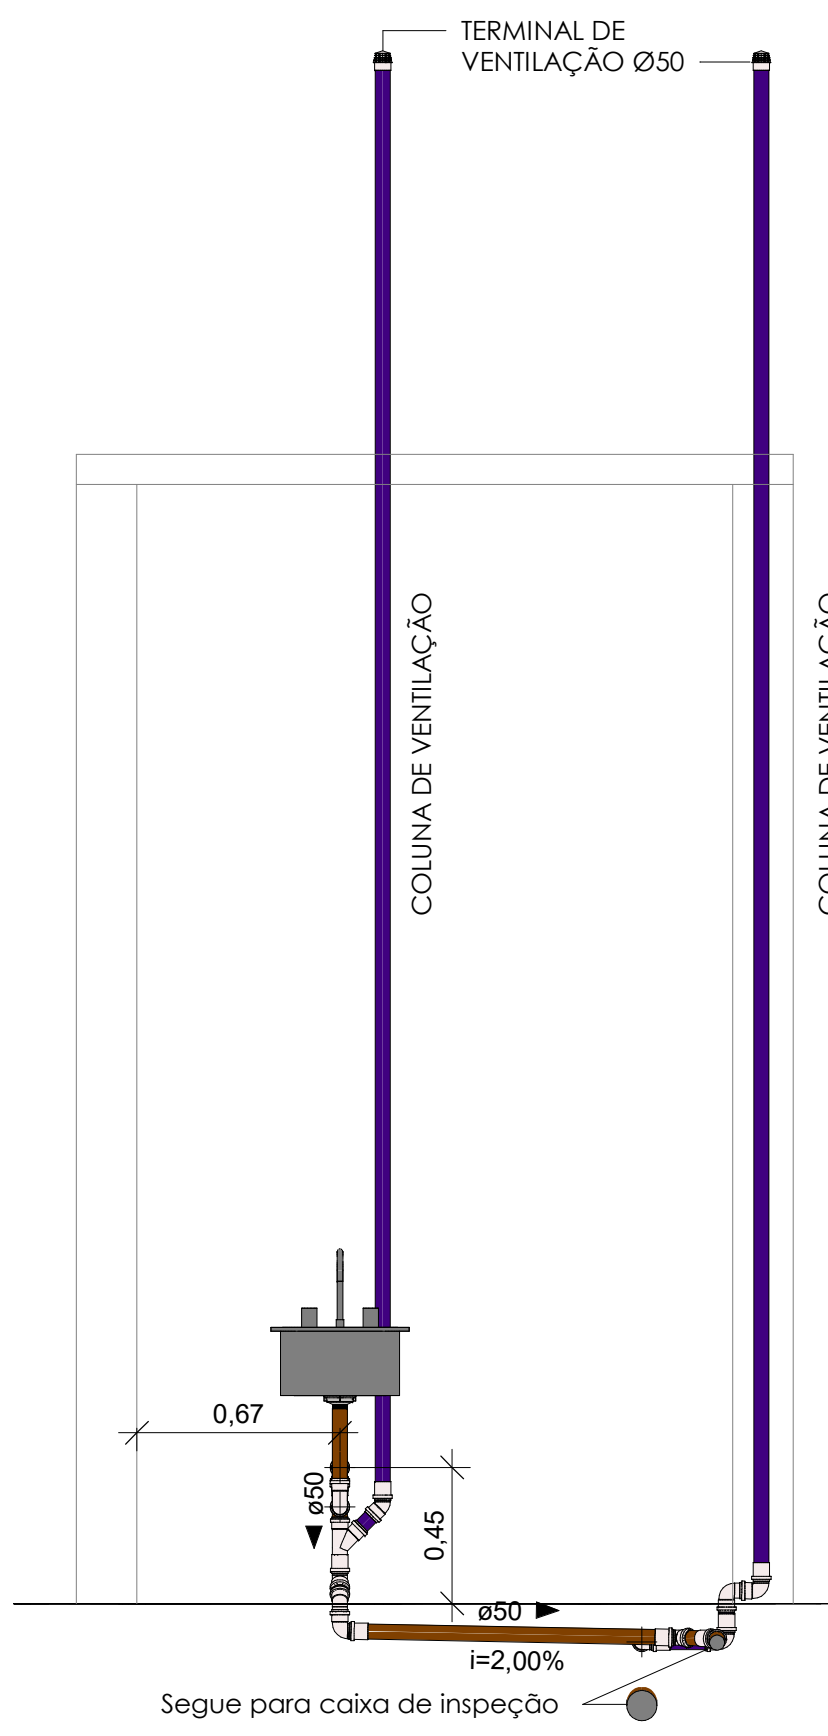

CORTE EE

ESC 1/25

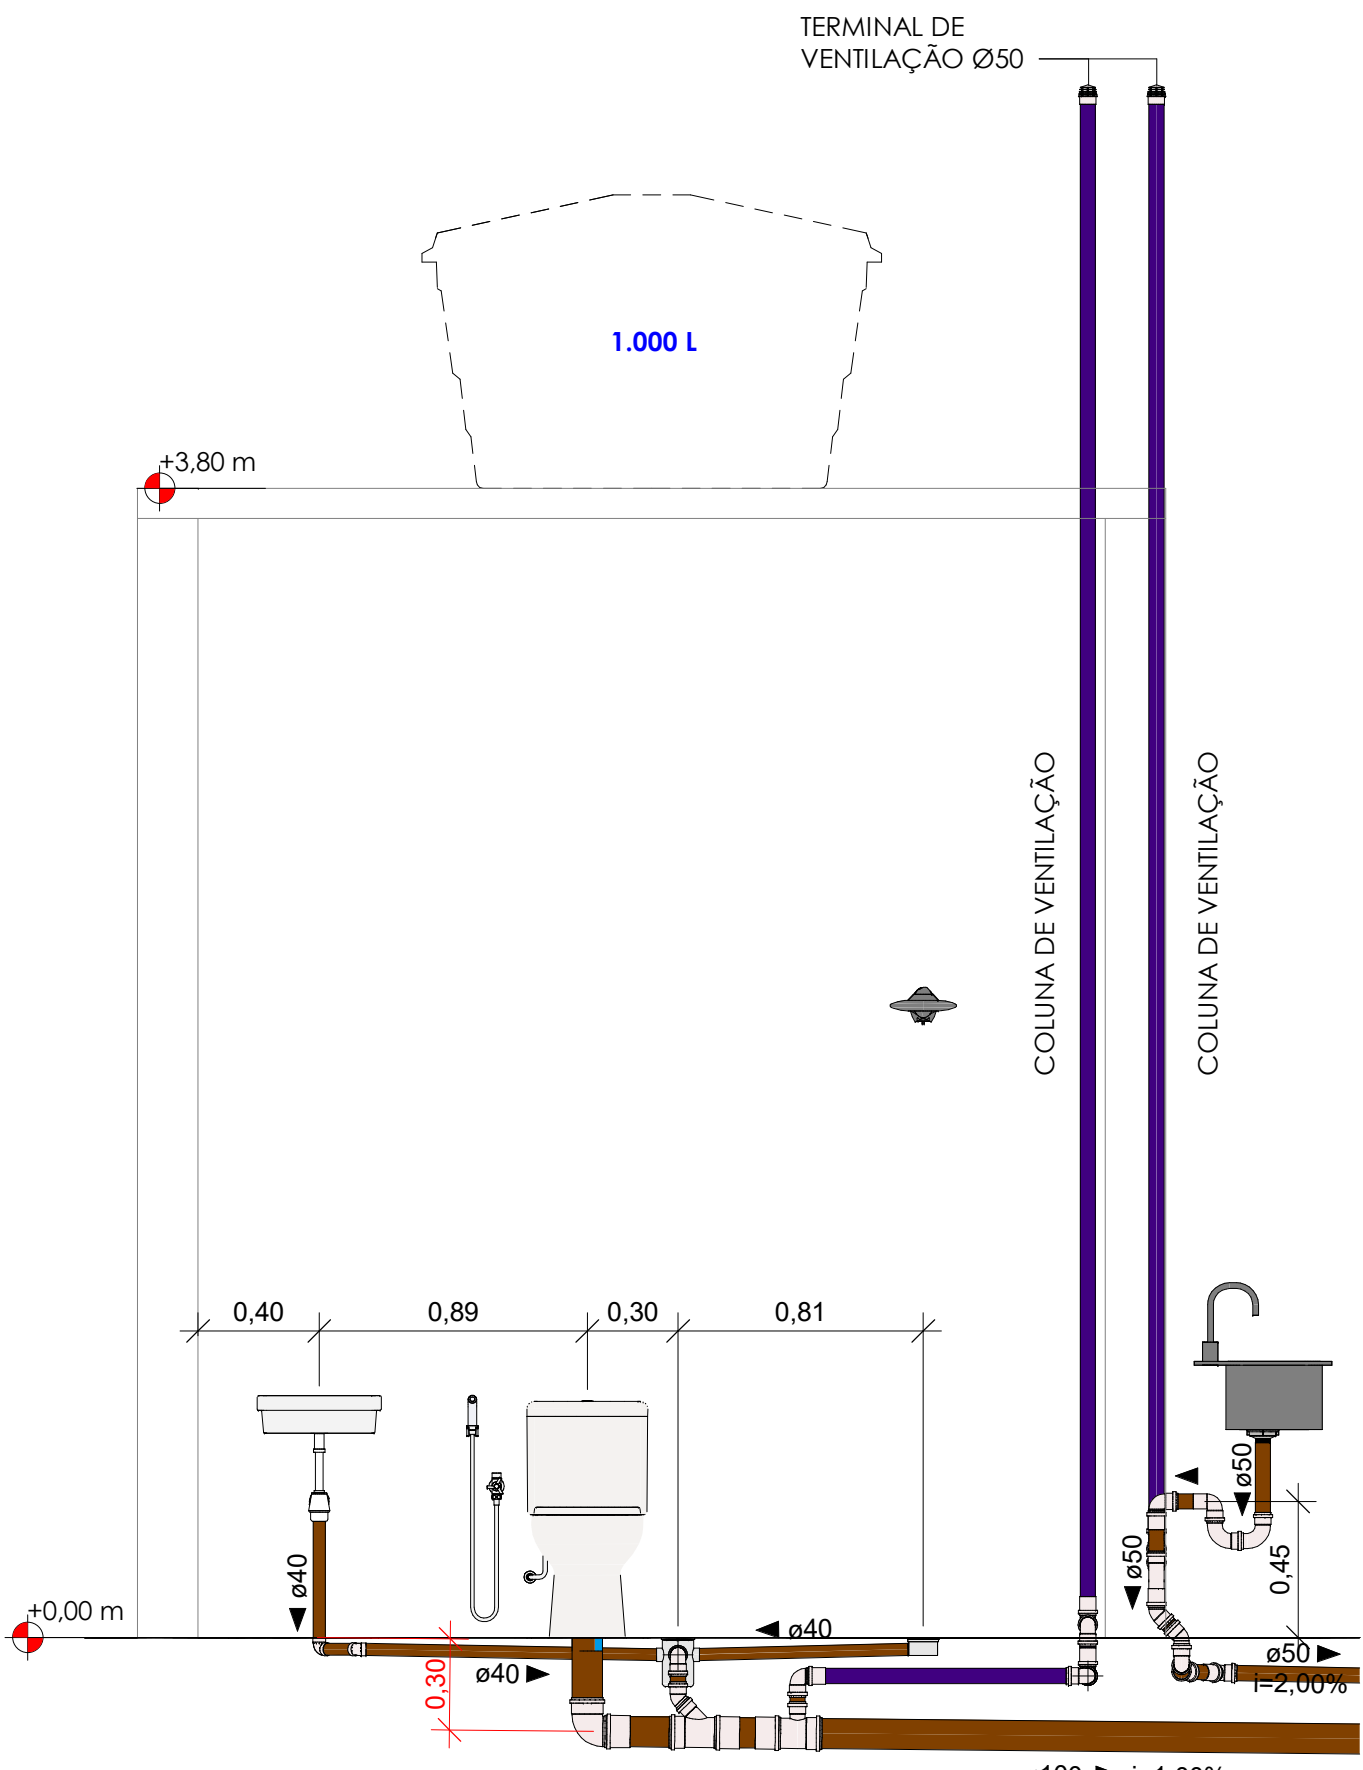

CORTE DD

ESC 1/25

MEMORIAL TÉCNICO F.S 02

NORMAS SEGUIDAS

NBR: 13969 - Unidades de Tratamento Complementar e Disposição Final dos Efluentes Líquidos - Projeto, Construção e Operação;

NBR 17076 - Projeto de sistema de tratamento de esgoto de menor porte. Requisitos;

NBR: 7229 - Projeto, Construção e Operação de Sistemas de Tanques Sépticos

DADOS PARA ELABORAÇÃO

Número de Contribuintes (N): 5 Pessoas
Contribuição de Despejos (q): 80
Período de Detenção (T): 1,00
Intervalo de Limpeza (Anos): 1 anos
Temperatura Ambiente > 20 °C
Taxa de Acumulação de Lodo Fresco (Lf): 97
Volume Mínimo (L): 1.449 L ou 1,449 m³

DIMENSÕES TANQUE SÉPTICO


B (Base): 1,00 m
L (Largura): 2,00 m
H (Altura): 1,00 m
Volume Real (L): 2.000 L ou 2,0 m³

ÁREA DE INFILTRAÇÃO SUMIDOURO

Volume de Contribuição (V): 400 L/pessoa.dia
Coeficiente de Infiltração (C1): 105,00 (Areia bem selecionada e limpa, variando a areia grossa com cascalho).
Área de Infiltração Mínima (m²): 3,81 m²

DIMENSÕES SUMIDOURO

Diâmetro (m): 1,00 m
Profundidade Útil (m): 2,00 m
Dimensões: Informadas em Planta Baixa
Área de Infiltração Lateral (m²): 6,30 m²
Área de Infiltração Fundo (m²): 0,80 m²
Área de Infiltração Total (m²): 7,1 m²

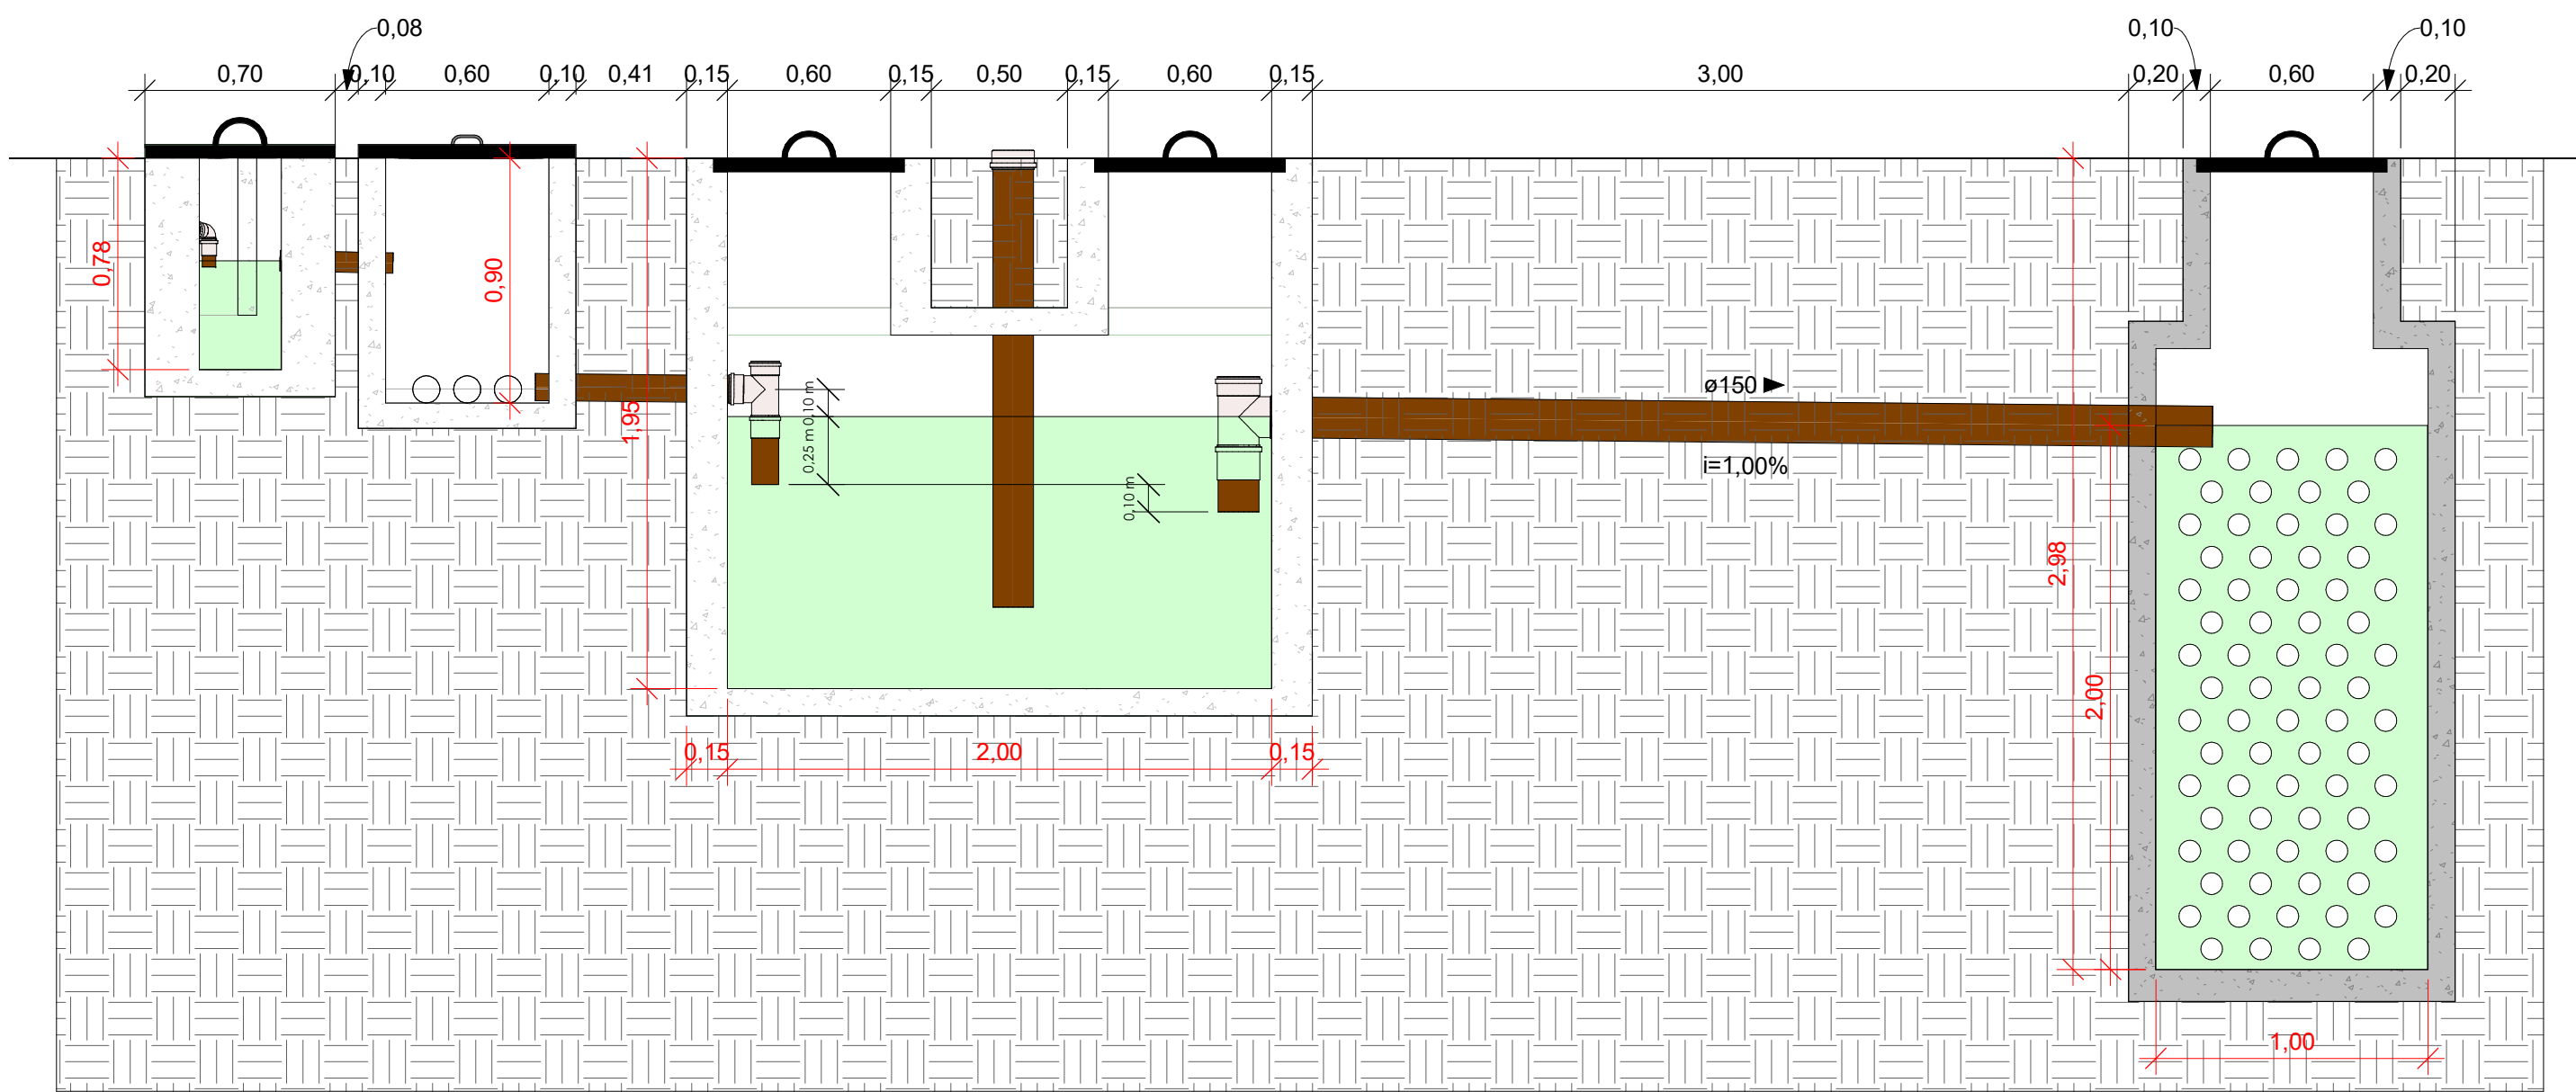

CORTE CC

ESC 1/25

CONFORME SUGERIDO PELA ABNT NBR 17076, É NECESSÁRIO UM ESTUDO TÉCNICO DO SOLO PARA VERIFICAÇÃO DA ABSORÇÃO DO SOLO EXISTENTE. O PRESENTE PROJETO NÃO CONTEMPLA OS DADOS DO SOLO LOCAL DESTA EMPREENDIMENTO, VISTO QUE NÃO FOI ENCAMINHADO PELA PREFEITURA. TALS CÁLCULOS AQUI DESCRITOS SÃO INTERPRETADOS COMO MODELO PADRÃO E QUE NÃO CARACTERIZAM A SITUAÇÃO REAL.

PROPRIETÁRIO: PREFEITURA MUNICIPAL DE COREMAS - PB
LINCOLN CARTAXO DE LIRA JÚNIOR:06897861405
Assinado de forma digital por LINCOLN CARTAXO DE LIRA JÚNIOR:06897861405
Dados: 2025.06.19 17:29:33 -03'00'

PROJETO: LINCOLN CARTAXO DE LIRA JÚNIOR CREA 160.814.689-8

PROJETO: INSTALAÇÕES SANITÁRIAS DA REFORMA DA GARAGEM DE COREMAS

CONCEDENTE: PREFEITURA MUNICIPAL DE COREMAS - PB
CONVENIENTE: MUNICÍPIO DE COREMAS - PB
LOCAL: COREMAS - PB

DATA	RESPONSÁVEL TÉCNICO	RUBRICA	DADOS
19/06/2025	LINCOLN CARTAXO		CREA 160.814.689-8
CÓPIA	CONVÊNIO	SICONV	

PRANCHA:	DESCRIÇÃO:	ESCALA:
02 /03	PLANTA BAIXA - WC, COPA E ARQUIVO FOSSA E SUMIDOURO, CORTES, MEMORIAL TÉCNICO E ISOMÉTRICA	INDICADA



Av. Gov. Flavio R. Coutinho, 500, sl. 601
Jd. Oceania, 58037-005 - João Pessoa (PB)
Tel +55 99924.4447
e-mail: contato@lclprojetos.com

Peças hidráulicas e sanitárias	
Quantidade	Descrição
1	
2	Antiespuma 100 mm, Esgoto - TIGRE
2	Caixa Sifonada Montada com Grelha e Porta Grelha Quadrados Brancos 100 x 150 x 50mm, Esgoto - TIGRE
2	Porta Grelha Quadrado p/ Grelha Quadrada Branca 100mm, Esgoto - TIGRE
2	Prolongamento p/ Caixa Sifonada 100 x 100mm, Esgoto - TIGRE
2	Ralo Quadrado Montado - Branco c/ grelha branca 100x53x40mm, Esgoto - TIGRE
1	Caixa de Inspeção de Alvenaria - Dimensões internas de 60x60cm
2	Bacia Sanitária com Caixa Acoplada
1	Chuveiro
1	Ducha higiênica
2	Cuba de sobrepor
2	Sifão para lavatório 1"x1.1/2" com tubo de 300 mm
2	Flexível 300mm aço inox

Tabela de conexão de tubo GUARITA					
Contagem	Tigre: Descrição	Tigre: Fabricante	Tigre: Linha	Tigre: Produto	Tigre: Sistema

2					
2	Cap 150mm, Esgoto Série Normal - TIGRE	© Tigre S/A	Série Normal	Cap	Esgoto
2	Curva 90° Curta 50mm, Esgoto Série Normal - TIGRE	© Tigre S/A	Série Normal	Curva 90°	Esgoto
2	Curvar 45° 100mm, Esgoto Série Normal - TIGRE	© Tigre S/A	Série Normal	Curvar	Esgoto
3	Joelho 45° 40mm, Esgoto Série Normal - TIGRE	© Tigre S/A	Série Normal	Joelho	Esgoto
9	Joelho 45° 50mm, Esgoto Série Normal - TIGRE	© Tigre S/A	Série Normal	Joelho	Esgoto
1	Joelho 45° 100mm, Esgoto Série Normal - TIGRE	© Tigre S/A	Série Normal	Joelho	Esgoto
5	Joelho 90° 40mm, Esgoto Série Normal - TIGRE	© Tigre S/A	Série Normal	Joelho	Esgoto
17	Joelho 90° 50mm, Esgoto Série Normal - TIGRE	© Tigre S/A	Série Normal	Joelho	Esgoto
2	Joelho 90° 100mm, Esgoto Série Normal - TIGRE	© Tigre S/A	Série Normal	Joelho	Esgoto
1	Junção Simples 50 x 50mm, Esgoto Série Normal - TIGRE	© Tigre S/A	Série Normal	Tê/Junção	Esgoto
2	Junção Simples 100 x 50mm, Esgoto Série Normal - TIGRE	© Tigre S/A	Série Normal	<varia>	Esgoto
1	Luva de Correr 100mm, Esgoto Série Normal - TIGRE	© Tigre S/A	Série Normal	Luva	Esgoto
18	Luva Simples 50mm, Esgoto Série Normal - TIGRE	© Tigre S/A	Série Normal	Luva	Esgoto
10	Luva Simples 100mm, Esgoto Série Normal - TIGRE	© Tigre S/A	Série Normal	Luva	Esgoto
2	Luva Simples 150mm, Esgoto Série Normal - TIGRE	© Tigre S/A	Série Normal	Luva	Esgoto
3	Terminal de Ventilação 50mm, Esgoto Série Normal - TIGRE	© Tigre S/A	Série Normal	Terminal	Esgoto
2	Tê 100 x 50mm, Esgoto Série Normal - TIGRE	© Tigre S/A	Série Normal	Tê/Junção	Esgoto
2	Tê 100 x 100mm, Esgoto Série Normal - TIGRE	© Tigre S/A	Série Normal	Tê/Junção	Esgoto
2	Tê 150 x 150mm, Esgoto Série Normal - TIGRE	© Tigre S/A	Série Normal	Tê/Junção	Esgoto

Caixas - Ralos - Complementos			
Quantidade	Descrição	Tipo de sistema	Fabricante
1	Caixa de Inspeção de Alvenaria - Dimensões internas de 60x60cm	Inspeção/ Esgoto	Moldada In Loco

Tubos de PVC Rígidos para Esgoto - Guarita	
Diâmetro	Comprimento (m)
40 mm	4,36
50 mm	28,17
75 mm	0,42
100 mm	17,08
150 mm	10,39

Conexões - Esgoto	
Quantidade	Descrição
2	Anel de vedação para Vaso Sanitário


LEGENDA:

- TUBULAÇÃO PVC BRANCO - ESGOTO
- TUBULAÇÃO PVC BRANCO SN - VENTILAÇÃO ESGOTO
- TUBULAÇÃO PVC MARROM - ÁGUA FRIA
- TQ-nn
Øxx


-TUBO DE QUEDA DE ESGOTO
nn: número da coluna
xx: diâmetro nominal da coluna
- CV-nn
Øxx

-COLUNA DE VENTILAÇÃO
nn: número da coluna
xx: diâmetro nominal da coluna
- AF-nn
Øxx


-COLUNA DE ÁGUA FRIA (BARRILETE)
nn: número da coluna
xx: diâmetro nominal da coluna

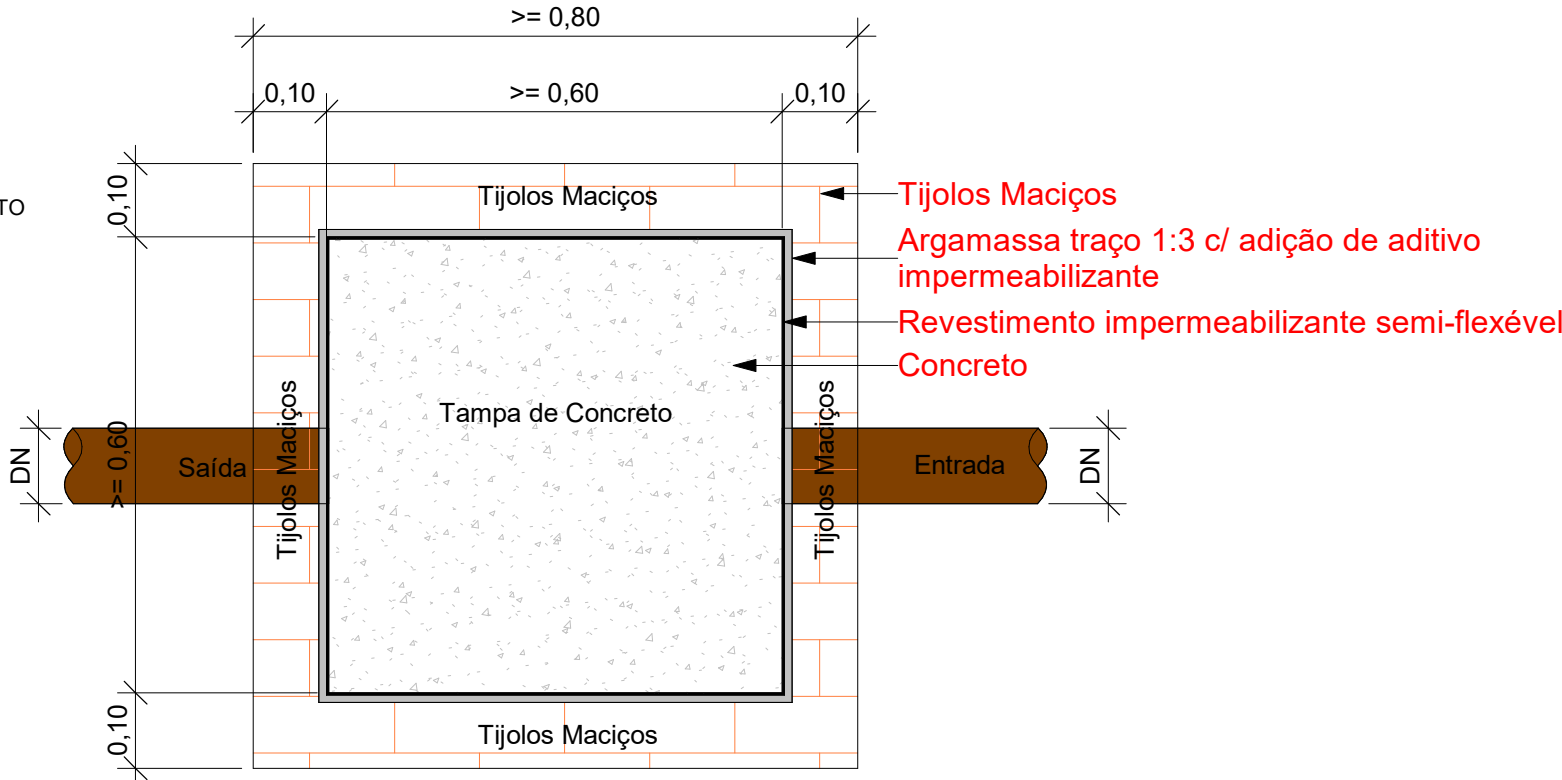

Planta Baixa - Caixa de inspeção
1 : 10

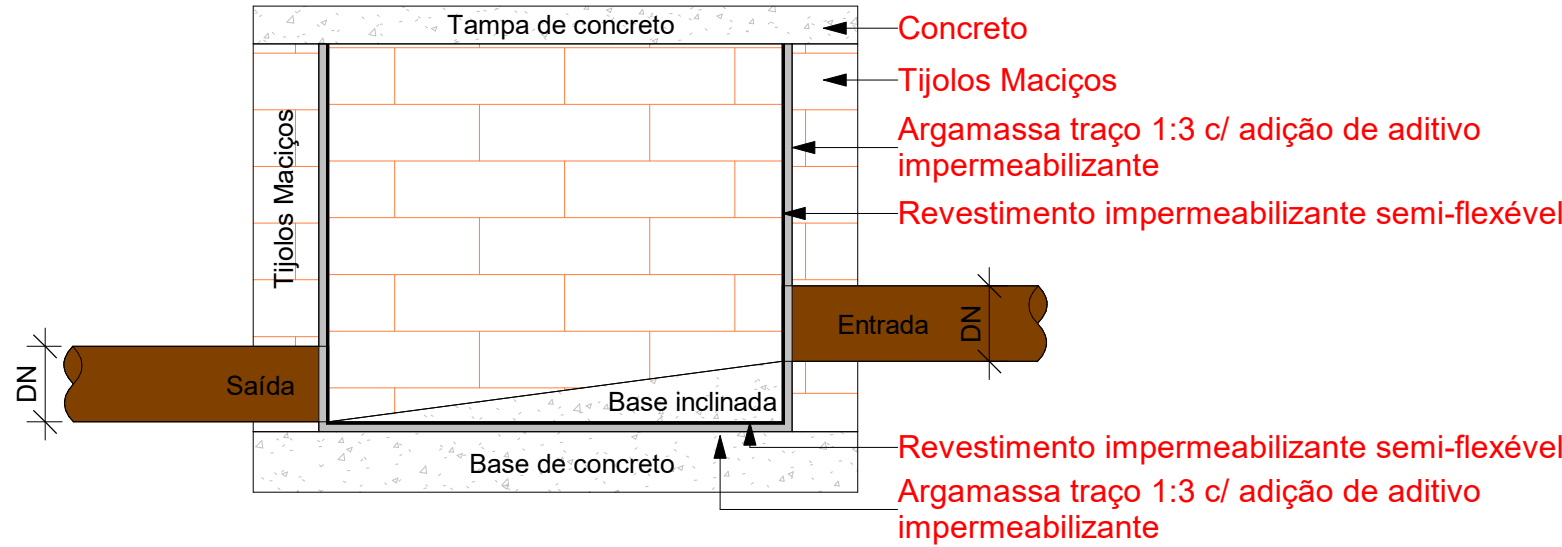

Corte lateral - Caixa de inspeção
1 : 10

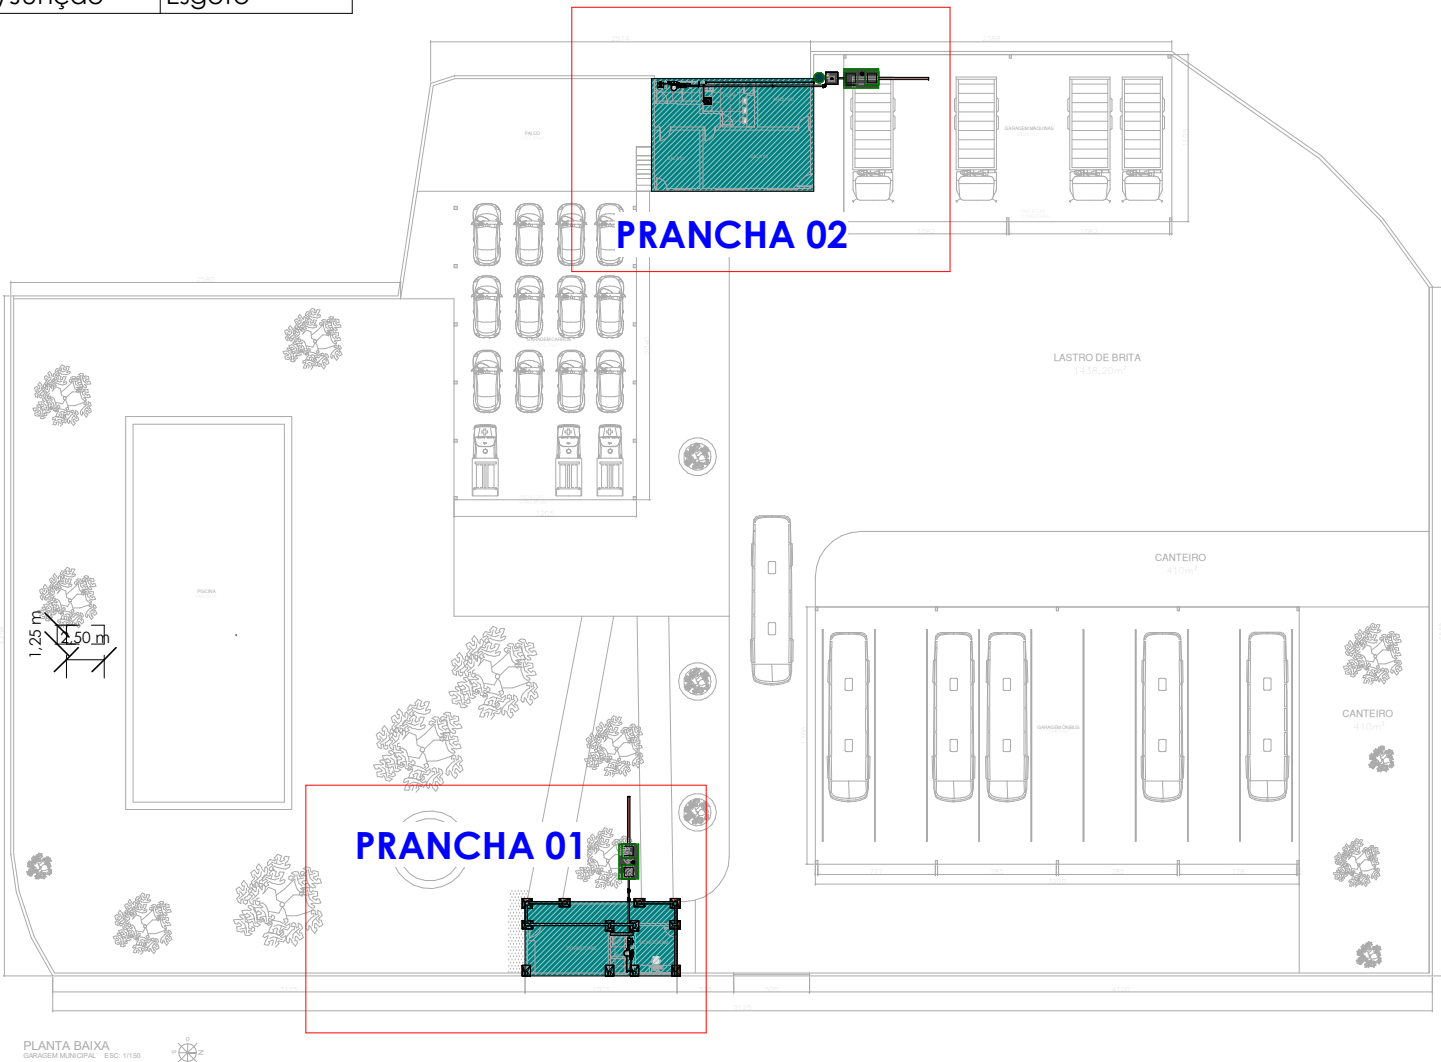

PLANTA BAIXA _GARAGEM_TÉRREO_GERAL_ - ESC 1/500

LINCOLN CARTAXO DE LIRA JUNIOR:06897861405		Assinado de forma digital por LINCOLN CARTAXO DE LIRA JUNIOR:06897861405 Dados: 2025.06.19 17:28:32 -03'00'	
PROPRIETÁRIO:		PREFEITURA MUNICIPAL DE COREMAS - PB	
PROJETO:		LINCOLN CARTAXO DE LIRA JÚNIOR CREA 160.814.689-8	
PROJETO:		INSTALAÇÕES SANITÁRIAS DA REFORMA DA GARAGEM DE COREMAS	
CONCEDENTE:		PREFEITURA MUNICIPAL DE COREMAS - PB	
CONVENIENTE:		MUNICÍPIO DE COREMAS - PB	
LOCAL:		COREMAS - PB	
		RESPONSÁVEL TÉCNICO	RUBRICA
DATA	19/06/2025	LINCOLN CARTAXO	CREA 160.814.689-8
CÓPIA			
VISTO			
PRANCHA:		DESCRIÇÃO:	ESCALA:
03 / 03		PLANTA BAIXA - GERAL TÉRREO MAPEAMENTO DAS PRANCHAS QUANTITATIVOS E CORTE	INDICADA



Av. Gov. Flavio R. Coutinho, 500, sl. 601
Jd. Oceania, 58037-005 - João Pessoa (PB)
Tel +55 99924.4447
e-mail: contato@lclprojetos.com


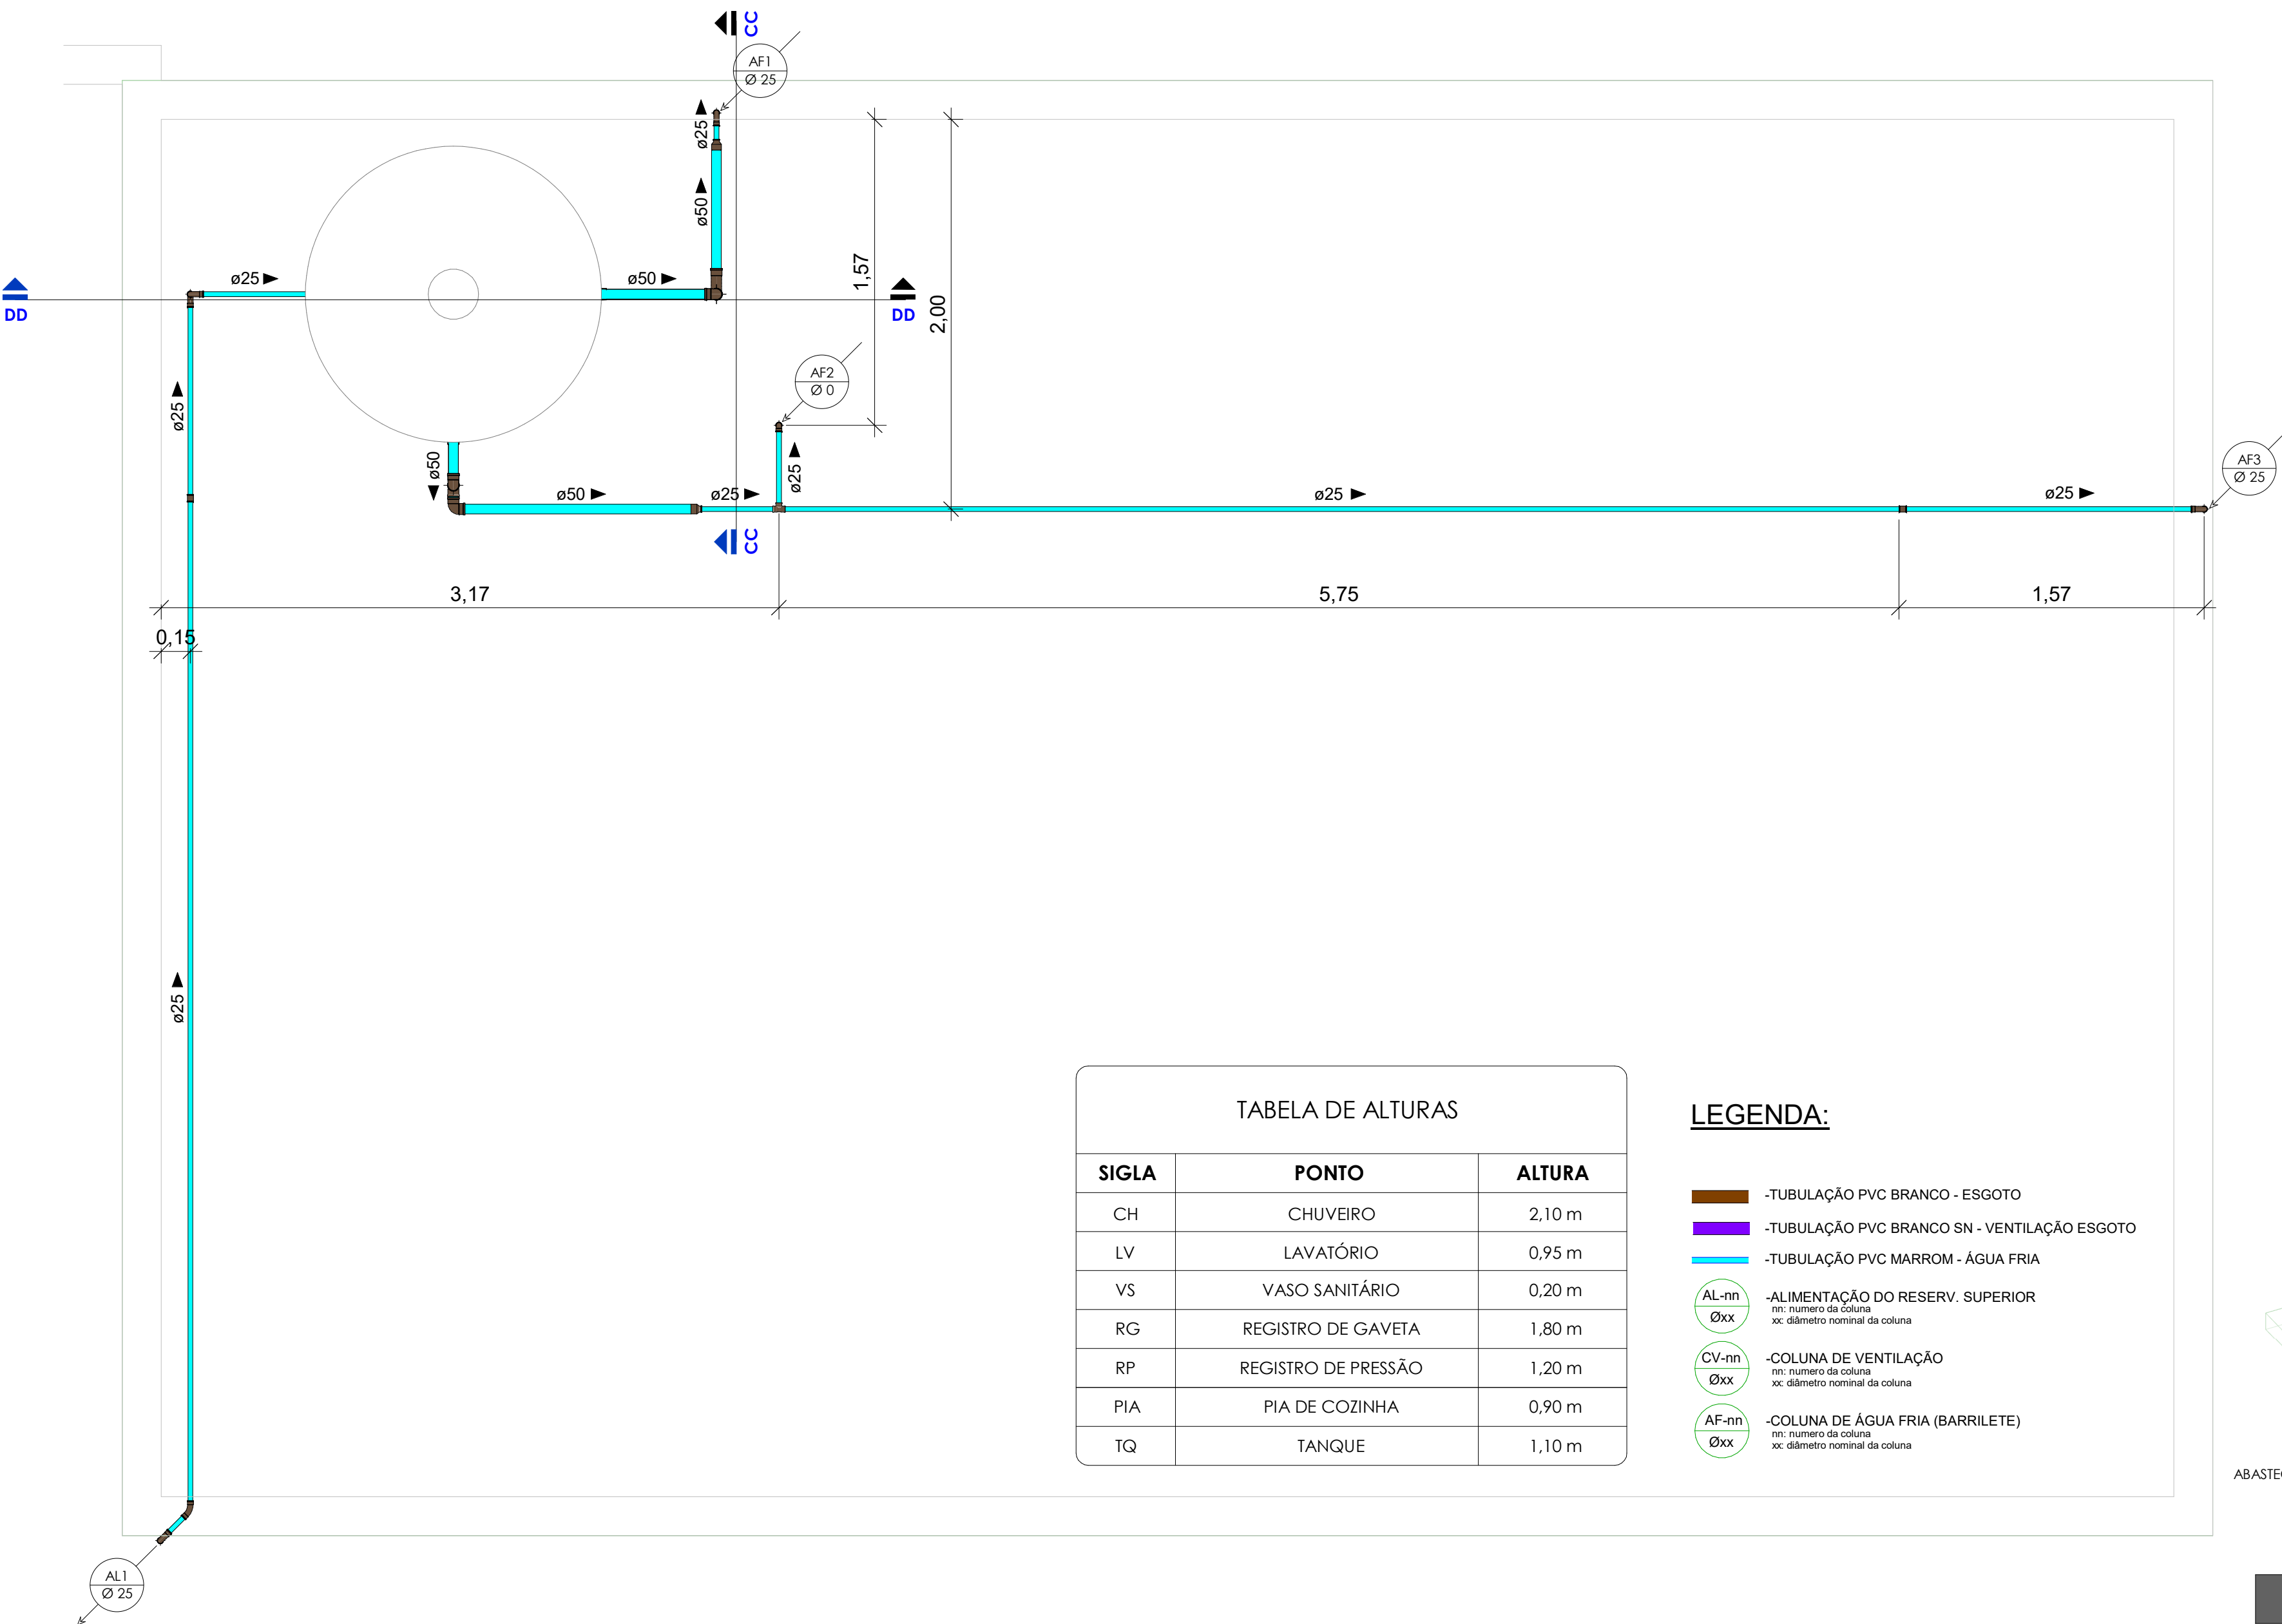



TABELA DE ALTURAS		
SIGLA	PONTO	ALTURA
CH	CHUVEIRO	2,10 m
LV	LAVATÓRIO	0,95 m
VS	VASO SANITÁRIO	0,20 m
RG	REGISTRO DE GAVETA	1,80 m
RP	REGISTRO DE PRESSÃO	1,20 m
PIA	PIA DE COZINHA	0,90 m
TQ	TANQUE	1,10 m

- LEGENDA:**
- TUBULAÇÃO PVC BRANCO - ESGOTO
 - TUBULAÇÃO PVC BRANCO SN - VENTILAÇÃO ESGOTO
 - TUBULAÇÃO PVC MARROM - ÁGUA FRIA
 - AL-nn
Øxx - ALIMENTAÇÃO DO RESERV. SUPERIOR
nn: número da coluna
xx: diâmetro nominal da coluna
 - CV-nn
Øxx - COLUNA DE VENTILAÇÃO
nn: número da coluna
xx: diâmetro nominal da coluna
 - AF-nn
Øxx - COLUNA DE ÁGUA FRIA (BARRILETE)
nn: número da coluna
xx: diâmetro nominal da coluna


PLANTA BAIXA_CAIXA_D'ÁGUA_02 - ESC 1/25

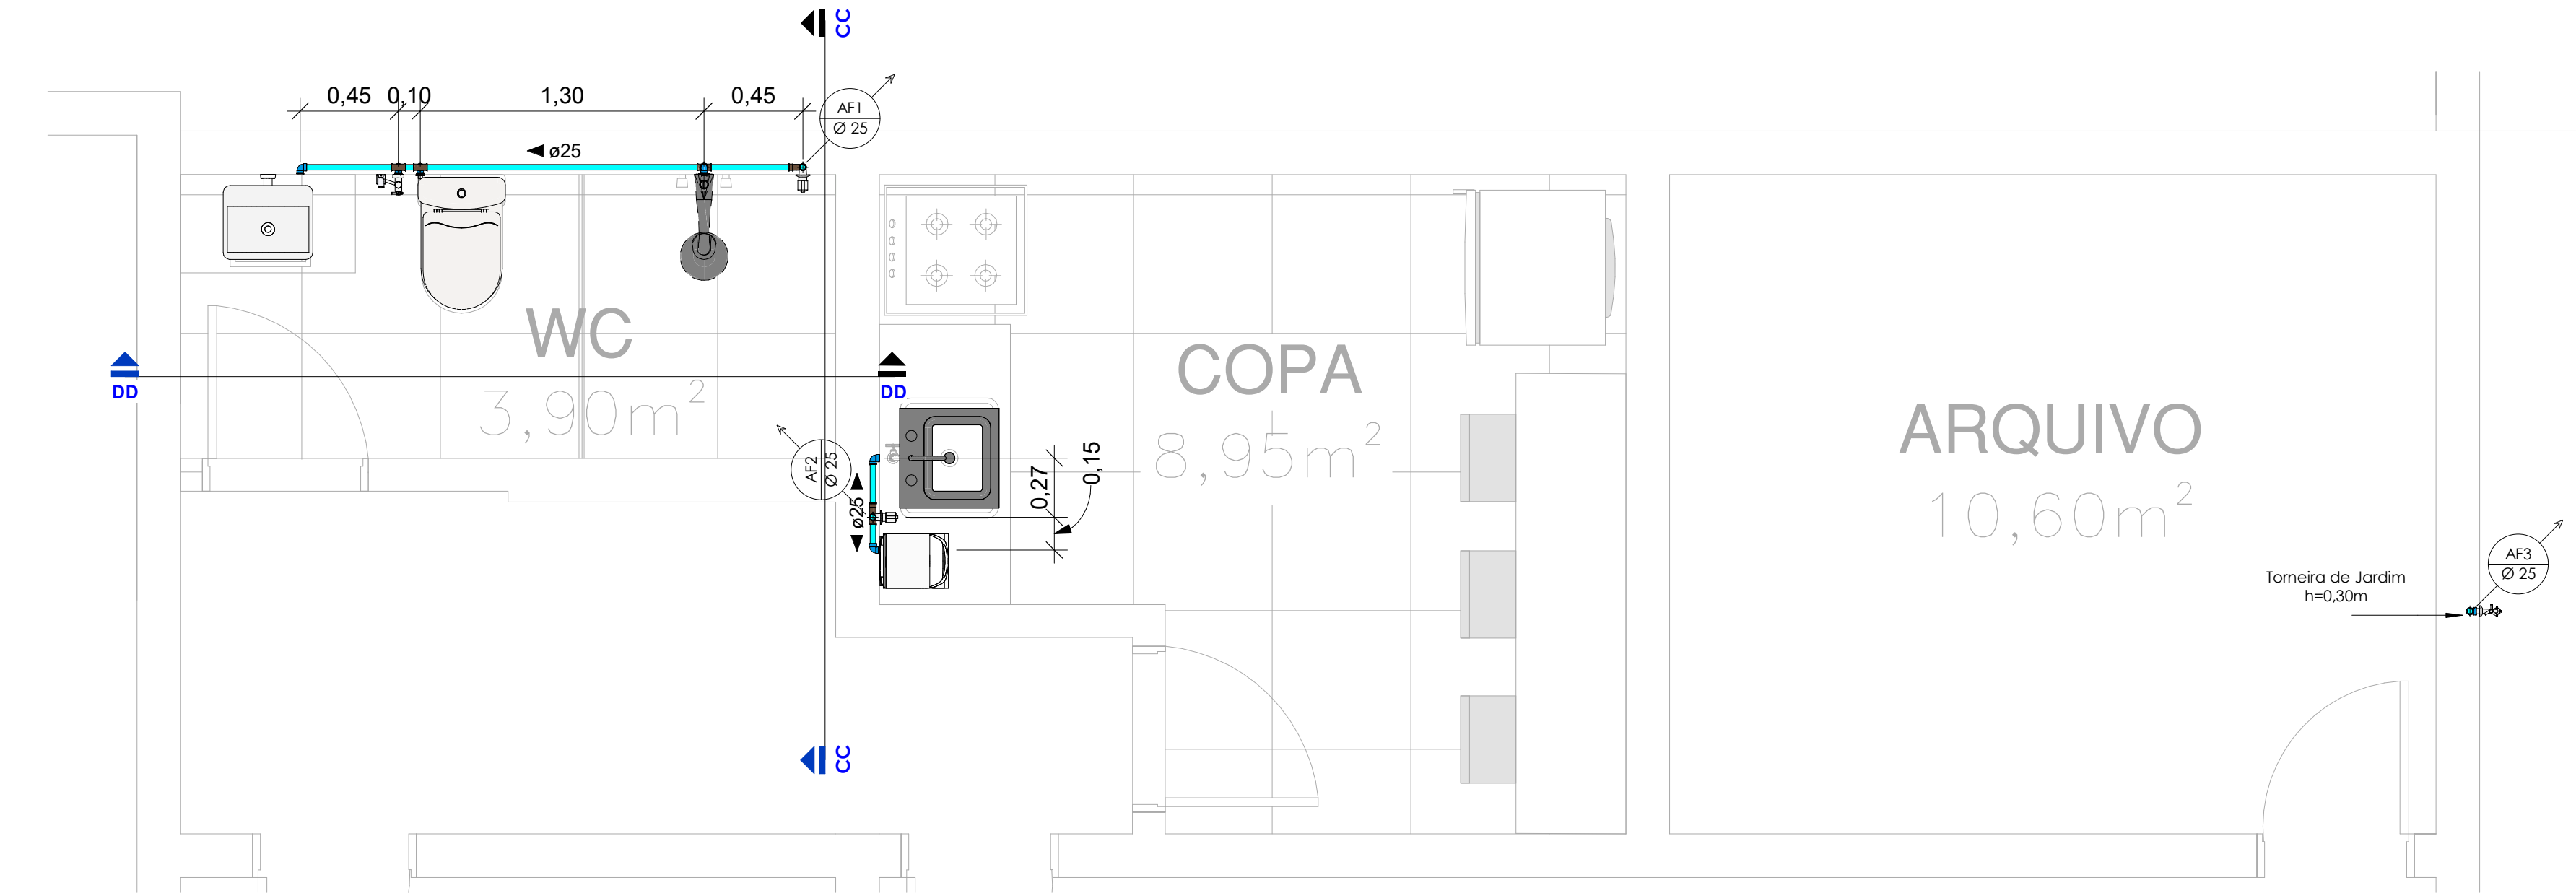


PLANTA BAIXA_REFORMA_GARAGEM_COREMAS_TÉRREO_COPA_WC_ARQUIVO - ESC 1/25

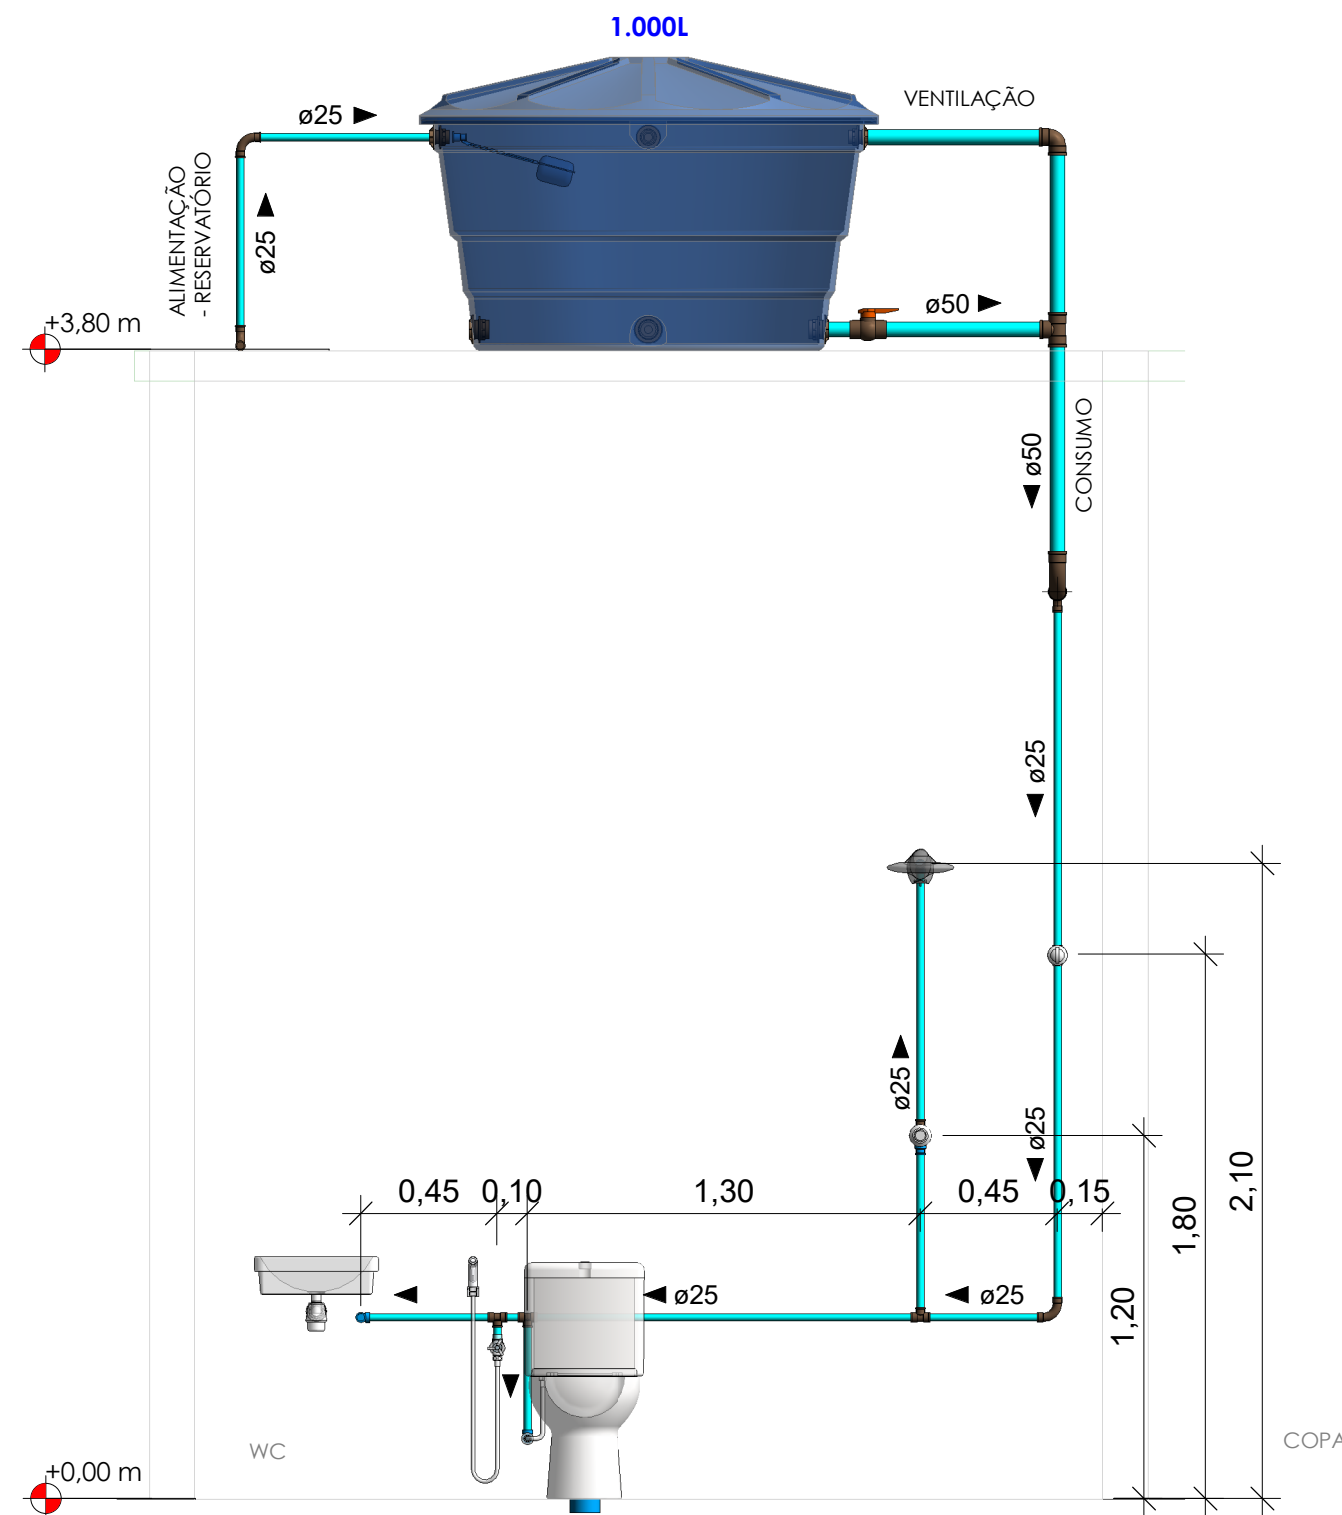


CORTE DD ESC 1/25

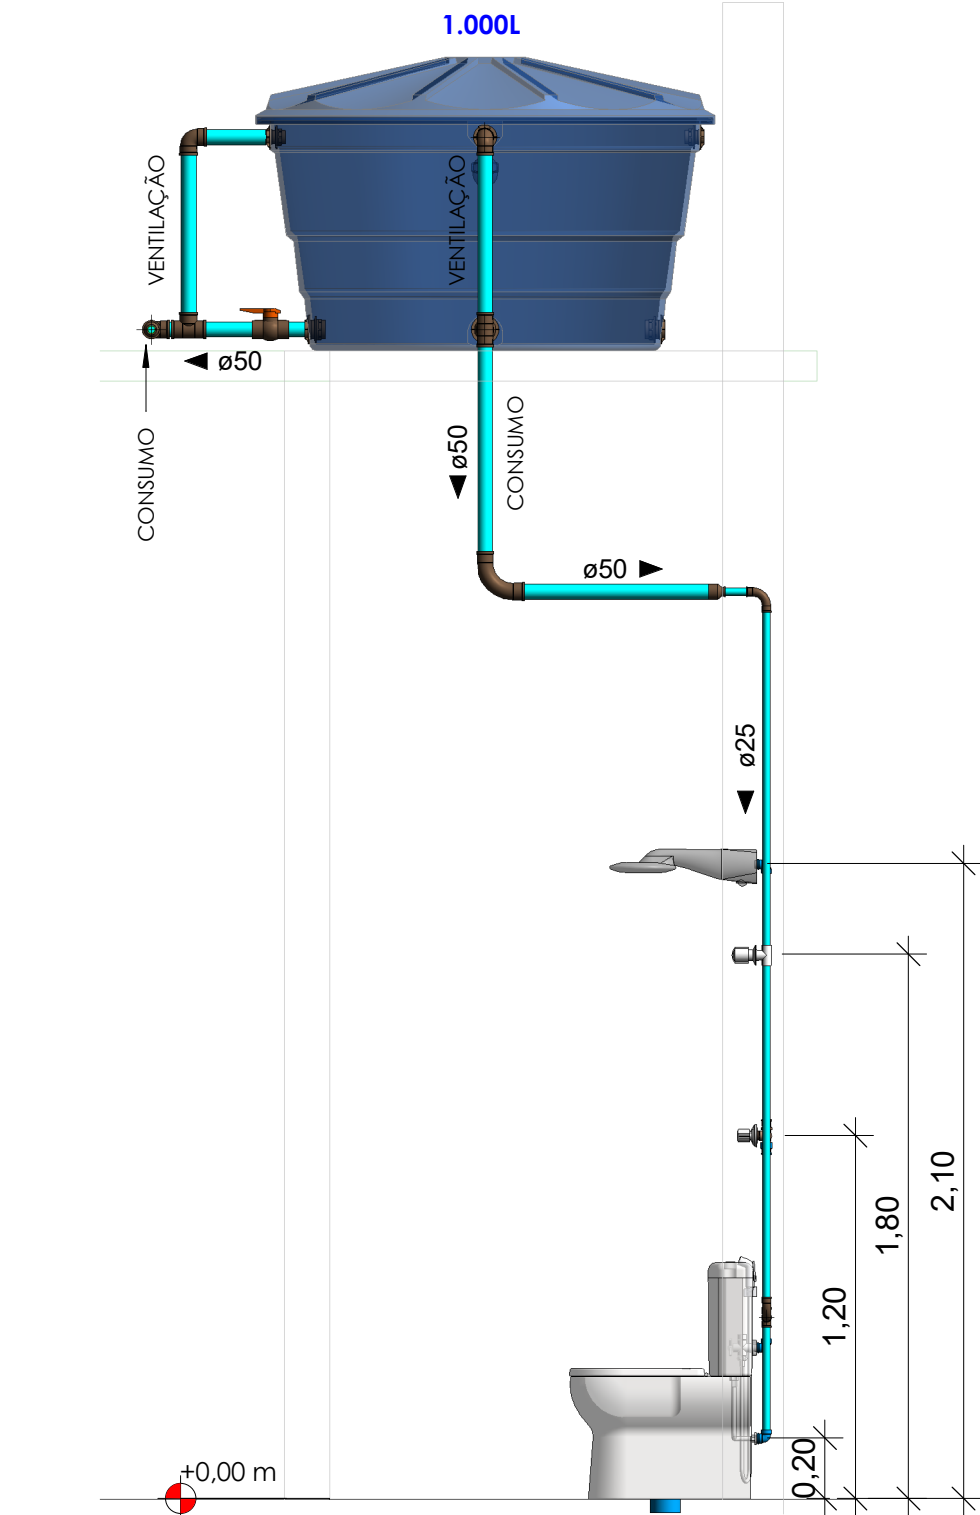


CORTE CC ESC 1/25

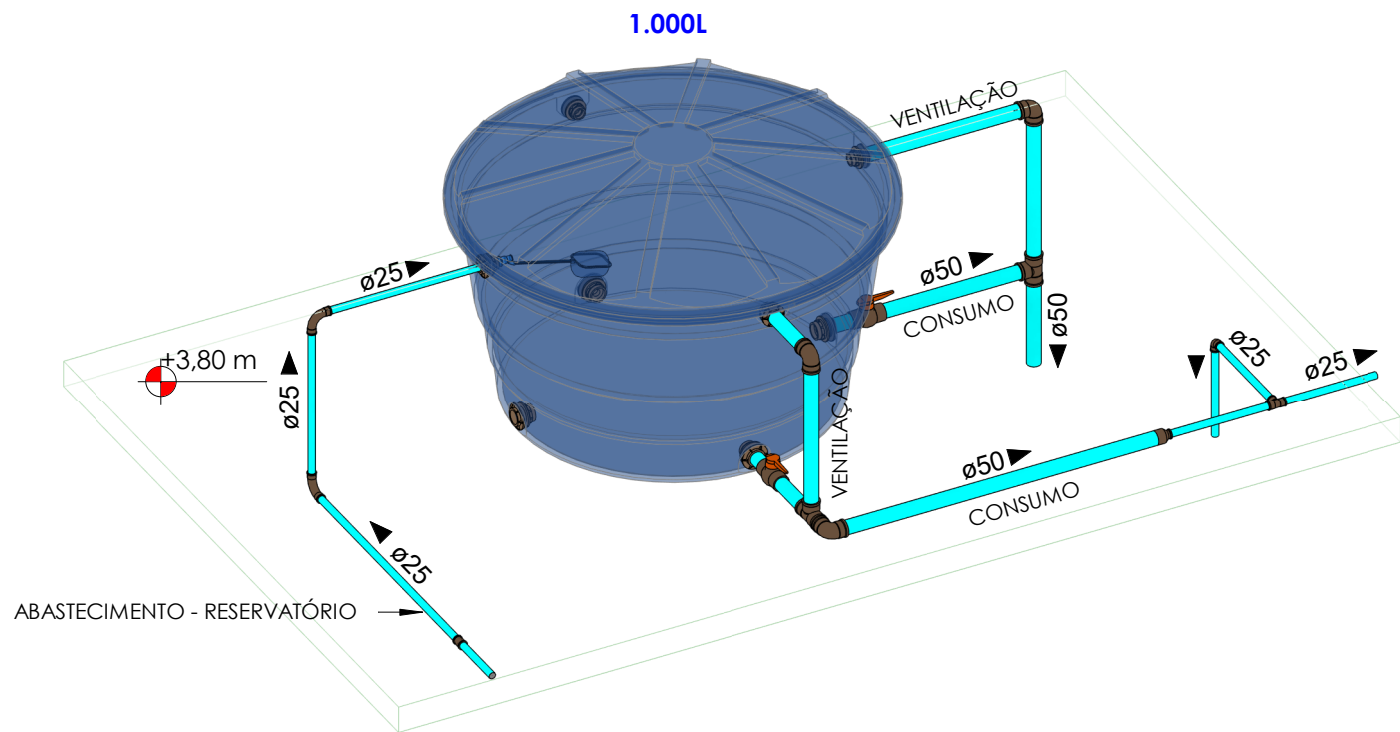

ISOMÉTRICA 05 - CAIXA D'ÁGUA - ESC 1/25

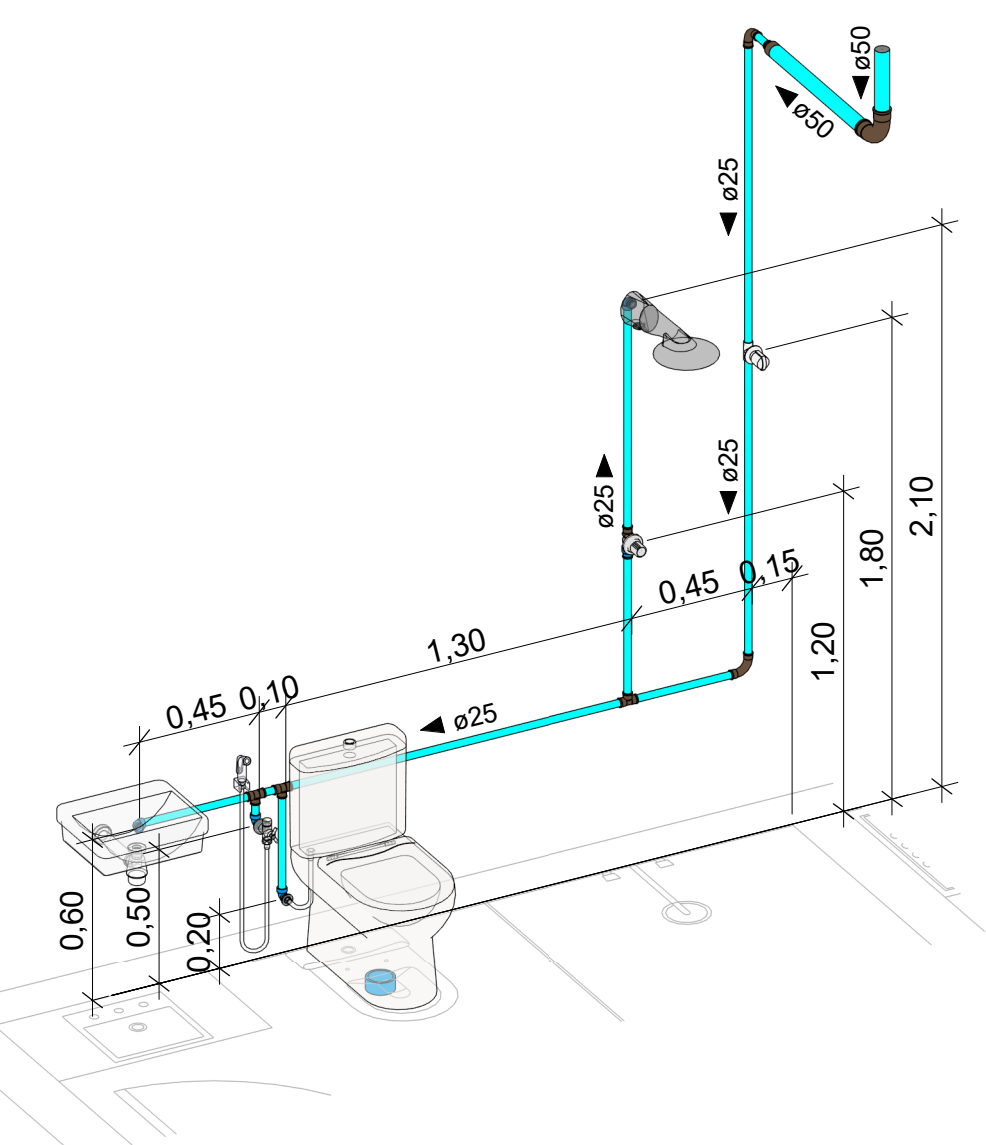

ISOMÉTRICA 03 - WC - ESC 1/25





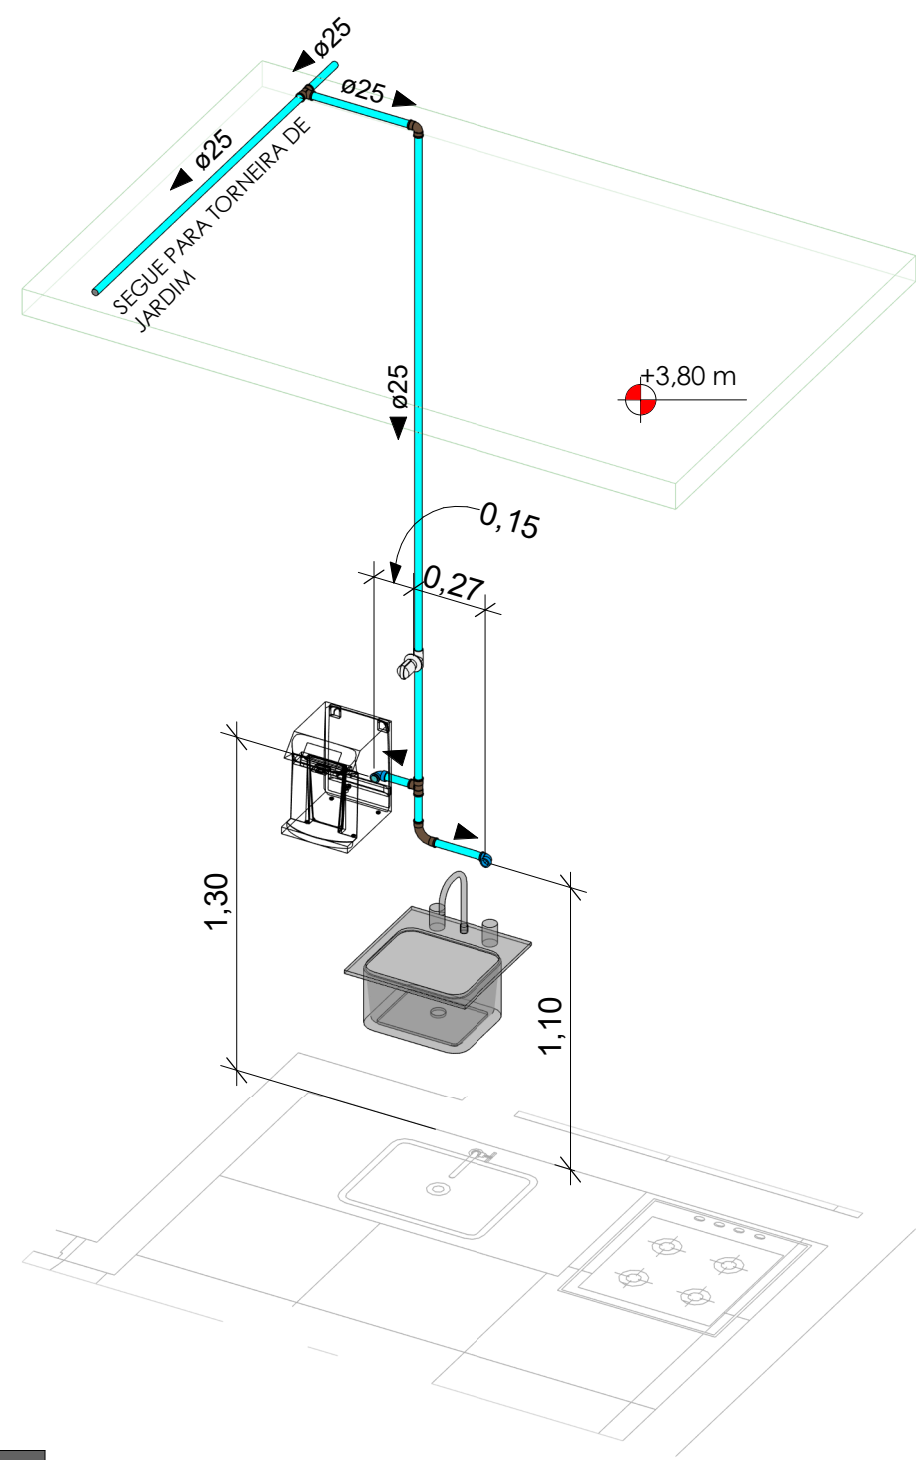


ISOMÉTRICA 04 - COPA - ESC 1/25

PROPRIETÁRIO: PREFEITURA MUNICIPAL DE COREMAS - PB LINCOLN CARTAXO DE LIRA JUNIOR:06897861405			
Assinado de forma digital por LINCOLN CARTAXO DE LIRA JUNIOR:06897861405 Dados: 2025.08.11 14:45:15 -03'00'			
PROJETO: LINCOLN CARTAXO DE LIRA JÚNIOR CREA 160.814.689-8			
PROJETO:		INSTALAÇÕES HIDRÁULICAS DA REFORMA DA GARAGEM	
CONCEDENTE:		PREFEITURA MUNICIPAL DE COREMAS - PB	
CONVENIENTE:		MUNICÍPIO DE COREMAS - PB	
LOCAL:		COREMAS - PB	
DATA		RUBRICA	
17/06/2025		DADOS	
CÓPIA		CREA 160.814.689-8	
VISTO			
PRANCHA:		DESCRIÇÃO:	
01 / 03		PLANTA BAIXA - CAIXA D'ÁGUA, TÉRREO CORTES E ISOMÉTRICAS	
		ESCALA:	
		INDICADA	




Av. Gov. Flavio R. Coutinho, 500, sl. 601
Jd. Oceania, 58037-005 - João Pessoa (PB)
Tel +55 99924.4447
e-mail: contato@lclprojetos.com

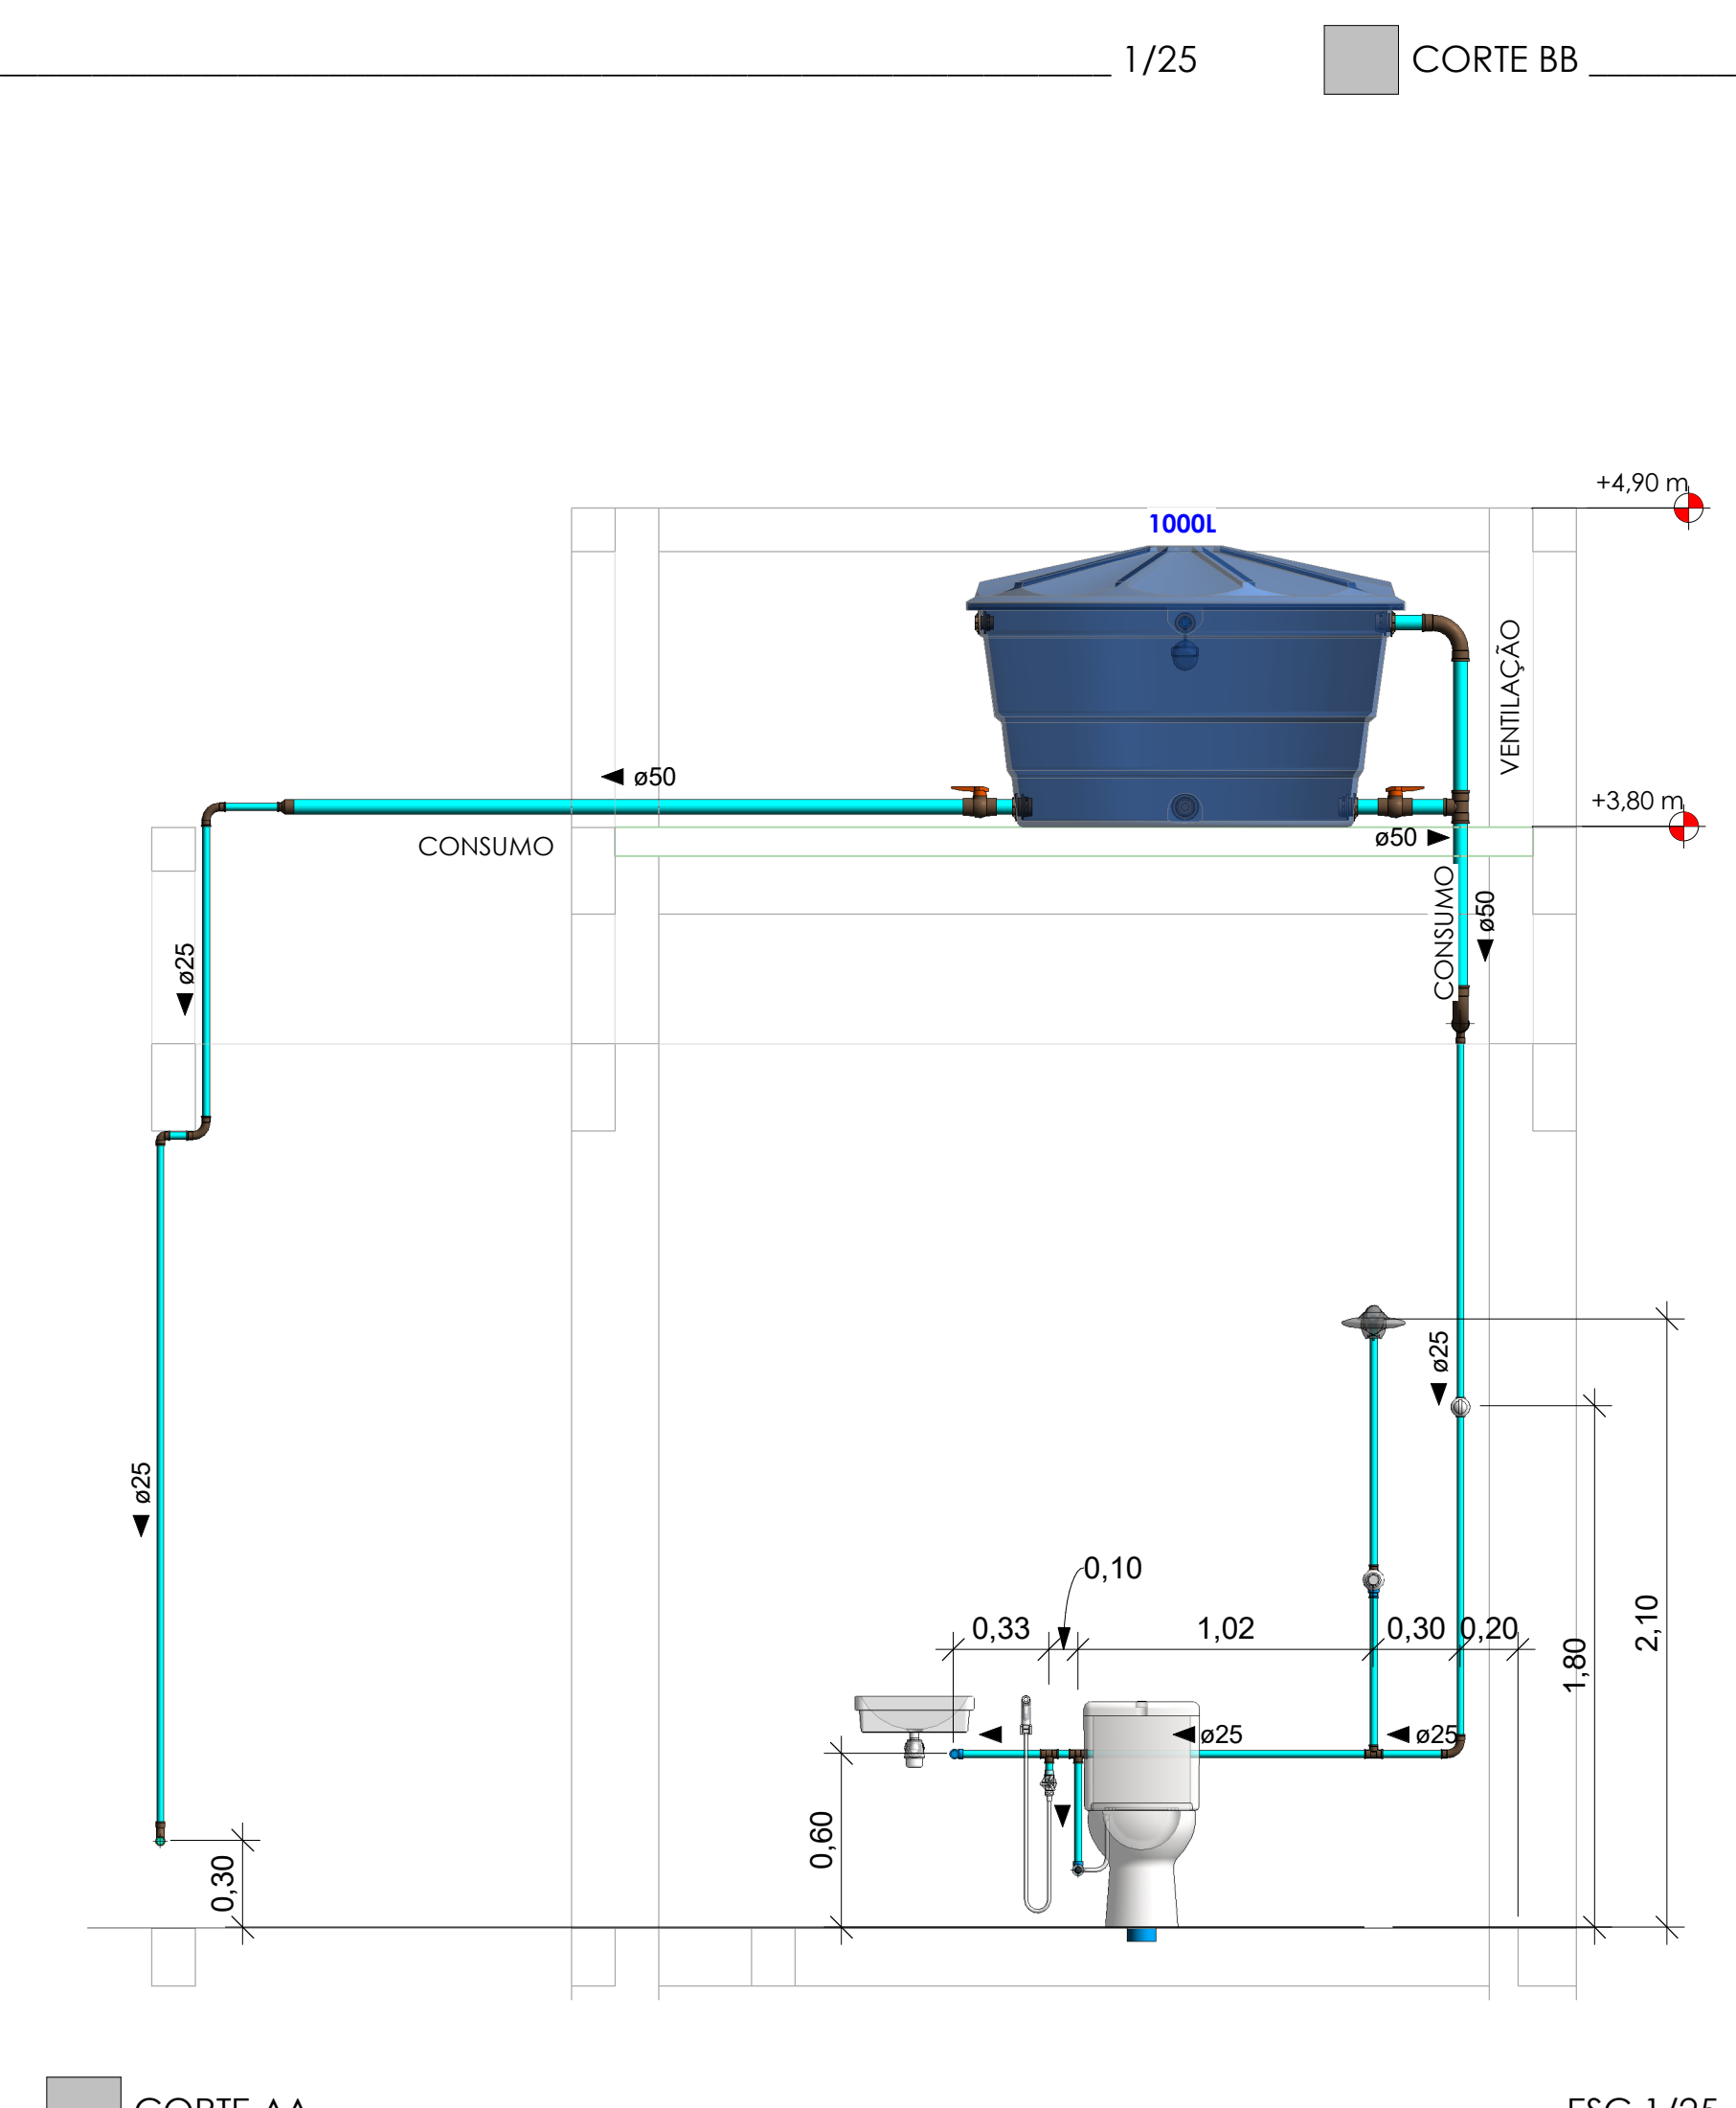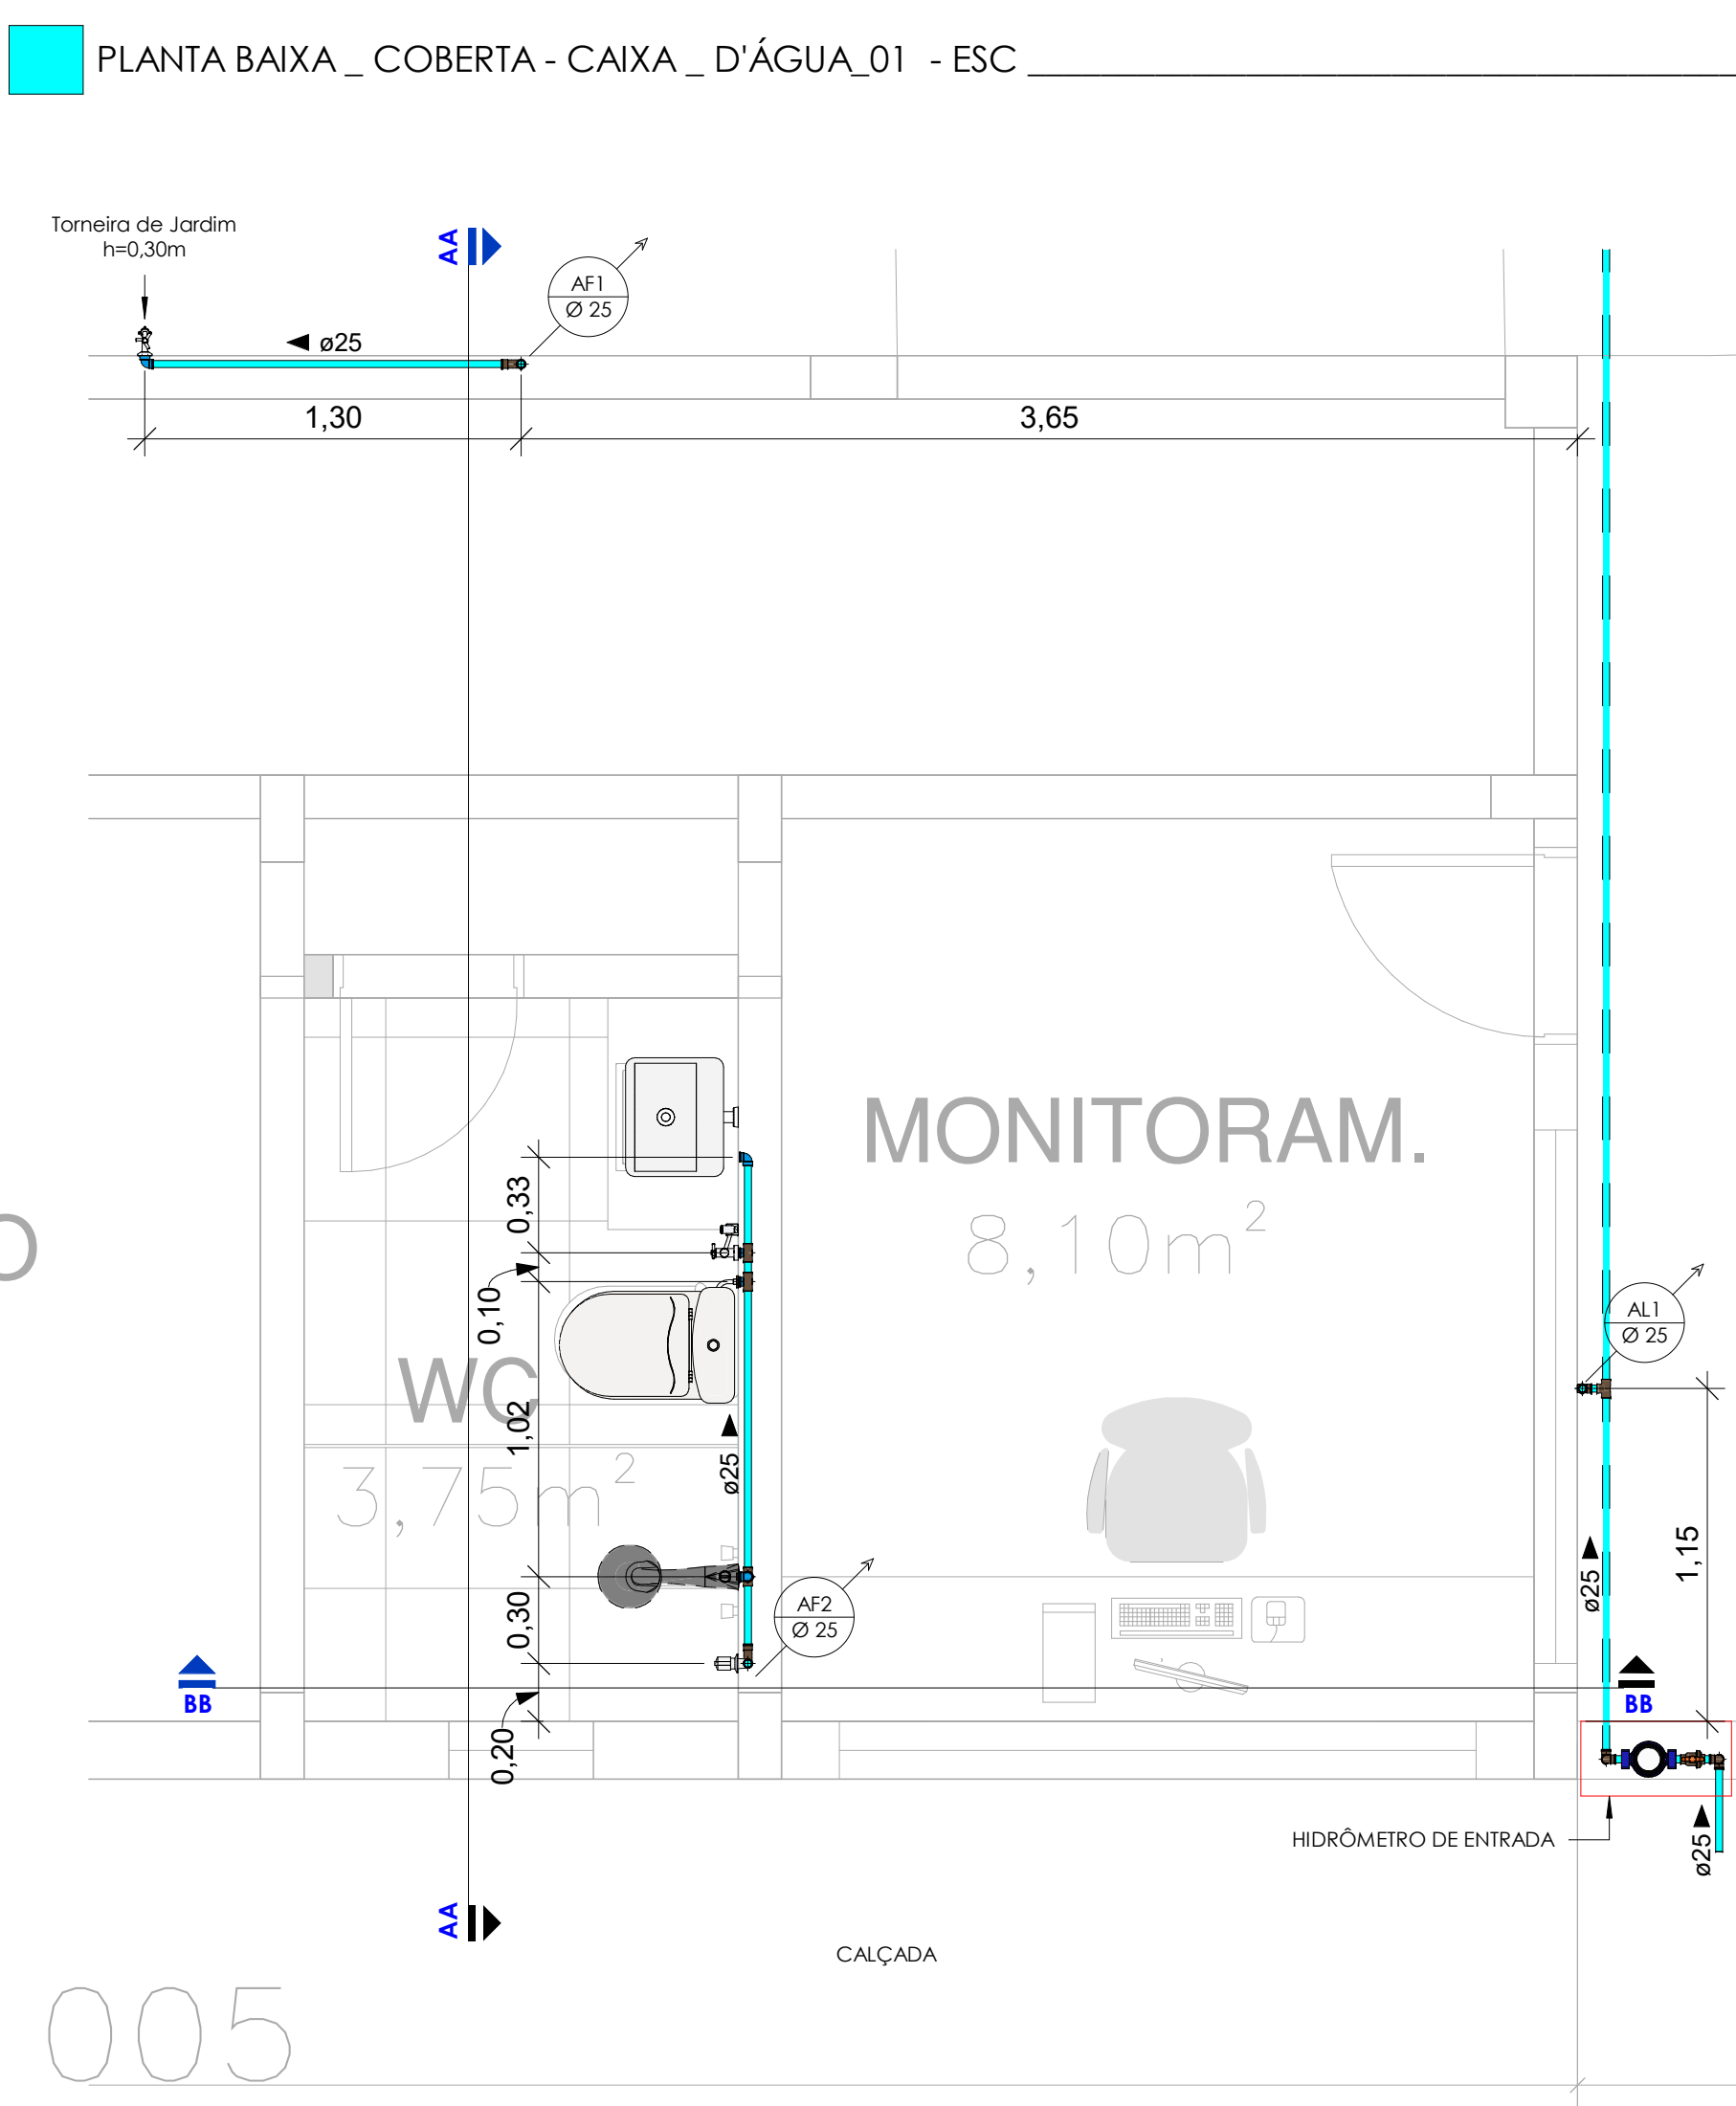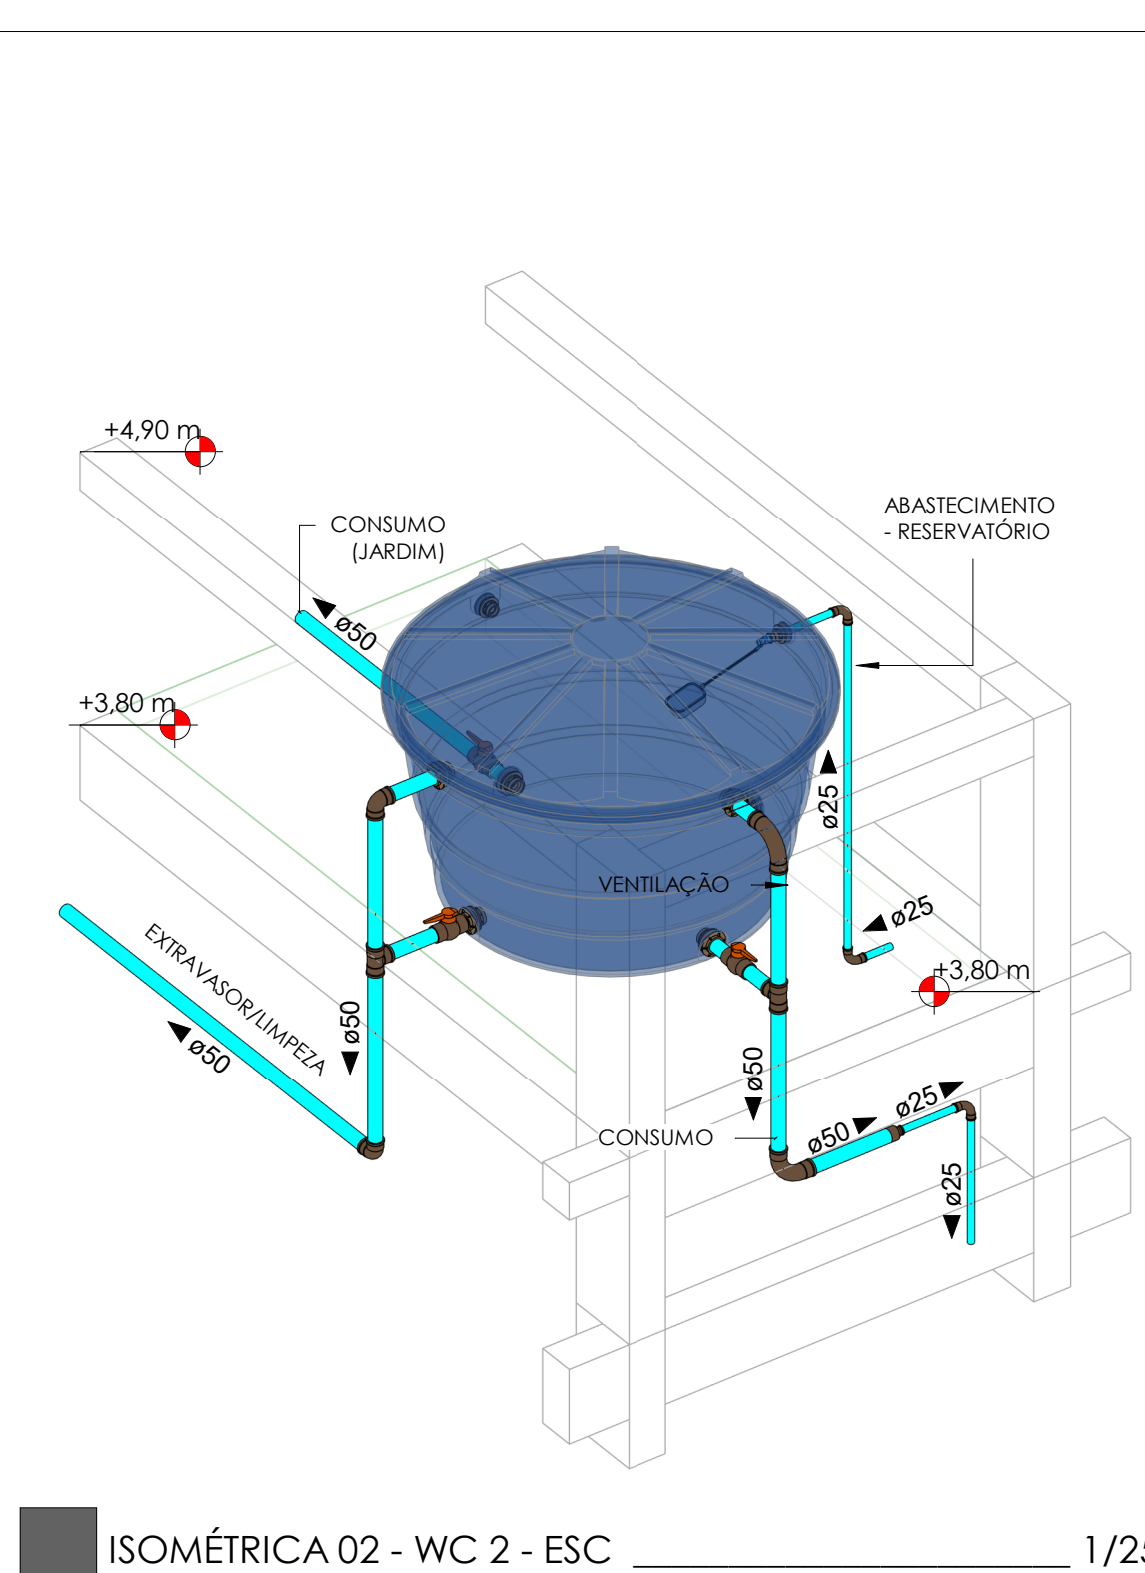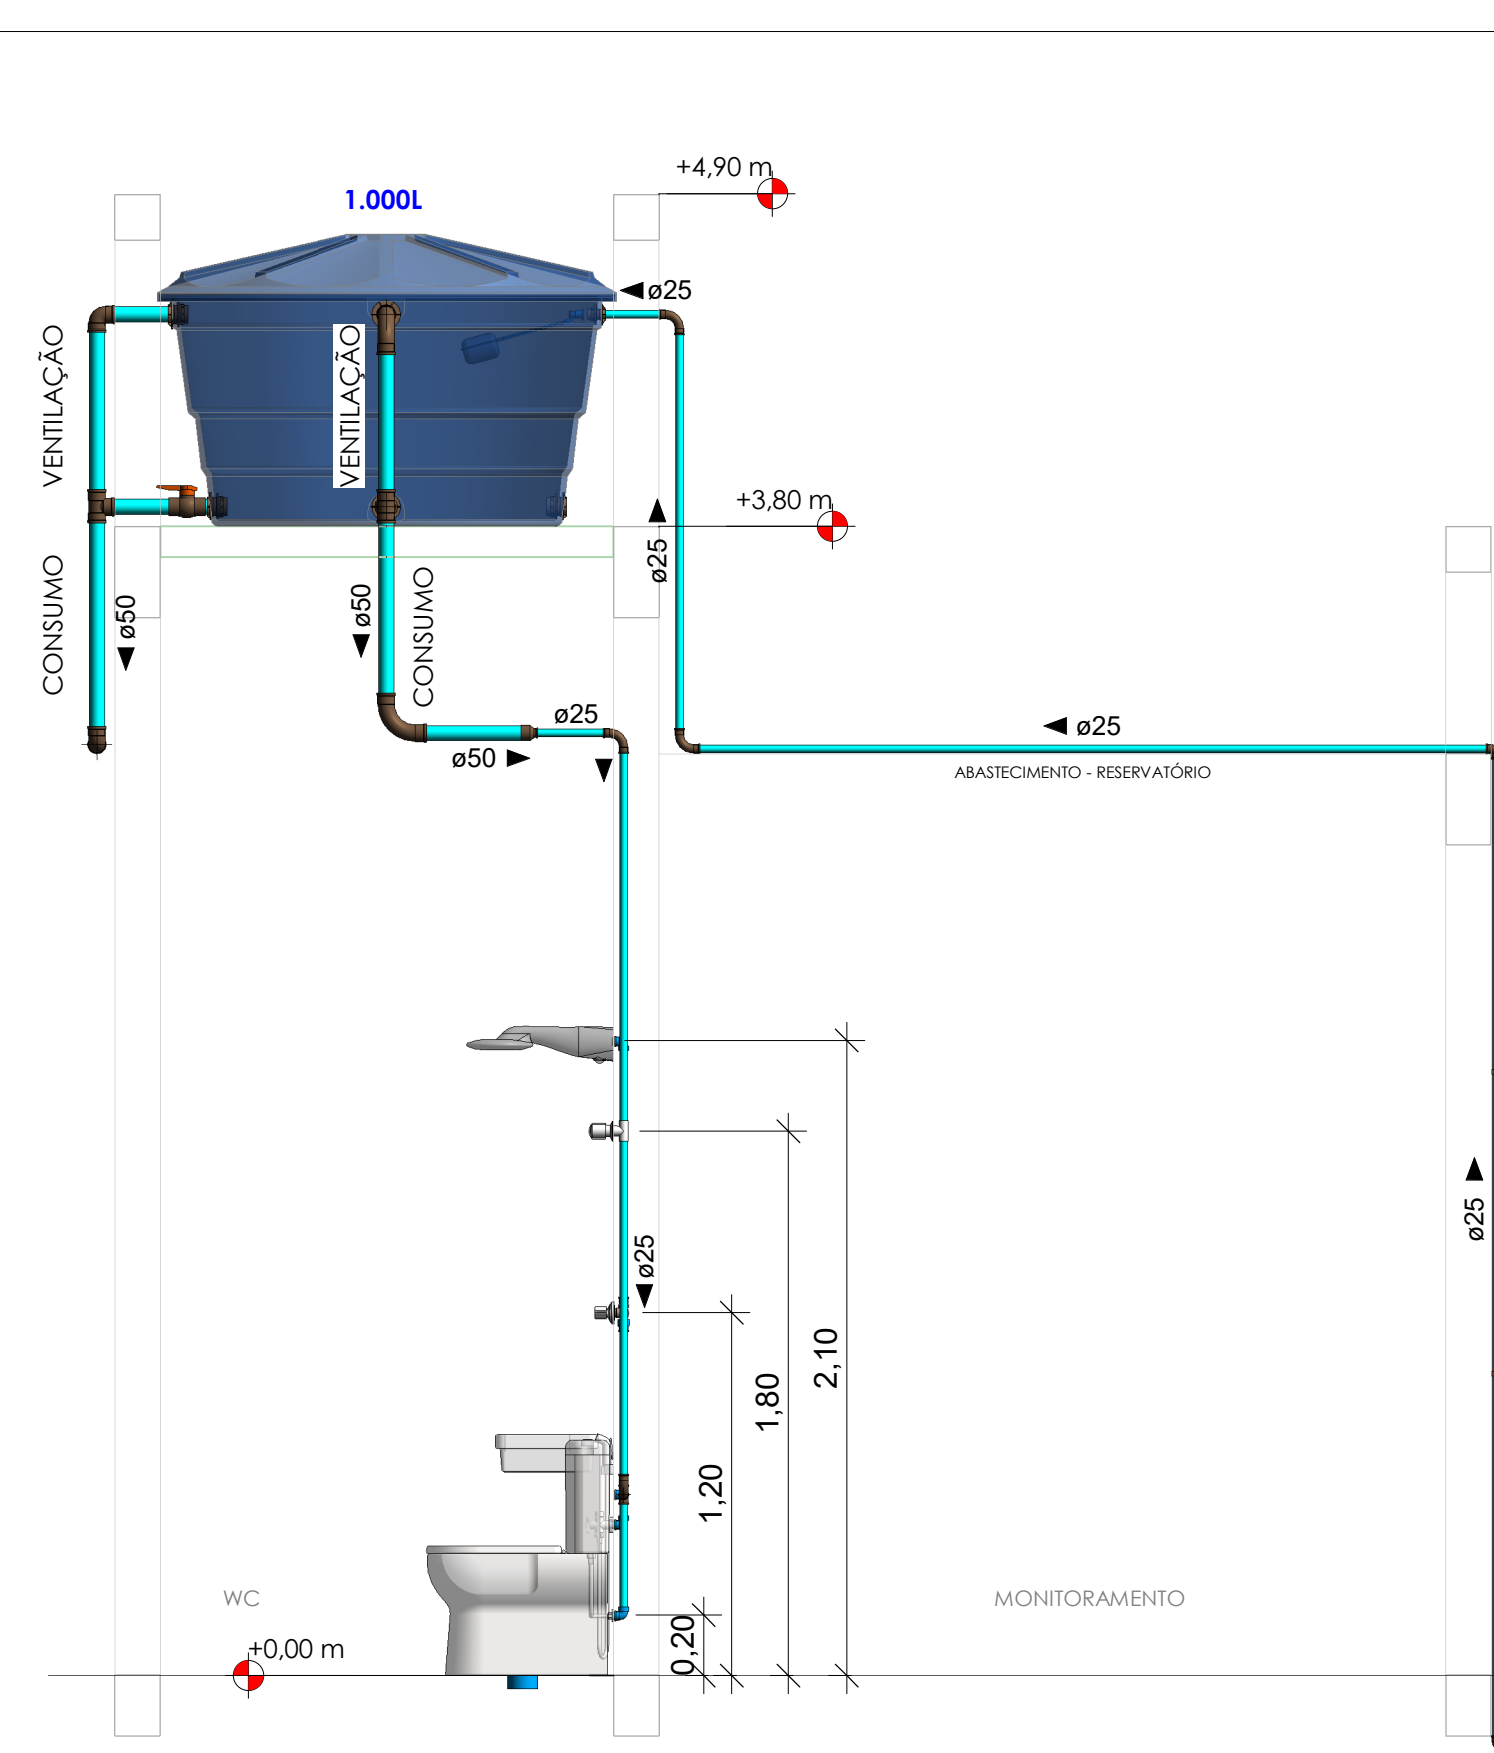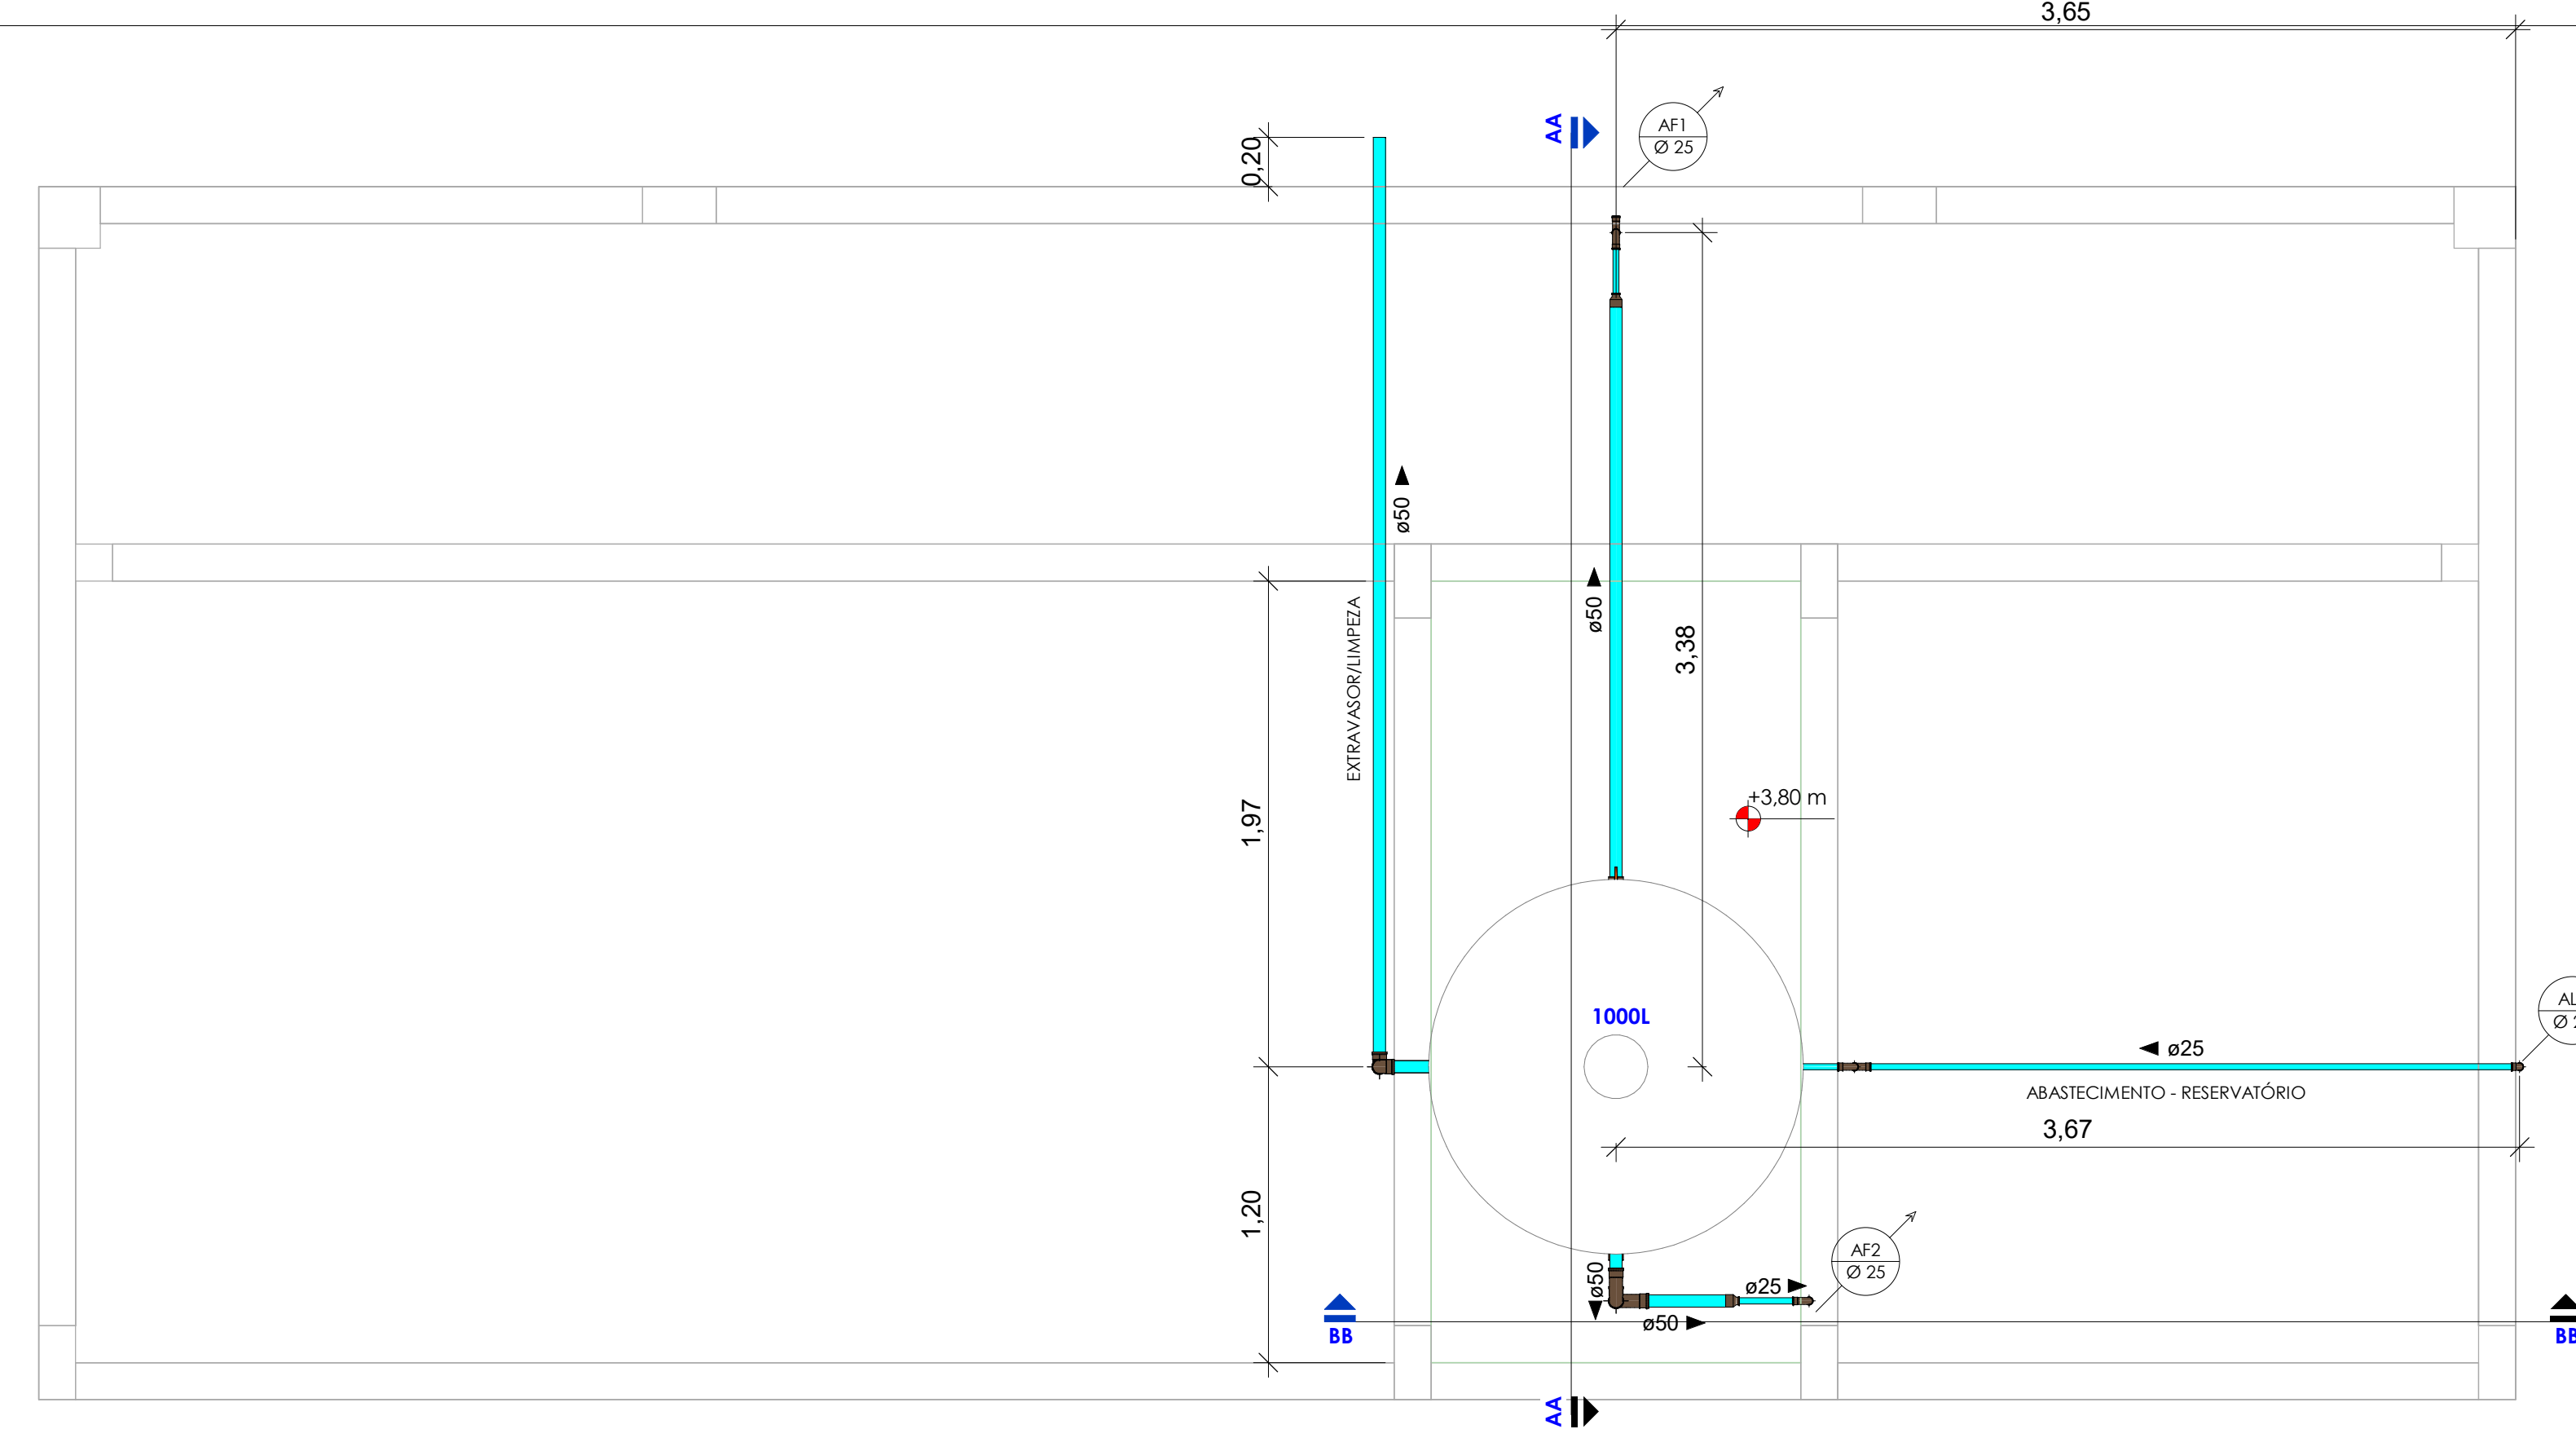

LEGENDA:

- TUBULAÇÃO PVC BRANCO - ESGOTO
- TUBULAÇÃO PVC BRANCO SN - VENTILAÇÃO ESGOTO
- TUBULAÇÃO PVC MARROM - ÁGUA FRIA
- AL-nn: -ALIMENTAÇÃO DO RESERV. SUPERIOR
nn: número da coluna
xx: diâmetro nominal da coluna
- CV-nn: -COLUNA DE VENTILAÇÃO
nn: número da coluna
xx: diâmetro nominal da coluna
- AF-nn: -COLUNA DE ÁGUA FRIA (BARRILETE)
nn: número da coluna
xx: diâmetro nominal da coluna

TABELA DE ALTURAS		
SIGLA	PONTO	ALTURA
CH	CHUVEIRO	2,10 m
LV	LAVATÓRIO	0,95 m
VS	VASO SANITÁRIO	0,20 m
RG	REGISTRO DE GAVETA	1,80 m
RP	REGISTRO DE PRESSÃO	1,20 m
PIA	PIA DE COZINHA	0,90 m
TQ	TANQUE	1,10 m

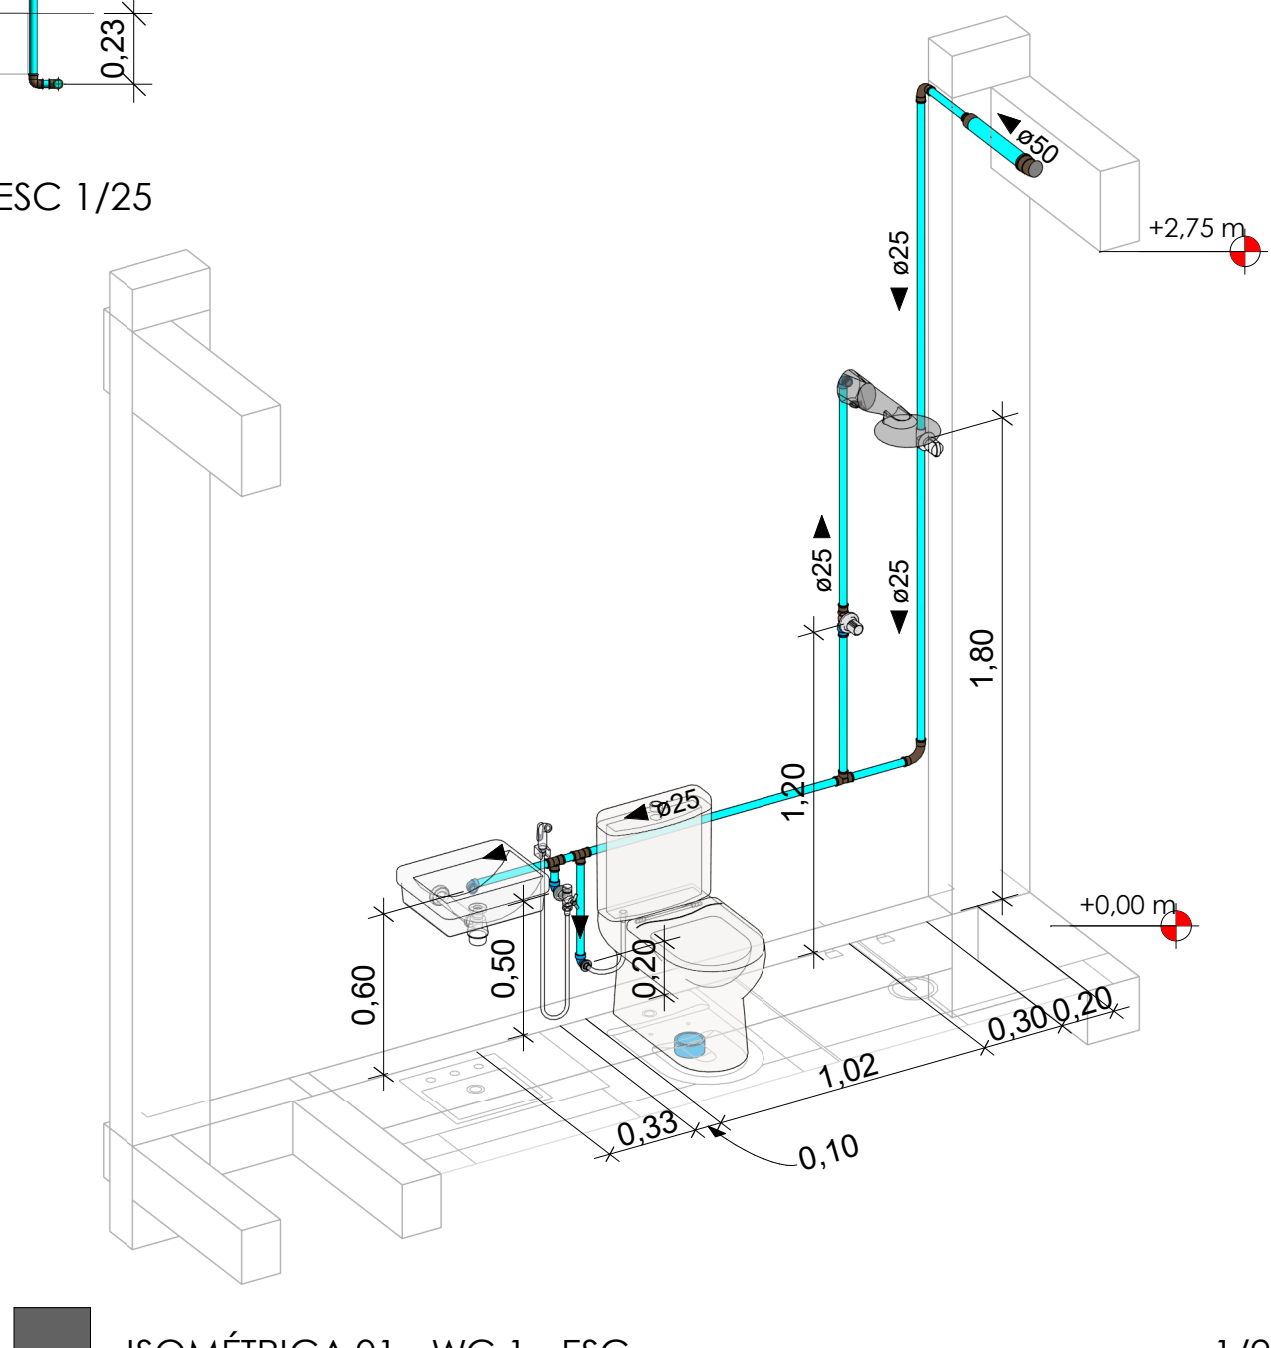

PROPRIETÁRIO: PREFEITURA MUNICIPAL DE COREMAS - PB
LINCOLN CARTAXO DE LIRA JÚNIOR:06897861405
Assinado de forma digital por LINCOLN CARTAXO DE LIRA JÚNIOR:06897861405
Dados: 2025.08.11 14:39:31 -03'00'

PROJETO: LINCOLN CARTAXO DE LIRA JÚNIOR CREA 160.814.689-8

PROJETO: INSTALAÇÕES HIDRÁULICAS DA REFORMA DA GARAGEM DE COREMAS

CONCEDENTE: PREFEITURA MUNICIPAL DE COREMAS - PB
CONVENIENTE: MUNICÍPIO DE COREMAS - PB
LOCAL: COREMAS - PB

DATA	RESPONSÁVEL TÉCNICO	RUBRICA	DADOS
17/06/2025	LINCOLN CARTAXO		CREA 160.814.689-8

PRANCHA: 02 / 03

DESCRIÇÃO: PLANTA BAIXA - CAIXA D'ÁGUA, TÉRREO CORTES E ISOMÉTRICAS

ESCALA: INDICADA

LCL PROJETOS

Av. Gov. Flavio R. Coutinho, 500, sl. 601
Jd. Oceania, 58037-005 - João Pessoa (PB)
Tel +55 99924.4447
e-mail: contato@lclprojetos.com


Peças hidráulicas e sanitárias			
Quantidade	Descrição	Abreviatura	Tipo de sistema
1			
2	Caixa d'água de polietileno, 1000 litros - Fortlev		
2	Torneira de Boia haste ABS Fortlev 1/2"		
2	Torneira de parede para tanque e jardim com bico união plástico (B5007CKCR3), linha Celite One - Metais Celite		
2	Bacia Sanitária com Caixa Acoplada	BS (CD)	Utilização
2	Chuveiro	CH	Utilização
2	Ducha higiênica	DH	Utilização
1	Purificador de água	FI	Utilização
2	Cuba de sobrepor	Cuba de sobrepor	Utilização/Esgoto
2	Sifão para lavatório 1"x1.1/2" com tubo de 300 mm	Sifão lavatório 1x1.1/2"	Utilização/Esgoto
2	Flexível 300mm aço inox	Flexível 300mm	Água Fria

Tabela de acessório de tubo			
Descrição	Família e tipo	Contagem	/Descrição/
	Hidrometro 7m³: 7 m³/h - 1"	1	1/
Registro de Gaveta PVC Cromado 25mm - TIGRE	Registro de Gaveta - Agua Fria - MEP - Tigre: PVC Cromado - 25 mm	3	3/Registro de Gaveta PVC Cromado 25mm - TIGRE/
Registro de pressão DocolBase 3/4" - DocolBásicos	AF_Registro de Pressão: Ø3/4" (25mm)	2	2/Registro de pressão DocolBase 3/4" - DocolBásicos/
Registro Esfera VS Compacto Soldável 50mm - TIGRE	AF_Registro Esfera VS Compacto: Soldável - 50 mm	5	5/Registro Esfera VS Compacto Soldável 50mm - TIGRE/
Registro Esfera VS Soldável 25mm - TIGRE	Registro Esfera VS - Agua Fria - MEP - Tigre: Soldável - 25 mm	1	1/Registro Esfera VS Soldável 25mm - TIGRE/

Total geral: 12

Tabela de conexão de tubo					
Contagem	Tigre: Descrição	Tigre: Fabricante	Tigre: Linha	Tigre: Produto	Tigre: Sistema
22					
2	Adaptador Soldável Curto com Bolsa e Rosca para Registro 25 x 3/4", PVC Marrom, Água Fria - TIGRE	© Tigre S/A	Soldável	Adaptador	Água Fria
2	Bucha de Redução Soldável Longa 50x25mm, PVC Marrom, Água Fria - TIGRE	© Tigre S/A	Soldável	Bucha de Redução	Água Fria
1	Curva 45° Soldável 25mm, PVC Marrom, Água Fria - TIGRE	© Tigre S/A	Soldável	Curva	Água Fria
16	Curva 90° Soldável 25mm, PVC Marrom, Água Fria - TIGRE	© Tigre S/A	Soldável	Curva	Água Fria
3	Curva 90° Soldável 50mm, PVC Marrom, Água Fria - TIGRE	© Tigre S/A	Soldável	Curva	Água Fria
8	Joelho 90° Soldável 25mm, PVC Marrom, Água Fria - TIGRE	© Tigre S/A	Soldável	Joelho	Água Fria
5	Joelho 90° Soldável 50mm, PVC Marrom, Água Fria - TIGRE	© Tigre S/A	Soldável	Joelho	Água Fria
12	Joelho 90° Soldável com Bucha de Latão 25 x 3/4", PVC Marrom, Água Fria - TIGRE	© Tigre S/A	Soldável	Joelho	Água Fria
10	Luva Soldável 25mm, PVC Marrom, Água Fria - TIGRE	© Tigre S/A	Soldável	Luva	Água Fria
2	Luva Soldável e com Bucha de Latão 25 x 3/4", PVC Marrom, Água Fria - TIGRE	© Tigre S/A	Soldável	Luva	Água Fria
9	Tê Soldável 25mm, PVC Marrom, Água Fria - TIGRE	© Tigre S/A	Soldável	Tê	Água Fria
4	Tê Soldável 50mm, PVC Marrom, Água Fria - TIGRE	© Tigre S/A	Soldável	Tê	Água Fria

Tubos Rígidos		
Descrição	Diâmetro	Comprimento (m)
Tubo PVC Marrom - Água Fria Soldável	25 mm	105,31
Tubo PVC Marrom - Água Fria Soldável	50 mm	15,46

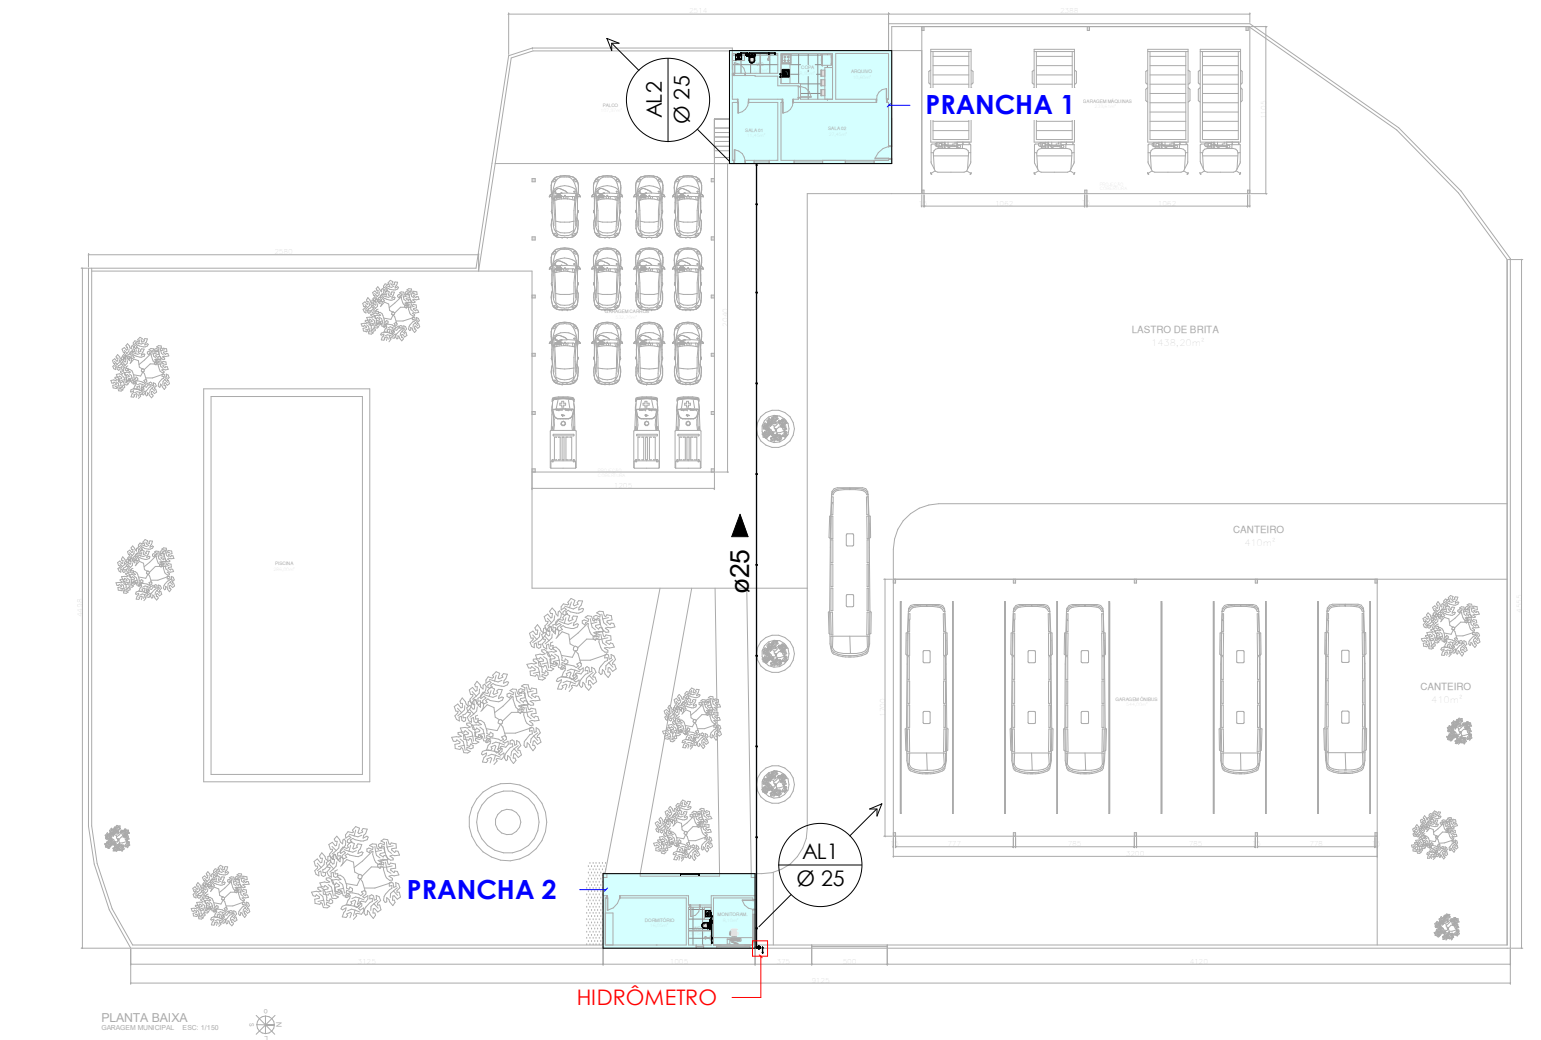

PLANTA BAIXA _REFORMA_GARAGEM_GERAL - ESC _____ 1/500




LEGENDA:

- | | |
|---|---|
|  | -TUBULAÇÃO PVC BRANCO - ESGOTO |
|  | -TUBULAÇÃO PVC BRANCO SN - VENTILAÇÃO ESGOTO |
|  | -TUBULAÇÃO PVC MARROM - ÁGUA FRIA |
|  | -ALIMENTAÇÃO DO RESERV. SUPERIOR
nn: número da coluna
xx: diâmetro nominal da coluna |
|  | -COLUMNA DE VENTILAÇÃO
nn: número da coluna
xx: diâmetro nominal da coluna |
|  | -COLUMNA DE ÁGUA FRIA (BARRILETE)
nn: número da coluna
xx: diâmetro nominal da coluna |

TABELA DE ALTURAS		
SIGLA	PONTO	ALTURA
CH	CHUVEIRO	2,10 m
LV	LAVATÓRIO	0,95 m
VS	VASO SANITÁRIO	0,20 m
RG	REGISTRO DE GAVETA	1,80 m
RP	REGISTRO DE PRESSÃO	1,20 m
PIA	PIA DE COZINHA	0,90 m
TQ	TANQUE	1,10 m

PROPRIETÁRIO: PREFEITURA MUNICIPAL DE COREMAS - PB			
LINCOLN CARTAXO DE LIRA		Assinado de forma digital por LINCOLN CARTAXO DE LIRA JUNIOR:06897861405	
JUNIOR:06897861405		Dados: 2025.08.11 14:47:18 -03'00'	
PROJETO:		LINCOLN CARTAXO DE LIRA JÚNIOR CREA 160.814.689-8	
PROJETO:		INSTALAÇÕES HIDRÁULICAS DA REFORMA DA GARAGEM DE COREMAS	
CONCEDENTE:		PREFEITURA MUNICIPAL DE COREMAS - PB	
CONVENENTE:		MUNICÍPIO DE COREMAS - PB	
LOCAL:		COREMAS - PB	
		RESPONSÁVEL TÉCNICO	RUBRICA
DATA	17/06/2025	LINCOLN CARTAXO	CREA 160.814.689-8
CÓPIA			
VISTO			
PRANCHA:		DESCRIÇÃO:	ESCALA:
03 / 03		QUANTITATIVOS , PLANTA BAIXA GERAL E MAPEAMENTO DAS PRANCHAS	INDICADA
 Av. Gov. Flavio R. Coutinho, 500, sl. 601 Jd. Oceania, 58037-005 - João Pessoa (PB) Tel +55 99924.4447 e-mail: contato@lclprojetos.com			

TODOS OS POSTES E ESTRUTURAS METÁLICAS, DEVEM SER DEVIDAMENTE ATERRADOS.

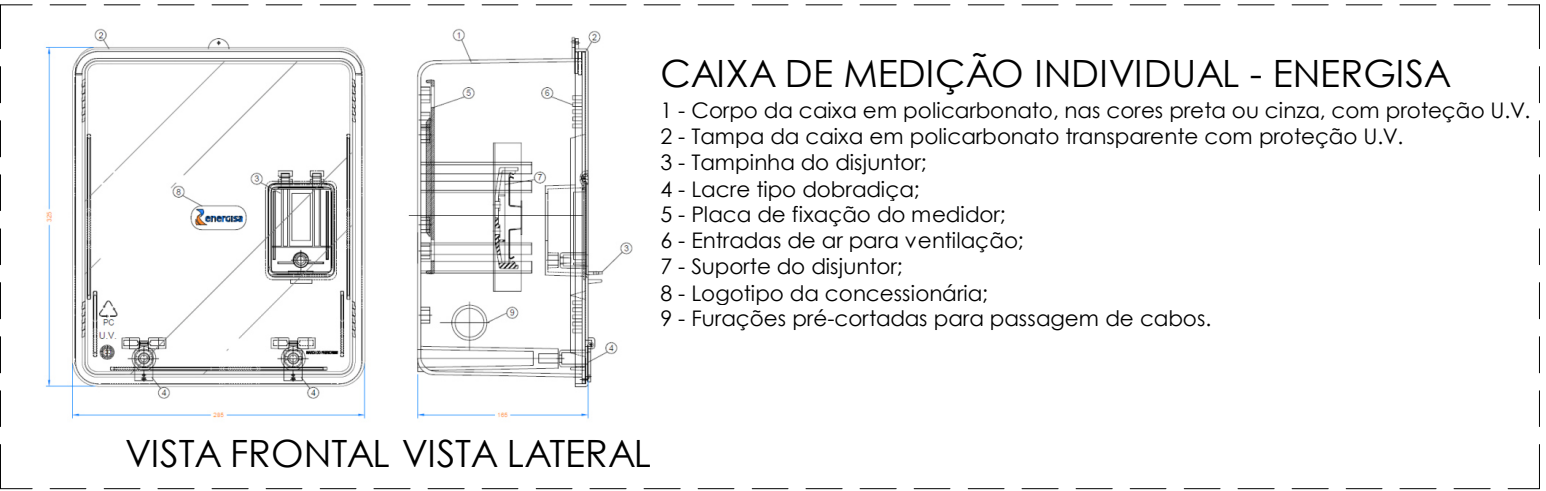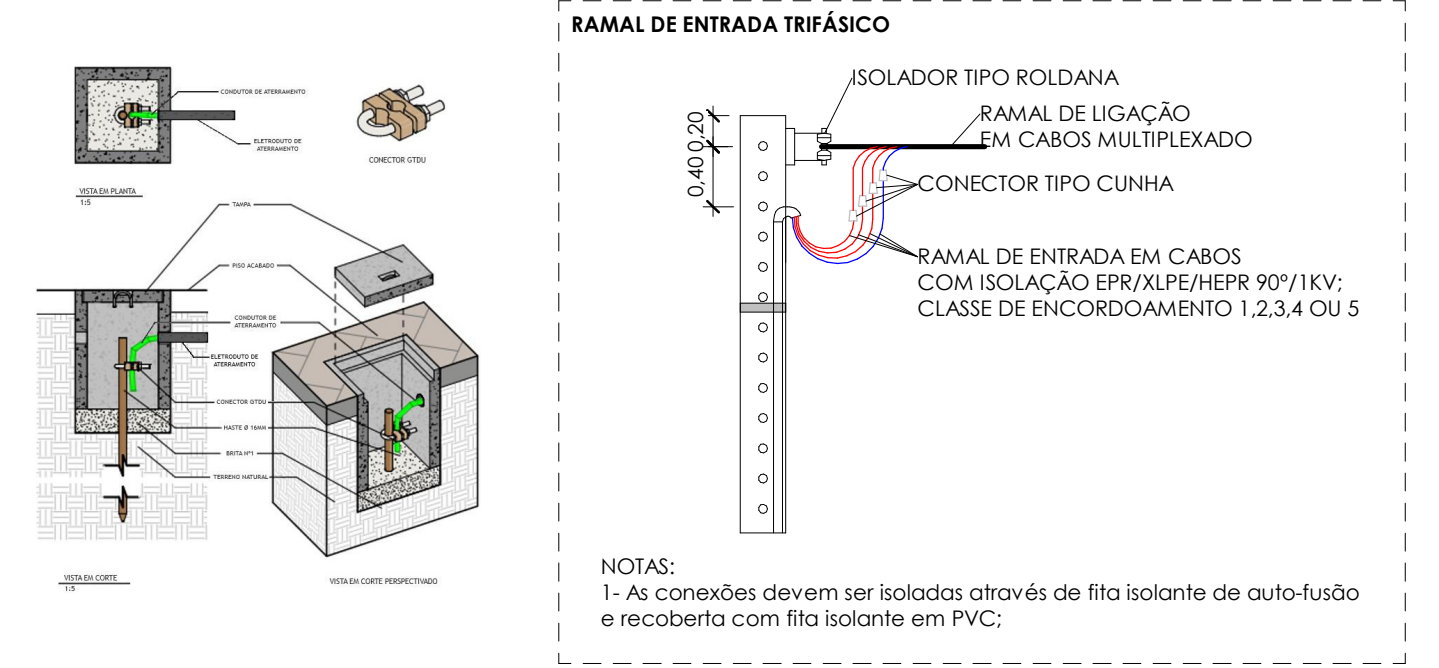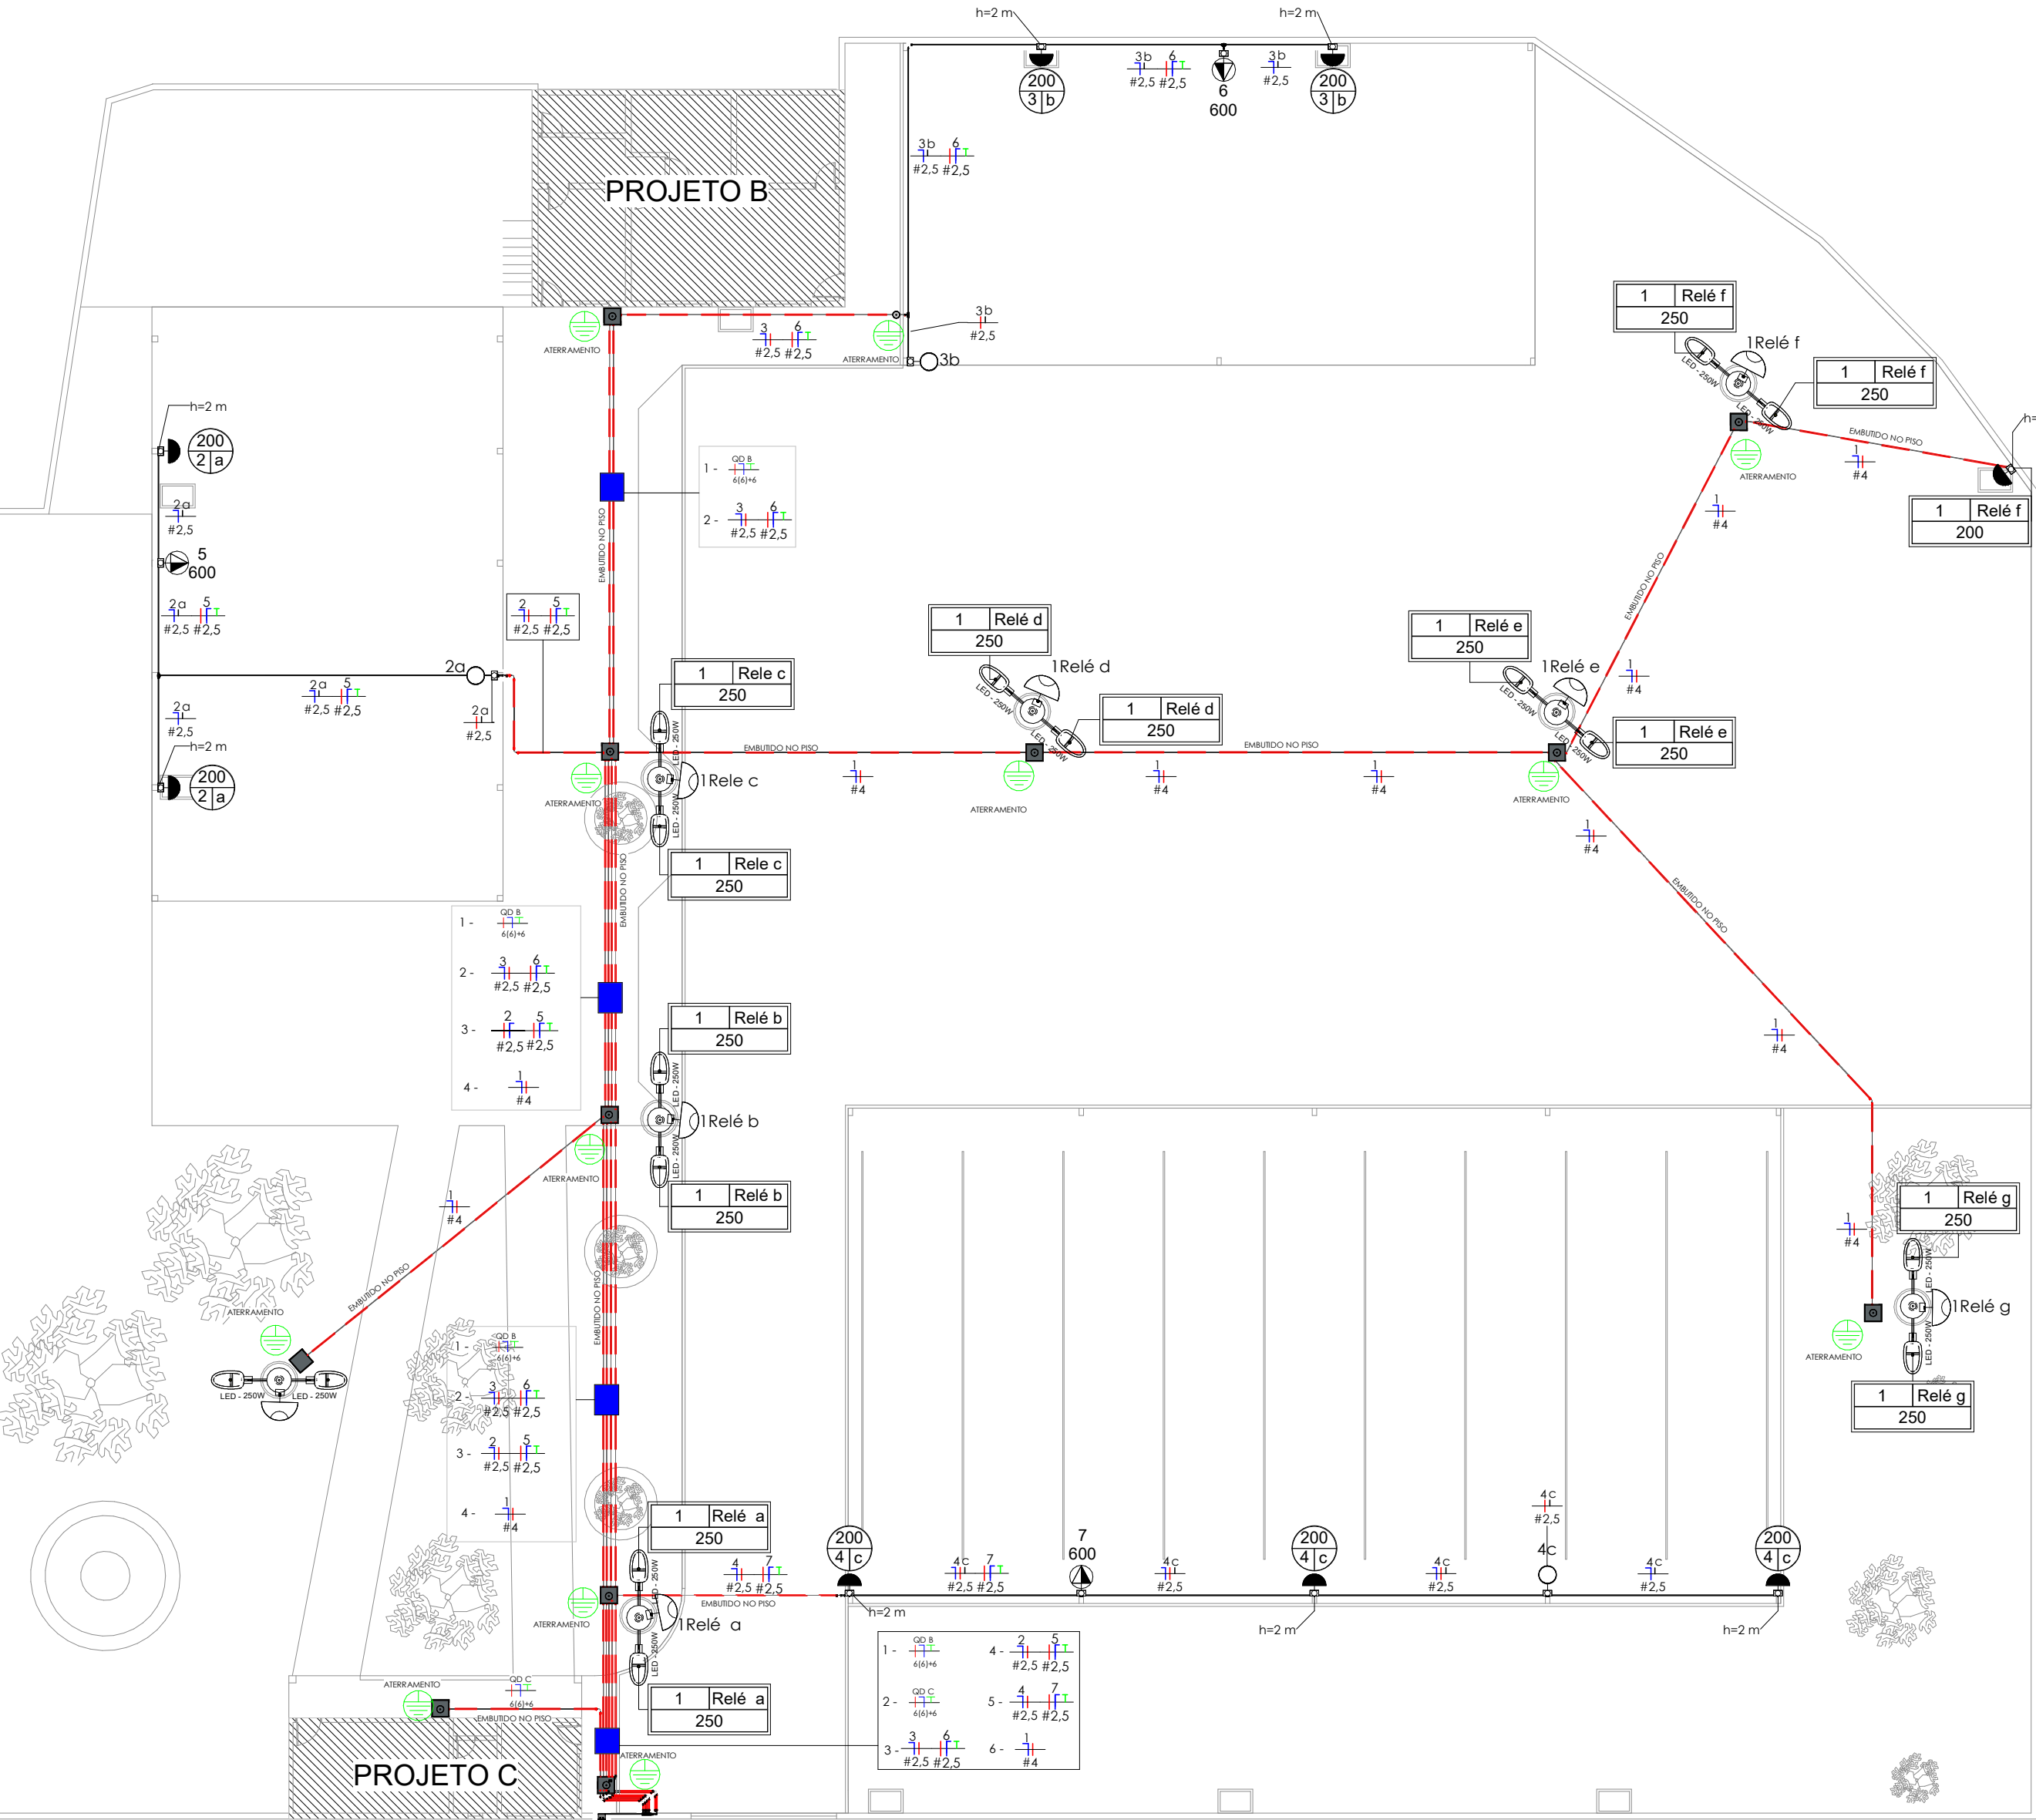

PLANTA BAIXA - PLANTA GERAL
ESCALA_____ 1 : 200

PROPRIETÁRIO: PREFEITURA MUNICIPAL DE COREMAS - PB
LINCOLN CARTAXO DE LIRA JUNIOR:06897861405
Assinado de forma digital por LINCOLN CARTAXO DE LIRA JUNIOR:06897861405
Dados: 2025.08.11 14:37:51 -03'00'

PROJETO:		LINCOLN CARTAXO DE LIRA JÚNIOR CREA 160.814.689-8		
PROJETO:		PROJETO A - ELÉTRICO GARAGEM COREMAS-PB		
PROPRIETÁRIO:		PREFEITURA MUNICIPAL DE COREMAS - PB MUNICÍPIO DE COREMAS - PB		
LOCAL:		COREMAS-PB		
		RESPONSÁVEL TÉCNICO	RUBRICA	DADOS
DATA	JUN/2025	LINCOLN CARTAXO		CREA 160.814.689-8
CÓPIA				
VISTO				
PRANCHA:		DESCRIÇÃO:		ESCALA:
01 /04		PROJETO ELÉTRICO - PLANTA BAIXA		INDICADA



Av. Gov. Flavio R. Coutinho, 500, sl. 601
Jd. Oceania, 58037-005 - João Pessoa (PB)
Tel +55 99924.4447
e-mail: contato@lclprojetos.com

GERAL - LISTA DE MATERIAIS - COMPONENTES		
Descrição do Material	Dimensões	Quantidade (peças)
Caixa de passagem		
Caixa em Alvenaria no passeio	40x40x40	11
Conduletes de PVC		
Adaptador de Redução para Condulete de PVC, Ø1"x3/4"	Ø1"x3/4"	34
Condulete de PVC multiplo antichamas na cor cinza, Ø1", sem tampa, com 5 entradas	Ø1"	21
inexistente	inexistente	1
Tampa Cega para Condulete Top de PVC antichama na cor cinza	Ø1"	15
Tampa para 1 Interruptor para Condulete Top de PVC antichama na cor cinza	Ø1"	3
Tampa para Tomada Hexagonal Horizontal para Condulete de PVC antichama na cor cinza	Ø1"	3
Derivações para Eletrodutos de PVC Rígido		
Curva 45° para eletroduto rígido de PVC DN40mm rosca Ø1.1/4" BSP conforme ABNT NBR 15465	DN40mm (1.1/4")	1
Curva 90° para eletroduto rígido de PVC DN25mm rosca Ø3/4" BSP conforme ABNT NBR 15465	DN25mm (3/4")	5
Curva 90° para eletroduto rígido de PVC DN32mm rosca Ø1" BSP conforme ABNT NBR 15465	DN32mm (1")	17
Curva 90° para eletroduto rígido de PVC DN40mm rosca Ø1.1/4" BSP conforme ABNT NBR 15465	DN40mm (1.1/4")	7
Curva 90° para eletroduto rígido de PVC DN50mm rosca Ø1.1/2" BSP conforme ABNT NBR 15465	DN50mm (1.1/2")	1
Luva para eletroduto de PVC rígido DN25mm rosca Ø3/4" BSP conforme ABNT NBR 15465	Ø 3/4"	10
Luva para eletroduto de PVC rígido DN32mm rosca Ø1" BSP conforme ABNT NBR 15465	Ø 1"	34
Luva para eletroduto de PVC rígido DN40mm rosca Ø1.1/4" BSP conforme ABNT NBR 15465	Ø 1.1/4"	16
Luva para eletroduto de PVC rígido DN50mm rosca Ø1.1/2" BSP conforme ABNT NBR 15465	Ø 1.1/2"	2
Disjuntores e Proteções		
DPS - Disjuntor de proteção contra surtos, monopolar, tensão nominal de operação UO 220/380V, máxima tensão de operação continua UC= 275 V, corrente de descarga máxima= 30kA, fixação em trilho DIN 35mm	VCL 275V 30kA Slim	4
IDR Interruptor Diferencial Residual Tetrapolar In=40A, 30mA	In=40 A, 30mA	1
Mini Disjuntor Monopolar 10A Curva C, conforme ABNT NBR NM 60898, encaixe perfil DIN 35mm	C 10A	6
Mini Disjuntor Monopolar 32A Curva C, conforme ABNT NBR NM 60898, encaixe perfil DIN 35mm	C 32A	2
Mini Disjuntor Monopolar 40A Curva C, conforme ABNT NBR NM 60898, encaixe perfil DIN 35mm	C 40A	1
Mini Disjuntor Tripolar 40A Curva C, conforme ABNT NBR NM 60898, encaixe perfil DIN 35mm	C 40A	1
Interruptores		
Sensor Fotoelétrico Completo	1Sensor, 4"x2"	8
Interruptores para Condulete de PVC		
1 Interruptor Simples, 10A 250V~, sem placa, para montagem em Condulete de PVC	1S, (para condulete)	3
Padrão de Entrada		
Caixa Para Medidor Polifásico com visor de vidro, Coelba/Celp/Cosern		1
Quadros		
Quadro de Distribuição 18/24 Disjuntores, de embutir, fabricado em PVC antichamas, com barramento de terra e neutro, porta branca, dimensões 350x379x78,7mm.	18/24 Disjuntores	1
Sistema de Aterramento		
Conjunto: Conector Tipo Cunha + Haste de aterramento Ø 16mm (5/8")X2400		11
Tomadas para Conduletes de PVC		
1 Tomada 2P+T 20A, sem placa, para montagem em Condulete de PVC	20A (para condulete)	3

Painel: Novo PV01

Localização:

Alimentação: 220/380V Trifásico (3F+N+T)

Alimentado por:

Montagem: Embutido

Notas:

Circuito	Descrição	Tensão (V)	Esquema	Potência Total (VA)	FP	Potência Total (W)	Corrente Nominal (A)	FCA	FCT	Ib: Corrente de Projeto Corrigida (A)	In: Disjuntor (A)	Tipo de Instalação	Condutor Pré-Dimensionado (Seção e Iz: Capacidade de condução de Corrente)	Seção do Condutor Adotado (mm²)	L Aprox. (m)	L Considerado (m)	Queda de Tensão (%)	Fase A	Fase B	Fase C
1	Iluminação Geral	220,00	FNT	4200 VA	0,92	3864 W	19,09 A	0,8	1	23,86 A	32,00 A	[Cu/PVC/750V/70°]-Un-B1-2Cc	1-#4,0(32A), 1-#4,0(32A), 1-#4,0	4	96,52	106,42	9,35	4200 VA		
2	Iluminação I	220,00	FNT	400 VA	0,92	368 W	1,82 A	0,8	1	2,27 A	10,00 A	[Cu/PVC/750V/70°]-Un-B1-2Cc	1-#2,5(24A), 1-#2,5(24A), 1-#2,5	2,5	66,98	76,88	1,03		400 VA	
3	Iluminação II	220,00	FNT	400 VA	0,92	368 W	1,82 A	0,8	1	2,27 A	10,00 A	[Cu/PVC/750V/70°]-Un-B1-2Cc	1-#2,5(24A), 1-#2,5(24A), 1-#2,5	2,5	87,73	97,63	1,31			400 VA
4	Iluminação III	220,00	FNT	600 VA	0,92	552 W	2,73 A	0,8	1	3,41 A	10,00 A	[Cu/PVC/750V/70°]-Un-B1-2Cc	1-#2,5(24A), 1-#2,5(24A), 1-#2,5	2,5	49,83	59,73	1,20	600 VA		
5	Tomada I	220,00	FNT	600 VA	0,92	552 W	2,73 A	0,8	1	3,41 A	10,00 A	[Cu/PVC/750V/70°]-Un-B1-2Cc	1-#2,5(24A), 1-#2,5(24A), 1-#2,5	2,5	64,80	74,7	1,50		600 VA	
6	Tomada II	220,00	FNT	600 VA	0,92	552 W	2,73 A	0,8	1	3,41 A	10,00 A	[Cu/PVC/750V/70°]-Un-B1-2Cc	1-#2,5(24A), 1-#2,5(24A), 1-#2,5	2,5	84,65	94,55	1,90			600 VA
7	Tomada III	220,00	FNT	600 VA	0,92	552 W	2,73 A	0,8	1	3,41 A	10,00 A	[Cu/PVC/750V/70°]-Un-B1-2Cc	1-#2,5(24A), 1-#2,5(24A), 1-#2,5	2,5	26,82	36,72	0,74	600 VA		
8	Quadro B	220,00	FNT	6039 VA	1	6039 W	27,45 A	1	1	27,45 A	40,00 A	[Cu/EPR-XLPE/0,6-1kV/90°]-Un-D-3Cc	1-#10,0 (61 A), 1-#10,0 (61 A), 1-#6,0	6	58,43	68,43	6,26		6039 VA	
9	Quadro C	220,00	FNT	4138 VA	1	4138 W	18,81 A	1	1	18,81 A	32,00 A	[Cu/EPR-XLPE/0,6-1kV/90°]-Un-D-3Cc	1-#10,0 (61 A), 1-#10,0 (61 A), 1-#4,0	6	15,79	25,79	1,62			4138 VA
10																				
Totais:																		5400 VA	6970 VA	5073 VA

Legenda:

FP: Fator de Potência

FCA:Fator de Correção por Agrupamento

FCT:Fator de Correção por Temperatura

Ib: Corrente de Projeto Corrigida(A)

In:Corrente Nominal do Disjuntor (A)



Iz: Capacidade de condução de corrente do condutor(A)

(Ib < In < Iz)

Tipo de Carga	Potência Instalada (VA)	Fator de Demanda	Potência Demandada (VA)	Totais do Pannel
Iluminação+TUGs (Residencial)	1800 VA	0,40	720 VA	
Outros	6039 VA	0,62	3744 VA	Potência Instalada: 17231 VA
Iluminação Pública	5600 VA	1,00	5600 VA	Potência Demandada: 12780 VA
Outros.	4138 VA	0,72	2979 VA	Corrente Total: 26,18 A
				Corrente Total Demandada: 19,42 A

TODOS OS POSTES E ESTRUTURAS METÁLICAS, DEVEM SER DEVIDAMENTE ATERRADOS.

Descrição do Material	Diâmetro Nominal	Comprimento (m)
Eletroduto de PVC Rígido Soldável	Ø40	321,72 m
Eletroduto de PVC Rígido Soldável	Ø32	20,68 m
Eletroduto de PVC Rígido Soldável	Ø25	96,68 m

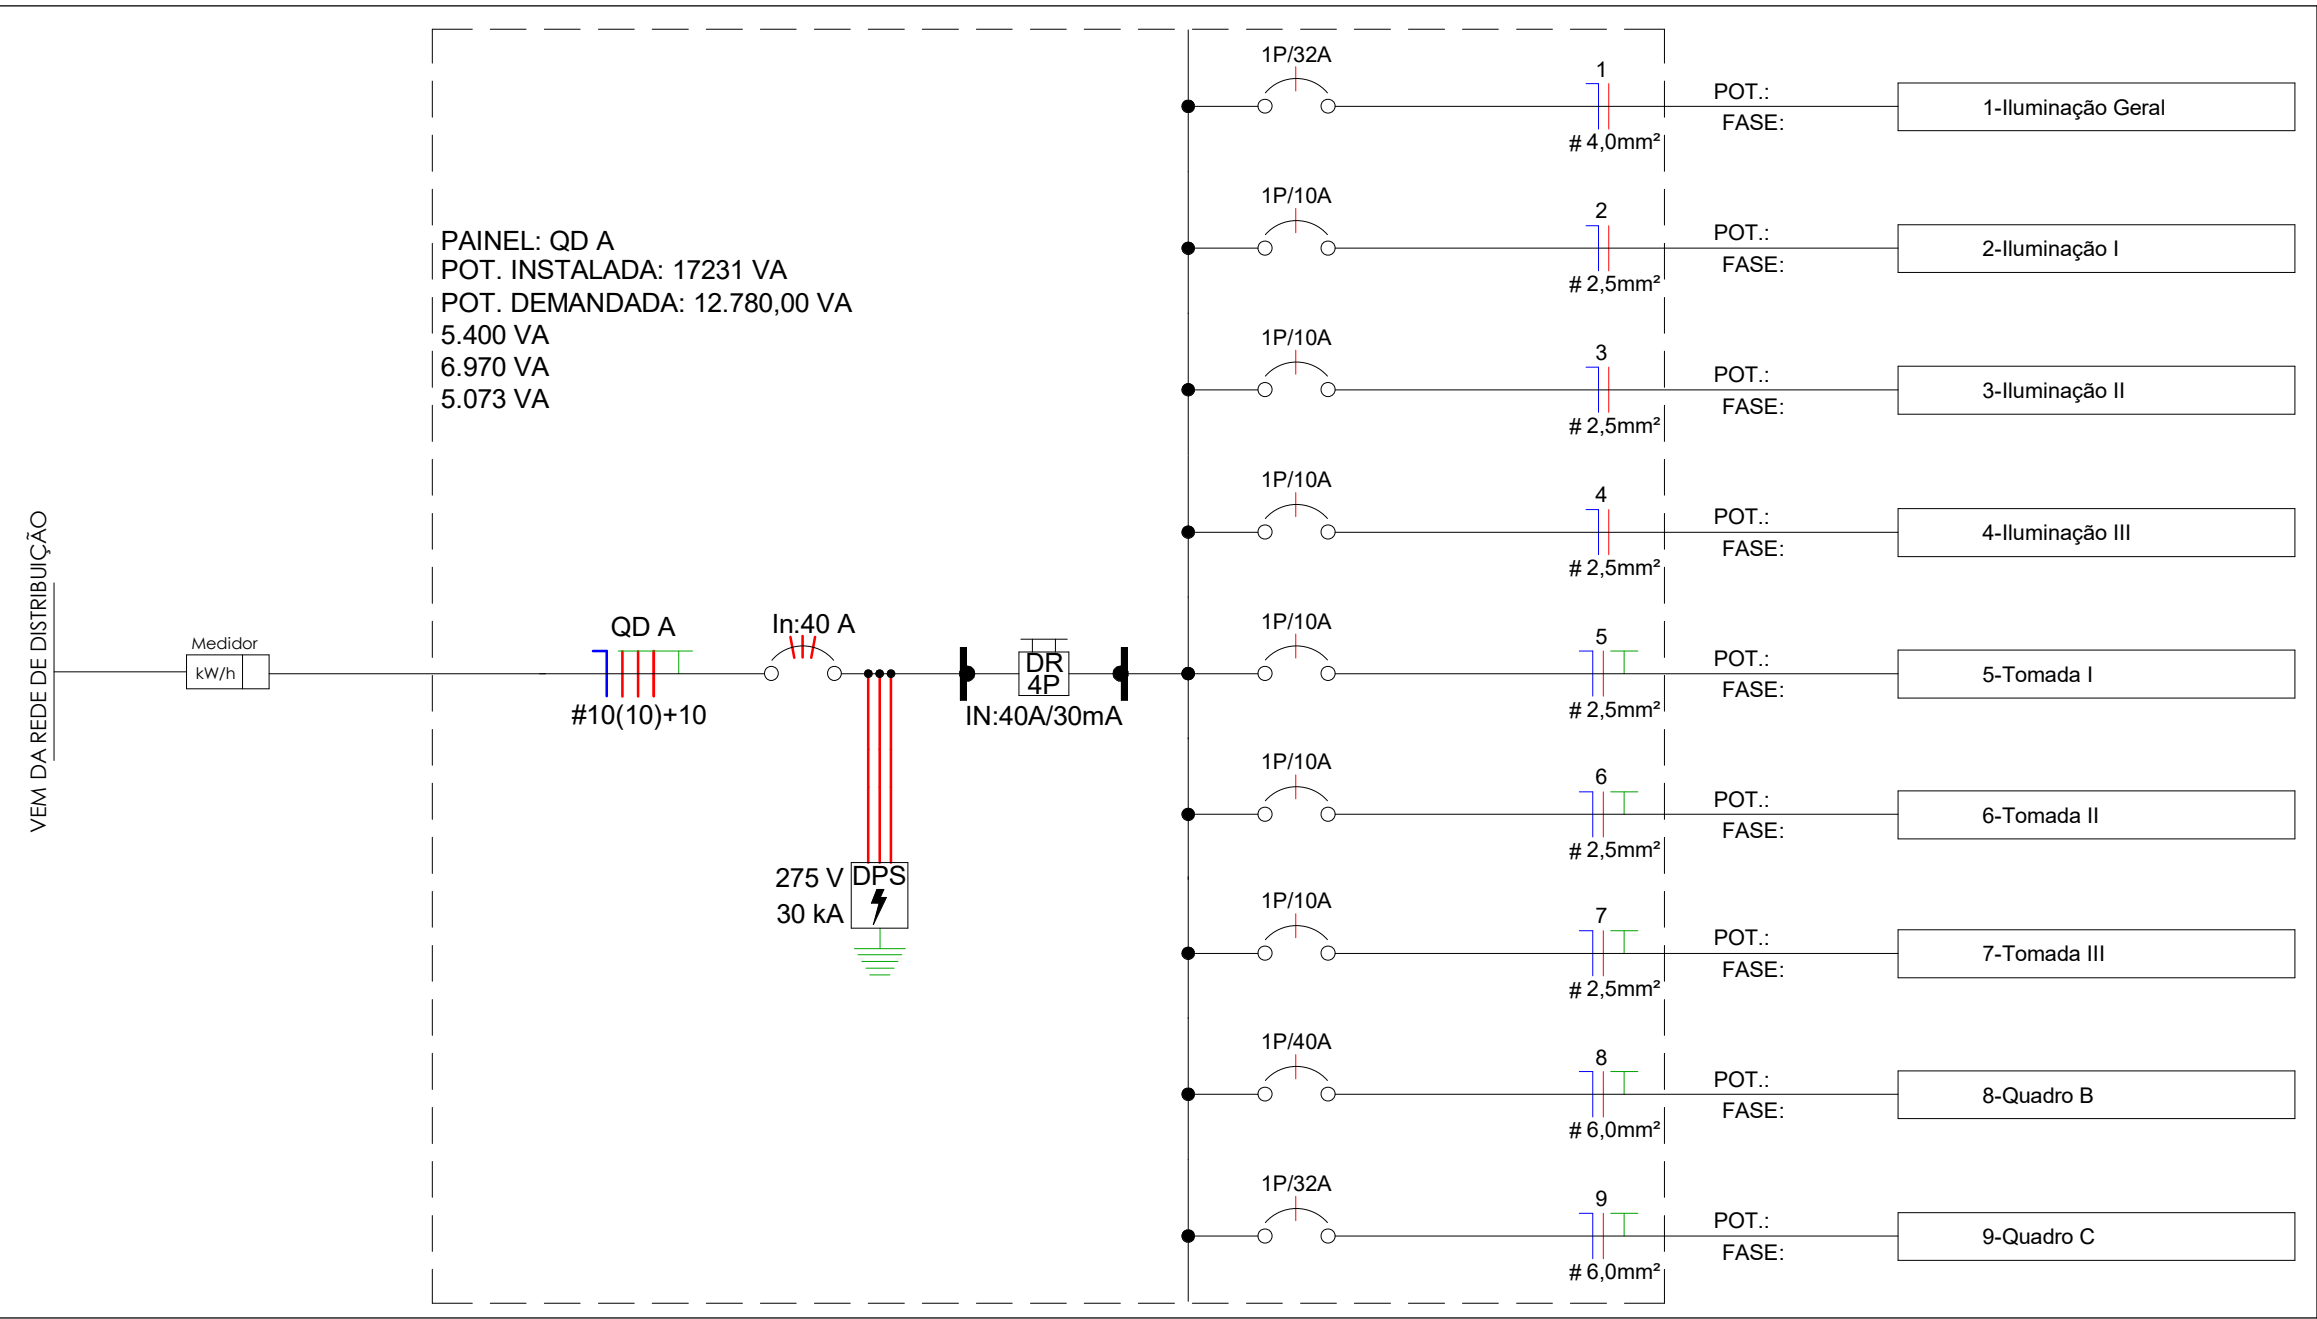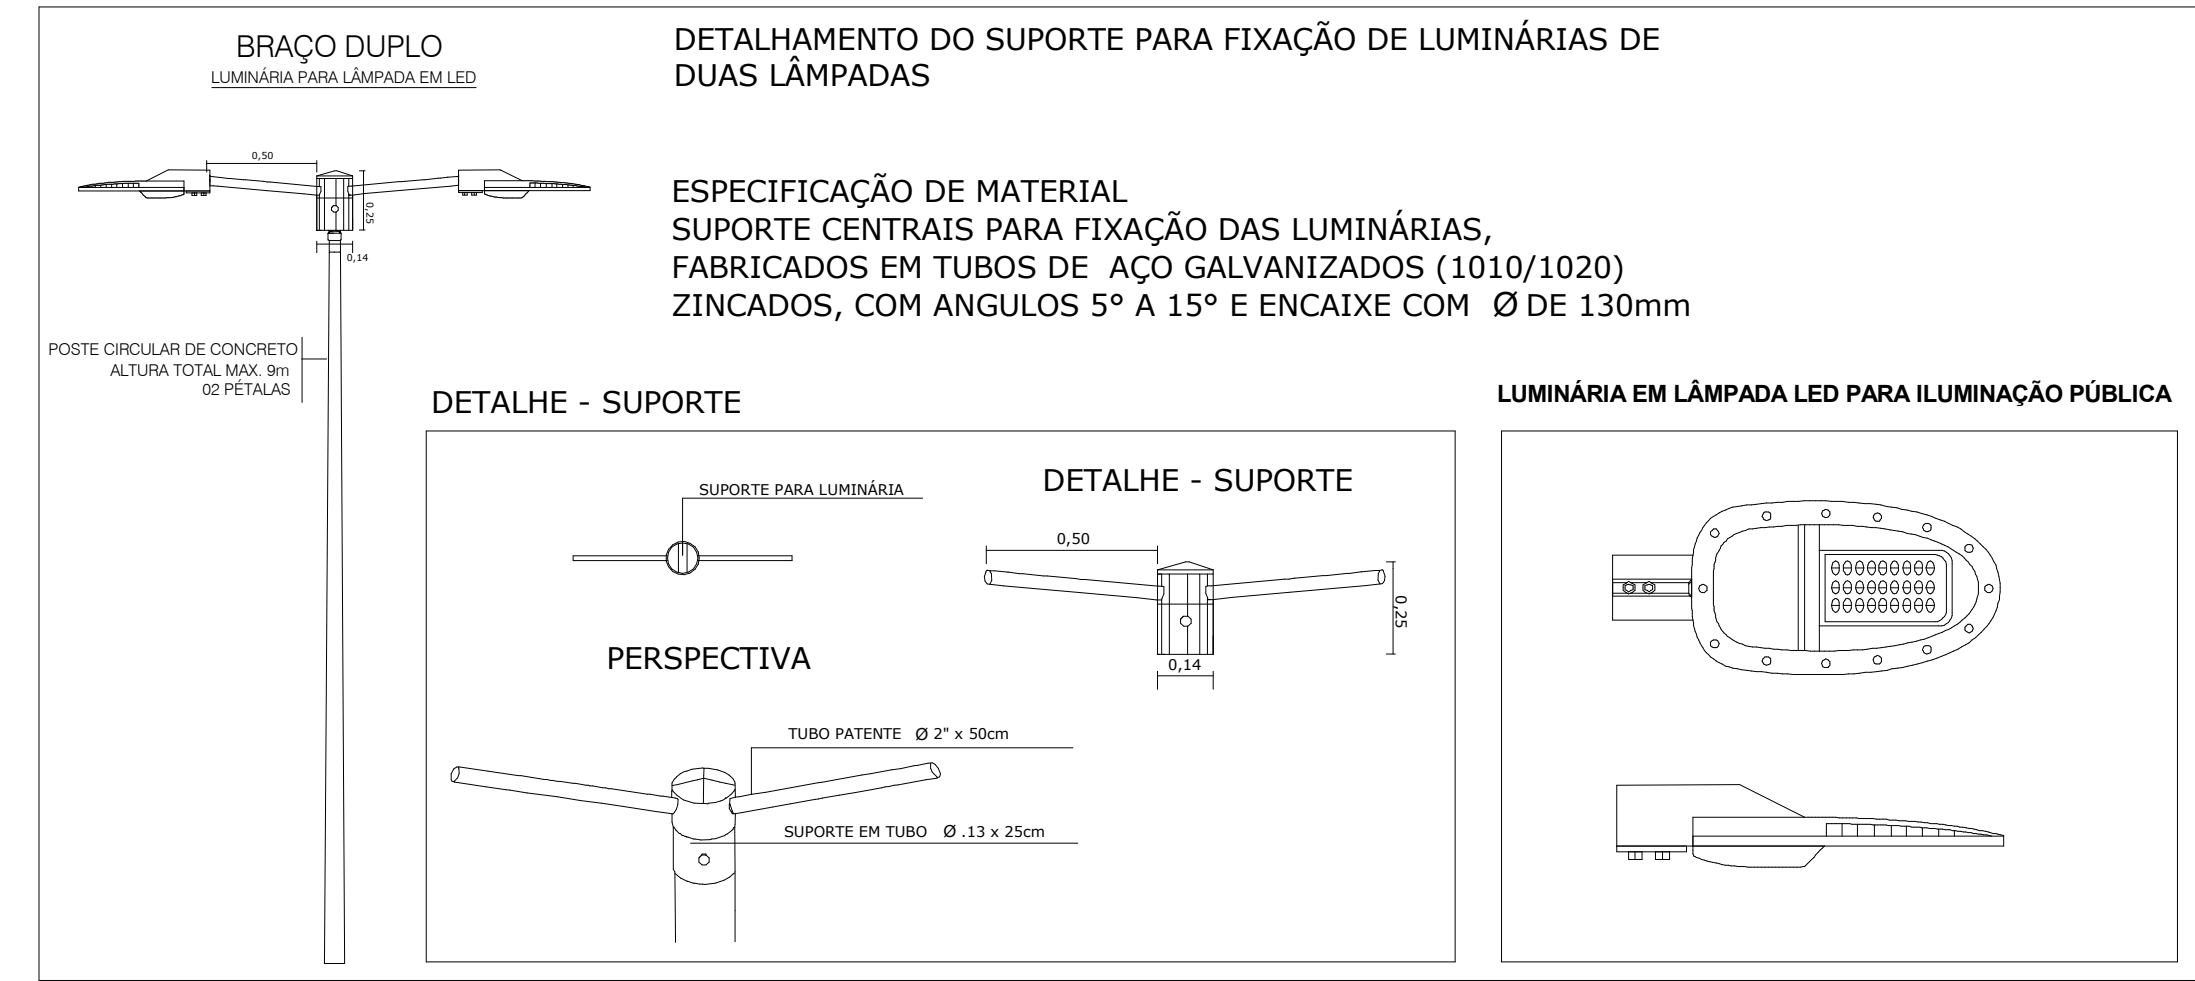

ILUMINAÇÃO		
DESCRIÇÃO DO PRODUTO	DIMENSÕES	QUANTIDADE
POSTE DE CONCRETO CIRCULAR H=	H = 9 Metros	8
REFLETOR LED 200W, COR BRANCA		8
LUMINÁRIA LED 250W, COR BRANCA (ILUMINAÇÃO PÚBLICA)		16

Quantitativo de Cabos em Metros (Cobre/Un/Isol. HEPR/0,6-1kV/90°C)			
(FA- Condutor Fase A), (FB- Condutor Fase B), (FC- Condutor...)			
Sugestão de Cores para os condutores- FA: Vermelho, FB:...			
F-6,0mm² 246	N -6,0mm² 83	T -6,0mm² 83	Tipo de Condutor Cabo Flexível HEPR 90°C 0,6/1 kV

Quantitativo de Cabos em Metros (Cobre/Un/Isol. PVC/750V/70°C)							
(FA- Condutor Fase A), (FB- Condutor Fase B), (FC- Condutor Fase C), (N - Condutor...)							
Sugestão de Cores para os condutores- FA: Vermelho, FB: Preto, FC:Amarelo, N: Azul...							
F-2,5mm² 356	F-4,0mm² 192	N -2,5mm² 411	N -4,0mm² 192	T -2,5mm² 191	T -4,0mm² 54	R -2,5mm² 91	Tipo de Condutor CABO COBRE PVC 70°C 450/750V

LINCOLN CARTAXO DE LIRA JUNIOR:06897861405

Assinado de forma digital por LINCOLN CARTAXO DE LIRA JUNIOR:06897861405

Dados: 2025.06.16 10:35:33 -03'00'


PROPRIETÁRIO:	PREFEITURA MUNICIPAL DE COREMAS-PB		
PROJETO:	LINCOLN CARTAXO DE LIRA JÚNIOR CREA 160.814.689-8		
PROJETO:	PROJETO A - ELÉTRICO GARAGEM COREMAS-PB		
CONCEDENTE:	PREFEITURA MUNICIPAL DE COREMAS - PB		
CONVENIENTE:	MUNICÍPIO DE COREMAS - PB		
LOCAL:	COREMAS-PB		
	DATA	RESPONSÁVEL TÉCNICO	RUBRICA
DESENHO	JUN/2025	LINCOLN CARTAXO	
CÓPIA			
VISTO			
PRANCHA:	DESCRIÇÃO:		ESCALA:
02	PROJETO ELÉTRICO - QUANTITATIVOS - DIAGRAMAS - DETALHAMENTOS		INDICADA
/04			



Av. Gov. Flavio R. Coutinho, 500, sl. 601
Jd. Oceania, 58037-005 - João Pessoa (PB)
Tel +55 99924.4447
e-mail: contato@lclprojetos.com



LINCOLN CARTAXO DE LIRA JUNIOR:06897861405		Assinado de forma digital por LINCOLN CARTAXO DE LIRA JUNIOR:06897861405 Dados: 2025.06.16 10:35:07 -03'00'	
PROPRIETÁRIO: PREFEITURA MUNICIPAL DE COREMAS-PB			
PROJETO: LINCOLN CARTAXO DE LIRA JÚNIOR		CREA 160.814.689-8	
PROJETO:	PROJETO B - ELÉTRICO GARAGEM COREMAS-PB		
CONCEDENTE:	PREFEITURA MUNICIPAL DE COREMAS - PB		
CONVENIENTE:	MUNICÍPIO DE COREMAS - PB		
LOCAL:	COREMAS-PB		
DATA	RESPONSÁVEL TÉCNICO	RUBRICA	DADOS
DESENHO JUN/2025	LINCOLN CARTAXO		CREA 160.814.689-8
CÓPIA			
VISTO			
PRANCHA:	DESCRIÇÃO: PROJETO ELÉTRICO - PLANTA BAIXA - QUANTITATIVOS -DETALHAMENTOS	ESCALA: INDICADA	

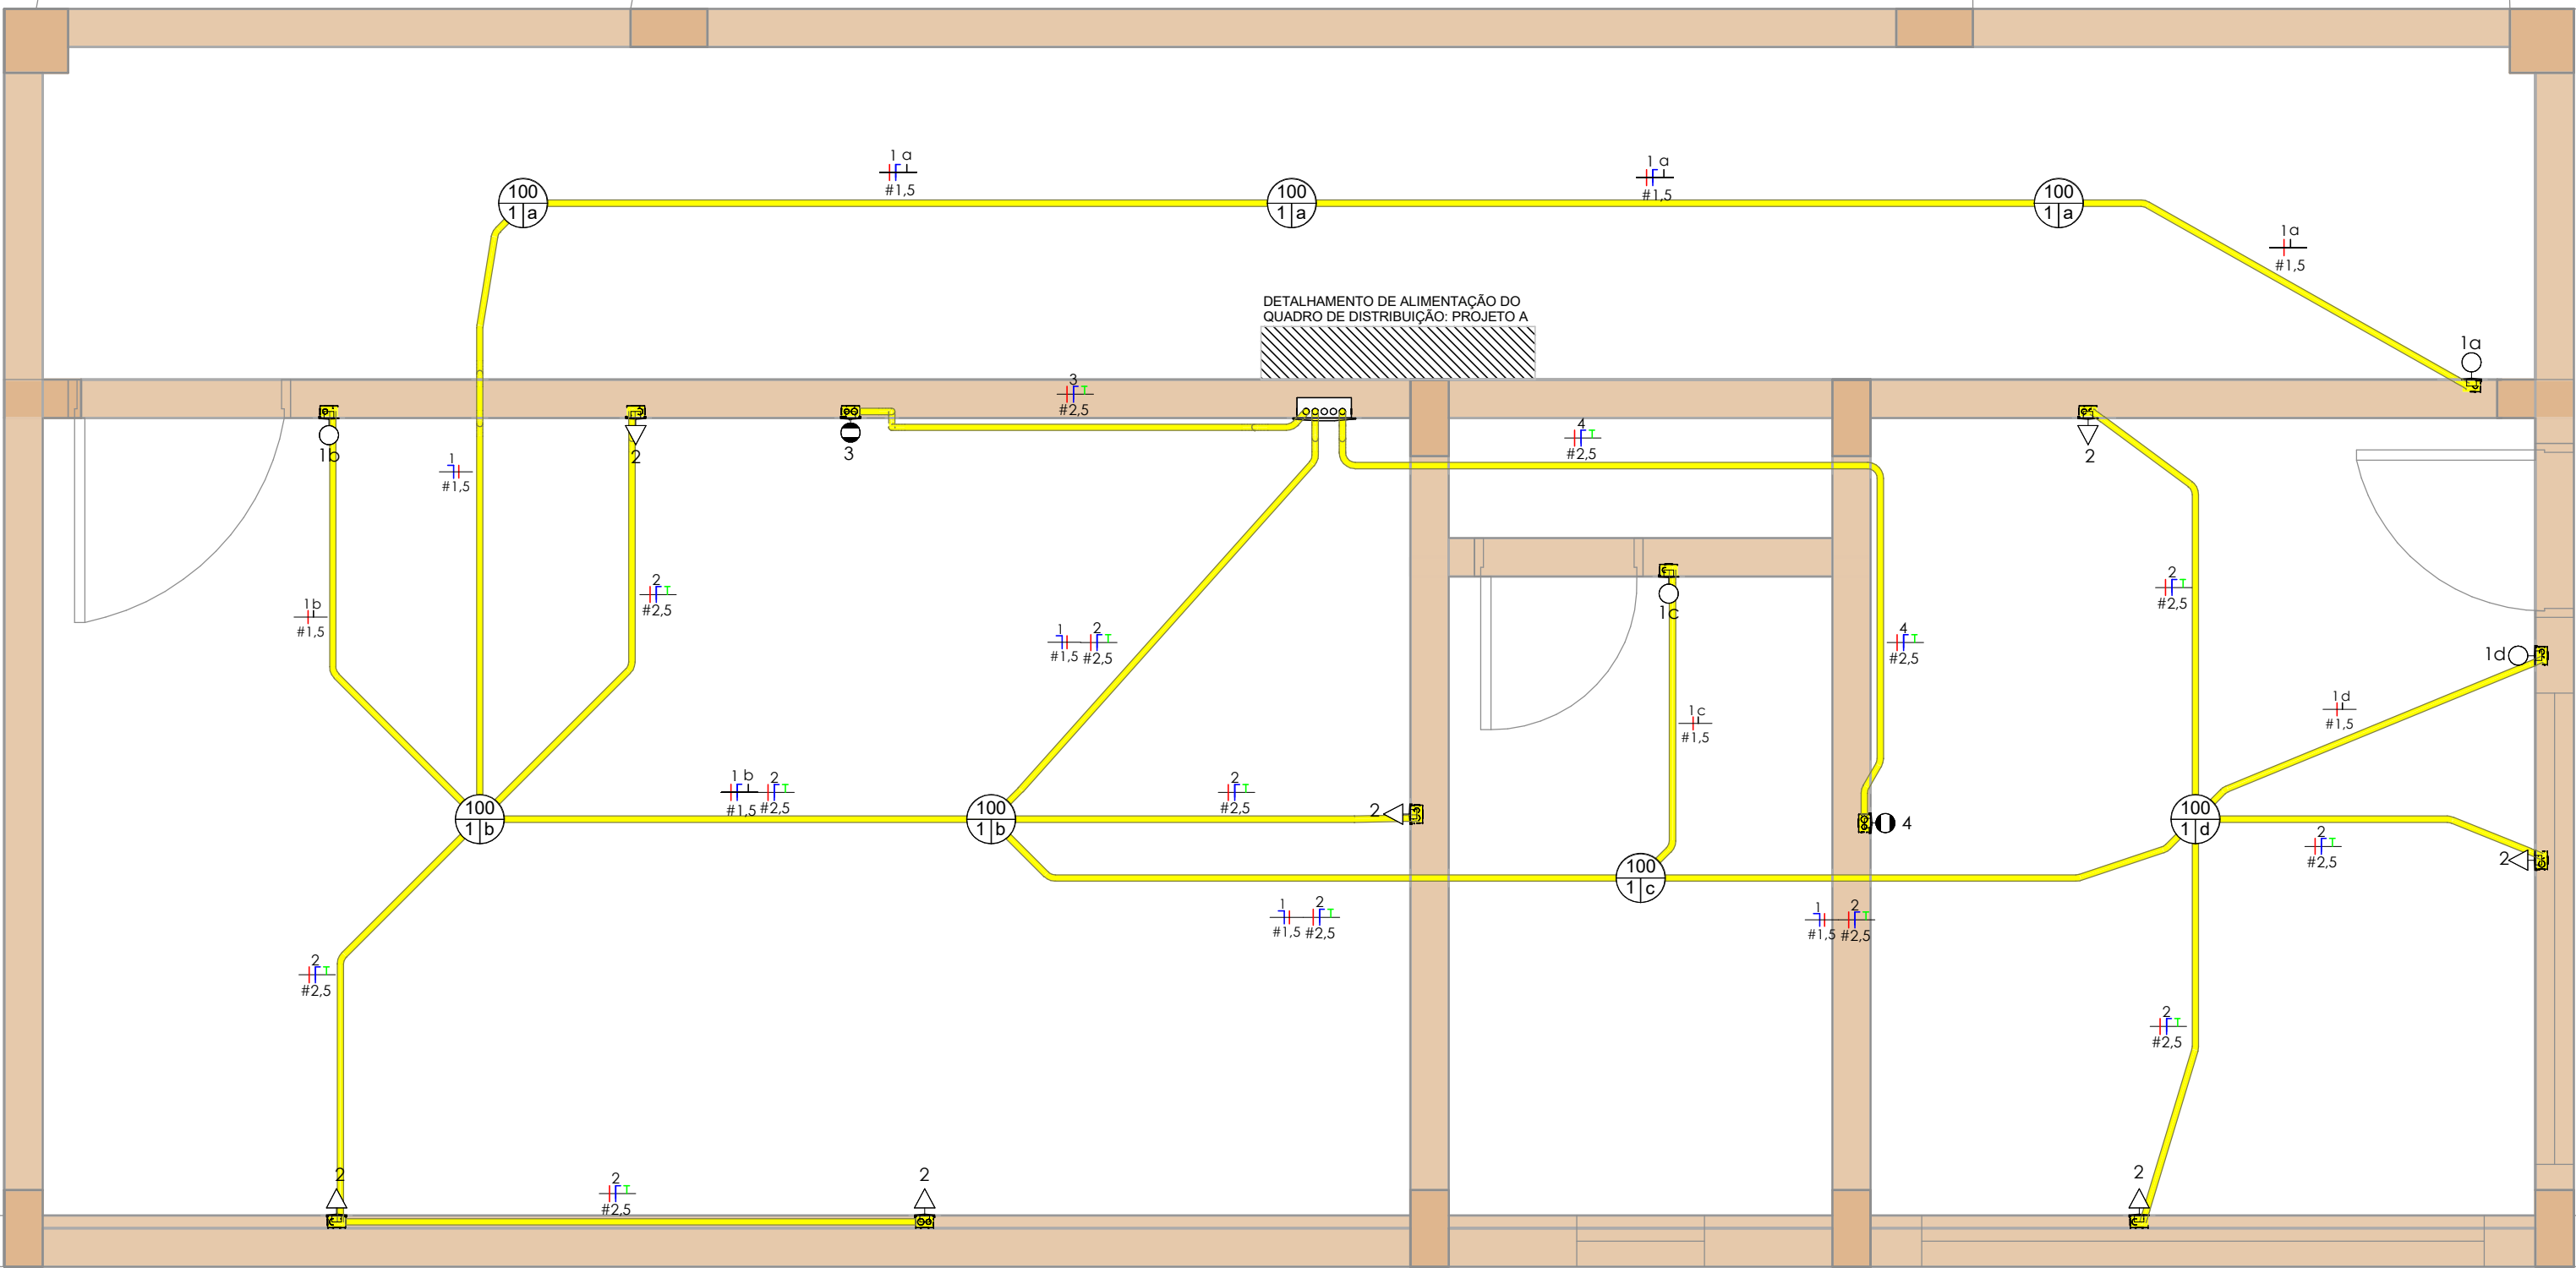

PLANTA BAIXA - TÉRREO

ESCALA_____ 1 : 25

GERAL - LISTA DE MATERIAIS - COMPONENTES

Descrição do Material	Dimensões	Quantidade (peças)
Interruptores Conjunto montado com 1 Interruptor simples, 10A 250V~, 4"x2"	1S, 4"x2"	4
Ponto de Ar Condicionado Ponto em caixa 4x2	Ponto de Ar Condicionado	2
Quadros Quadro de Distribuição 6/8 Disjuntores, de embutir, fabricado em PVC antichamas, com barramento de terra e neutro, porta branca, dimensões 245x190x78,7mm.	6/8 Disjuntores	1
Tomadas Conjunto montado de 1 Tomada 2P+T, 10A, posto horizontal, 4"x2"	10A, 4"x2"	7

QUANTITATIVO DE CABOS EM METROS (Cobre/Un/Iso. PVC/750V/70°C)


(F - Condutor Fase), (N - Condutor Neutro), (T - Condutor Terra), (Re - Condutor de Retorno)

Sugestão de Cores para os condutores- F: Vermelho, N: Azul Claro, PE: Verde, Re - Branco

F-1,5mm²	F-2,5mm²	N-1,5mm²	N-2,5mm²	T-2,5mm²	Re-1,5mm²	Tipo de Condutor
35,1	47,7	20,9	47,7	47,7	23,5	CABO COBRE PVC 70°C 450/750V

GERAL - LISTA DE MATERIAIS - ELETRODUTOS

Descrição do Material	Diâmetro Nominal	Comprimento (m)
Eletroduto flexível corrugado	Ø25	68,60 m

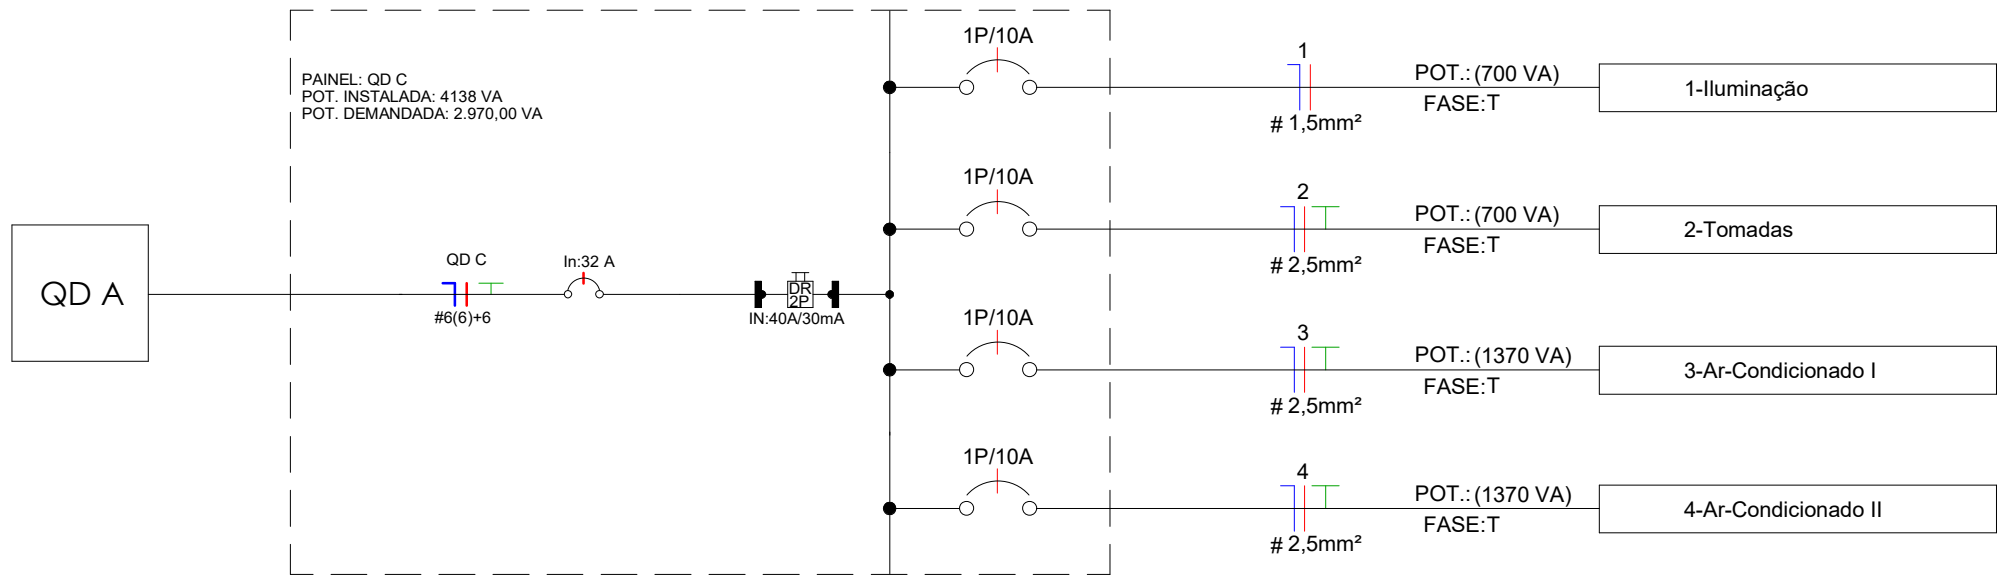

COMO ALTERNATIVA À ADOÇÃO DE FITA ISOLANTE, PARA UNIÃO DAS FIAÇÕES, QUE PORVENTURA IRÃO SER NECESSÁRIAS, RECOMENDAMOS A UTILIZAÇÃO DE CONECTORES.

ABAIXO ALGUNS MODELOS DISPONÍVEIS NO MERCADO.



Painel: QD C

Localização: Alimentação por: Montagem: Notas:

Alimentação: 220V/380V Monofásico (F+N+T)

Embutido

Circuito	Descrição	Tensão (V)	Esquema	Potência Total (VA)	FP	Potência Total (W)	Corrente Nominal (A)	FCA	FCT	Ib: Corrente de Projeto Corrigida (A)	In: Disjuntor (A)	Tipo de Instalação	Condutor Pré-Dimensionado (Seção e Iz: Capacidade de condução de Corrente)	Seção do Condutor Adotado (mm²)	L Aprox. (m)	L Considerado (m)	Queda de Tensão (%)	Potência
1	Iluminação	220,00	FNT	700 VA	0,92	644 W	3,18 A	0,8	1	3,98 A	10,00 A	[Cu/PVC/750V/70°]-Un-B1-2Cc (Ilum.)	1-#1,5(17,5A), 1-#1,5(17,5A), 1-#1,5	1,5	7,83	10	0,39	700 VA
2	Tomadas	220,00	FNT	700 VA	0,9	630 W	3,18 A	0,8	1	3,98 A	10,00 A	[Cu/PVC/750V/70°]-Un-B1-2Cc	1-#2,5(24A), 1-#2,5(24A), 1-#2,5	2,5	12,18	15	0,34	700 VA
3	Ar-Condicionado I	220,00	FNT	1370 VA	0,92	1260 W	6,23 A	1	1	6,23 A	10,00 A	[Cu/PVC/750V/70°]-Un-B1-2Cc	1-#2,5(24A), 1-#2,5(24A), 1-#2,5	2,5	4,99	10	0,46	1370 VA
4	Ar-Condicionado II	220,00	FNT	1370 VA	0,92	1260 W	6,23 A	1	1	6,23 A	10,00 A	[Cu/PVC/750V/70°]-Un-B1-2Cc	1-#2,5(24A), 1-#2,5(24A), 1-#2,5	2,5	6,58	10	0,46	1370 VA
5																		

Legenda:

FP: Fator de Potência
FCA:Fator de Correção por Agrupamento
FCT:Fator de Correção por Temperatura

Ib: Corrente de Projeto Corrigida(A)
In:Corrente Nominal do Disjuntor (A)
Iz: Capacidade de condução de corrente do condutor(A)

(Ib < In < Iz)

Tipo de Carga	Potência Instalada (VA)	Fator de Demanda	Potência Demandada (VA)	Totais do Pannel
Iluminação+TUGs (Residencial)	1400 VA	0,40	560 VA	
Ar Condicionado	2739 VA	0,88	2410 VA	
				Potência Instalada: 4138 VA
				Potência Demandada: 2970 VA
				Corrente Total: 18,81 A
				Corrente Total Demandada: 13,50 A

Notas:

LINCOLN CARTAXO DE LIRA JUNIOR:06897861405

Assinado de forma digital por LINCOLN CARTAXO DE LIRA JUNIOR:06897861405

Dados: 2025.06.16 10:34:16 -03'00'

PROPRIETÁRIO: PREFEITURA MUNICIPAL DE COREMAS-PB

PROJETO: LINCOLN CARTAXO DE LIRA JÚNIOR CREA 160.814.689-8

PROJETO: PROJETO C - ELÉTRICO GARAGEM COREMAS - PB

CONCEDENTE: PREFEITURA MUNICIPAL DE COREMAS - PB

CONVENIENTE: MUNICÍPIO DE COREMAS - PB

LOCAL: COREMAS-PB

DATA	RESPONSÁVEL TÉCNICO	RUBRICA	DADOS
DESENHO JUN/2025	LINCOLN CARTAXO		CREA 160.814.689-8
CÓPIA			
VISTO			

PRANCHA: DESCRIÇÃO: PROJETO ELÉTRICO

04 /04

- PLANTA BAIXA
- QUANTITATIVOS
- DETALHAMENTOS

ESCALA:

INDICADA



Av. Gov. Flavio R. Coutinho, 500, sl. 601
Jd. Oceania, 58037-005 - João Pessoa (PB)
Tel +55 99924.4447
e-mail: contato@lclprojetos.com