


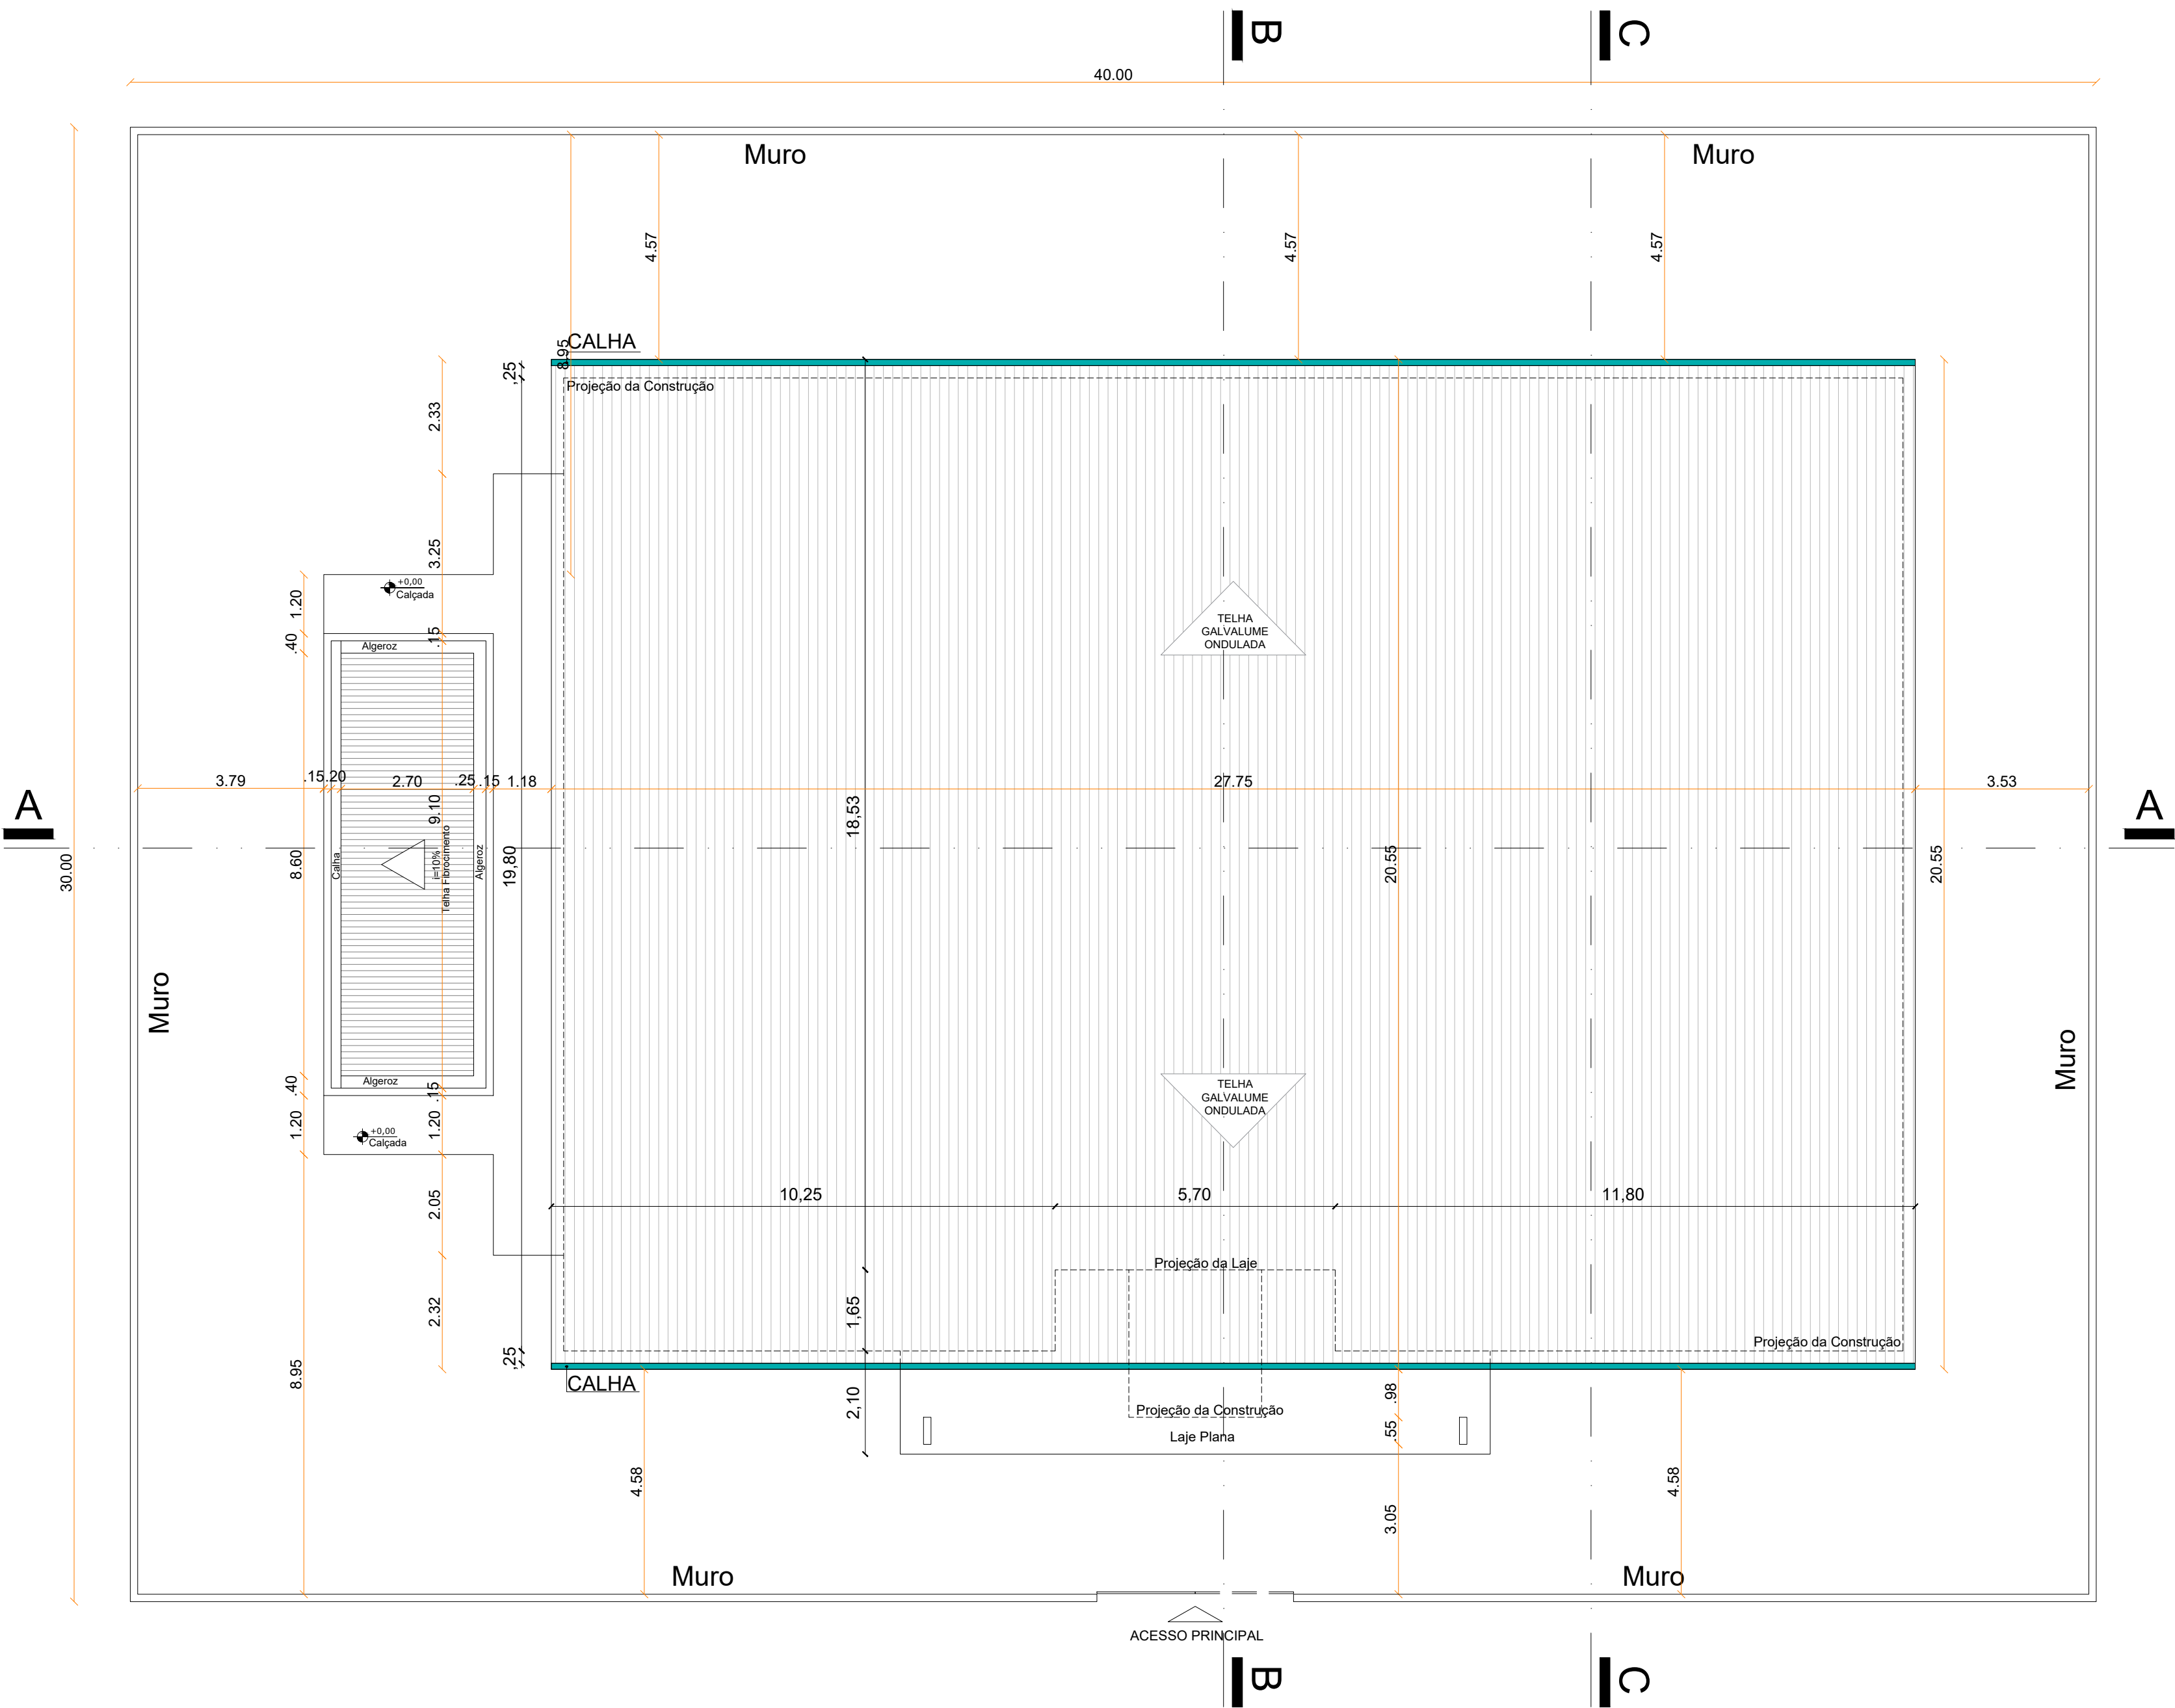

PLANTA DE COBERTA  
ESC.: 1:100



PROPRIETÁRIO: PREFEITURA MUNICIPAL DE COREMAS - PB  
LINCOLN CARTAXO DE LIRA JUNIOR:06897861405  
PROJETO: LINCOLN CARTAXO DE LIRA JÚNIOR CREA 160.814.689-8

CONSTRUÇÃO:


FOLHA 01/08  
PROJETO: CONSTRUÇÃO DE GINÁSIO POLIESPORTIVO  
CONVENIENTE: PREFEITURA MUNICIPAL DE COREMAS - PB  
CONVENIADO: MUNICÍPIO DE COREMAS - PB  
LOCALIDADE: COREMAS - PB

|          | DATA              | RESPONSÁVEL     | RUBRICA | DADOS |
|----------|-------------------|-----------------|---------|-------|
| DESENHO  | AGO/2025          | LINCOLN CARTAXO |         |       |
| CÓPIA    |                   |                 |         |       |
| VISTO    |                   |                 |         |       |
| ESCALAS  | DESENHOS          | CONVÊNIO        |         |       |
| Indicada | Planta de Coberta | ARQUIVO         |         |       |

Aprovações:




Av. Gov. Flávio Ribeiro Coutinho, 500, sl. 601  
Jardim Oceania, 58037-005 - João Pessoa (PB)  
Tel +55 (83) 99924.4447  
e-mail: contato@lclprojetos.com

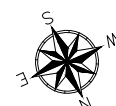


Av. Gov. Flávio Ribeiro Coutinho, 500, sl. 601  
Jardim Oceania, 58037-005 - João Pessoa (PB)  
Tel +55 (83) 99924.4447  
e-mail: contato@lclprojetos.com




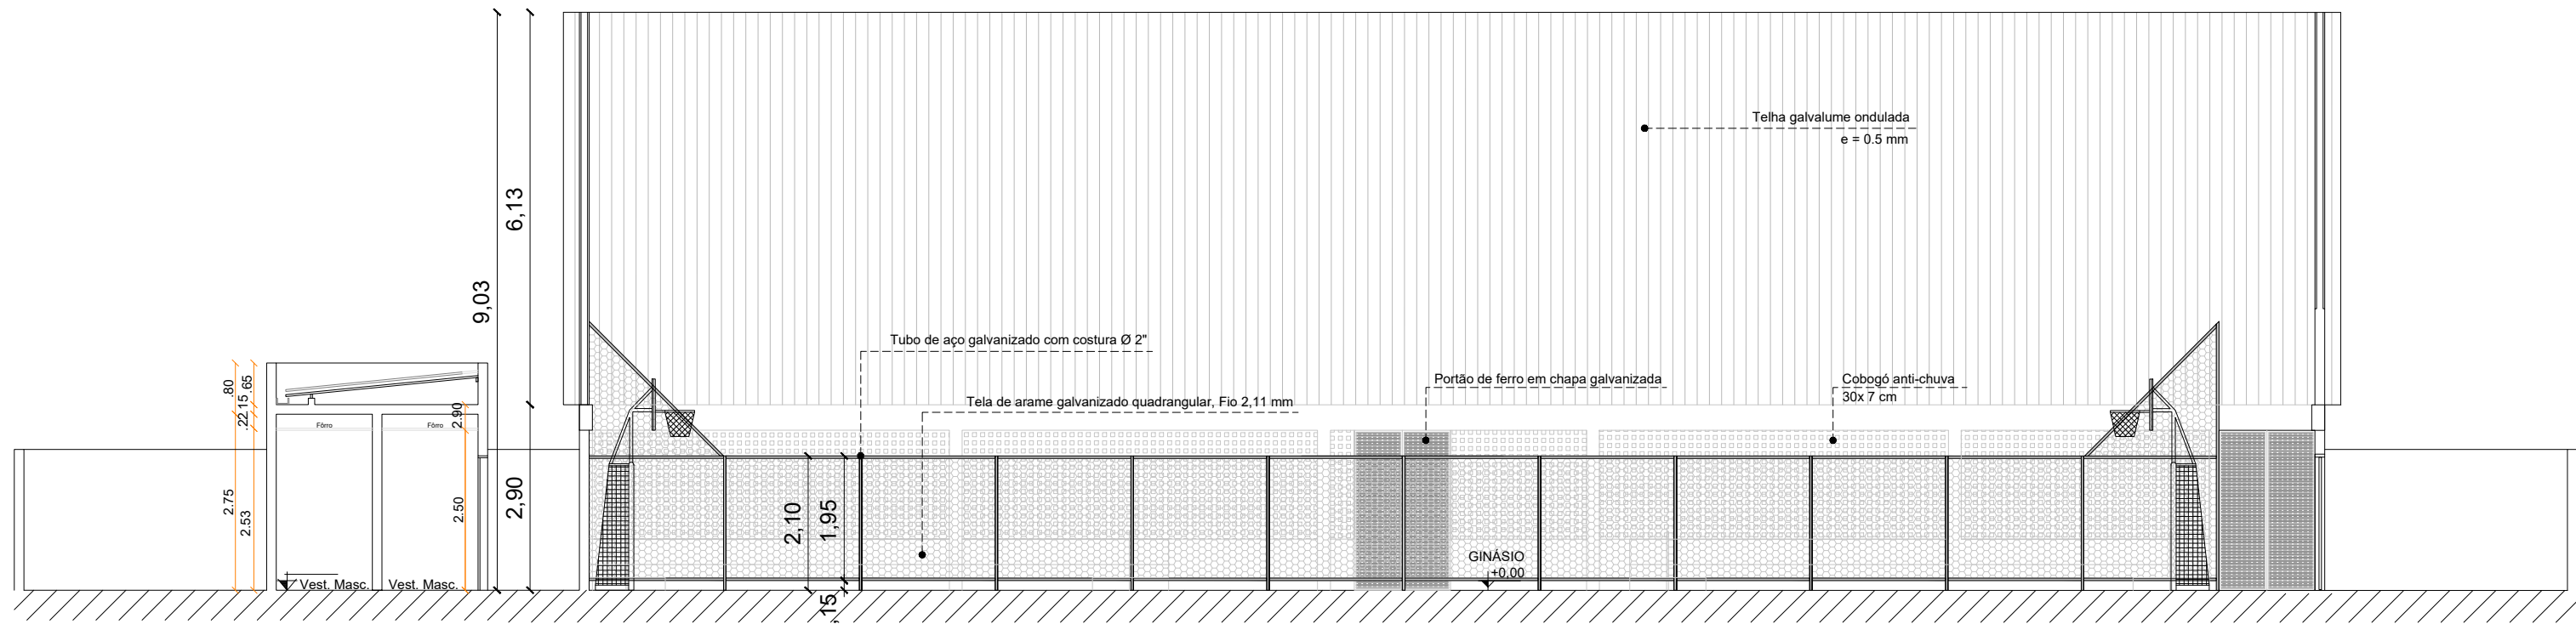

CORTE A-A  
escala 1/100

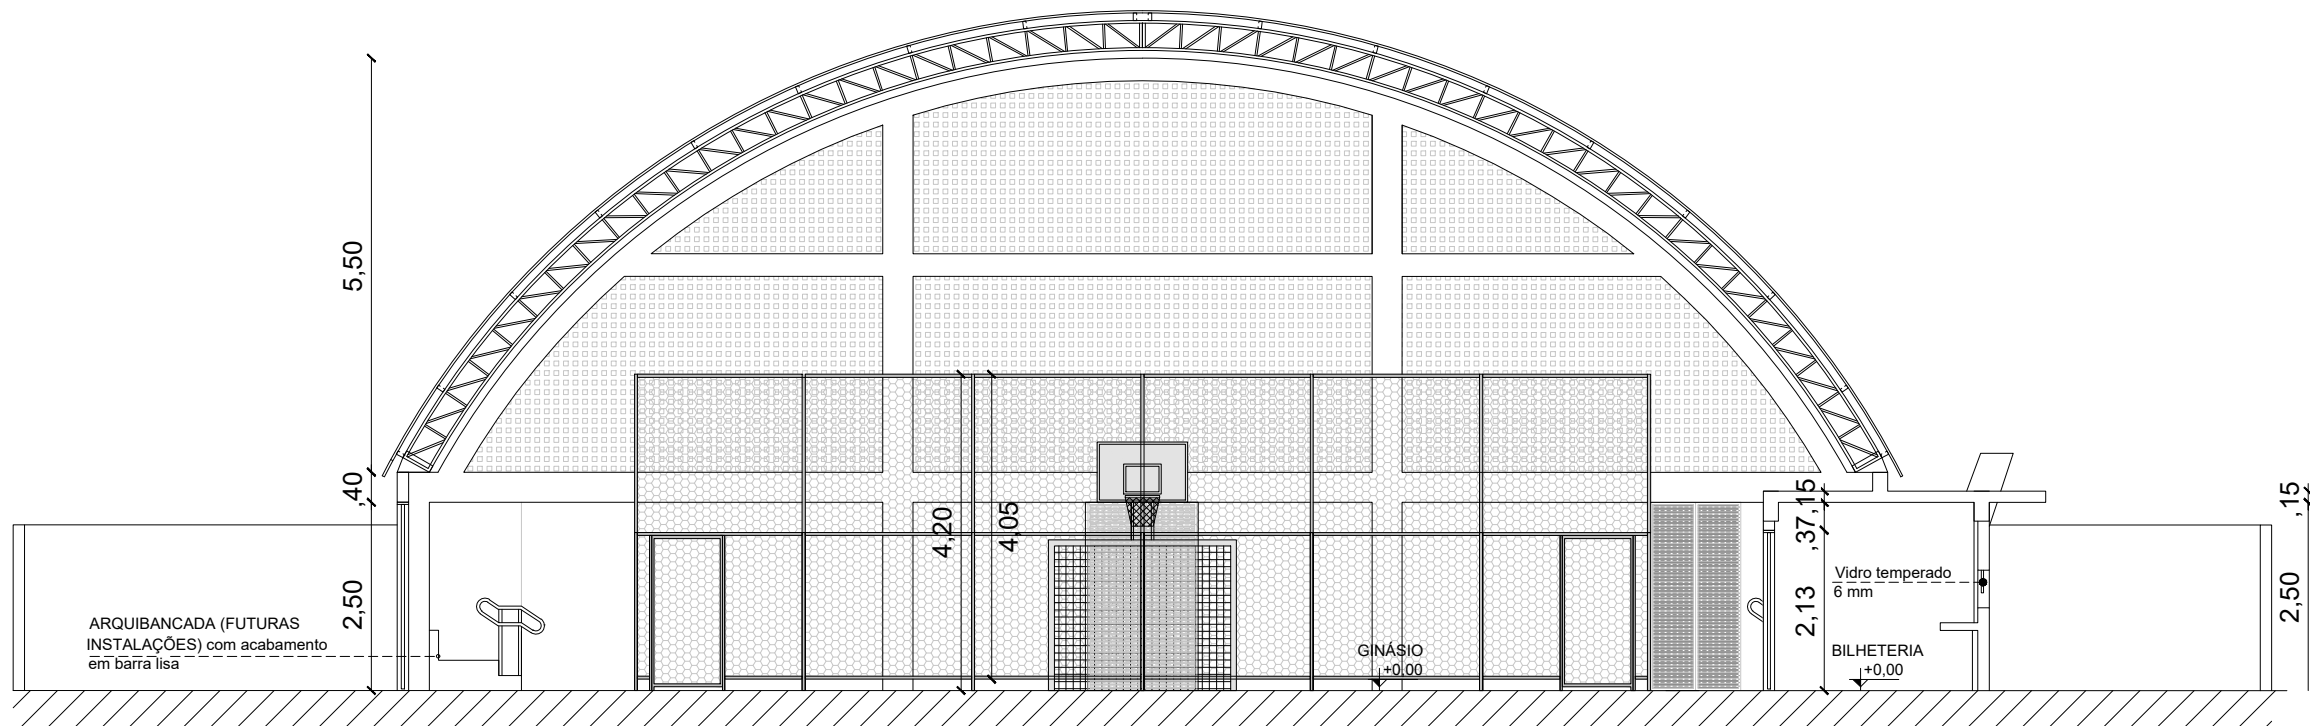

CORTE B-B  
escala 1/100

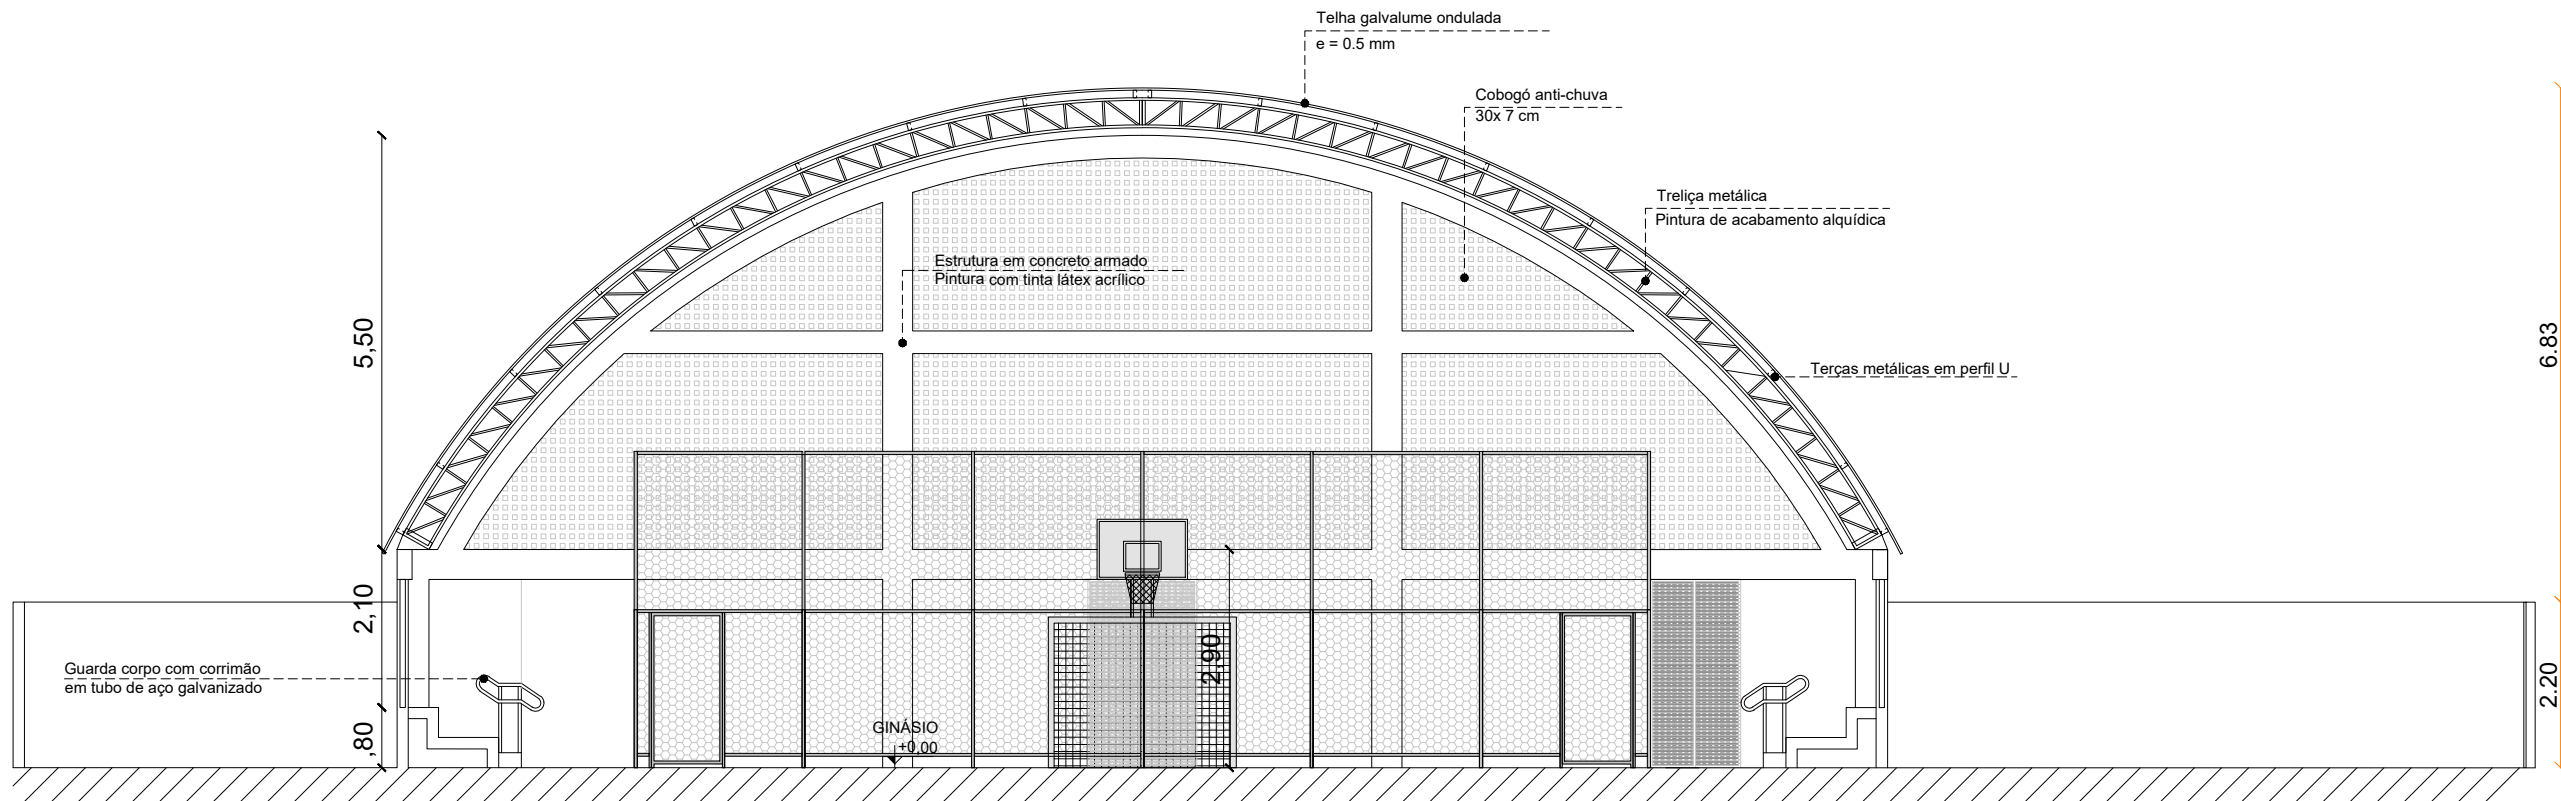

CORTE C-C  
escala 1/100

PROPRIETÁRIO: PREFEITURA MUNICIPAL DE COREMAS - PB  
**LINCOLN CARTAXO DE LIRA JÚNIOR:06897861405** Assinado de forma digital por LINCOLN CARTAXO DE LIRA JÚNIOR:06897861405  
Dados: 2025.08.08 12:13:56 -03'00'  
PROJETO: LINCOLN CARTAXO DE LIRA JÚNIOR CREA 160.814.689-8

CONSTRUÇÃO:

|       |              |                                      |
|-------|--------------|--------------------------------------|
| FOLHA | PROJETO:     | CONSTRUÇÃO DE GINÁSIO POLIESPORTIVO  |
|       | CONVENIENTE: | PREFEITURA MUNICIPAL DE COREMAS - PB |
|       | CONVENIADO:  | MUNICÍPIO DE COREMAS - PB            |
|       | LOCALIDADE:  | COREMAS - PB                         |

|         | DATA     | RESPONSÁVEL     | RUBRICA | DADOS |
|---------|----------|-----------------|---------|-------|
| DESENHO | AGO/2025 | LINCOLN CARTAXO |         |       |
| CÓPIA   |          |                 |         |       |
| VISTO   |          |                 |         |       |


| ESCALAS  | DESENHOS                         | CONVÊNIO |
|----------|----------------------------------|----------|
| Indicada | Corte AA<br>Corte BB<br>Corte CC |          |
|          |                                  | ARQUIVO  |

Aprovações:




Av. Gov. Flávio Ribeiro Coutinho, 500, sl. 601  
Jardim Oceania, 58037-005 - João Pessoa (PB)  
Tel +55 (83) 99924-4447  
e-mail: contato@lclprojetos.com



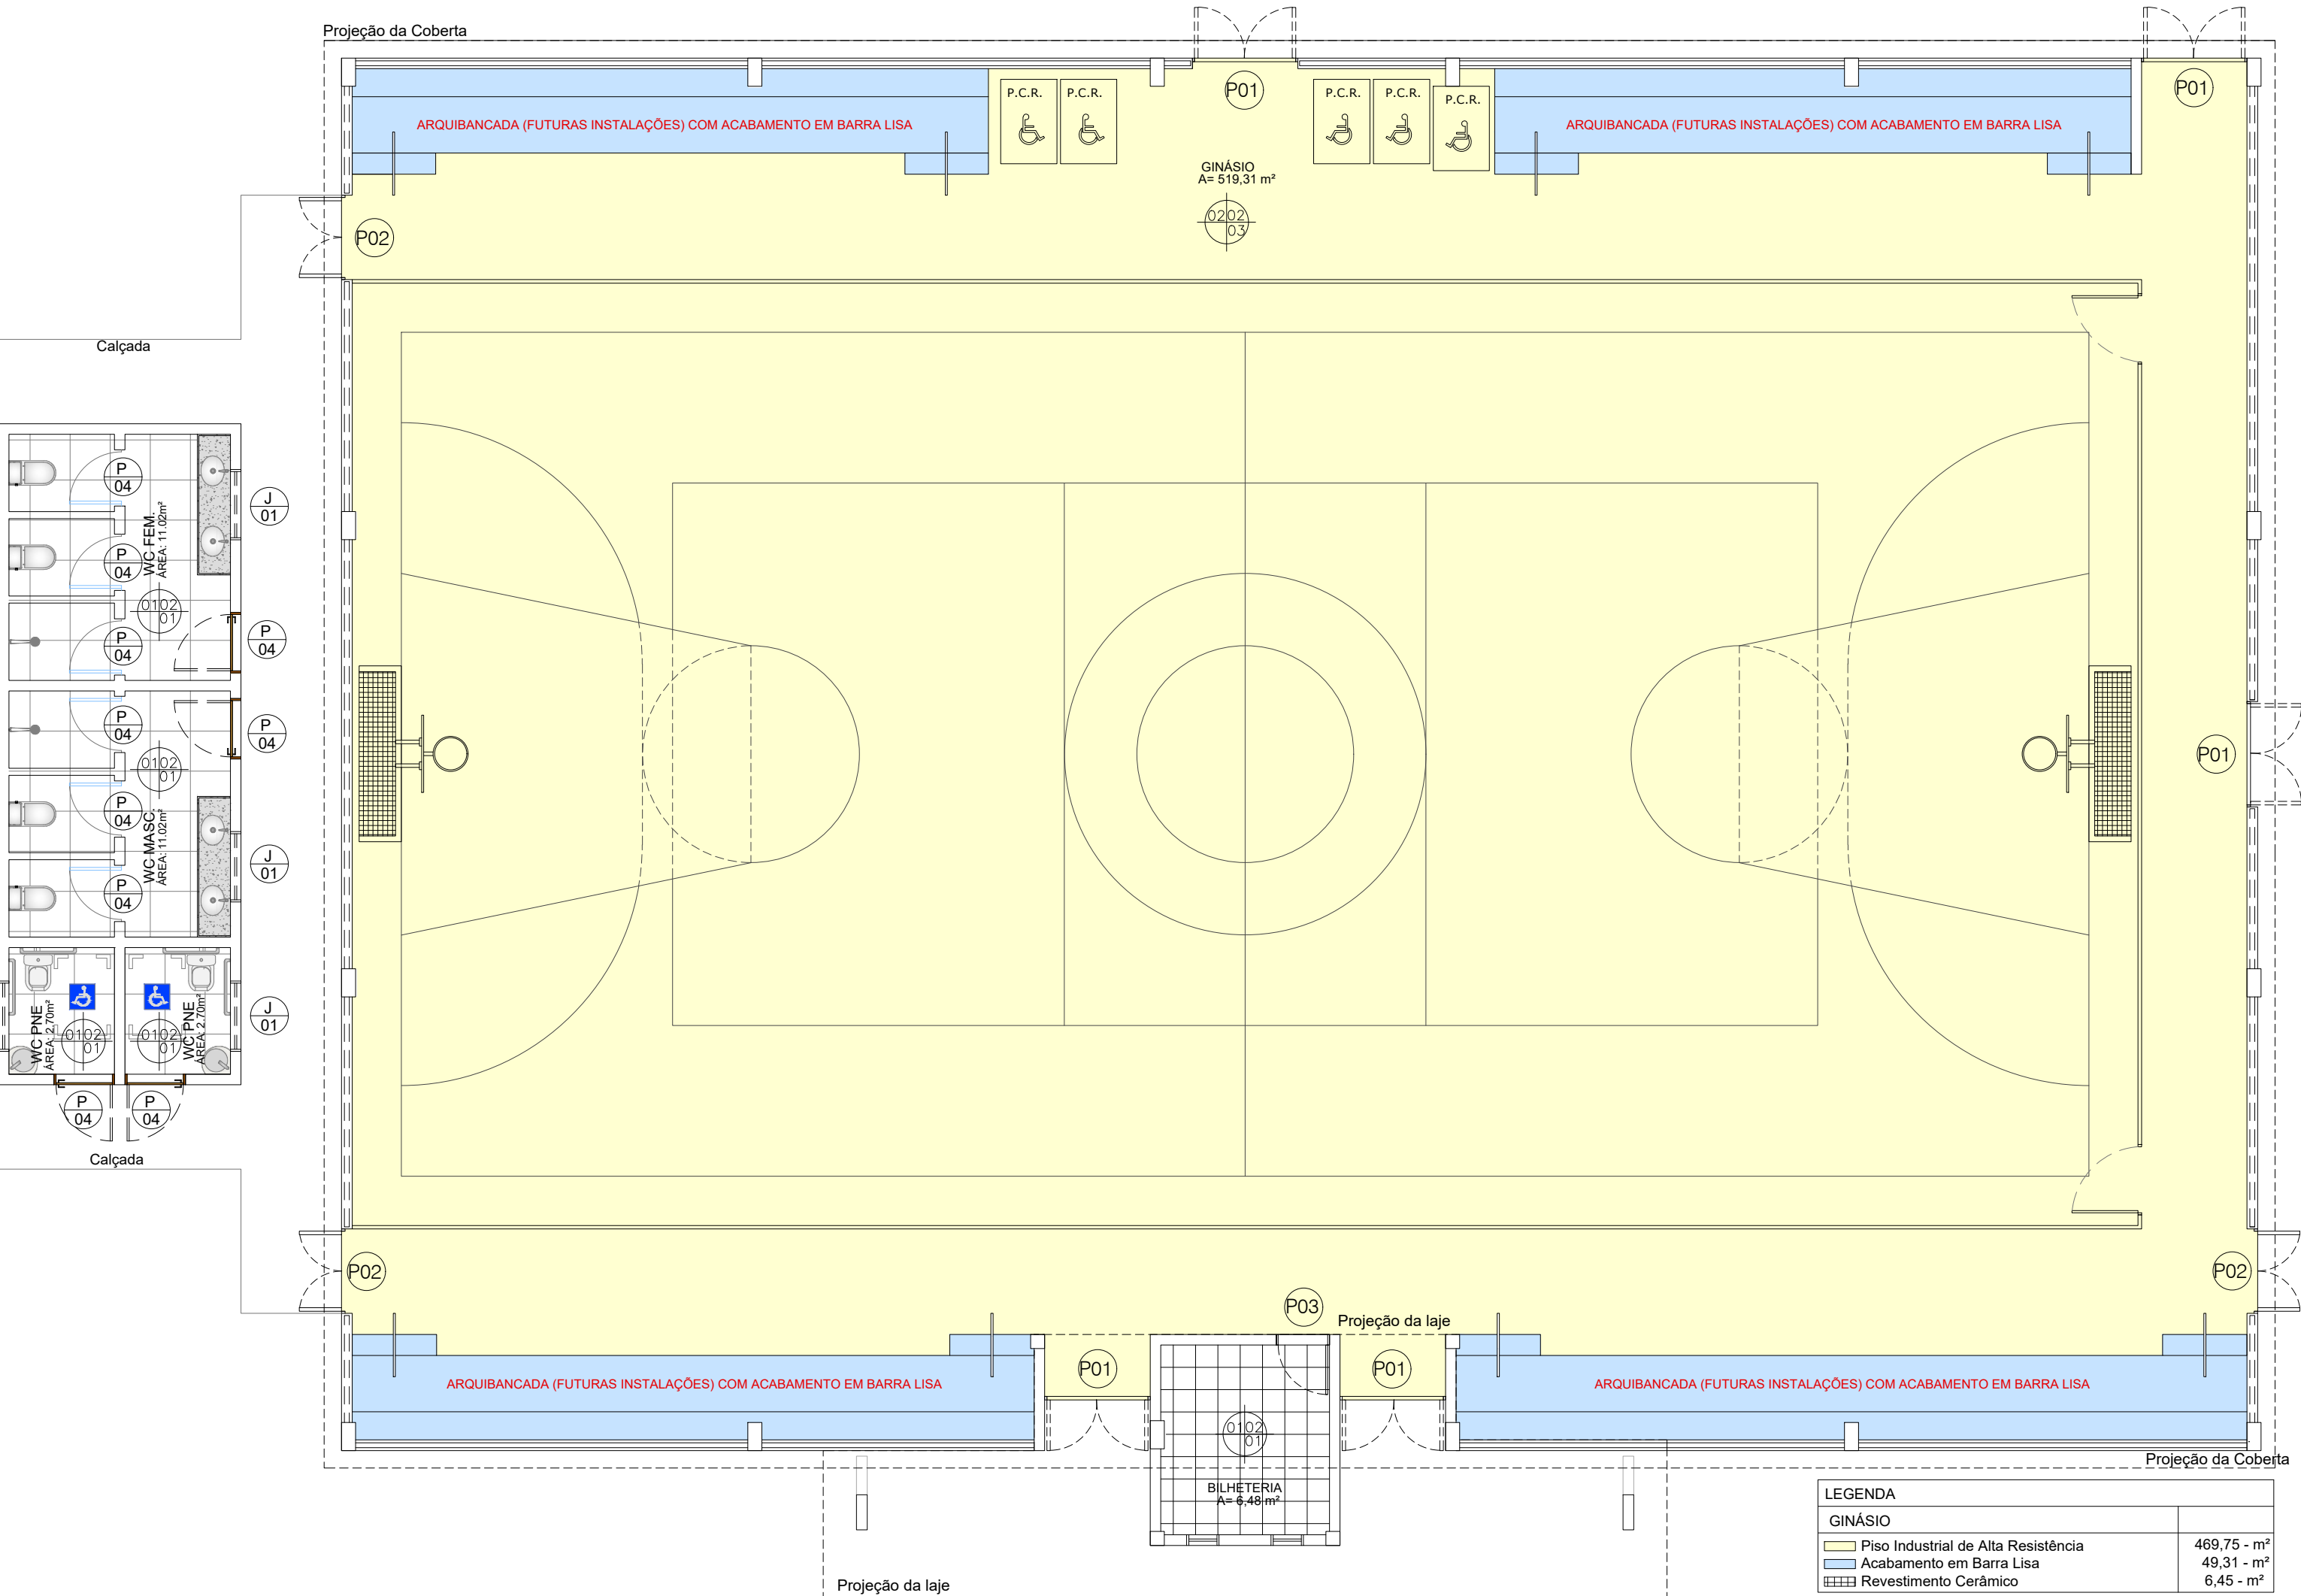


| QUADRO DE ESQUADRIAS |         |        |          |        |                                      |                            |
|----------------------|---------|--------|----------|--------|--------------------------------------|----------------------------|
| PORTAS - GINÁSIO     |         |        |          |        |                                      |                            |
| TIPO                 | LARGURA | ALTURA | QUANT.   | TIPO   | ESPECIFICAÇÕES                       |                            |
| P01                  | 1.50    | 2.50   | 5        | ABRIR  | PORTÃO DE FERRO EM CHAPA GALVANIZADA |                            |
| P02                  | 1.20    | 2.50   | 3        | ABRIR  | PORTÃO DE FERRO EM CHAPA GALVANIZADA |                            |
| P03                  | 0.70    | 2.13   | 1        | ABRIR  | PORTÃO DE ALUMÍNIO                   |                            |
| P04                  | 0.80    | 2.10   | 10       | ABRIR  | PORTA DE ALUMÍNIO                    |                            |
| JANELAS - GINÁSIO    |         |        |          |        |                                      |                            |
| TIPO                 | LARGURA | ALTURA | PEITORIL | QUANT. | TIPO                                 | ESPECIFICAÇÕES             |
| J01                  | 1.00    | 0.50   | 0.60     | 4      | BOCA DE LOBO                         | JANELA DE ALUMÍNIO E VIDRO |


| QUADRO DE ESPECIFICAÇÕES |                                                                                                   |                                                                                            |                                                                                          |
|--------------------------|---------------------------------------------------------------------------------------------------|--------------------------------------------------------------------------------------------|------------------------------------------------------------------------------------------|
|                          |  PISO          |  PAREDE |  TETO |
| PISO                     | 01 - Piso em revestimento cerâmico com placa tipo grês (35x35 cm)                                 |                                                                                            |                                                                                          |
|                          | 02 - Piso industrial de alta resistência (e=8mm), com junta de dilatação plástica e pintura epóxi |                                                                                            |                                                                                          |
| PAREDE                   | 01 - Revestimento em cerâmica (até h=1,2m), Emassamento e pintura acrílica                        |                                                                                            |                                                                                          |
|                          | 02 - Emassamento e Pintura com tinta acrílica                                                     |                                                                                            |                                                                                          |
| TETO                     | 01 - Forro de gesso em placas sob laje.                                                           |                                                                                            |                                                                                          |
|                          | 02 - Laje pré-moldada, e=12 cm, Fck=12Mpa.                                                        |                                                                                            |                                                                                          |
|                          | 03 - Coberta de estrutura metálica em tesouras ou treliças e cobertura em telha de aço zincado.   |                                                                                            |                                                                                          |
| OBS.                     | Todas as Bancadas serão em Granito Cinza, e=2,5mm                                                 |                                                                                            |                                                                                          |

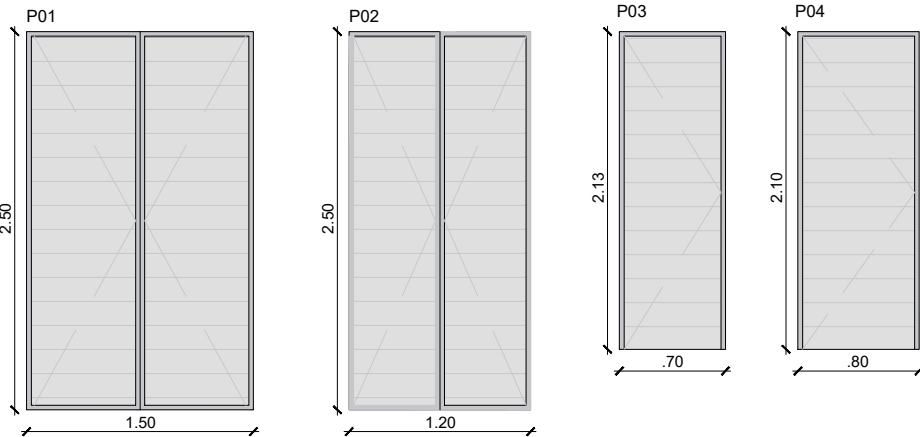

DETALHE 01 - ESQUADRIAS  
ESC.: 1:50

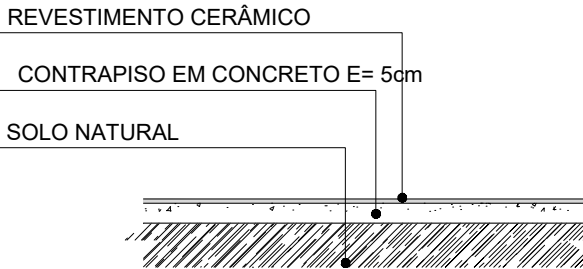

DETALHE 02 - REVESTIMENTO CERÂMICO  
ESC.: S/E

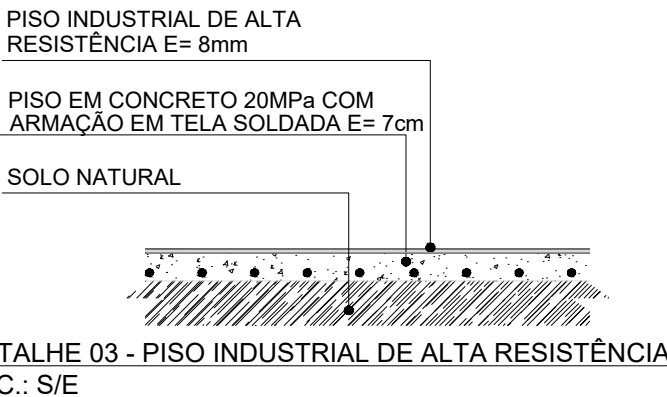

DETALHE 03 - PISO INDUSTRIAL DE ALTA RESISTÊNCIA  
ESC.: S/E

PROPRIETÁRIO: PREFEITURA MUNICIPAL DE COREMAS - PB  
**LINCOLN CARTAXO DE LIRA JUNIOR:06897861405**  
Assinado de forma digital por LINCOLN CARTAXO DE LIRA JUNIOR:06897861405  
Dados: 2025.08.08 12:12:56 -03'00'

PROJETO: LINCOLN CARTAXO DE LIRA JÚNIOR CREA 160.814.689-8

CONSTRUÇÃO:


FOLHA **04/08**  
PROJETO: CONSTRUÇÃO DE GINÁSIO POLIESPORTIVO  
CONVENIENTE: PREFEITURA MUNICIPAL DE COREMAS - PB  
CONVENIADO: MUNICÍPIO DE COREMAS - PB  
LOCALIDADE: COREMAS - PB

|          | DATA                                             | RESPONSÁVEL     | RUBRICA | DADOS    |
|----------|--------------------------------------------------|-----------------|---------|----------|
| DESENHO  | AGO/2025                                         | LINCOLN CARTAXO |         |          |
| CÓPIA    |                                                  |                 |         |          |
| VISTO    |                                                  |                 |         |          |
| ESCALAS  | DESENHOS                                         |                 |         | CONVÊNIO |
| Indicada | Planta Baixa - Acabamentos e Esquadrias          |                 |         |          |
|          | Detalhe 01 - Esquadrias                          |                 |         |          |
|          | Detalhe 02 - Revestimento Cerâmico               |                 |         |          |
|          | Detalhe 03 - Piso Industrial de Alta Resistência |                 |         | ARQUIVO  |


Aprovações:

**LCL PROJETOS**

Av. Gov. Flávio Ribeiro Coutinho, 500, sl. 601  
Jardim Oceania, 58037-005 - João Pessoa (PB)  
Tel +55 (83) 99924.4447  
e-mail: contato@lclprojetos.com

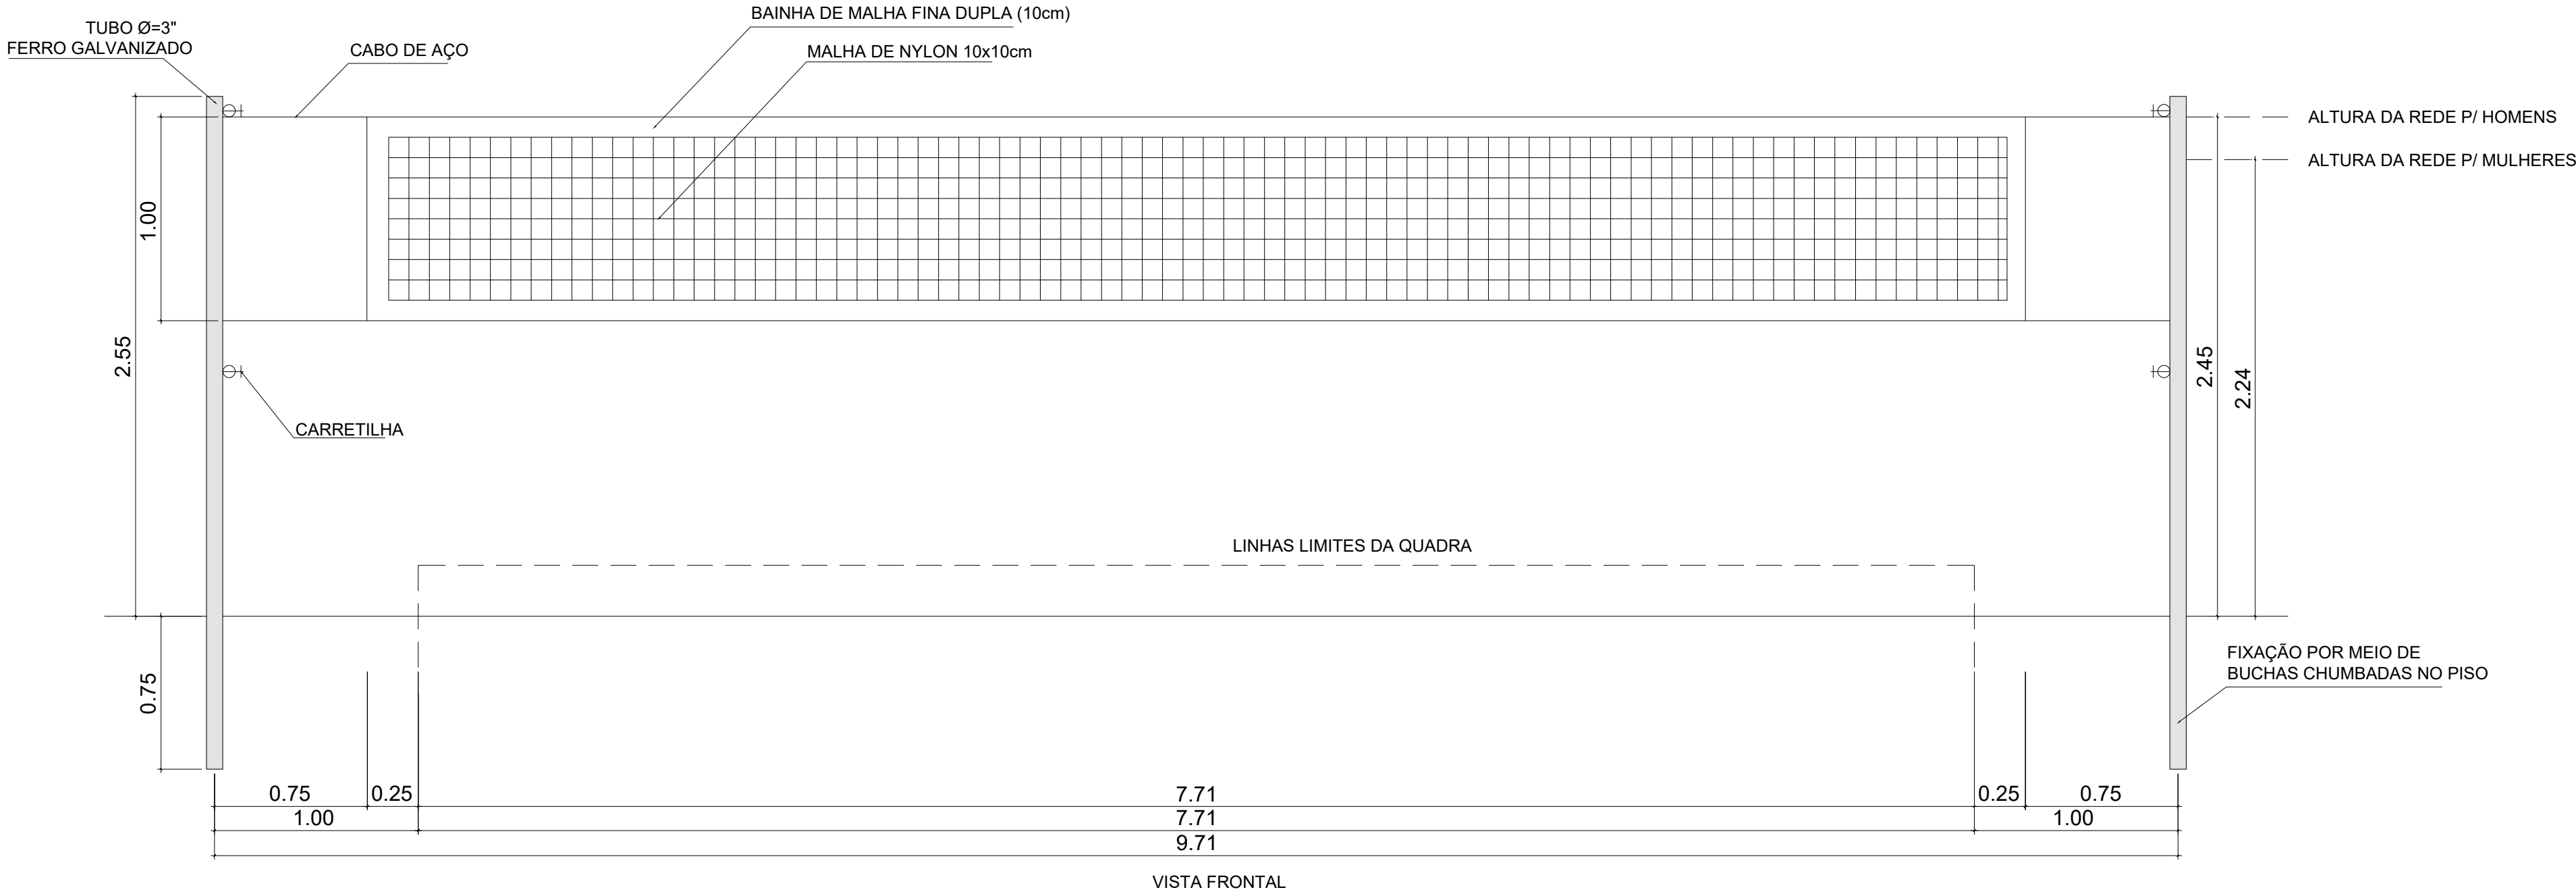

Detalhe 01 - Rede de Vôlei  
ESC.: 1:25

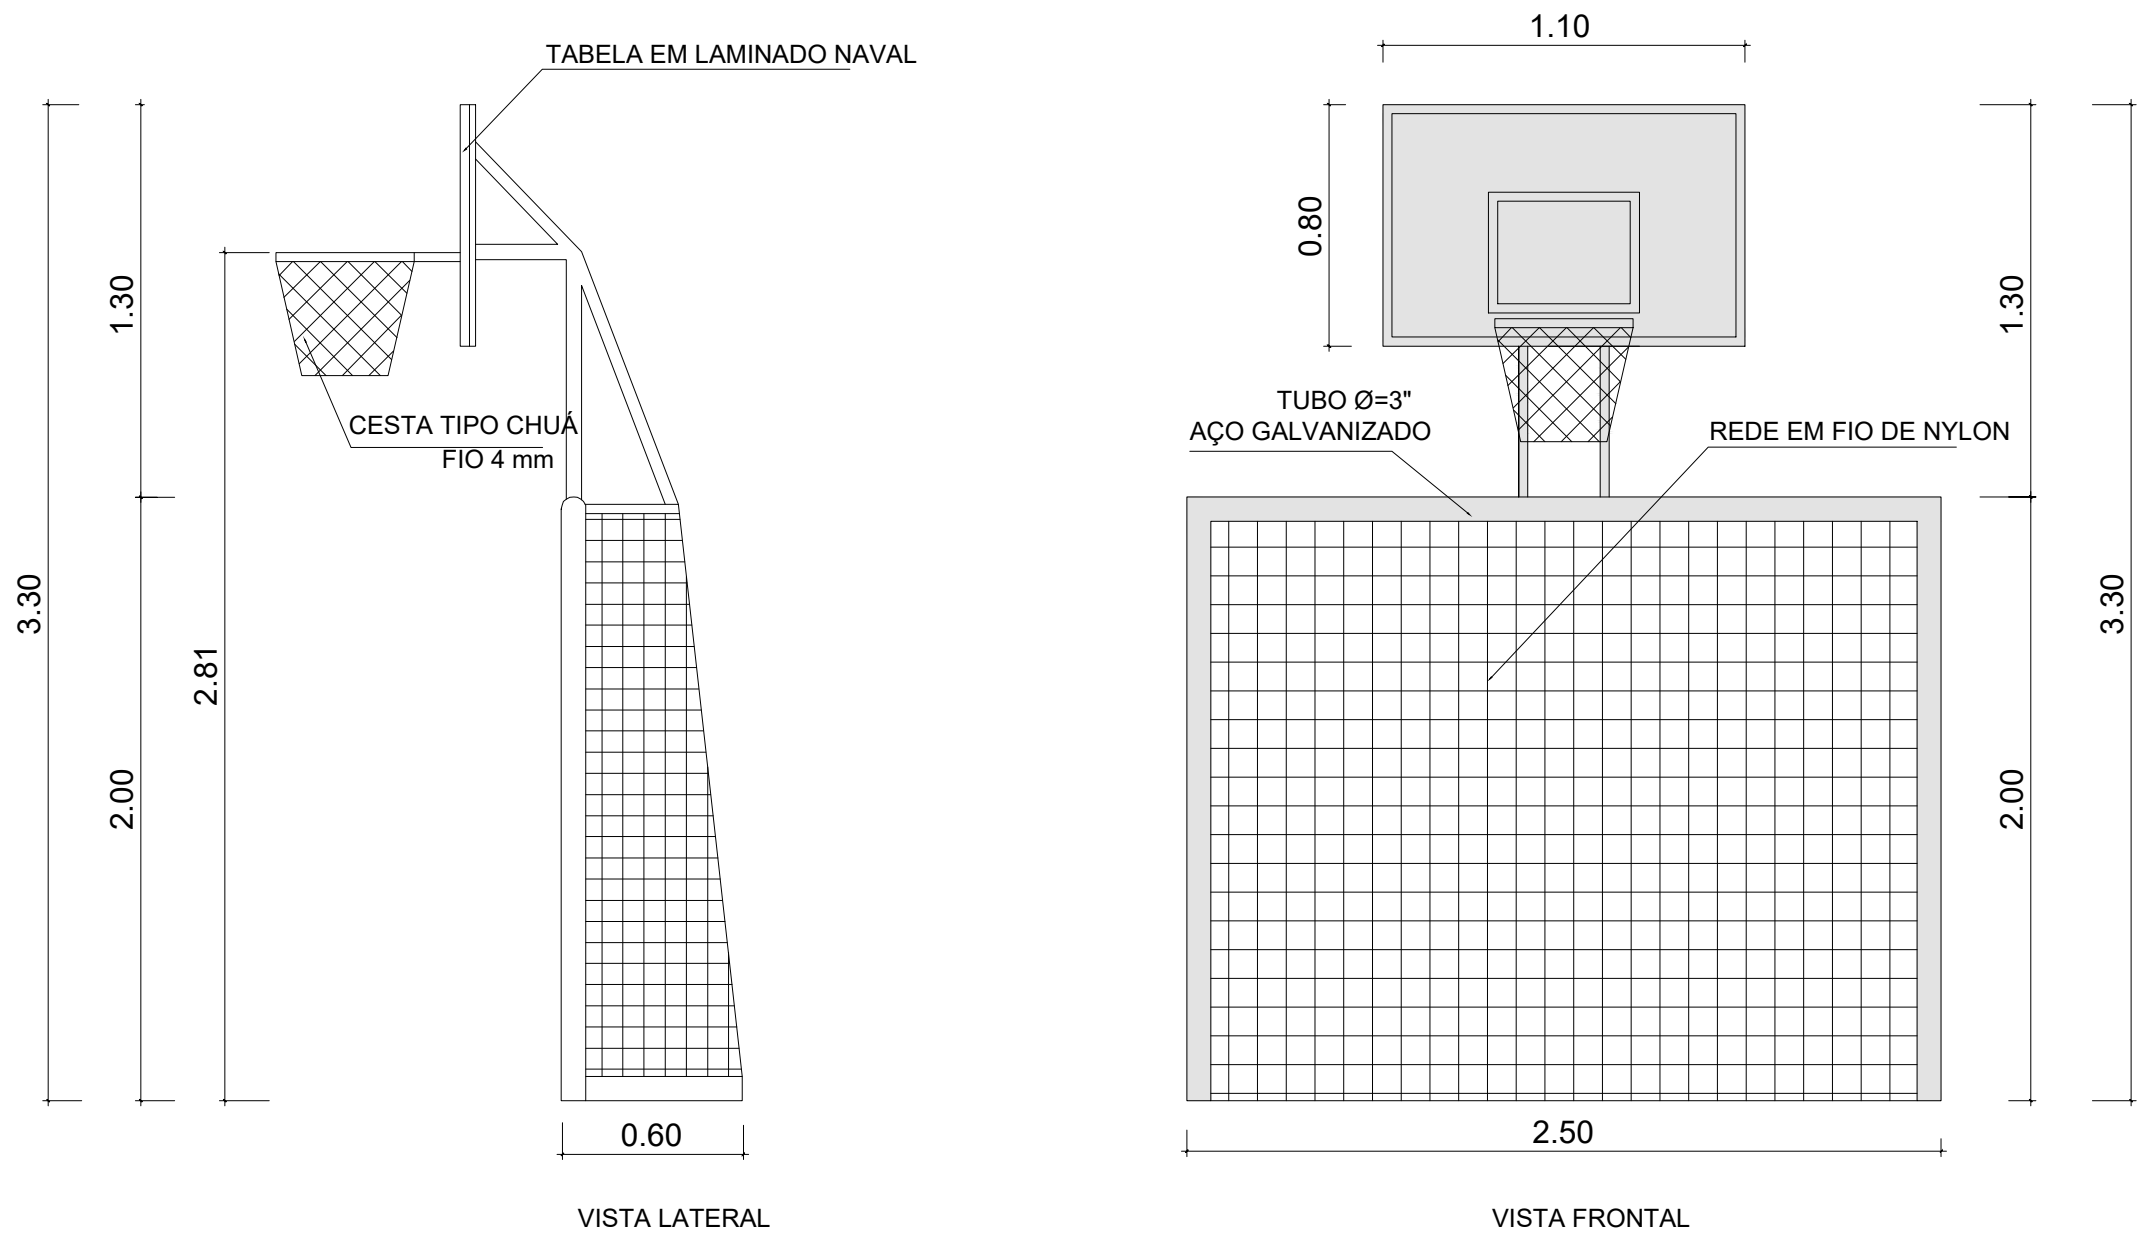

Detalhe 02 - Trave de Futebol conjugada com Tabela de Basquete  
ESC.: 1:25




PROPRIETÁRIO: PREFEITURA MUNICIPAL DE COREMAS - PB  
**LINCOLN CARTAXO DE LIRA JÚNIOR:06897861405**  
PROJETO: LINCOLN CARTAXO DE LIRA JÚNIOR CREA 160.814.689-8

CONSTRUÇÃO:

|          |                                                                                              |                 |         |          |
|----------|----------------------------------------------------------------------------------------------|-----------------|---------|----------|
| FOLHA    | PROJETO: CONSTRUÇÃO DE GINÁSIO POLIESPORTIVO                                                 |                 |         |          |
|          | CONVENIENTE: PREFEITURA MUNICIPAL DE COREMAS - PB                                            |                 |         |          |
|          | CONVENIADO: MUNICÍPIO DE COREMAS - PB                                                        |                 |         |          |
|          | LOCALIDADE: COREMAS - PB                                                                     |                 |         |          |
|          | DATA                                                                                         | RESPONSÁVEL     | RUBRICA | DADOS    |
| DESENHO  | AGO/2025                                                                                     | LINCOLN CARTAXO |         |          |
| CÓPIA    |                                                                                              |                 |         |          |
| VISTO    |                                                                                              |                 |         |          |
| ESCALAS  | DESENHOS                                                                                     |                 |         | CONVÊNIO |
| Indicada | Detalhe 01 - Rede de Vôlei<br>Detalhe 02 - Trave de Futebol conjugada com Tabela de Basquete |                 |         | ARQUIVO  |


Aprovações:



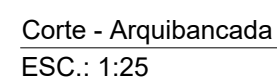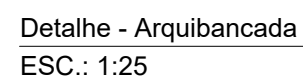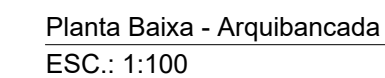


CONSTRUÇÃO:

Aprovações:

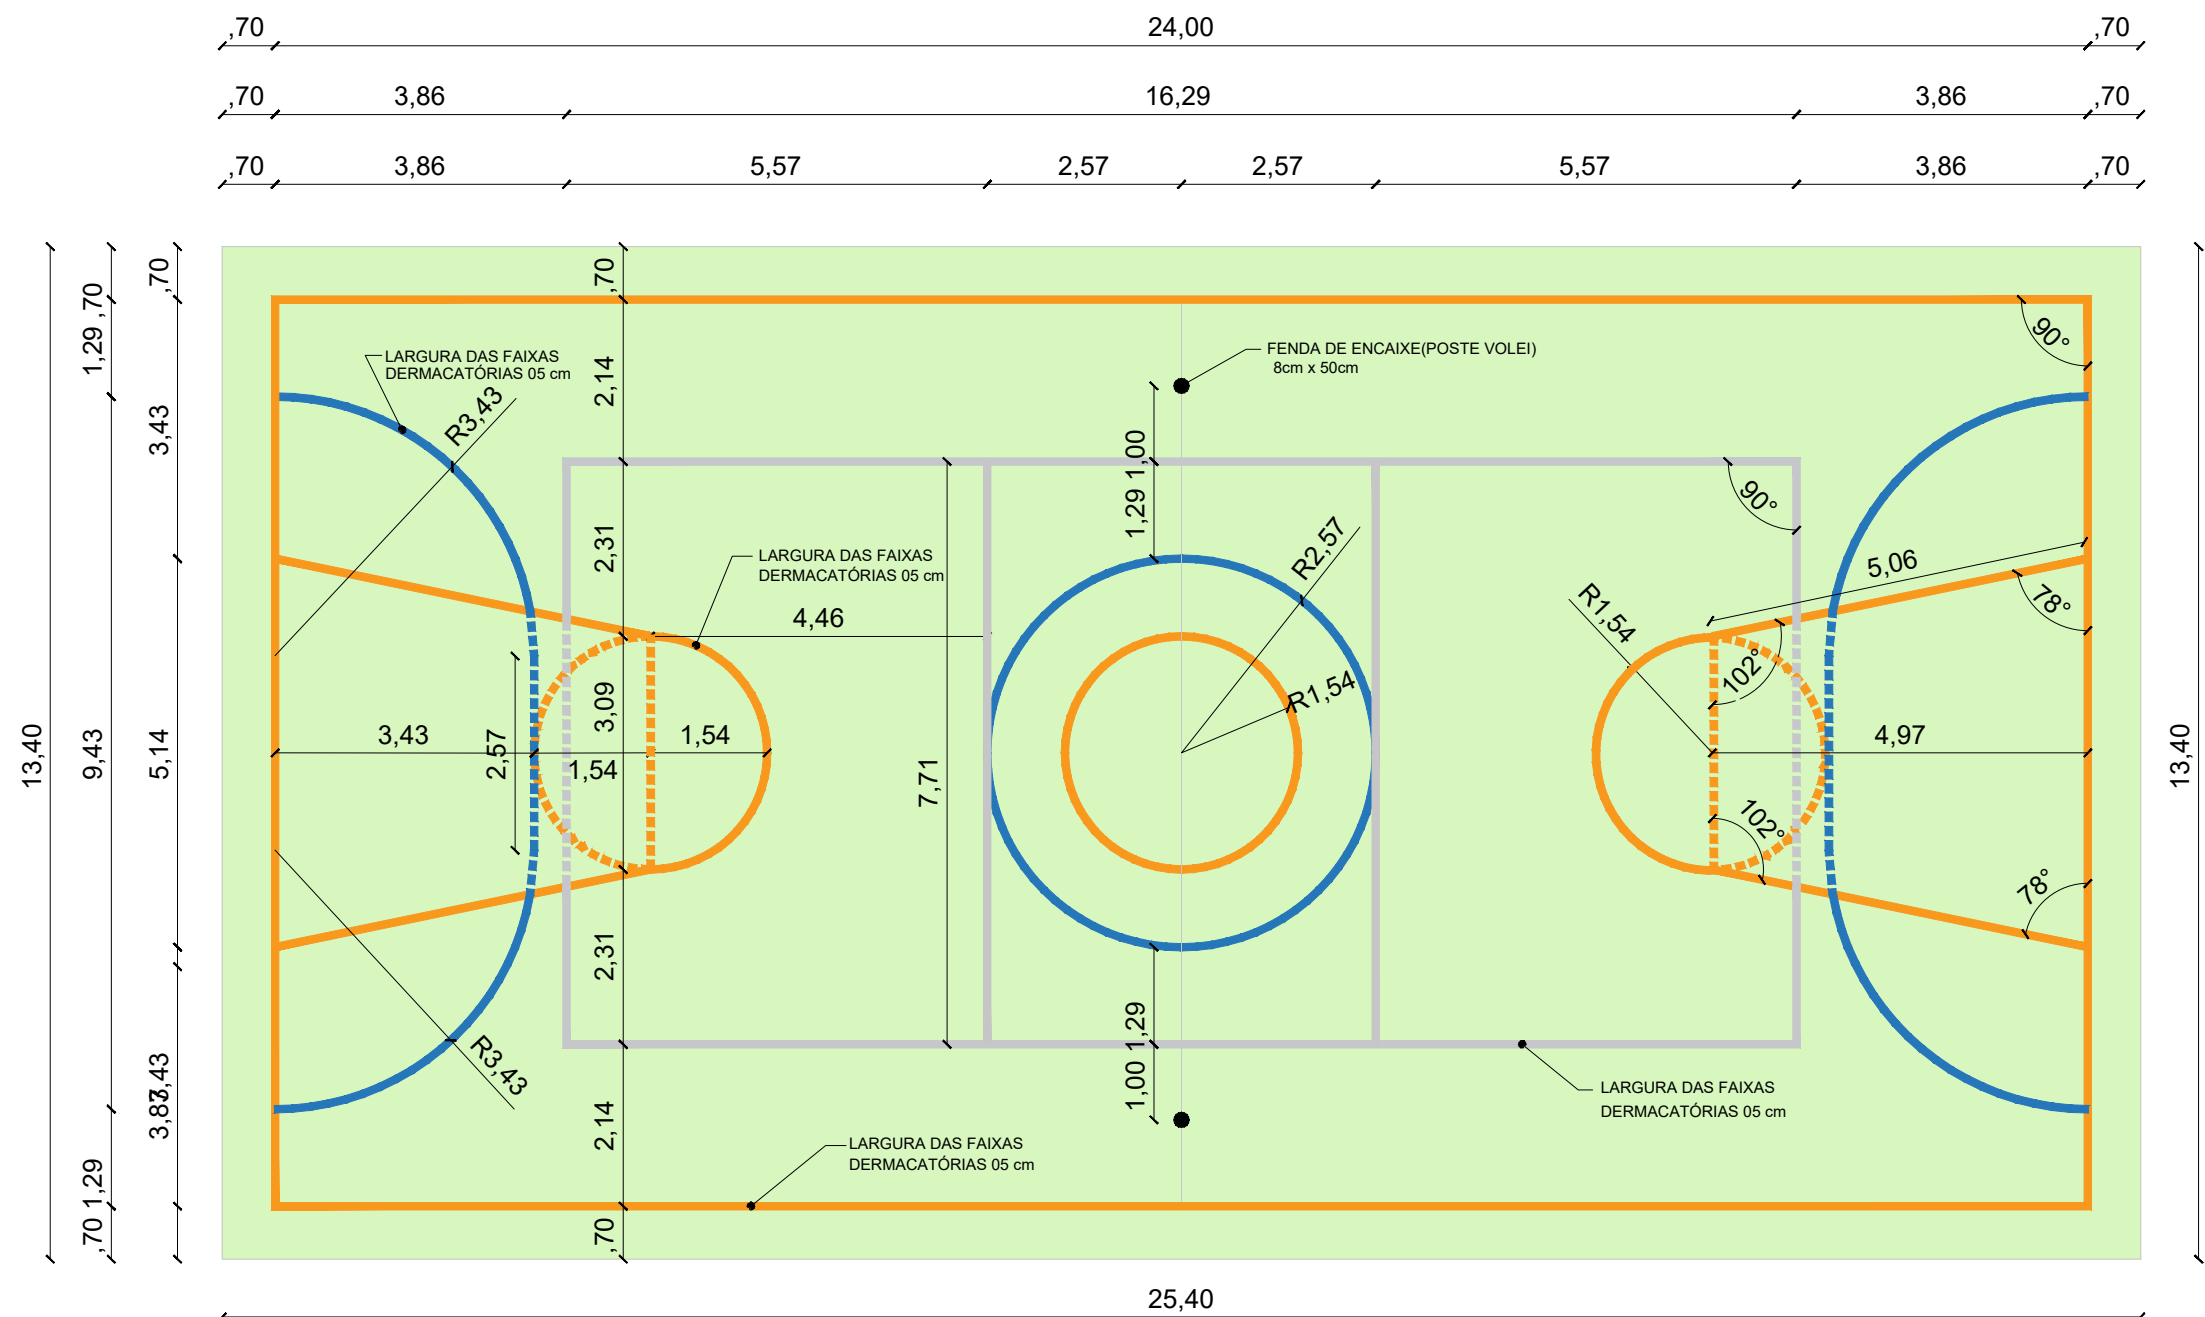


PINTURA DO PISO DA QUADRA - FAIXAS  
ESC.: 1:100

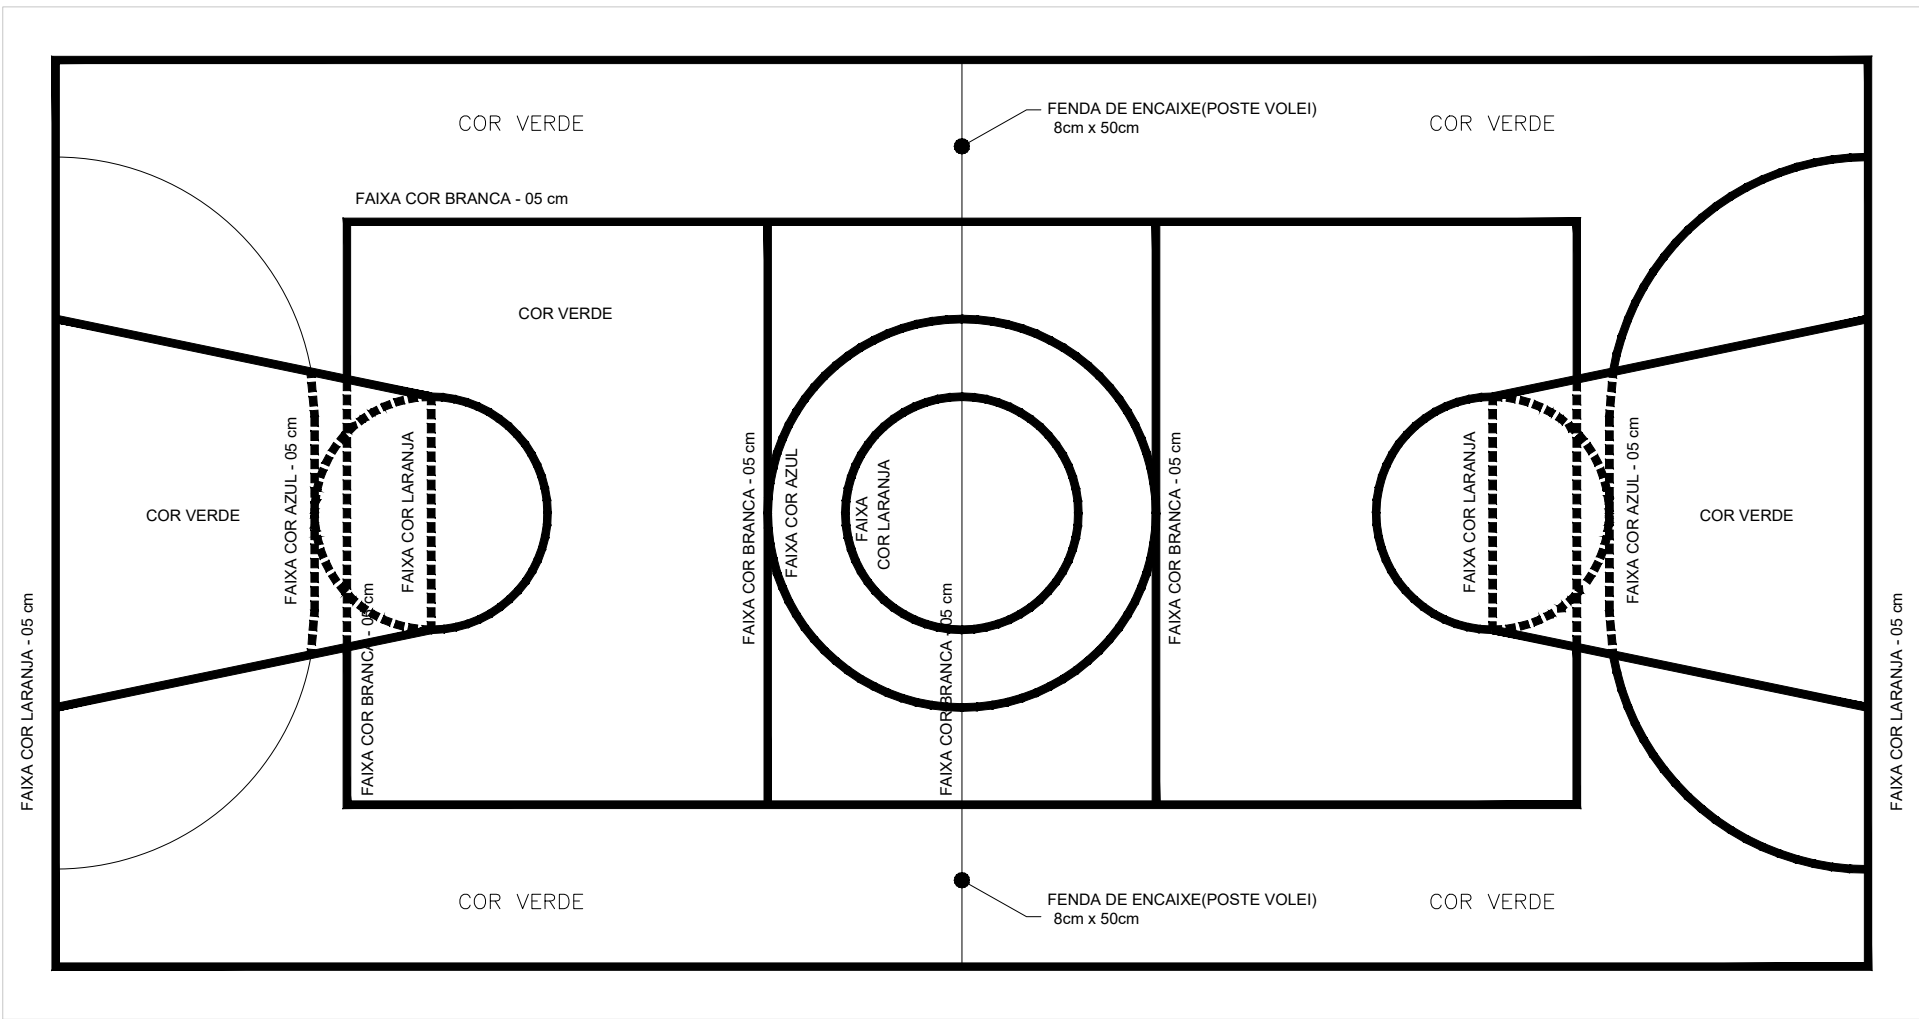

OBS.:PINTURA COM TINTA A BASE DE EPÓXI PARA PISO

PINTURA DO PISO DA QUADRA - ÁREA INTERNA: 340,36M²  
ESC.: 1:100

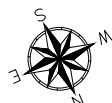

PROPRIETÁRIO: PREFEITURA MUNICIPAL DE COREMAS - PB  
**LINCOLN CARTAXO DE LIRA JUNIOR:06897861405**  
Assinado de forma digital por LINCOLN CARTAXO DE LIRA JUNIOR:06897861405  
Dados: 2025.08.08 12:13:12 -03'00'  
PROJETO: LINCOLN CARTAXO DE LIRA JÚNIOR CREA 160.814.689-8

CONSTRUÇÃO:


|          |          |                                                    |         |          |
|----------|----------|----------------------------------------------------|---------|----------|
| FOLHA    |          | PROJETO: CONSTRUÇÃO DE GINÁSIO POLIESPORTIVO       |         |          |
| 07/08    |          | CONVENIENTE: PREFEITURA MUNICIPAL DE COREMAS - PB  |         |          |
|          |          | CONVENIADO: MUNICÍPIO DE COREMAS - PB              |         |          |
|          |          | LOCALIDADE: COREMAS - PB                           |         |          |
|          | DATA     | RESPONSÁVEL                                        | RUBRICA | DADOS    |
| DESENHO  | AGO/2025 | LINCOLN CARTAXO                                    |         |          |
| CÓPIA    |          |                                                    |         |          |
| VISTO    |          |                                                    |         |          |
| ESCALAS  |          | DESENHOS                                           |         | CONVÊNIO |
| Indicada |          | Pintura do Piso da Quadra - Faixas                 |         | ARQUIVO  |
|          |          | Pintura do Piso da Quadra - Área Interna: 340,36m² |         |          |

Aprovações:


**LCL PROJETOS**

Av. Gov. Flávio Ribeiro Coutinho, 500, sl. 601  
Jardim Oceania, 58037-005 - João Pessoa (PB)  
Tel +55 (83) 99924.4447  
e-mail: contato@lclprojetos.com




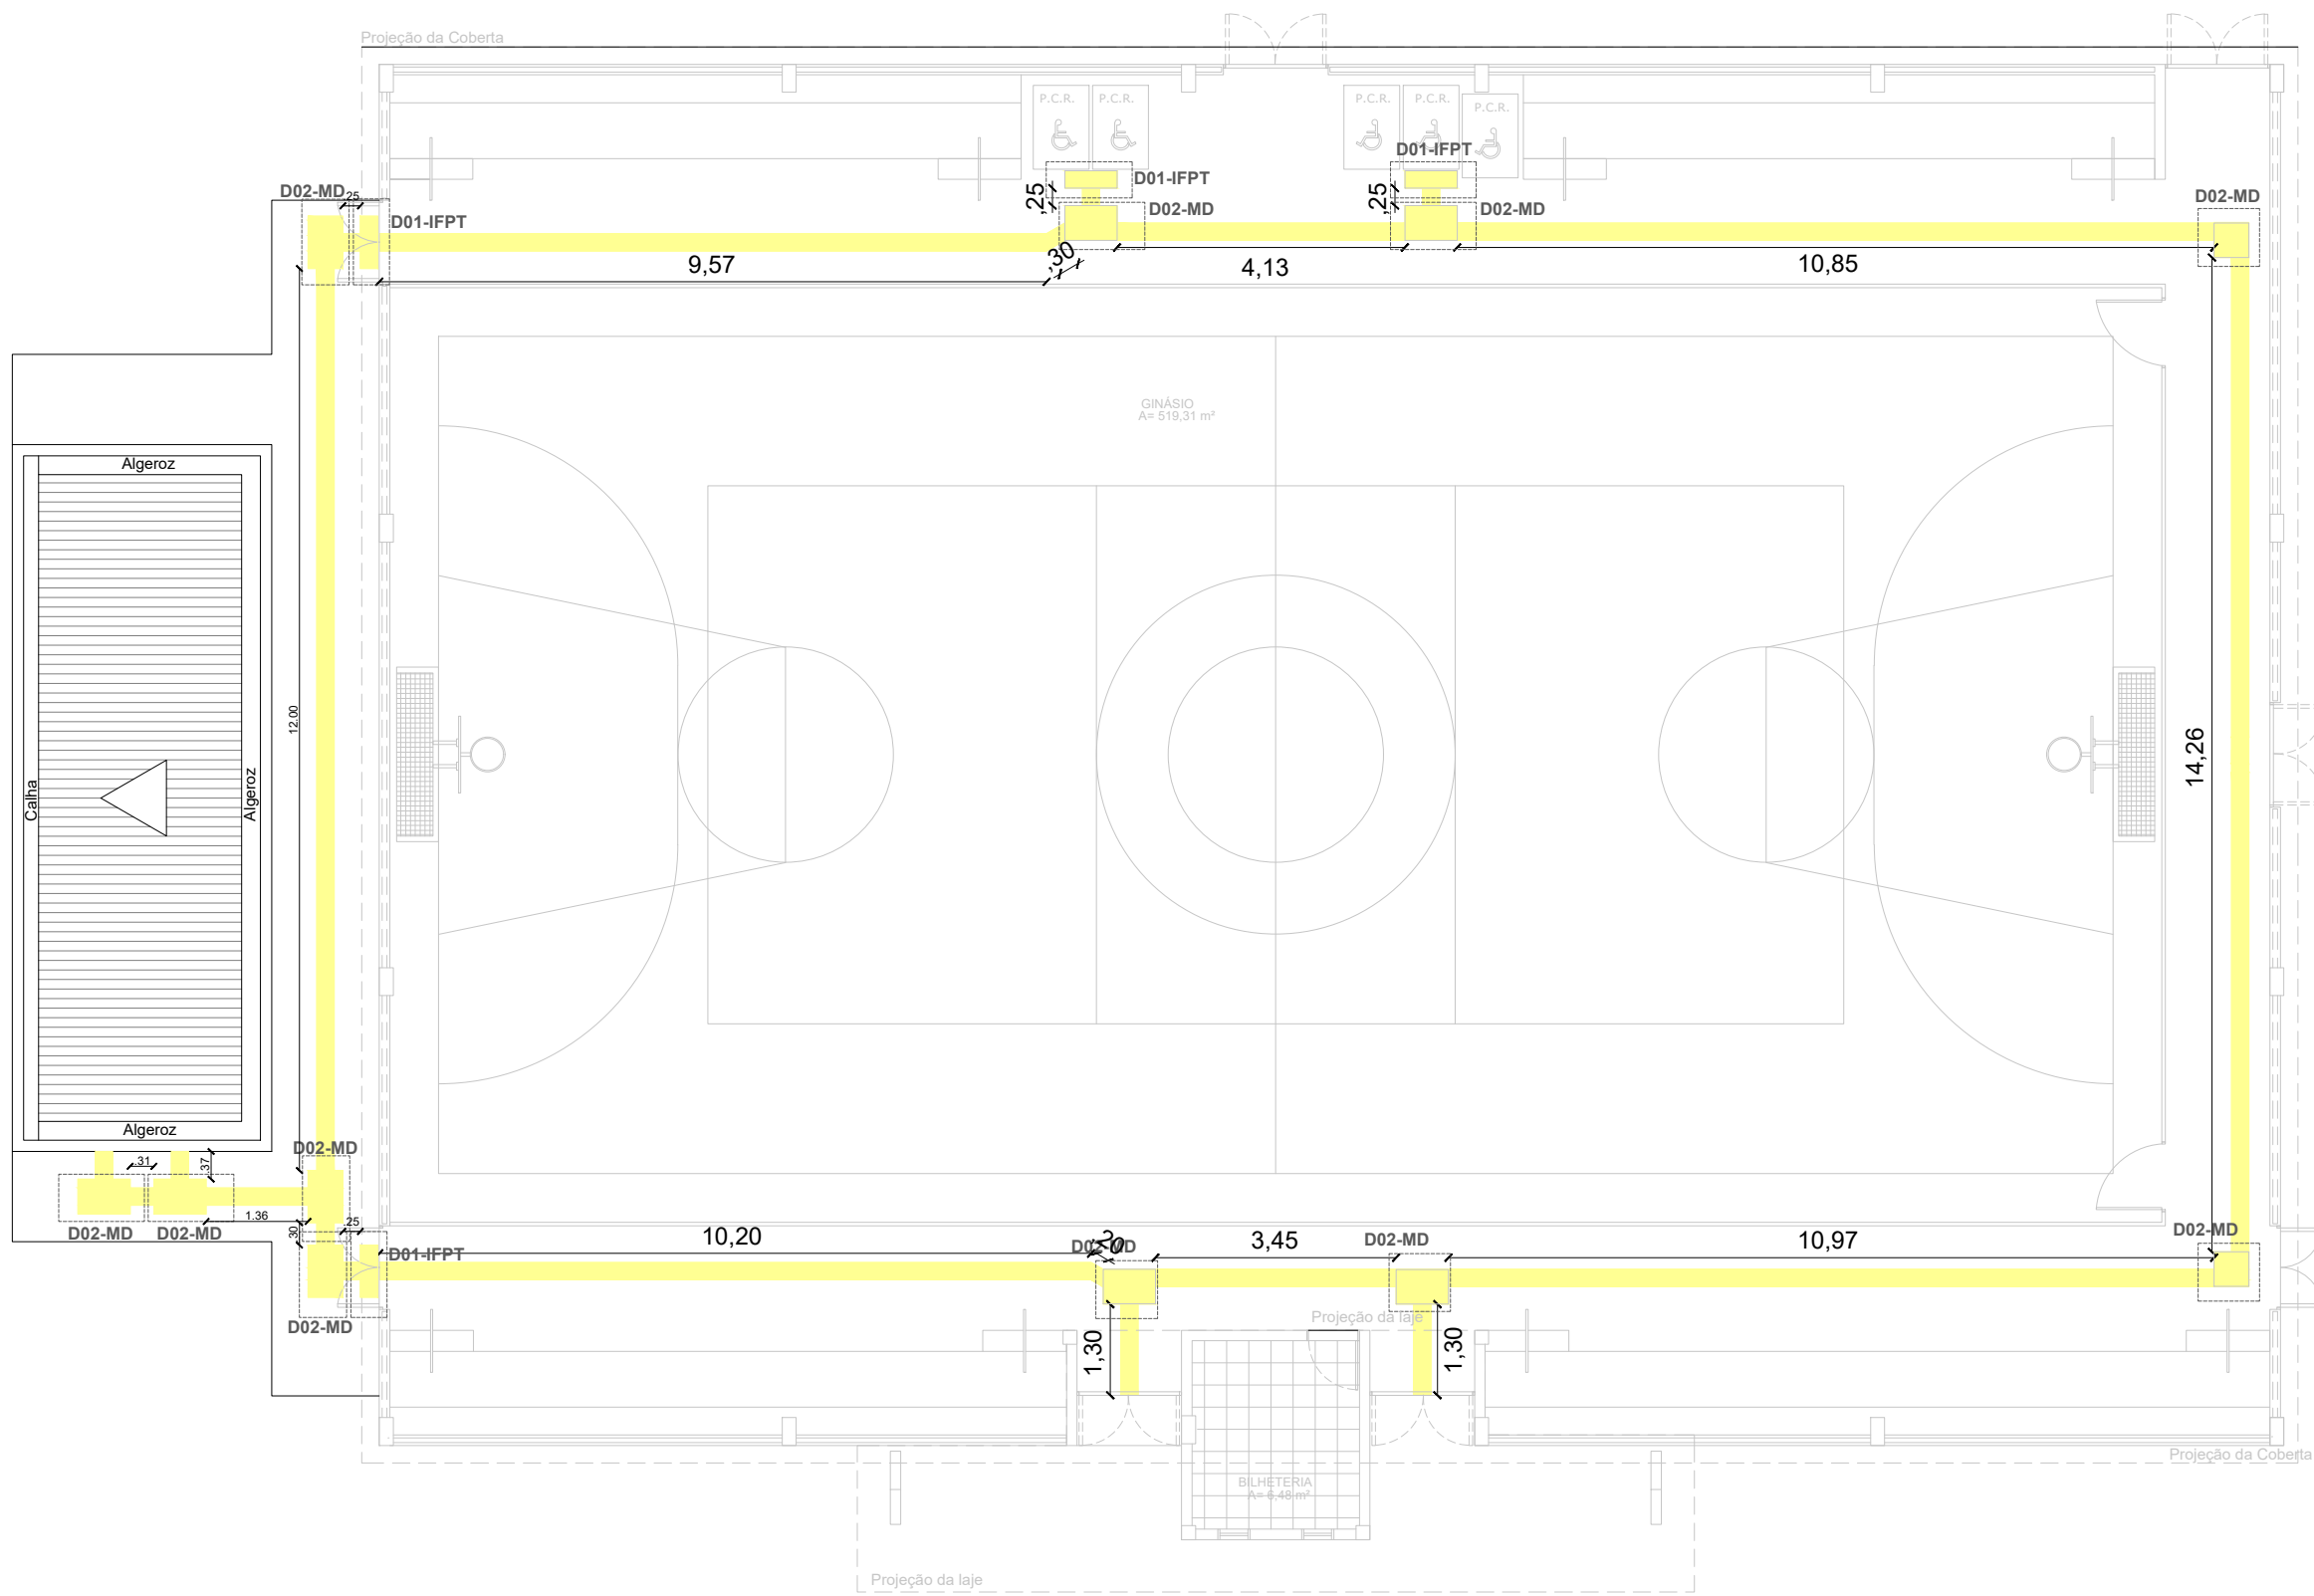


Planta Baixa - Acessibilidade  
escala 1/100

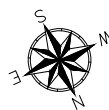


| LEGENDA |                                         |            |
|---------|-----------------------------------------|------------|
| GINÁSIO |                                         |            |
|         | Piso Tátil Direcional                   | 19,93 - m² |
|         | Piso Tátil de Alerta Mudança de Direção | 0,50 - m²  |
|         | Piso Tátil de Alerta em Início e Fim    | 1,50 - m²  |
|         |                                         | 2,58 - m²  |

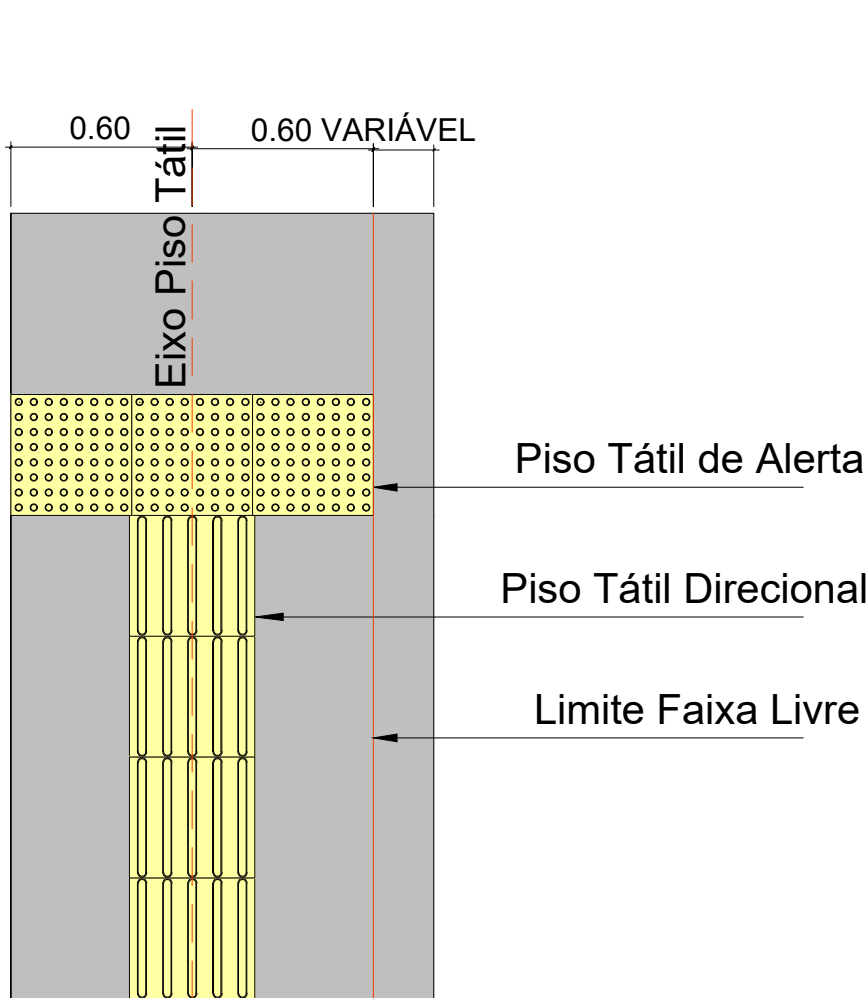

Detalhe 01  
ESC.: 1:25

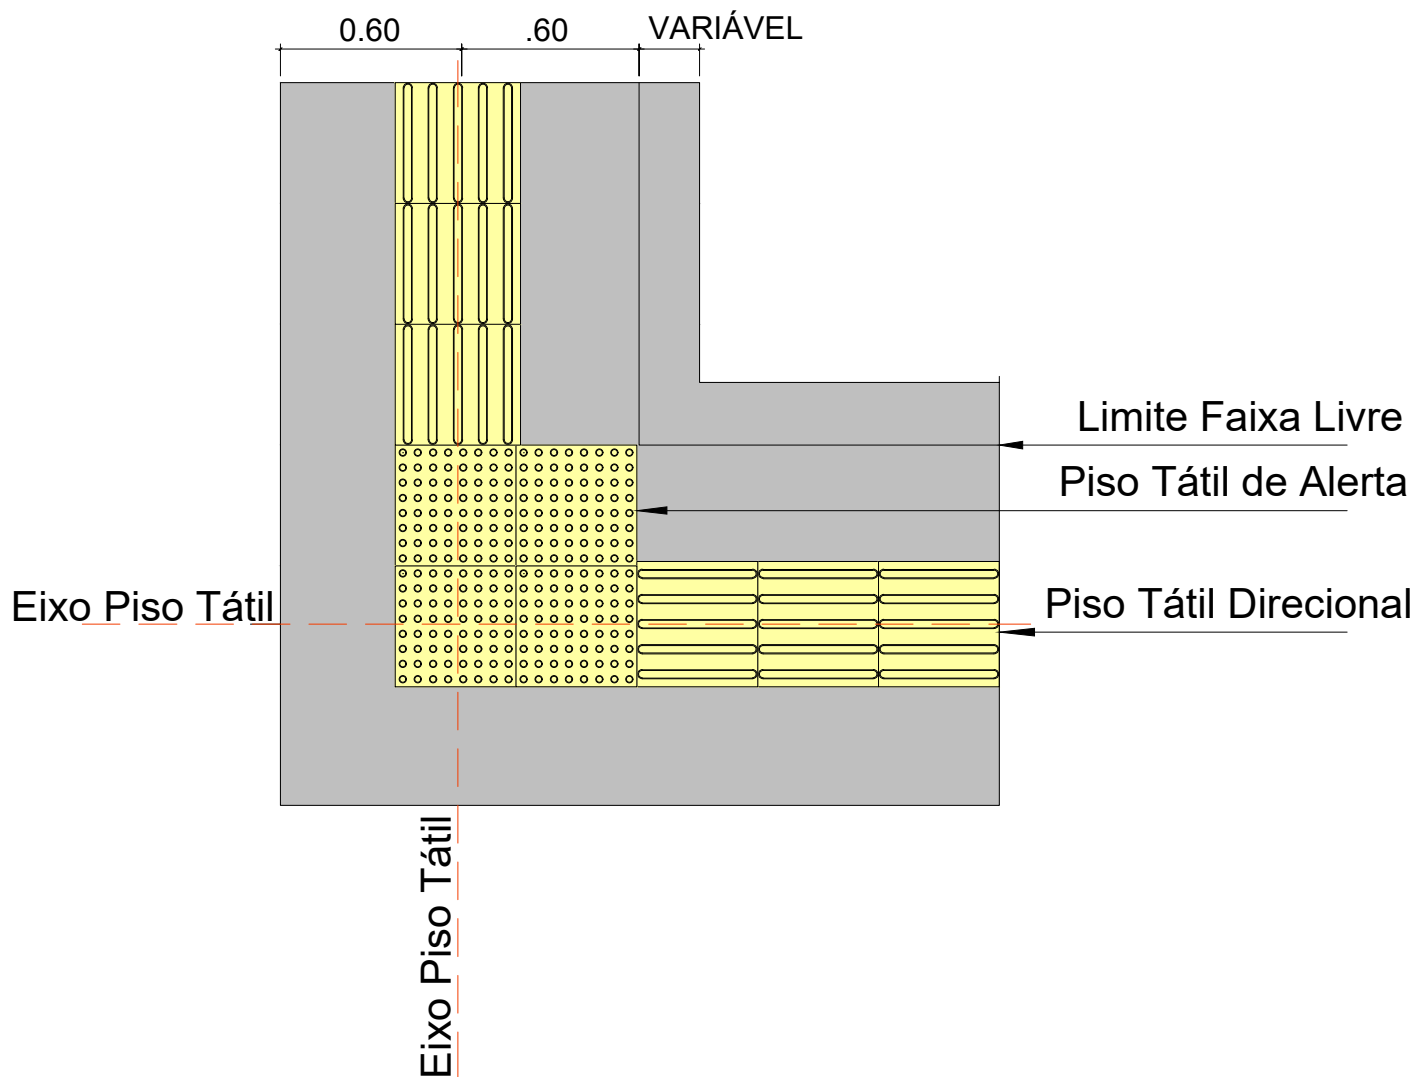

Detalhe 02  
ESC.: 1:25

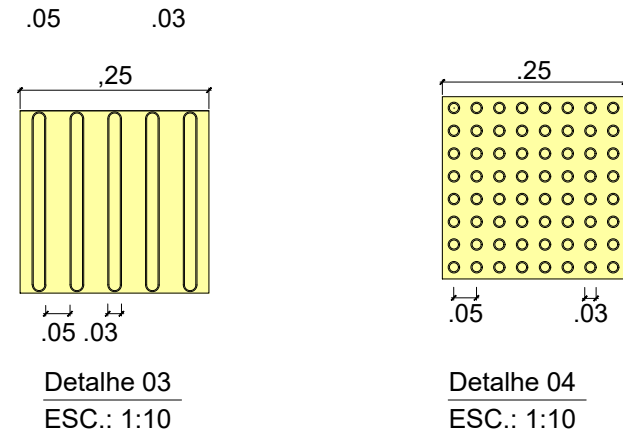

PROPRIETÁRIO: PREFEITURA MUNICIPAL DE COREMAS - PB  
**LINCOLN CARTAXO DE LIRA JUNIOR:06897861405** Assinado de forma digital por LINCOLN CARTAXO DE LIRA JUNIOR:06897861405  
PROJETO: LINCOLN CARTAXO DE LIRA JÚNIOR CREA 160.814.689-8

CONSTRUÇÃO:

|                       |                                                                                 |                                      |         |          |
|-----------------------|---------------------------------------------------------------------------------|--------------------------------------|---------|----------|
| FOLHA<br><b>08/08</b> | PROJETO:                                                                        | CONSTRUÇÃO DE GINÁSIO POLIESPORTIVO  |         |          |
|                       | CONVENIENTE:                                                                    | PREFEITURA MUNICIPAL DE COREMAS - PB |         |          |
|                       | CONVENIADO:                                                                     | MUNICÍPIO DE COREMAS - PB            |         |          |
|                       | LOCALIDADE:                                                                     | COREMAS - PB                         |         |          |
|                       | DATA                                                                            | RESPONSÁVEL                          | RUBRICA | DADOS    |
| DESENHO               | AGO/2025                                                                        | LINCOLN CARTAXO                      |         |          |
| CÓPIA                 |                                                                                 |                                      |         |          |
| VISTO                 |                                                                                 |                                      |         |          |
| ESCALAS               | DESENHOS                                                                        |                                      |         | CONVÊNIO |
|                       | Indicada<br>Planta Baixa - Acessibilidade<br>Detalhe 01 e 02<br>Detalhe 03 e 04 |                                      |         | ARQUIVO  |

Aprovações:



Av. Gov. Flávio Ribeiro Coutinho, 500, sl. 601  
Jardim Oceania, 58037-005 - João Pessoa (PB)  
Tel +55 (83) 99924.4447  
e-mail: contato@lclprojetos.com