


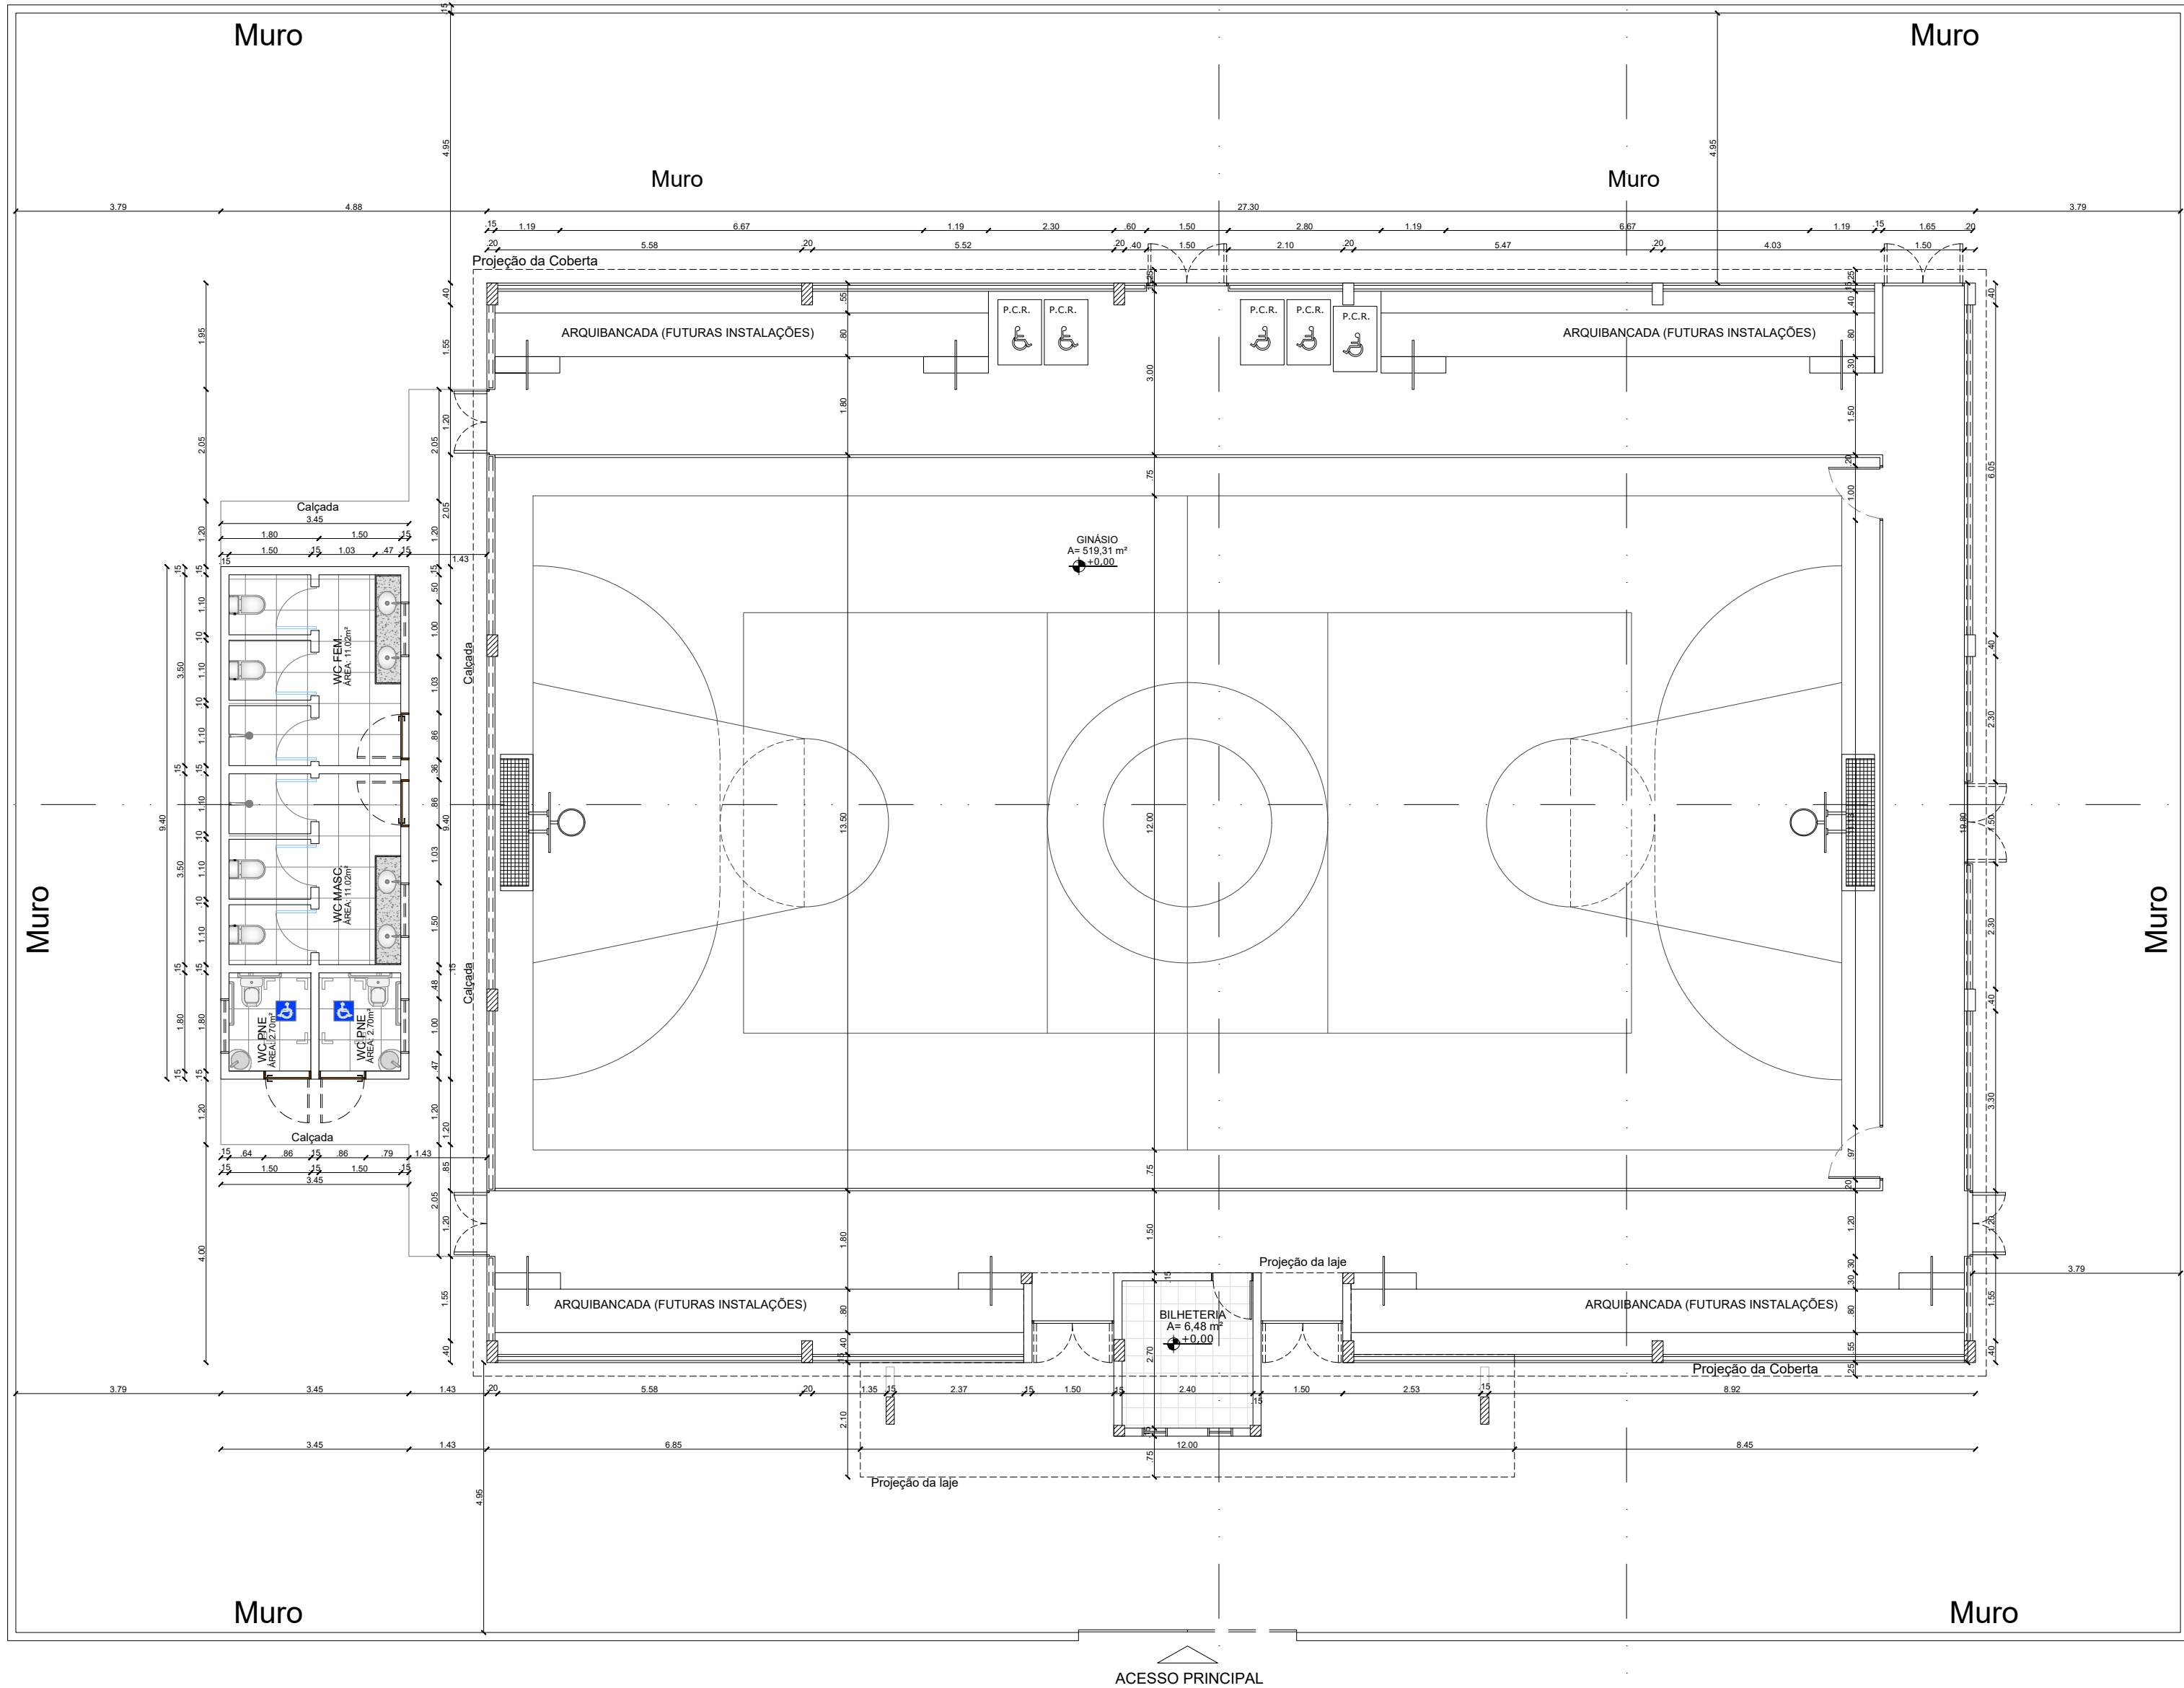

PROPRIETÁRIO: PREFEITURA MUNICIPAL DE COREMAS - PB

**LINCOLN CARTAXO DE LIRA JÚNIOR:06897861405**

PROJETO: LINCOLN CARTAXO DE LIRA JÚNIOR CREA 160.814.689-8

CONSTRUÇÃO:

Assinado de forma digital por LINCOLN CARTAXO DE LIRA JÚNIOR:06897861405

Dados: 2025.08.08 12:14:44 -03'00'

|          |          |                                                   |         |          |
|----------|----------|---------------------------------------------------|---------|----------|
| FOLHA    |          | PROJETO: CONSTRUÇÃO DE GINÁSIO POLIESPORTIVO      |         |          |
| 02/08    |          | CONVENIENTE: PREFEITURA MUNICIPAL DE COREMAS - PB |         |          |
|          |          | CONVENIADO: MUNICÍPIO DE COREMAS - PB             |         |          |
|          |          | LOCALIDADE: COREMAS - PB                          |         |          |
|          | DATA     | RESPONSÁVEL                                       | RUBRICA | DADOS    |
| DESENHO  | AGO/2025 | LINCOLN CARTAXO                                   |         |          |
| CÓPIA    |          |                                                   |         |          |
| VISTO    |          |                                                   |         |          |
| ESCALAS  |          | DESENHOS                                          |         | CONVÊNIO |
| Indicada |          | Planta de Baixa                                   |         |          |
|          |          |                                                   |         | ARQUIVO  |