




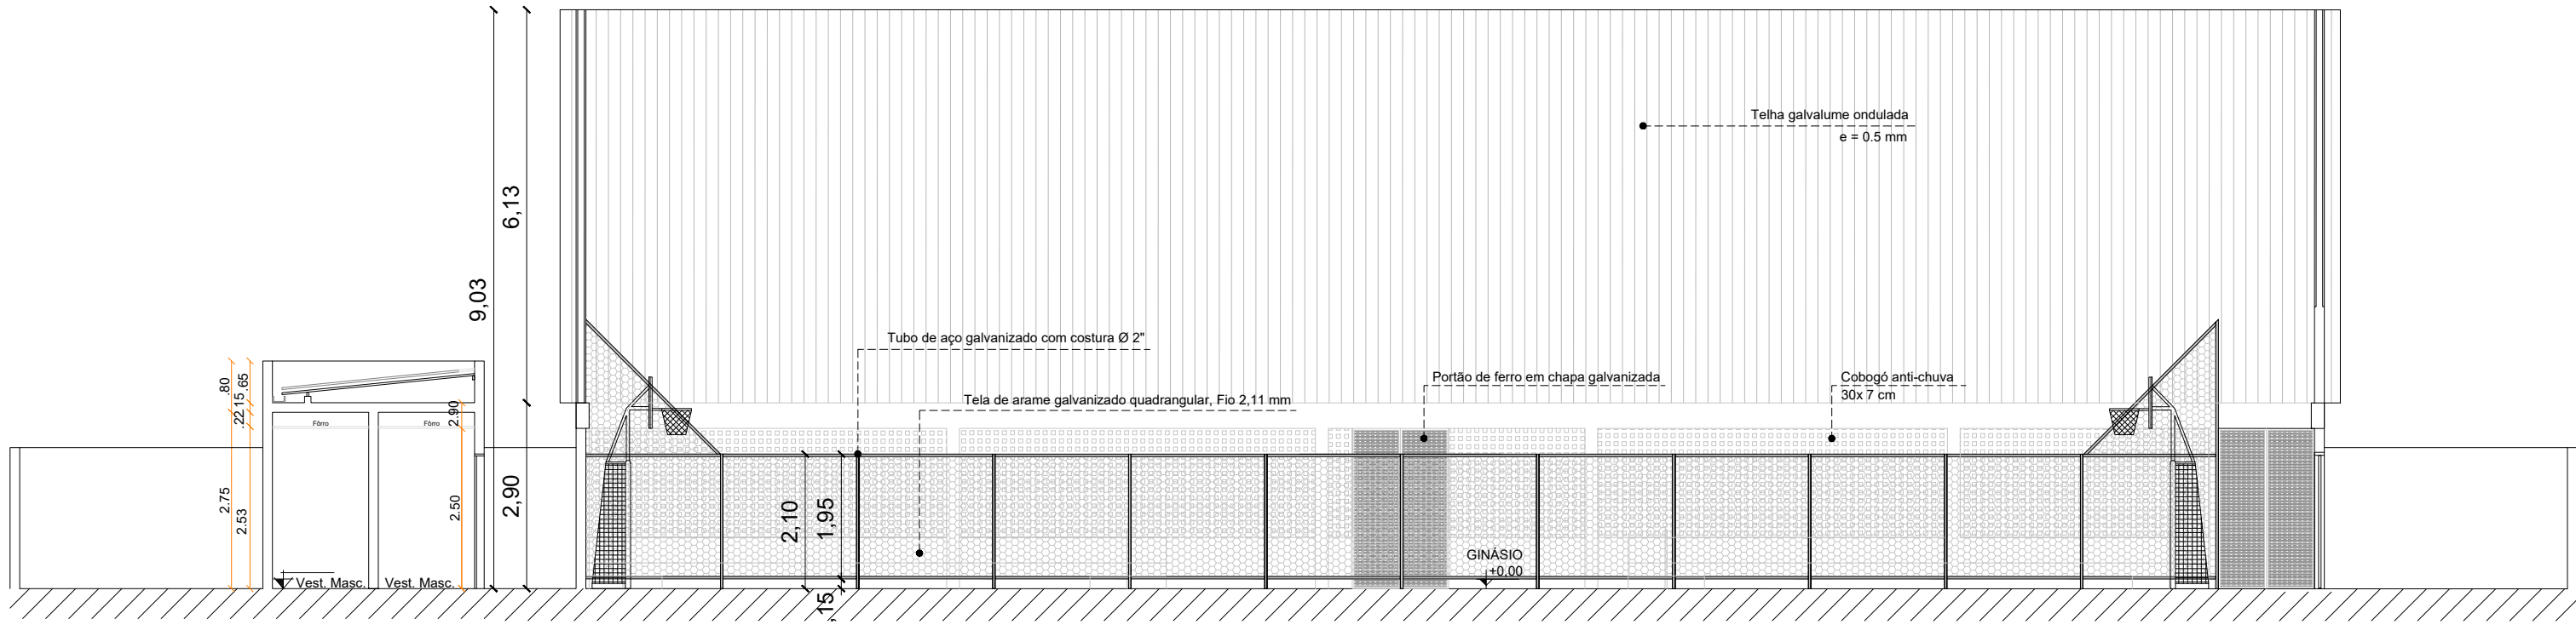

CORTE A-A  
escala 1/100

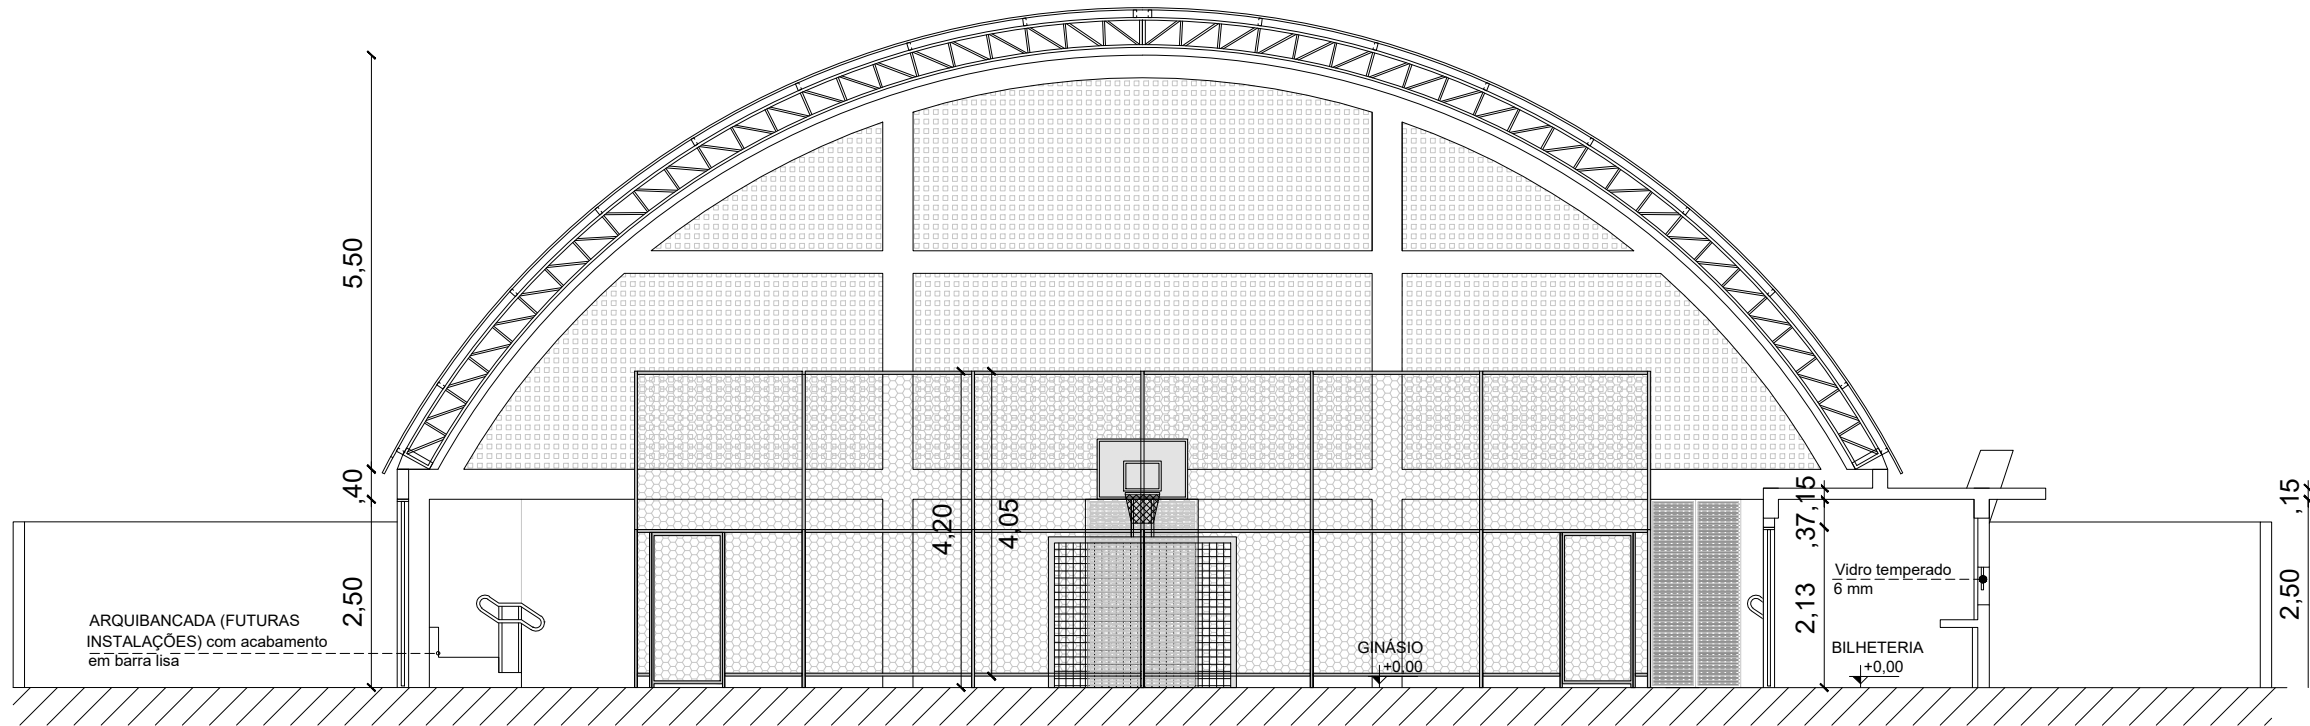

CORTE B-B  
escala 1/100

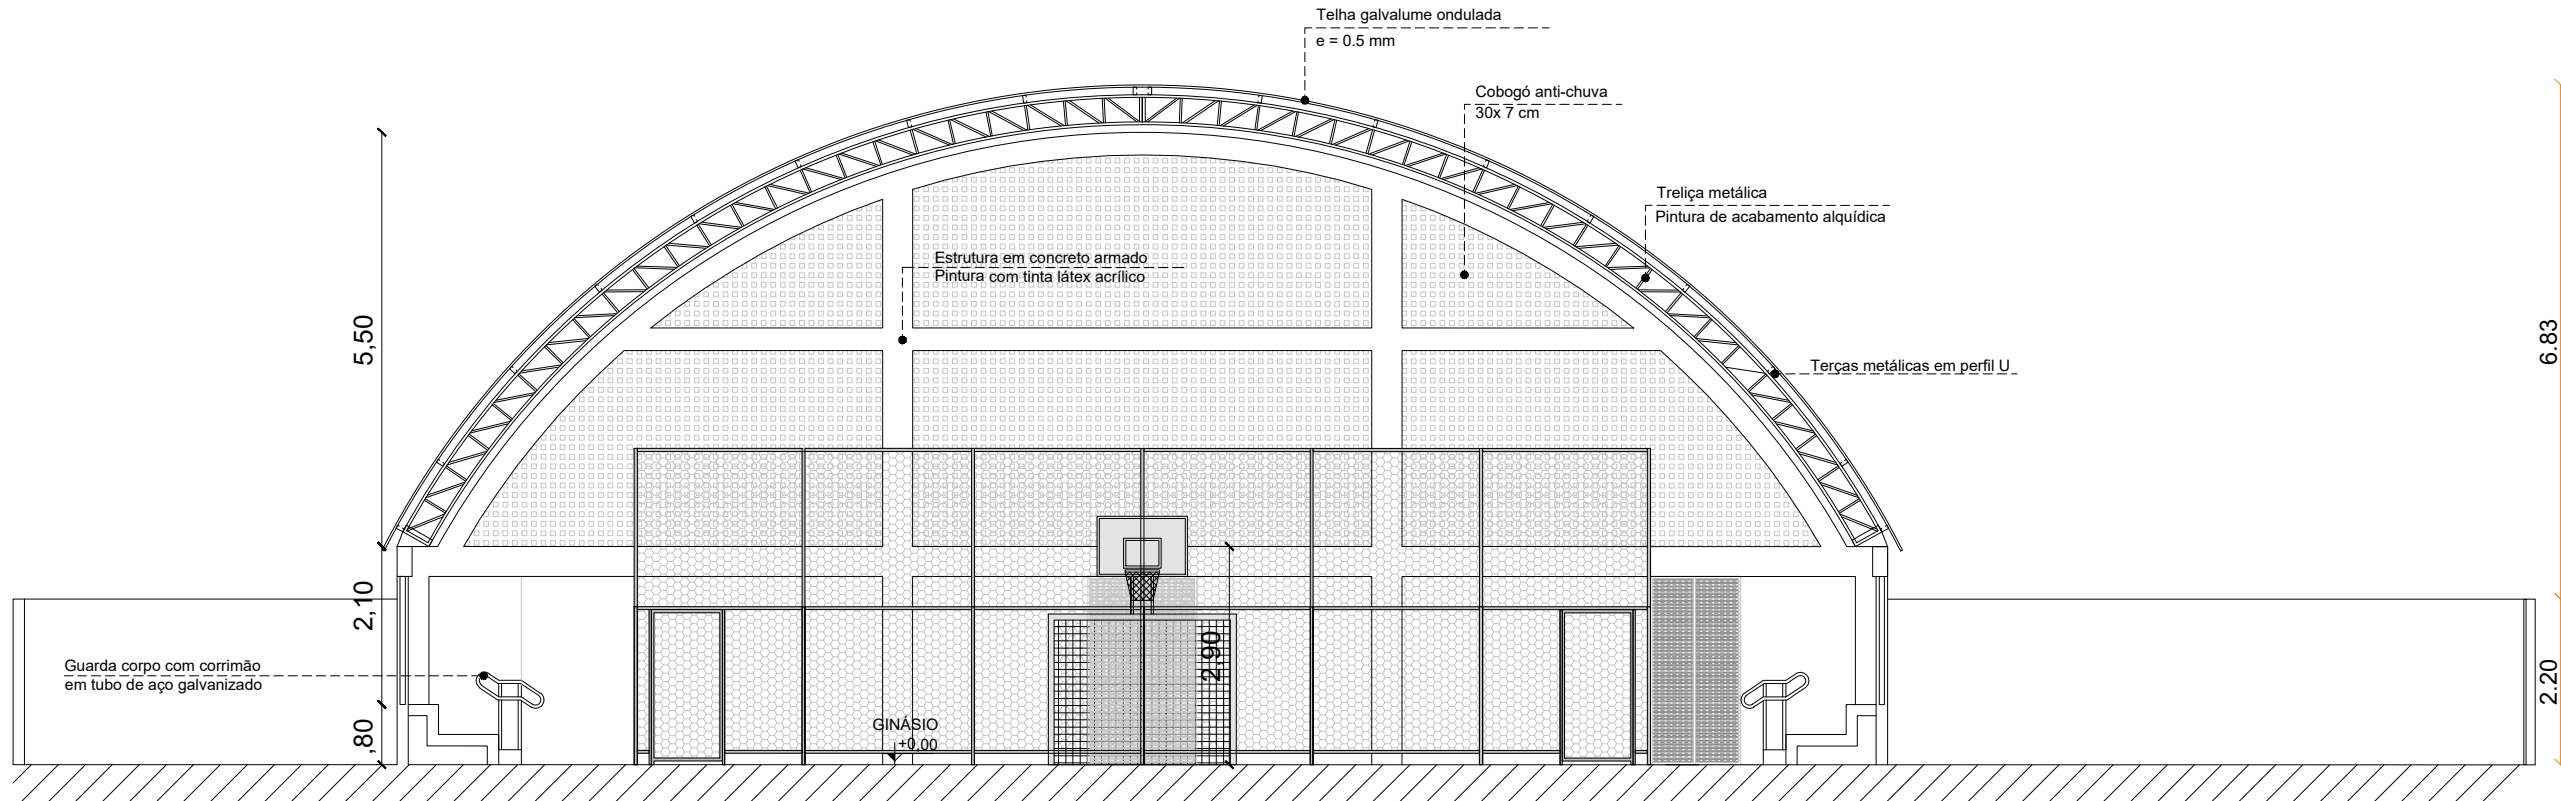

CORTE C-C  
escala 1/100

PROPRIETÁRIO: PREFEITURA MUNICIPAL DE COREMAS - PB

PROJETO: LINCOLN CARTAXO DE LIRA JÚNIOR CREA 160.814.689-8

CONSTRUÇÃO:

FOLHA 03/08  
PROJETO: CONSTRUÇÃO DE GINÁSIO POLIESPORTIVO  
CONVENIENTE: PREFEITURA MUNICIPAL DE COREMAS - PB  
CONVENIADO: MUNICÍPIO DE COREMAS - PB  
LOCALIDADE: COREMAS - PB

|         | DATA     | RESPONSÁVEL     | RUBRICA | DADOS |
|---------|----------|-----------------|---------|-------|
| DESENHO | AGO/2025 | LINCOLN CARTAXO |         |       |
| CÓPIA   |          |                 |         |       |
| VISTO   |          |                 |         |       |

| ESCALAS  | DESENHOS                         | CONVÊNIO |
|----------|----------------------------------|----------|
| Indicada | Corte AA<br>Corte BB<br>Corte CC |          |
|          |                                  | ARQUIVO  |

Aprovações: