


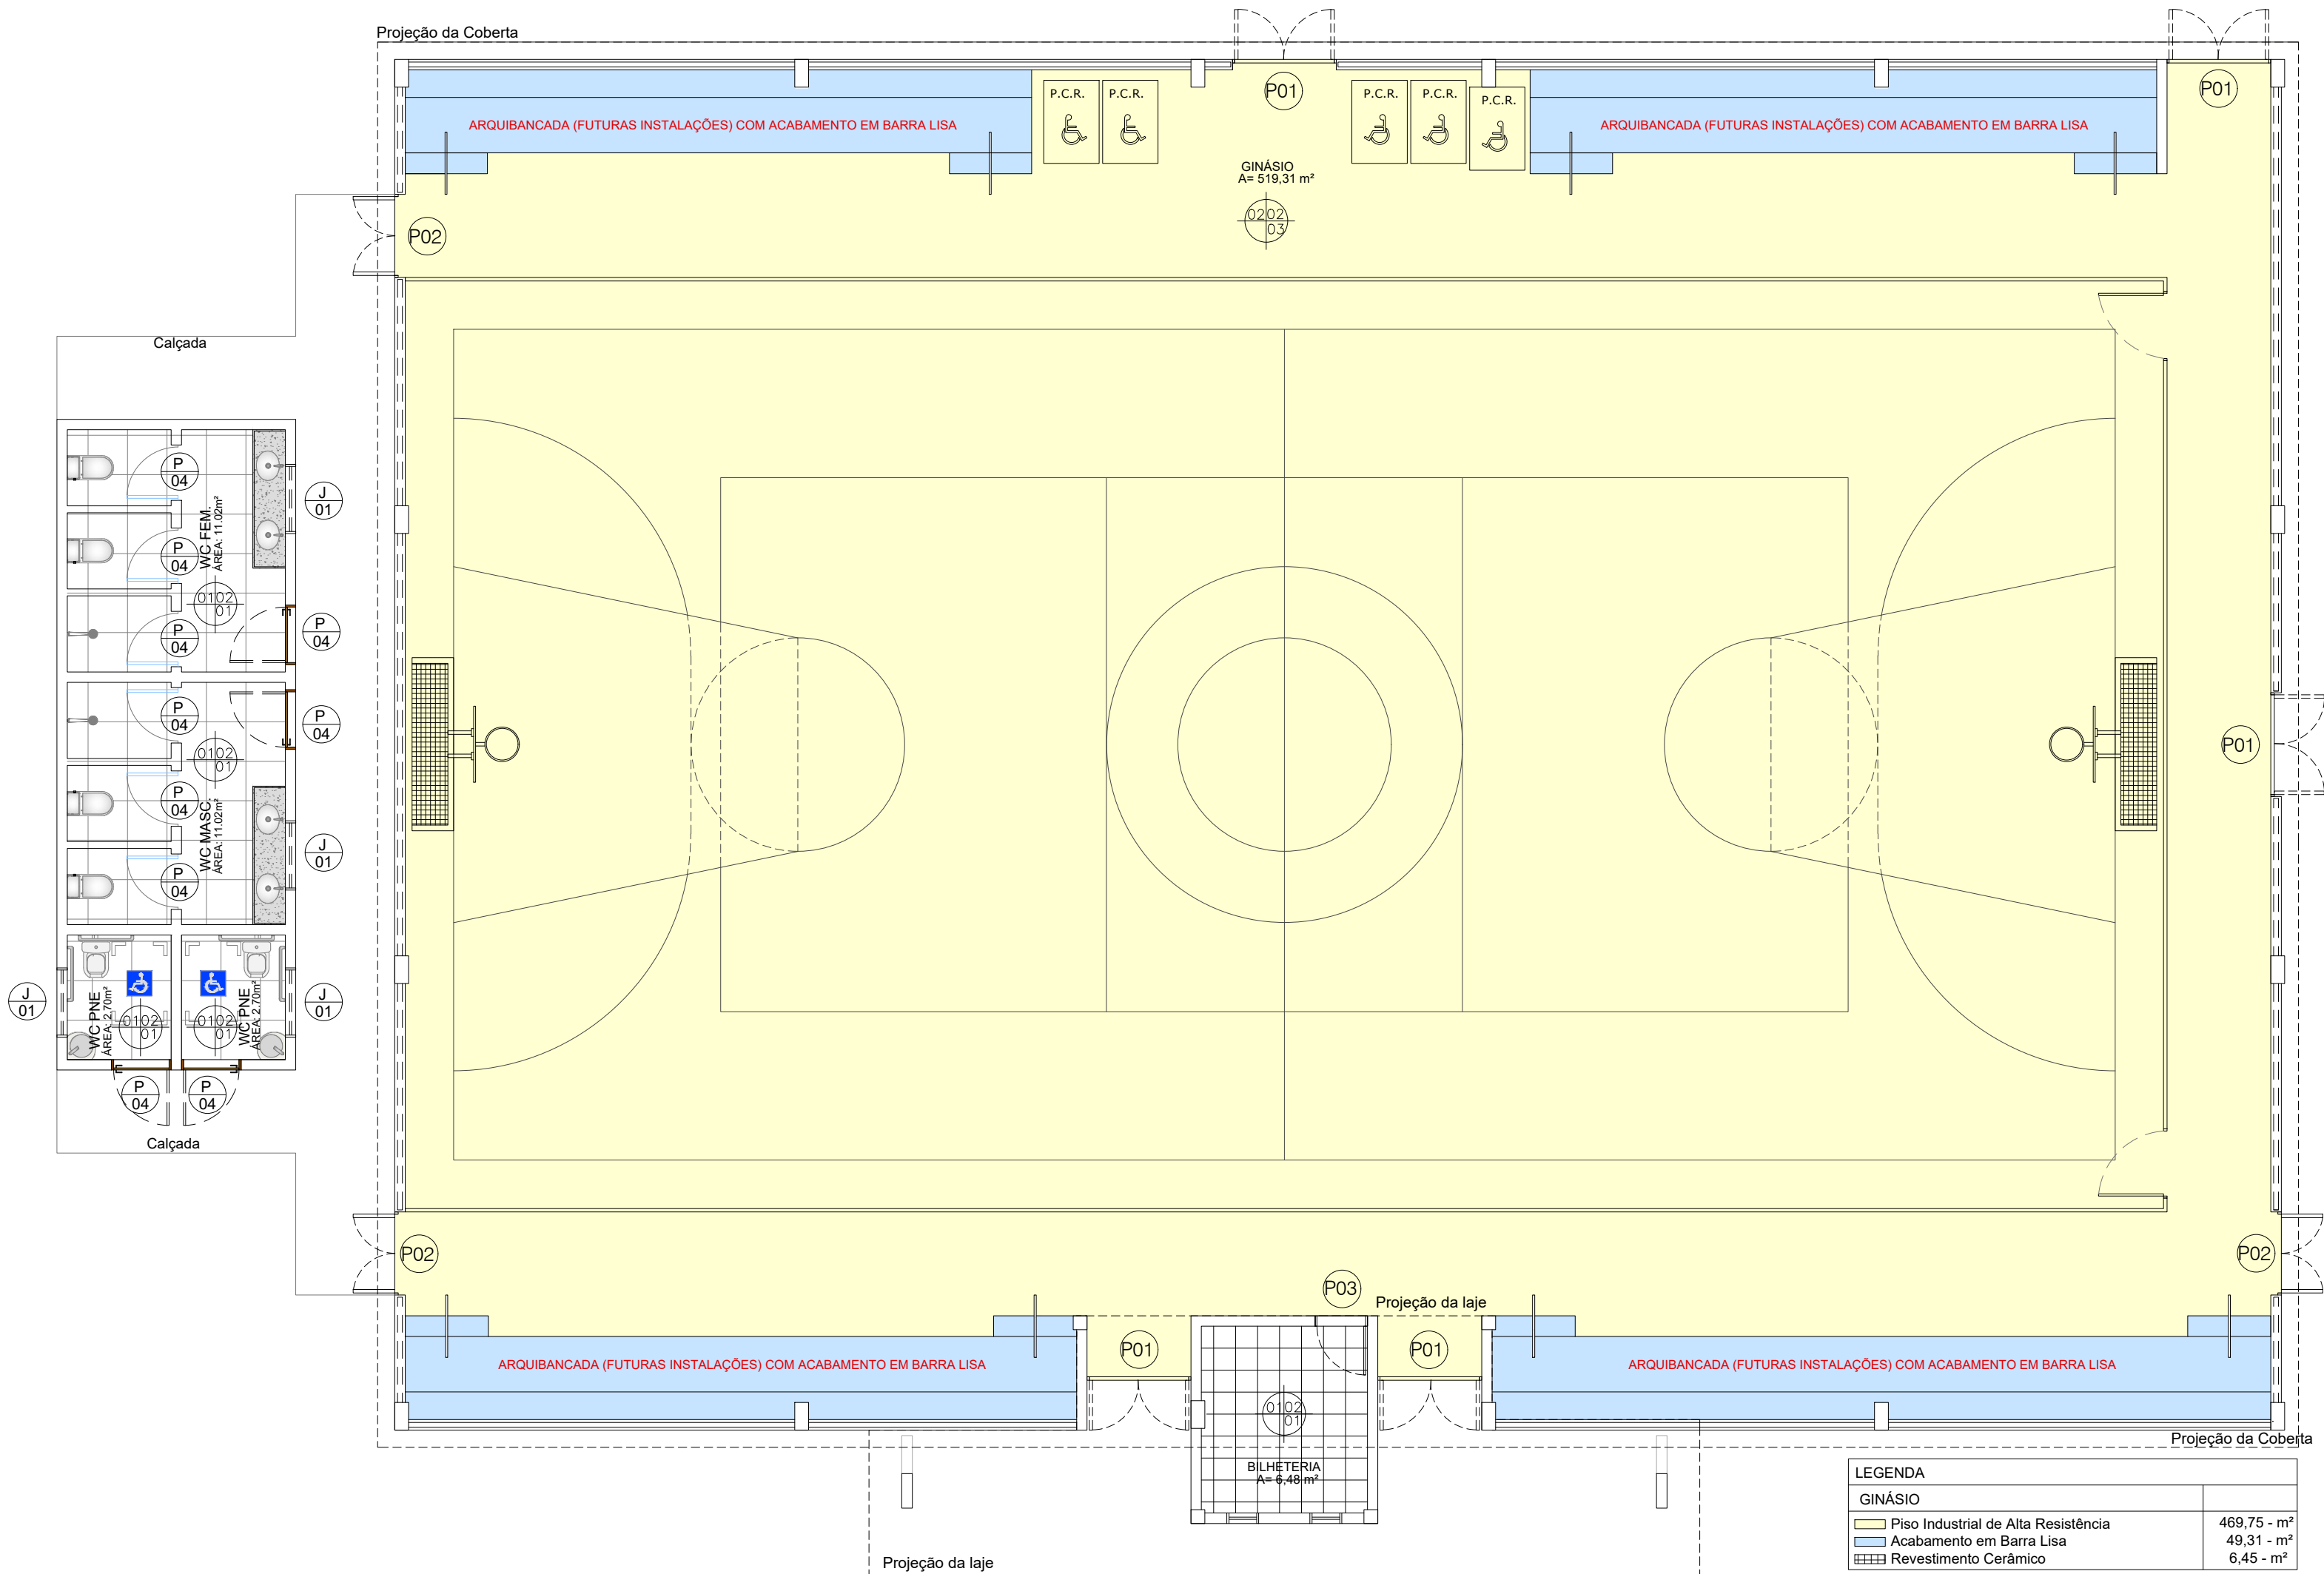


PLANTA BAIXA - ACABAMENTOS E ESQUADRIAS
ESC.: 1:100




LEGENDA	
GINÁSIO	
Piso Industrial de Alta Resistência	469,75 - m²
Acabamento em Barra Lisa	49,31 - m²
Revestimento Cerâmico	6,45 - m²

QUADRO DE ESQUADRIAS					
PORTAS - GINÁSIO					
TIPO	LARGURA	ALTURA	QUANT.	TIPO	ESPECIFICAÇÕES
P01	1.50	2.50	5	ABRIR	PORTÃO DE FERRO EM CHAPA GALVANIZADA
P02	1.20	2.50	3	ABRIR	PORTÃO DE FERRO EM CHAPA GALVANIZADA
P03	0.70	2.13	1	ABRIR	PORTÃO DE ALUMÍNIO
P04	0.80	2.10	10	ABRIR	PORTA DE ALUMÍNIO
JANELAS - GINÁSIO					
TIPO	LARGURA	ALTURA	PEITORIL	QUANT.	TIPO
J01	1.00	0.50	0.60	4	BOCA DE LOBO
			JANELA DE ALUMÍNIO E VIDRO		


QUADRO DE ESPECIFICAÇÕES	
PISO	01 - Piso em revestimento cerâmico com placa tipo grês (35x35 cm) 02 - Piso industrial de alta resistência (e=8mm), com junta de dilatação plástica e pintura epóxi
PAREDE	01 - Revestimento em cerâmica (até h=1,2m), Emassamento e pintura acrílica 02 - Emassamento e Pintura com tinta acrílica
TETO	01 - Forro de gesso em placas sob laje. 02 - Laje pré-moldada, e=12 cm, Fck=12Mpa. 03 - Coberta de estrutura metálica em tesouras ou treliças e cobertura em telha de aço zincado.
OBS.	Todas as Bancadas serão em Granito Cinza, e=2,5mm

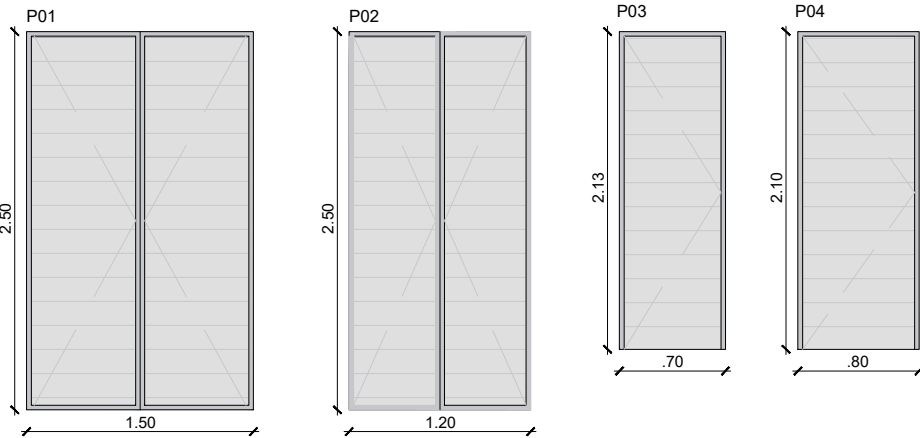

DETALHE 01 - ESQUADRIAS
ESC.: 1:50

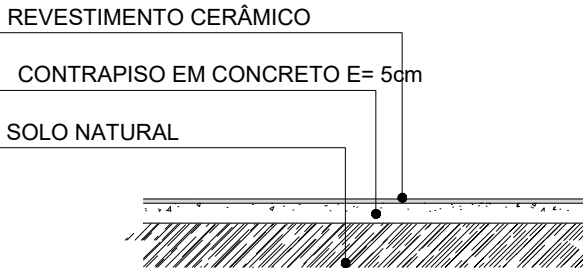

DETALHE 02 - REVESTIMENTO CERÂMICO
ESC.: S/E

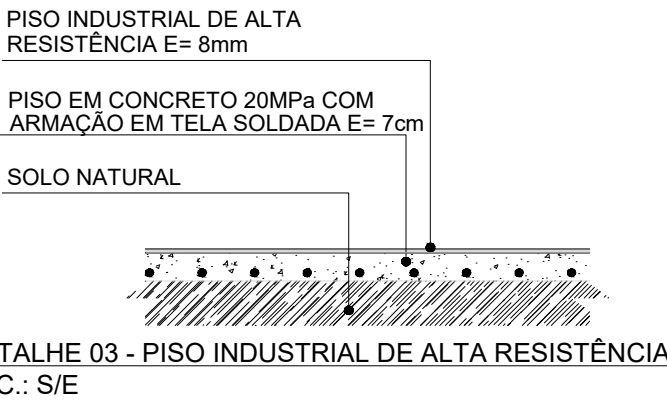

PROPRIETÁRIO: PREFEITURA MUNICIPAL DE COREMAS - PB

PROJETO: LINCOLN CARTAXO DE LIRA JÚNIOR CREA 160.814.689-8

CONSTRUÇÃO:

FOLHA 04/08
PROJETO: CONSTRUÇÃO DE GINÁSIO POLIESPORTIVO
CONVENIENTE: PREFEITURA MUNICIPAL DE COREMAS - PB
CONVENIADO: MUNICÍPIO DE COREMAS - PB
LOCALIDADE: COREMAS - PB

	DATA	RESPONSÁVEL	RUBRICA	DADOS
DESENHO	AGO/2025	LINCOLN CARTAXO		
CÓPIA				
VISTO				
ESCALAS	DESENHOS			CONVÊNIO
Indicada	Planta Baixa - Acabamentos e Esquadrias Detalhe 01 - Esquadrias Detalhe 02 - Revestimento Cerâmico Detalhe 03 - Piso Industrial de Alta Resistência			ARQUIVO

Aprovações:



Av. Gov. Flávio Ribeiro Coutinho, 500, sl. 601
Jardim Oceania, 58037-005 - João Pessoa (PB)
Tel +55 (83) 99924.4447
e-mail: contato@lclprojetos.com