



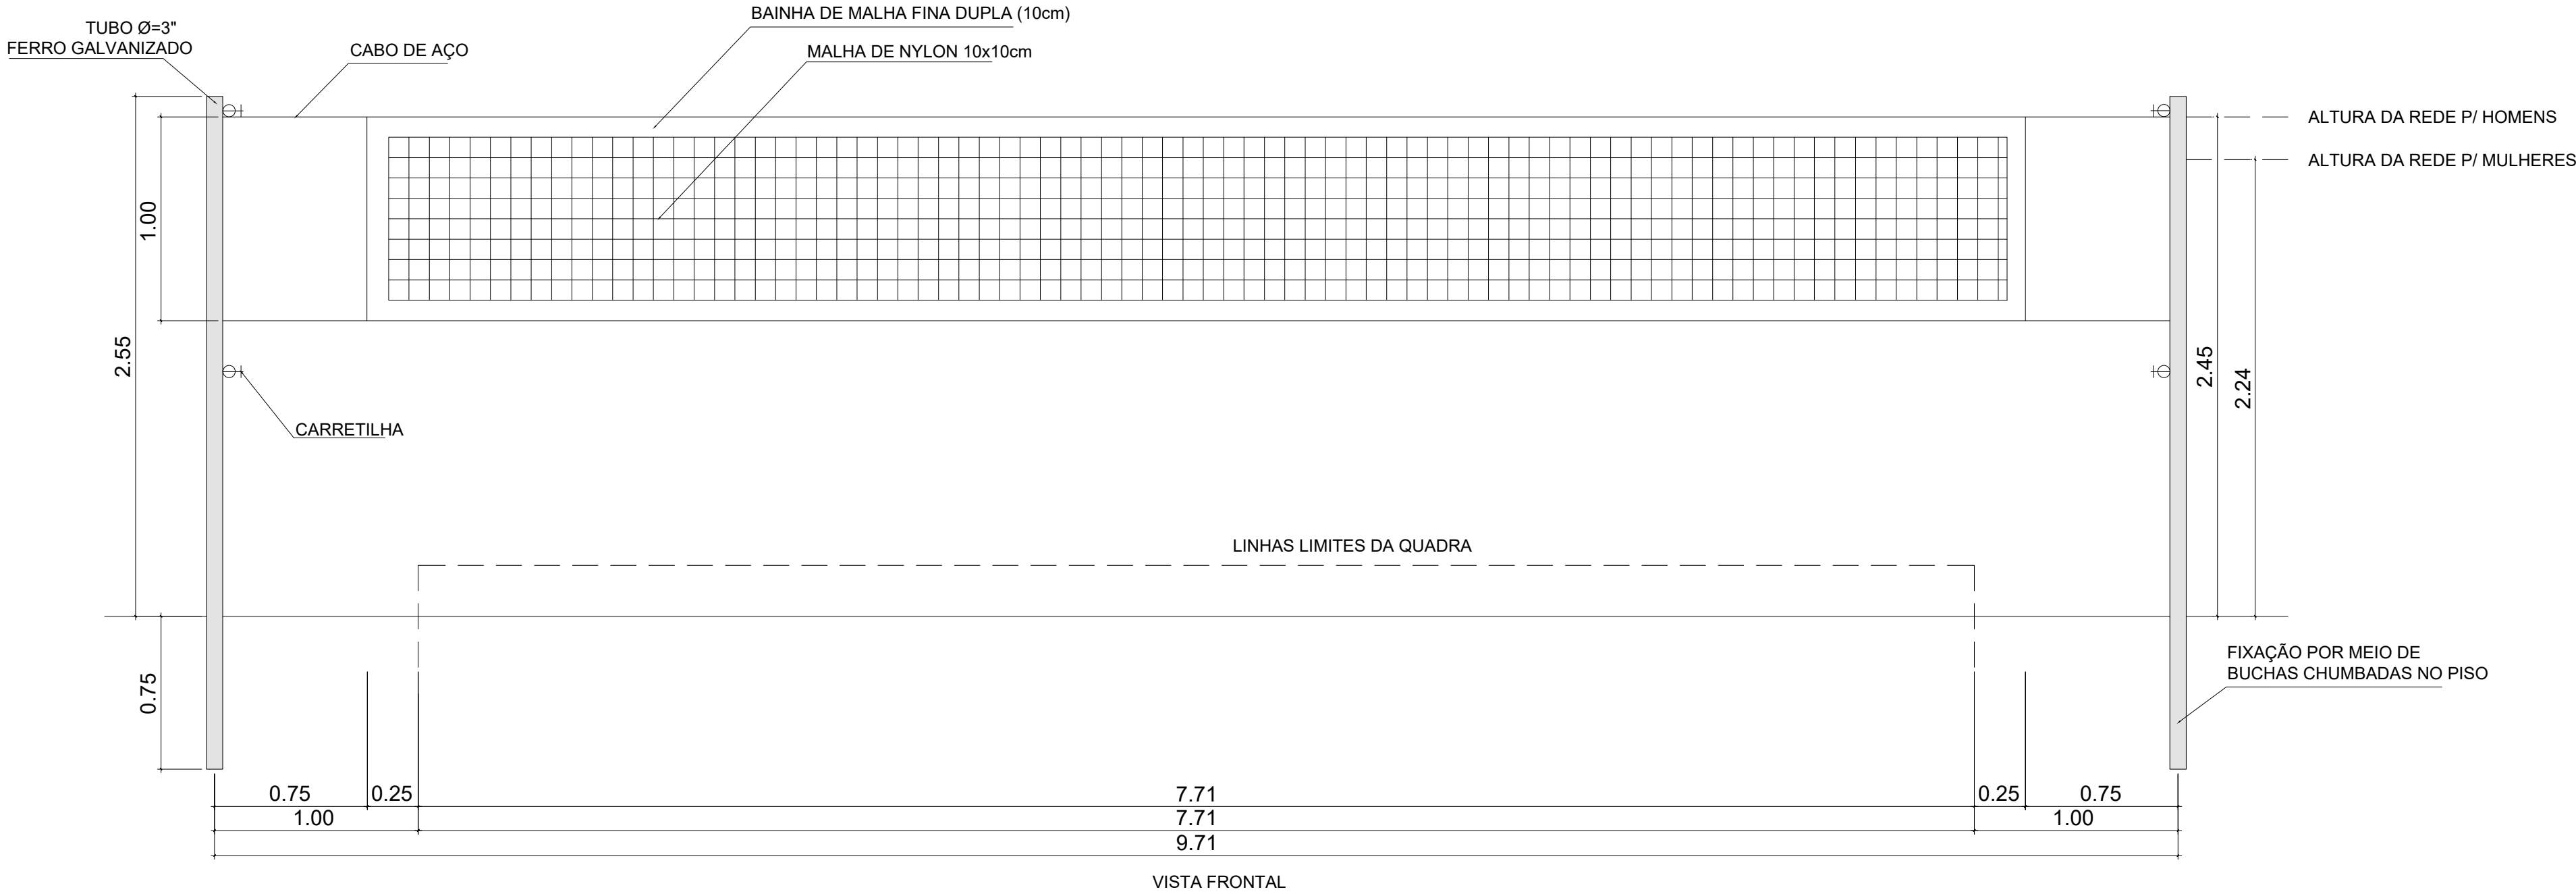

Detalhe 01 - Rede de Vôlei
ESC.: 1:25

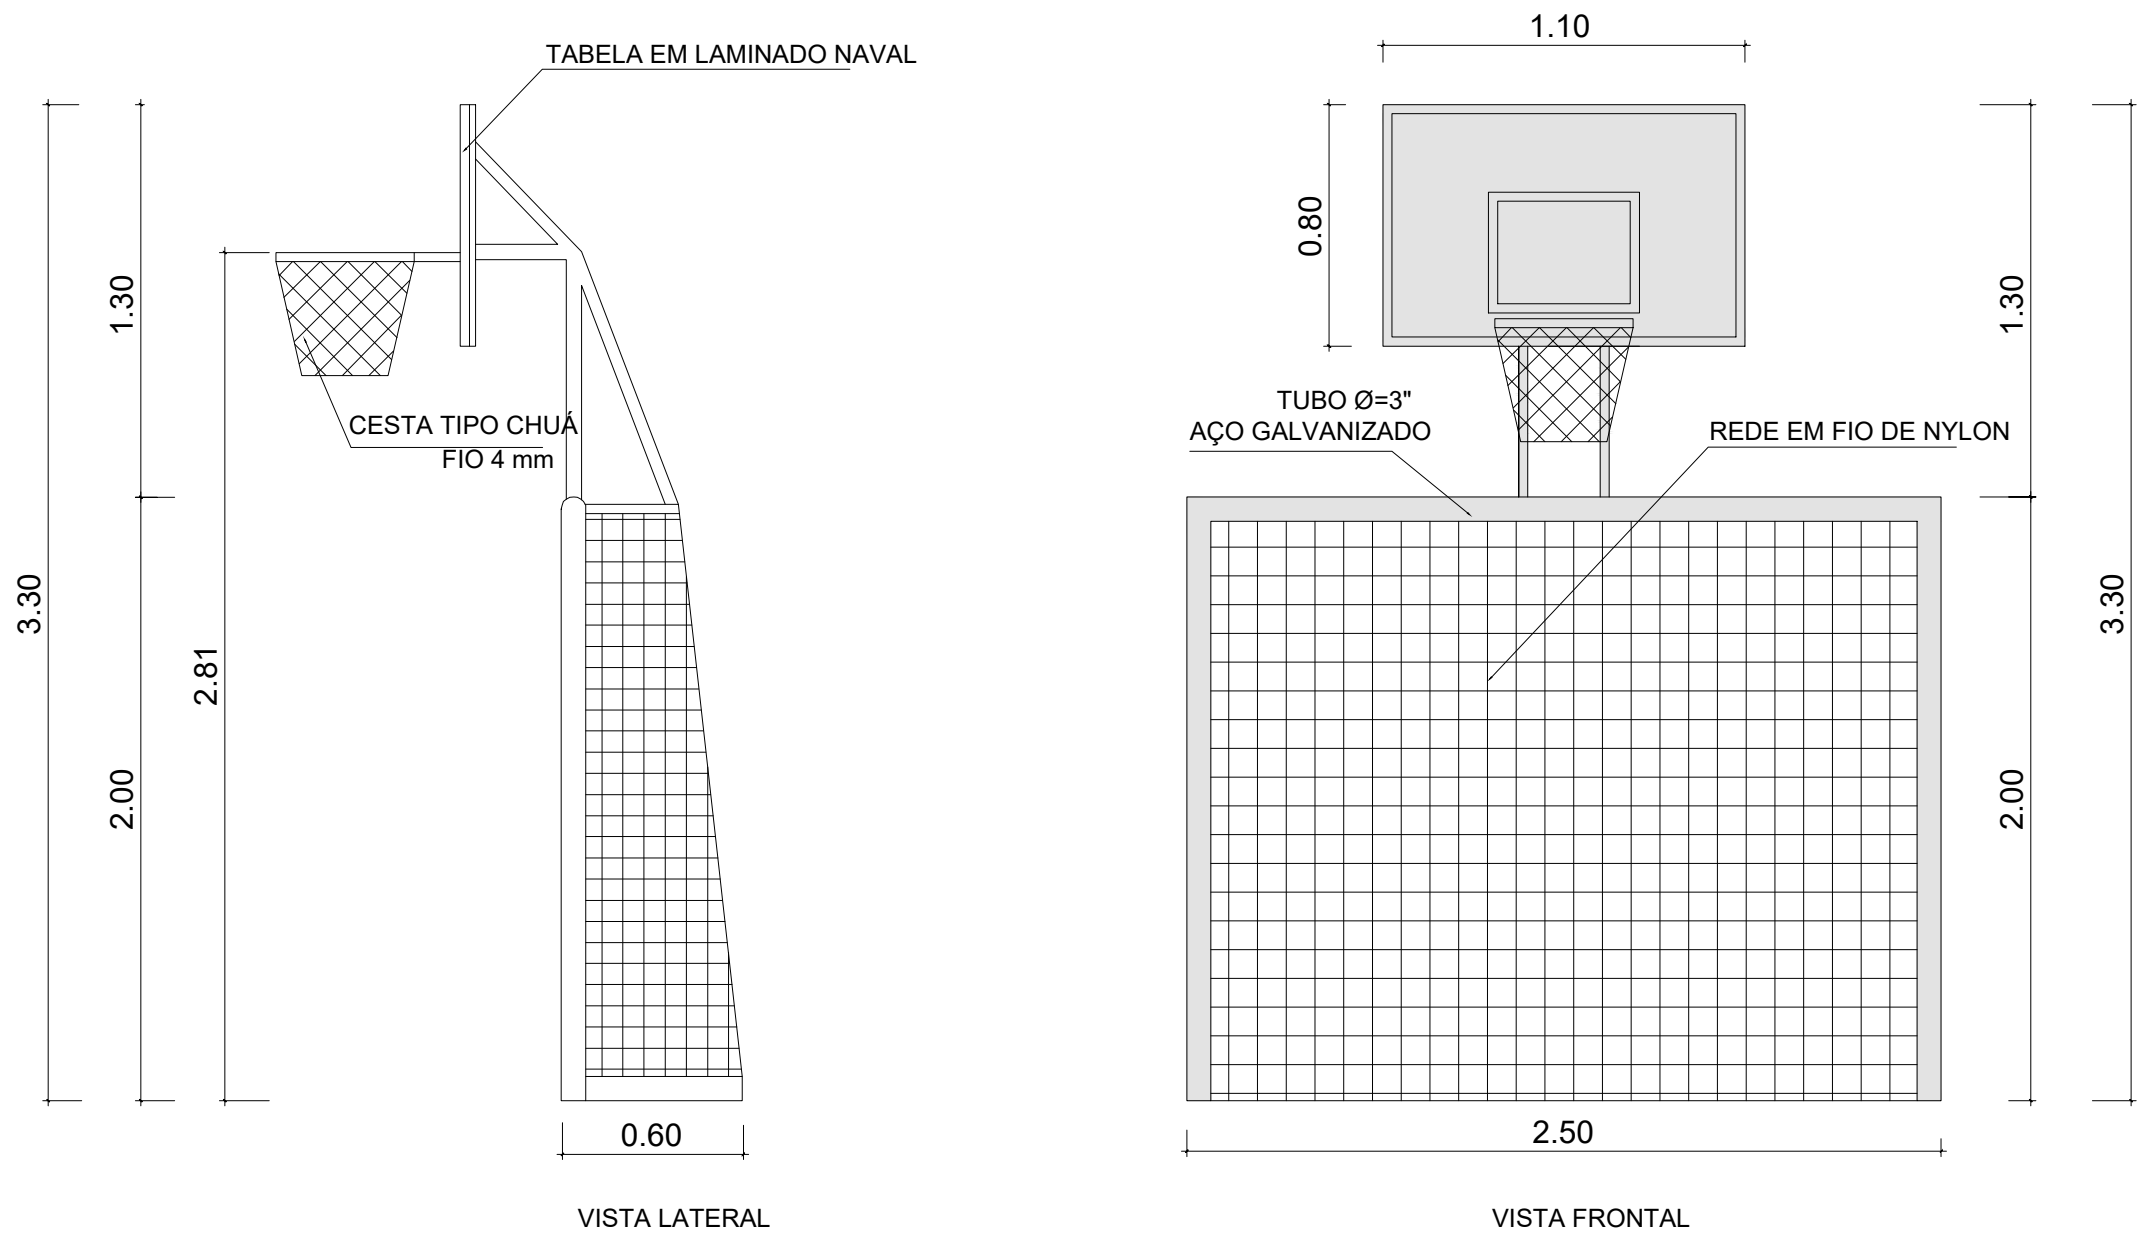

Detalhe 02 - Trave de Futebol conjugada com Tabela de Basquete
ESC.: 1:25

PROPRIETÁRIO: PREFEITURA MUNICIPAL DE COREMAS - PB

PROJETO: LINCOLN CARTAXO DE LIRA JÚNIOR CREA 160.814.689-8

CONSTRUÇÃO:

FOLHA	PROJETO:	CONSTRUÇÃO DE GINÁSIO POLIESPORTIVO		
05/08	CONVENIENTE:	PREFEITURA MUNICIPAL DE COREMAS - PB		
	CONVENIADO:	MUNICÍPIO DE COREMAS - PB		
	LOCALIDADE:	COREMAS - PB		

	DATA	RESPONSÁVEL	RUBRICA	DADOS
DESENHO	AGO/2025	LINCOLN CARTAXO		
CÓPIA				
VISTO				

ESCALAS	DESENHOS	CONVÊNIO
Indicada	Detalhe 01 - Rede de Vôlei Detalhe 02 - Trave de Futebol conjugada com Tabela de Basquete	
		ARQUIVO

Aprovações: