




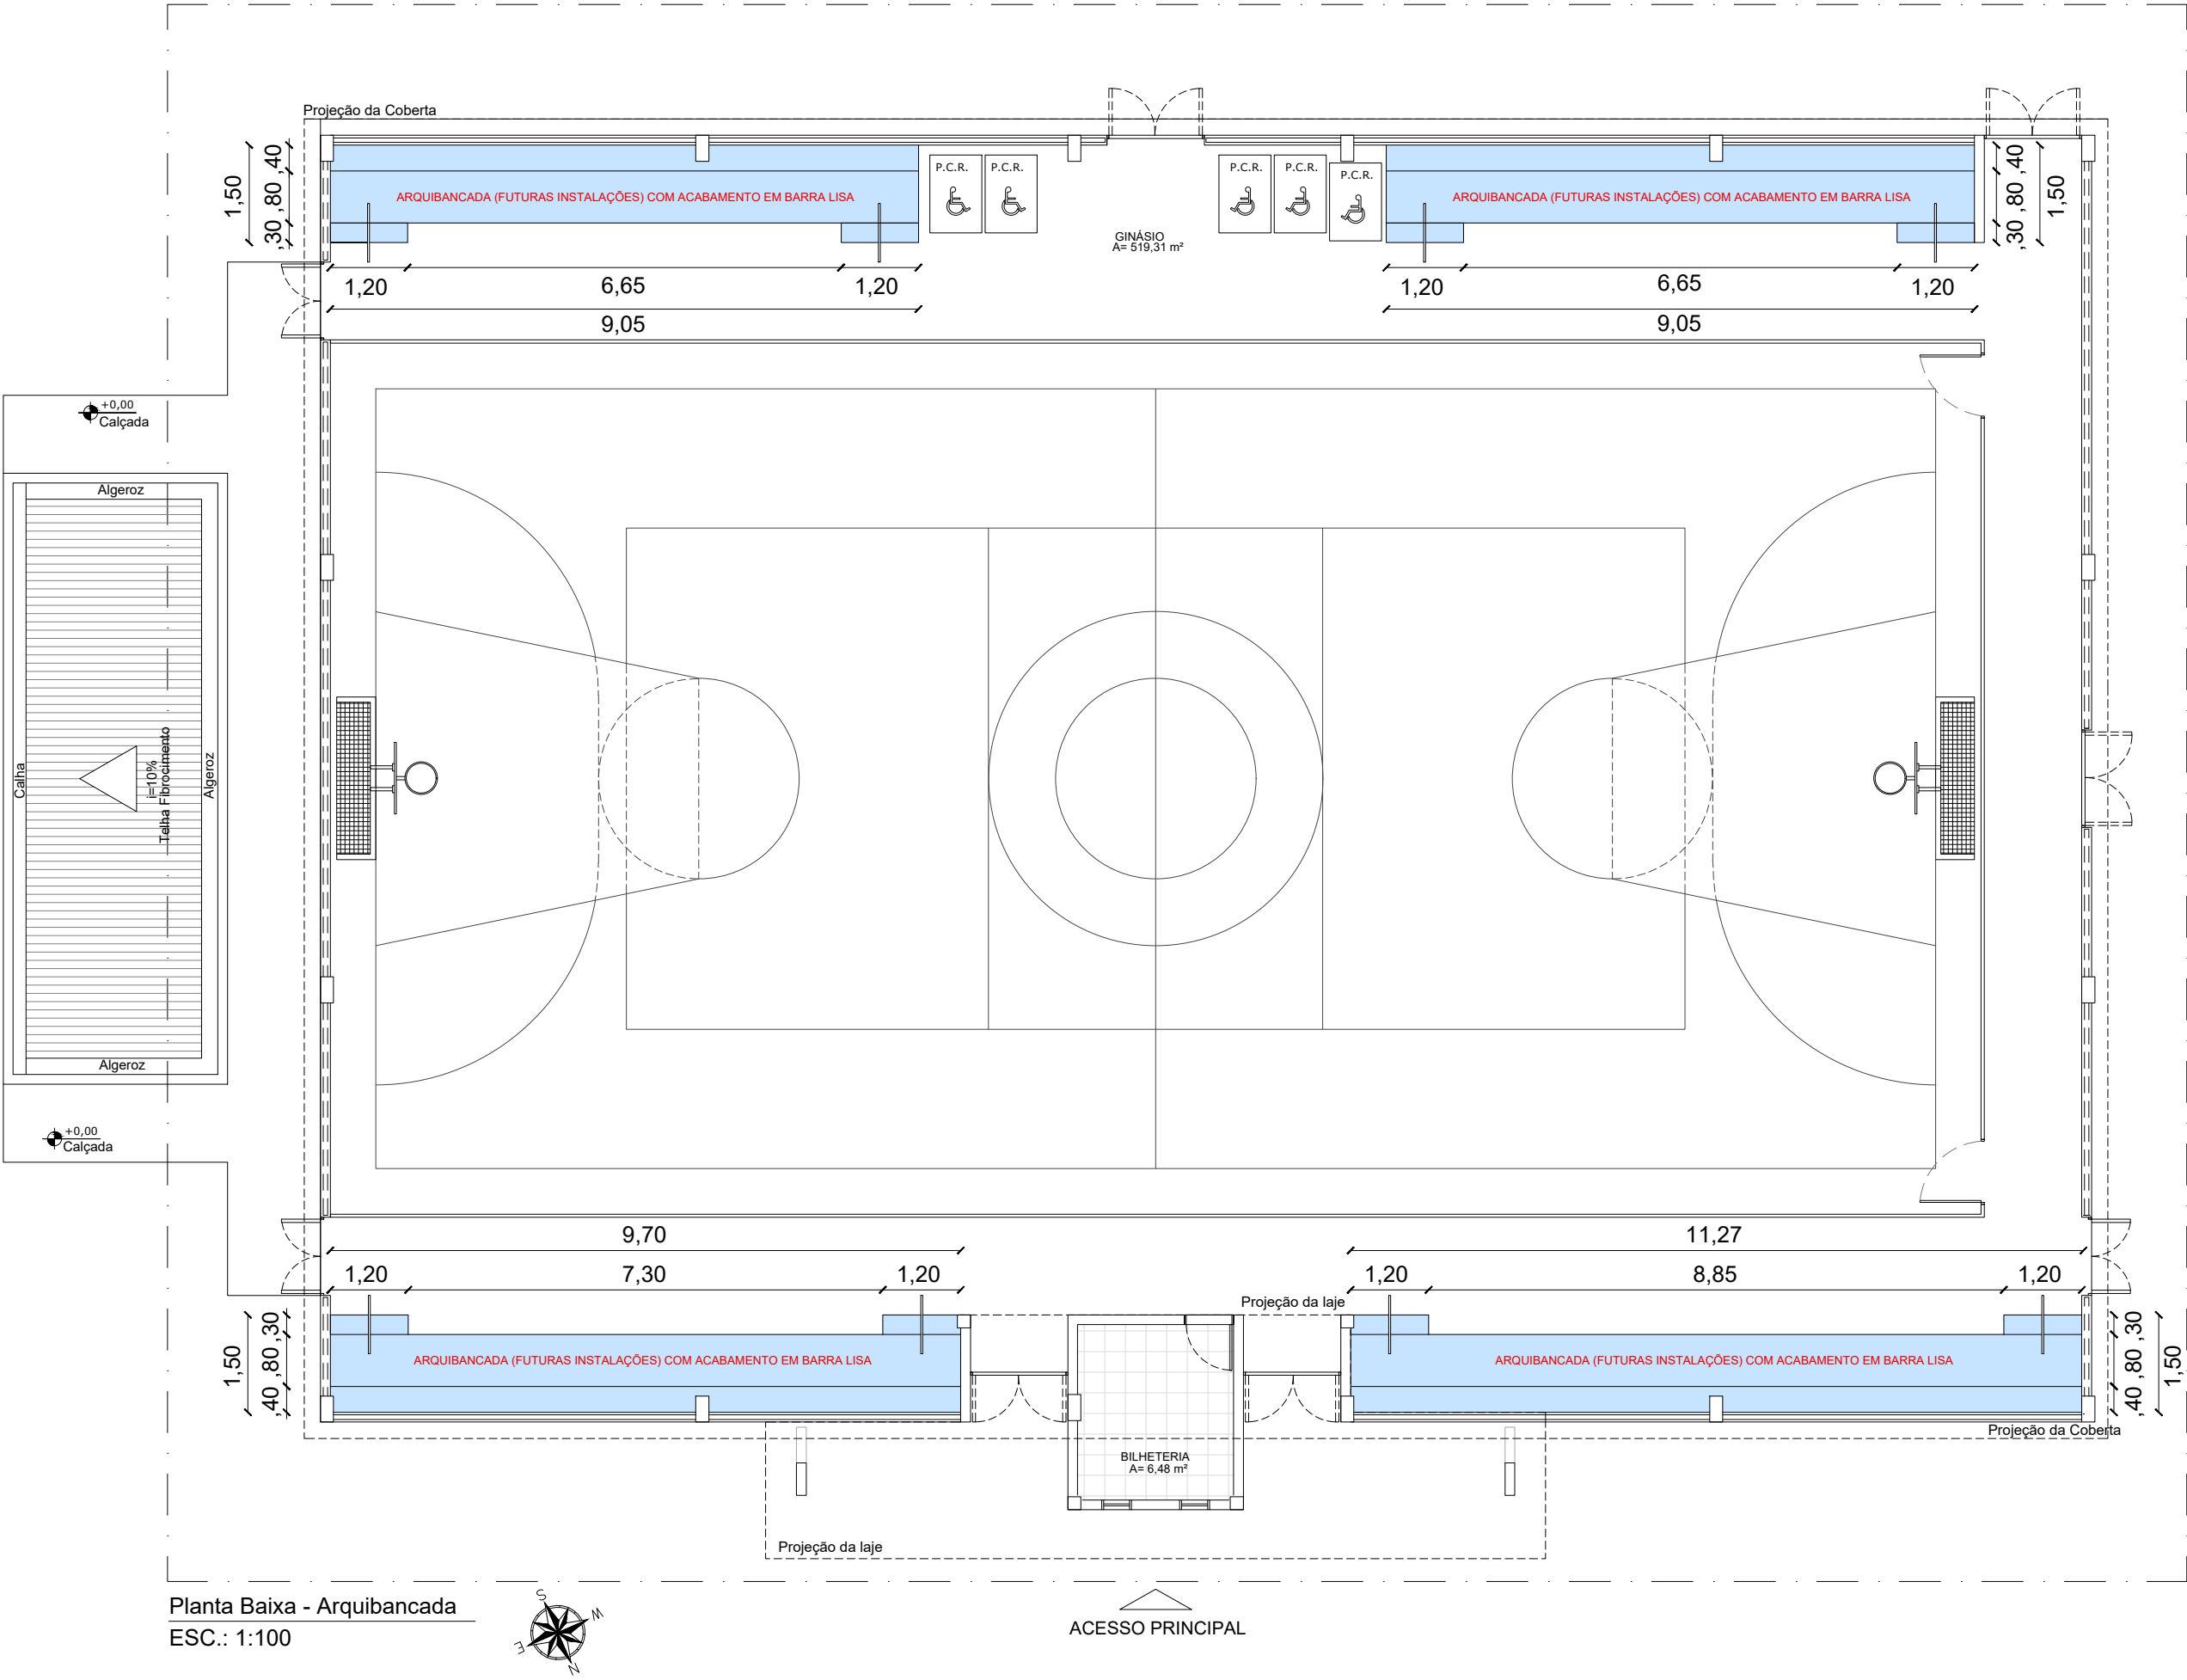

Planta Baixa - Arquibancada
ESC.: 1:100

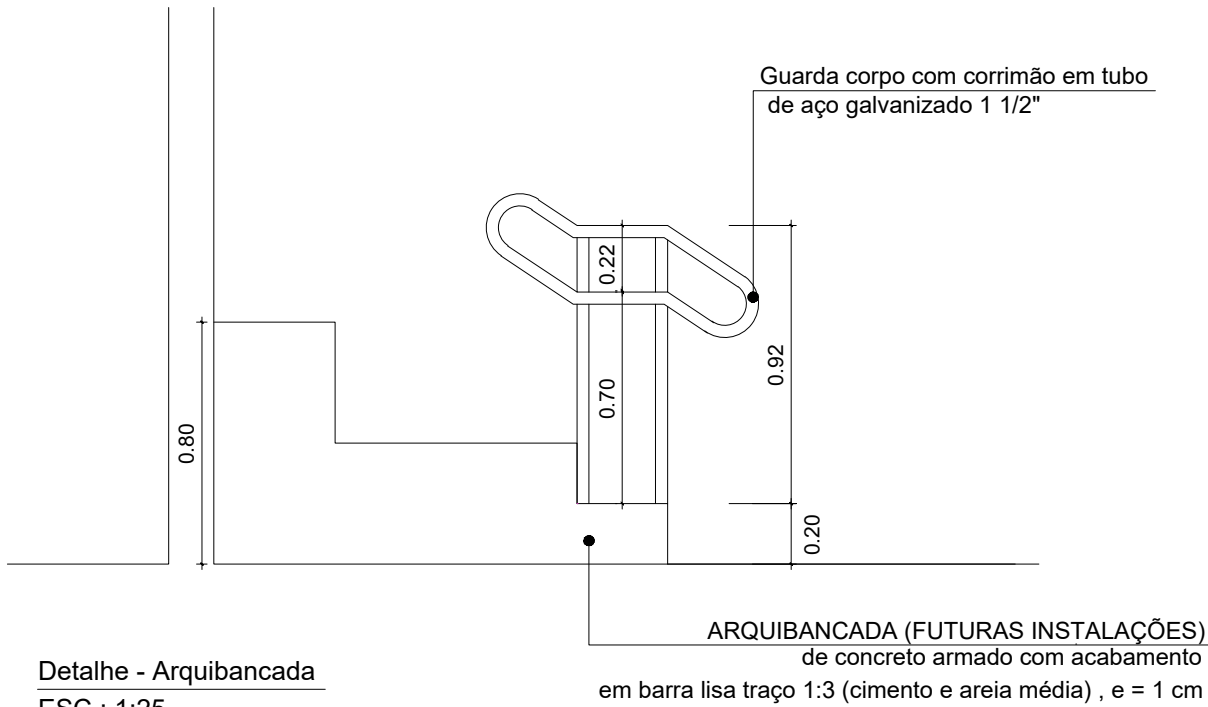

Detalhe - Arquibancada
ESC.: 1:25

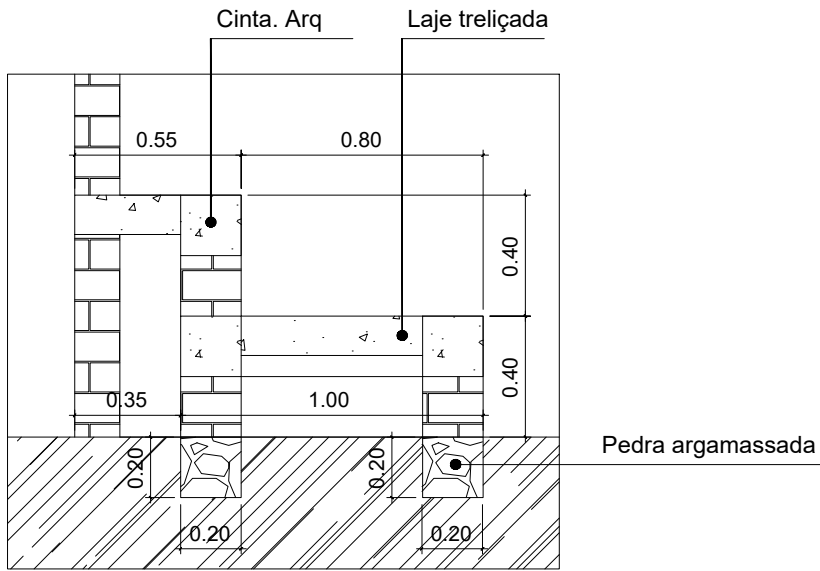

Corte - Arquibancada
ESC.: 1:25

PROPRIETÁRIO: PREFEITURA MUNICIPAL DE COREMAS - PB

PROJETO: LINCOLN CARTAXO DE LIRA JÚNIOR CREA 160.814.689-8

CONSTRUÇÃO:

FOLHA 06/08
PROJETO: CONSTRUÇÃO DE GINÁSIO POLIESPORTIVO
CONVENIENTE: PREFEITURA MUNICIPAL DE COREMAS - PB
CONVENIADO: MUNICÍPIO DE COREMAS - PB
LOCALIDADE: COREMAS - PB

	DATA	RESPONSÁVEL	RUBRICA	DADOS
DESENHO	AGO/2025	LINCOLN CARTAXO		
CÓPIA				
VISTO				
ESCALAS	DESENHOS			CONVÊNIO
Indicada	Planta Baixa - Arquibancada Detalhe - Arquibancada Corte - Arquibancada			ARQUIVO

Aprovações: