



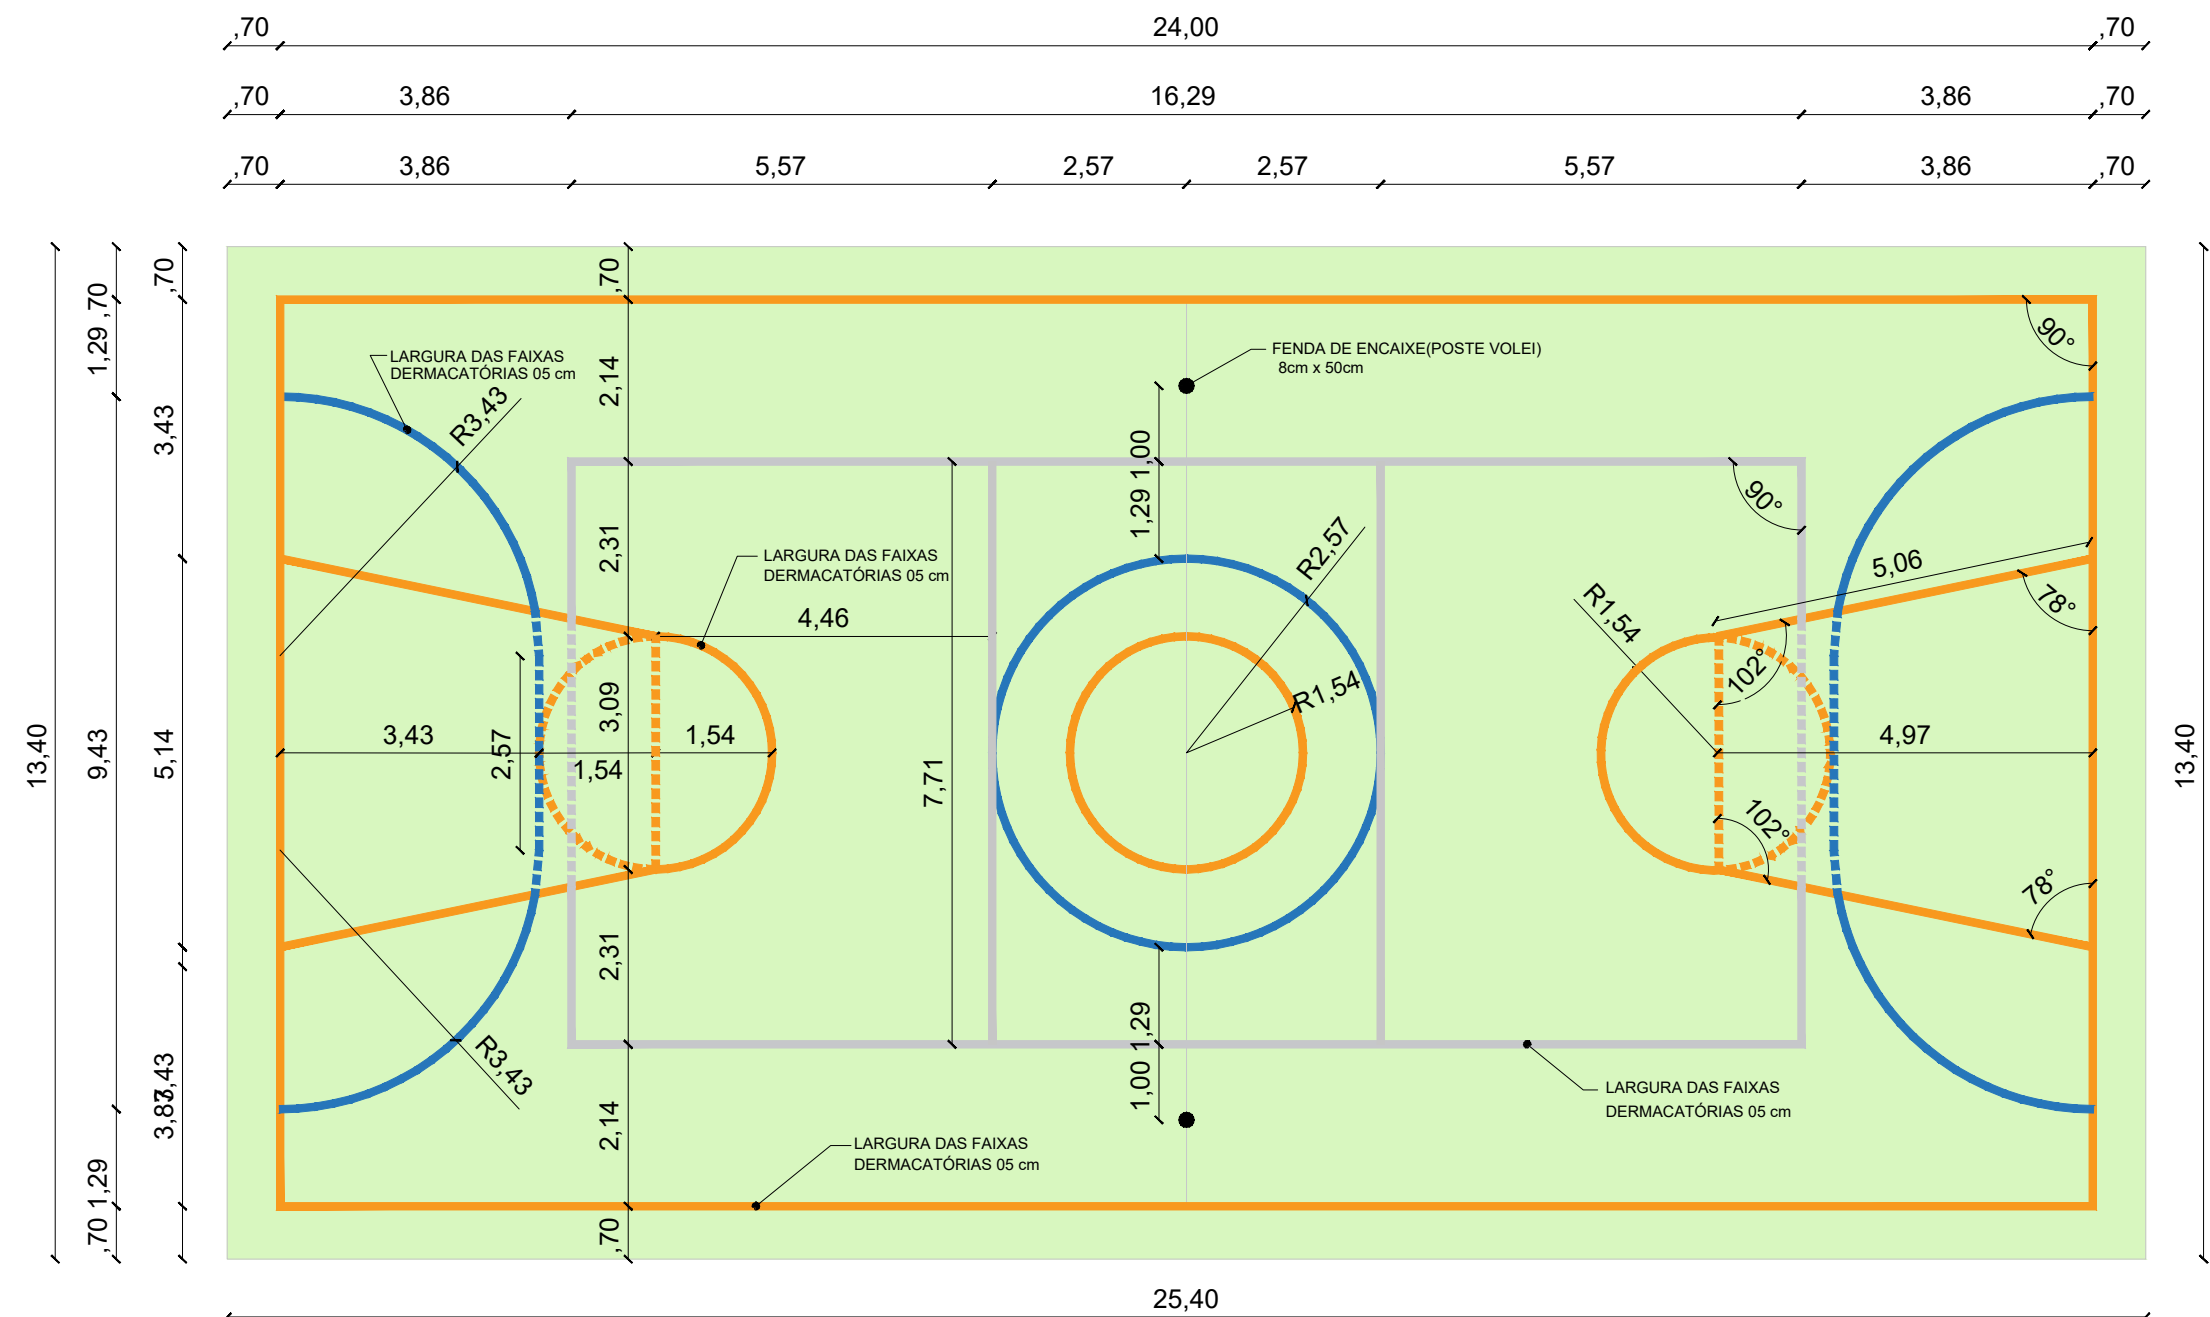


PINTURA DO PISO DA QUADRA - FAIXAS
ESC.: 1:100

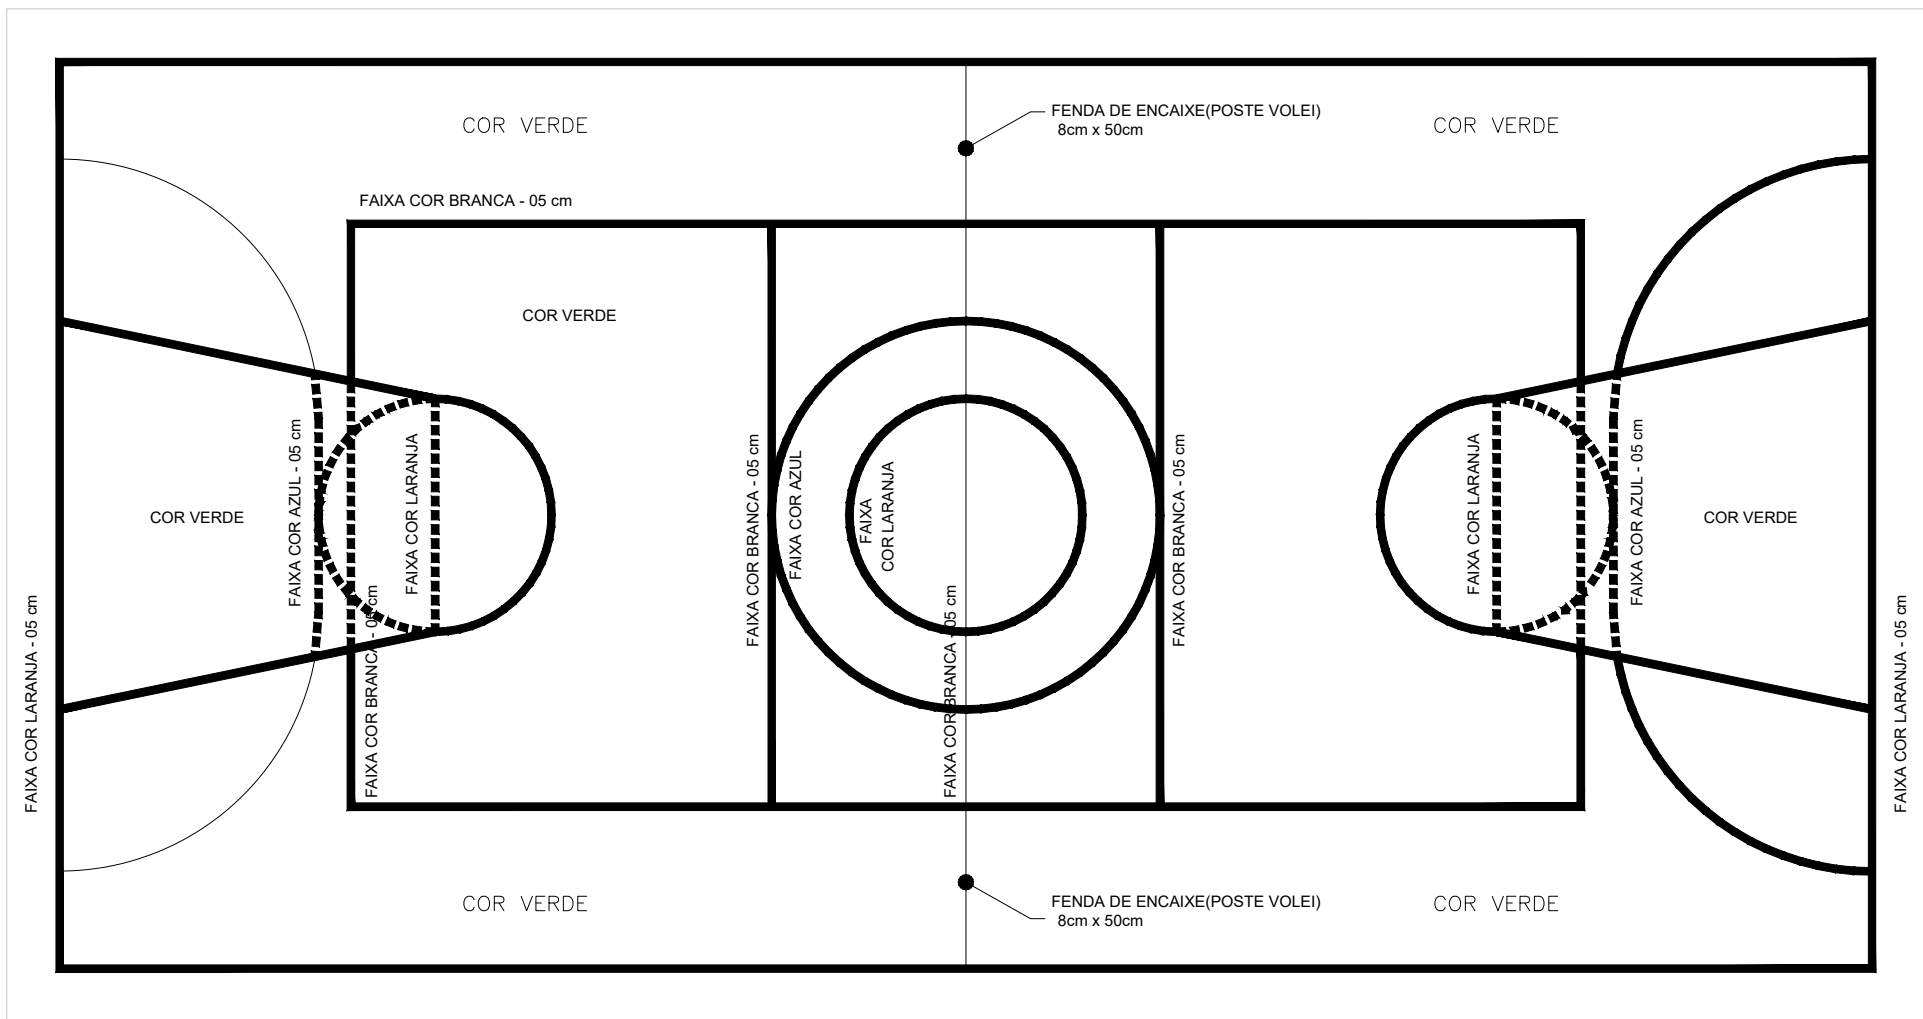

OBS.:PINTURA COM TINTA A BASE DE EPÓXI PARA PISO

PINTURA DO PISO DA QUADRA - ÁREA INTERNA: 340,36M²
ESC.: 1:100

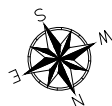

PROPRIETÁRIO: PREFEITURA MUNICIPAL DE COREMAS - PB

PROJETO: LINCOLN CARTAXO DE LIRA JÚNIOR CREA 160.814.689-8

CONSTRUÇÃO:

FOLHA
07/08
PROJETO: CONSTRUÇÃO DE GINÁSIO POLIESPORTIVO
CONVENIENTE: PREFEITURA MUNICIPAL DE COREMAS - PB
CONVENIADO: MUNICÍPIO DE COREMAS - PB
LOCALIDADE: COREMAS - PB

	DATA	RESPONSÁVEL	RUBRICA	DADOS
DESENHO	AGO/2025	LINCOLN CARTAXO		
CÓPIA				
VISTO				

ESCALAS	DESENHOS	CONVÊNIO
		ARQUIVO
Indicada	Pintura do Piso da Quadra - Faixas Pintura do Piso da Quadra - Área Interna: 340,36m²	

Aprovações:

LCL PROJETOS

Av. Gov. Flávio Ribeiro Coutinho, 500, sl. 601
Jardim Oceania, 58037-005 - João Pessoa (PB)
Tel +55 (83) 99924.4447
e-mail: contato@lclprojetos.com