




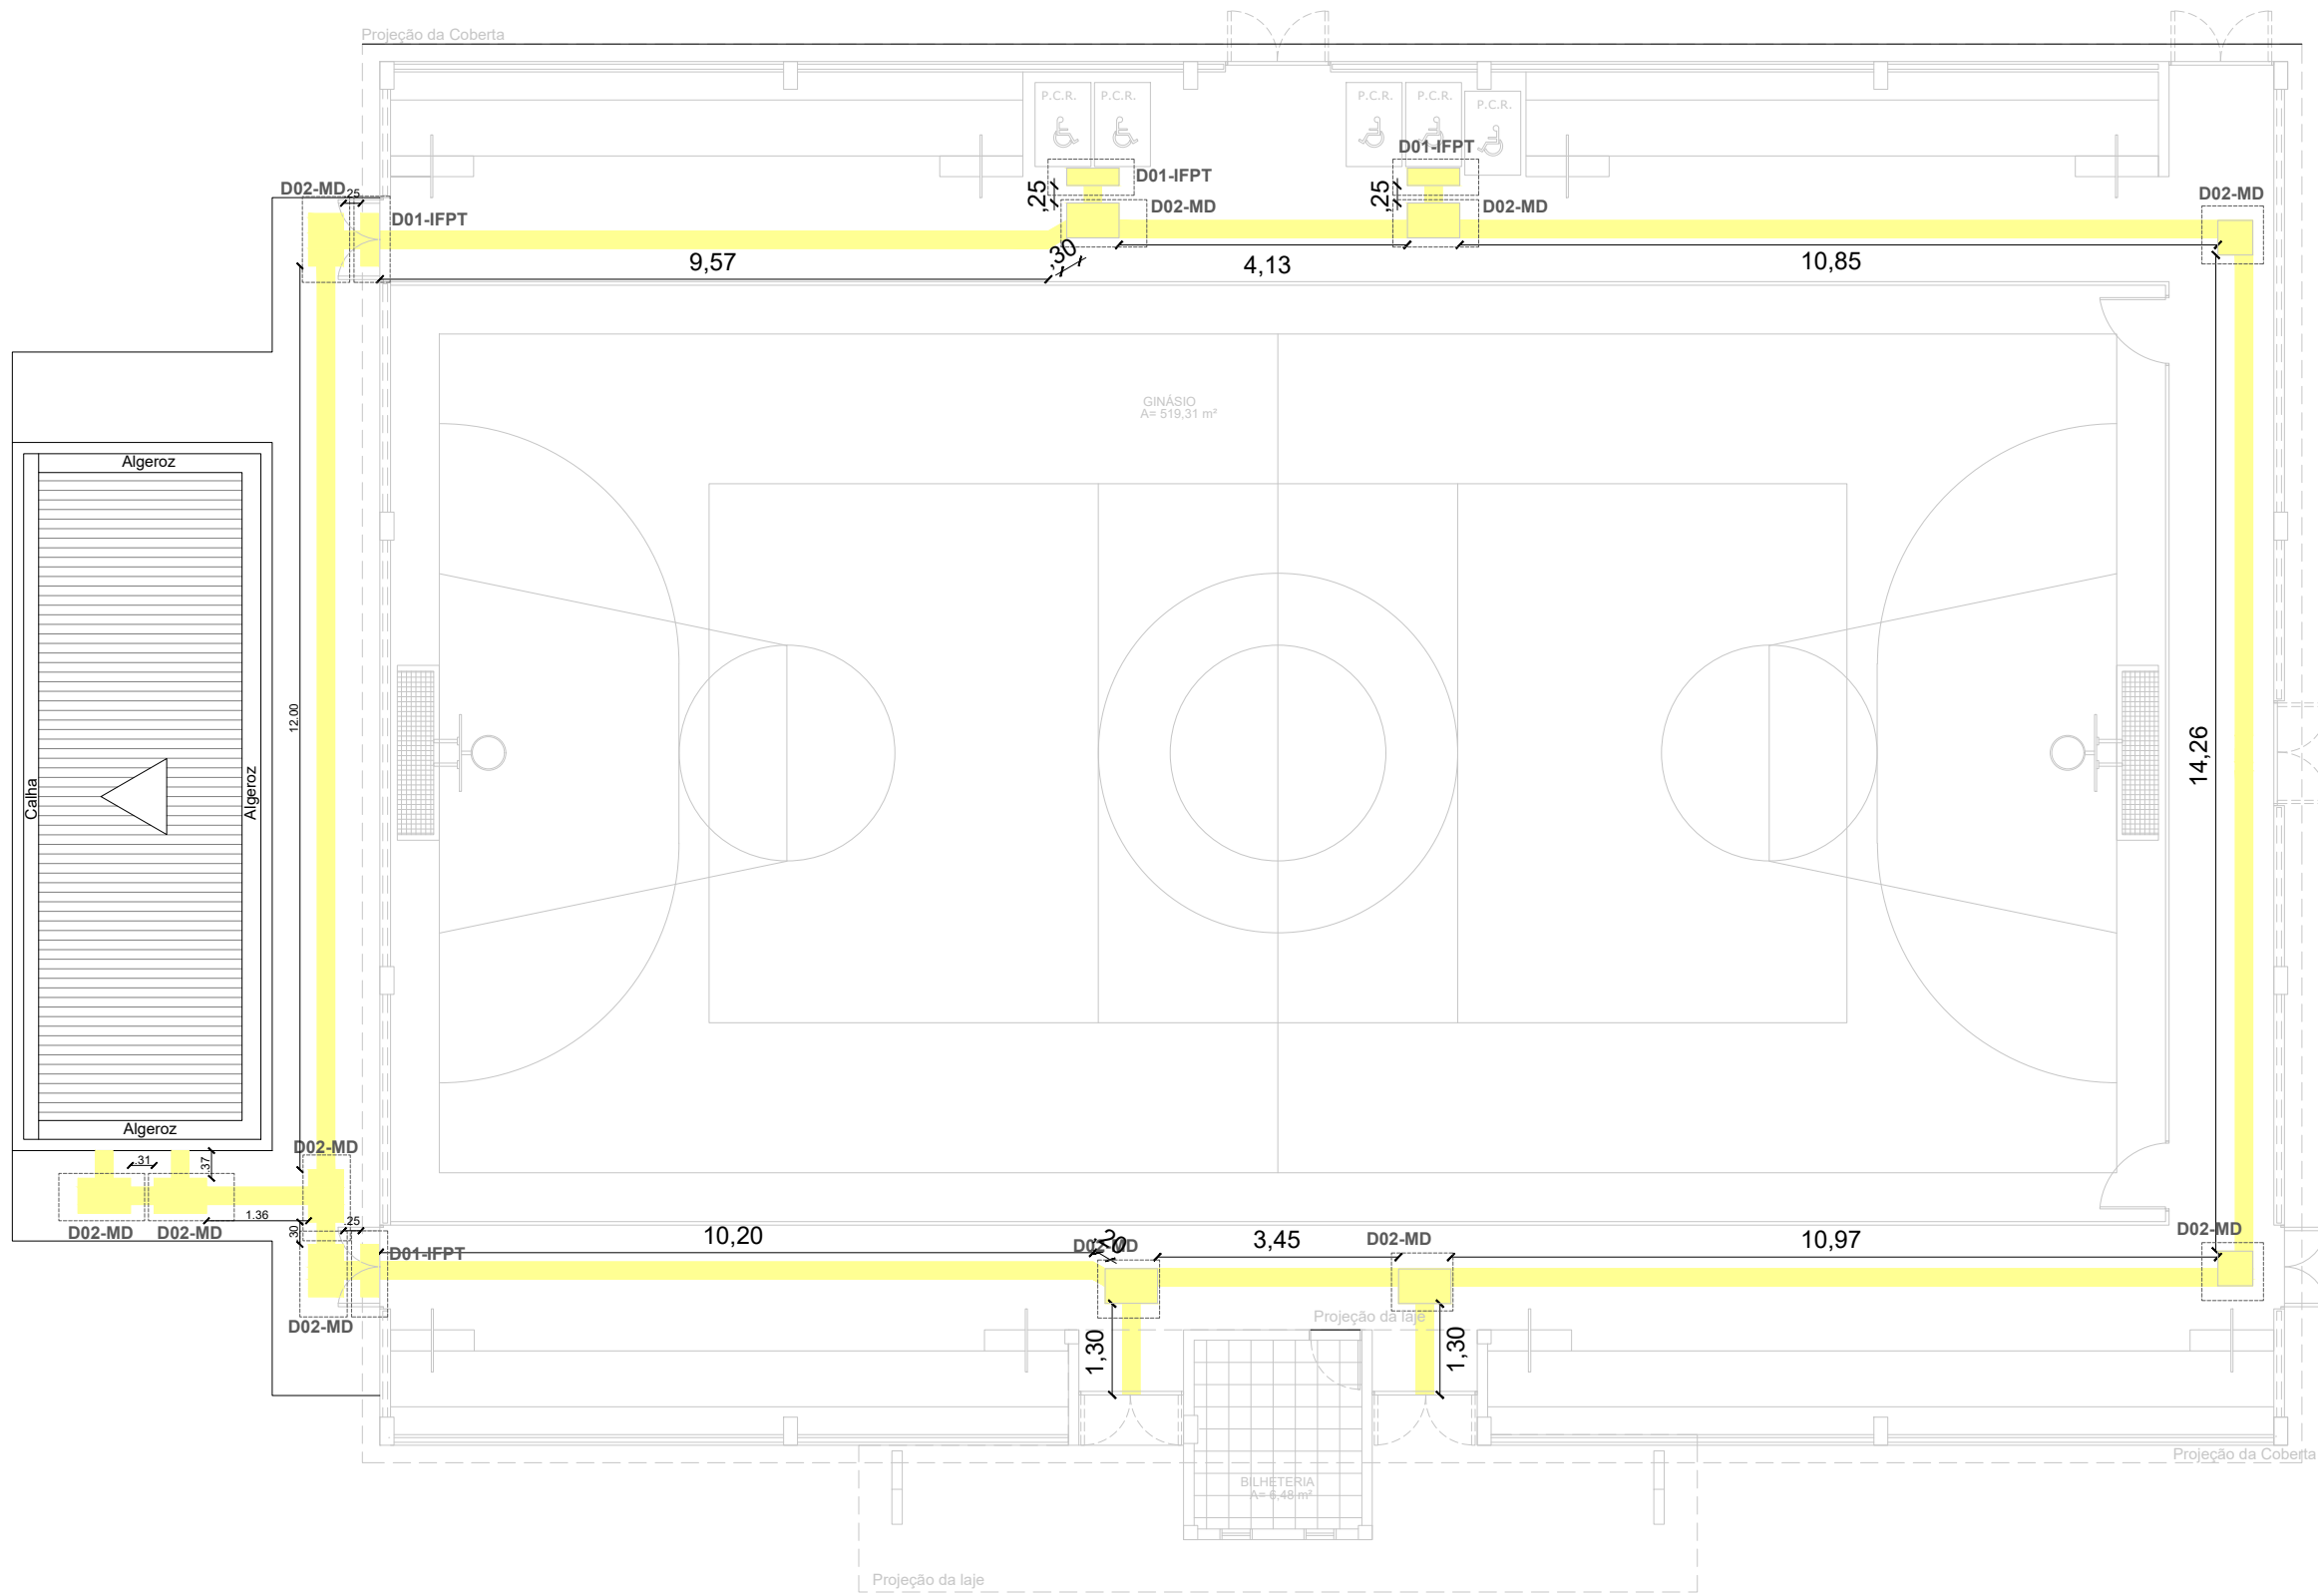

Planta Baixa - Acessibilidade
escala h1/100

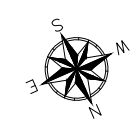


LEGENDA		
GINÁSIO		
	Piso Tátil Direcional	19,93- m²
	Piso Tátil de Alerta Mudança de Direção	0,50 - m²
	Piso Tátil de Alerta em Início e Fim	1,50 - m²
		2,58 - m²

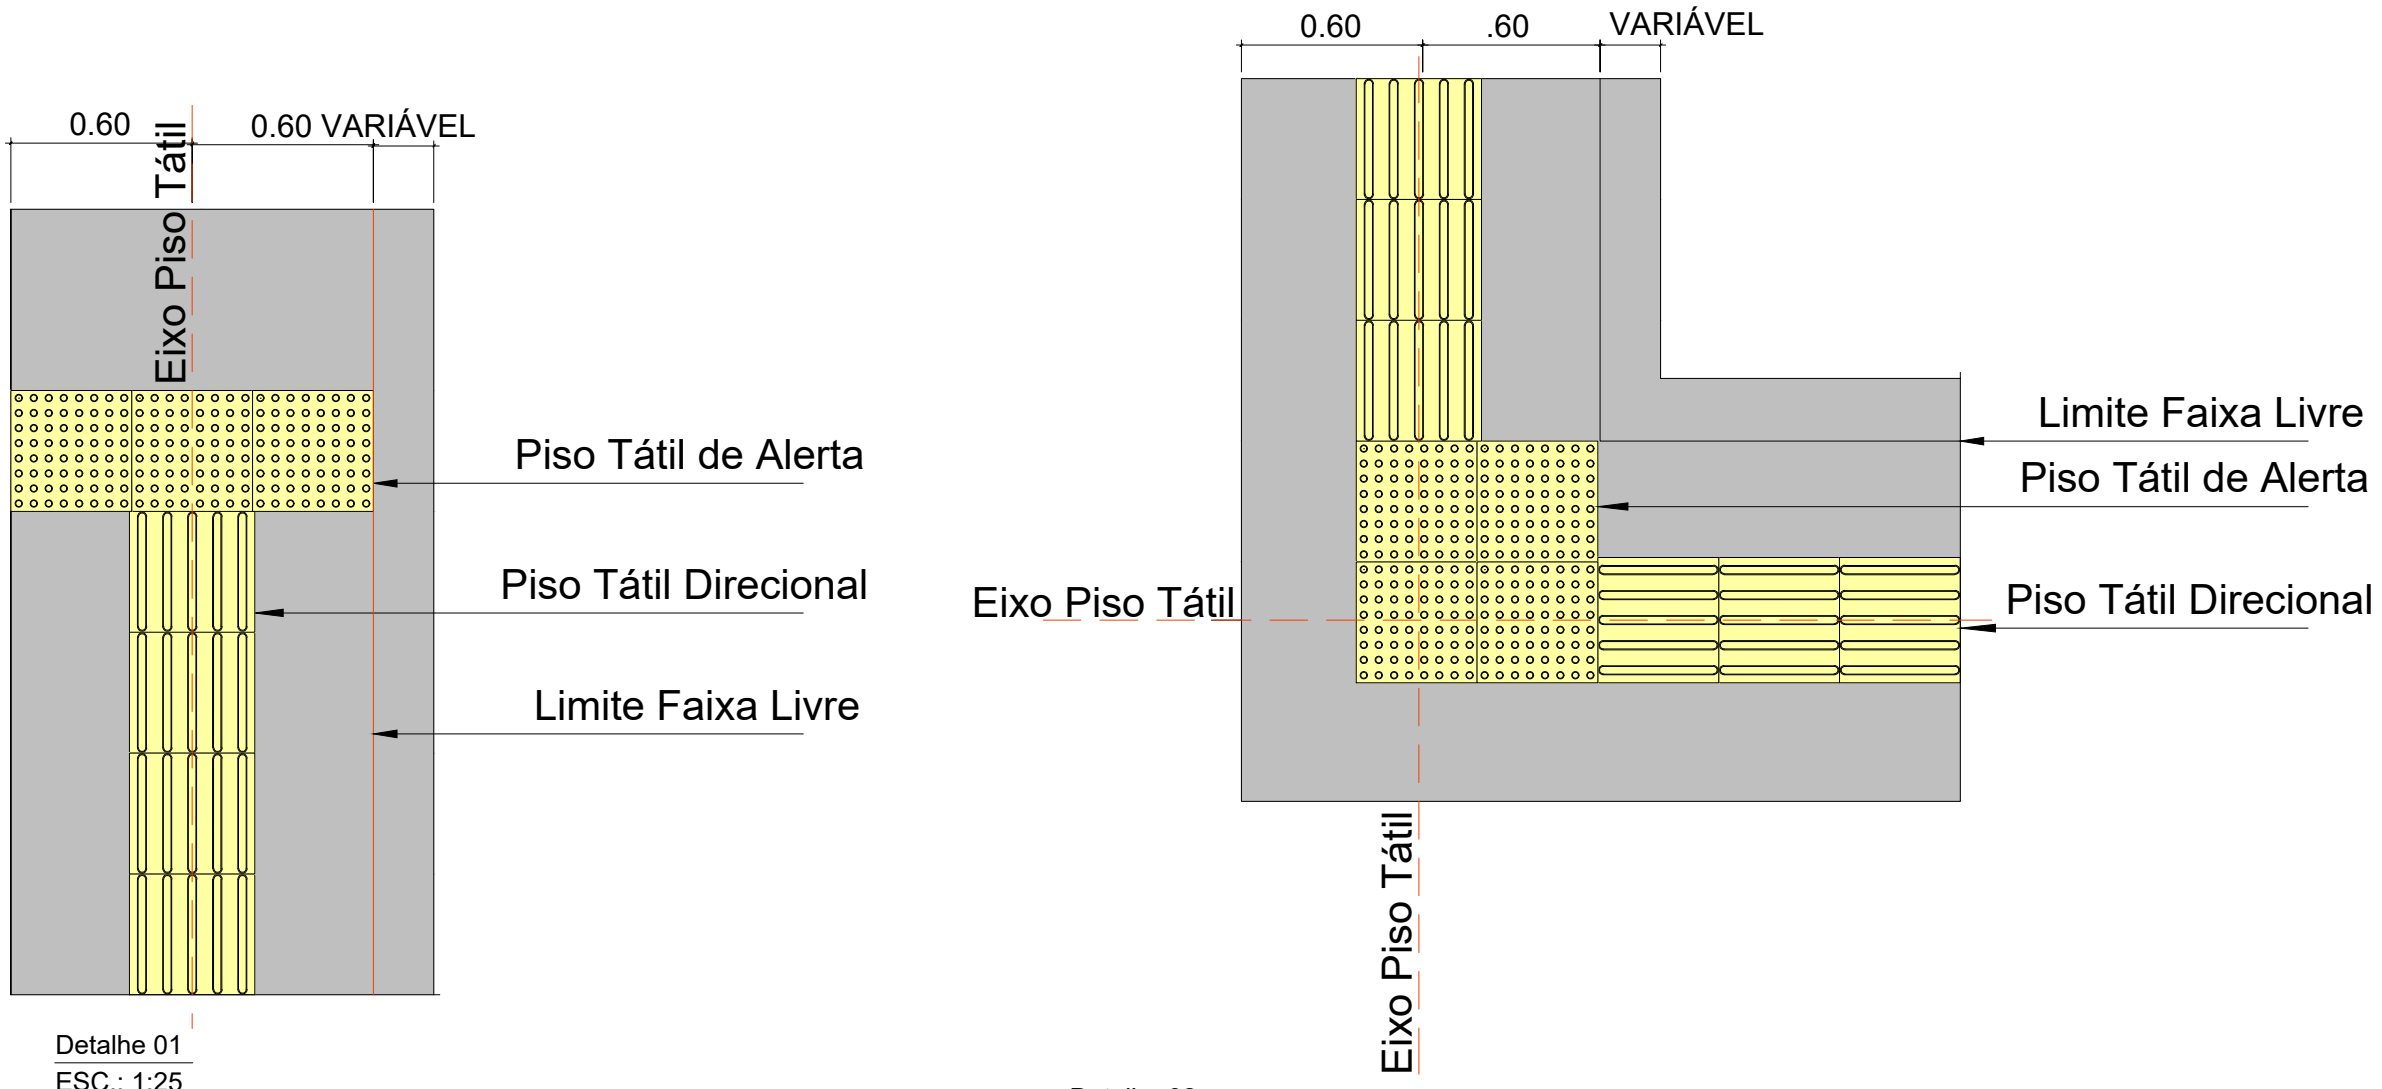

Detalhe 01
ESC.: 1:25

Detalhe 02
ESC.: 1:25

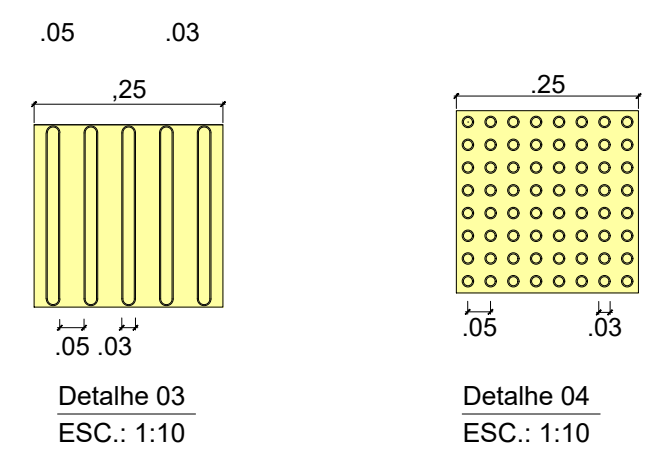

PROPRIETÁRIO: PREFEITURA MUNICIPAL DE COREMAS - PB
LINCOLN CARTAXO DE LIRA JUNIOR:06897861405 Assinado de forma digital por LINCOLN CARTAXO DE LIRA JUNIOR:06897861405
Dados: 2025.08.08 12:14:28 -03'00'
PROJETO: LINCOLN CARTAXO DE LIRA JÚNIOR CREA 160.814.689-8

CONSTRUÇÃO:

FOLHA 08/08	PROJETO:	CONSTRUÇÃO DE GINÁSIO POLIESPORTIVO		
	CONVENIENTE:	PREFEITURA MUNICIPAL DE COREMAS - PB		
	CONVENIADO:	MUNICÍPIO DE COREMAS - PB		
	LOCALIDADE:	COREMAS - PB		
	DATA	RESPONSÁVEL	RUBRICA	DADOS
DESENHO	AGO/2025	LINCOLN CARTAXO		
CÓPIA				
VISTO				
ESCALAS	DESENHOS			CONVÊNIO
	Indicada Planta Baixa - Acessibilidade Detalhe 01 e 02 Detalhe 03 e 04			ARQUIVO

Aprovações: