



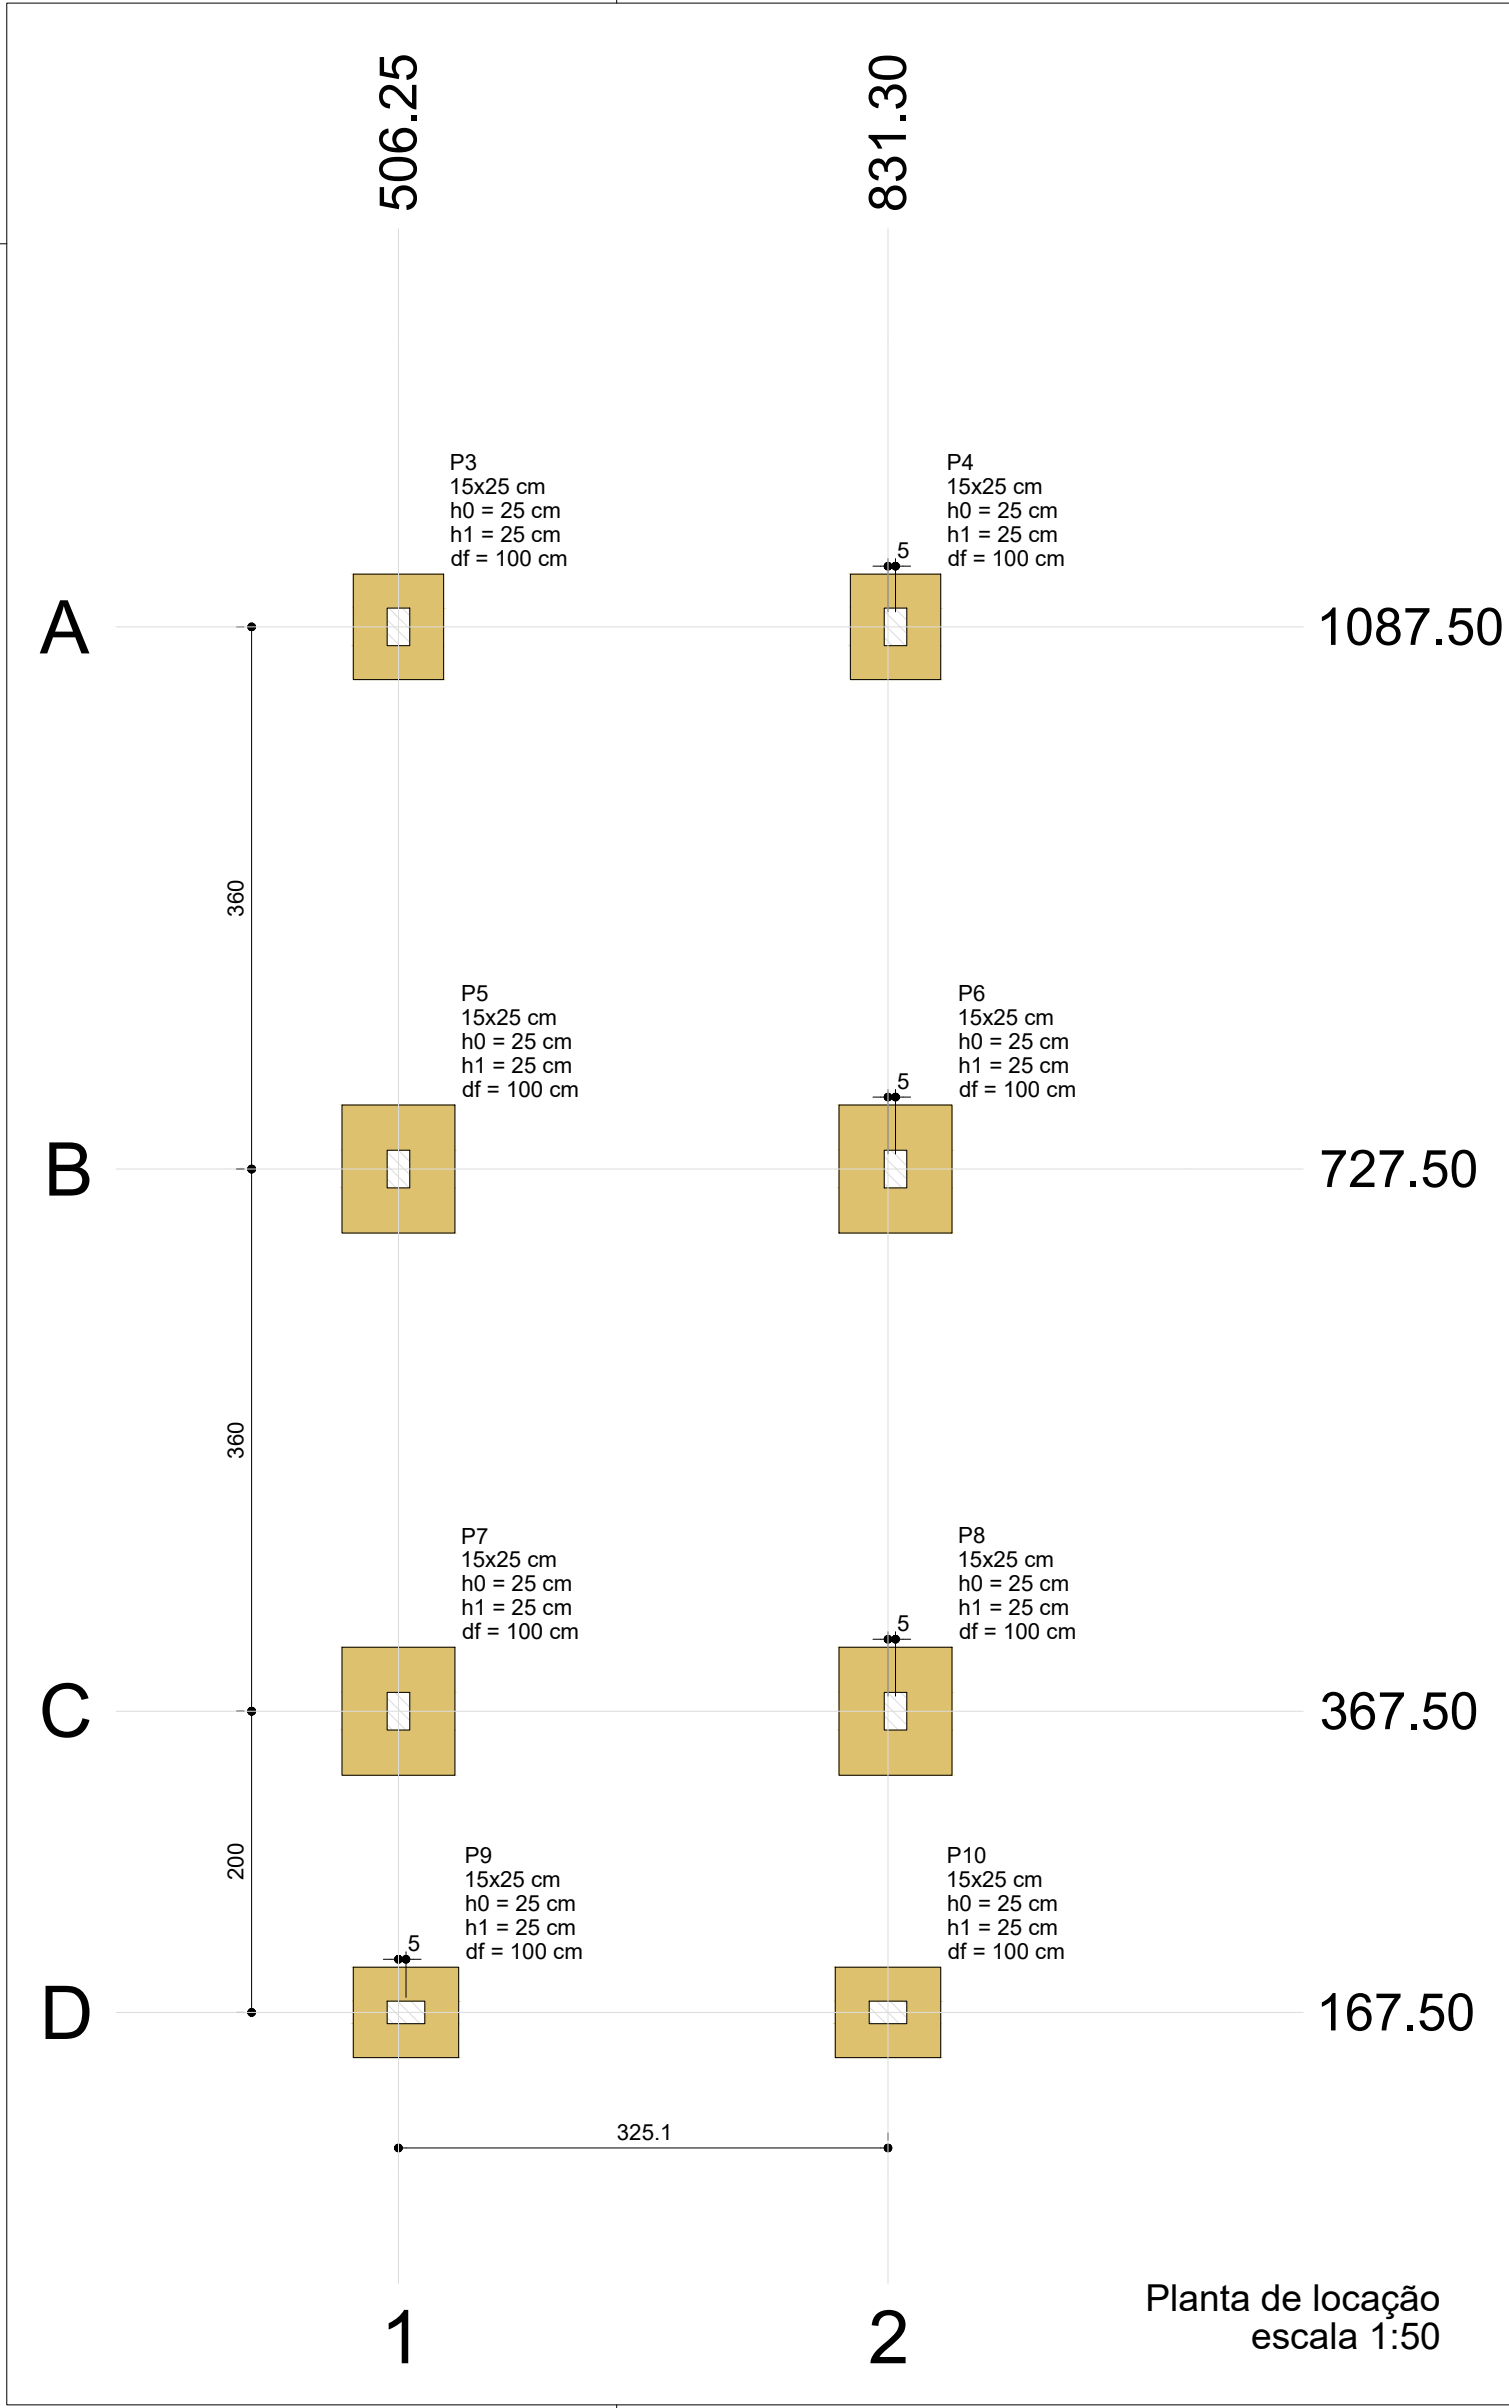

| Pilar |            |        |         |                 |                 | Fundação    |             |              |              |         |
|-------|------------|--------|---------|-----------------|-----------------|-------------|-------------|--------------|--------------|---------|
| Nome  | Seção (cm) | X (cm) | Y (cm)  | Carga Máx. (tf) | Carga Mín. (tf) | Lado B (cm) | Lado H (cm) | h0 / ha (cm) | h1 / hb (cm) | df (cm) |
| P3    | 15x25      | 506.25 | 1087.50 | 5.5             | 4.1             | 60          | 70          | 25           | 25           | 100     |
| P4    | 15x25      | 836.30 | 1087.50 | 5.5             | 4.1             | 60          | 70          | 25           | 25           | 100     |
| P5    | 15x25      | 506.25 | 727.50  | 8.7             | 7.2             | 75          | 85          | 25           | 25           | 100     |
| P6    | 15x25      | 836.30 | 727.50  | 8.7             | 7.2             | 75          | 85          | 25           | 25           | 100     |
| P7    | 15x25      | 506.25 | 367.50  | 9.5             | 8.0             | 75          | 85          | 25           | 25           | 100     |
| P8    | 15x25      | 836.30 | 367.50  | 9.5             | 7.9             | 75          | 85          | 25           | 25           | 100     |
| P9    | 15x25      | 511.25 | 167.50  | 5.9             | 4.4             | 60          | 70          | 25           | 25           | 100     |
| P10   | 15x25      | 831.30 | 167.50  | 5.9             | 4.3             | 60          | 70          | 25           | 25           | 100     |

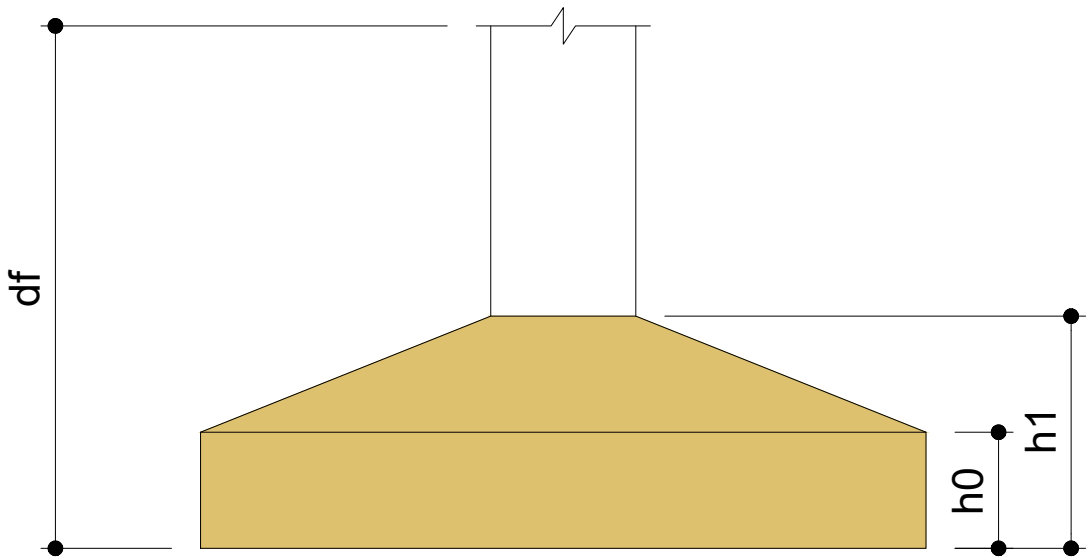


| Locação no eixo X |            | Locação no eixo Y |         |
|-------------------|------------|-------------------|---------|
| Coordenadas (cm)  | Nome       | Coordenadas (cm)  | Nome    |
| 506.25            | P3, P5, P7 | 1087.50           | P3, P4  |
| 511.25            | P9         | 727.50            | P5, P6  |
| 831.30            | P10        | 367.50            | P7, P8  |
| 836.30            | P4, P6, P8 | 167.50            | P9, P10 |

| Vigas |            |               |            |
|-------|------------|---------------|------------|
| Nome  | Seção (cm) | Elevação (cm) | Nível (cm) |
| VB2   | 15x30      | 0             | 0          |
| VB3   | 15x30      | 0             | 0          |
| VB4   | 15x30      | 0             | 0          |
| VB5   | 15x30      | 0             | 0          |
| VB6   | 15x30      | 0             | 0          |
| VB7   | 15x30      | 0             | 0          |
| VB8   | 15x30      | 0             | 0          |
| VB9   | 15x30      | 0             | 0          |
| VB10  | 15x30      | 0             | 0          |

| Pilares |            |               |            |
|---------|------------|---------------|------------|
| Nome    | Seção (cm) | Elevação (cm) | Nível (cm) |
| P3      | 15x25      | 0             | 0          |
| P4      | 15x25      | 0             | 0          |
| P5      | 15x25      | 0             | 0          |
| P6      | 15x25      | 0             | 0          |
| P7      | 15x25      | 0             | 0          |
| P8      | 15x25      | 0             | 0          |
| P9      | 15x25      | 0             | 0          |
| P10     | 15x25      | 0             | 0          |

| Características dos materiais |               |
|-------------------------------|---------------|
| fck (kgf/cm²)                 | Ecs (kgf/cm²) |
| 250                           | 241500        |

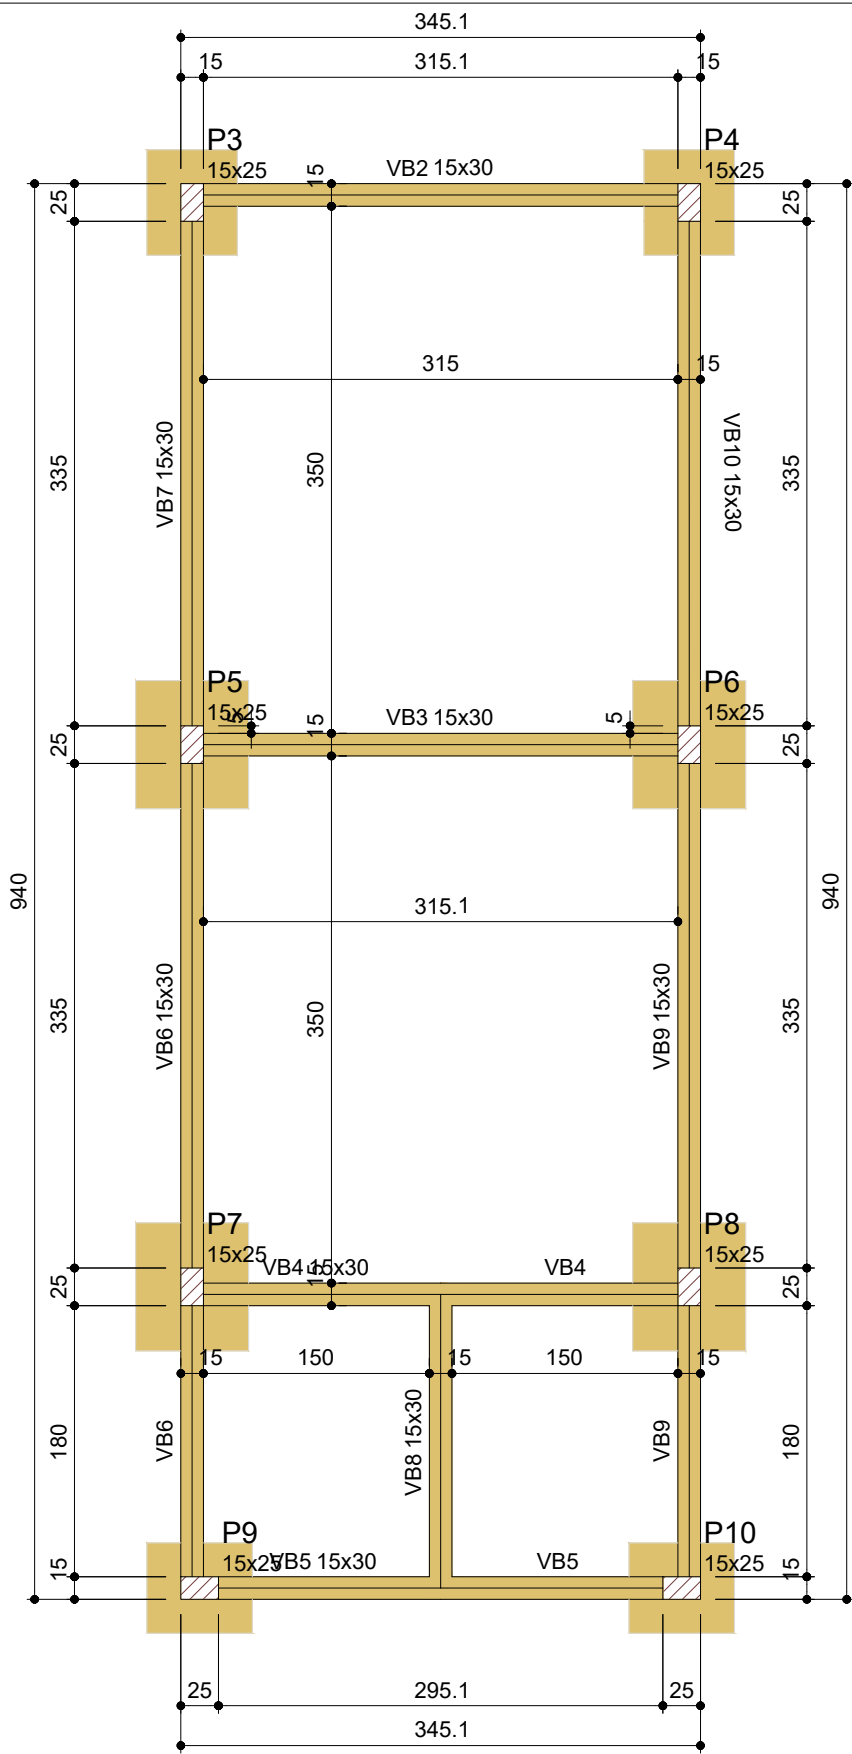

| Legenda dos pilares |                 |
|---------------------|-----------------|
|                     | Pilar que passa |

| Legenda das vigas e paredes |      |
|-----------------------------|------|
|                             | Viga |

PROPRIETÁRIO: PREFEITURA MUNICIPAL DE COREMAS - PB  
**LINCOLN CARTAXO DE LIRA JÚNIOR:06897861405**  
Assinado de forma digital por LINCOLN CARTAXO DE LIRA JÚNIOR:06897861405  
Dados: 2025.08.08 13:33:38 -03'00'

PROJETO: LINCOLN CARTAXO DE LIRA JÚNIOR CREA 160.814.689-8

CONSTRUÇÃO:

FOLHA 01/12  
PROJETO: CONSTRUÇÃO DE GINÁSIO POLIESPORTIVO  
CONVENIENTE: PREFEITURA MUNICIPAL DE COREMAS - PB  
CONVENIADO: MUNICÍPIO DE COREMAS - PB  
LOCALIDADE: COREMAS - PB

|         | DATA     | RESPONSÁVEL     | RUBRICA | DADOS |
|---------|----------|-----------------|---------|-------|
| DESENHO | AGO/2025 | LINCOLN CARTAXO |         |       |
| CÓPIA   |          |                 |         |       |
| VISTO   |          |                 |         |       |

| ESCALAS  | DESENHOS                                                       | CONVÊNIO          |
|----------|----------------------------------------------------------------|-------------------|
| Indicada | - Planta de Locação<br>- Forma do Pavimento Fundação (Nível 0) | GOVERNO DO ESTADO |
|          |                                                                | ARQUIVO           |

Aprovações:



Av. Gov. Flávio Ribeiro Coutinho, 500, sl. 601  
Jardim Oceania, 58037-005 - João Pessoa (PB)  
Tel +55 (83) 99924.4447  
e-mail: contato@lclprojetos.com