


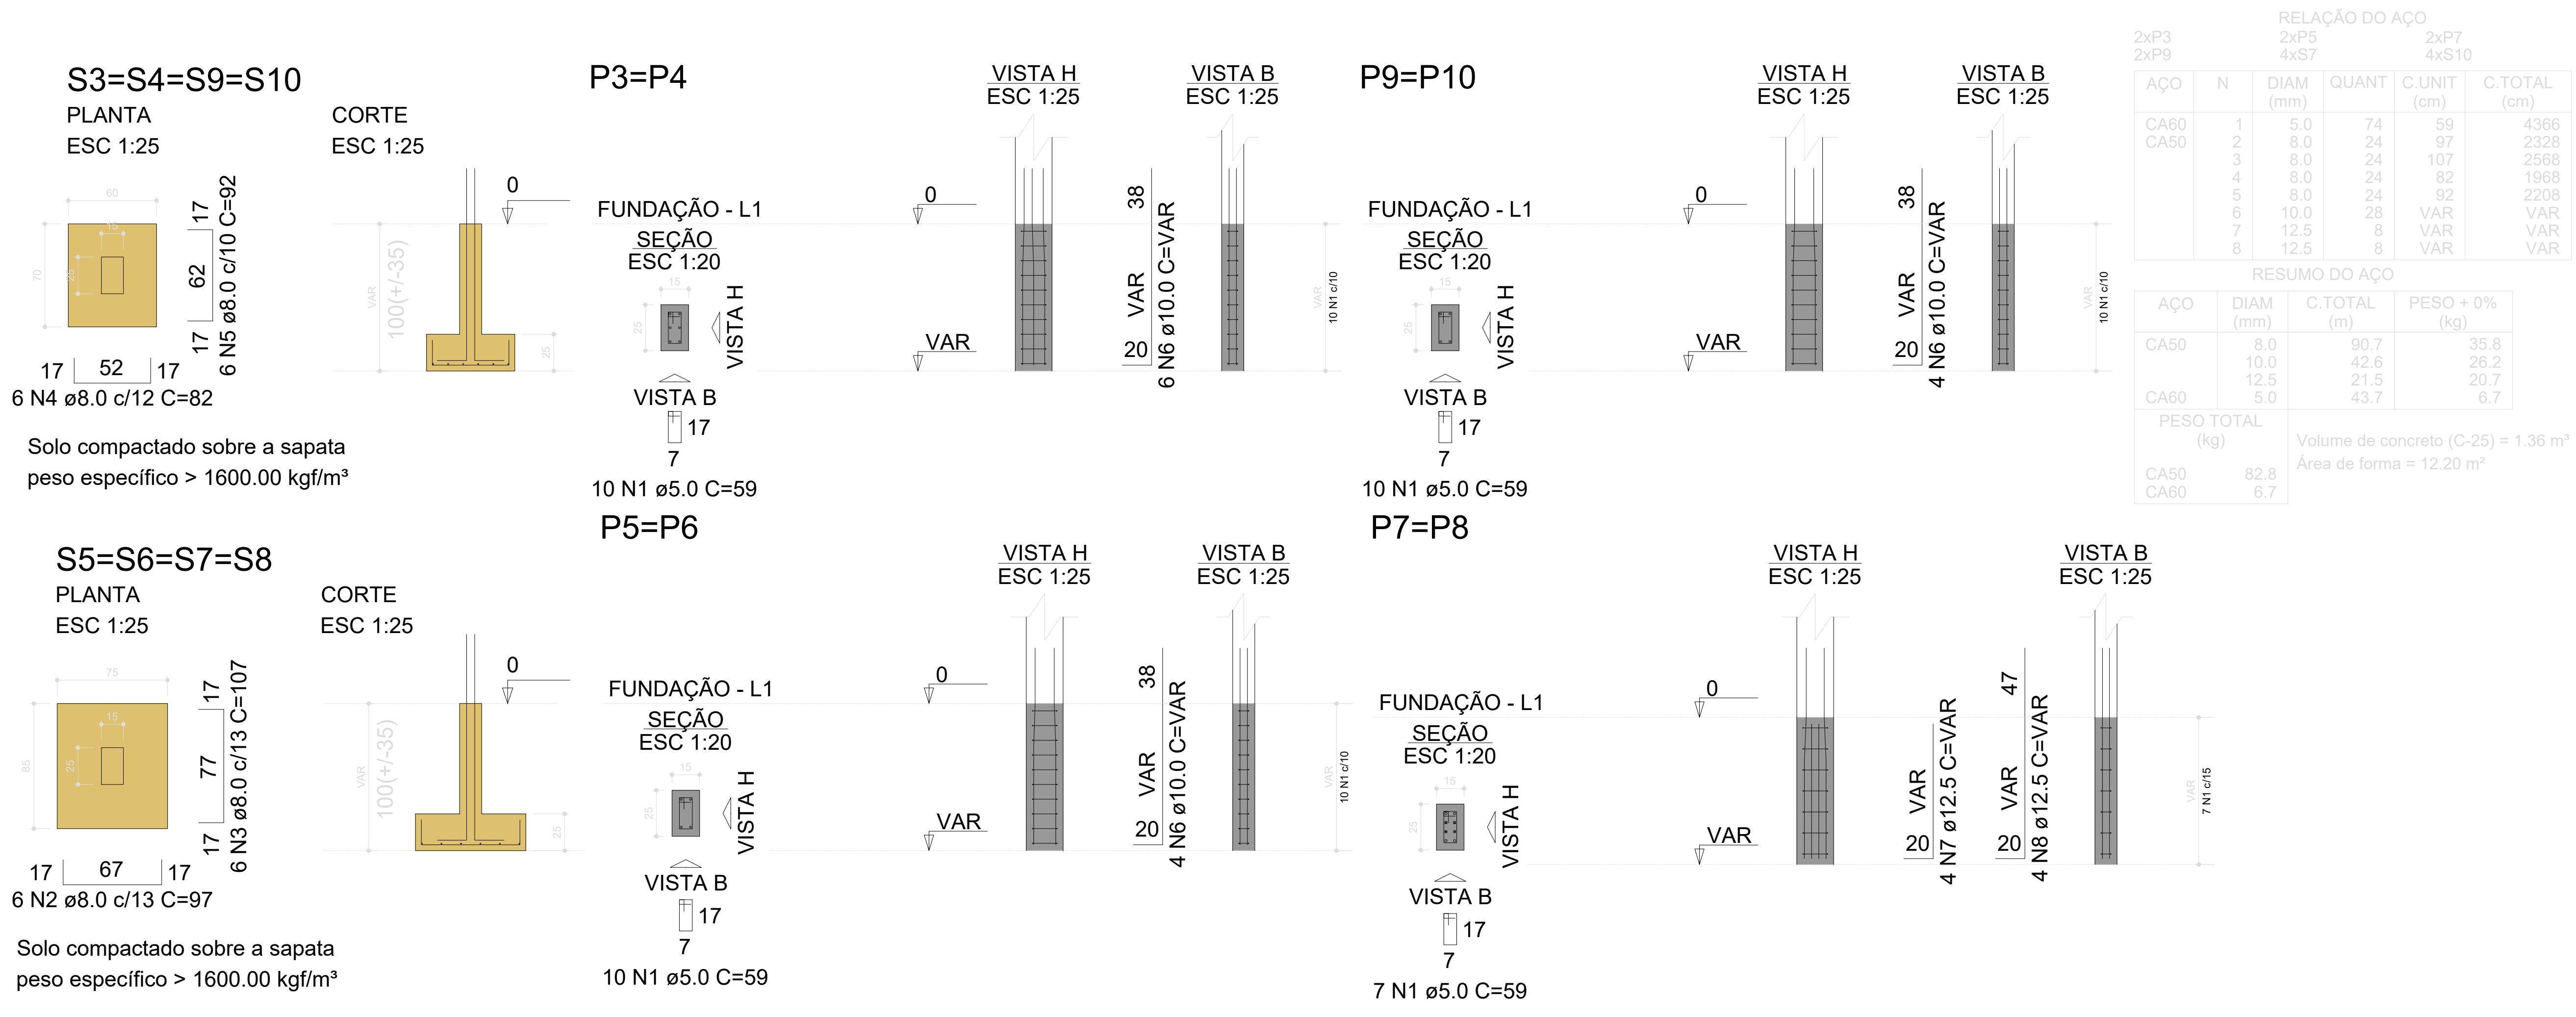

P7=P8

FUNDAÇÃO - L1

SEÇÃO

ESC 1:20

VISTA H

VISTA B

VISTA H

ESC 1:25

VISTA B

ESC 1:25

RELAÇÃO DO AÇO					
2xP3 2xP9		2xP5 4xS7		2xP7 4xS10	
AÇO	N	DIAM (mm)	QUANT	C.UNIT (cm)	C.TOTAL (cm)
CA60 CA50	1	5.0	74	59	4366
	2	8.0	24	97	2328
	3	8.0	24	107	2568
	4	8.0	24	82	1968
	5	8.0	24	92	2208
	6	10.0	28	VAR	VAR
	7	12.5	8	VAR	VAR
	8	12.5	8	VAR	VAR
RESUMO DO AÇO					
AÇO	DIAM (mm)	C.TOTAL (m)	PESO + 0% (kg)		
CA50	8.0	90.7	35.8		
	10.0	42.6	26.2		
	12.5	21.5	20.7		
CA60	5.0	43.7	6.7		
PESO TOTAL (kg)		Volume de concreto (C-25) = 1.36 m³ Área de forma = 12.20 m²			
CA50	82.8				
CA60	6.7				

PROPRIETÁRIO: PREFEITURA MUNICIPAL DE COREMAS - PB

PROJETO: LINCOLN CARTAXO DE LIRA JÚNIOR CREA 160.814.689-8

CONSTRUÇÃO:

FOLHA

02/12

PROJETO: CONSTRUÇÃO DE GINÁSIO POLIESPORTIVO

CONVENIENTE: PREFEITURA MUNICIPAL DE COREMAS - PB

CONVENIADO: MUNICÍPIO DE COREMAS - PB

LOCALIDADE: COREMAS - PB

	DATA	RESPONSÁVEL	RUBRICA	DADOS
DESENHO	AGO/2025	LINCOLN CARTAXO		
CÓPIA				
VISTO				

ESCALAS

Indicada

DESENHOS

- Fundações

CONVÊNIO

GOVERNO DO ESTADO

ARQUIVO

Aprovações:

LCL PROJETOS

Av. Gov. Flávio Ribeiro Coutinho, 500, sl. 601
Jardim Oásia, 59037-005 - João Pessoa (PB)
Tel +55 (83) 99924.4447
e-mail: contato@lclprojetos.com