




VB2

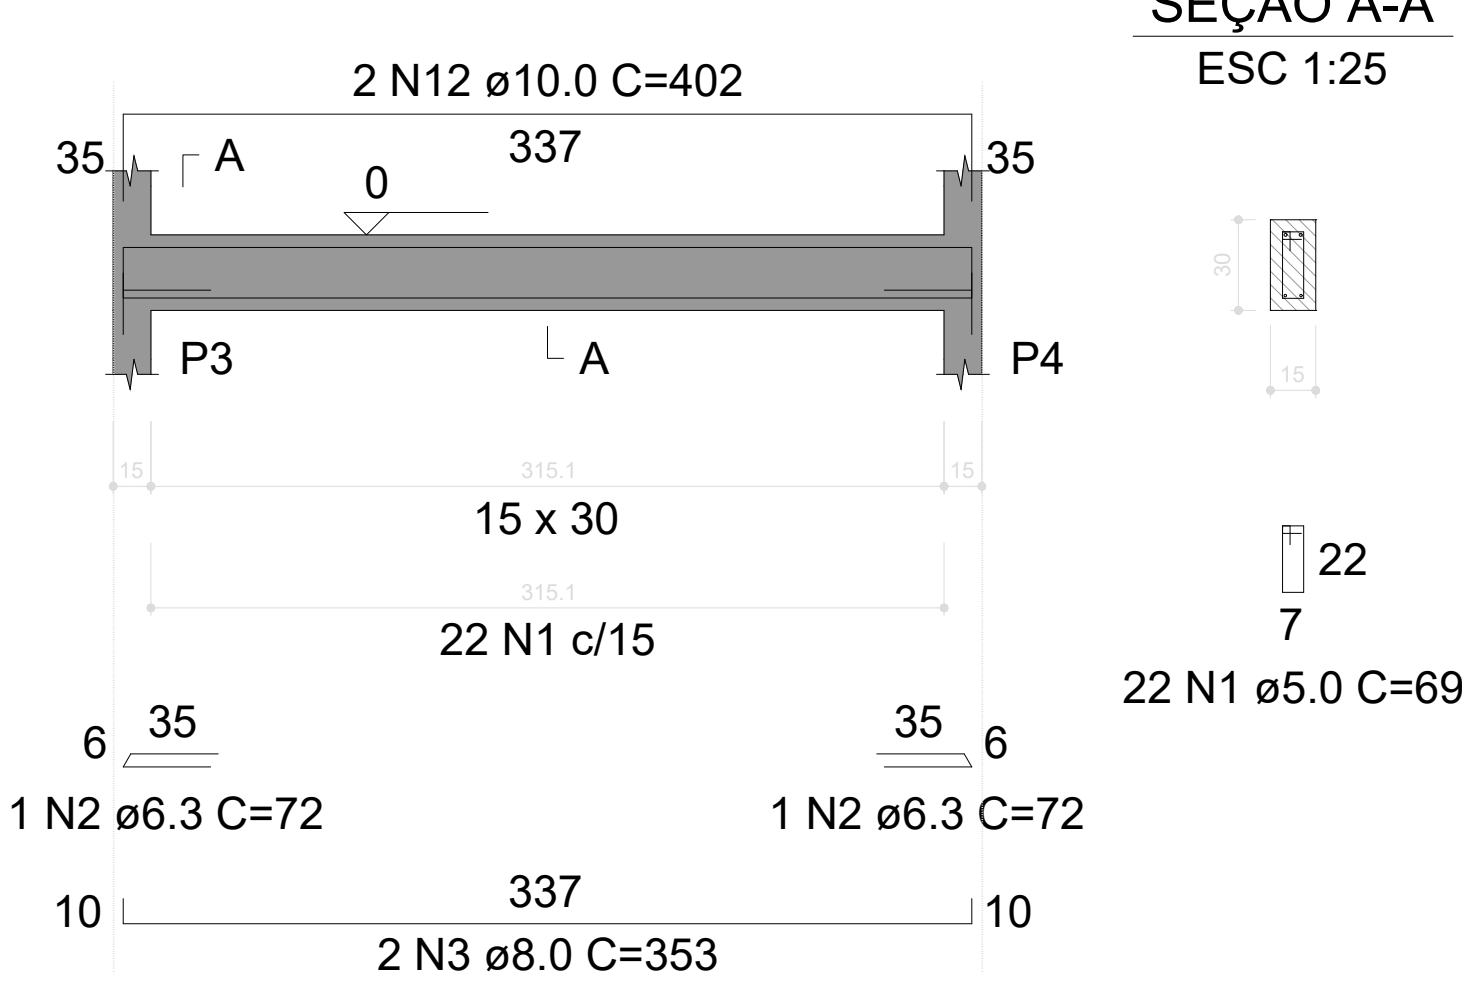


VB3

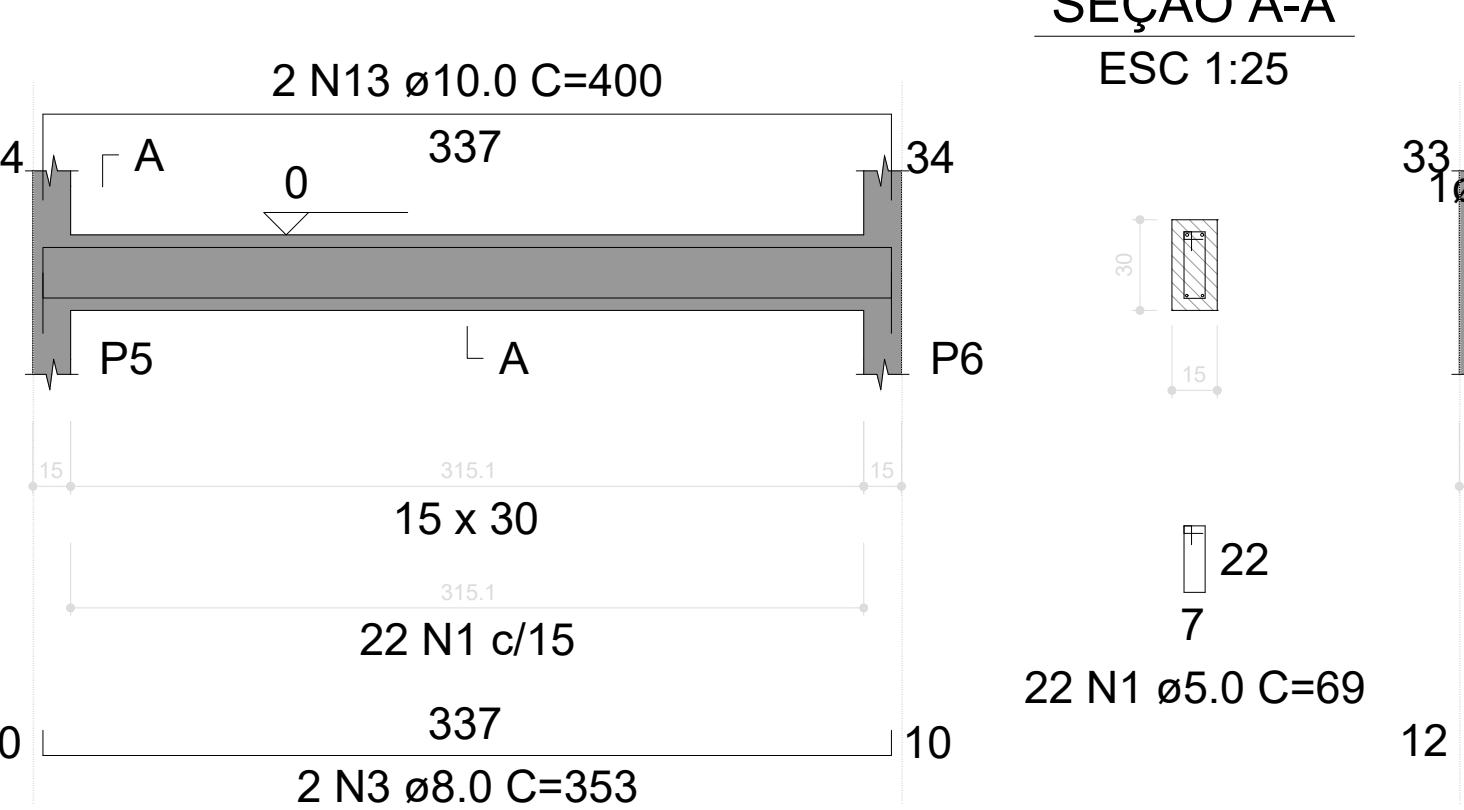


VB4

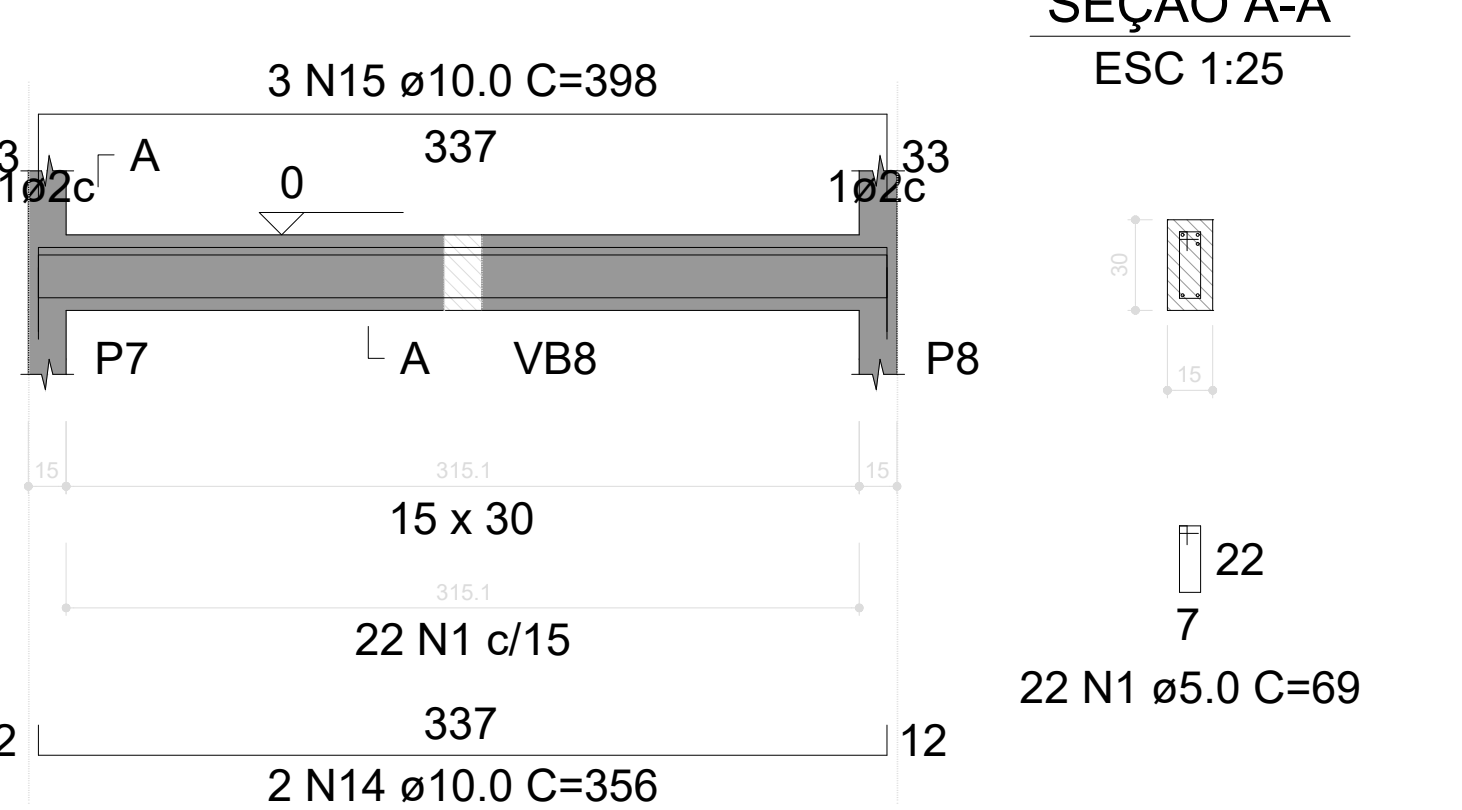


VB5

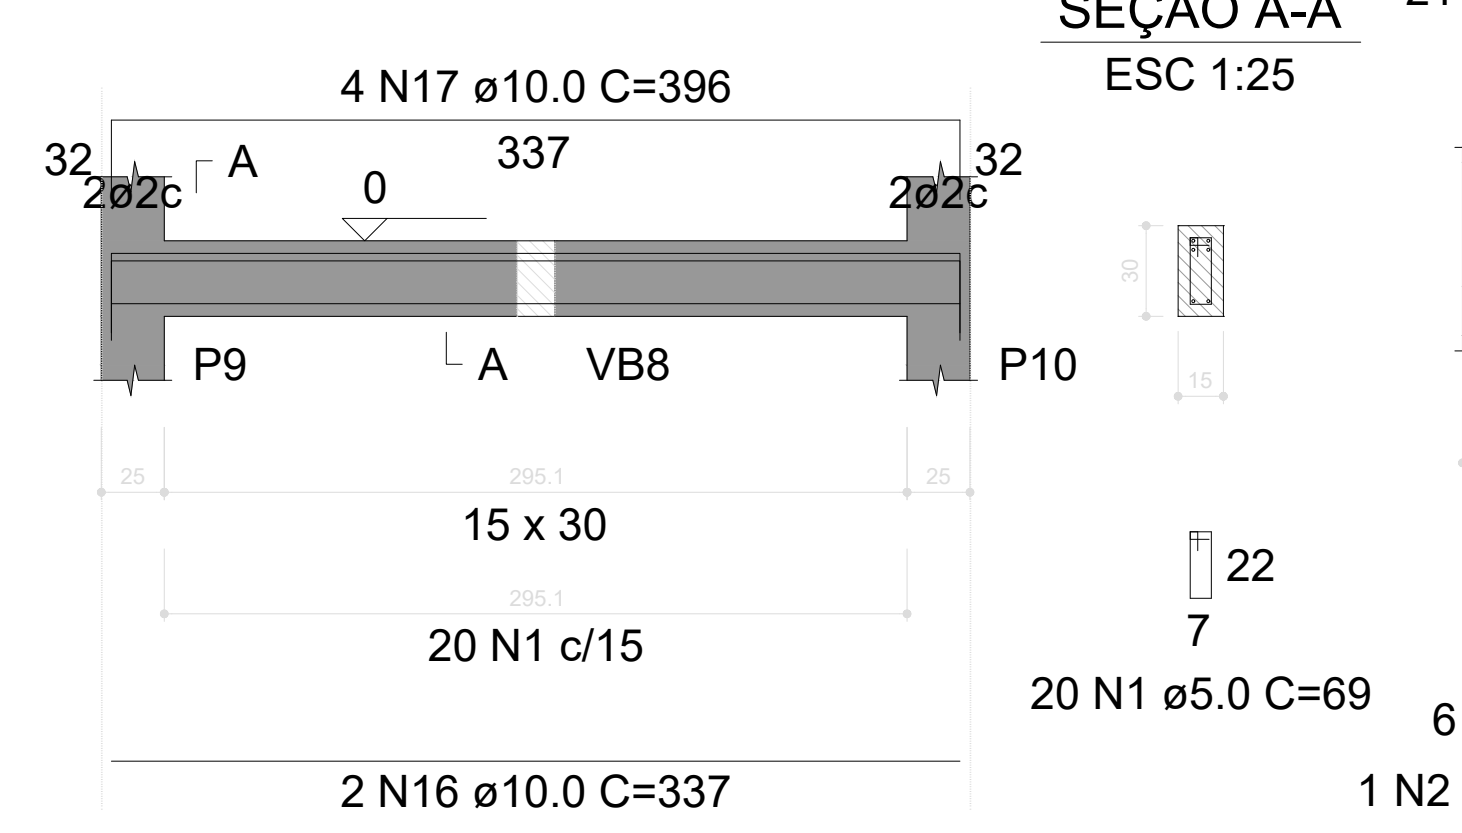


VB6

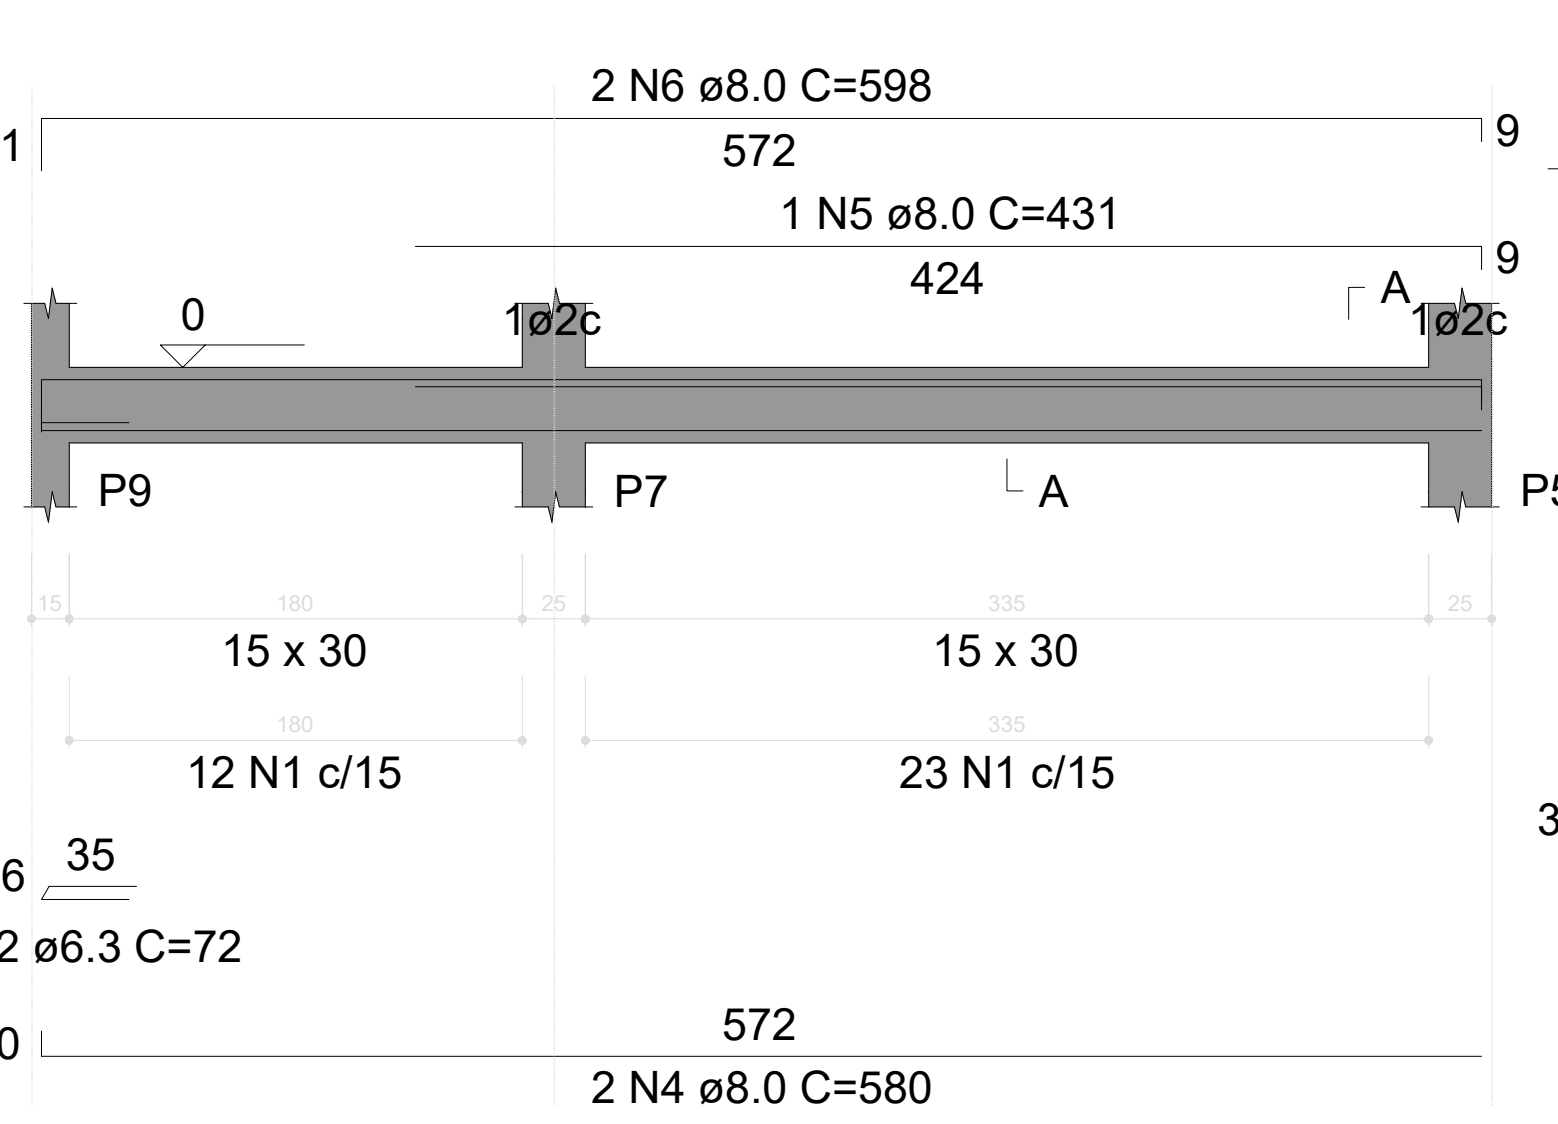


VB7

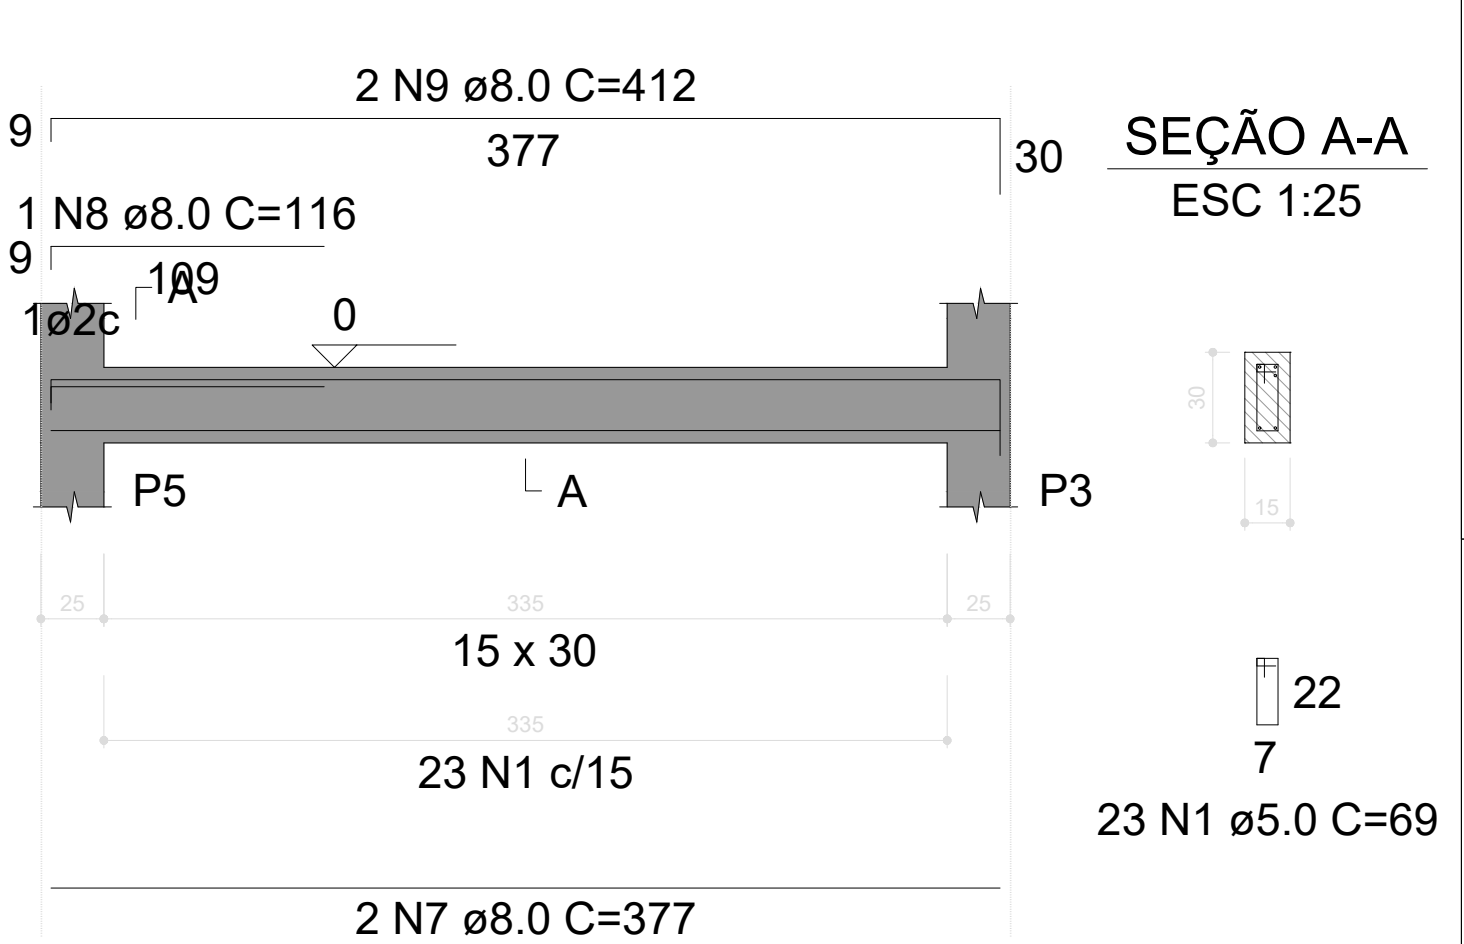


VB8

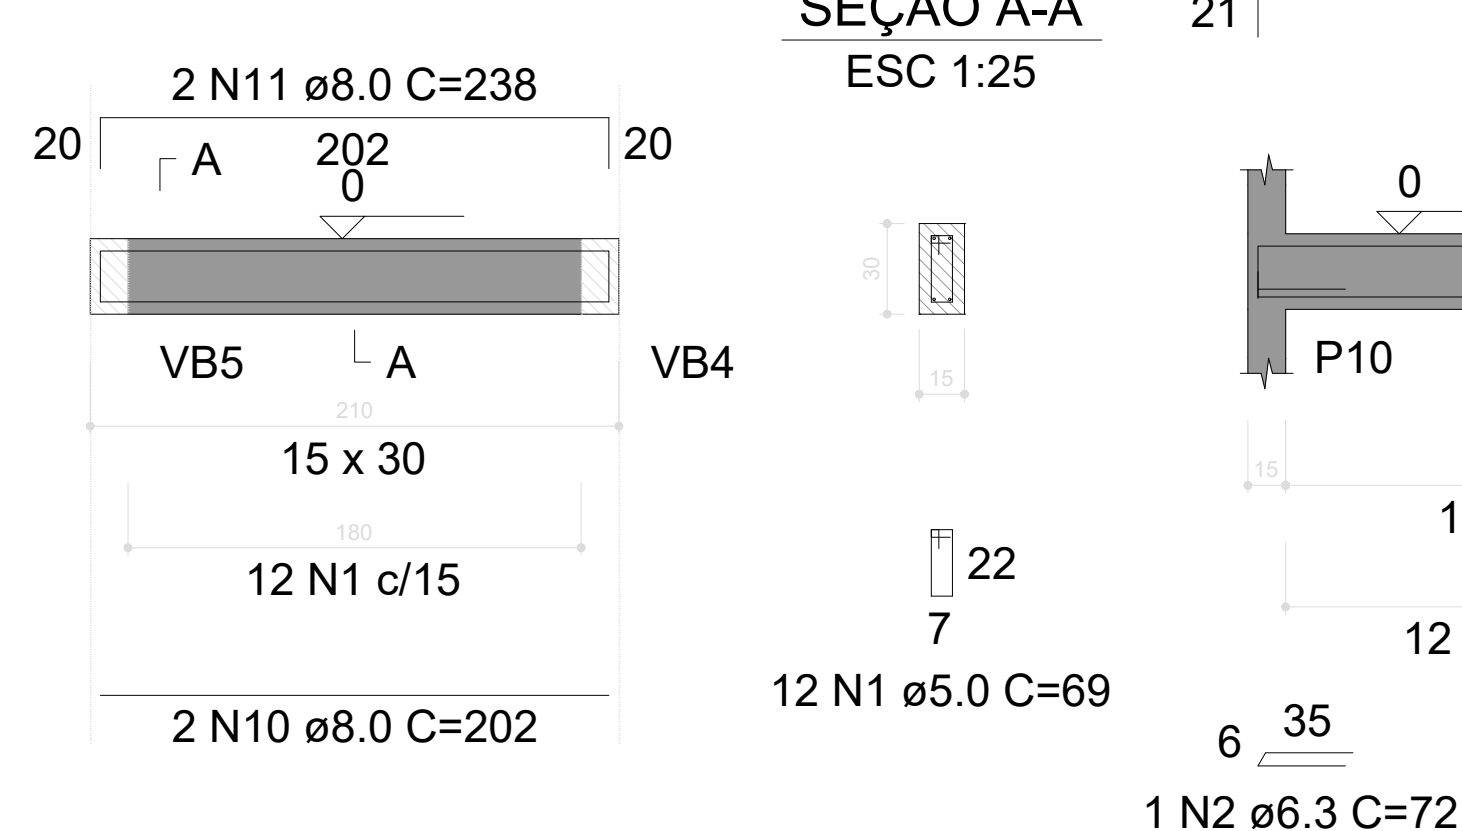

VB9

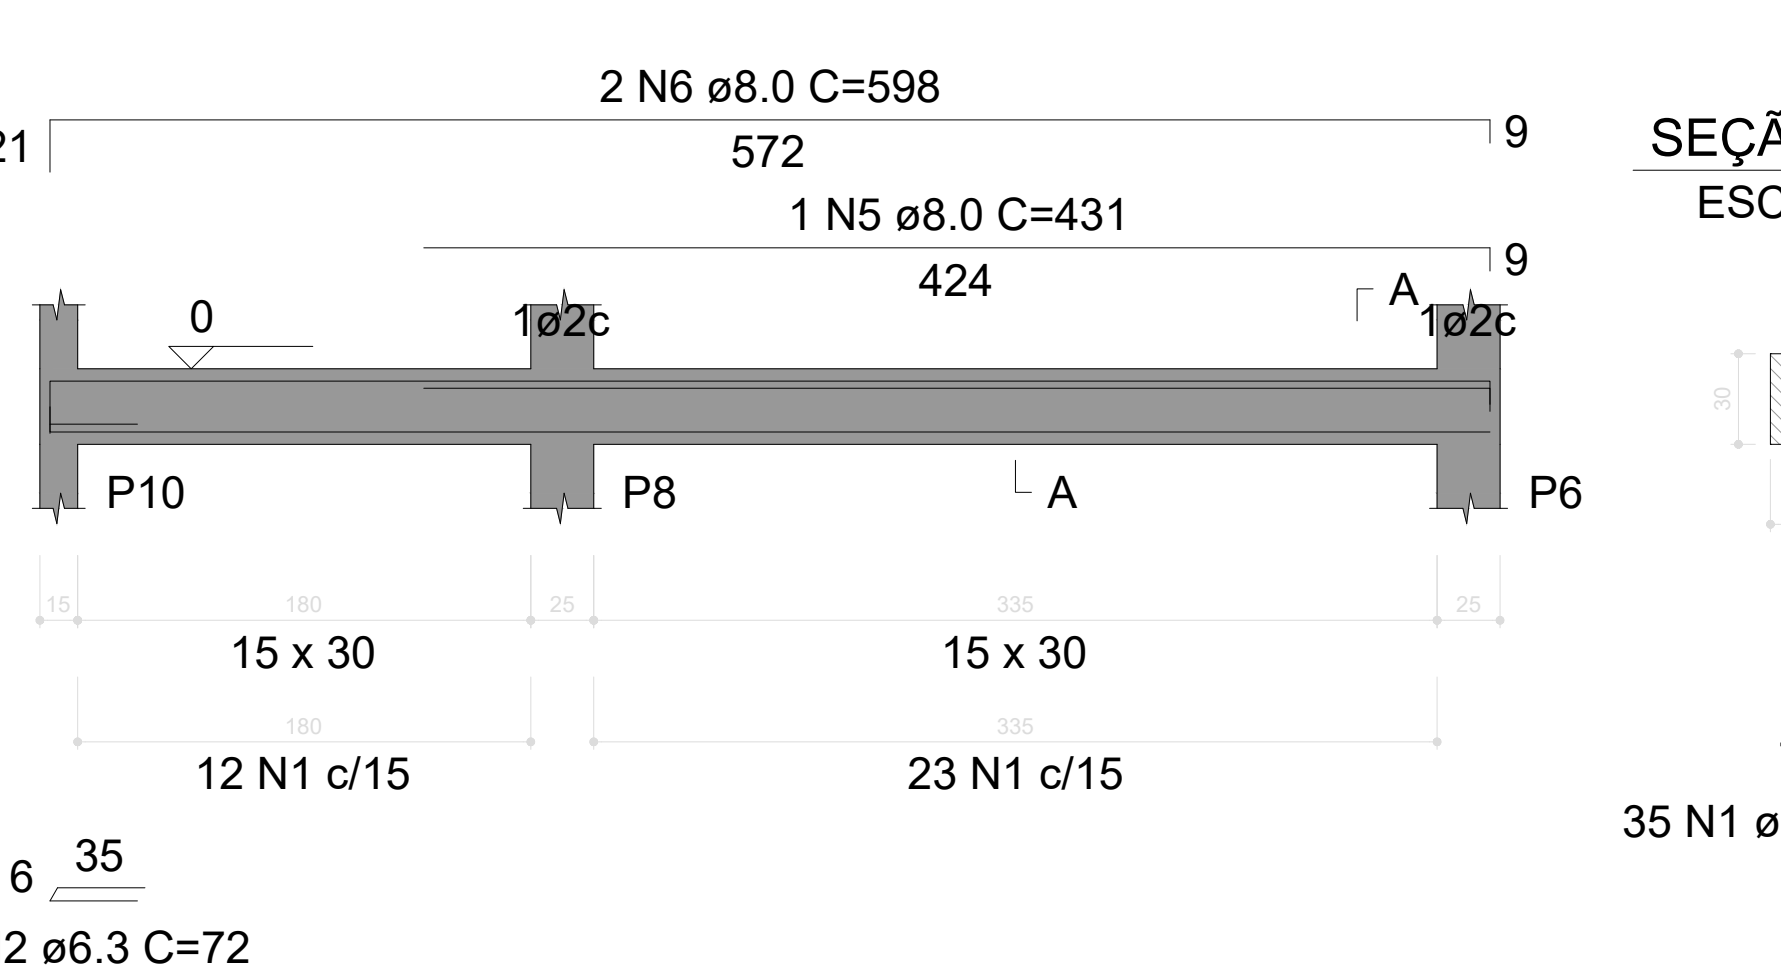

VB10

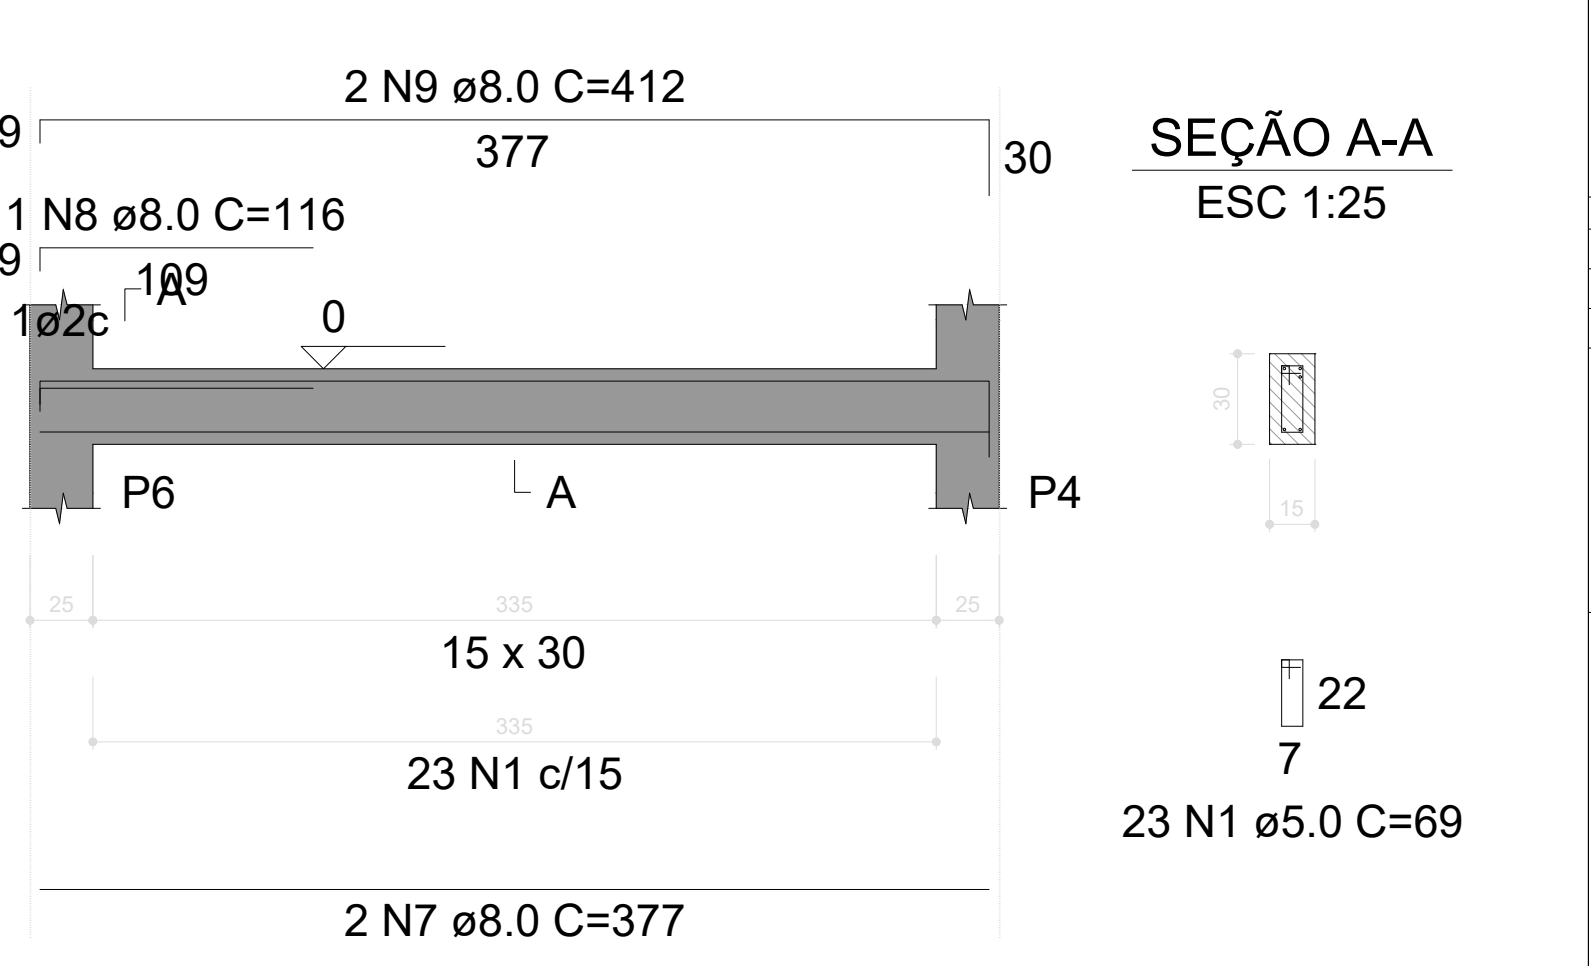

RELAÇÃO DO AÇO					
AÇO	N	DIAM (mm)	QUANT	VB2	
				VB3	
				VB4	
				VB7	
CA60	2	6.3	4	VB8	
				VB9	
				VB10	
CA50	1	5.0	214	69	14766
	2	6.3	4	72	288
	3	8.0	4	353	1412
	4	8.0	4	580	2320
	5	8.0	2	431	862
	6	8.0	4	598	2392
	7	8.0	4	377	1508
	8	8.0	2	116	232
	9	8.0	4	412	1648
	10	8.0	2	202	404
	11	8.0	2	238	476
	12	10.0	2	402	804
	13	10.0	2	400	800
	14	10.0	2	356	712
	15	10.0	3	398	1194
	16	10.0	2	337	674
	17	10.0	4	396	1584

RESUMO DO AÇO			
AÇO	DIAM (mm)	C.TOTAL (m)	PESO + 0% (kg)
CA50	6.3	2.9	0.7
	8.0	112.5	44.4
	10.0	57.7	35.6
CA60	5.0	147.7	22.8
PESO TOTAL (kg)		Volume de concreto (C-25) = 1.58 m³	
CA50	80.7	Área de forma = 26.40 m²	
CA60	22.8		

PROPRIETÁRIO:	PREFEITURA MUNICIPAL DE COREMAS - PB
PROJETO:	LINCOLN CARTAXO DE LIRA JÚNIOR CREA 160.814.689-8
CONSTRUÇÃO:	

FOLHA	03/12	PROJETO:	CONSTRUÇÃO DE GINÁSIO POLIESPORTIVO
CONVENIENTE:	PREFEITURA MUNICIPAL DE COREMAS - PB	CONVENIADO:	MUNICÍPIO DE COREMAS - PB
LOCALIDADE:	COREMAS - PB	CONVÊNIO	GOVERNO DO ESTADO
DESENHO	DATA	RESPONSÁVEL	RUBRICA
DESENHO	AGO/2025	LINCOLN CARTAXO	
CÓPIA			
VISTO			
ESCALAS	DESENHOS	CONVÊNIO	GOVERNO DO ESTADO
Indicada	- Vigas Baldrames	ARQUIVO	