


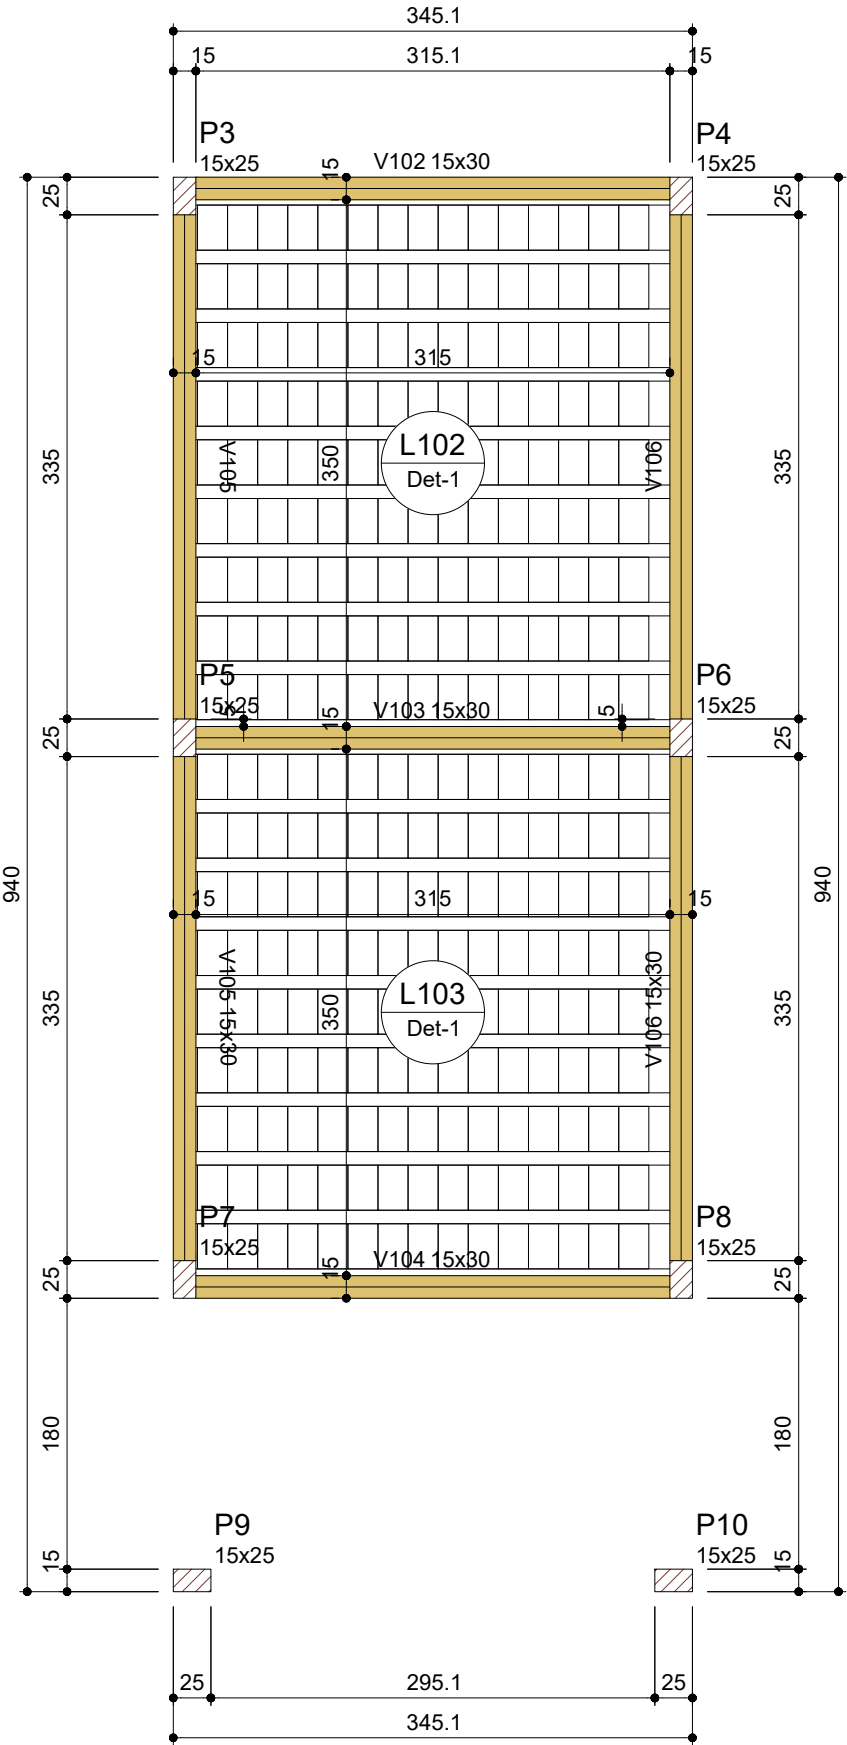

Forma do pavimento Térreo (Nível 290)
escala 1:50

Vigas			
Nome	Seção (cm)	Elevação (cm)	Nível (cm)
V102	15x30	0	290
V103	15x30	0	290
V104	15x30	0	290
V105	15x30	0	290
V106	15x30	0	290

Pilares			
Nome	Seção (cm)	Elevação (cm)	Nível (cm)
P3	15x25	0	290
P4	15x25	0	290
P5	15x25	0	290
P6	15x25	0	290
P7	15x25	0	290
P8	15x25	0	290
P9	15x25	0	290
P10	15x25	0	290

Legenda dos pilares	
	Pilar que passa

Legenda das vigas e paredes	
	Viga


Características dos materiais	
fck (kgf/cm²)	Ecs (kgf/cm²)
250	241500

Lajes								
Dados						Sobrecarga (kgf/m²)		
Nome	Tipo	Altura (cm)	Elevação (cm)	Nível (cm)	Peso próprio (kgf/m²)	Adicional	Acidental	Localizada
L102	Treliçada 1D	15	0	290	316	50	50	-
L103	Treliçada 1D	15	0	290	316	50	50	-

Área de lajes			
Tipo	Altura (cm)	Bloco de Enchimento	Área (m²)
Treliçada 1D	15	B10/30/20	22.05

Blocos de enchimento						
Detalhe	Tipo	Nome	Dimensões(cm)			Quantidade
			hb	bx	by	
1	Lajota cerâmica	B10/30/20	10	30	20	270

Detalhe 1 (esc. 1:30)

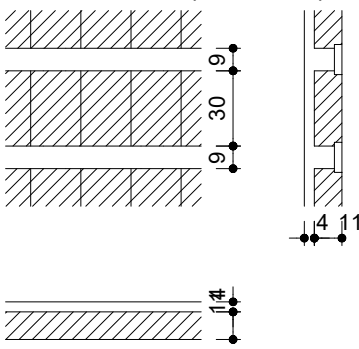

PROPRIETÁRIO: PREFEITURA MUNICIPAL DE COREMAS - PB

LINCOLN CARTAXO DE LIRA JUNIOR:06897861405

Assinado de forma digital por LINCOLN CARTAXO DE LIRA JUNIOR:06897861405
Dados: 2025.08.08 13:32:39 -03'00'

PROJETO: LINCOLN CARTAXO DE LIRA JÚNIOR CREA 160.814.689-8

CONSTRUÇÃO:

FOLHA
04/12

PROJETO: CONSTRUÇÃO DE GINÁSIO POLIESPORTIVO
CONVENIENTE: PREFEITURA MUNICIPAL DE COREMAS - PB
CONVENIADO: MUNICÍPIO DE COREMAS - PB
LOCALIDADE: COREMAS - PB

	DATA	RESPONSÁVEL	RUBRICA	DADOS
DESENHO	AGO/2025	LINCOLN CARTAXO		
CÓPIA				
VISTO				
ESCALAS	DESENHOS	CONVÊNIO		
Indicada	- Forma do Pavimento Térreo (Nível 290)	GOVERNO DO ESTADO		
		ARQUIVO		

Aprovações:

LCL PROJETOS

Av. Gov. Flávio Ribeiro Coutinho, 500, sl. 601
Jardim Oceania, 58037-005 - João Pessoa (PB)
Tel +55 (83) 99924.4447
e-mail: contato@lclprojetos.com