


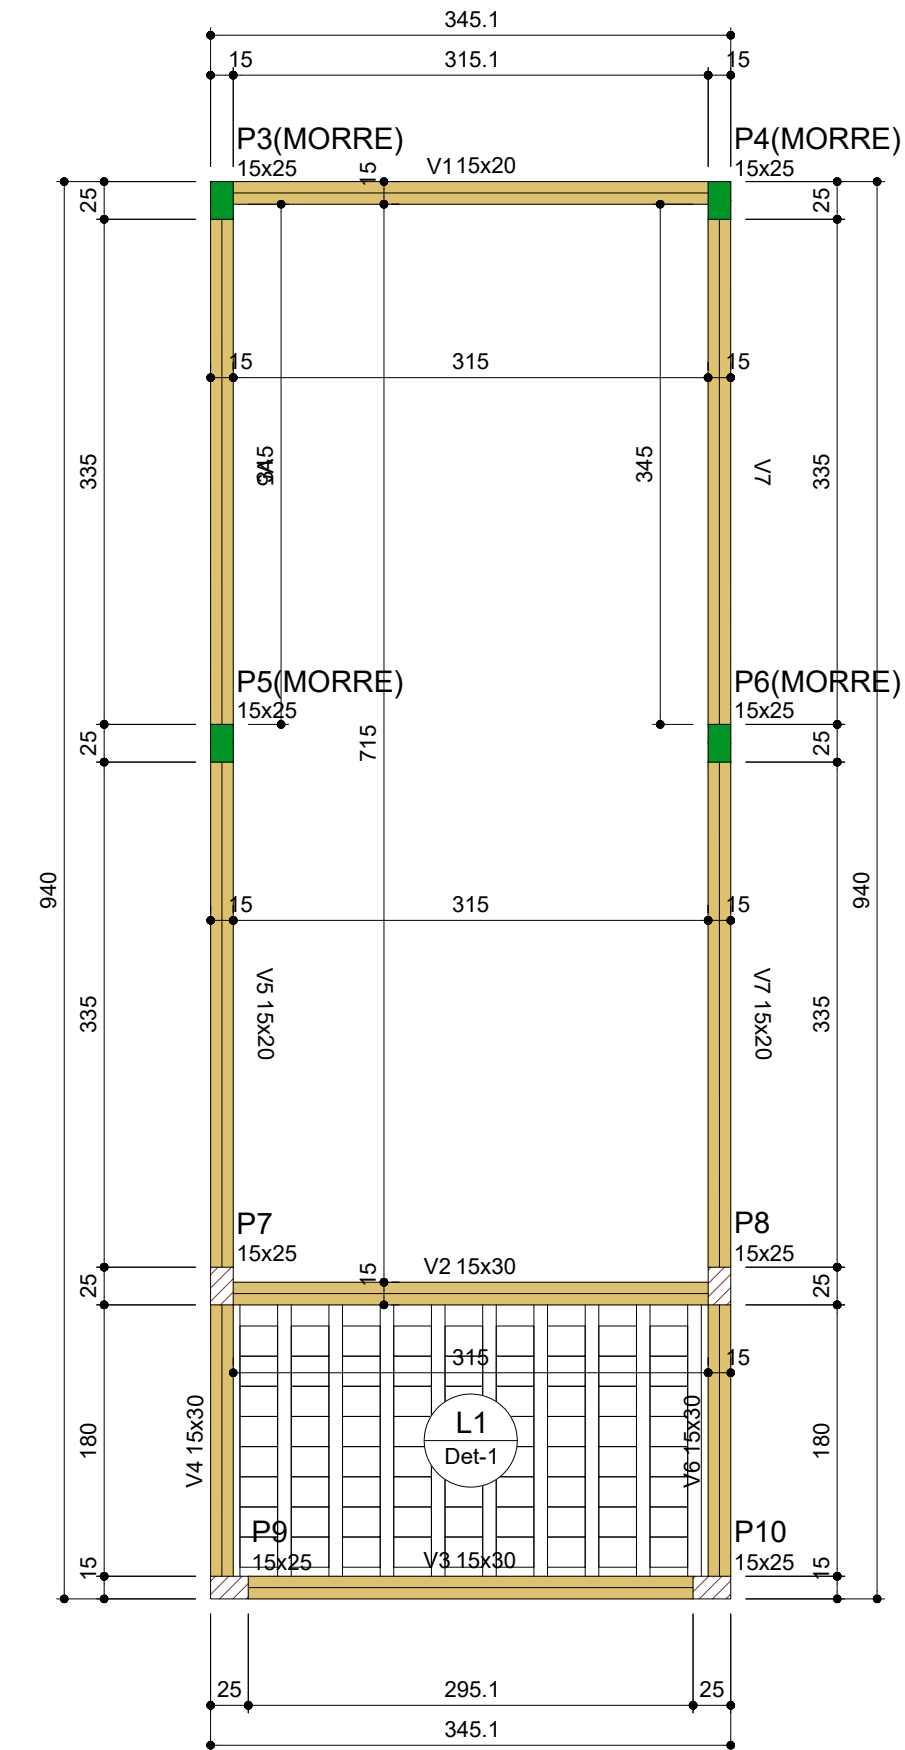

Forma do pavimento Fundo de Caixa d'água (Nível 390)
escala 1:50

Vigas			
Nome	Seção (cm)	Elevação (cm)	Nível (cm)
V1	15x20	0	390
V2	15x30	0	390
V3	15x30	0	390
V4	15x30	0	390
V5	15x20	0	390
V6	15x30	0	390
V7	15x20	0	390

Pilares			
Nome	Seção (cm)	Elevação (cm)	Nível (cm)
P3	15x25	0	390
P4	15x25	0	390
P5	15x25	0	390
P6	15x25	0	390
P7	15x25	0	390
P8	15x25	0	390
P9	15x25	0	390
P10	15x25	0	390

Legenda dos pilares	
	Pilar que morre
	Pilar que passa


Legenda das vigas e paredes	
	Viga

Lajes								
Dados						Sobrecarga (kgf/m²)		
Nome	Tipo	Altura (cm)	Elevação (cm)	Nível (cm)	Peso próprio (kgf/m²)	Adicional	Acidental	Localizada
L1	Treliçada 1D	12	0	390	259	342	50	-

Área de lajes				Características dos materiais	
Tipo	Altura (cm)	Bloco de Enchimento	Área (m²)	fck (kgf/cm²)	Ecs (kgf/cm²)
Treliçada 1D	12	B8/25/20	5.67	250	241500

Blocos de enchimento						
Detalhe	Tipo	Nome	Dimensões(cm)			Quantidade
			hb	bx	by	
1	Lajota cerâmica	B8/25/20	8	25	20	72

Detalhe 1 (esc. 1:30)

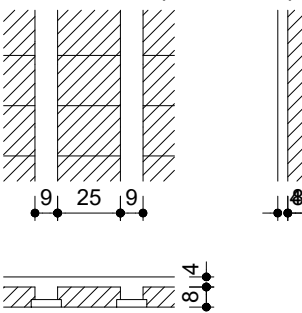

PROPRIETÁRIO: PREFEITURA MUNICIPAL DE COREMAS - PB

PROJETO: LINCOLN CARTAXO DE LIRA JÚNIOR CREA 160.814.689-8

CONSTRUÇÃO:

FOLHA 08/12
PROJETO: CONSTRUÇÃO DE GINÁSIO POLIESPORTIVO
CONVENIENTE: PREFEITURA MUNICIPAL DE COREMAS - PB
CONVENIADO: MUNICÍPIO DE COREMAS - PB
LOCALIDADE: COREMAS - PB

	DATA	RESPONSÁVEL	RUBRICA	DADOS
DESENHO	AGO/2025	LINCOLN CARTAXO		
CÓPIA				
VISTO				

ESCALAS	DESENHOS	CONVÊNIO
Indicada	- Forma do Pavimento Fundo de Caixa d'água (Nível 390)	GOVERNO DO ESTADO
		ARQUIVO

Aprovações:



Av. Gov. Flávio Ribeiro Coutinho, 500, sl. 601
Jardim Oceania, 58037-005 - João Pessoa (PB)
Tel +55 (83) 99924.4447
e-mail: contato@lclprojetos.com