


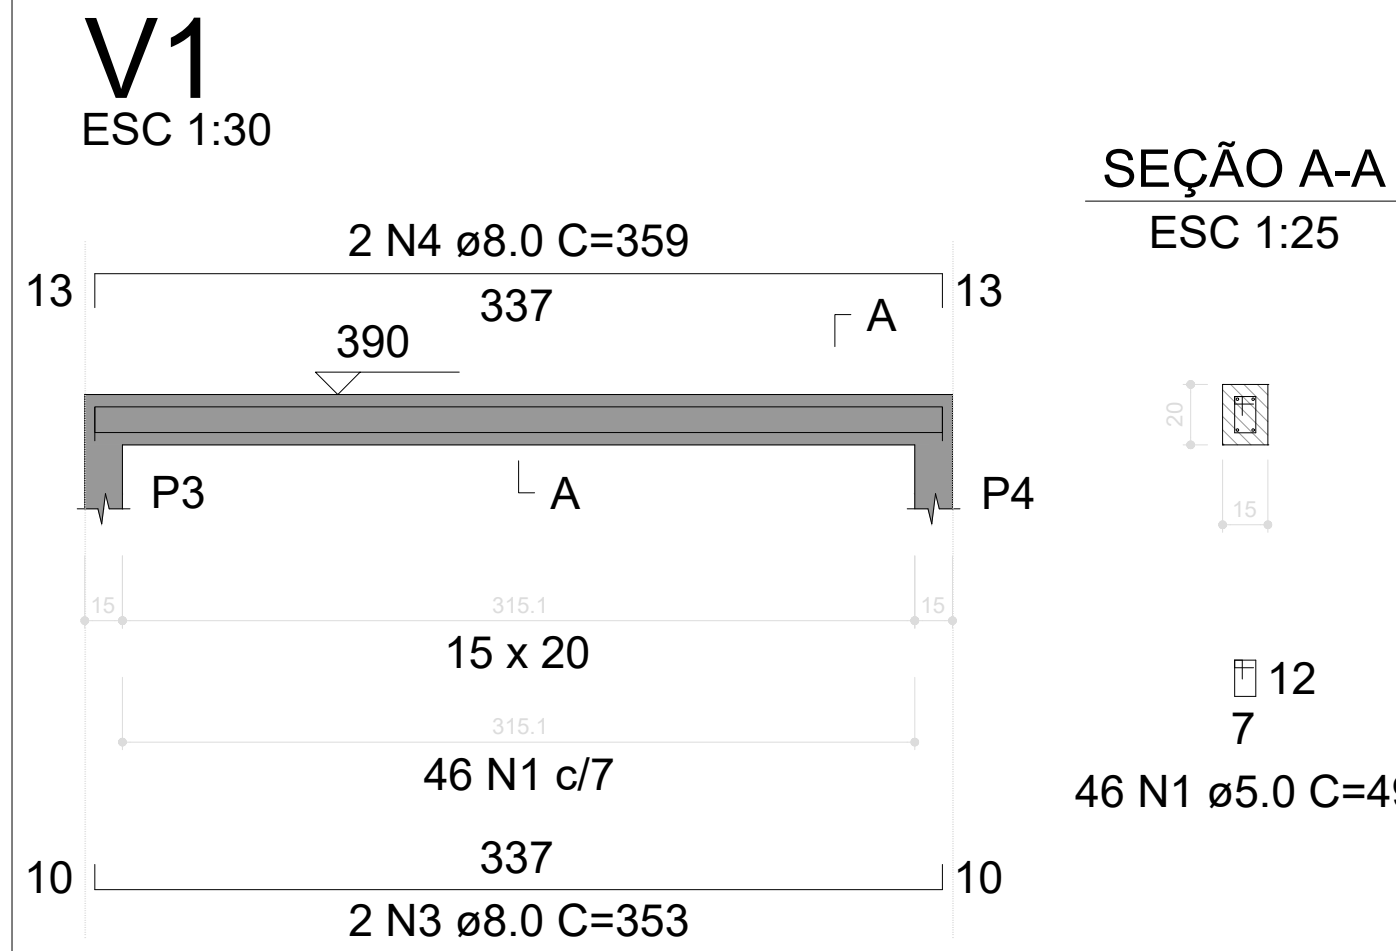


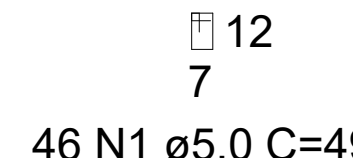



SEÇÃO A-A
ESC 1:25

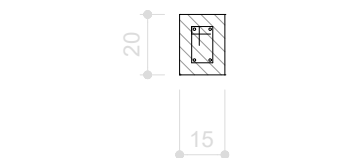


46 N1 ø5.0 C=45

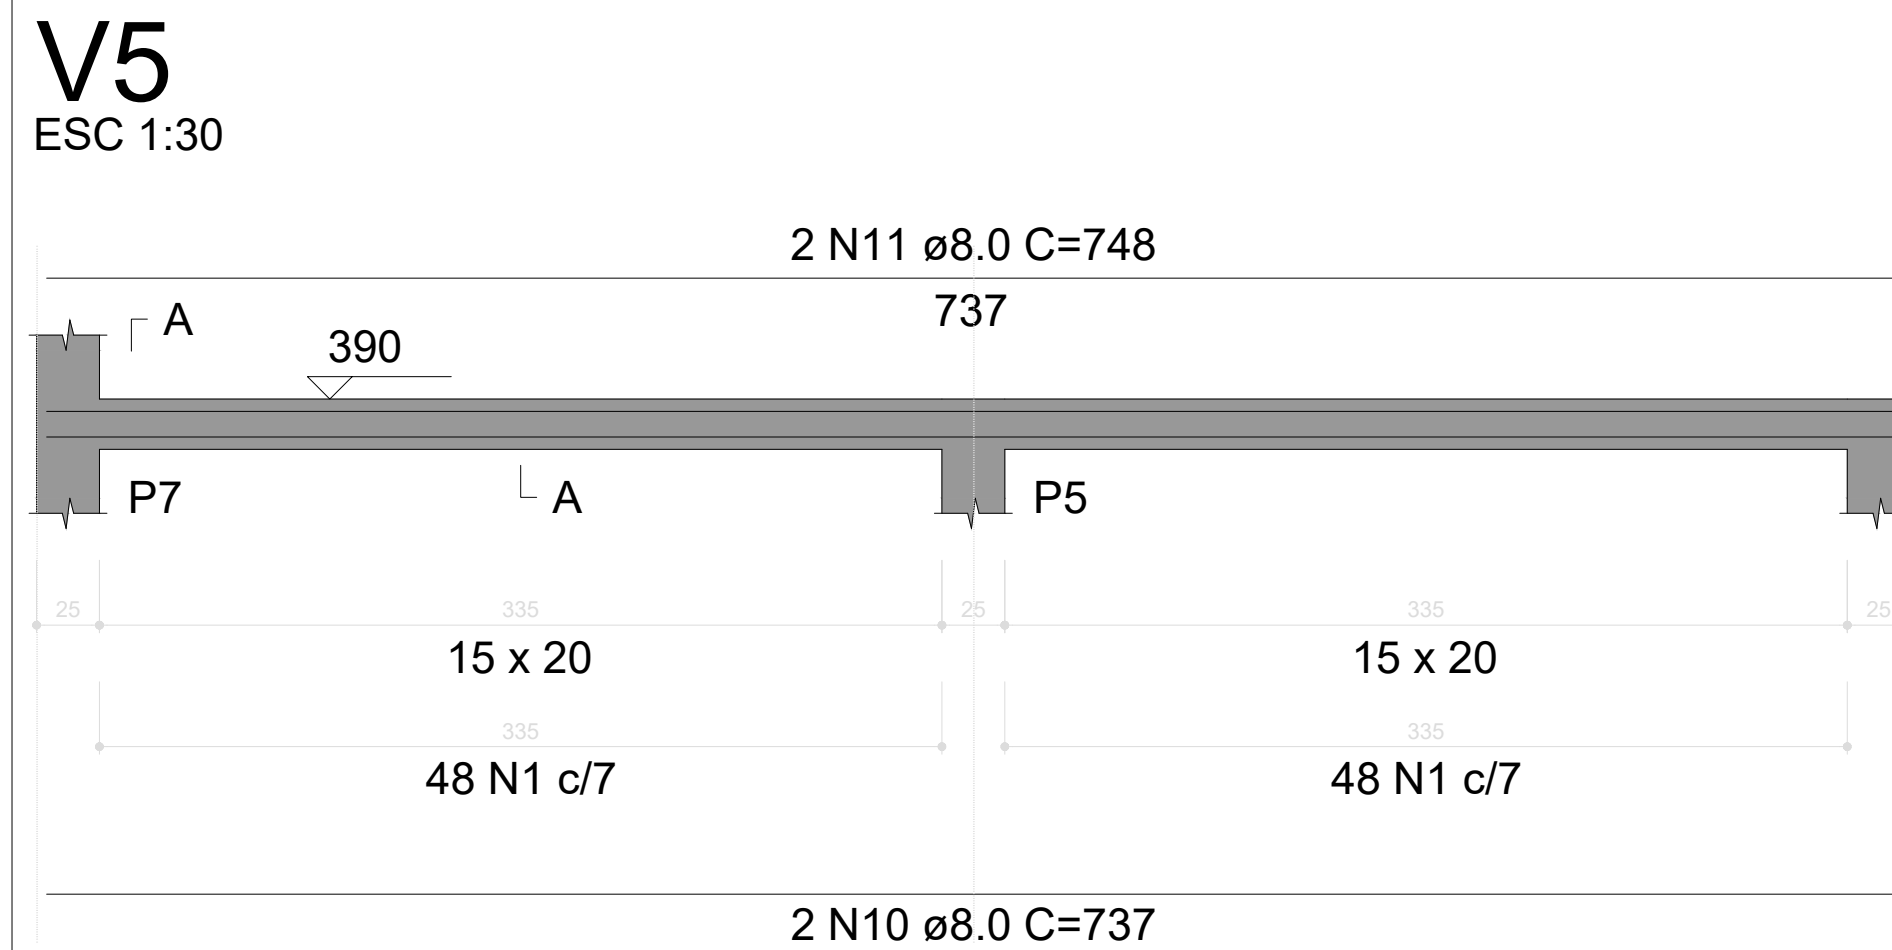



SEÇÃO A-A
ESC 1:25

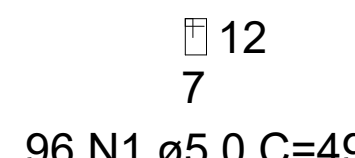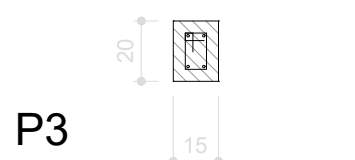


96 N1 ø5.0 C=49

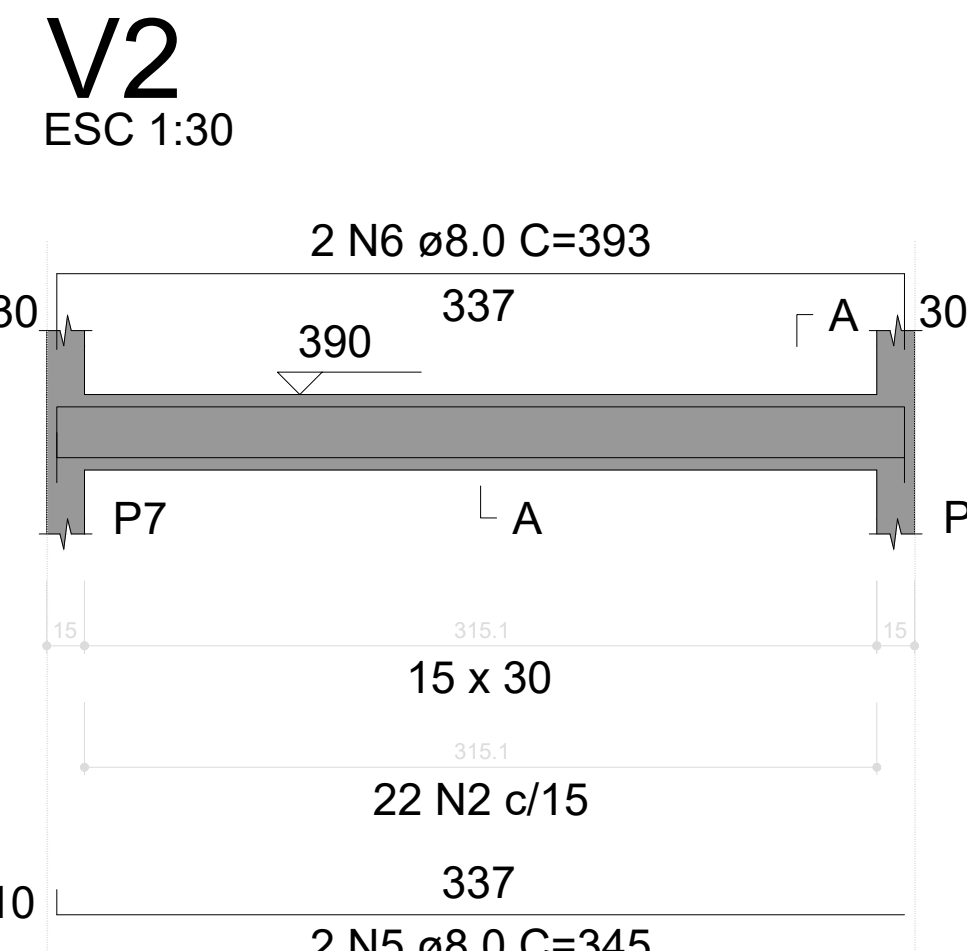



SEÇÃO A-A
ESC 1:25

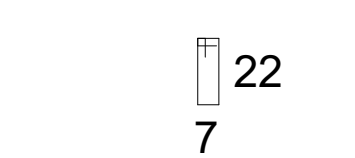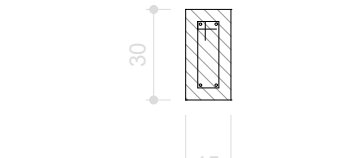


7

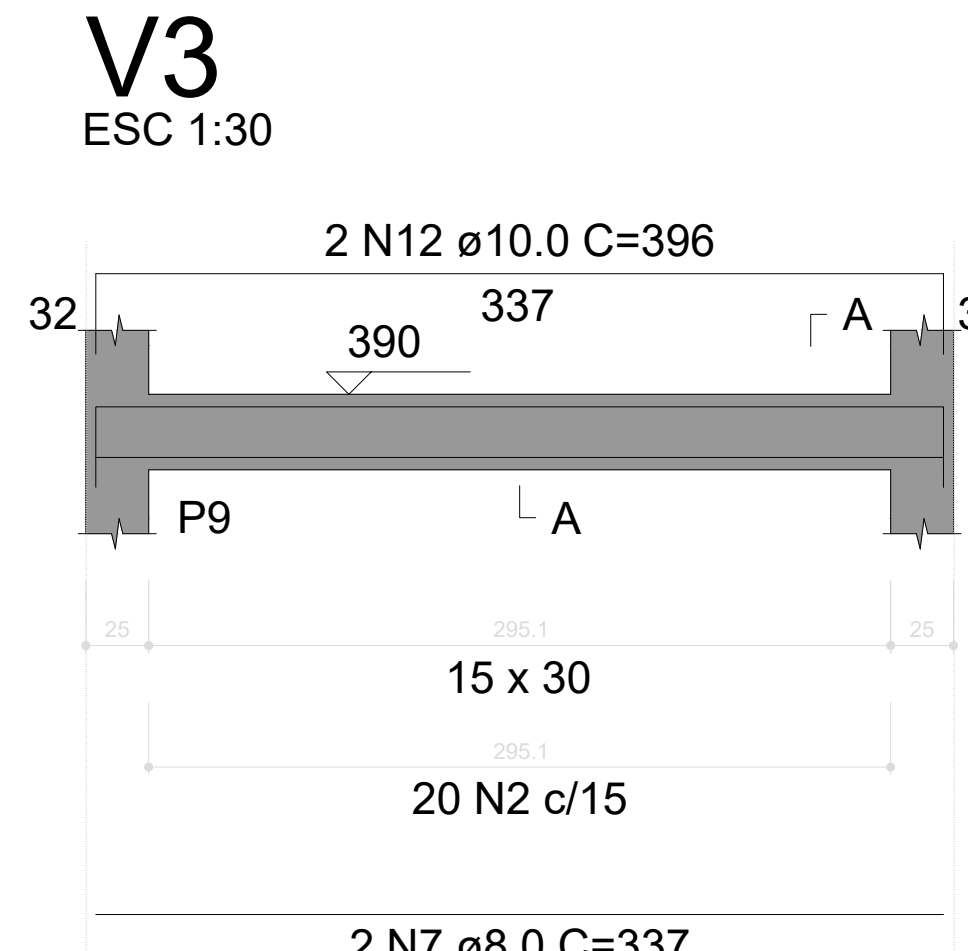



SEÇÃO A-A
ESC 1:25

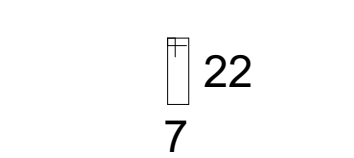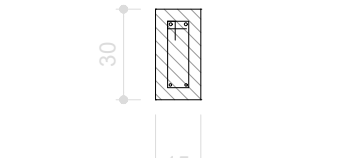

7

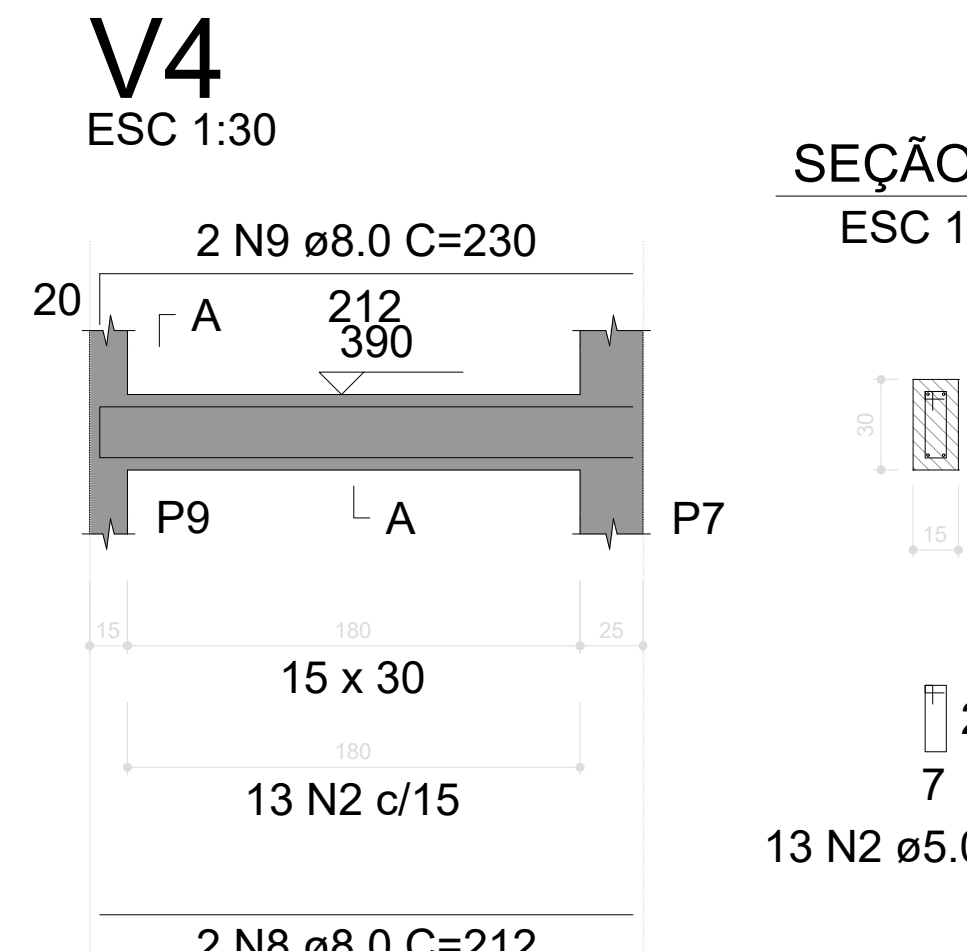

SEÇÃO A-A
ESC 1:25

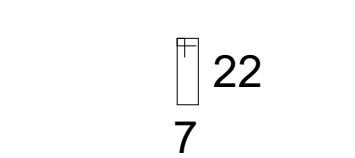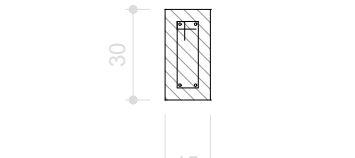

7

RELAÇÃO DO AÇO					
V1		V2		V3	
V4		V5		V6	
V7					
AÇO	N	DIAM (mm)	QUANT	C.UNIT (cm)	C.TOTAL (cm)
CA60	1	5.0	238	49	11662
	2	5.0	67	69	4623
CA50	3	8.0	2	353	706
	4	8.0	2	359	718
	5	8.0	2	345	690
	6	8.0	2	393	786
	7	8.0	2	337	674
	8	8.0	4	212	848
	9	8.0	4	230	920
	10	8.0	4	737	2948
	11	8.0	4	748	2992
	12	10.0	2	396	792

RESUMO DO AÇO			
AÇO	DIAM (mm)	C.TOTAL (m)	PESO + 0% (kg)
CA50	8.0	112.8	44.5
	10.0	7.9	4.9
CA60	5.0	162.8	25.1
PESO TOTAL (kg)			
CA50	49.4		
CA60	25.1		

⁴⁹ Volume de concreto (C-25) = 1.06 m³

Área de forma = 18.57 m²

FOLHA		PROJETO: CONSTRUÇÃO DE GINÁSIO POLIESPORTIVO	
09/12		CONVENIENTE: PREFEITURA MUNICIPAL DE COREMAS - PB	
		CONVENIADO: MUNICÍPIO DE COREMAS - PB	
		LOCALIDADE: COREMAS - PB	
DATA	RESPONSÁVEL	RUBRICA	DADOS
DESENHO	AGO/2025	LINCOLN CARTAXO	
CÓPIA			
VISTO			
ESCALAS	DESENHOS		CONVÊNIO
Indicada	- Vigas Caixa D'água		GOVERNO DO ESTADO
			ARQUIVO

Aprovações: