




Armação positiva das lajes do pavimento Fundo de Caixa d'água (Eixo Y) escala 1:50

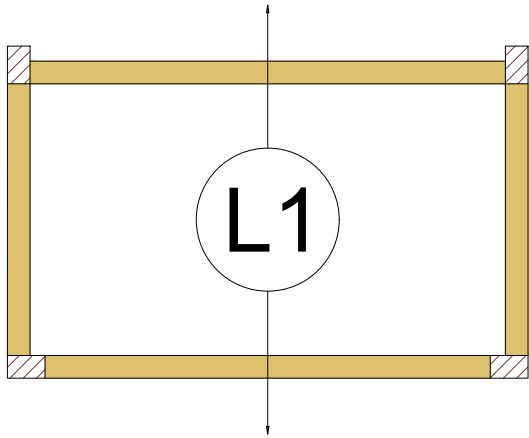


Armação negativa das lajes do pavimento Fundo de Caixa d'água (Eixo X) escala 1:50

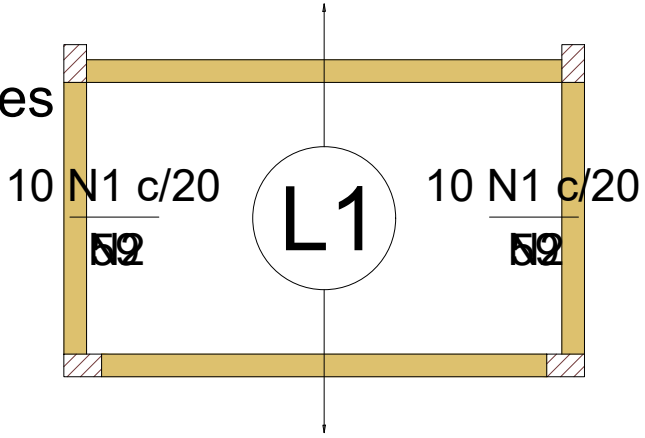

Armação negativa das lajes do pavimento Fundo de Caixa d'água (Eixo Y) escala 1:50

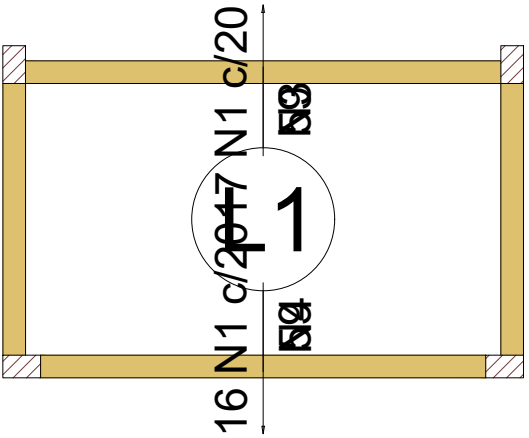


Planta de vigotas pré-moldadas escala 1:50

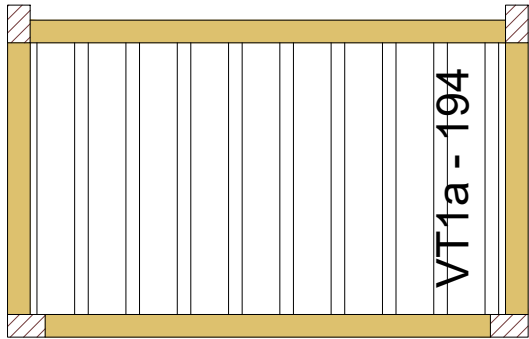

Armaduras de distribuição	
Armadura	Armadura de distribuição
N1	3 N2 ø5.0 c/20 C=197
N1	3 N2 ø5.0 c/20 C=197

Armaduras de distribuição	
Armadura	Armadura de distribuição
N1	3 N3 ø5.0 c/20 C=330
N1	3 N4 ø5.0 c/20 C=313

DETALHE DA ARMADURA DE SUPERIOR DE CONTINUIDADE DA LAJE E MONTAGEM DA ARMADURA DE DISTRIBUIÇÃO

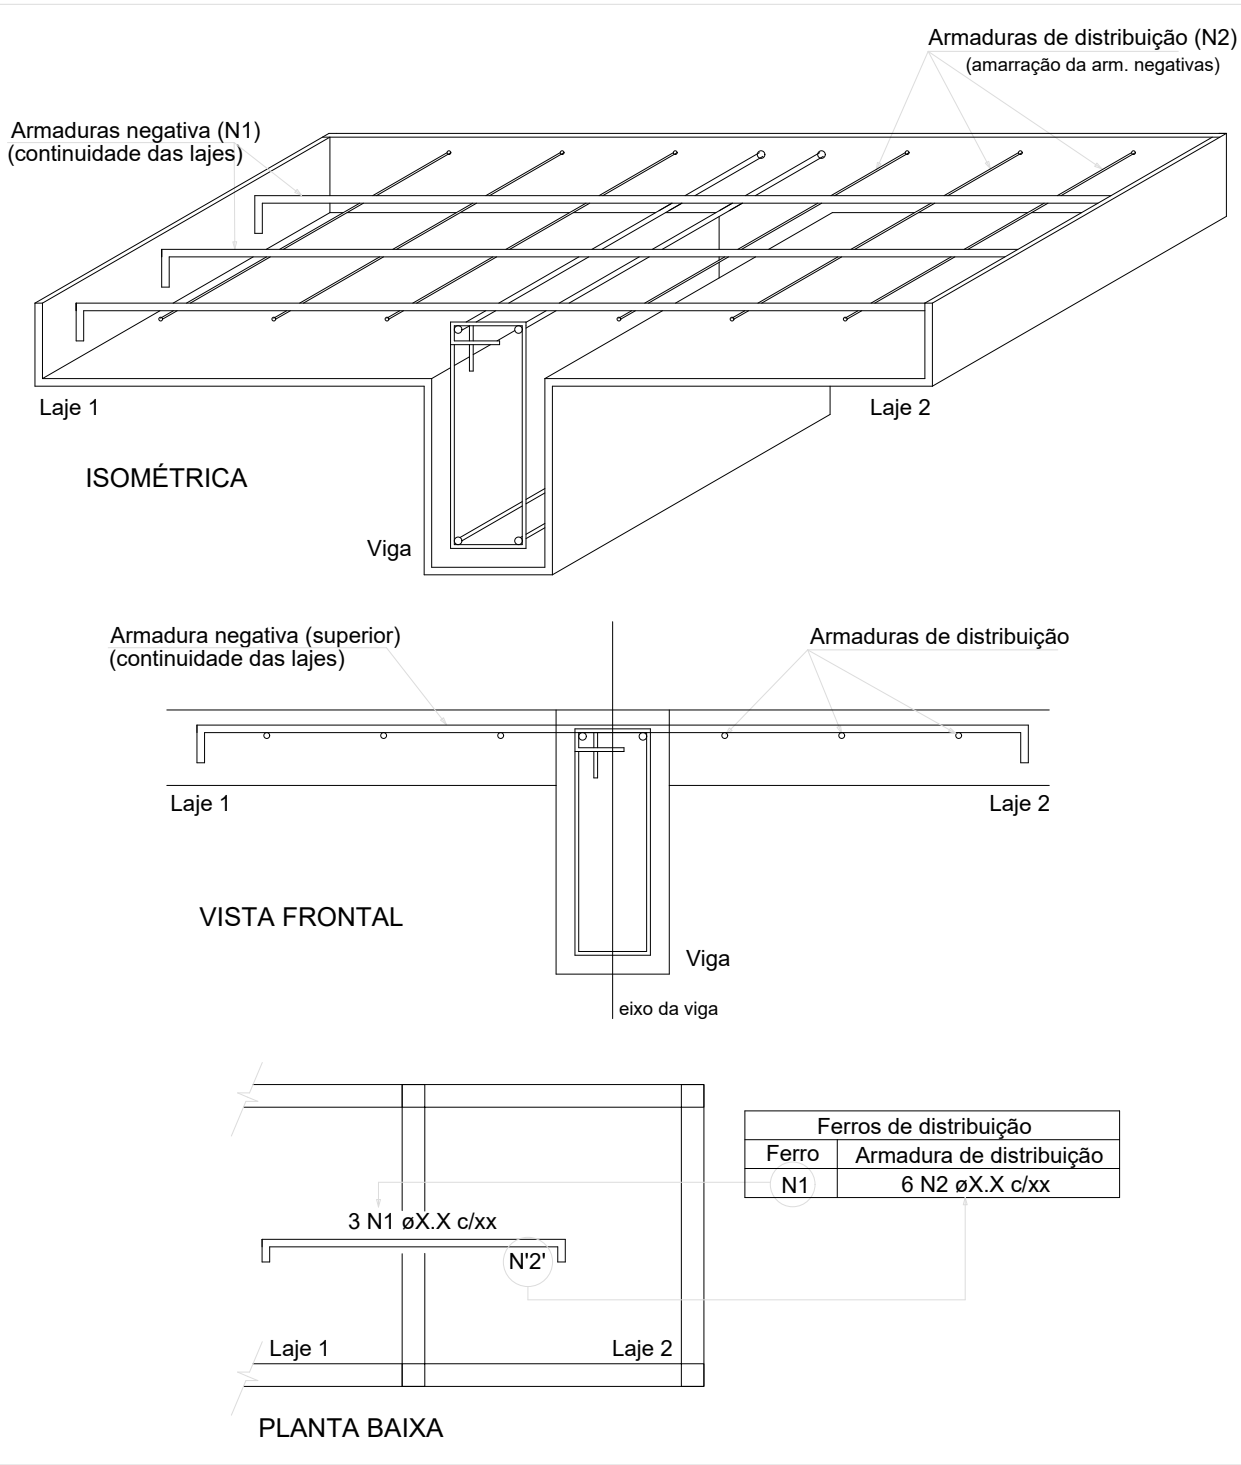

RELAÇÃO DO AÇO

Negativos X

Negativos Y

AÇO	N	DIAM (mm)	QUANT	C.UNIT (cm)	C.TOTAL (cm)
CA60	1	5.0	53	59	3127
	2	5.0	6	197	1182
	3	5.0	3	330	990
	4	5.0	3	313	939

RESUMO DO AÇO

AÇO	DIAM (mm)	C.TOTAL (m)	PESO + 0% (kg)
CA60	5.0	62.4	9.6
PESO TOTAL (kg)			
CA60	9.6		

Volume de concreto (C-25) = 0.30 m³

Área de forma = 0.00 m²

PROPRIETÁRIO: PREFEITURA MUNICIPAL DE COREMAS - PB

PROJETO: LINCOLN CARTAXO DE LIRA JÚNIOR CREA 160.814.689-8

CONSTRUÇÃO:

FOLHA 11/12
PROJETO: CONSTRUÇÃO DE GINÁSIO POLIESPORTIVO
CONVENIENTE: PREFEITURA MUNICIPAL DE COREMAS - PB
CONVENIADO: MUNICÍPIO DE COREMAS - PB
LOCALIDADE: COREMAS - PB

	DATA	RESPONSÁVEL	RUBRICA	DADOS
DESENHO	AGO/2025	LINCOLN CARTAXO		
CÓPIA				
VISTO				

ESCALAS	DESENHOS	CONVÊNIO
Indicada	- Laje Caixa D'água	GOVERNO DO ESTADO
		ARQUIVO

Aprovações:



Av. Gov. Flávio Ribeiro Coutinho, 500, sl. 601
Jardim Oceania, 58037-005 - João Pessoa (PB)
Tel +55 (83) 99924.4447
e-mail: contato@lclprojetos.com