



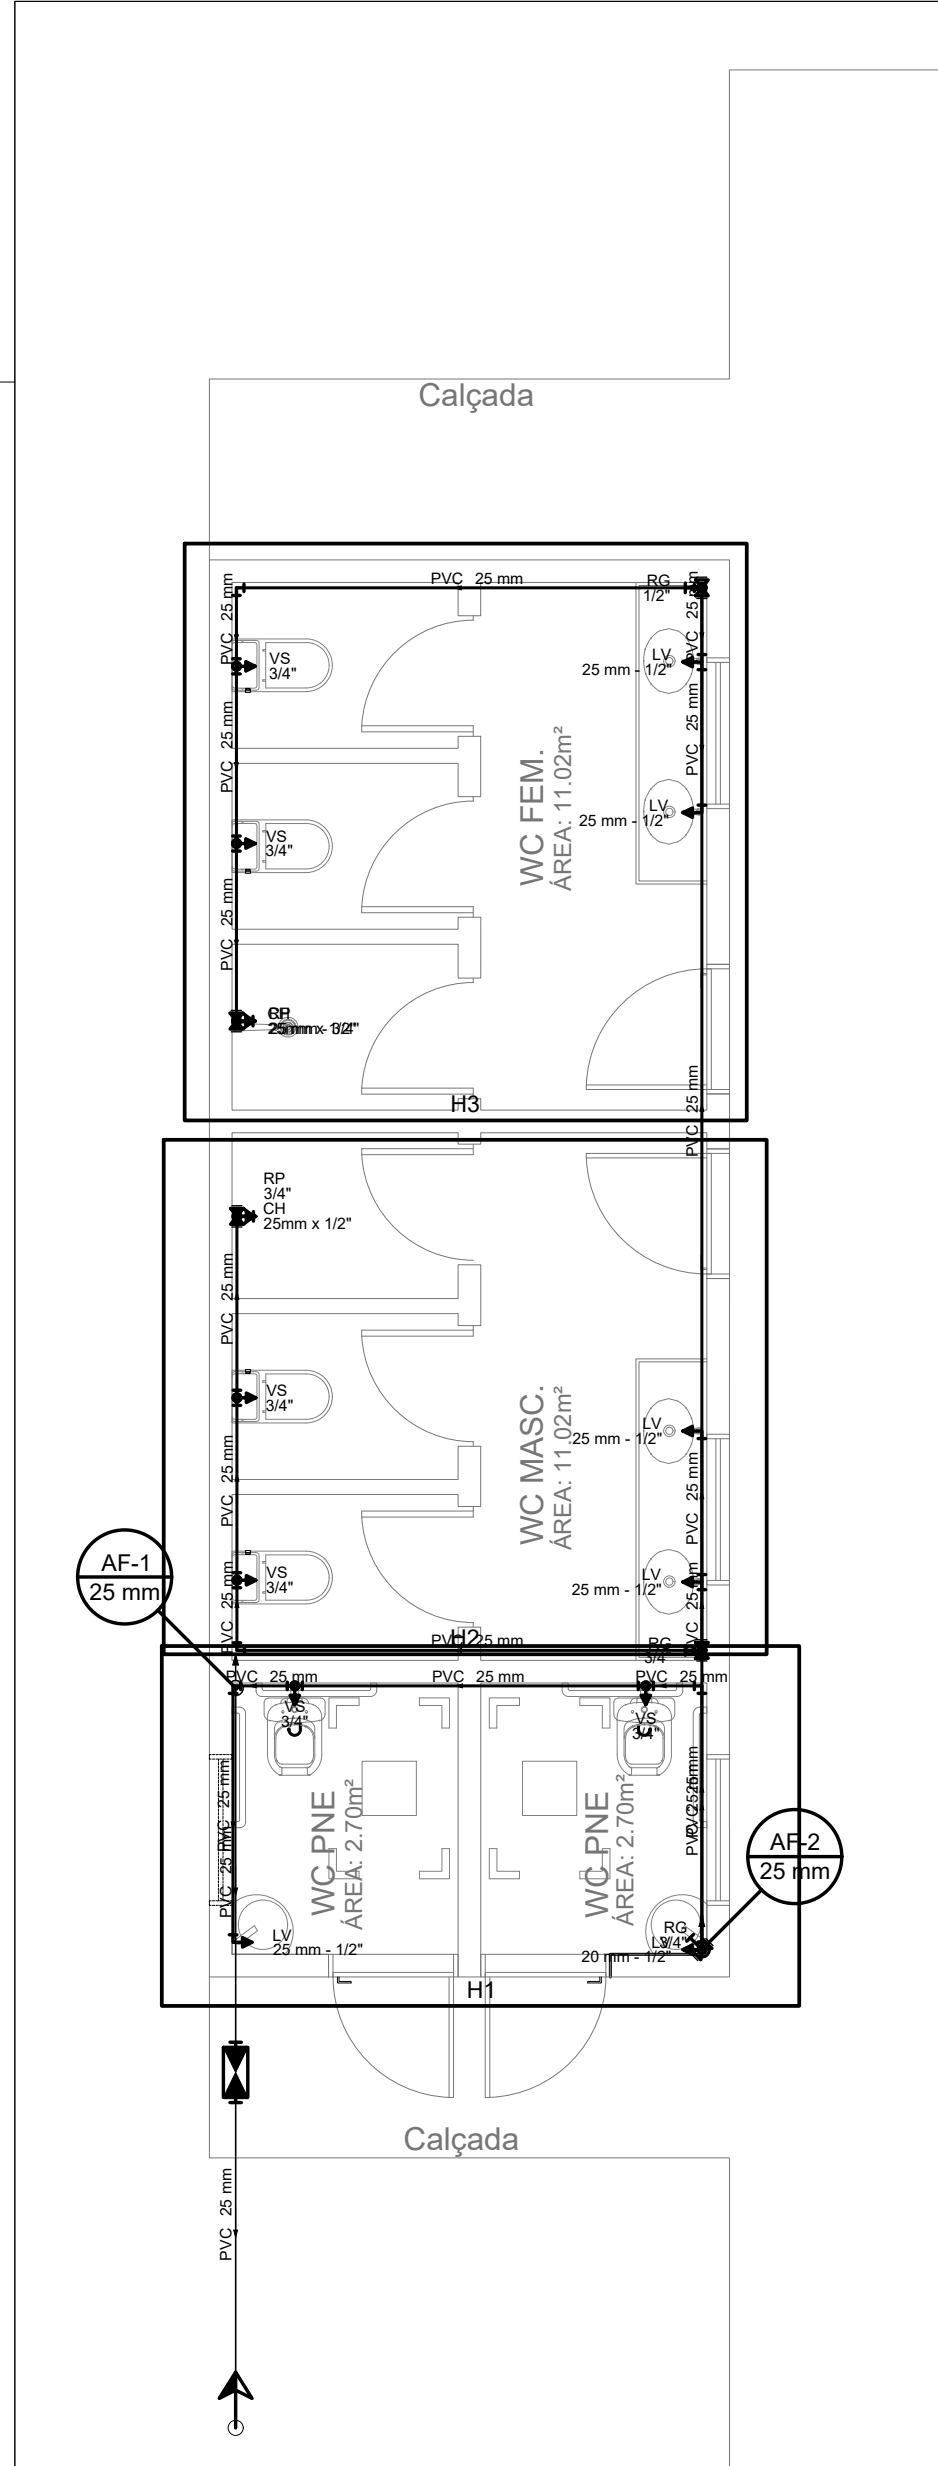

Lista de Materiais		
Aparelho		
Chuveiro		
25mm x 1/2"	2	pç
Torneira de lavatório		
20 mm - 1/2"	1	pç
25 mm - 1/2"	5	pç
Vaso Sanitário c/ cx. acoplada		
1/2"	6	pç
Ferro maleável classe 10		
Colar de tomada de f" f"		
1 1/2"	1	pç
Metais		
Registro de Chuveiro branco PVC		
3/4"	1	pç
Registro de esfera		
1 1/2"	1	pç
Registro de gaveta bruto ABNT		
1/2"	1	pç
3/4"	2	pç
Registro de pressão c/ canopla cromada		
3/4"	1	pç
Registro esfera borboleta bruto PVC		
3/4"	1	pç
PVC Acessórios		
Engate flexível cobre cromado com canopla		
1/2 - 30cm	6	pç
Engate flexível plástico		
1/2 - 30cm	6	pç
PVC misto soldável		
Joelho 90 soldável c/ rosca		
25 mm - 3/4"	3	pç
Joelho de redução soldável c/ rosca		
25 mm - 1/2"	6	pç
Luva soldável c/ rosca		
25 mm - 3/4"	1	pç
PVC rígido roscável		
Curva 90 c/ rosca		
1.1/2"	1	pç
Tubos		
3/4"	0.28	m
PVC rígido soldável		
Adapt sold.c/roscas/bolsa-rosca p registro		
20 mm - 1/2"	2	pç
25 mm - 3/4"	6	pç
50 mm - 1.1/2"	1	pç
Curva 90 soldável		
25 mm	6	pç
Joelho 90° soldável		
25 mm	1	pç
Tubos		
25 mm	48.62	m
Tê 90 soldável		
25 mm	7	pç
PVC soldável azul c/ bucha latão		
Joelho 90° soldável com bucha de latão		
20 mm - 1/2"	1	pç
Joelho de redução 90° soldável com bucha de latão		
25 mm - 1/2"	5	pç
Tê red.90 sold c/ bucha latão B central		
25 mm - 1/2"	2	pç


Legenda das indicações	
CH	Chuveiro - 25mm x 1/2"
LV	Lavatório com Tê de 90° - 25 mm - 1/2"
LV	Lavatório com joelho de 90° - 20 mm - 1/2"
LV	Lavatório com joelho de 90° - 25 mm - 1/2"
RG	Registro bruto gaveta ABNT c/PVC soldável - 1/2"
RG	Registro bruto gaveta ABNT c/PVC soldável - 3/4"
RP	Registro de Pressão com PVC soldável - 25 mm - 3/4"
RP	Registro de chuveiro branco - 3/4"
VS	Vaso sanitário com caixa acoplada - 3/4"

Legenda	
◀	Alimentador Predial
▲	Hidrômetros
✚	Registro bruto gaveta ABNT c/PVC soldável
✚	Registro de Pressão com PVC soldável
✚	Registro de chuveiro branco

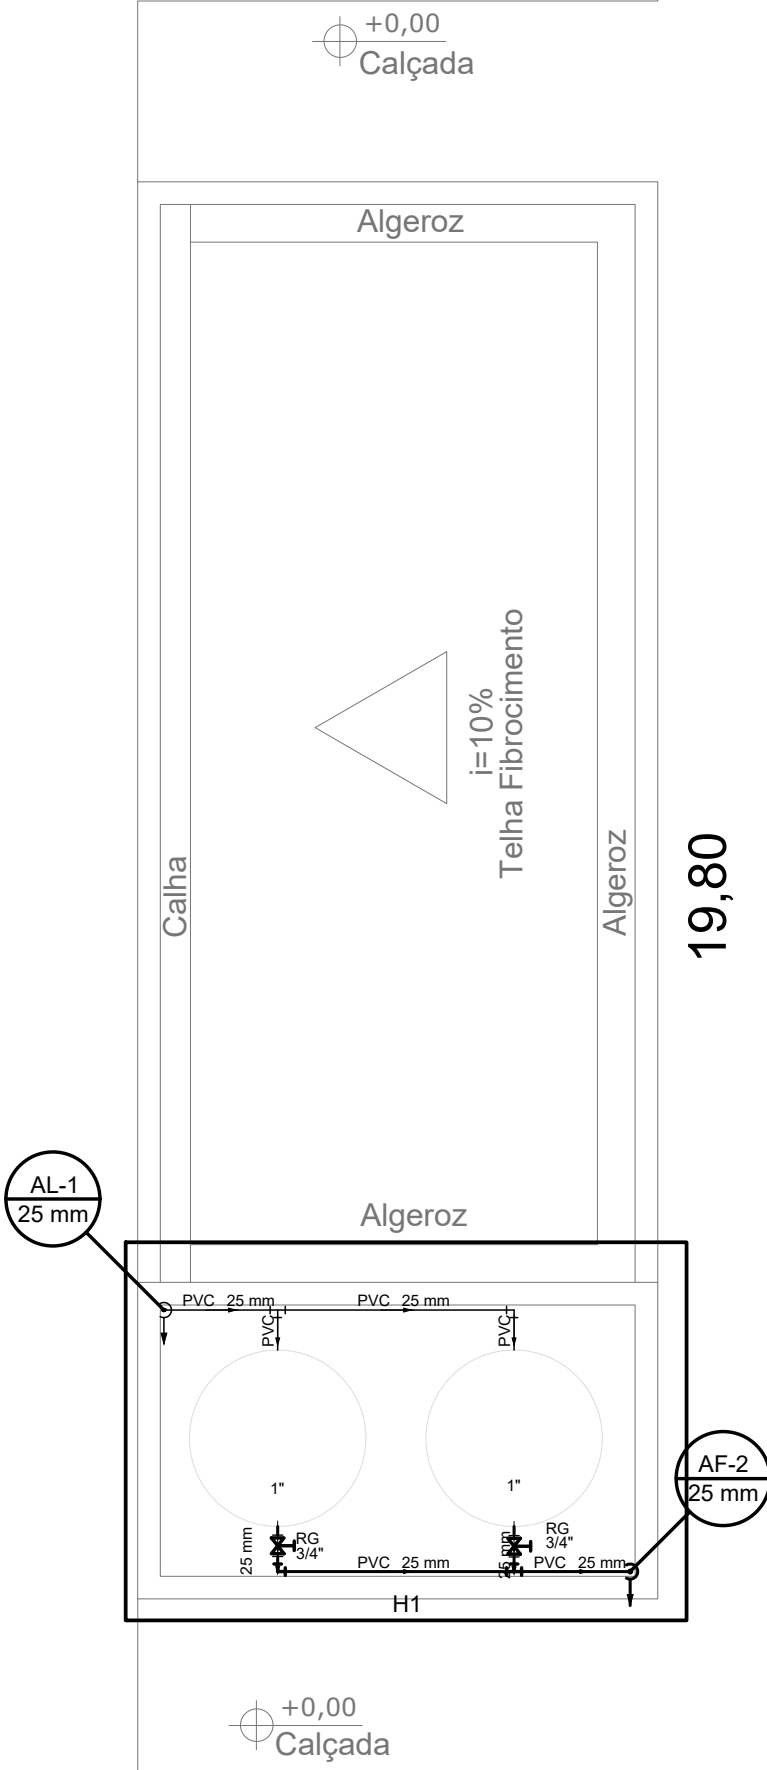

Lista de Materiais		
Metais		
Registro de gaveta bruto ABNT 3/4"	2	pç
PVC rígido soldável		
Adapt sold. c/ flange livre p/ cx. d' água 32 mm - 1"	2	pç
Adapt sold.curto c/bolsa-rosca p registro 25 mm - 3/4"	4	pç
Curva 90 soldável 25 mm	2	pç
Tubos 25 mm	11,01	m
Tê 90 soldável 25 mm	1	pç
Reservatório cilíndrico		
Poliétileno 500 L	2	pç

Legenda das indicações	
RG	Registro bruto gaveta ABNT c/PVC soldável - 3/4"

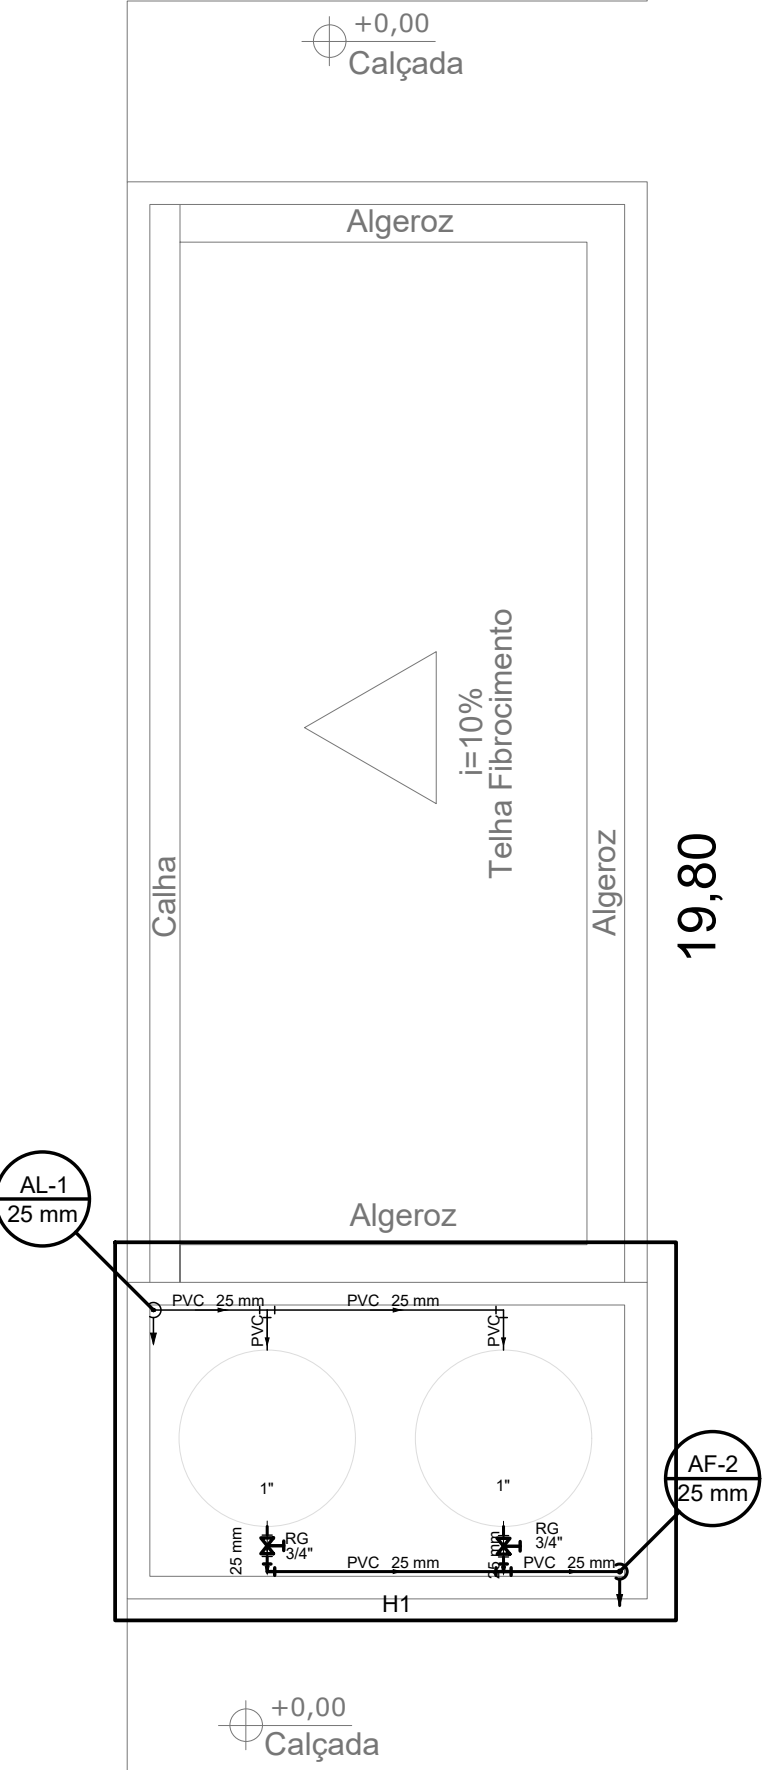

Lista de Materiais		
Metais		
Registro de gaveta bruto ABNT 3/4"		2 pç
PVC rígido soldável		
Adapt sold. c/ flange livre p/ cx. d'água 32 mm - 1"		2 pç
Adapt sold.c/roscas/bolsa-rosca p registro 25 mm - 3/4"		4 pç
Curva 90 soldável 25 mm		2 pç
Tubos 25 mm		11.01 m
Tê 90 soldável 25 mm		1 pç
Reservatório cilíndrico		
Poliétileno 500 L		2 pç

Legenda das indicações	
RG	Registro bruto gaveta ABNT c/PVC soldável - 3/4"

PROPRIETÁRIO: PREFEITURA MUNICIPAL DE COREMAS - PB

PROJETO: LINCOLN CARTAXO DE LIRA JÚNIOR CREA 160.814.689-8

FOLHA
01/02

PROJETO: CONSTRUÇÃO DE GINÁSIO POLIESPORTIVO
CONVENIENTE: PREFEITURA MUNICIPAL DE COREMAS - PB
CONVENIADO: MUNICÍPIO DE COREMAS - PB
LOCALIDADE: COREMAS - PB

	DATA	RESPONSÁVEL	RUBRICA	DADOS
DESENHO	AGO/2025	LINCOLN CARTAXO		CREA 160.814.689-8
CÓPIA				
VISTO				

ESCALAS	DESENHOS	CONVÊNIO
INDICADO	- PROJETO HIDRÁULICO	ARQUIVO

Aprovações: