




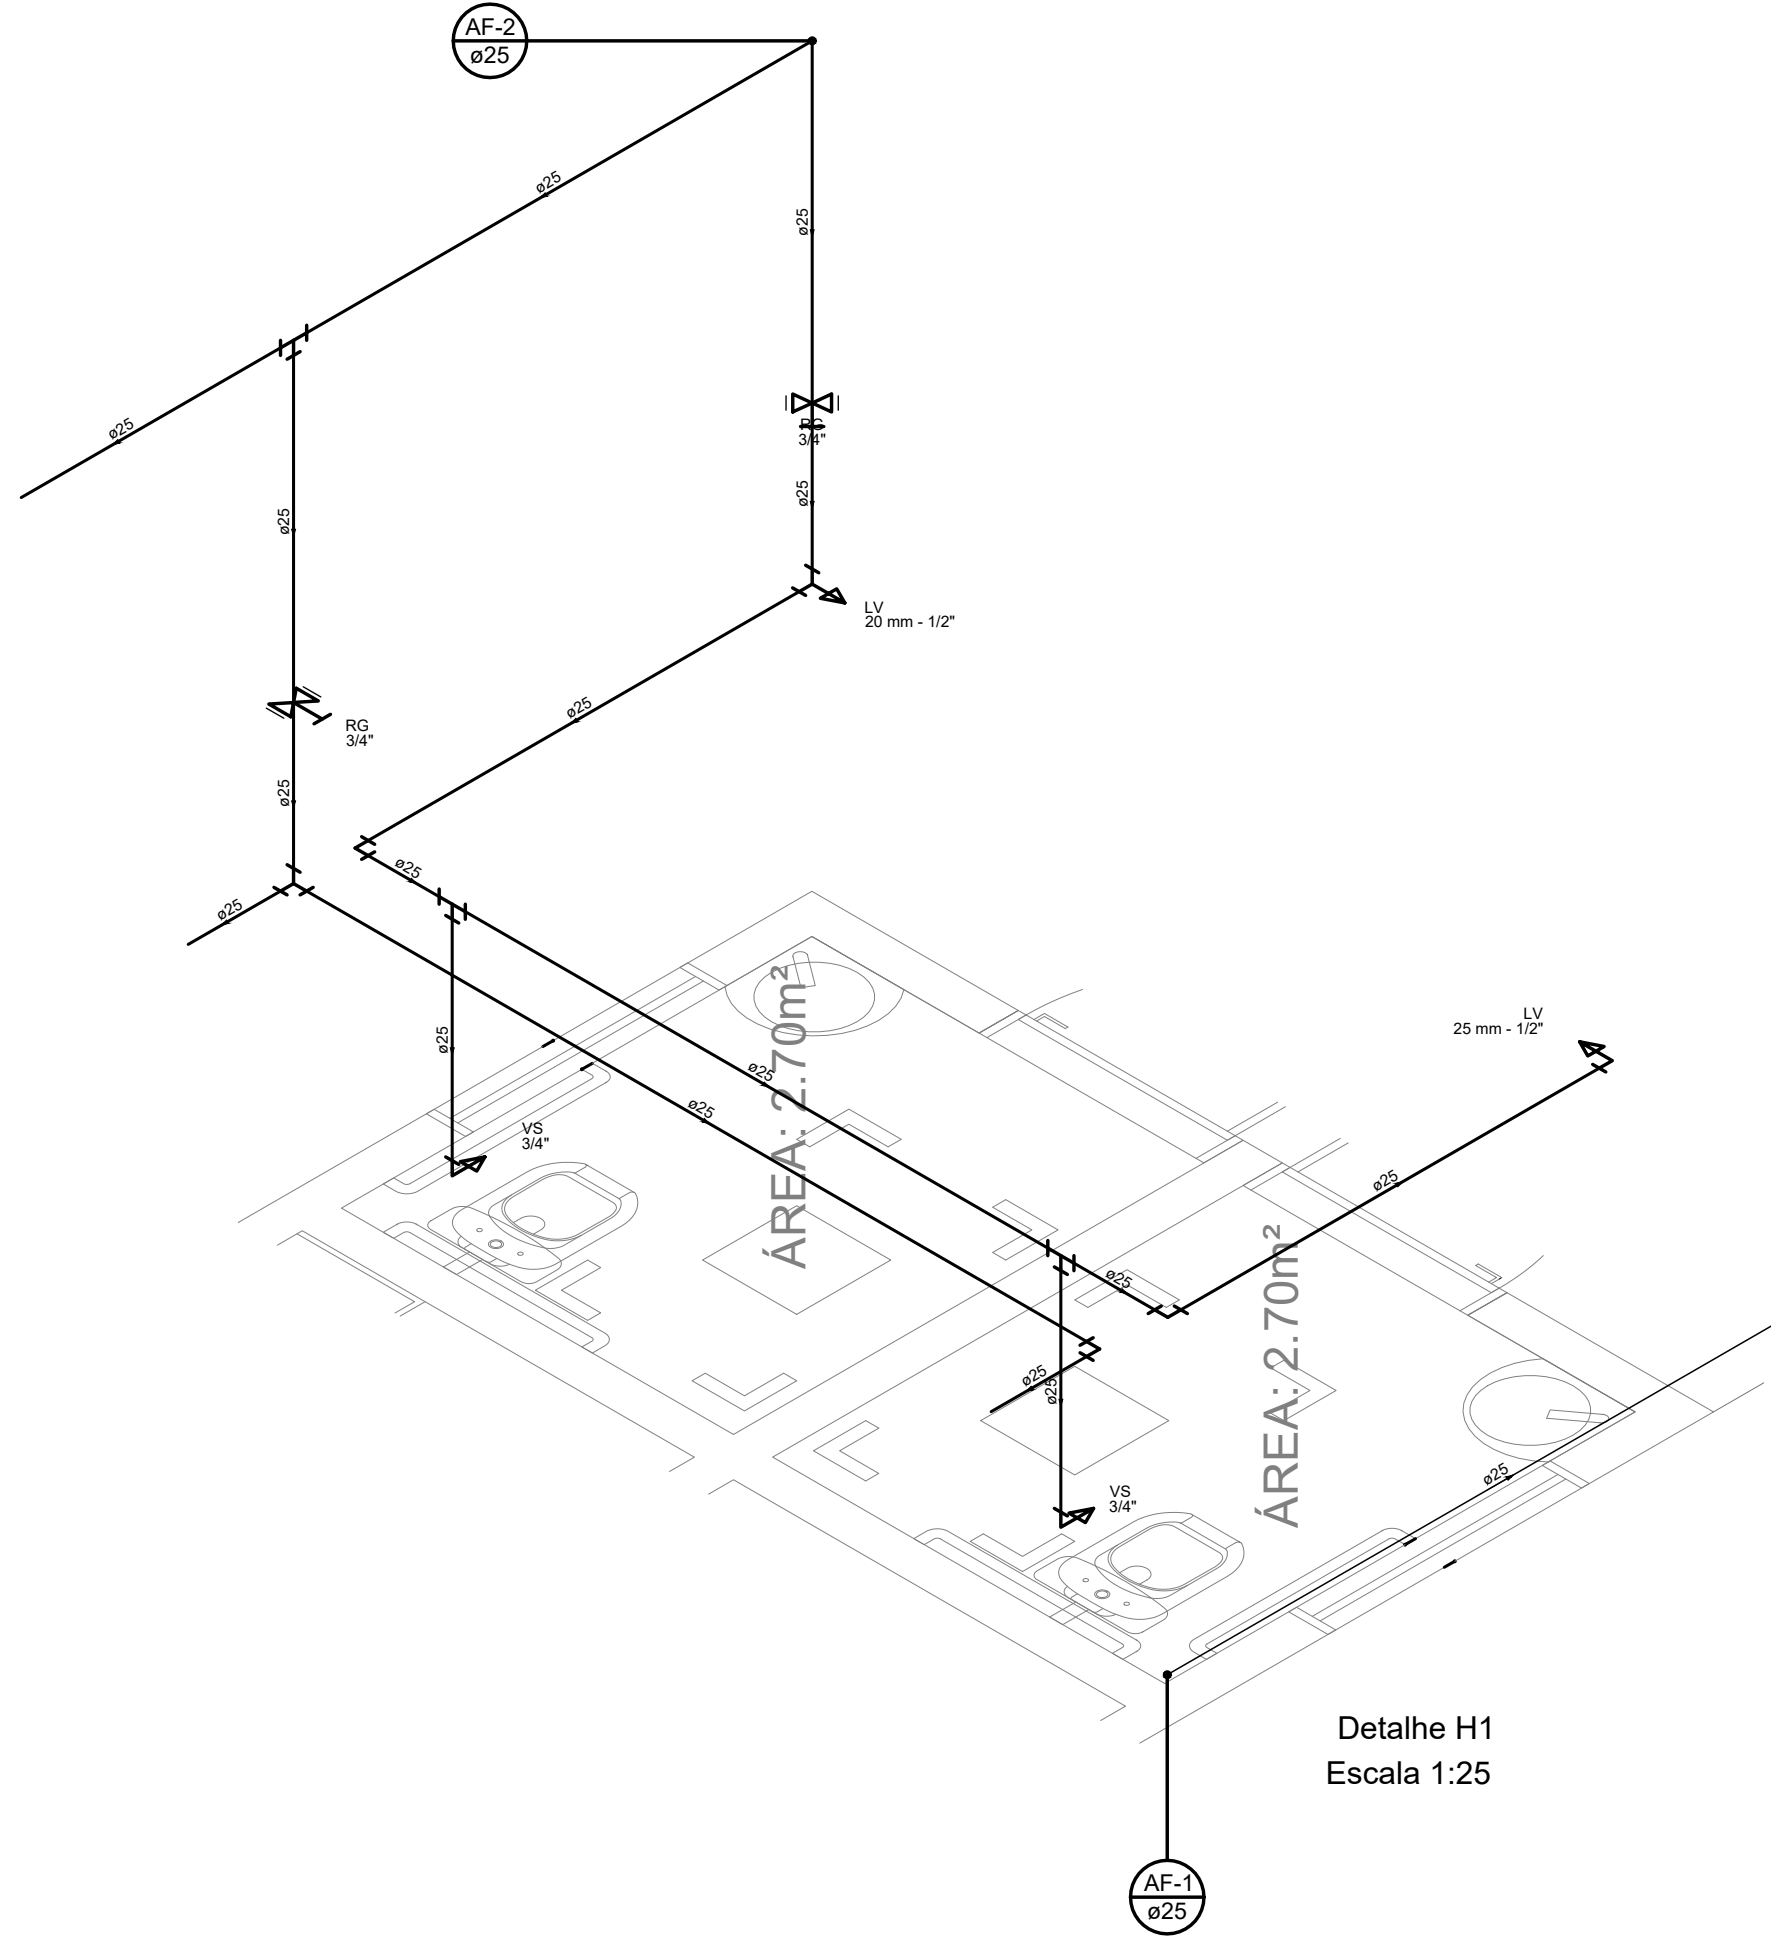


Detalhe H1
Escala 1:25

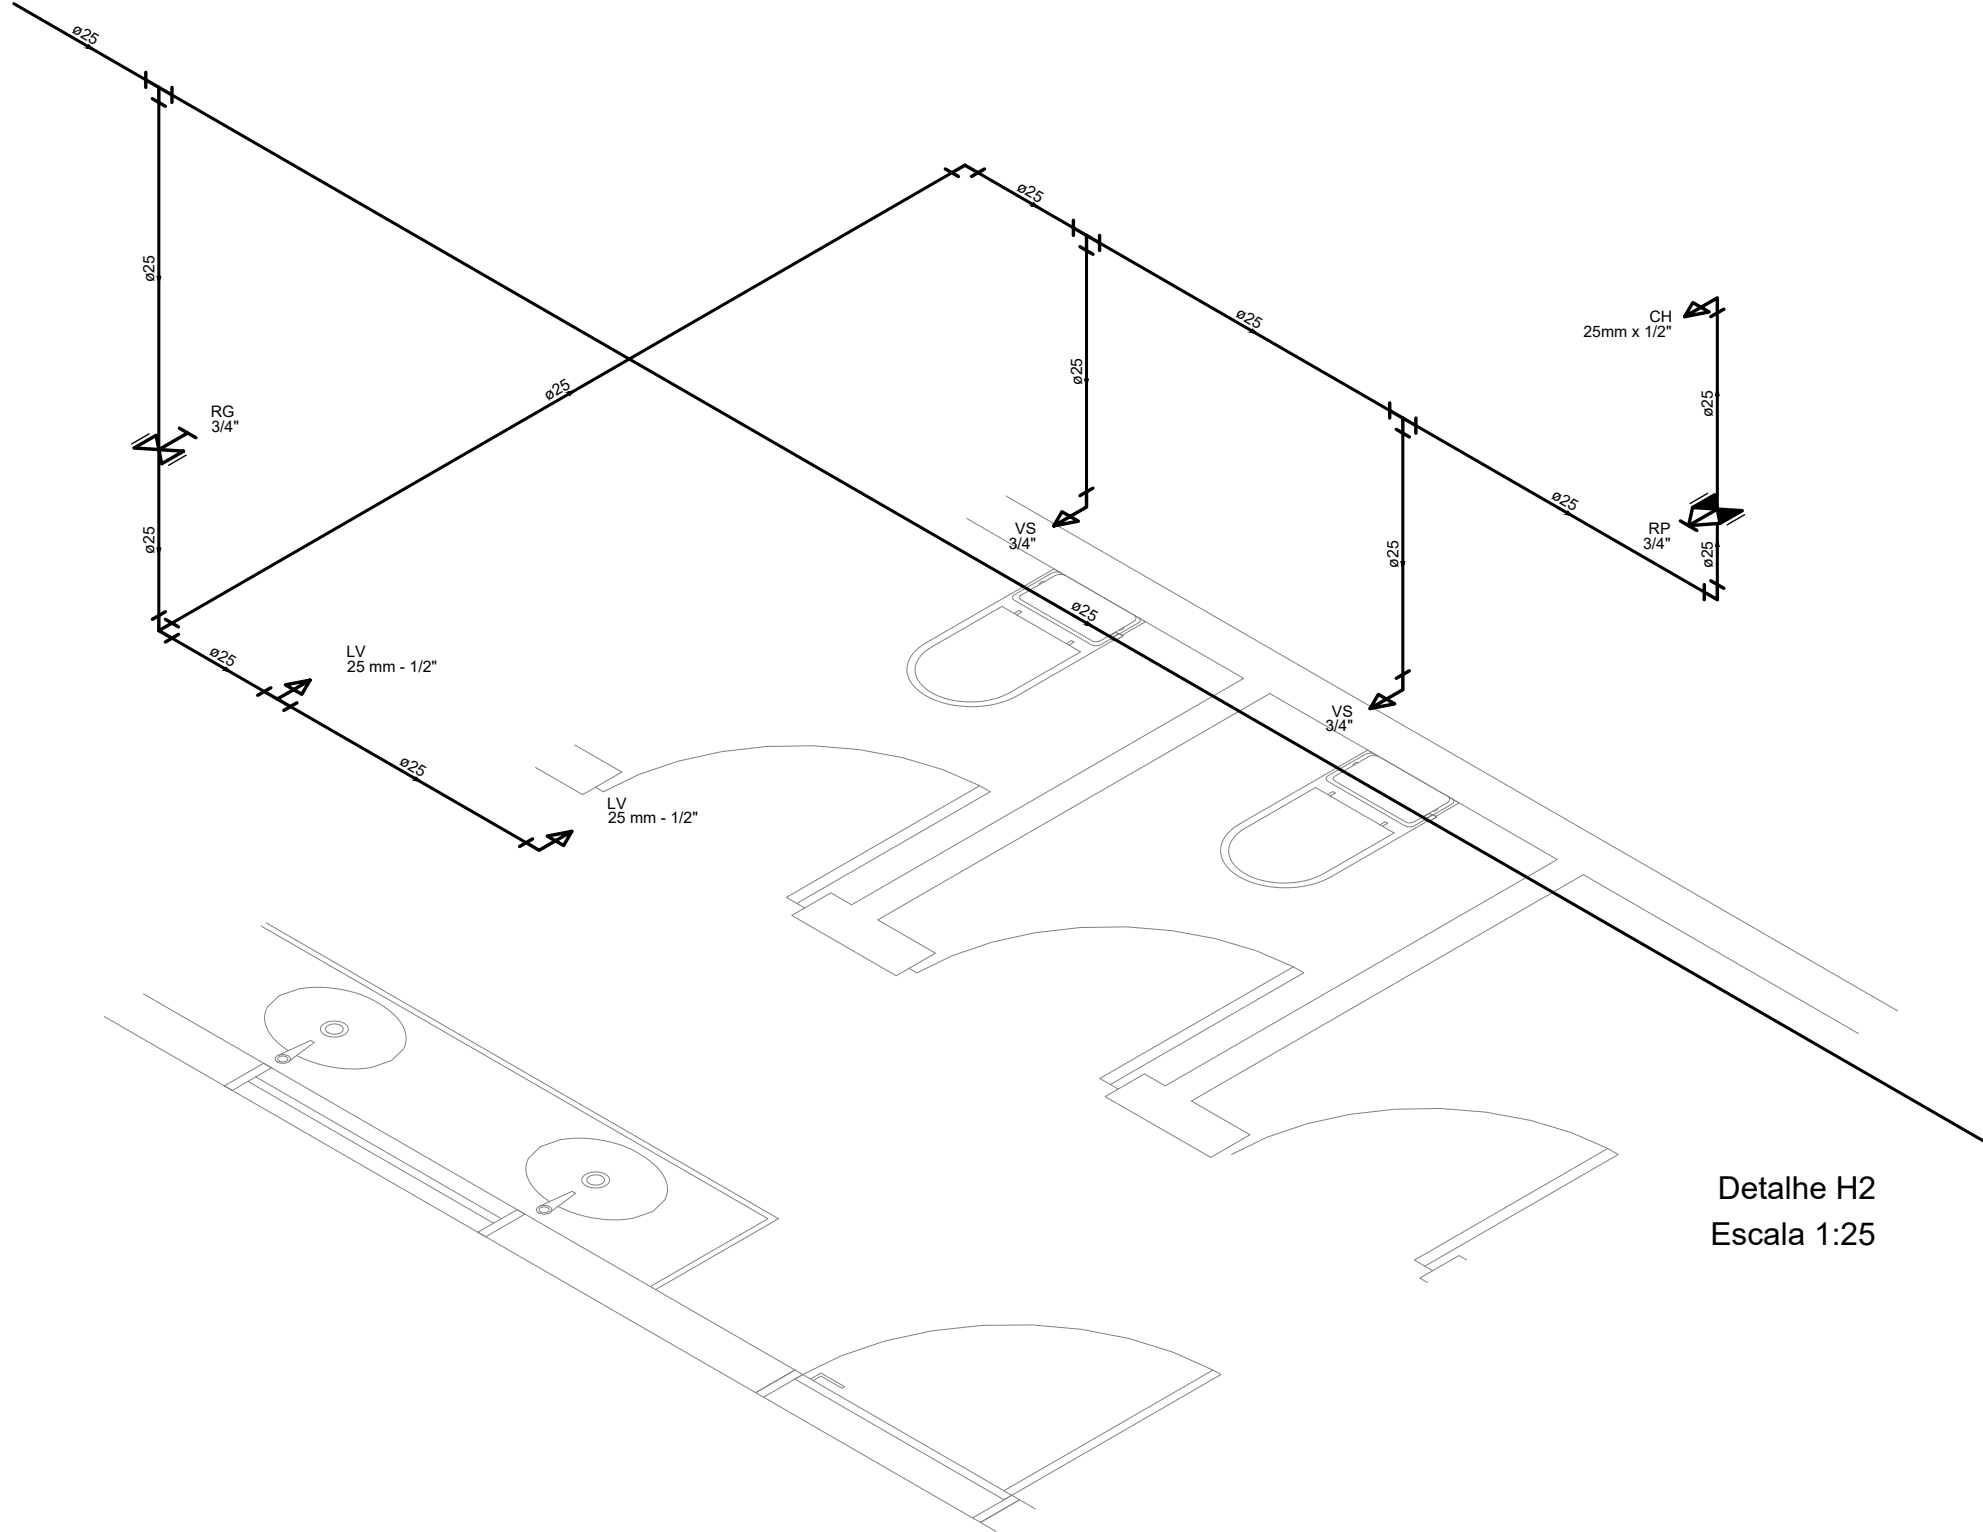

Detalhe H2
Escala 1:25

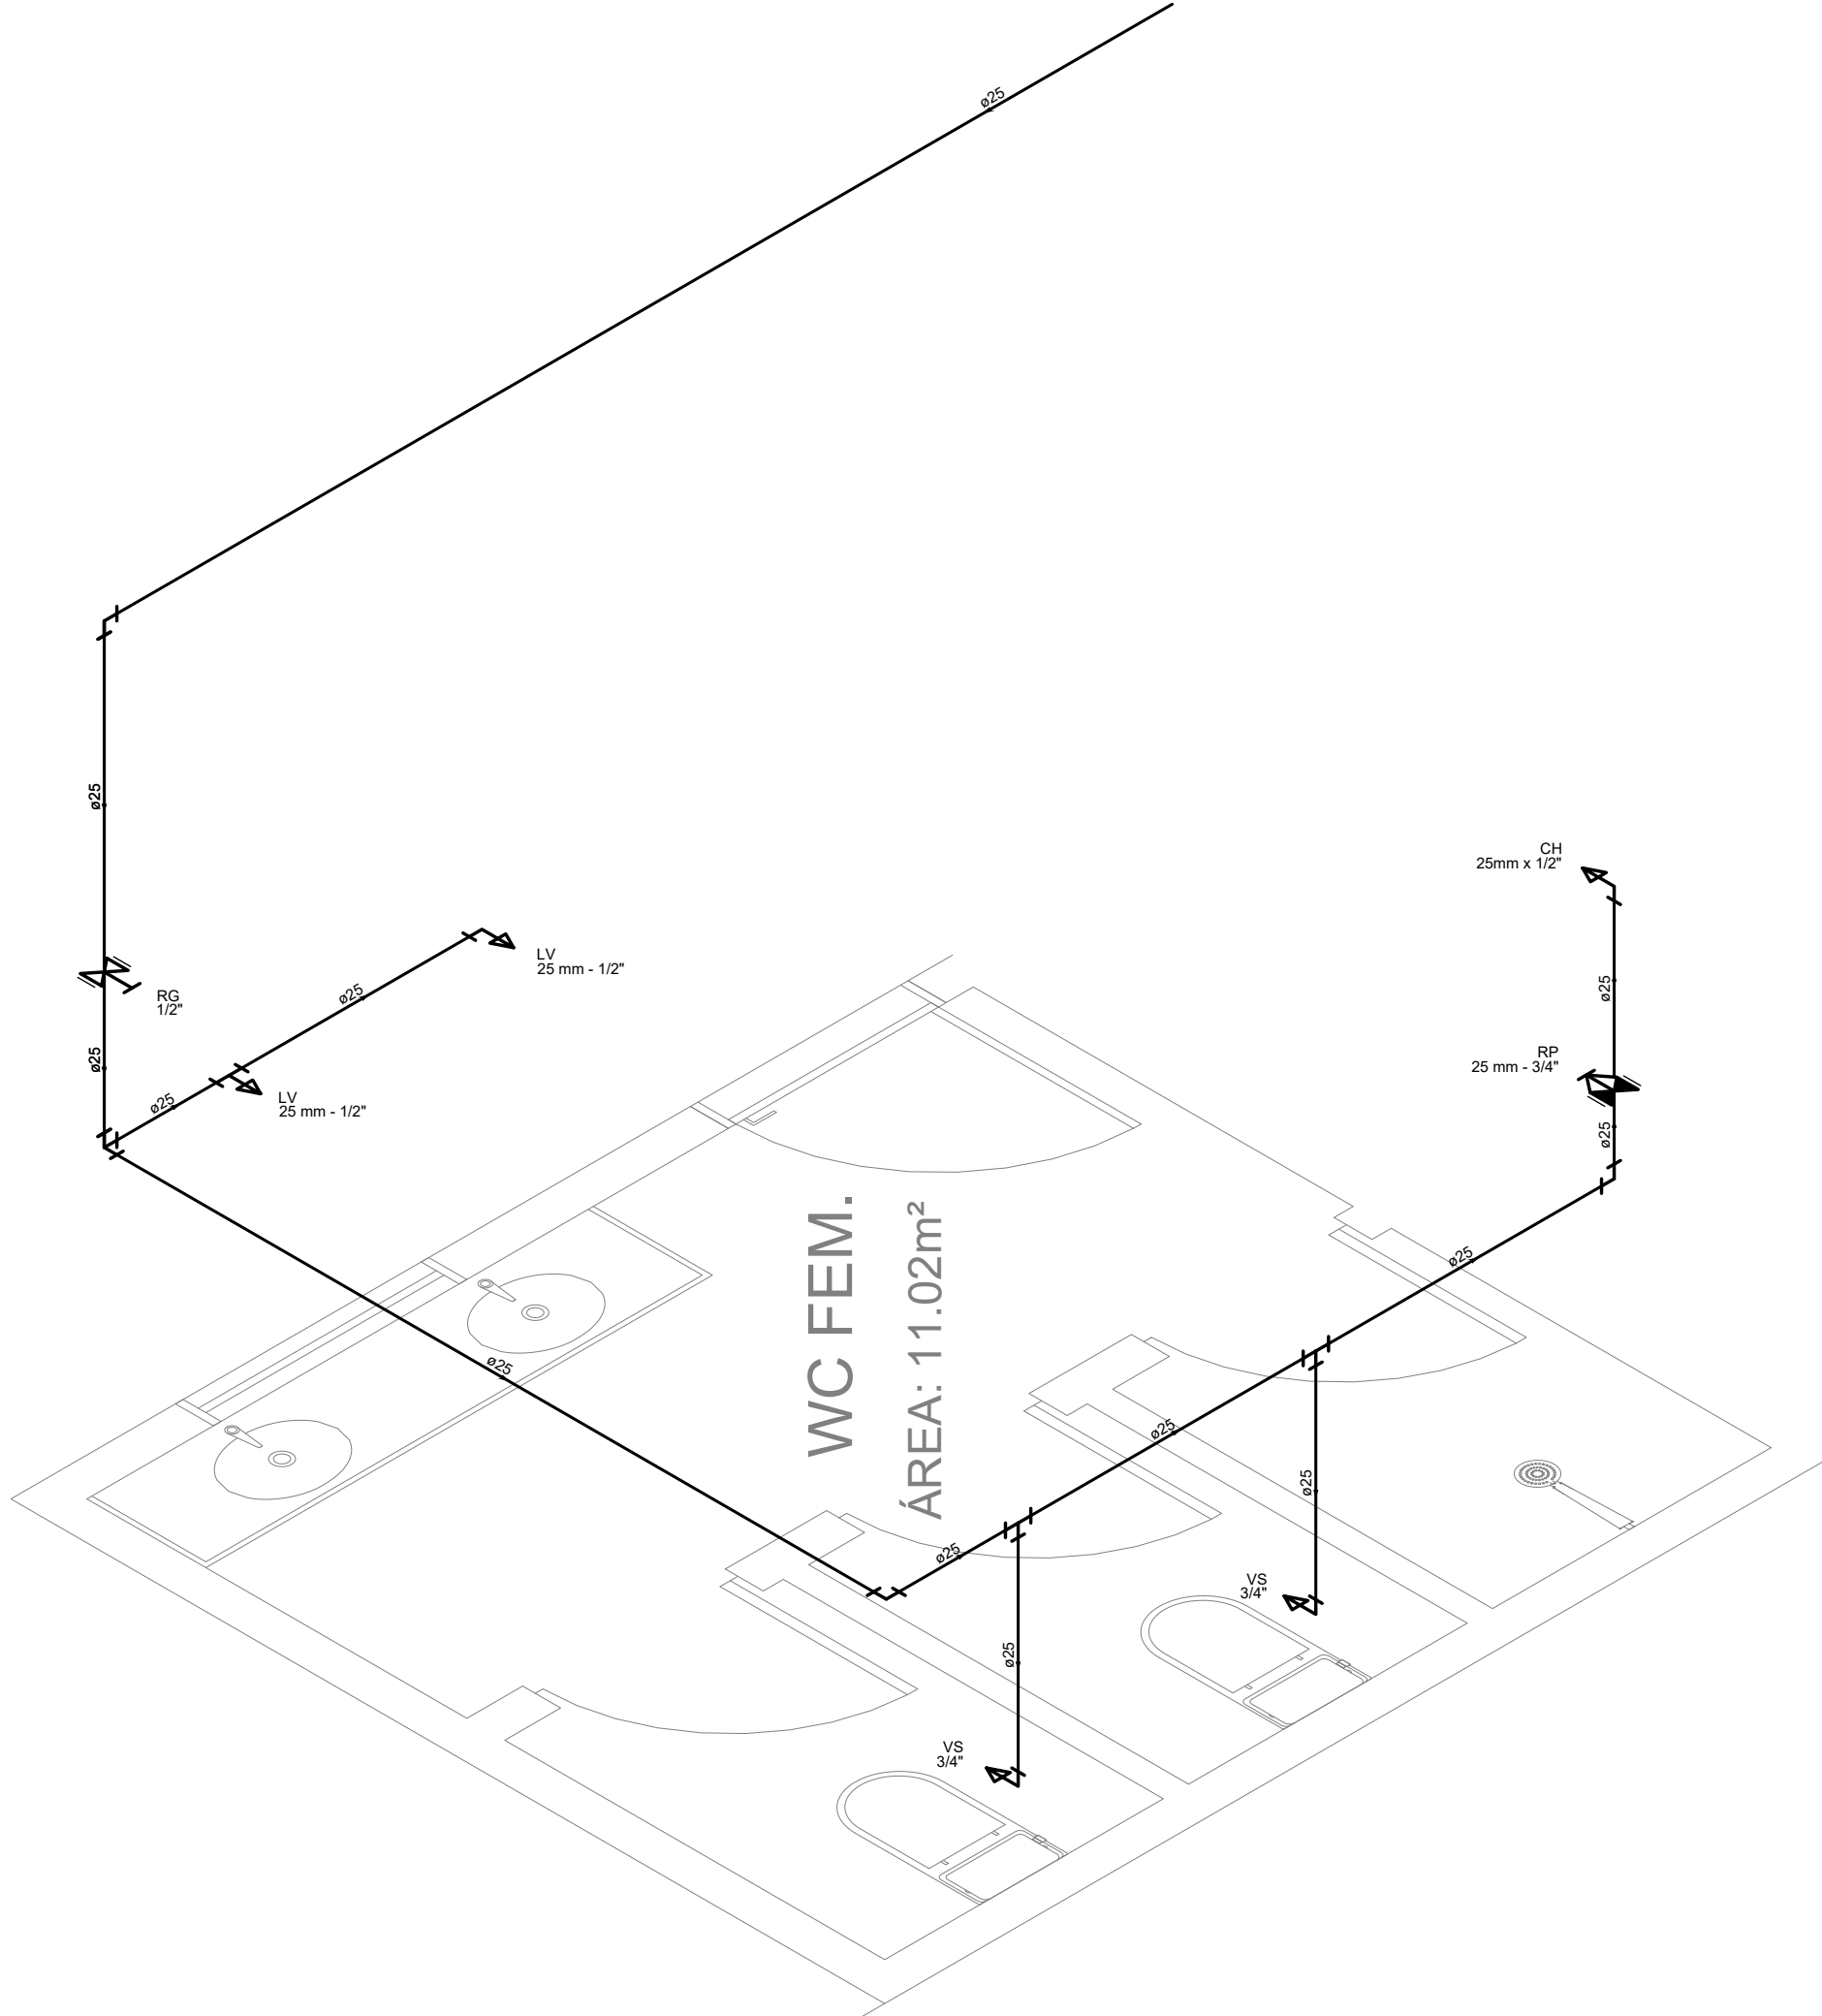

Detalhe H3
Escala 1:25

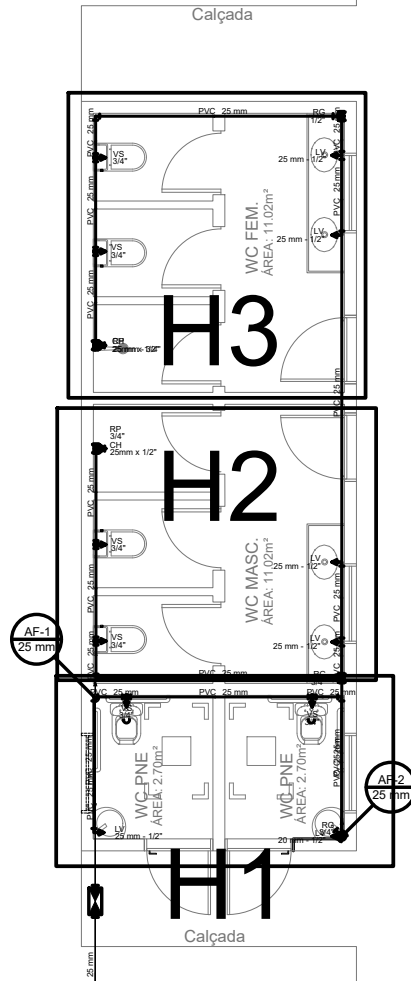

PROPRIETÁRIO: PREFEITURA MUNICIPAL DE COREMAS - PB
LINCOLN CARTAXO DE LIRA JÚNIOR:06897861405
PROJETO: LINCOLN CARTAXO DE LIRA JÚNIOR CREA 160.814.689-8

Assinado de forma digital por LINCOLN CARTAXO DE LIRA JÚNIOR:06897861405
Dados: 2025.08.08 13:35:09 -03'00'

FOLHA

02/02

PROJETO:

CONSTRUÇÃO DE GINÁSIO POLIESPORTIVO

CONVENIENTE:

PREFEITURA MUNICIPAL DE COREMAS - PB

CONVENIADO:

MUNICÍPIO DE COREMAS - PB

LOCALIDADE:

COREMAS - PB

DESENHO	DATA	RESPONSÁVEL	RUBRICA	DADOS
CÓPIA	AGO/2025	LINCOLN CARTAXO		CREA 160.814.689-8
VISTO				
ESCALAS	DESENHOS			CONVÊNIO
				ARQUIVO
INDICADO	- PROJETO HIDRÁULICO DETALHE H1 DETALHE H2 DETALHE H3			

Aprovações:

LCL PROJETOS

Av. Gov. Flávio R. Coutinho, 500, sl. 601
Jd. Oceania, 58037-005 - João Pessoa (PB)
Tel +55 (83) 99624 4447
e-mail: lclprojetos@hotmail.com