



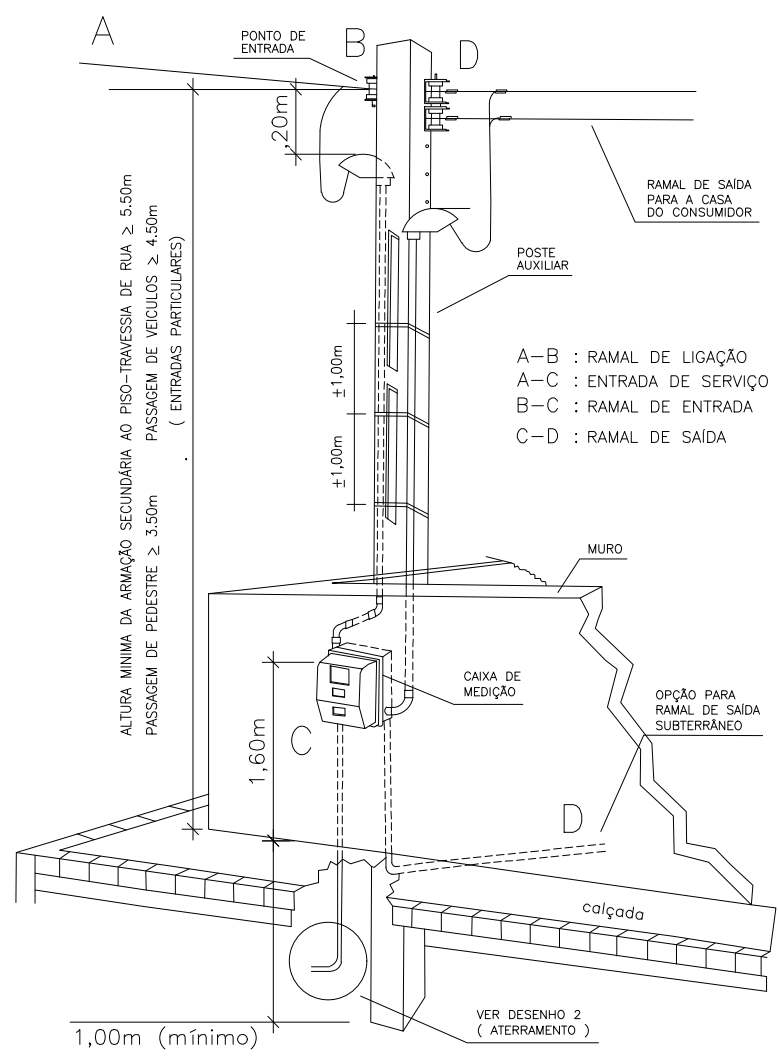

Detalhe de entrada de energia

escala s/esc

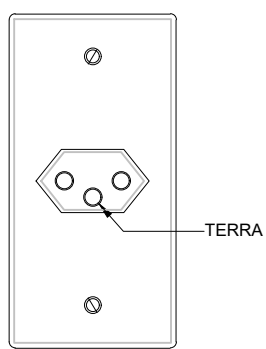

Detalhe tomada 2P+T

escala 1/75


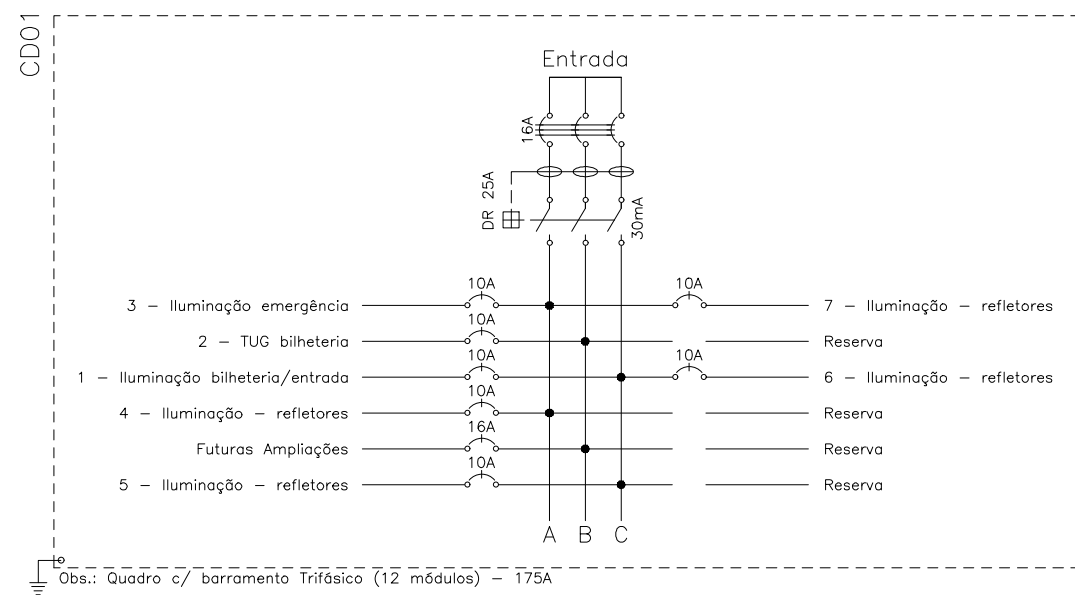



Diagrama Unifilar - Quadra

escala s/esc

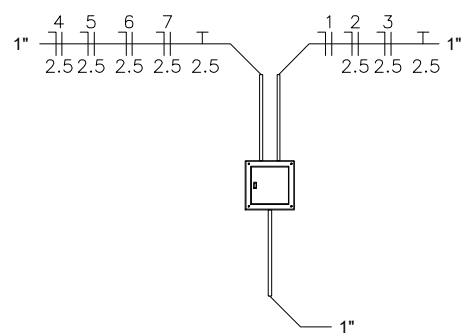

Detalhe do quadro de energia - Quadra

escala 1/75

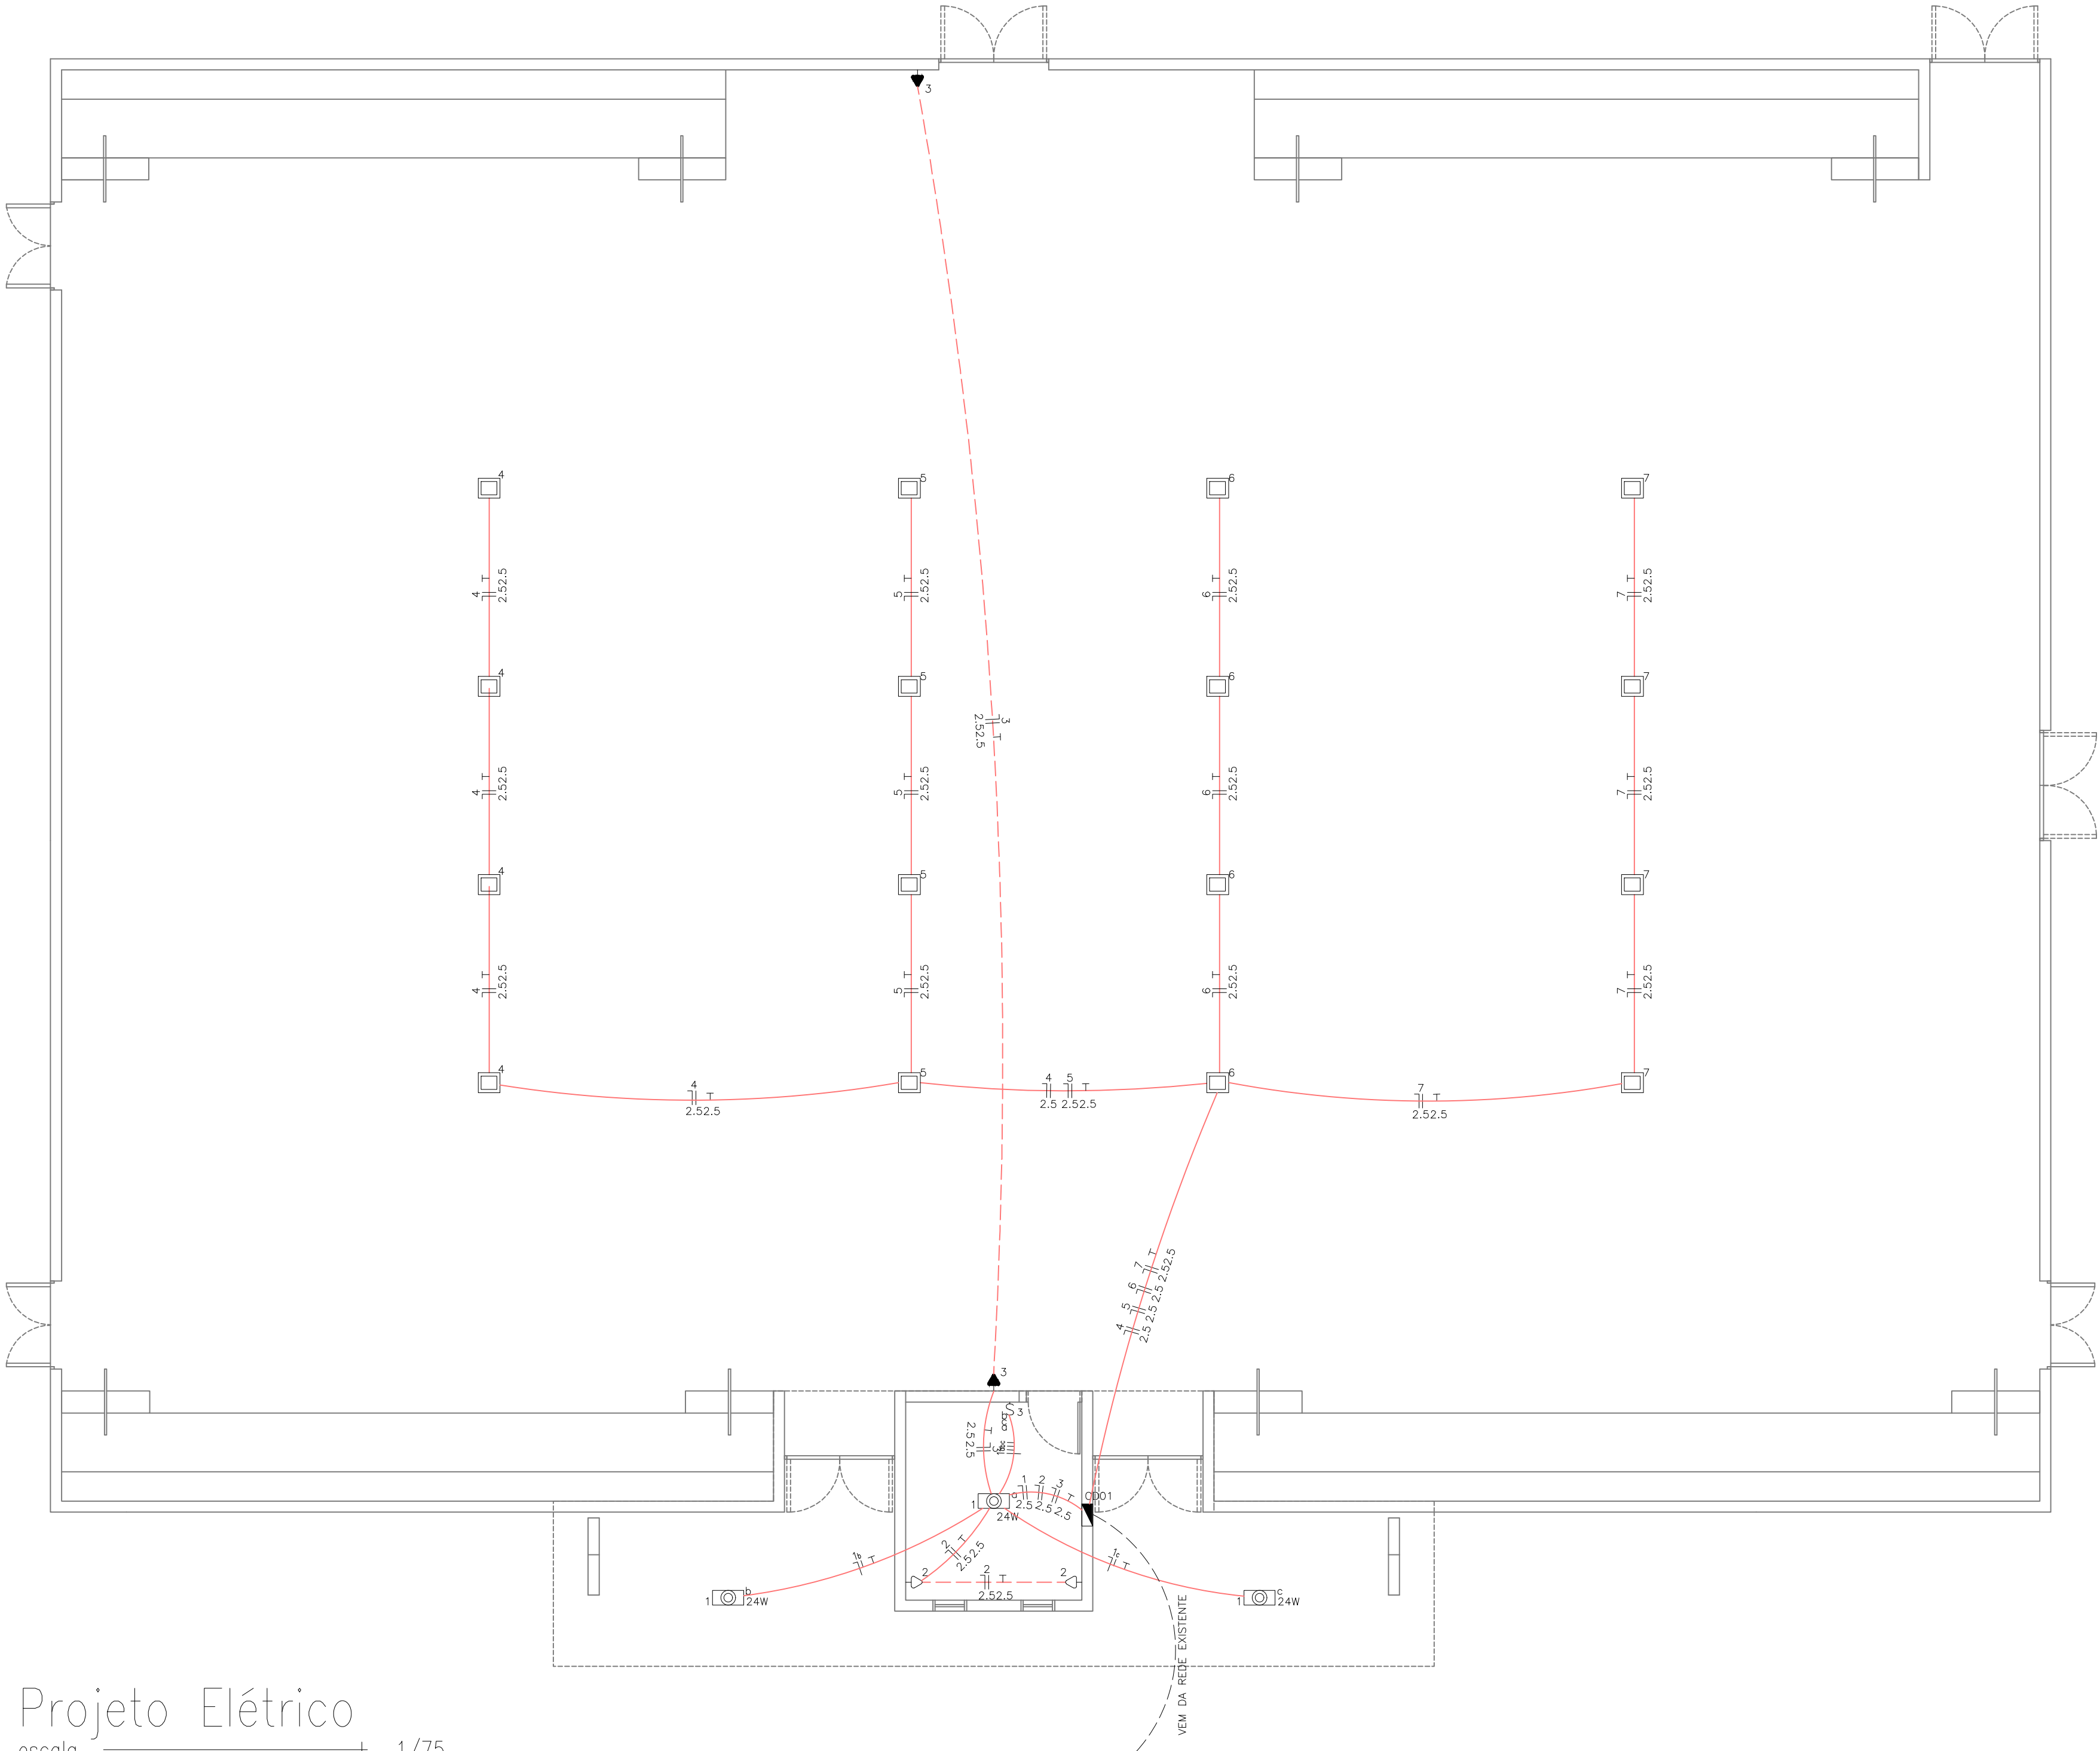

Projeto Elétrico

escala 1/75

Quadro de Cargas - Quadra											
CD01											
Circ.	Descrição	Ilu. (W)	Tomas (W)	Qd. (W)	Pot. (W)	Dem. (W)	Fat. (W)	Corr. (W)	Fases	Prot. (W)	Obs.
1	Ilu. bilheteria/entrada	3			240,0	266,7	100%	0,90	1,21	1	Obs.
2	TUG bilheteria		2		200,0	250,0	100%	0,80	1,14	1	Obs.
3	Ilu. emergência		2		200,0	250,0	100%	0,80	1,14	1	Obs.
4	Ilu. refletores		4		800,0	1000,0	100%	0,80	4,55	1	Obs.
5	Ilu. refletores		4		800,0	1000,0	100%	0,80	4,55	1	Obs.
6	Ilu. refletores		4		800,0	1000,0	100%	0,80	4,55	1	Obs.
7	Ilu. refletores		4		800,0	1000,0	100%	0,80	4,55	1	Obs.
Futuras Ampliações				1	2500,0	2986,1	70%	0,84	13,57	1	Obs.
Total		3	16	4		6340,0	7752,8				
Aliment.	C=10m O=2%				5723,6	7020,8	100%	0,82	10,60	3	Obs.
Potência Total (6340,0 W) (7752,8 V.A) Potência Demandada: 88,17% (5590,0 W) (6856,9 V.A)											
Corrente nas Fases: A=10,2A B=10,6A C=10,3A											

Lista de Materiais - Quadra					
Num.	Quant.	Und.	Dimensão	Código	Descrição
1	4	pc	1"	PECCX2X4	Caixa 2x4
2	3	pc		PECCX6S	Caixa Sextavada
3	147,98	m			Eletroduto Flexível - Parede
4	36,90	m			Eletroduto Flexível - Teto
5	3	pc			Quadro Geral de luz e força (12 módulos) Barra
6	1	pc			Tomada 200cm
7	2	pc			Tomada baixa 30cm
8	2	pc			Refletor LED 200W - 20.000 lm
9	16	pc			

Interruptor com letra S - Quadra					
Num.	Quant.	Und.	Dimensão	Código	Descrição
1	1	pc		PECCX2X4	Caixa 2x4
2	1	pc			Interruptor triplo

Fiação e Dispositivos de Proteção - Quadra					
Num.	Quant.	Und.	Dimensão	Código	Descrição
1	1	pc		1P16A	Disjuntor a seco - DIN
2	7	pc		1P10A	Disjuntor a seco - DIN
3	1	pc		3P16A	Disjuntor a seco - DIN
4	236,22	m	2,5 mm2	3000	Fio cabo 750 V - PVC - Fase
5	5,73	m	1,5 mm2		Fio cabo 750 V - PVC - Fase
6	10,37	m	1,5 mm2		Fio cabo 750 V - PVC - Neutro
7	236,22	m	2,5 mm2	3000	Fio cabo 750 V - PVC - Neutro
8	16,91	m	1,5 mm2		Fio cabo 750 V - PVC - Retorno
9	7,70	m	1,5 mm2		Fio cabo 750 V - PVC - Terra
10	194,53	m	2,5 mm2	3000	Fio cabo 750 V - PVC - Terra
11	1	pc		4P25A/30mA	Disjuntor diferencial - DR

LEGENDA:

	- Luminária painel quadrado de sobrepor 24 W
	- Interruptor duplo
	- Interruptor simples
	- Interruptor triplo
	- REFLETOR LED 200W - 20.000 lm
	- Tomada 130cm
	- Tomada 200cm
	- Tomada baixa 30cm
	- Quadro Geral de luz e força
	- Disjuntor a seco - DIN 10A 1P
	- Disjuntor a seco - DIN 16A 1P
	- Disjuntor a seco - DIN 16A 3P
	- Eletroduto Rígido no Piso
	- Eletroduto Flexível no Teto/Parede
	- Neutro, Fase, Retorno, Terra
	- Disjuntor diferencial - DR

Onde não for indicado Ø eletroduto, considerar 1"

PROPRIETÁRIO: PREFEITURA MUNICIPAL DE COREMAS - PB

LINCOLN CARTAXO DE LIRA JUNIOR:06897861405
Assinado de forma digital por LINCOLN CARTAXO DE LIRA JUNIOR:06897861405
Dados: 2025.08.08 12:15:46 -03'00'

PROJETO: LINCOLN CARTAXO DE LIRA JÚNIOR CREA 160.814.689-8

FOLHA		PROJETO: CONSTRUÇÃO DE QUADRA POLIESPORTIVA			
01/01		CONVENIENTE: PREFEITURA MUNICIPAL DE COREMAS - PB			
		CONVENIADO: MUNICIPIO DE COREMAS - PB			
		LOCALIDADE: COREMAS - PB			
DESENHO	DATA	RESPONSÁVEL	RUBRICA	DADOS	
CÓPIA	AGO/2025	LINCOLN CARTAXO		CREA 160.814.689-8	
VISTO					
ESCALAS		DESENHOS			CONVÊNIO
INDICADO		PROJETO ELÉTRICO			RECUSOS PRÓPRIOS
					ARQUIVO
Aprovações:					
		 LCL PROJETOS			
Av. Gov. Flávio R. Coutinho, 500, sl. 601 Jd. Oceania, 58037-005 - João Pessoa (PB) Tel +55 (83) 99924.4447 e-mail: lclprojetos@hotmail.com					