



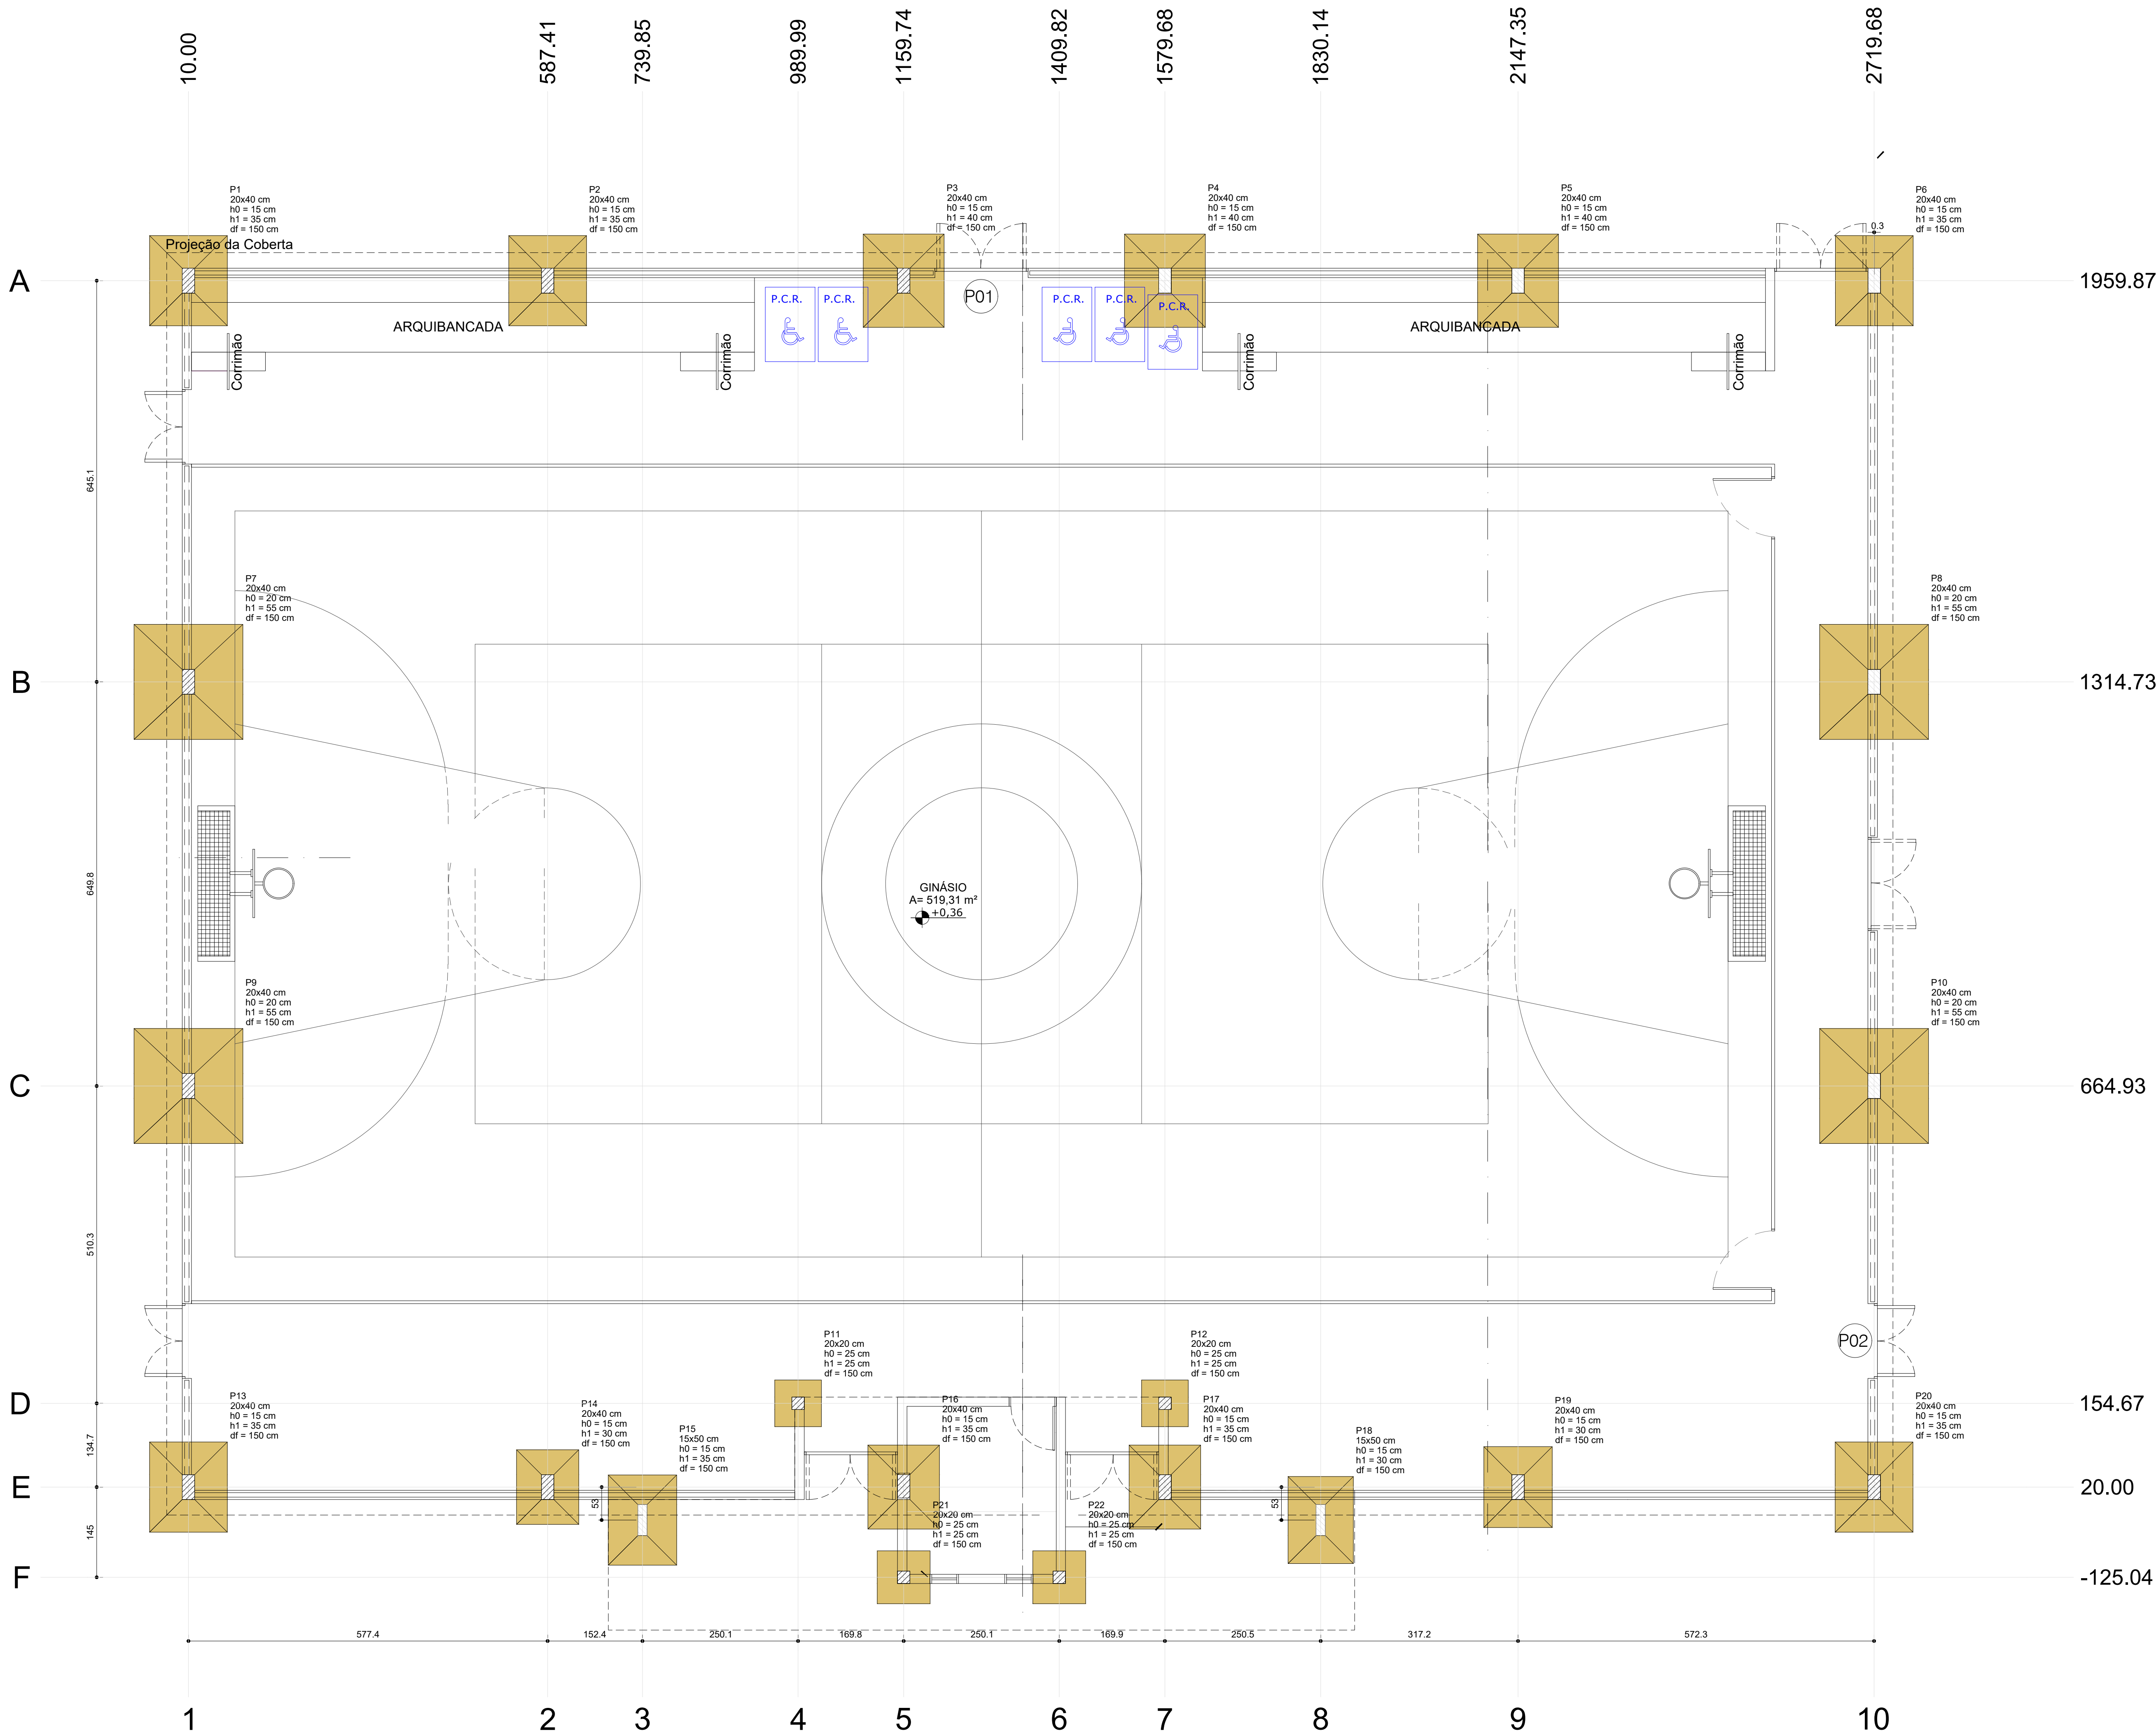

Planta de locação
escala 1:50

		Pilar		Carga Máx. (tf)	Carga Mín. (tf)	Fundação		h1 / hb (cm)	df (cm)
Nome	Seção (cm)	X (cm)	Y (cm)			Lado B (cm)	Lado H (cm)		
P1	20x40	10.00	1959.87	8.7	5.6	125	145	15	35
P2	20x40	587.41	1959.87	7.5	7.0	125	145	15	35
P3	20x40	1159.74	1959.87	7.1	6.5	130	150	15	40
P4	20x40	1579.68	1959.87	7.1	6.5	130	150	15	40
P5	20x40	2147.35	1959.87	7.5	7.0	130	150	15	40
P6	20x40	2720.00	1959.87	8.7	5.6	125	145	15	35
P7	20x40	10.00	1314.73	4.7	4.1	175	185	20	55
P8	20x40	2719.68	1314.73	4.7	4.1	175	185	20	55
P9	20x40	10.00	664.93	4.7	4.1	175	185	20	55
P10	20x40	2719.68	664.93	4.7	4.1	175	185	20	55
P11	20x20	989.99	154.67	1.8	0.6	75	75	25	25
P12	20x20	1579.68	154.67	2.0	0.2	75	75	25	25
P13	20x40	10.00	20.00	8.8	5.6	125	145	15	35
P14	20x40	587.41	20.00	7.0	5.5	100	120	15	30
P15	15x50	739.85	-33.04	6.0	3.9	110	145	15	35
P16	20x40	1159.74	20.00	11.1	8.4	115	135	15	35
P17	20x40	1579.68	20.00	8.9	8.1	115	135	15	35
P18	15x50	1830.14	-33.04	5.2	3.8	105	140	15	30
P19	20x40	2147.35	20.00	7.0	6.3	110	130	15	30
P20	20x40	2719.68	20.00	8.8	5.6	125	145	15	35
P21	20x20	1159.74	-125.04	5.1	2.1	85	85	25	25
P22	20x20	1409.82	-125.04	3.8	2.5	85	85	25	25

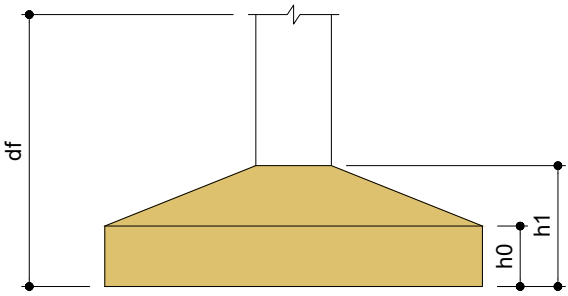

Localização no eixo X		Localização no eixo Y	
Coordenadas (cm)	Nome	Coordenadas (cm)	Nome
10.00	P1, P7, P9, P13	1959.87	P1, P2, P3, P4, P5, P6
587.41	P2, P14	1314.73	P7, P8
739.85	P15	664.93	P9, P10
989.99	P11	154.67	P11, P12
1159.74	P3, P16, P21	20.00	P13, P14, P16, P17, P19, P20
1409.82	P22	-33.04	P15, P18
1579.68	P4, P12, P17	-125.04	P21, P22
1830.14	P18		
2147.35	P5, P19		
2719.68	P8, P10, P20		
2720.00	P6		

B - CARACTERÍSTICAS DAS SAPATAS:

1. DADOS PARA O DIMENSIONAMENTO ESTRUTURAL DAS SAPATAS:

- FUNDAÇÕES NA COTA DE -1,5 METROS
- VIGAS BALDRAMES NÍVEL +40 CM
- TENSÃO ADMISSÍVEL DO SOLO 1,5 KGf/cm²

PROPRIETÁRIO: PREFEITURA MUNICIPAL DE COREMAS - PB

PROJETO: LINCOLN CARTAXO DE LIRA JÚNIOR CREA 160.814.689-8

CONSTRUÇÃO:

FOLHA 01/26
PROJETO: CONSTRUÇÃO DE GINÁSIO POLIESPORTIVO - ESTRUTURAL
CONVENIENTE: PREFEITURA MUNICIPAL DE COREMAS - PB
CONVENIADO: MUNICÍPIO DE COREMAS - PB
LOCALIDADE: COREMAS - PB

	DATA	RESPONSÁVEL	RUBRICA	DADOS
DESENHO	AGO/2025	LINCOLN CARTAXO		
CÓPIA				
VISTO				

ESCALAS	DESENHOS	CONVÊNIO
Indicada	- Planta de Locação	GOVERNO DO ESTADO
		ARQUIVO

Aprovações: