


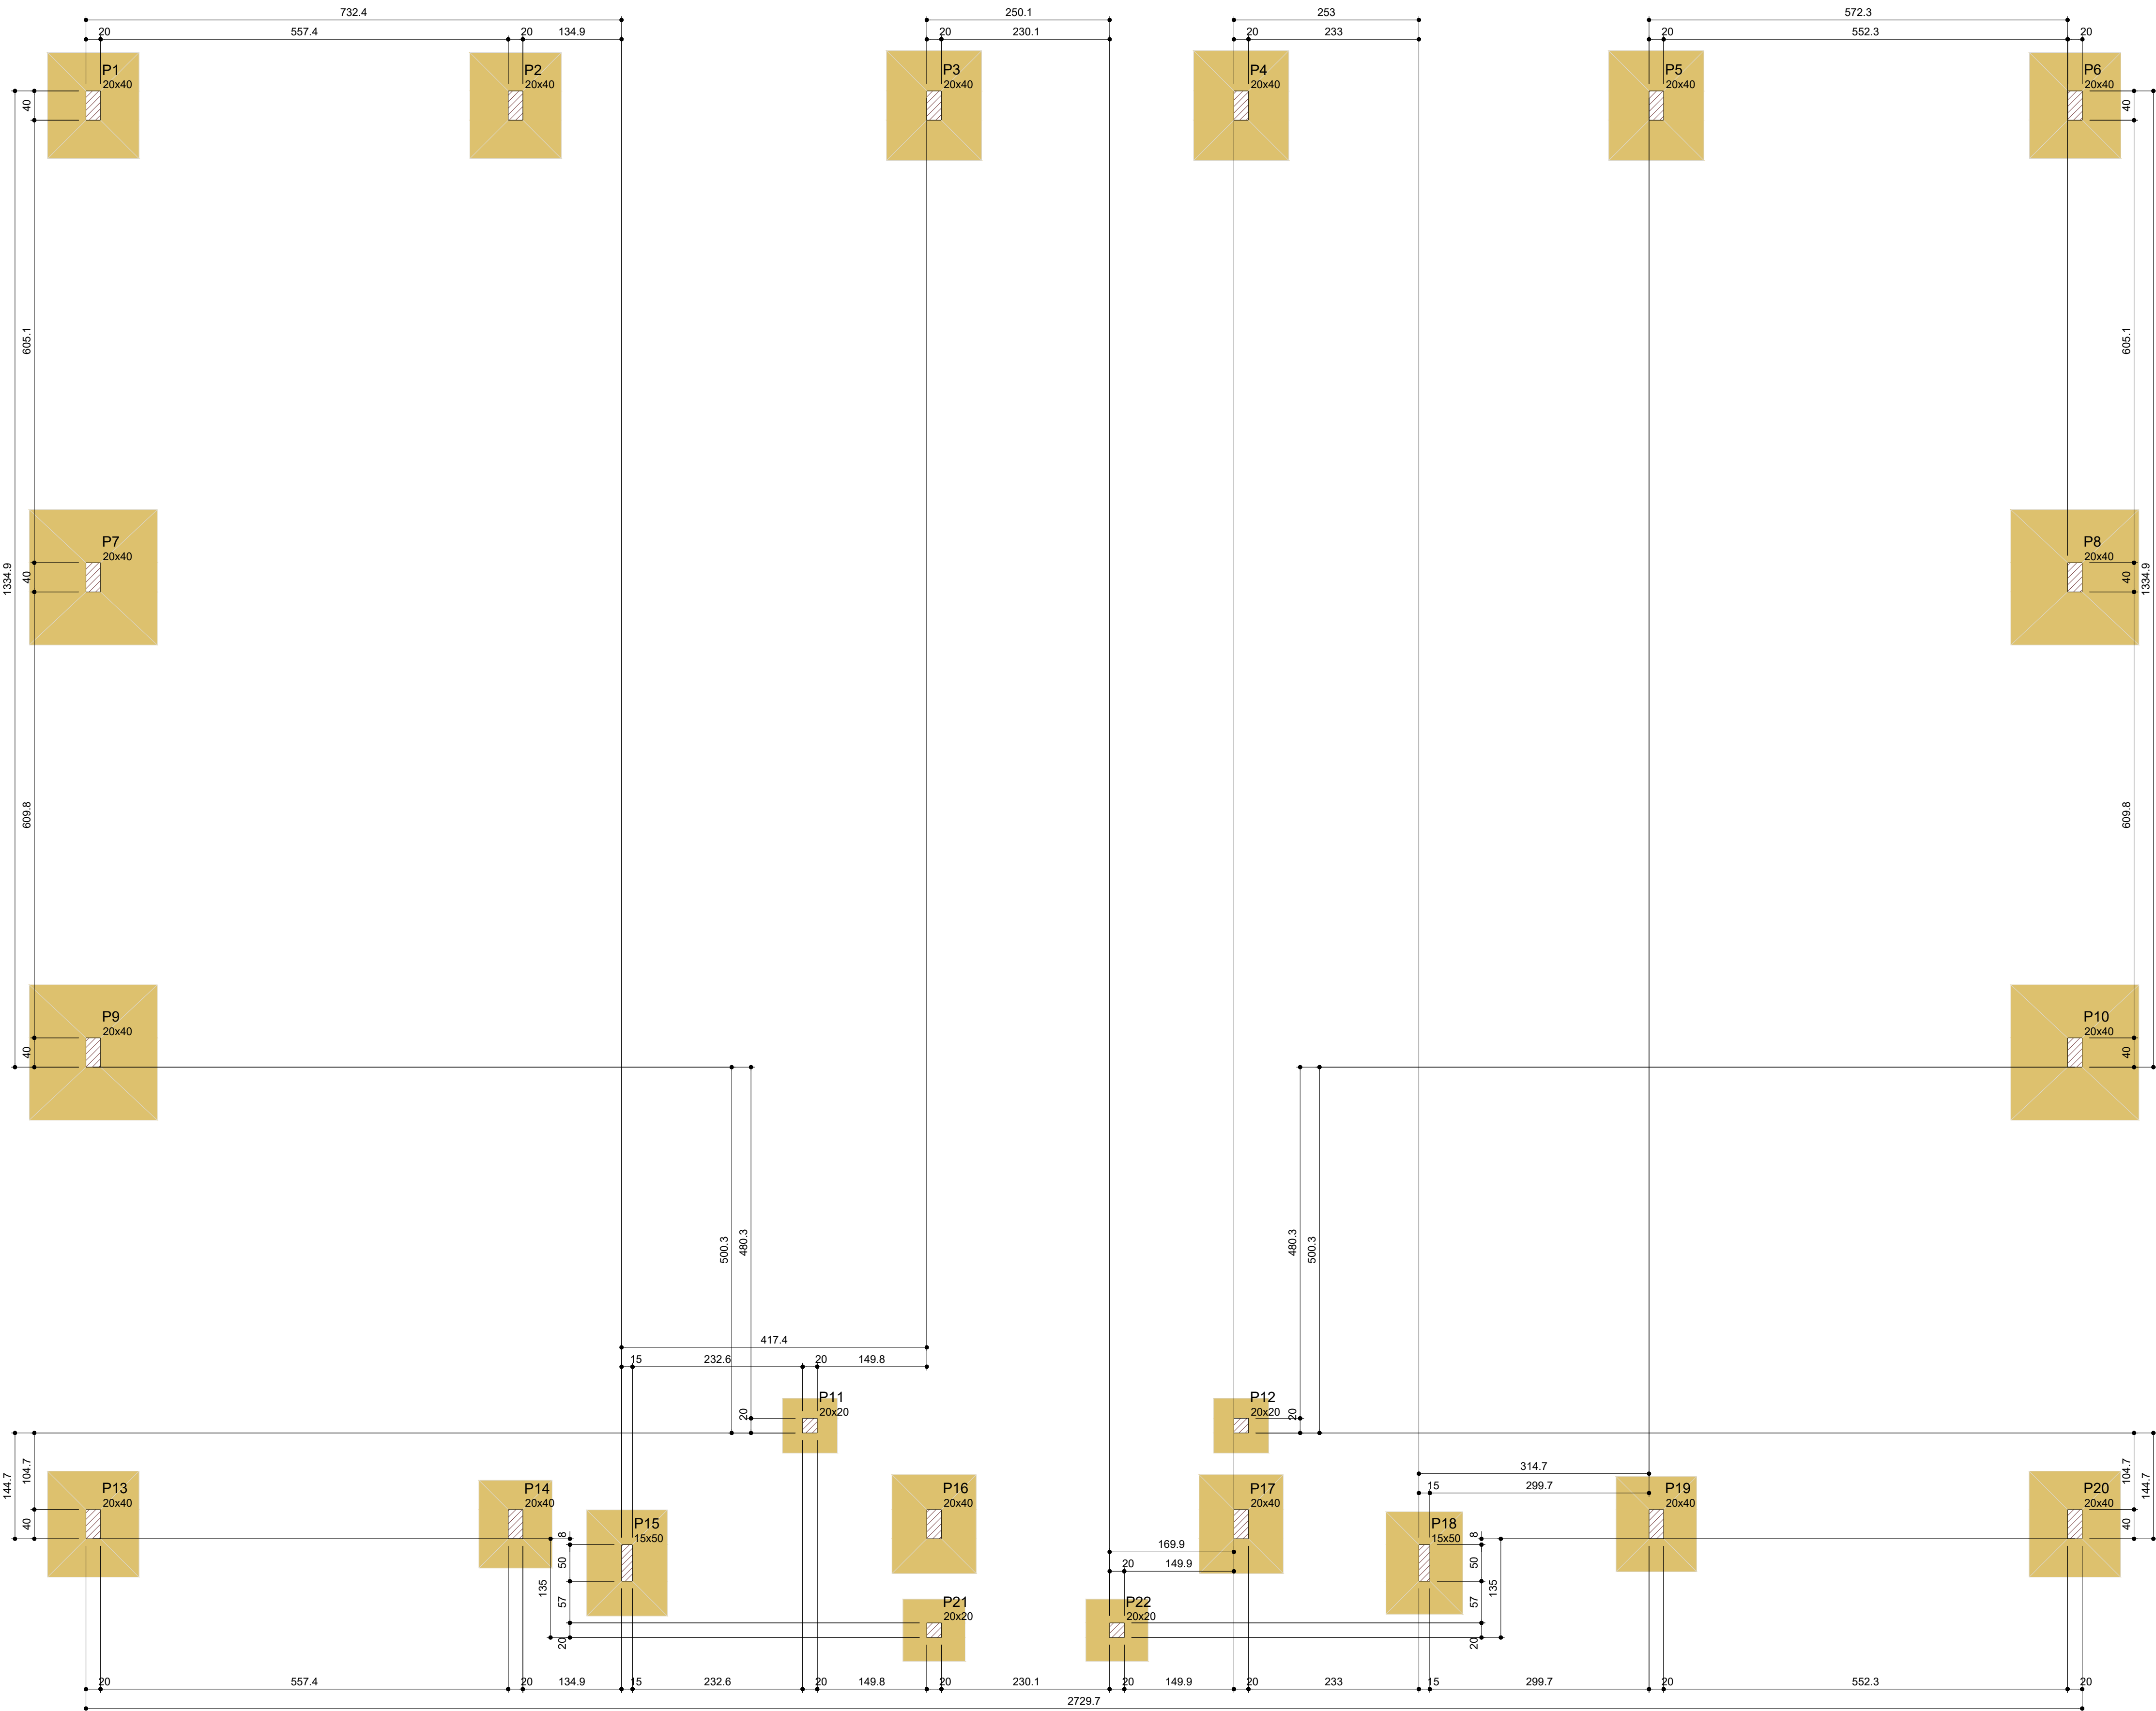

Características dos materiais		
Elemento	1cx (kg/cm²)	Eco (kg/cm²)
Pilares	250	241500
Sapatas	300	268384

Pilares			
Nome	Seção (cm)	Elevação (cm)	Nível (cm)
P1	20x40	0	0
P2	20x40	0	0
P3	20x40	0	0
P4	20x40	0	0
P5	20x40	0	0
P6	20x40	0	0
P7	20x40	0	0
P8	20x40	0	0
P9	20x40	0	0
P10	20x40	0	0
P11	20x20	0	0
P12	20x20	0	0
P13	20x40	0	0
P14	20x40	0	0
P15	15x50	0	0
P16	20x40	0	0
P17	20x40	0	0
P18	15x50	0	0
P19	20x40	0	0
P20	20x40	0	0
P21	20x20	0	0
P22	20x20	0	0

Legenda dos pilares	
	Pilar que passa

Forma do pavimento Fundação (Nível 0)
escala 1:50

PROPRIETÁRIO: PREFEITURA MUNICIPAL DE COREMAS - PB

PROJETO: LINCOLN CARTAXO DE LIRA JÚNIOR CREA 160.814.689-8

CONSTRUÇÃO:

FOLHA 02/26	PROJETO: CONSTRUÇÃO DE GINÁSIO POLIESPORTIVO - ESTRUTURAL			
	CONVENIENTE: PREFEITURA MUNICIPAL DE COREMAS - PB			
	CONVENIADO: MUNICÍPIO DE COREMAS - PB			
	LOCALIDADE: COREMAS - PB			
DESENHO	DATA	RESPONSÁVEL	RUBRICA	DADOS
CÓPIA	AGO/2025	LINCOLN CARTAXO		
VISTO				
ESCALAS	DESENHOS			CONVÊNIO
Indicada	- Forma do Pavimento Fundação (Nível 0)			GOVERNO DO ESTADO
				ARQUIVO

Aprovações: