


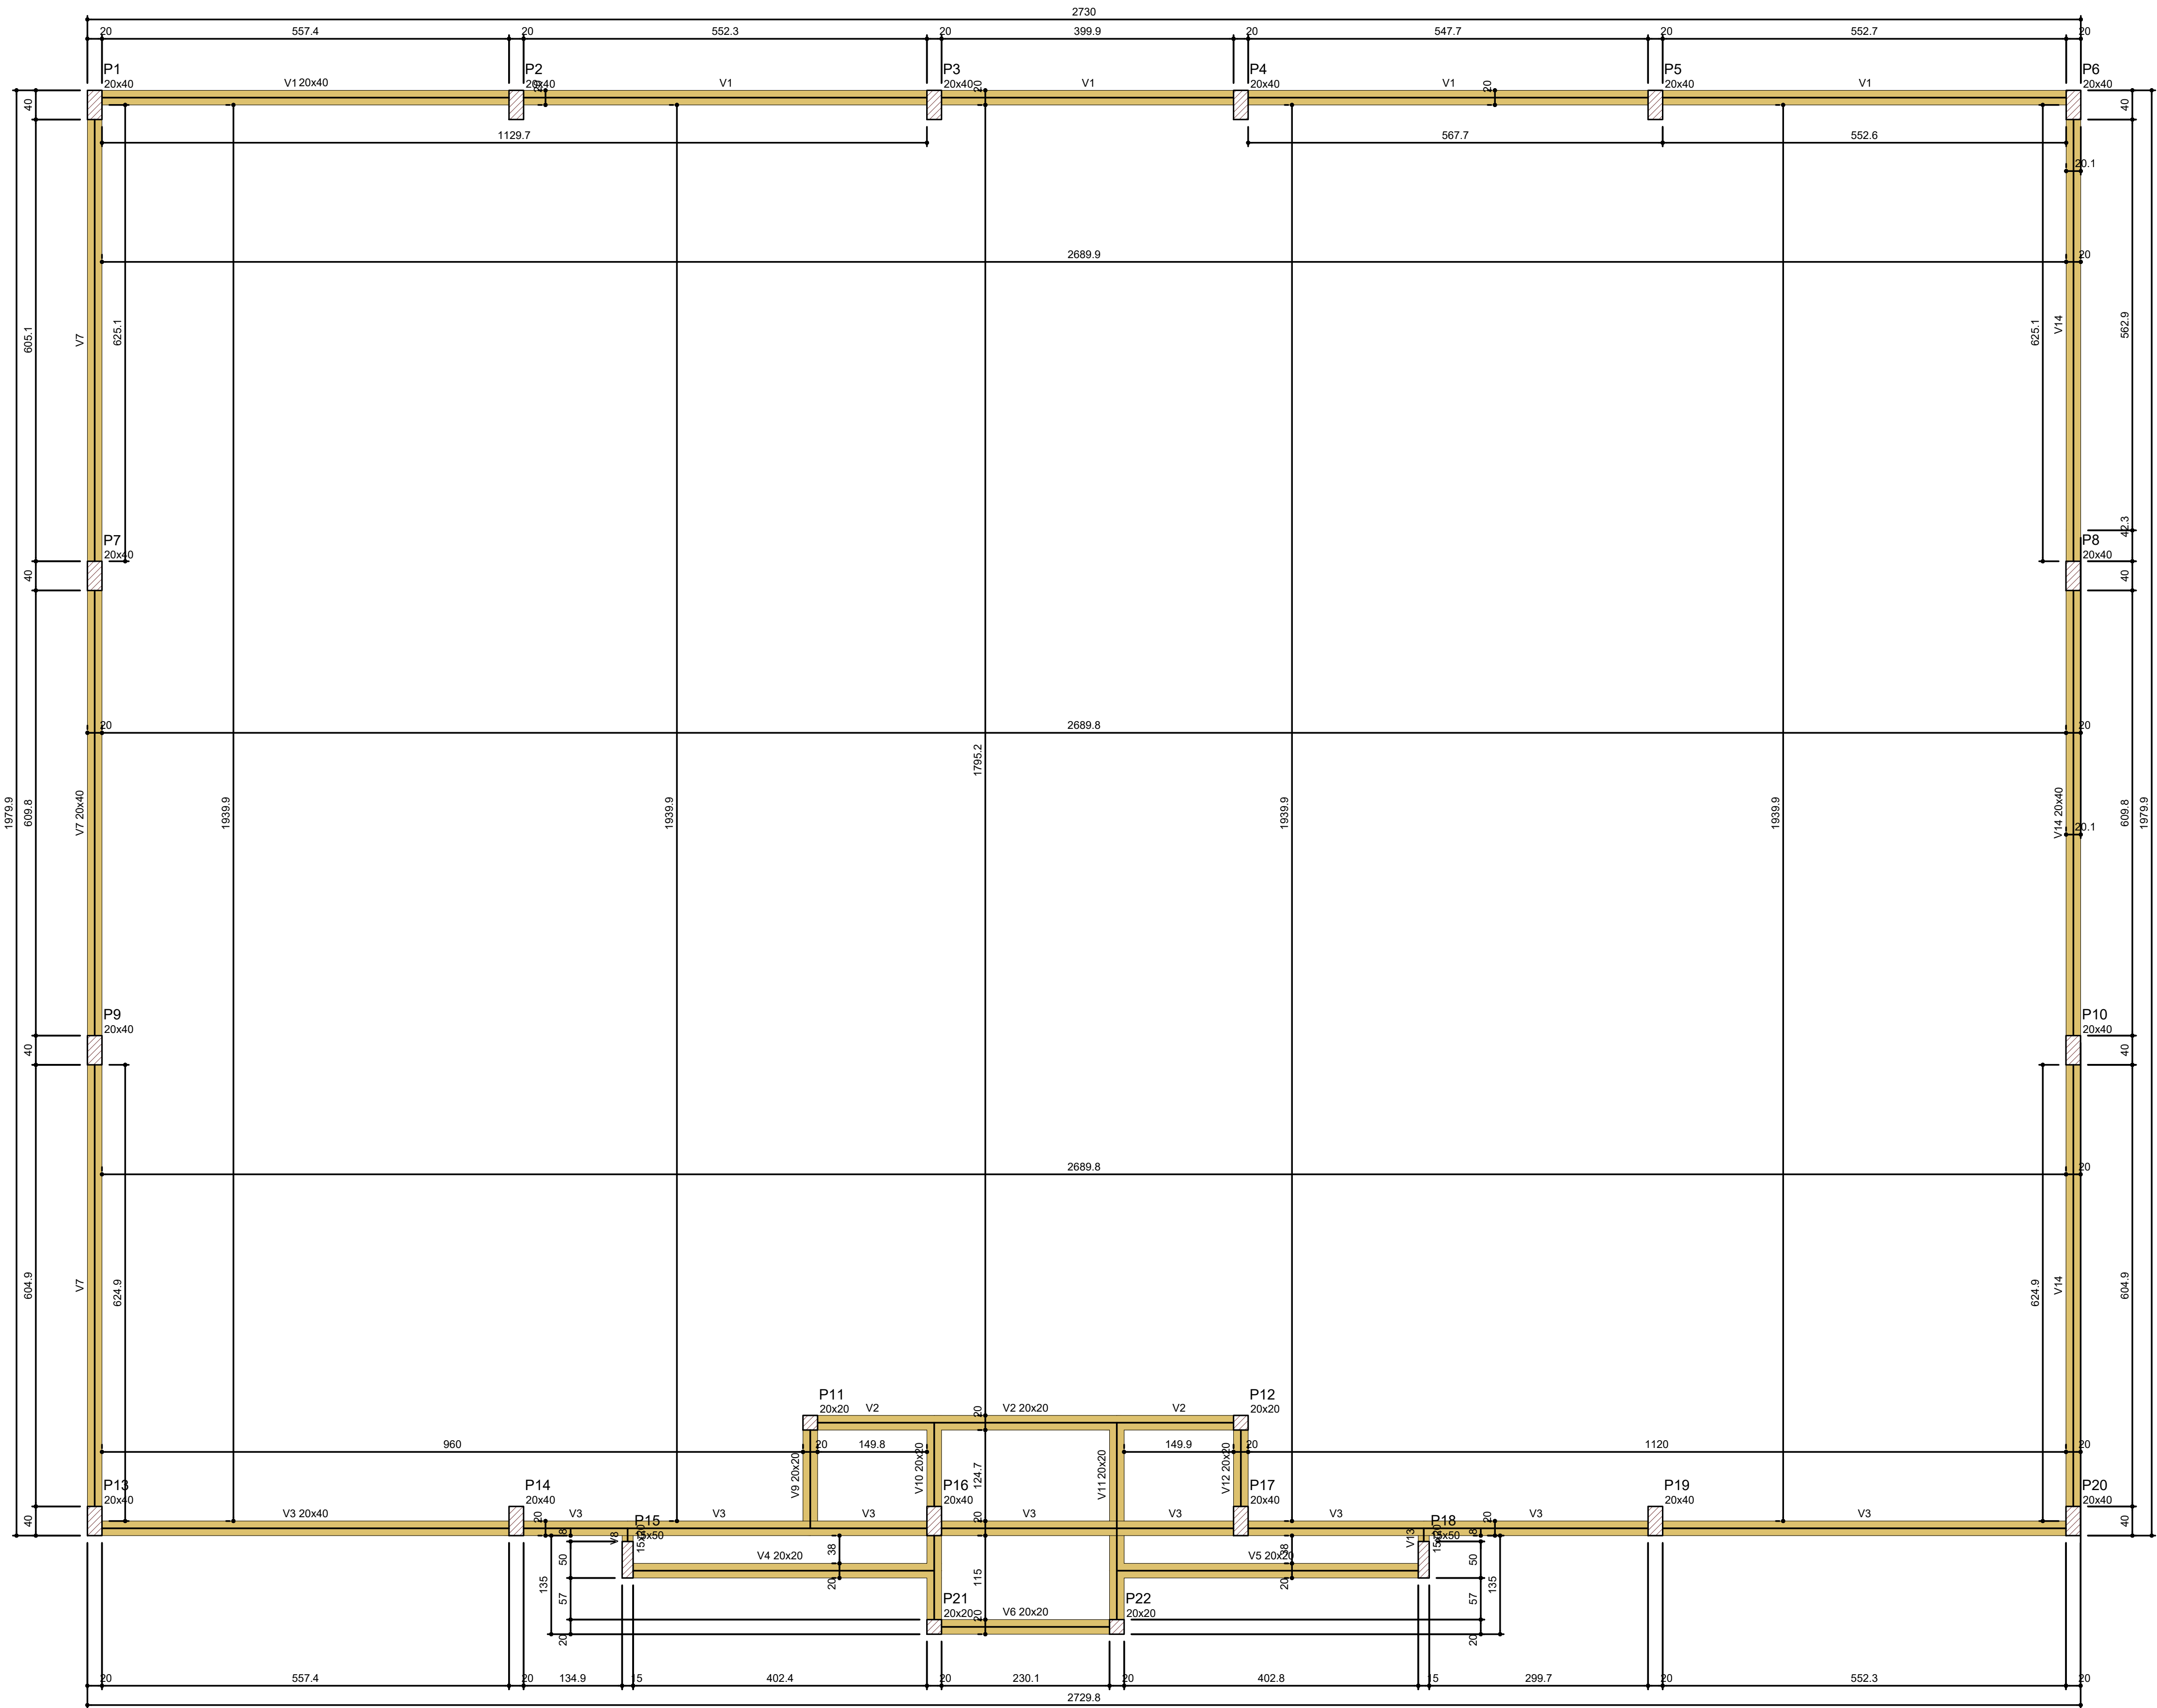

Forma do pavimento Baldrames (Nível 40)
escala 1:50

Vigas			
Nome	Seção (cm)	Elevação (cm)	Nível (cm)
V1	20x40	0	40
V2	20x20	0	40
V3	20x40	0	40
V4	20x20	0	40
V5	20x20	0	40
V6	20x20	0	40
V7	20x40	0	40
V8	15x20	0	40
V9	20x20	0	40
V10	20x20	0	40
V11	20x20	0	40
V12	20x20	0	40
V13	15x20	0	40
V14	20x40	0	40

Características dos materiais	
fck (kgf/cm²)	Ecs (kgf/cm²)
250	241500

Pilares			
Nome	Seção (cm)	Elevação (cm)	Nível (cm)
P1	20x40	0	40
P2	20x40	0	40
P3	20x40	0	40
P4	20x40	0	40
P5	20x40	0	40
P6	20x40	0	40
P7	20x40	0	40
P8	20x40	0	40
P9	20x40	0	40
P10	20x40	0	40
P11	20x20	0	40
P12	20x20	0	40
P13	20x40	0	40
P14	20x40	0	40
P15	15x50	0	40
P16	20x40	0	40
P17	20x40	0	40
P18	15x50	0	40
P19	20x40	0	40
P20	20x40	0	40
P21	20x20	0	40
P22	20x20	0	40

Legenda dos pilares	
	Pilar que passa
	Pilar com mudança de seção

Legenda das vigas e paredes	
	Viga

PROPRIETÁRIO: PREFEITURA MUNICIPAL DE COREMAS - PB

PROJETO: LINCOLN CARTAXO DE LIRA JÚNIOR CREA 160.814.689-8

CONSTRUÇÃO:

FOLHA 06/26
PROJETO: CONSTRUÇÃO DE GINÁSIO POLIESPORTIVO - ESTRUTURAL
CONVENIENTE: PREFEITURA MUNICIPAL DE COREMAS - PB
CONVENIADO: MUNICÍPIO DE COREMAS - PB
LOCALIDADE: COREMAS - PB

DESENHO	DATA	RESPONSÁVEL	RUBRICA	DADOS
CDMA	AGO/2025	LINCOLN CARTAXO		
VISTO				
ESCALAS		DESENHOS		CONVÊNIO
Indicada		- FORMA DO PAV. BALDRAMES (NÍVEL 40)		GOVERNO DO ESTADO
				ARQUIVO

Aprovações: