


P5=P14=P16=P17=P19

VISTA H
ESC 1:2

VISTA B
ESC 1:2

BALDRAMES - L2


SEÇÃO
ESC 1:20

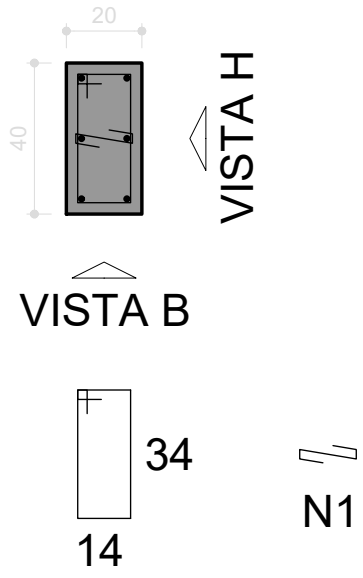

4 N2 ø5.0 C=107
4 N1 ø5.0 C=29


40

0

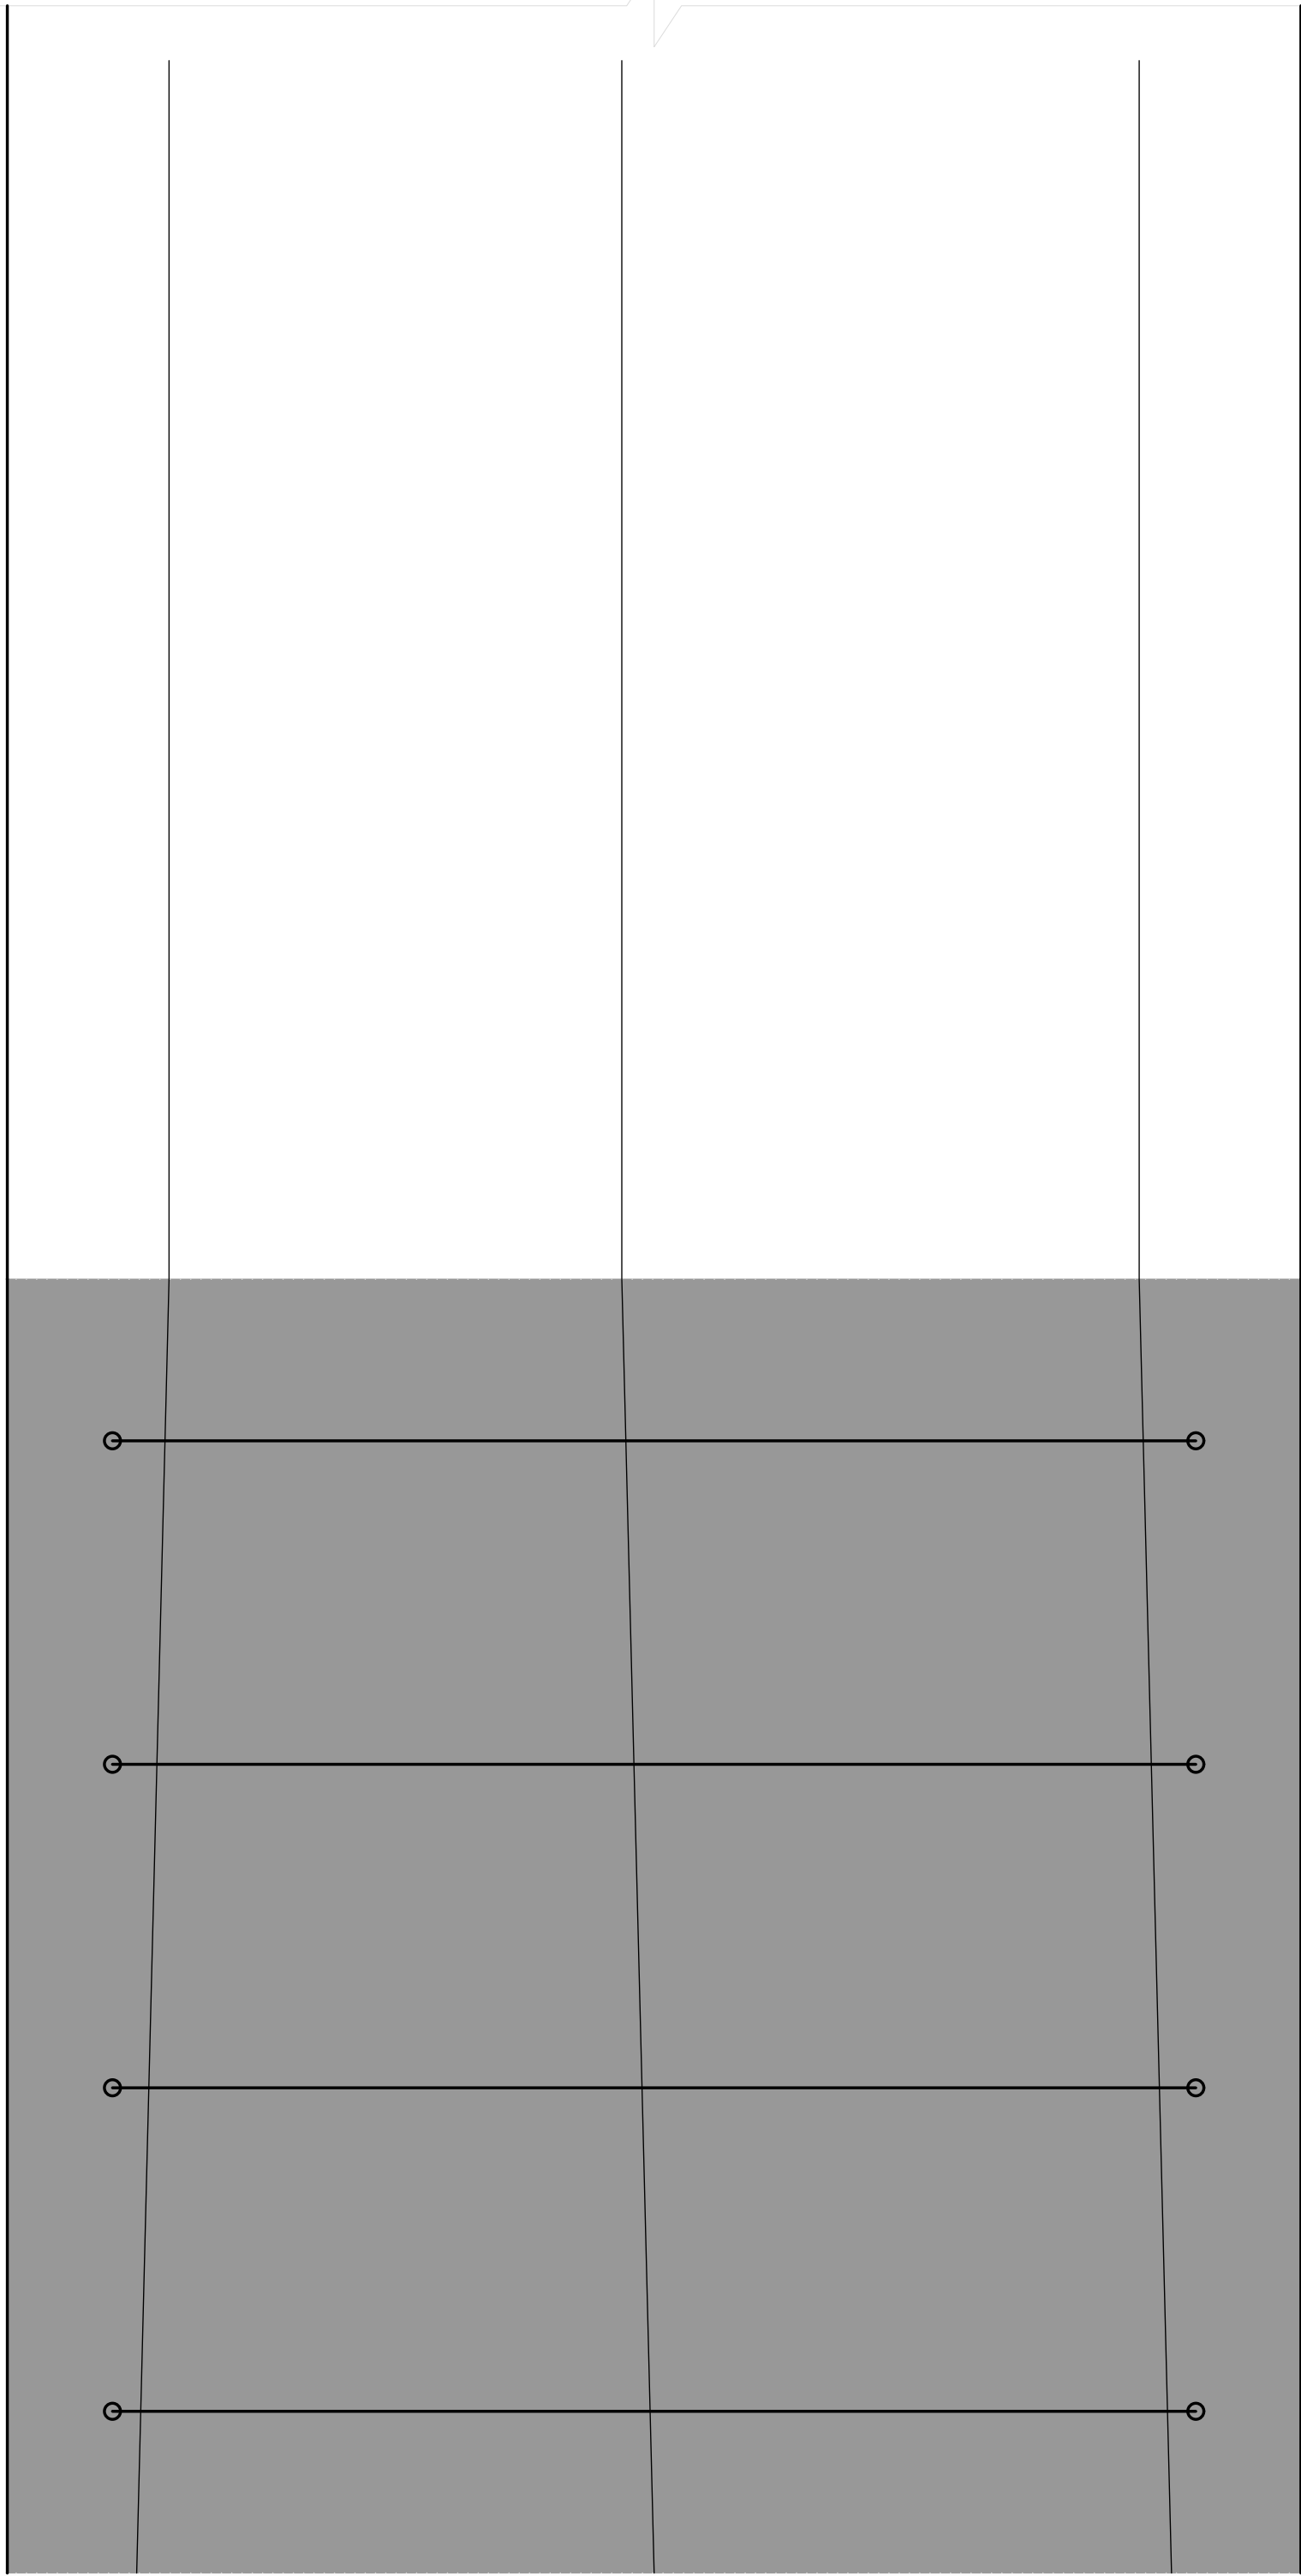

38

40
6 N7 ø10.0 C=78

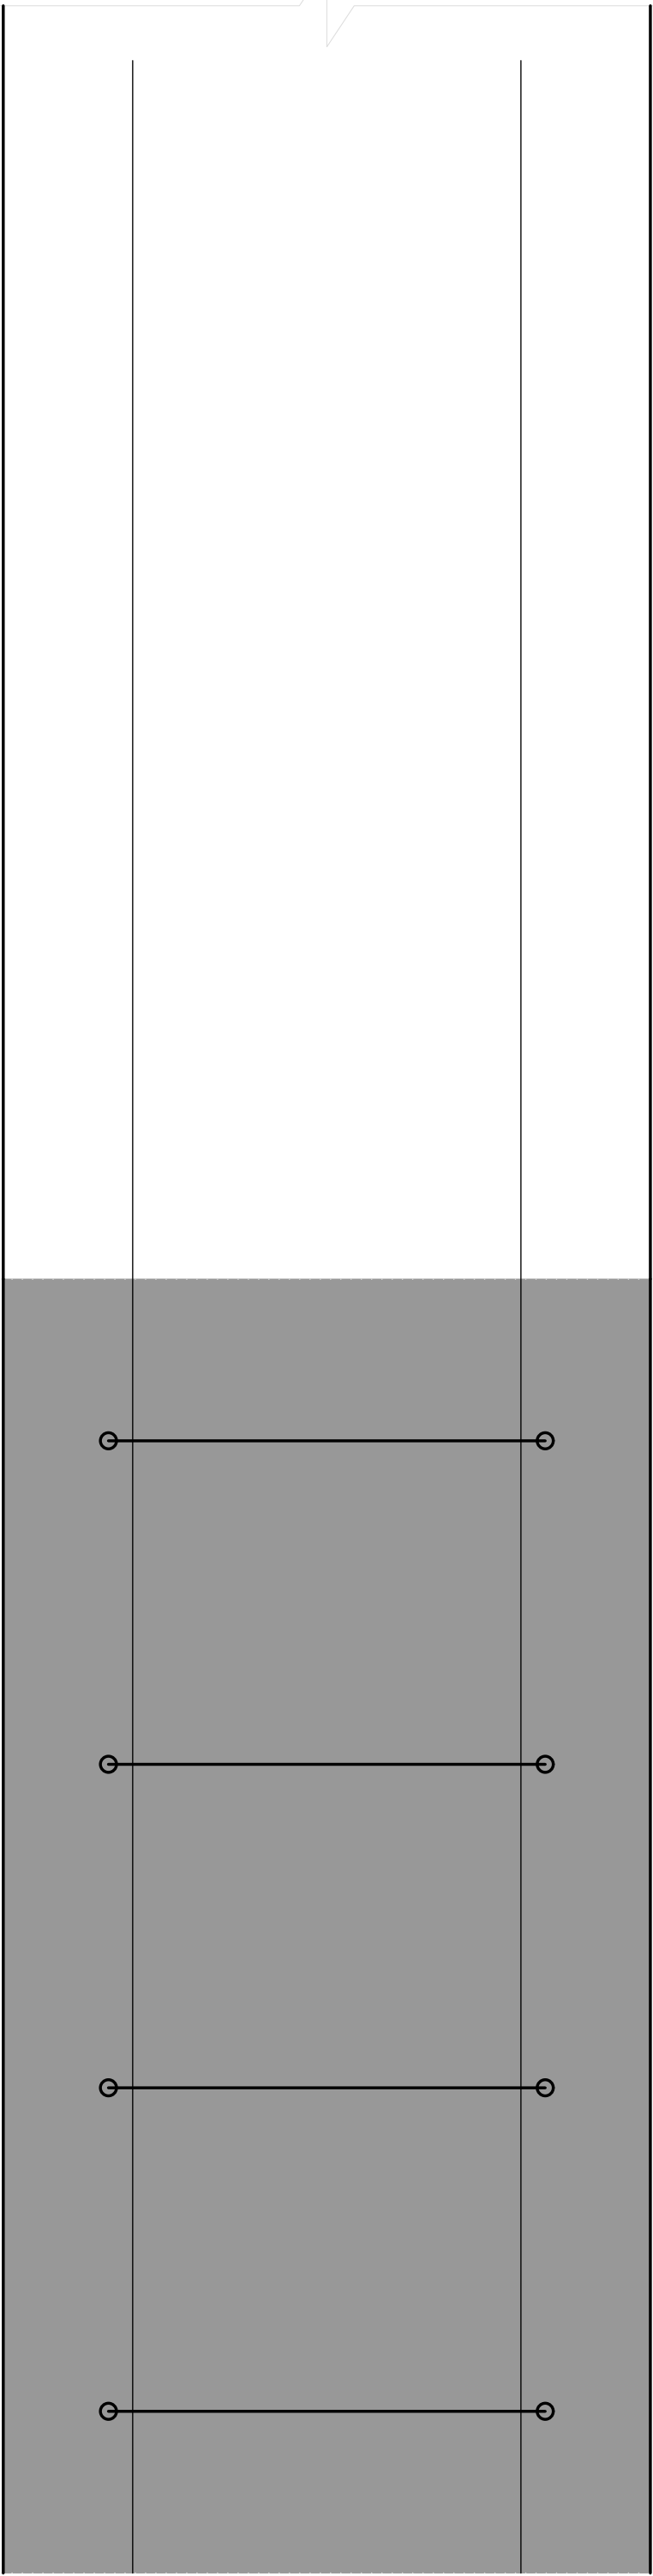

40

4 N2 ø10

***OBS.: OS QUADROS RESUMO REFERENTES A
ESTA PRANCHA CONSTAM NA PRANCHA 11/26**

PROPRIETÁRIO: PREFEITURA MUNICIPAL DE COREMAS - PB

PROJETO: LINCOLN CARTAXO DE LIRA JÚNIOR CREA 160.814.689-8

CONSTRUÇÃO:

FOLHA 09/26	PROJETO: CONSTRUÇÃO DE GINÁSIO POLIESPORTIVO - ESTRUTURAL			
	CONVENIENTE: PREFEITURA MUNICIPAL DE COREMAS - PB			
	CONVENIADO: MUNICÍPIO DE COREMAS - PB			
	LOCALIDADE: COREMAS - PB			
	DATA	RESPONSÁVEL	RUBRICA	DADOS
DESENHO	AGO/2025	LINCOLN CARTAXO		
CÓPIA				
VISTO				
ESCALAS	DESENHOS			CONVÊNIO
	Indicada			GOVERNO DO ESTADO
				ARQUIVO

Aprovações: