




V1
ESC 1:30

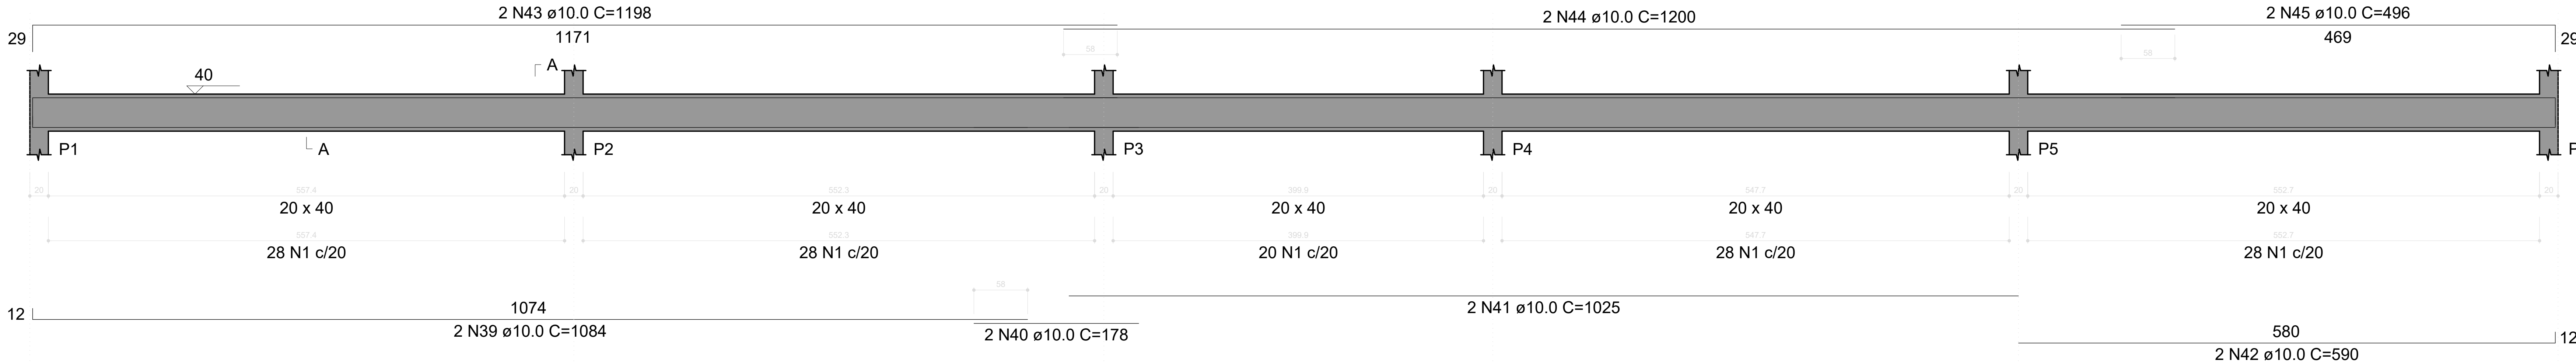


SEÇÃO A-A
ESC 1:25

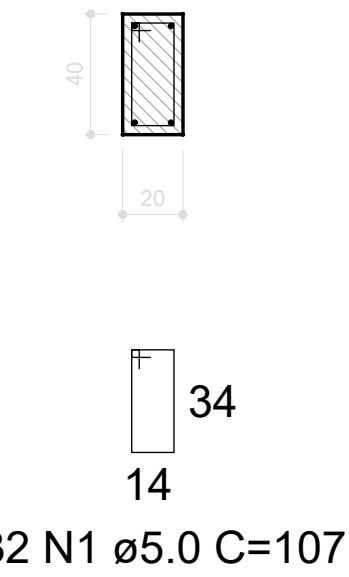


V6
ESC 1:30

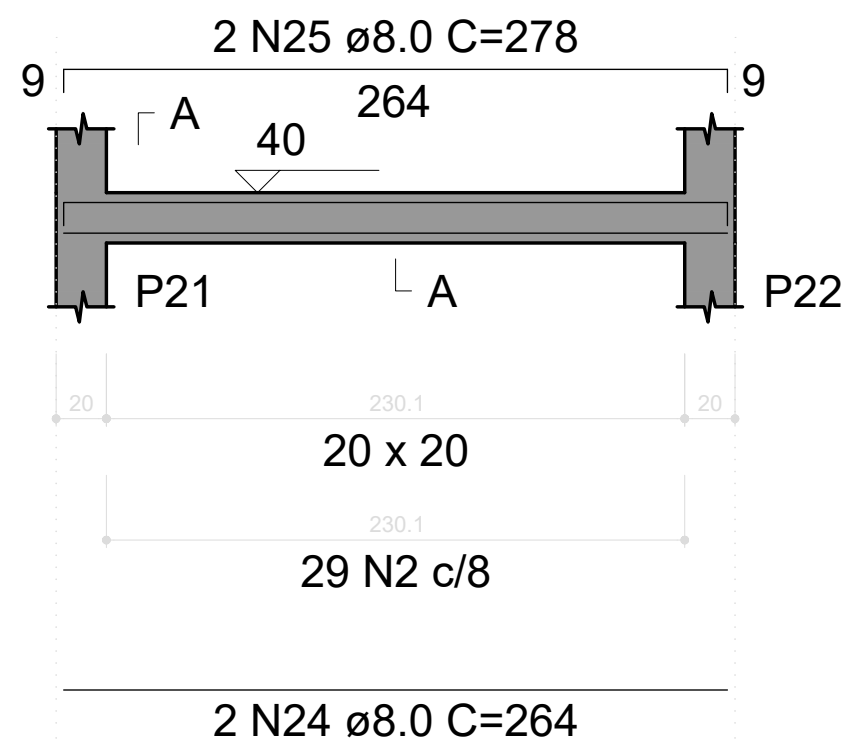


V7
ESC 1:30

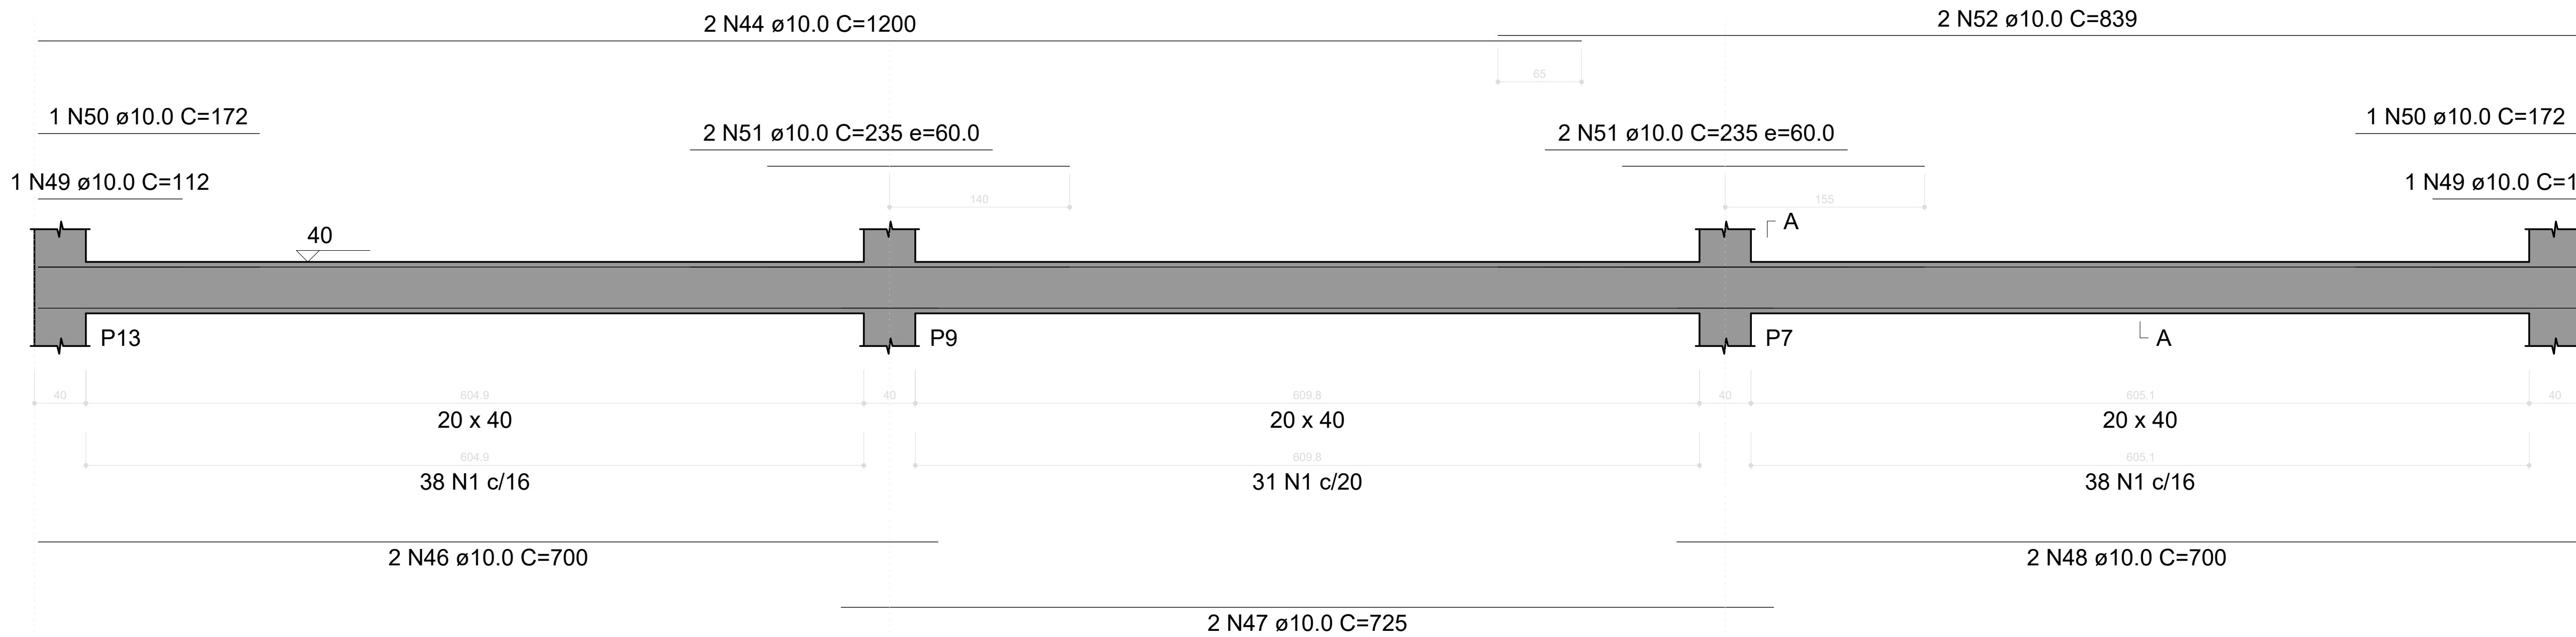

V8
ESC 1:30

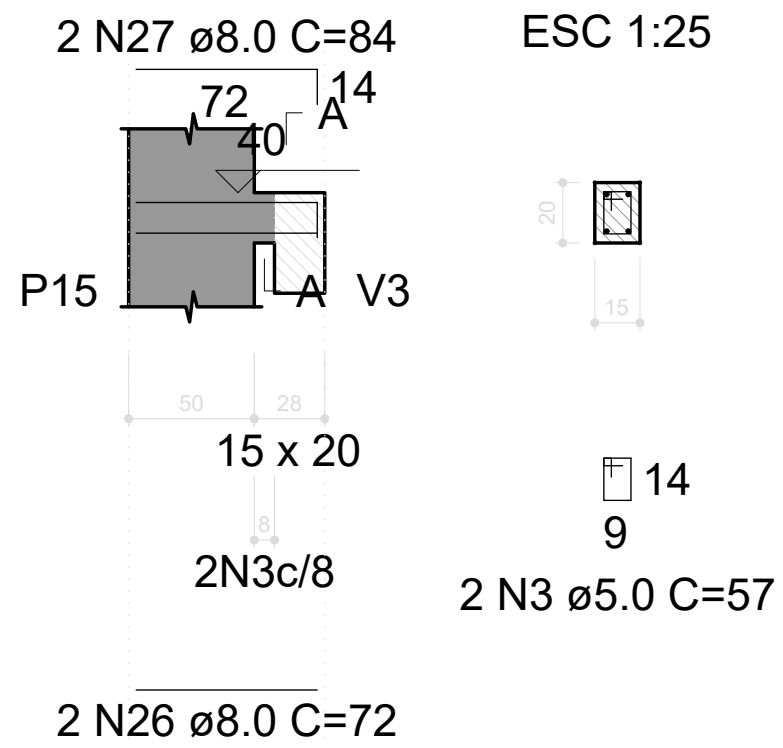

SEÇÃO A-A
ESC 1:25

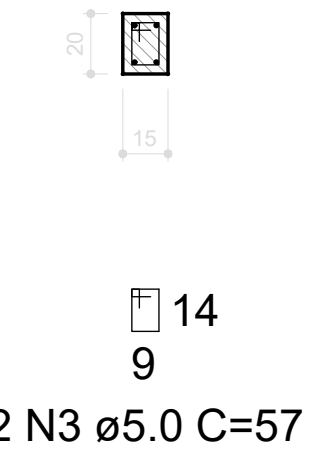

*OBS.: OS QUADROS RESUMO REFERENTES A ESTA PRANCHA CONSTAM NA PRANCHA 14/26

PROPRIETÁRIO: PREFEITURA MUNICIPAL DE COREMAS - PB
LINCOLN CARTAXO DE LIRA
Assinado de forma digital por LINCOLN CARTAXO DE LIRA JUNIOR:06897861405
Dados: 2025.08.08 12:22:23 -03'00'
PROJETO: LINCOLN CARTAXO DE LIRA JÚNIOR CREA 160.814.689-8

CONSTRUÇÃO:

FOLHA	PROJETO:	CONSTRUÇÃO DE GINÁSIO POLIESPORTIVO - ESTRUTURAL		
12/26	CONVENIENTE:	PREFEITURA MUNICIPAL DE COREMAS - PB		
	CONVENIADO:	MUNICÍPIO DE COREMAS - PB		
	LOCALIDADE:	COREMAS - PB		
DESENHO	DATA	RESPONSÁVEL	RUBRICA	DADOS
CÓPIA	AGO/2025	LINCOLN CARTAXO		
VISTO				
ESCALAS	DESENHOS			CONVÊNIO
Indicada	- VIGAS PAV. BALDRAMES (NÍVEL 40)			GOVERNO DO ESTADO
				ARQUIVO

Aprovações: