

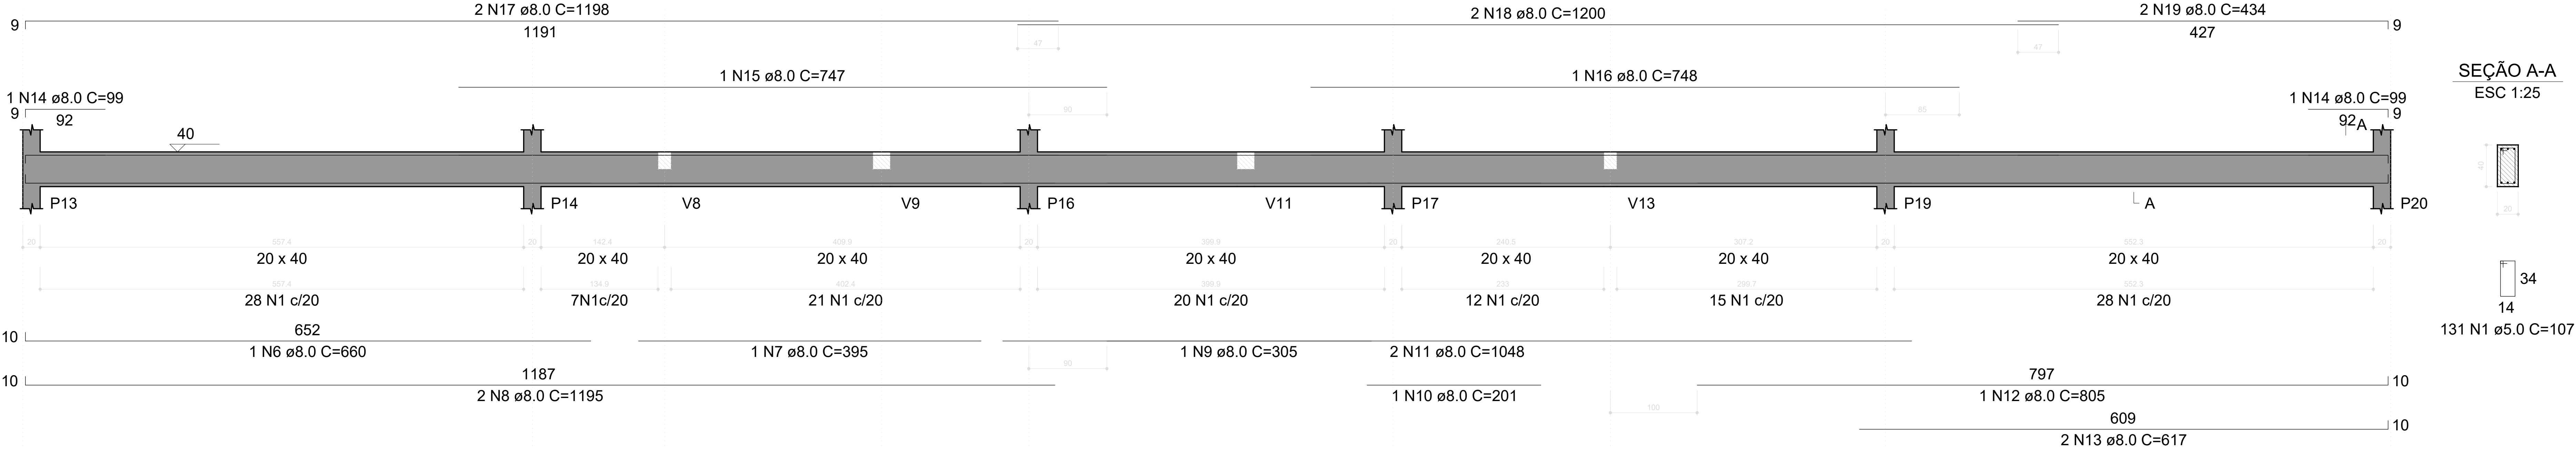


V3
ESC 1:30

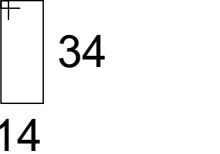


SEÇÃO A-A
ESC 1:25

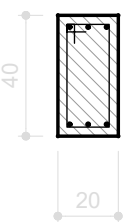


131 N1 ø5.0 C=107

V2
ESC 1:30

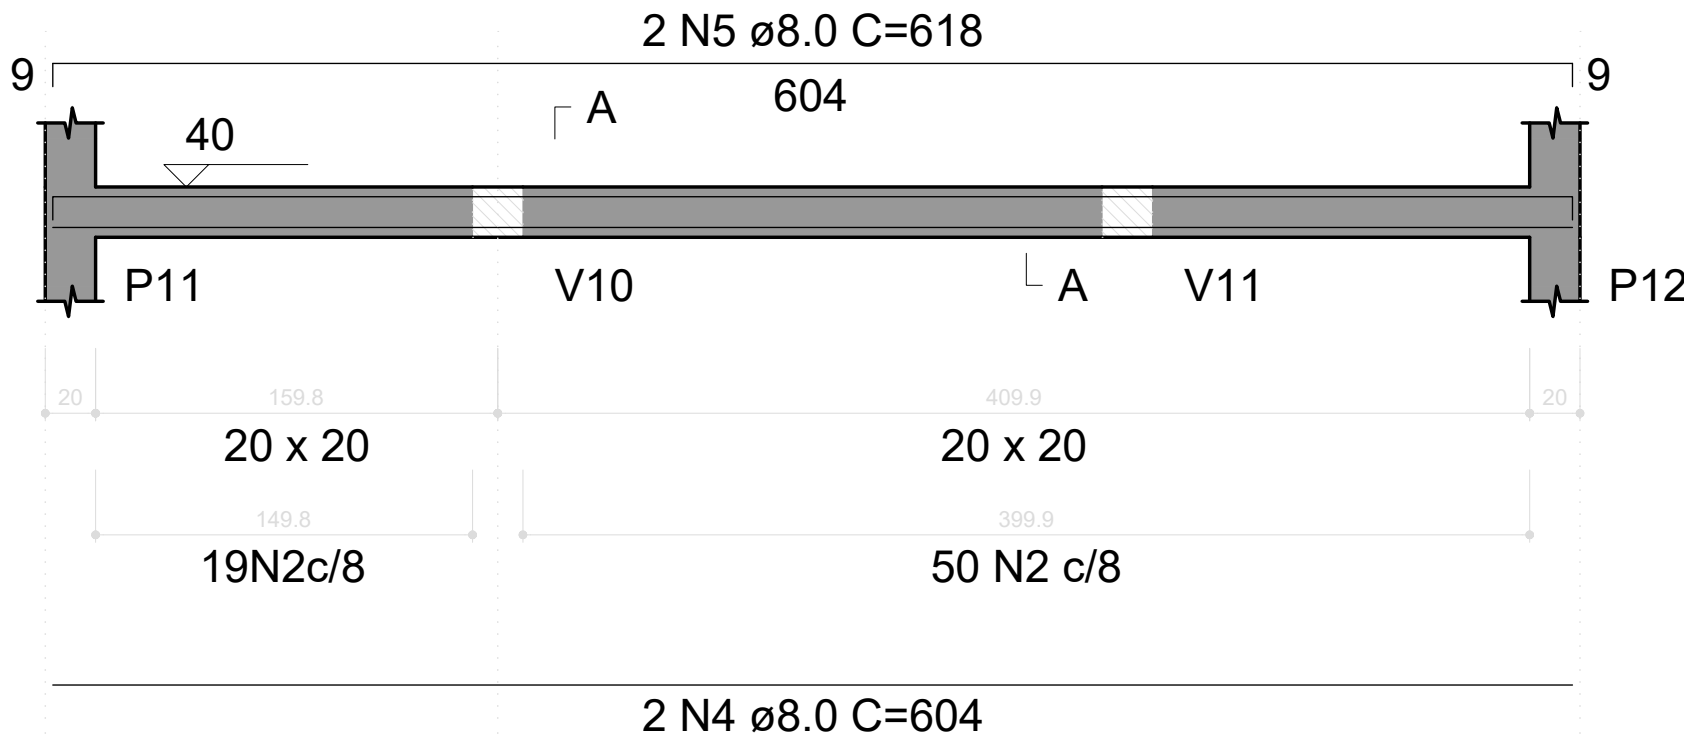


SEÇÃO A-A
ESC 1:25

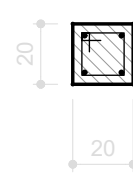


69 N2 ø5.0 C=67

V9
ESC 1:30

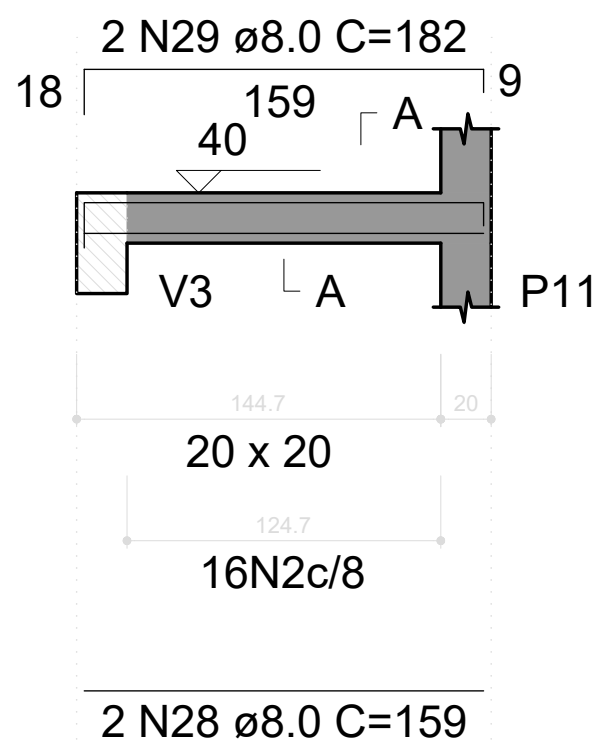


SEÇÃO A-A
ESC 1:25

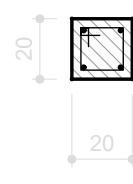


16 N2 ø5.0 C=67

V10
ESC 1:30

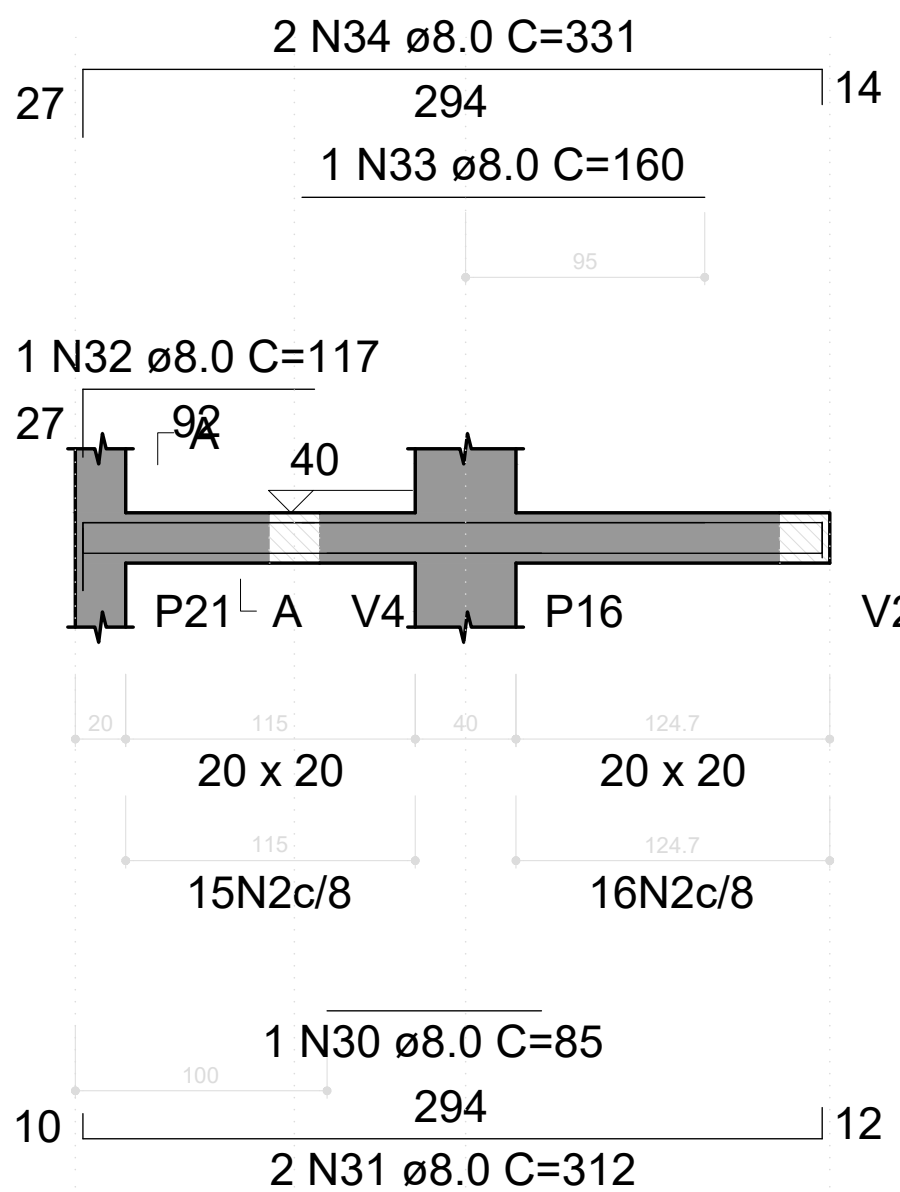


SEÇÃO A-A
ESC 1:25

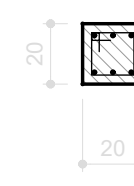


31 N2 ø5.0 C=67

V11
ESC 1:30

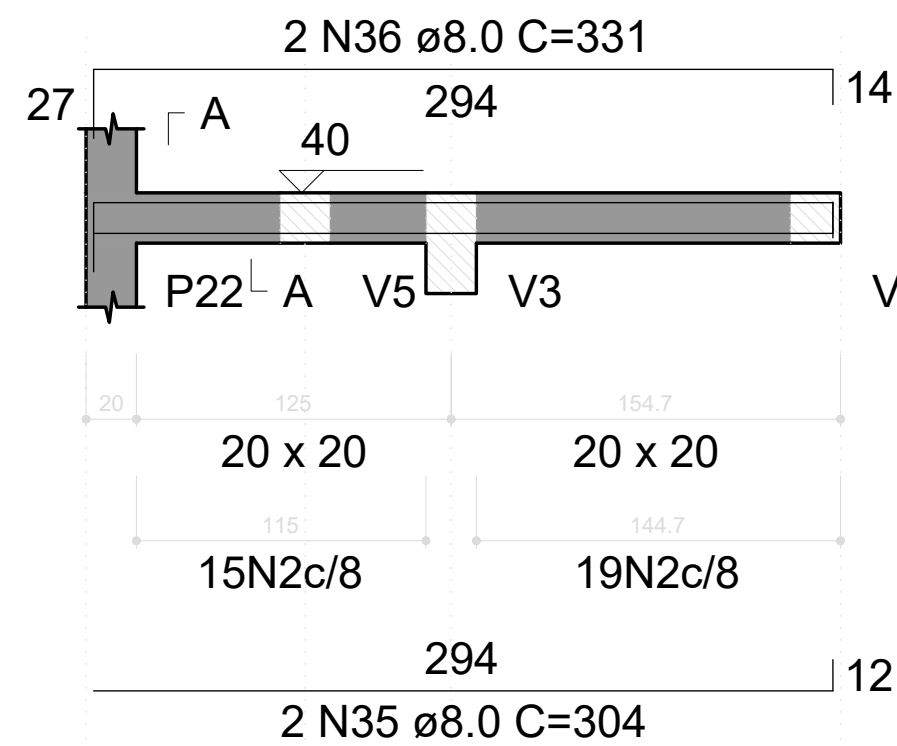


SEÇÃO A-A
ESC 1:25

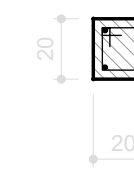


34 N2 ø5.0 C=67

V12
ESC 1:30

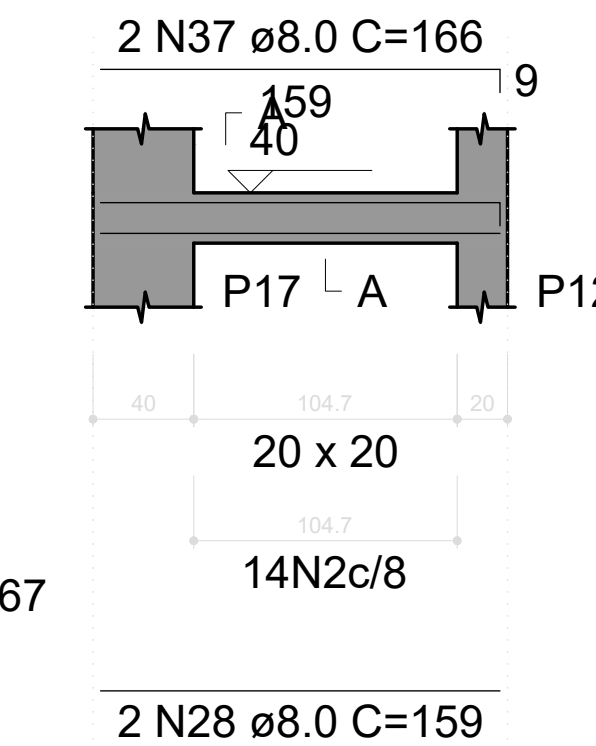


SEÇÃO A-A
ESC 1:25

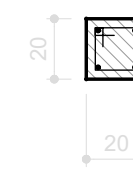


14 N2 ø5.0 C=67

V13
ESC 1:30

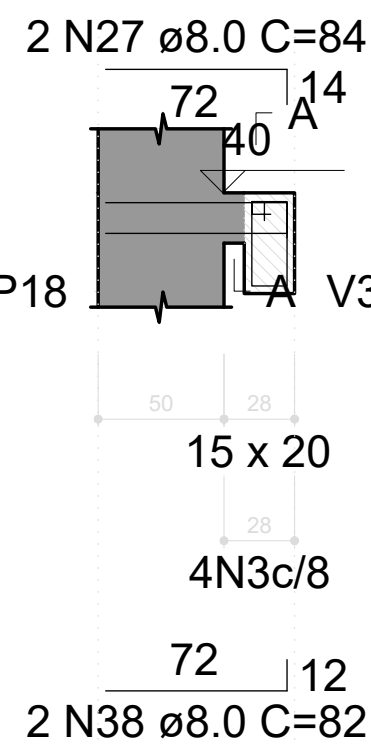


SEÇÃO A-A
ESC 1:25

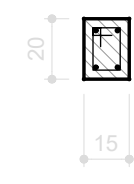

4 N3 ø5.0 C=57

SUSPENSÃO V3
ESC 1:25

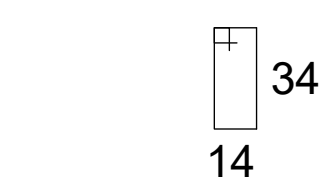

1 N53 ø10.0 C=109

*OBS.: OS QUADROS RESUMO REFERENTES A ESTA PRANCHA CONSTAM NA PRANCHA 14/26

PROPRIETÁRIO: PREFEITURA MUNICIPAL DE COREMAS - PB

PROJETO: LINCOLN CARTAXO DE LIRA JÚNIOR CREA 160.814.689-8

CONSTRUÇÃO:

FOLHA
13/26

PROJETO: CONSTRUÇÃO DE GINÁSIO POLIESPORTIVO - ESTRUTURAL
CONVENIENTE: PREFEITURA MUNICIPAL DE COREMAS - PB
CONVENIADO: MUNICÍPIO DE COREMAS - PB
LOCALIDADE: COREMAS - PB

DESENHO	DATA	RESPONSÁVEL	RUBRICA	DADOS
CÓPIA	AGO/2025	LINCOLN CARTAXO		
VISTO				
ESCALAS	DESENHOS			CONVÊNIO
Indicada	- VIGAS PAV. BALDRAMES (NÍVEL 40)			GOVERNO DO ESTADO
				ARQUIVO

Aprovações: